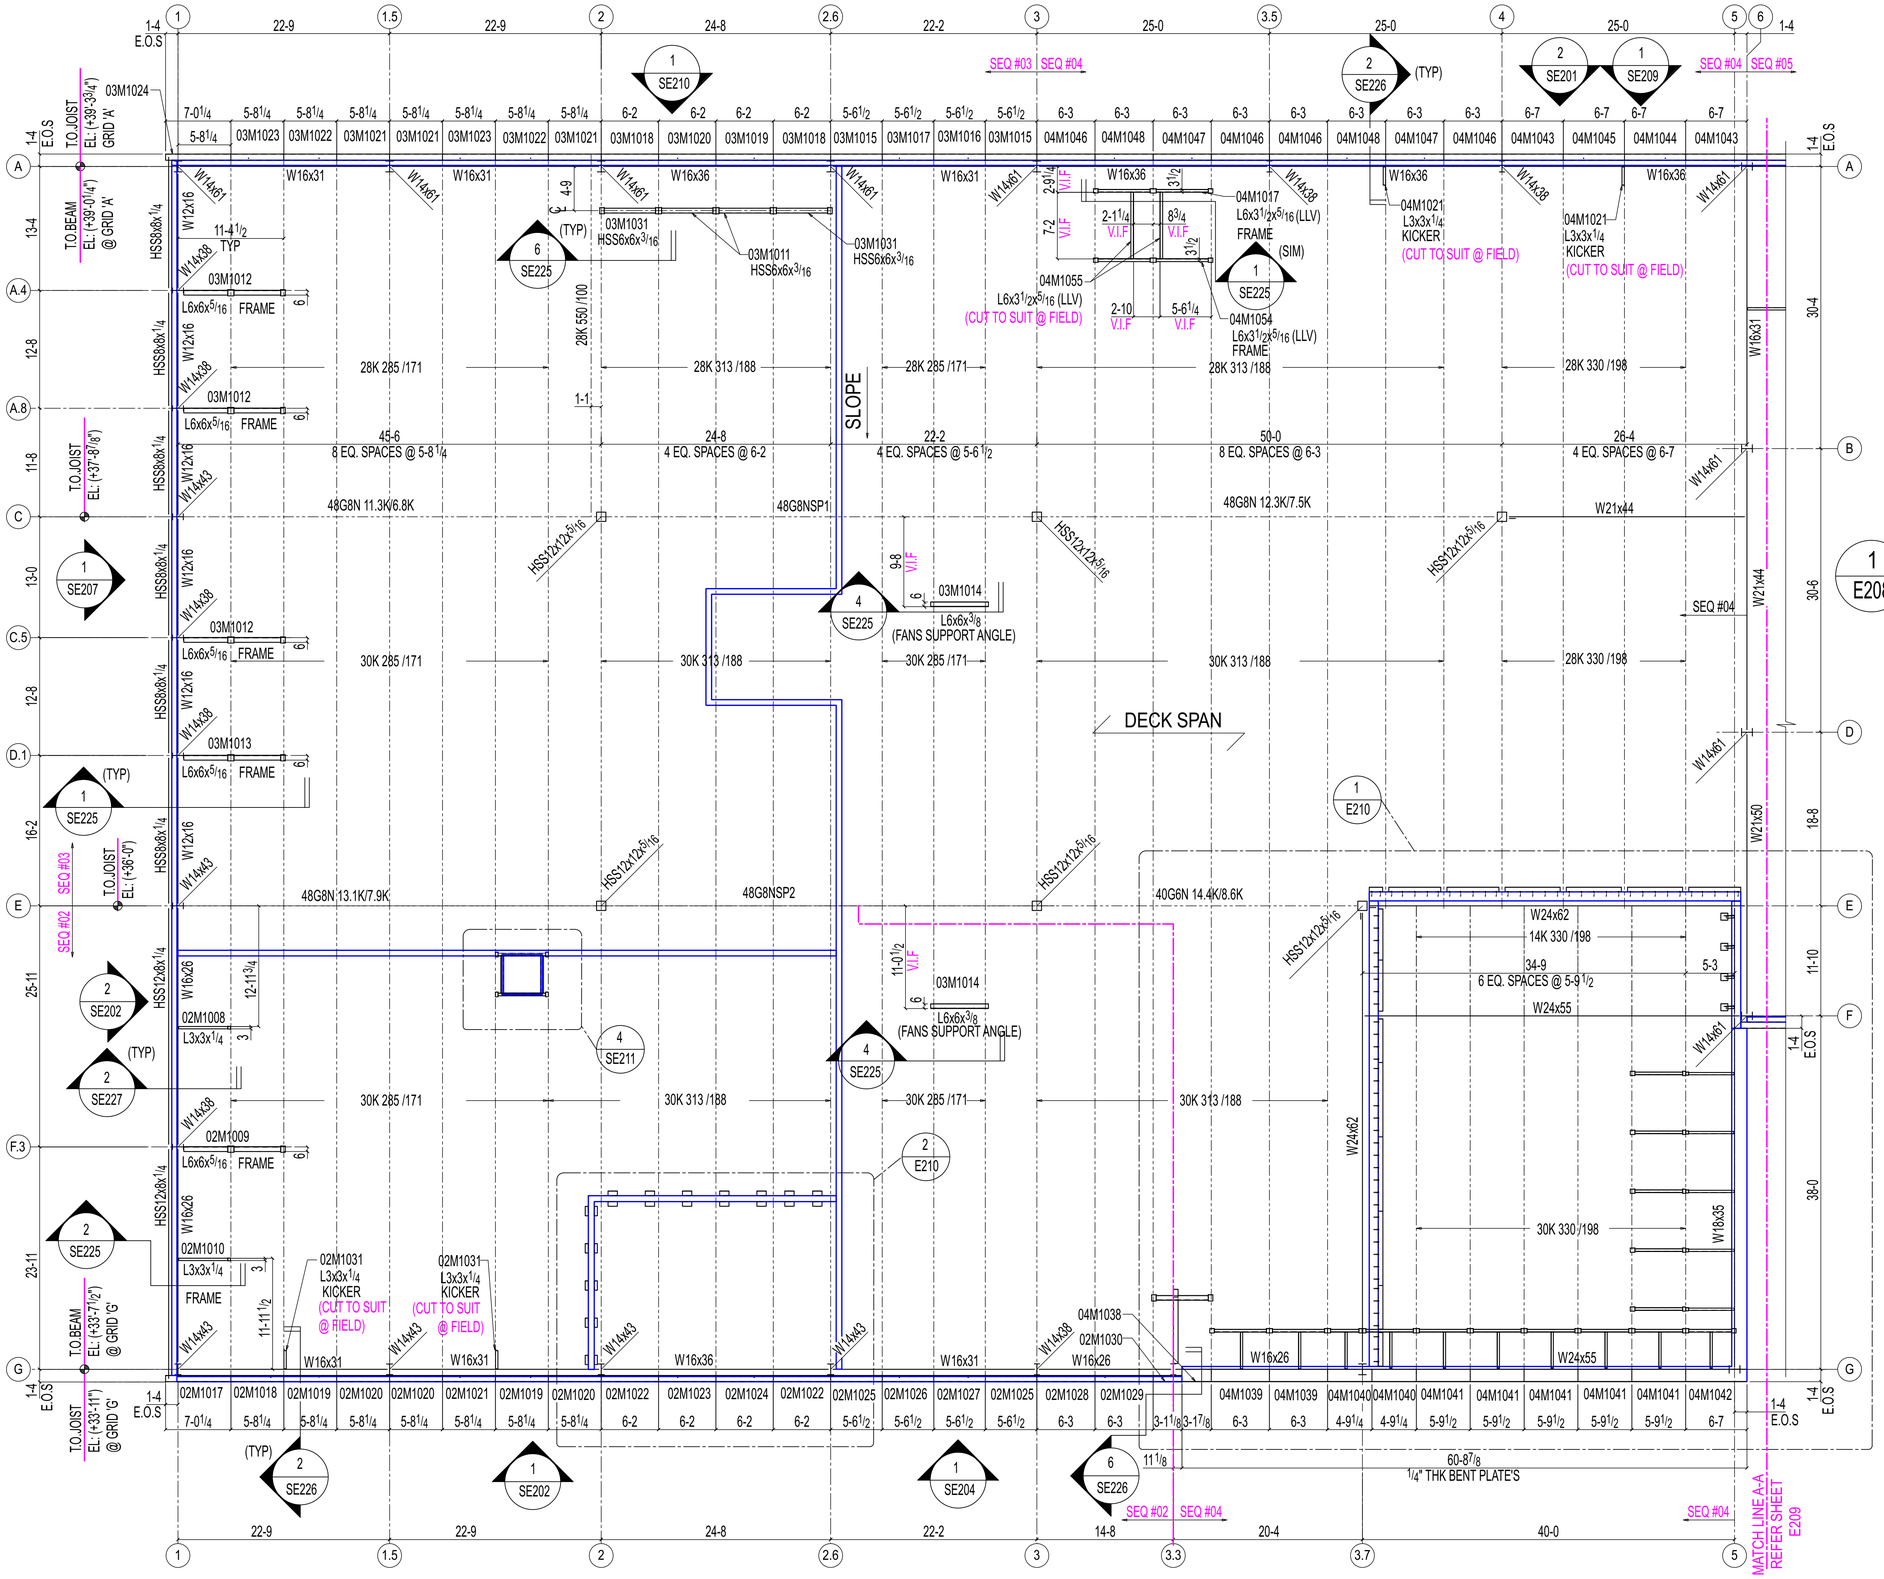

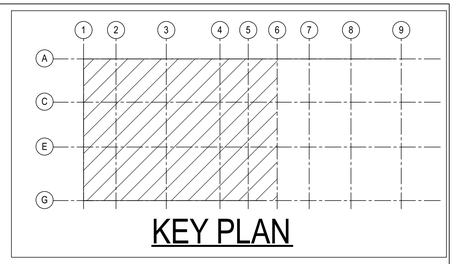

1 / E208 ROOF MISC FRAMING PLAN

(REF: 1/S104,1/A161)

TRUE NORTH PROJECT NORTH

NOTE:
1. ALL ELEVATION ARE REFERENCED FROM THE FINISHED FLOOR EL: [0'-0"] = DATUM EL: 100'-0" (U.N.O).
2. E.O.S- INDICATES EDGE OF SLAB.
3. ALL SLAB EDGE BENT PLATES ARE 5/16" THK. (U.N.O)
4. ——— - INDICATES JOIST (U.N.O).
5. ⟵⟶ - INDICATES METAL DECK SPAN DIRECTION.

NOTE:
FIELD APPLIED PAINT AND THERMAL BREAK PAINT WILL BE BY OTHERS.

REVISIONS

REV#	DWN BY	DESCRIPTION	DATE
A	SRP	ISSUED FOR APPROVAL	Jun 11 2025
0	GSV	ISSUED FOR CONSTRUCTION	Sep 5 2025

THE INFORMATION NOTED HEREON THIS DRAWING IS THE PROPERTY OF STEEL FAB ENTERPRISES, INC. AND SHALL NOTED BE USED WITHOUT WRITTEN CONSENT.

STEEL FAB ENTERPRISES, LLC
MISCELLANEOUS METALS FABRICATOR AND ERECTORS
623 BAUMGARDNER ROAD, LANCASTER, PA 17603
TEL. (717)464-0330 FAX (717)464-9464
WWW.STEELFABENTERPRISES.COM

AISC CERTIFIED FABRICATOR AND ERECTOR

PROJECT OWNER : CK CAPITAL, LLC
PROJECT DESCRIPTION : CLEVELAND BROTHERS-MILESBURG
PROJECT ADDRESS : 4025N. EAGLE VALLEY ROAD, HOWARD, PA 16841
CONTRACTOR : KINSLEY CONSTRUCTION, INC.

DRAWN BY : BAS	DATE : 5-20-25	PROJ. NO. : 25012	REV # 0
CHECKED BY : SRP	DATE : 5-20-25	DWG NO. : E208	

DWG DESCRIPTION : ROOF MISC FRAMING PLAN