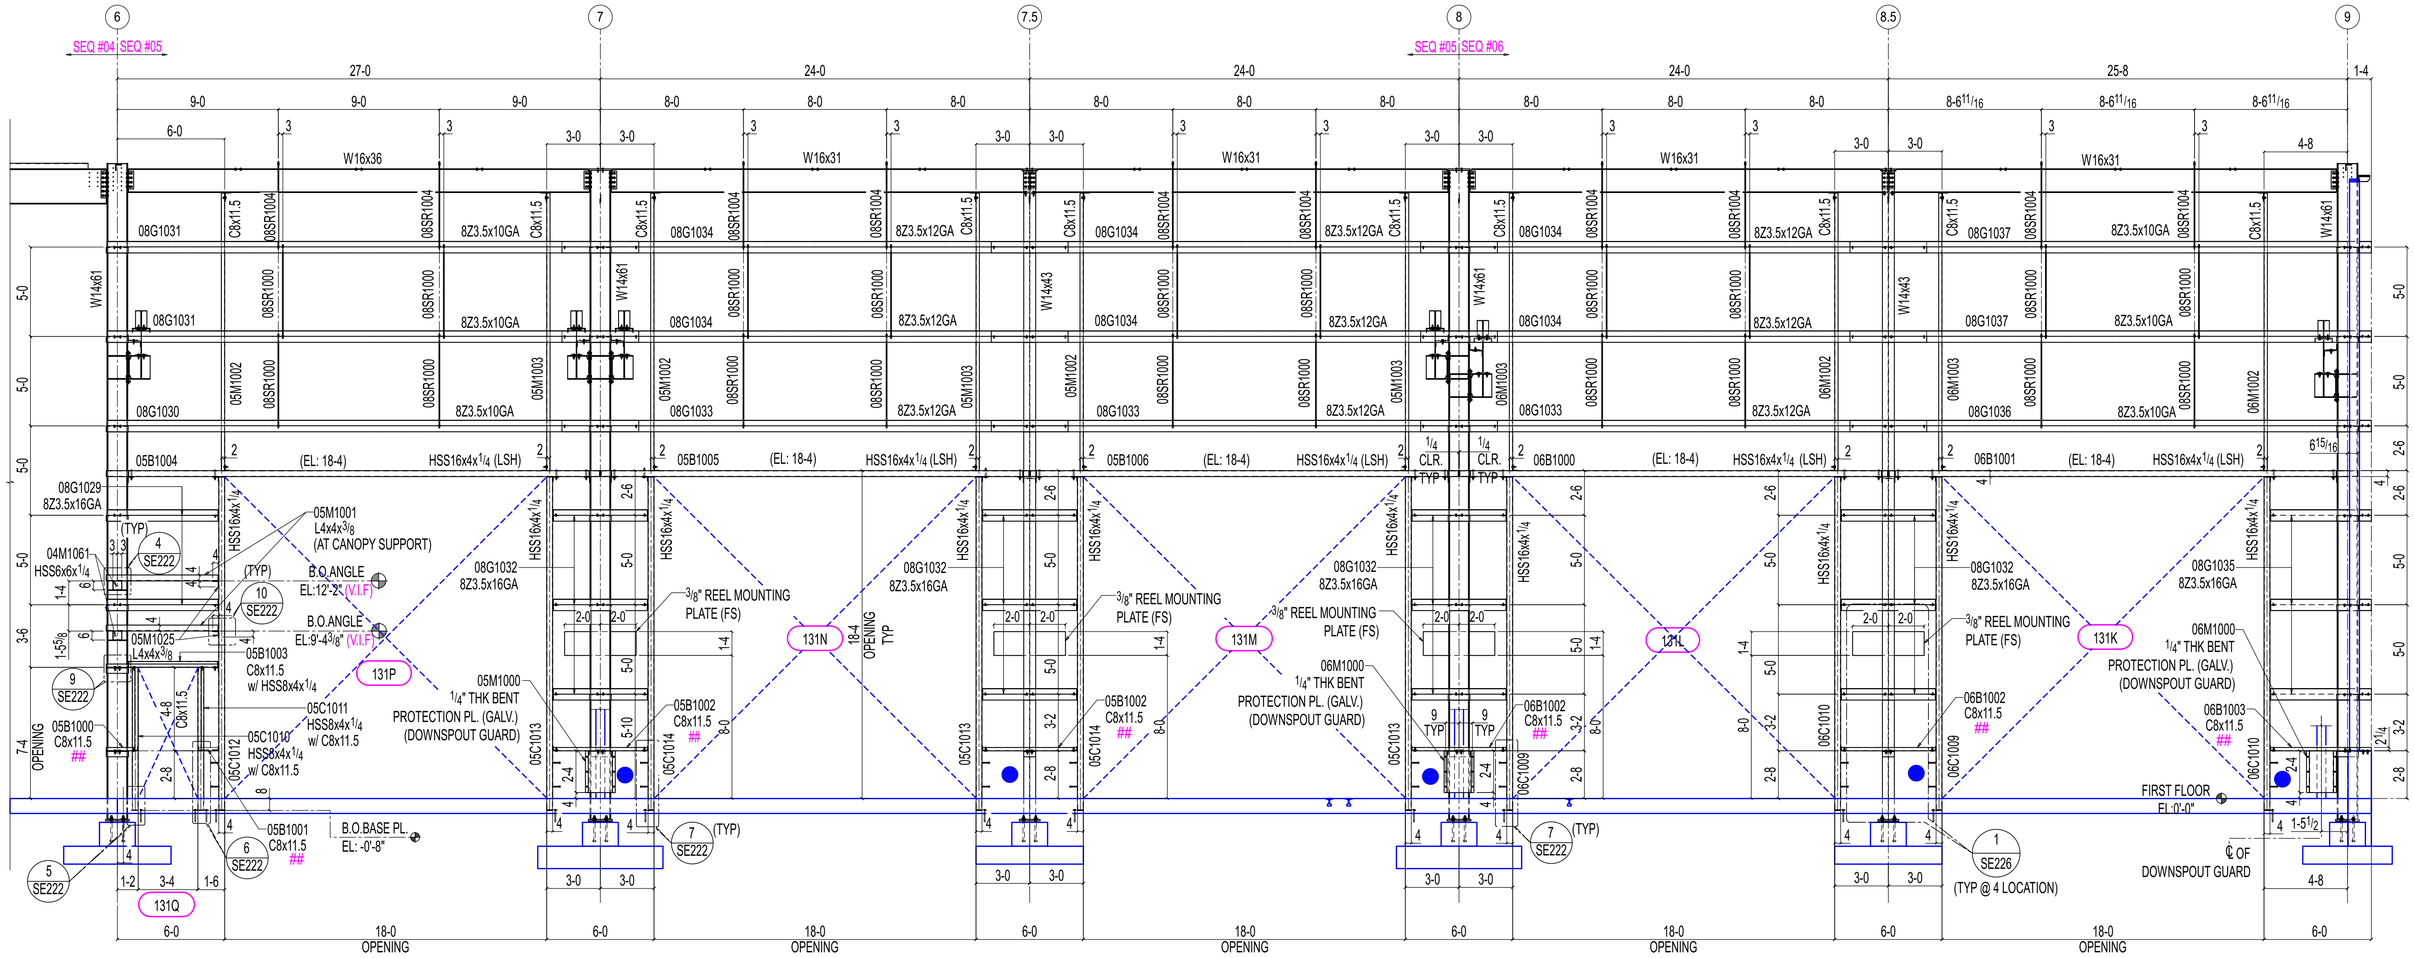

1 / SE205

ELEVATION VIEW- SOUTH

(REF: 1/S102,2/S200)

OTHER NOT SHOWN FOR CLARITY

NOTES:

1. ALL SHOWN ELEVATIONS ARE REFERENCED FROM FINISHED FLOOR ELEVATION (EL:0'-0") = DATUM EL:100'-0" (U.N.O).
2. REFER SHEET SE227 FOR TYPICAL SECTIONS.
3. ALL DOOR FRAME STEELS ARE GALVANIZED (U.N.O)
4. ALL SAG RODS SHALL BE 1/2"Ø ROD. (U.N.O).

##- ERECTOR NOTE:
ERECT THIS CHANNEL BEFORE CMU WALL CONSTRUCTION.

LEGEND

---CMU WALL

NOTE:
FIELD APPLIED PAINT AND THERMAL BREAK PAINT WILL BE BY OTHERS.

REVISIONS

REV#	DWN BY	DESCRIPTION	DATE
A	SRP	ISSUED FOR APPROVAL	Jun 11 2025
0	GSV	ISSUED FOR CONSTRUCTION	Sep 5 2025

THE INFORMATION NOTED HEREON THIS DRAWING IS THE PROPERTY OF STEEL FAB ENTERPRISES, INC. AND SHALL NOTED BE USED WITHOUT WRITTEN CONSENT.

STEEL FAB
ENTERPRISES, LLC
MISCELLANEOUS METALS FABRICATOR AND ERECTORS
623 BAUMGARDNER ROAD, LANCASTER, PA 17603
TEL. (717)464-0330 FAX (717)464-9464
WWW.STEELFABENTERPRISES.COM

AISC CERTIFIED FABRICATOR AND ERECTOR

PROJECT OWNER : CK CAPITAL, LLC

PROJECT DESCRIPTION : CLEVELAND BROTHERS-MILESBURG

PROJECT ADDRESS : 1025N. EAGLE VALLEY ROAD, HOWARD, PA 16841

CONTRACTOR : KINSLEY CONSTRUCTION, INC.

DRAWN BY : BAS	DATE : 05-20-25	PROJ. NO. : 25012	REV # 0
CHECKED BY : SRP	DATE : 05-20-25	DWG NO. : SE205	

DWG DESCRIPTION : ELEVATION VIEW