APPROVER,
PLEASE CONFIRM THE ORIENTATION OF THE CLOUDED COLUMNS. THE ARCHITECTURAL DRAWINGS SHOW THE COLUMN WEB ALIGNED PARALLEL TO GRIDS 7 & 8, WHILE THE STRUCTURAL DRAWINGS INDICATE THE WEB IS PARALLEL TO GRID A. ACCORDINGLY, WE HAVE PROCEEDED WITH THE COLUMN WEB ORIENTATION PARALLEL TO GRID A, AS PER THE STRUCTURAL DRAWINGS. PLEASE CONFIRM IF THIS OK TO PROCEED?

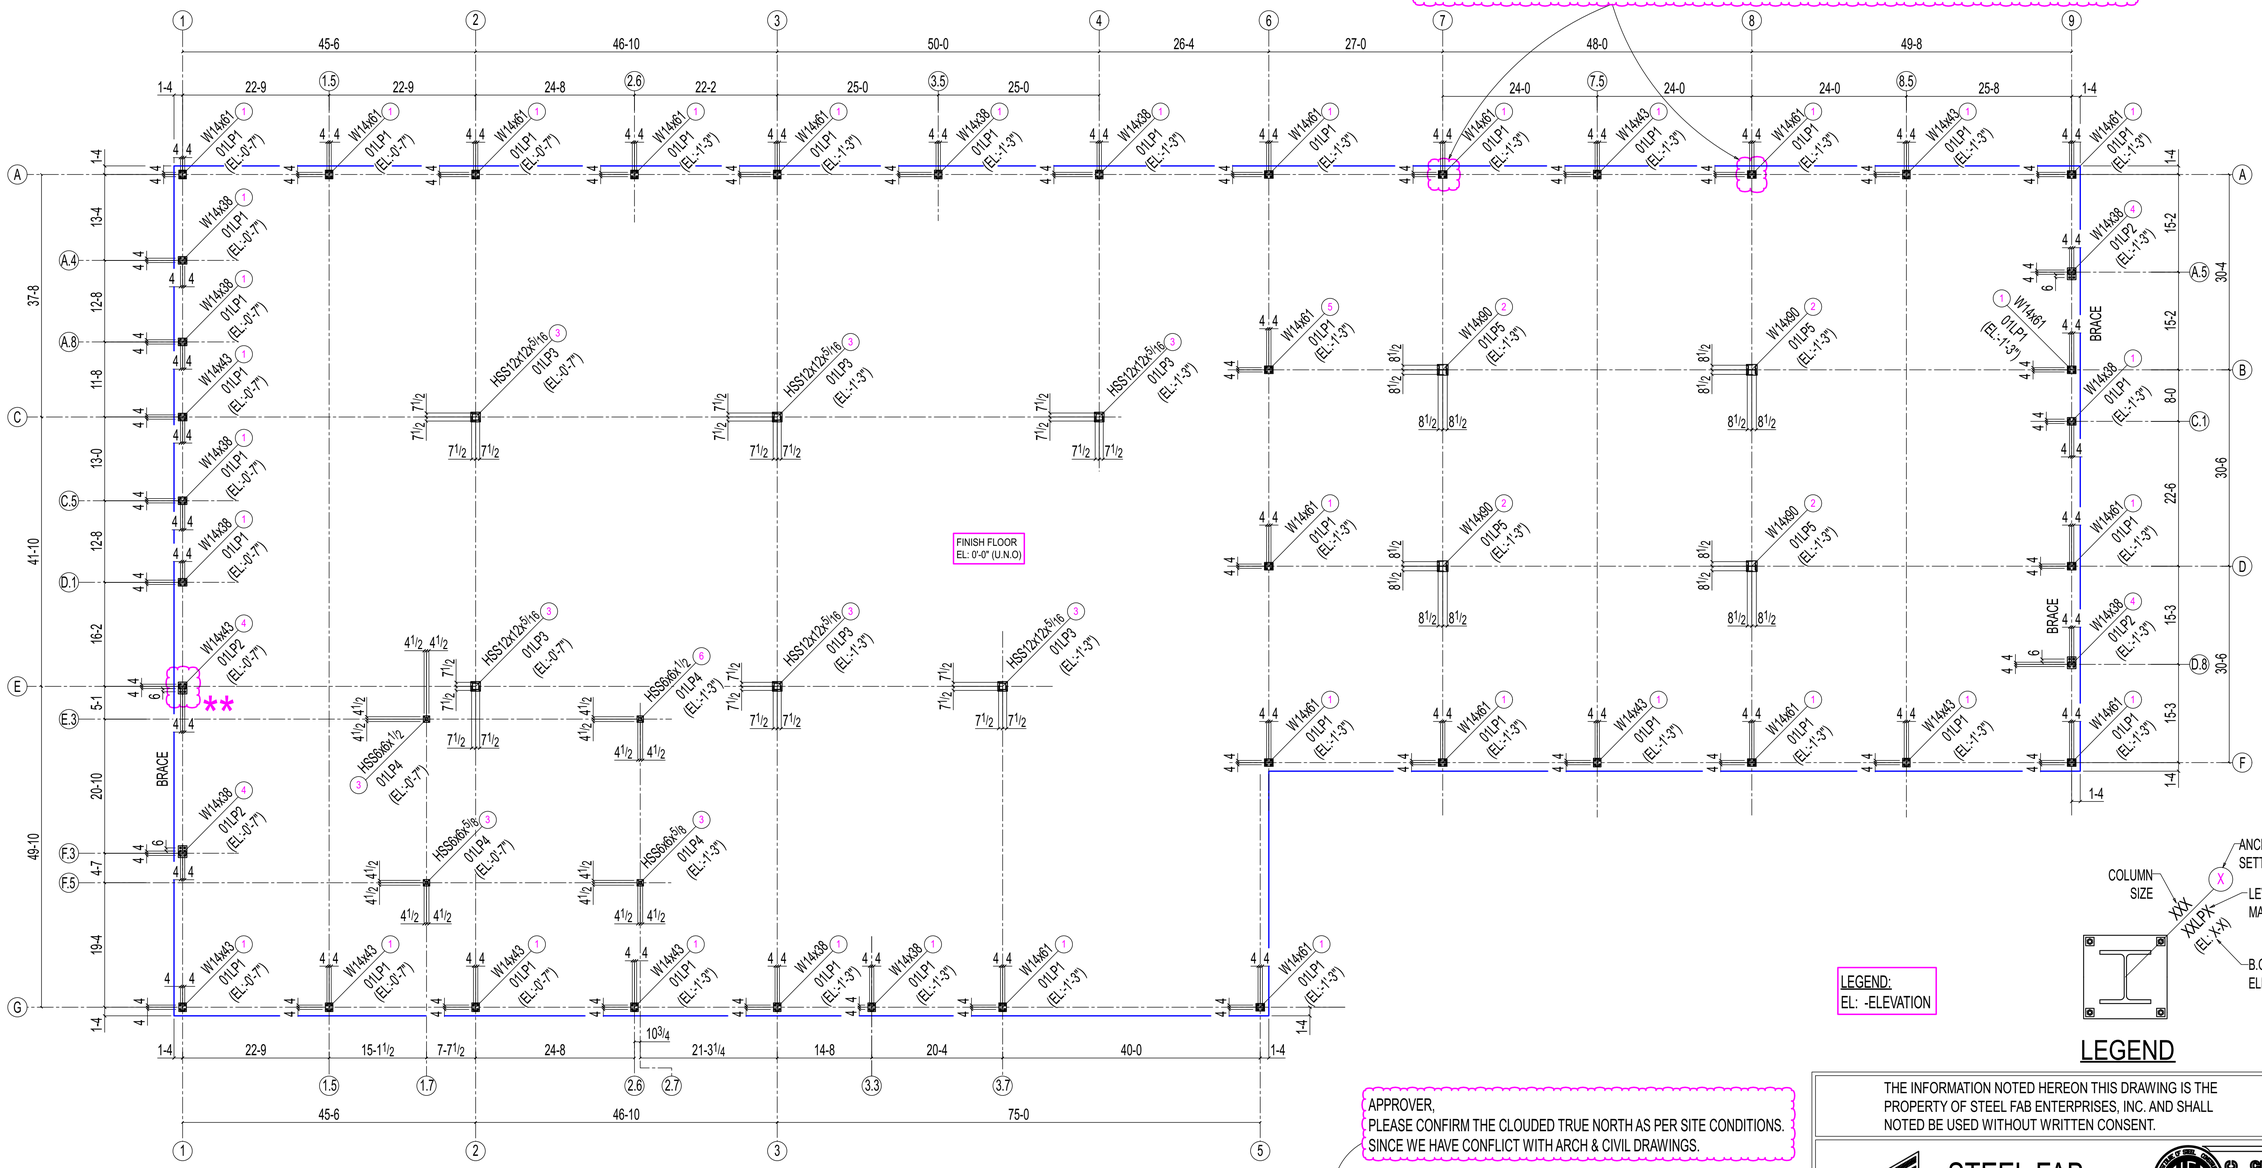

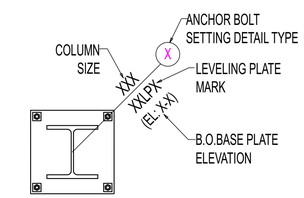

LEGEND

LEGEND:
EL: -ELEVATION

APPROVER,
PLEASE CONFIRM THE CLOUDED TRUE NORTH AS PER SITE CONDITIONS. SINCE WE HAVE CONFLICT WITH ARCH & CIVIL DRAWINGS.

TRUE NORTH PROJECT NORTH

1 / AB01

ANCHOR BOLT SETTING PLAN

(REF: 1/S101,2/S101)

NOTES:
1.ELEVATIONS SHOWN IN (+/-) ARE TO THE BOTTOM OF BASE PLATE /TOP OF LEVELING PLATE AND ARE REFERENCED FROM FINISHED FLOOR ELEVATION (EL:0'-0") = DATUM EL:100'-0" (U.N.O).
2.REFER SHEET AB02 FOR ANCHOR SETTING TYPES.

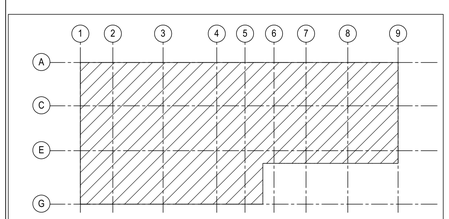

KEY PLAN

** -APPROVER,
WE NEED TO EXTEND OUR BASEPLATE FOR VERTICAL BRACE'S BOTTOM CONNECTION AS SHOWN IN SECTION 9 /201 & 4/AB02 AND DUE TO BASE PLATE EXTENTIONS,CONTRACTOR TO EXTEND THE PIER FOR 1-9 TO SOUTH FROM GRID 'E' IN LIEU OF EXTENTING 1-9" TO NORTH FROM GRID 'E' AS GRAPHICALLY SHOWN IN STRUCTURAL FOUNDATION PLAN S101.

PLEASE CONFIRM & COORDINATE WITH OTHER TRADES.

REVISIONS

REV#	DWN BY	DESCRIPTION	DATE
A	GSV	ISSUED FOR APPROVAL	May 27 2025

THE INFORMATION NOTED HEREON THIS DRAWING IS THE PROPERTY OF STEEL FAB ENTERPRISES, INC. AND SHALL NOT BE USED WITHOUT WRITTEN CONSENT.

STEEL FAB
ENTERPRISES, LLC
MISCELLANEOUS METALS FABRICATOR AND ERECTORS
623 BAUMGARDNER ROAD, LANCASTER, PA 17603
TEL. (717)464-0330 FAX (717)464-9464
WWW.STEELFABENTERPRISES.COM

AISC CERTIFIED FABRICATOR AND ERECTOR

PROJECT OWNER : CK CAPITAL, LLC
PROJECT DESCRIPTION : CLEVELAND BROTHERS-MILESBURG
PROJECT ADDRESS : 1025N. EAGLE VALLEY ROAD, HOWARD, PA 16841
CONTRACTOR : KINSLEY CONSTRUCTION, INC.

DRAWN BY : BAS	DATE : 5-20-25	PROJ. NO. : 25012	REV # A
CHECKED BY : SRP	DATE : 5-20-25	DWG NO. : AB01	
DWG DESCRIPTION : ANCHOR BOLT SETTING PLAN			