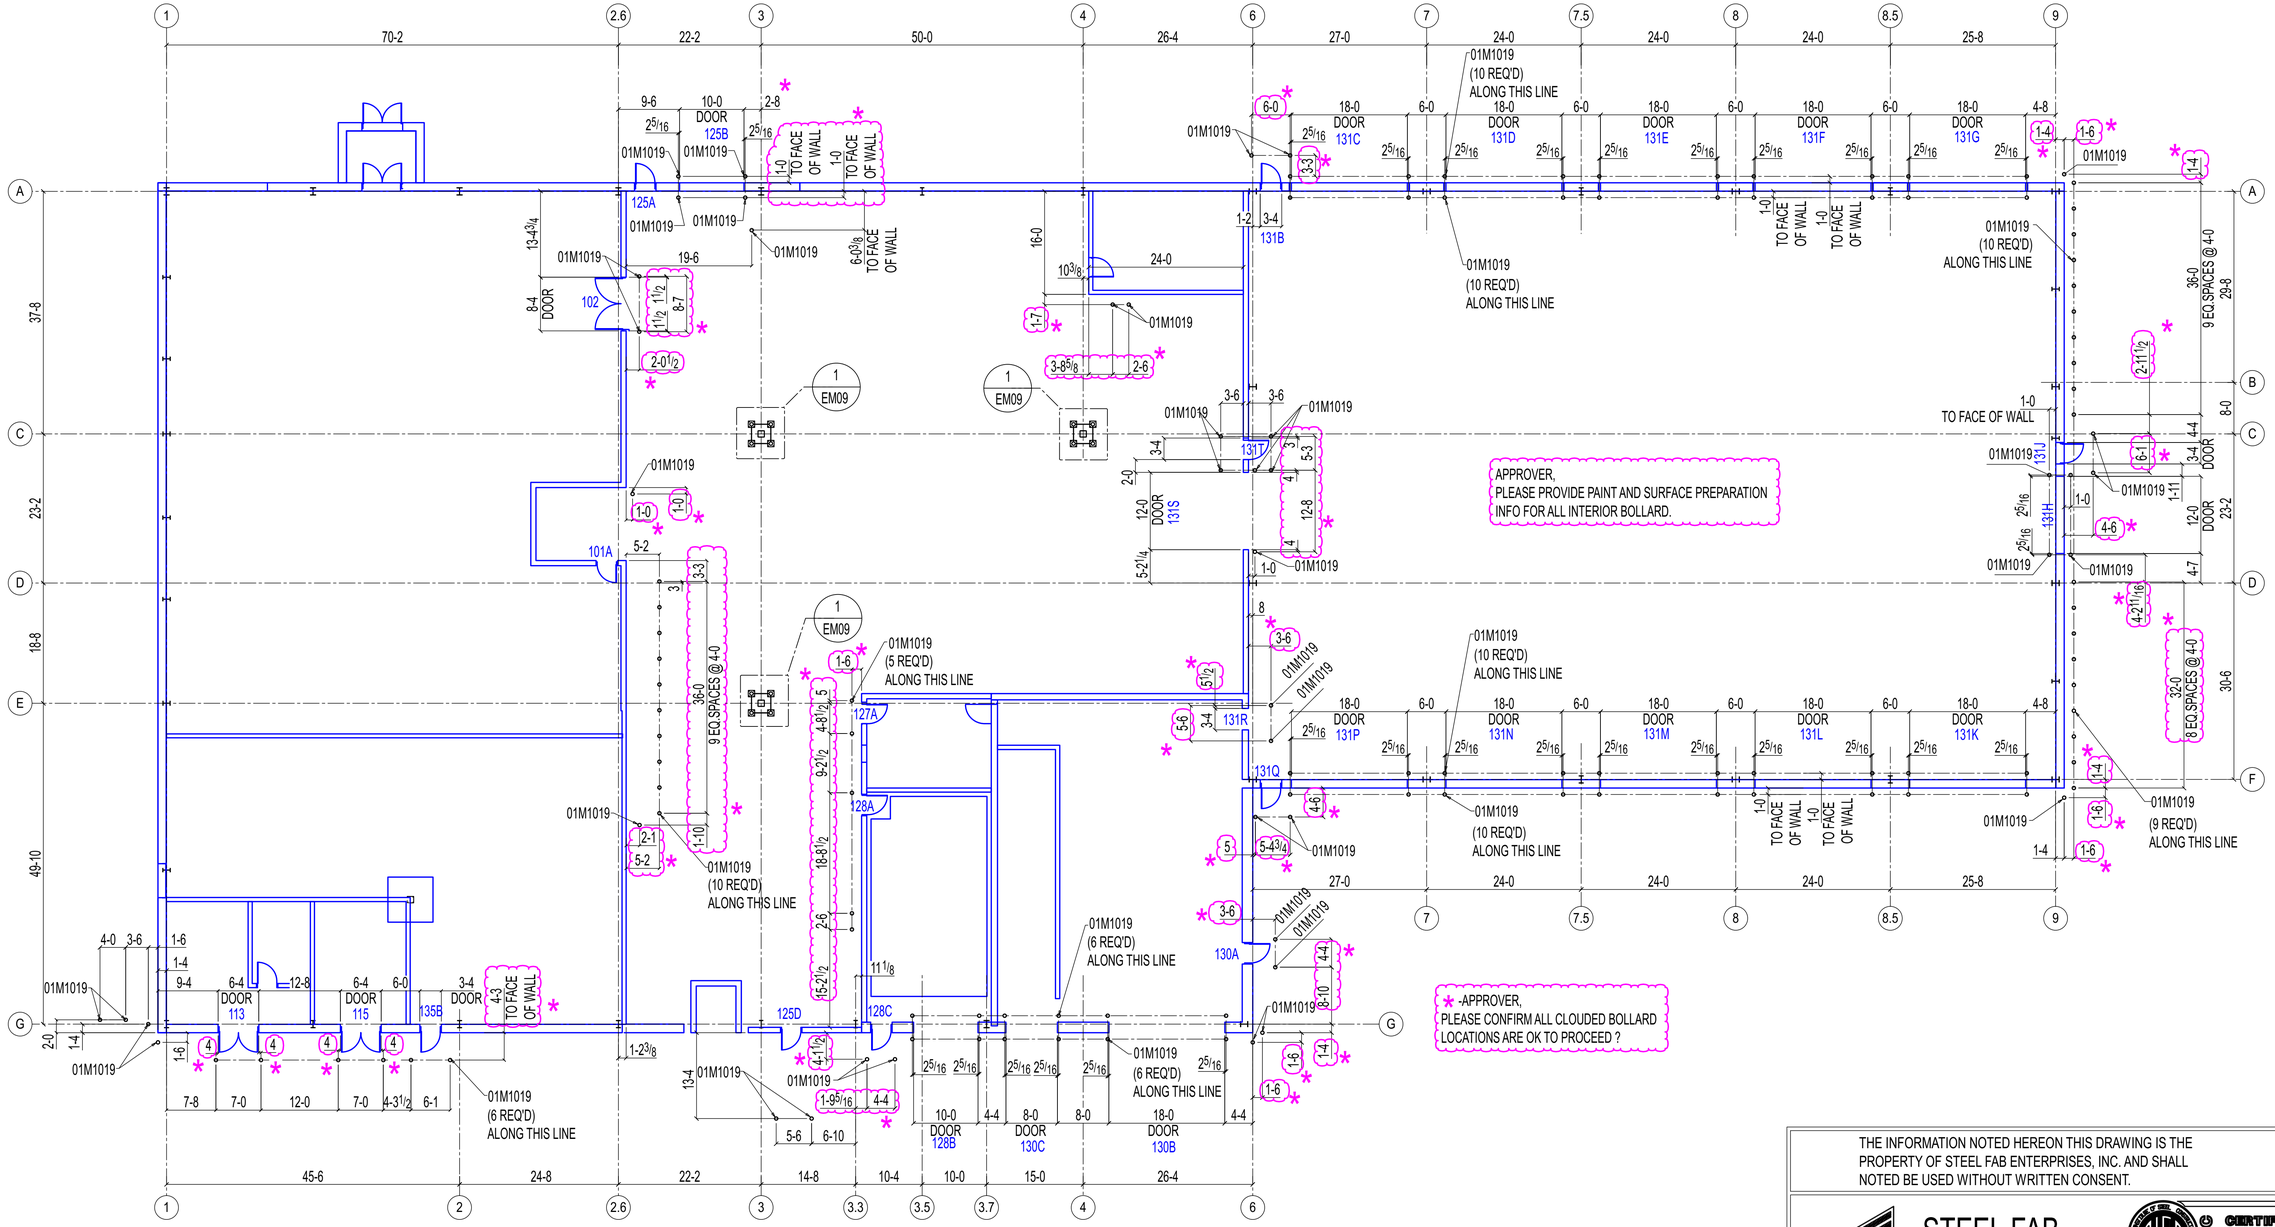

1
EM08

BOLLARD FRAMING PLAN

(REF: 1/A101)

TRUE NORTH PROJECT NORTH

NOTE
1. REFERENCED FROM THE FINISHED FLOOR EL: [0'-0"] = DATUM EL: 100'-0" (U.N.O).
2. ALL BOLLARDS ARE PIPE 6 SCH80 U.N.O.
3. ALL DIMENSIONS ARE CENTER LINE OF BOLLARD. (U.N.O)

APPROVER,
PLEASE CONFIRM THE PAINT & SURFACE
PREPARATION FOR ALL EXTERIOR BOLLARDS.

APPROVER,
PLEASE REVIEW AND CONFIRM ANY ADDITIONAL
BOLLARDS ARE REQUIRED IN ANY OTHER LOCATIONS.

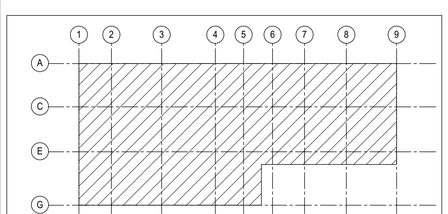

KEY PLAN

REVISIONS

REV#	DWN BY	DESCRIPTION	DATE
A	GSV	ISSUED FOR APPROVAL	May 27 2025

THE INFORMATION NOTED HEREON THIS DRAWING IS THE PROPERTY OF STEEL FAB ENTERPRISES, INC. AND SHALL NOTED BE USED WITHOUT WRITTEN CONSENT.

STEEL FAB
ENTERPRISES, LLC
MISCELLANEOUS METALS FABRICATOR AND ERECTORS
623 BAUMGARDNER ROAD, LANCASTER, PA 17603
TEL. (717)464-0330 FAX (717)464-9464
WWW.STEELFABENTERPRISES.COM

AISC CERTIFIED FABRICATOR AND ERECTOR

PROJECT OWNER : CK CAPITAL, LLC
PROJECT DESCRIPTION : CLEVELAND BROTHERS-MILESBURG
PROJECT ADDRESS : 1025N. EAGLE VALLEY ROAD, HOWARD, PA 16841
CONTRACTOR : KINSLEY CONSTRUCTION, INC.

DRAWN BY : BAS	DATE : 5-20-25	PROJ. NO. :	25012	REV # A
CHECKED BY : SRP	DATE : 5-20-25	DWG NO. :	EM08	

DWG DESCRIPTION : BOLLARD PLAN