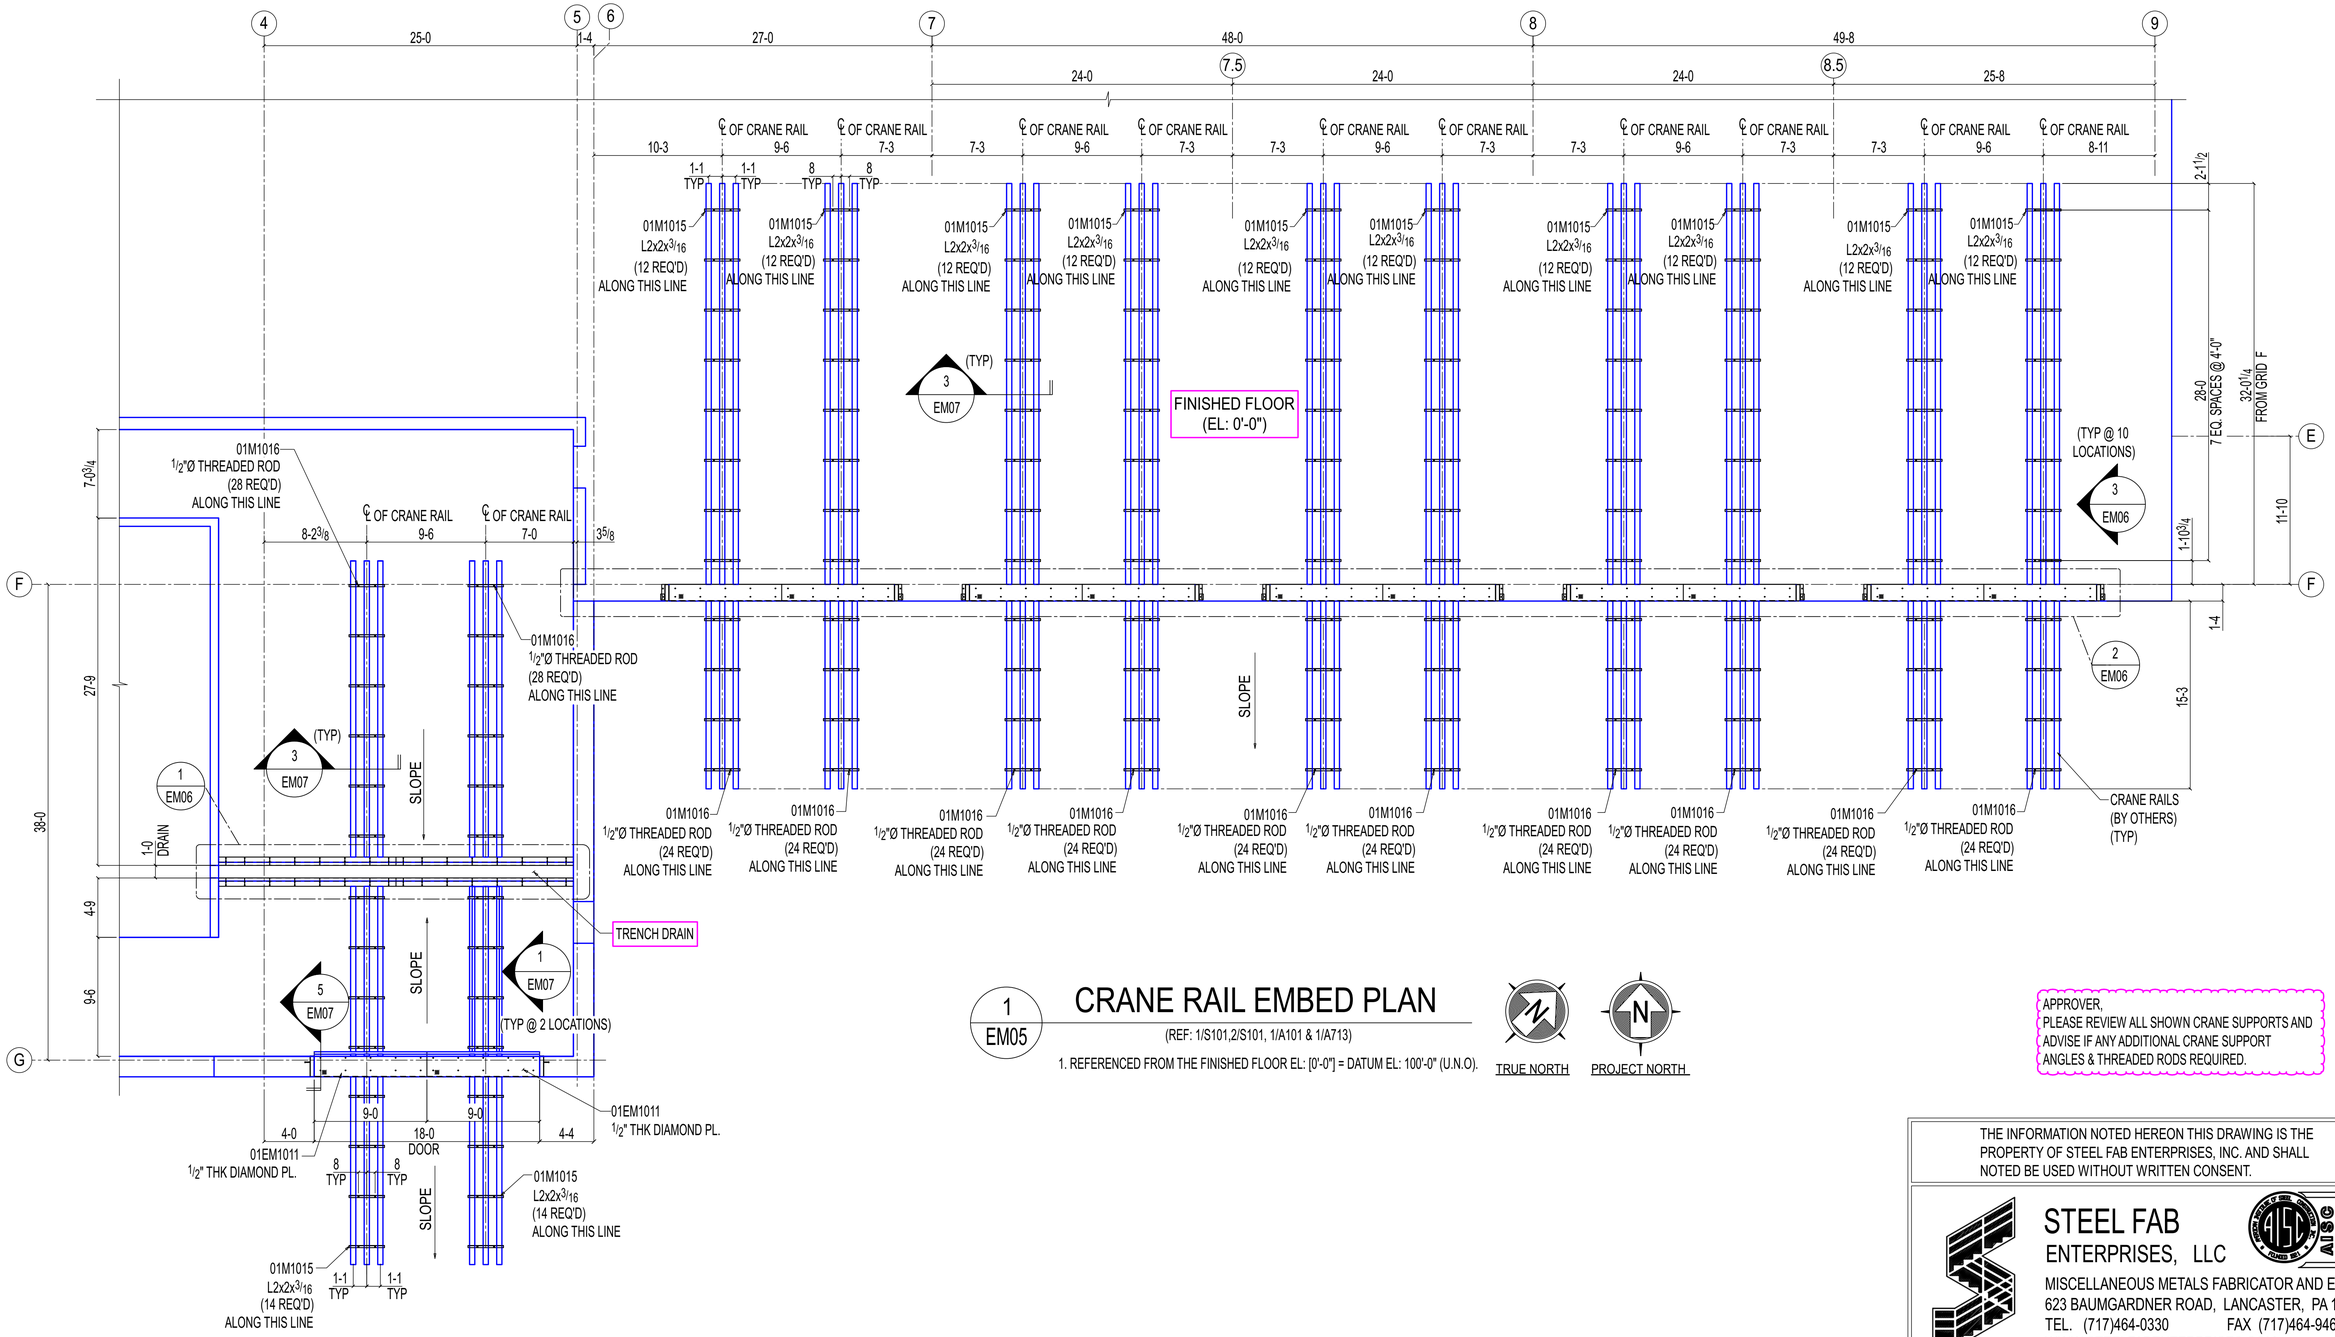

1
EM05

CRANE RAIL EMBED PLAN

(REF: 1/S101,2/S101, 1/A101 & 1/A713)

1. REFERENCED FROM THE FINISHED FLOOR EL: [0'-0"] = DATUM EL: 100'-0" (U.N.O).

TRUE NORTH

PROJECT NORTH

APPROVER,
PLEASE REVIEW ALL SHOWN CRANE SUPPORTS AND ADVISE IF ANY ADDITIONAL CRANE SUPPORT ANGLES & THREADED RODS REQUIRED.

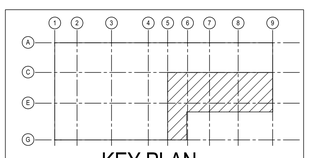

KEY PLAN

REVISIONS

REV#	DWN BY	DESCRIPTION	DATE
A	GSV	ISSUED FOR APPROVAL	May 27 2025

THE INFORMATION NOTED HEREON THIS DRAWING IS THE PROPERTY OF STEEL FAB ENTERPRISES, INC. AND SHALL NOT BE USED WITHOUT WRITTEN CONSENT.

STEEL FAB
ENTERPRISES, LLC
MISCELLANEOUS METALS FABRICATOR AND ERECTORS
623 BAUMGARDNER ROAD, LANCASTER, PA 17603
TEL. (717)464-0330 FAX (717)464-9464
WWW.STEELFABENTERPRISES.COM

AISC CERTIFIED FABRICATOR AND ERECTOR

PROJECT OWNER : CK CAPITAL, LLC

PROJECT DESCRIPTION : CLEVELAND BROTHERS-MILESBURG

PROJECT ADDRESS : 1025N. EAGLE VALLEY ROAD, HOWARD, PA 16841

CONTRACTOR : KINSLEY CONSTRUCTION, INC.

DRAWN BY : BAS	DATE : 5-20-25	PROJ. NO. : 25012	REV # A
CHECKED BY : SRP	DATE : 5-20-25	DWG NO. : EM05	

DWG DESCRIPTION : CRANE RAIL EMBED PLAN