



BILL OF MATERIAL							
LINE #	QTY	PC	MARK	DESCRIPTION	LENGTH	WEIGHT	ADVANCE
	TOTAL		MARK			TOTAL	MILL #
ONE	F-08.00C1	COLUMN				390	
1	F-08.00C1	HSS6x6x3/8		S/E A500C	12 9	350	
1	bp1002	PL1/4x8		A36	1 2	40	
ONE	F-08.00C2	COLUMN				329	
1	F-08.00C2	HSS6x6x3/8		S/E A500C	10 4	284	
1	p1964	PL1/4x7		A36	1 6	45	
2		FIELD BOLTS					
		3/4 Dia HILTI HAS V-36		(3/4" EMBED)	0 8		
		w/HILTI HY-200 EPOXY					
ONE	F-08.00C3	COLUMN				396	
1	F-08.00C3	HSS6x6x3/8		S/E A500C	13 0 1/4	359	
1	p3367	PL3/8x6 1/2		A36	1 6	21	
1	p230	PL3/8x6 1/2		A36	1 2	16	
2		FIELD BOLTS					
		3/4 Dia HILTI HAS V-36		(4" EMBED)	0 8		
		THREADED ROD					
		w/ HILTI HY-200 EPOXY					
2		1/2 Dia HILTI KWIK HUS-EZ		(3/4" EMBED)	0 4 1/2		
		SCREW ANCHOR					
ONE	F-08.00C4	COLUMN				354	
1	F-08.00C4	HSS6x6x3/8		A500C	9 10 1/2	271	
1	hss70	HSS4x4x3/16		A500C	1 6 3/4	23	
1	hss69	HSS4x4x3/16		A500C	1 1	16	
1	a155	L1 1/2x1x3/16		A36	0 5	1	
1	p404	PL3/8x6 1/2		A36	1 6	21	
1	p3367	PL3/8x6 1/2		A36	1 6	21	
1	p3632	PL1/4x4		A36	0 4	1	
2		FIELD BOLTS					
		3/4 Dia HILTI KWIK HUS-EZ		(3/4" EMBED)	0 4 1/2		
		SCREW ANCHOR					
ONE	F-08.00B1	BEAM				688	
1	F-08.00B1	HSS10x8x1/2		A500C	12 1 7/8	677	
2	p3657	PL1/4x8		A36	0 10	11	

Total weight : 2156

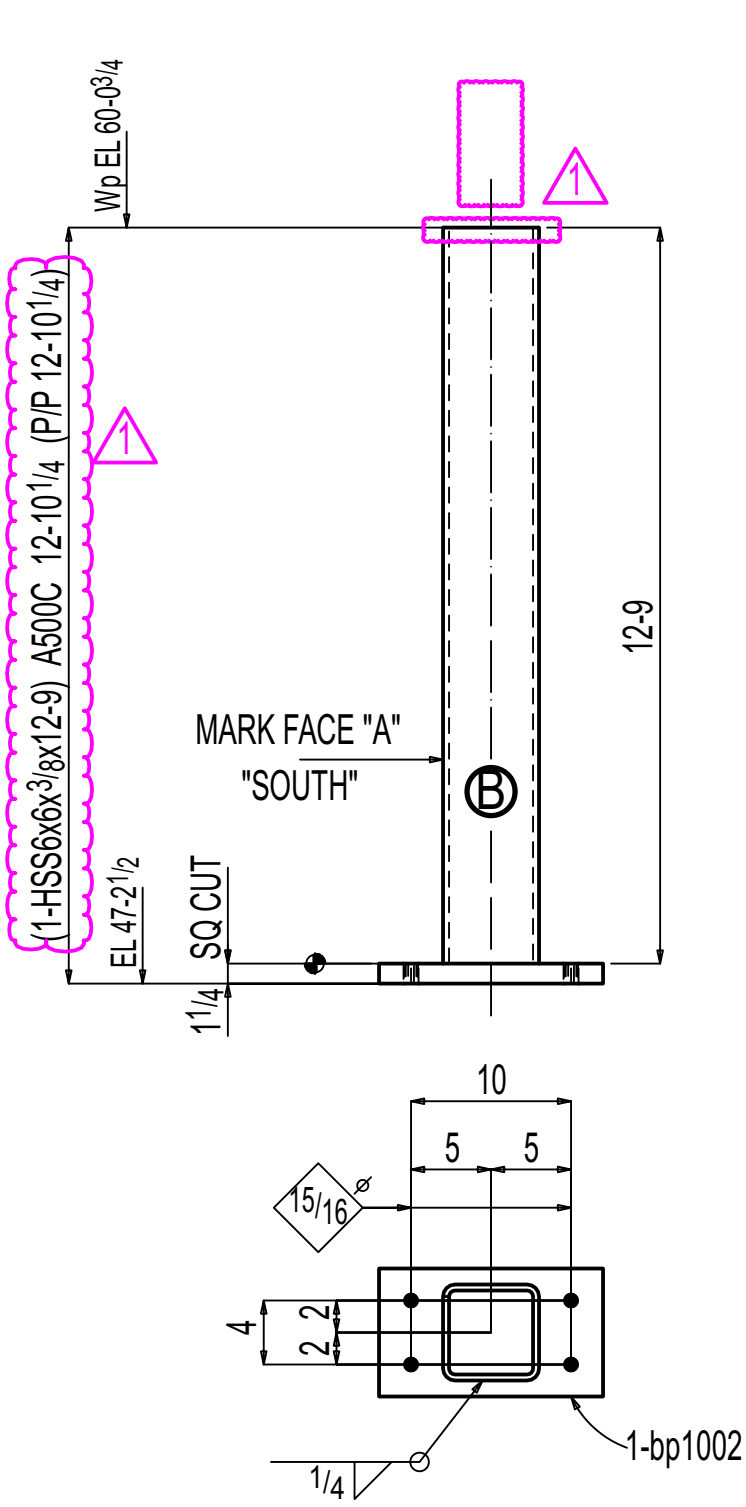


ONE COLUMN F-08.00C1

AT GRID:
EE & A

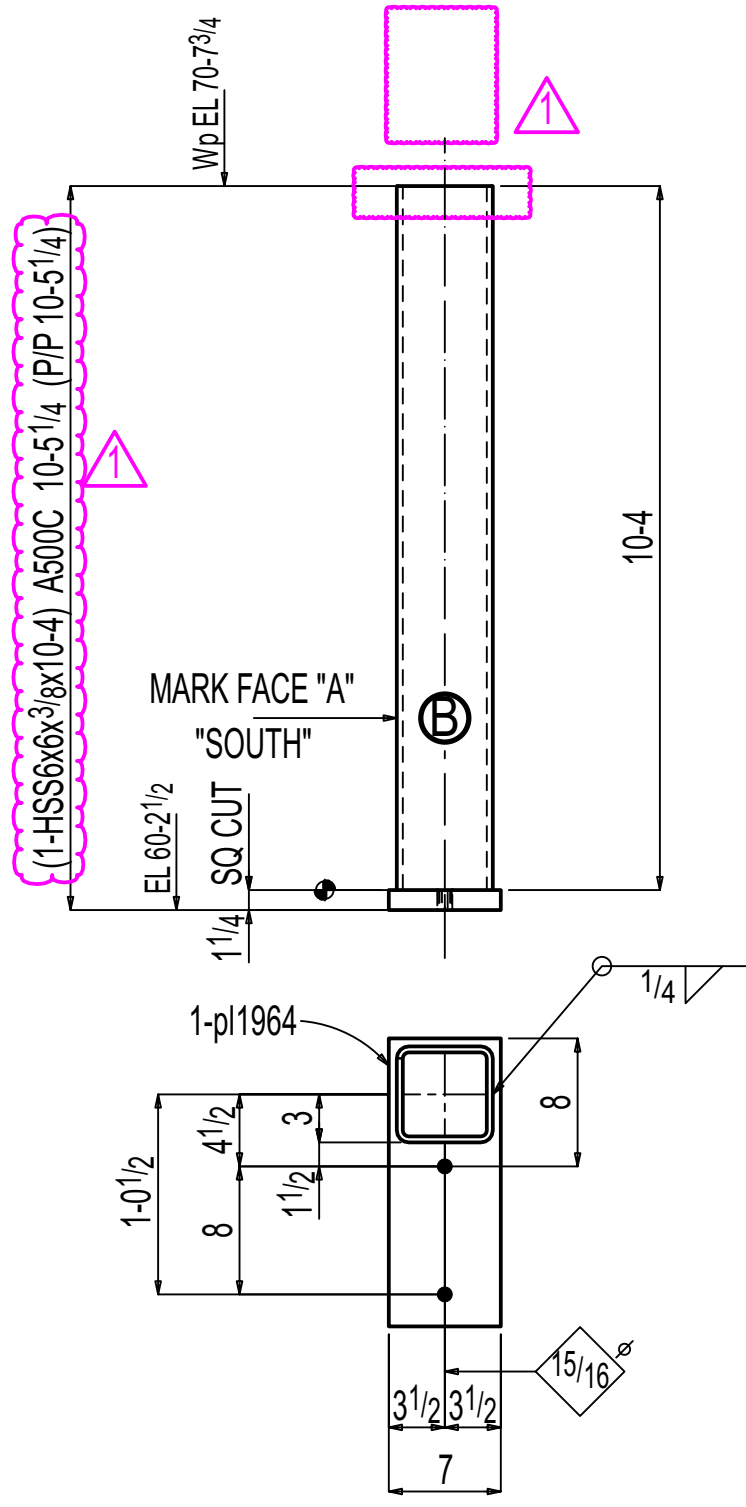



ONE COLUMN F-08.00C2

AT GRID:
EE & A

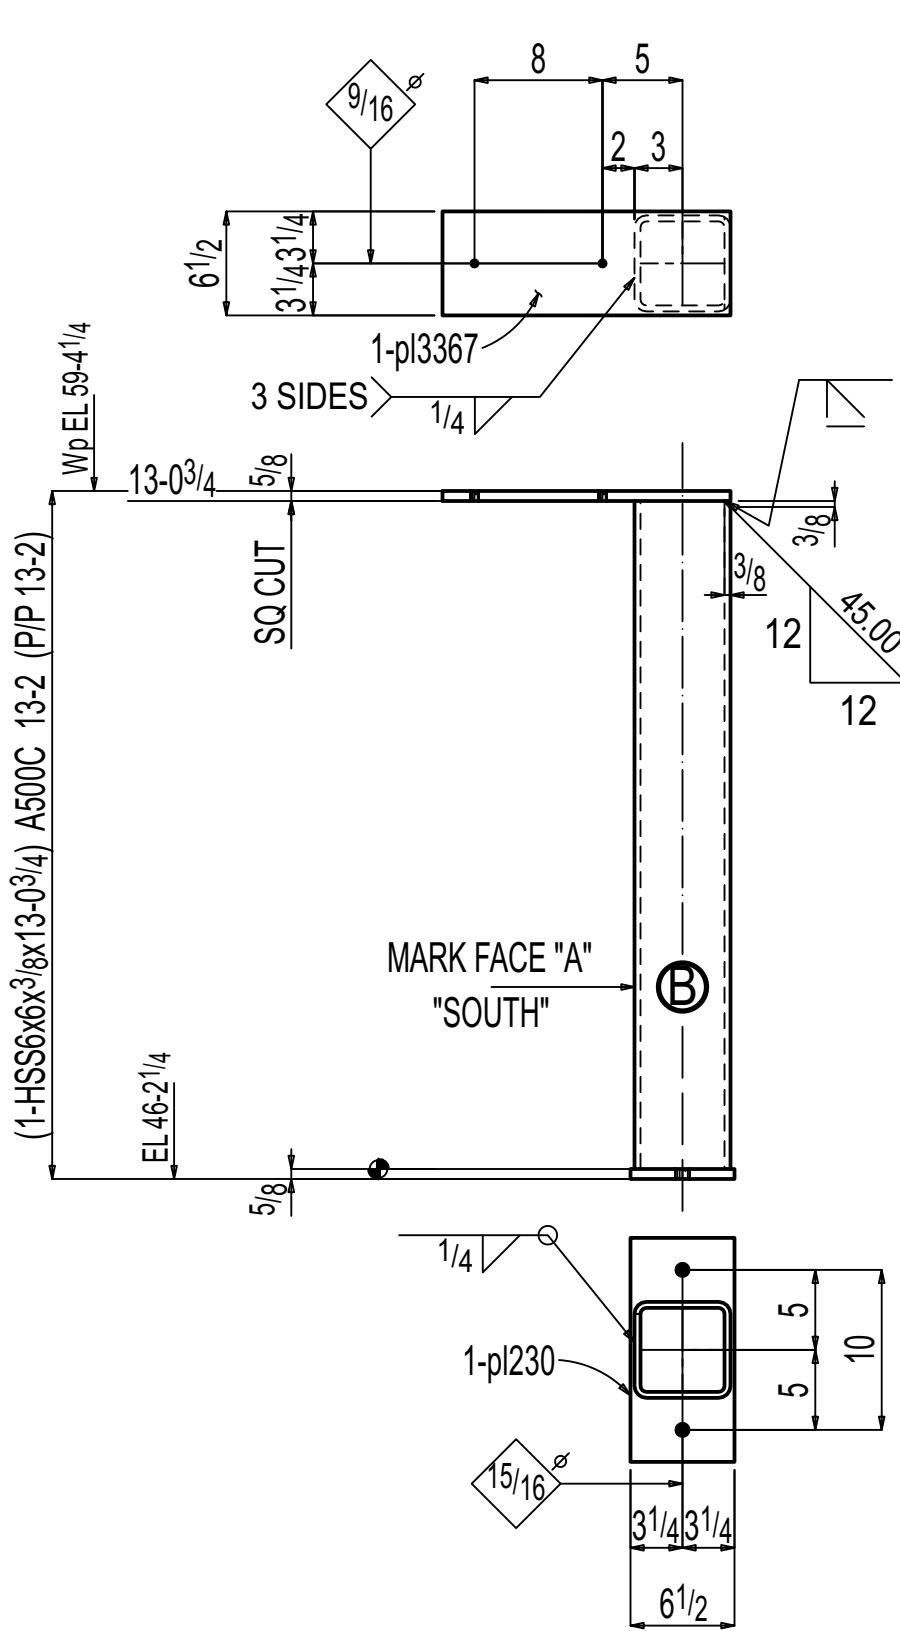


ONE COLUMN F-08.00C3

AT GRID:
AA & K

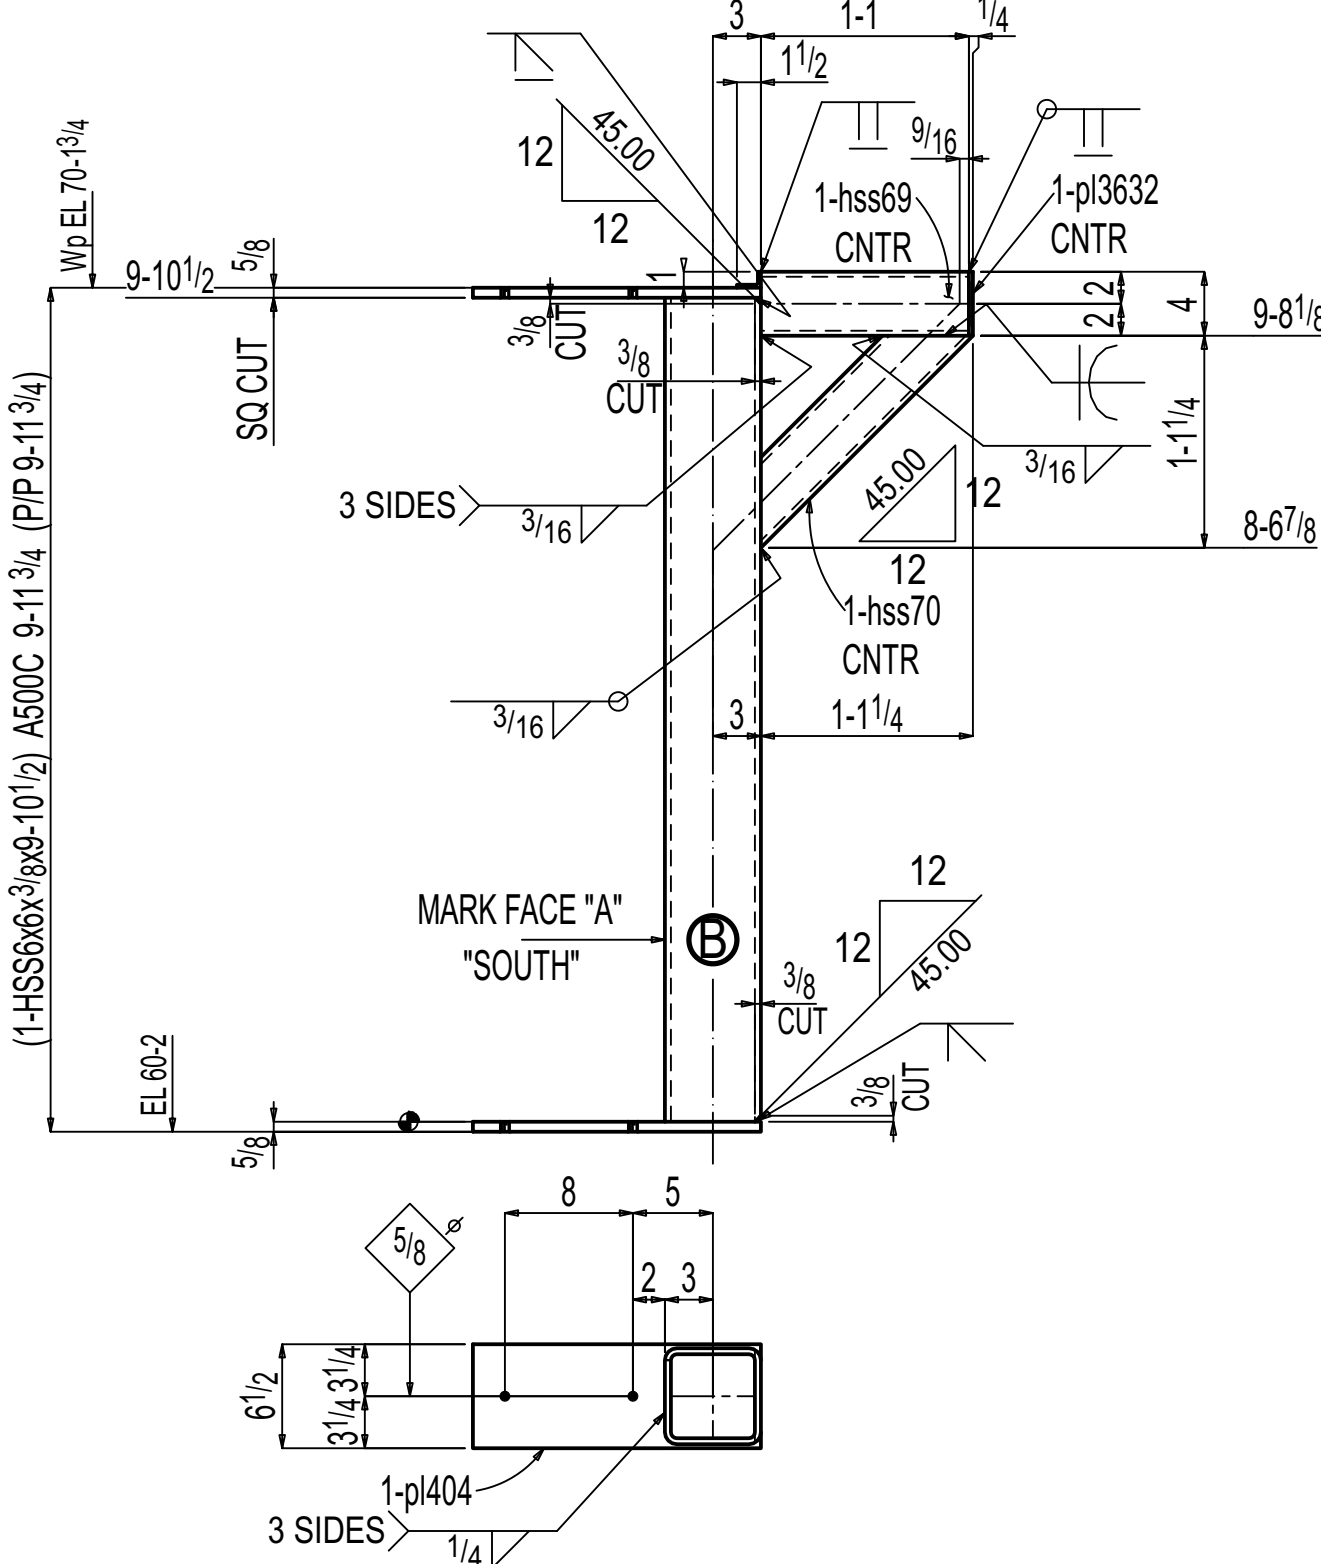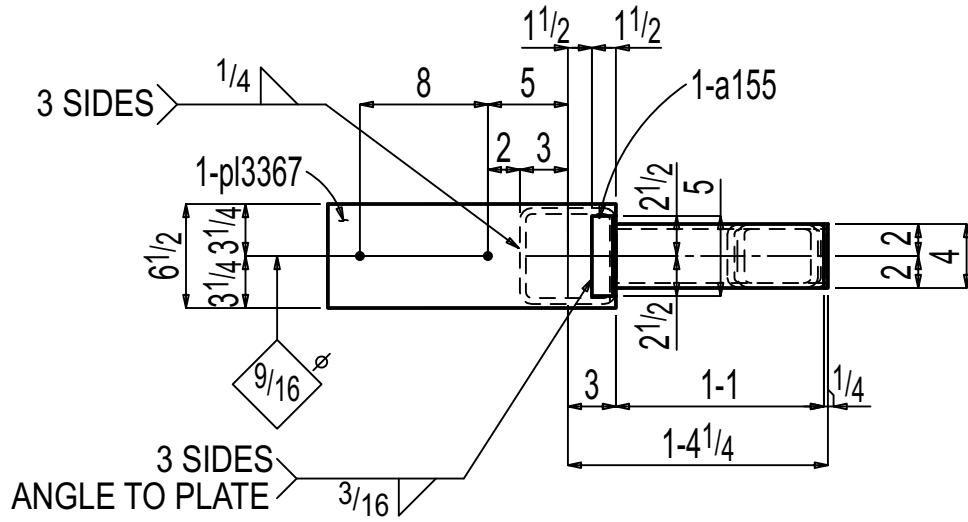

AT GRID:
AA & K

ONE COLUMN F-08.00C4

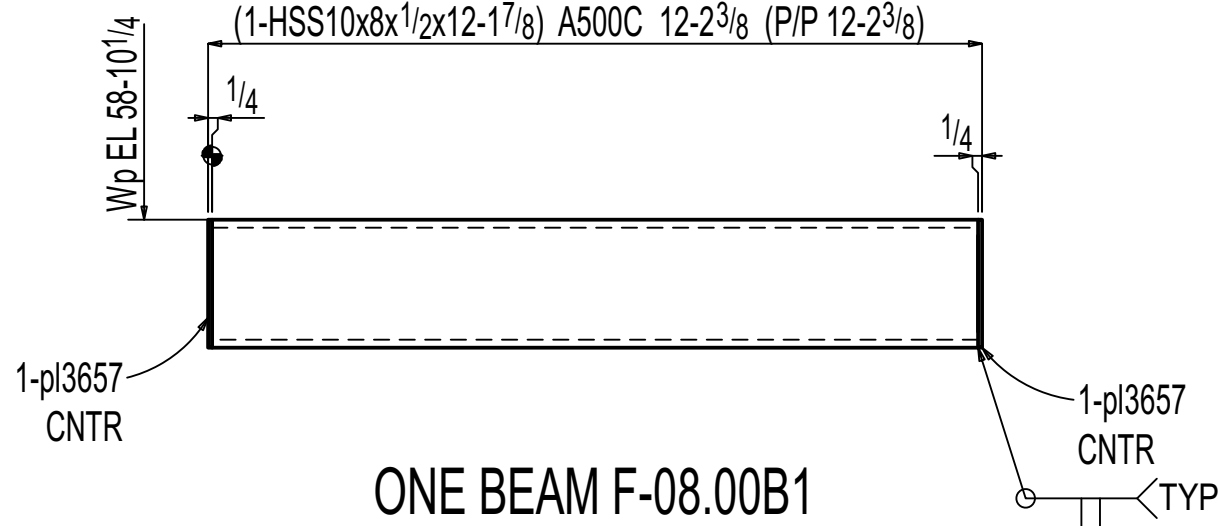

ONE BEAM F-08.00B1

PAINT :NO PAINT
PREPARATION :SSPC-SP3

General Notes			
*Structural steel shall conform to ASTM-A992.			
*Structural SQR/RND,tubing conform to ASTM A500 Grade C.			
*Pipe shall conform to ASTM A53, Grade B.			
*Channels, Angles and plates shall conform to A36.			
*All bolts shall be 3/4" High strength in accordance with ASTM A325 (UNO)			
*Welding Electrodes for Carbon steel :E70xx			
6	1	Revised as noted	11-11-2025
5	0	For Fabrication	11-03-2025
4	D	For Re-Approval	10-24-2025
3	C	For Re-Approval	09-19-2025
2	B	For Re-Approval	06-23-2025
1	A	For Approval	02-25-2025
# of Copies	Revision/ Issue	Destination	Date

IRON FABRICATION SERVICES, LLC.

3029 M. Street, NW, Suite 202
Washington, DC 20007
Tel: 202-800-5599
Fax: 202-478-0303

Project Name and Address
MARYLAND AVENUE
Location: **1250 MARYLAND AVENUE SW**
WASHINGTON, DC 20024

Contractor:
BALFOUR BEATTY

Approved for Fabrication by: Signature

Contract # **224009** Drawing # **F-08.00**

Contract Item: **COLUMN ,BEAM**

Ref:
SOW - 08: E-08.00 - E-08.04

Date **01/ 23/ 2025** Drawing Title: **COLUMN & BEAM DETAIL**
Scale **VARIES**