

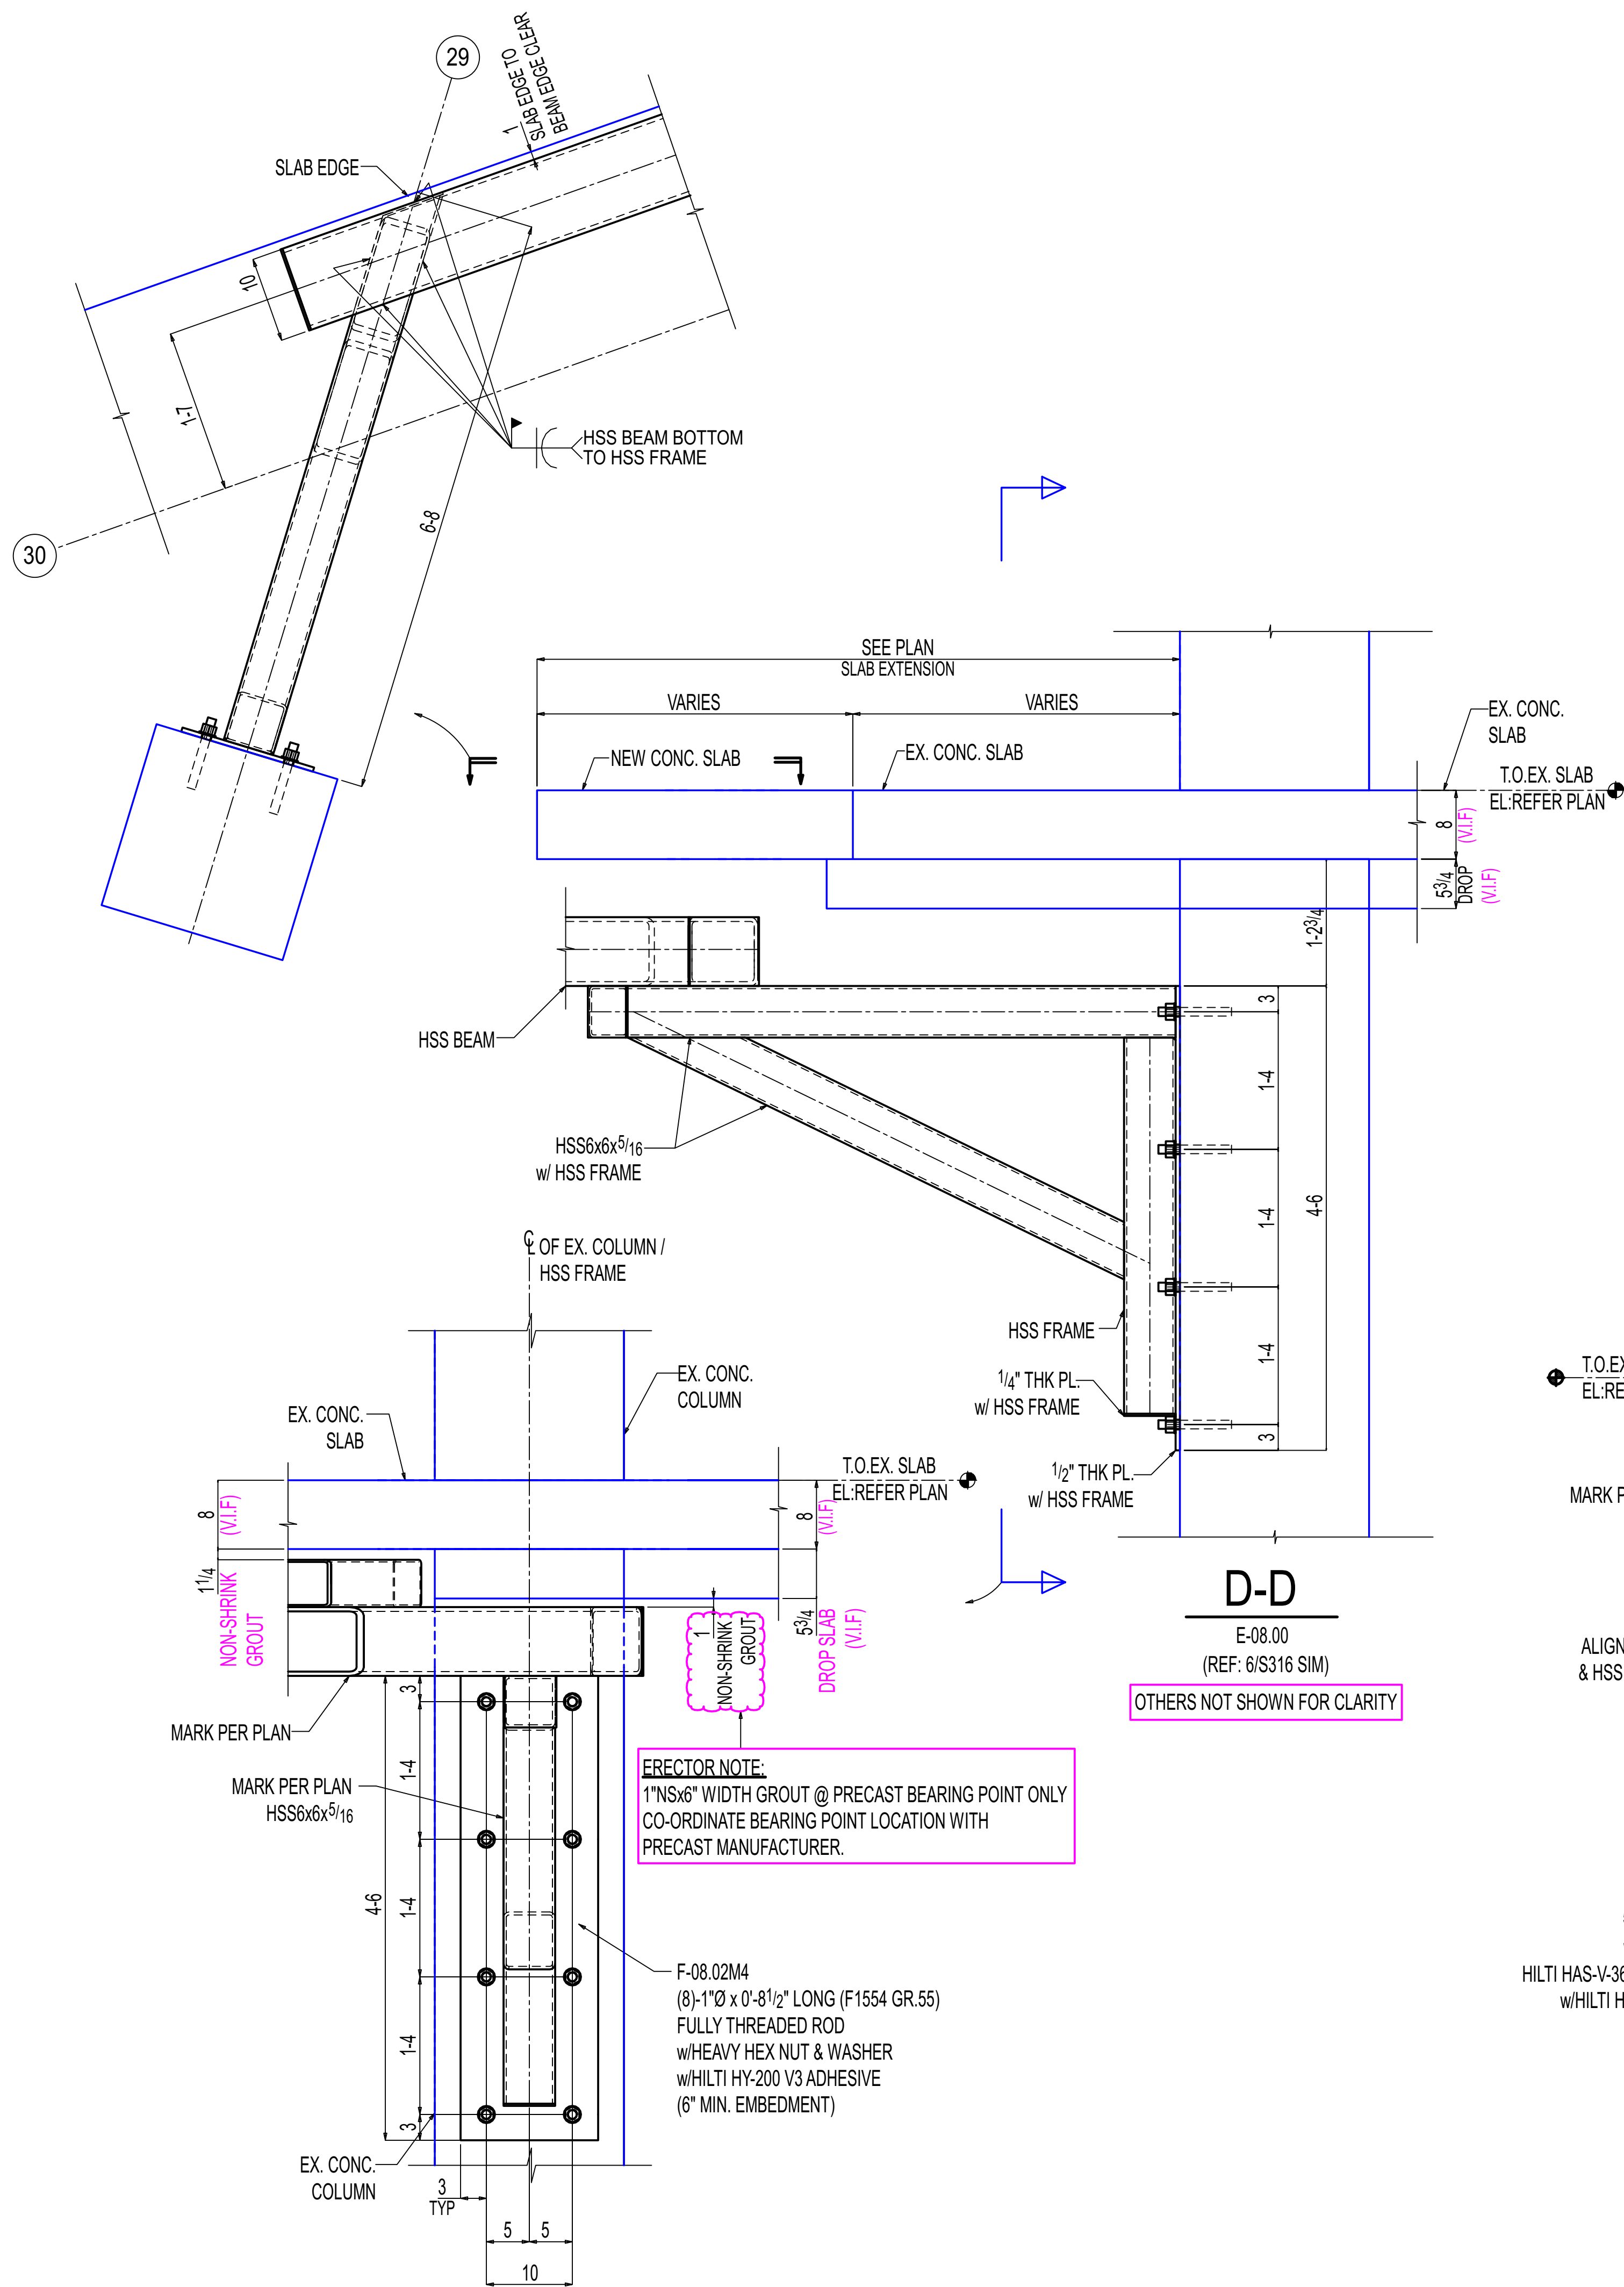


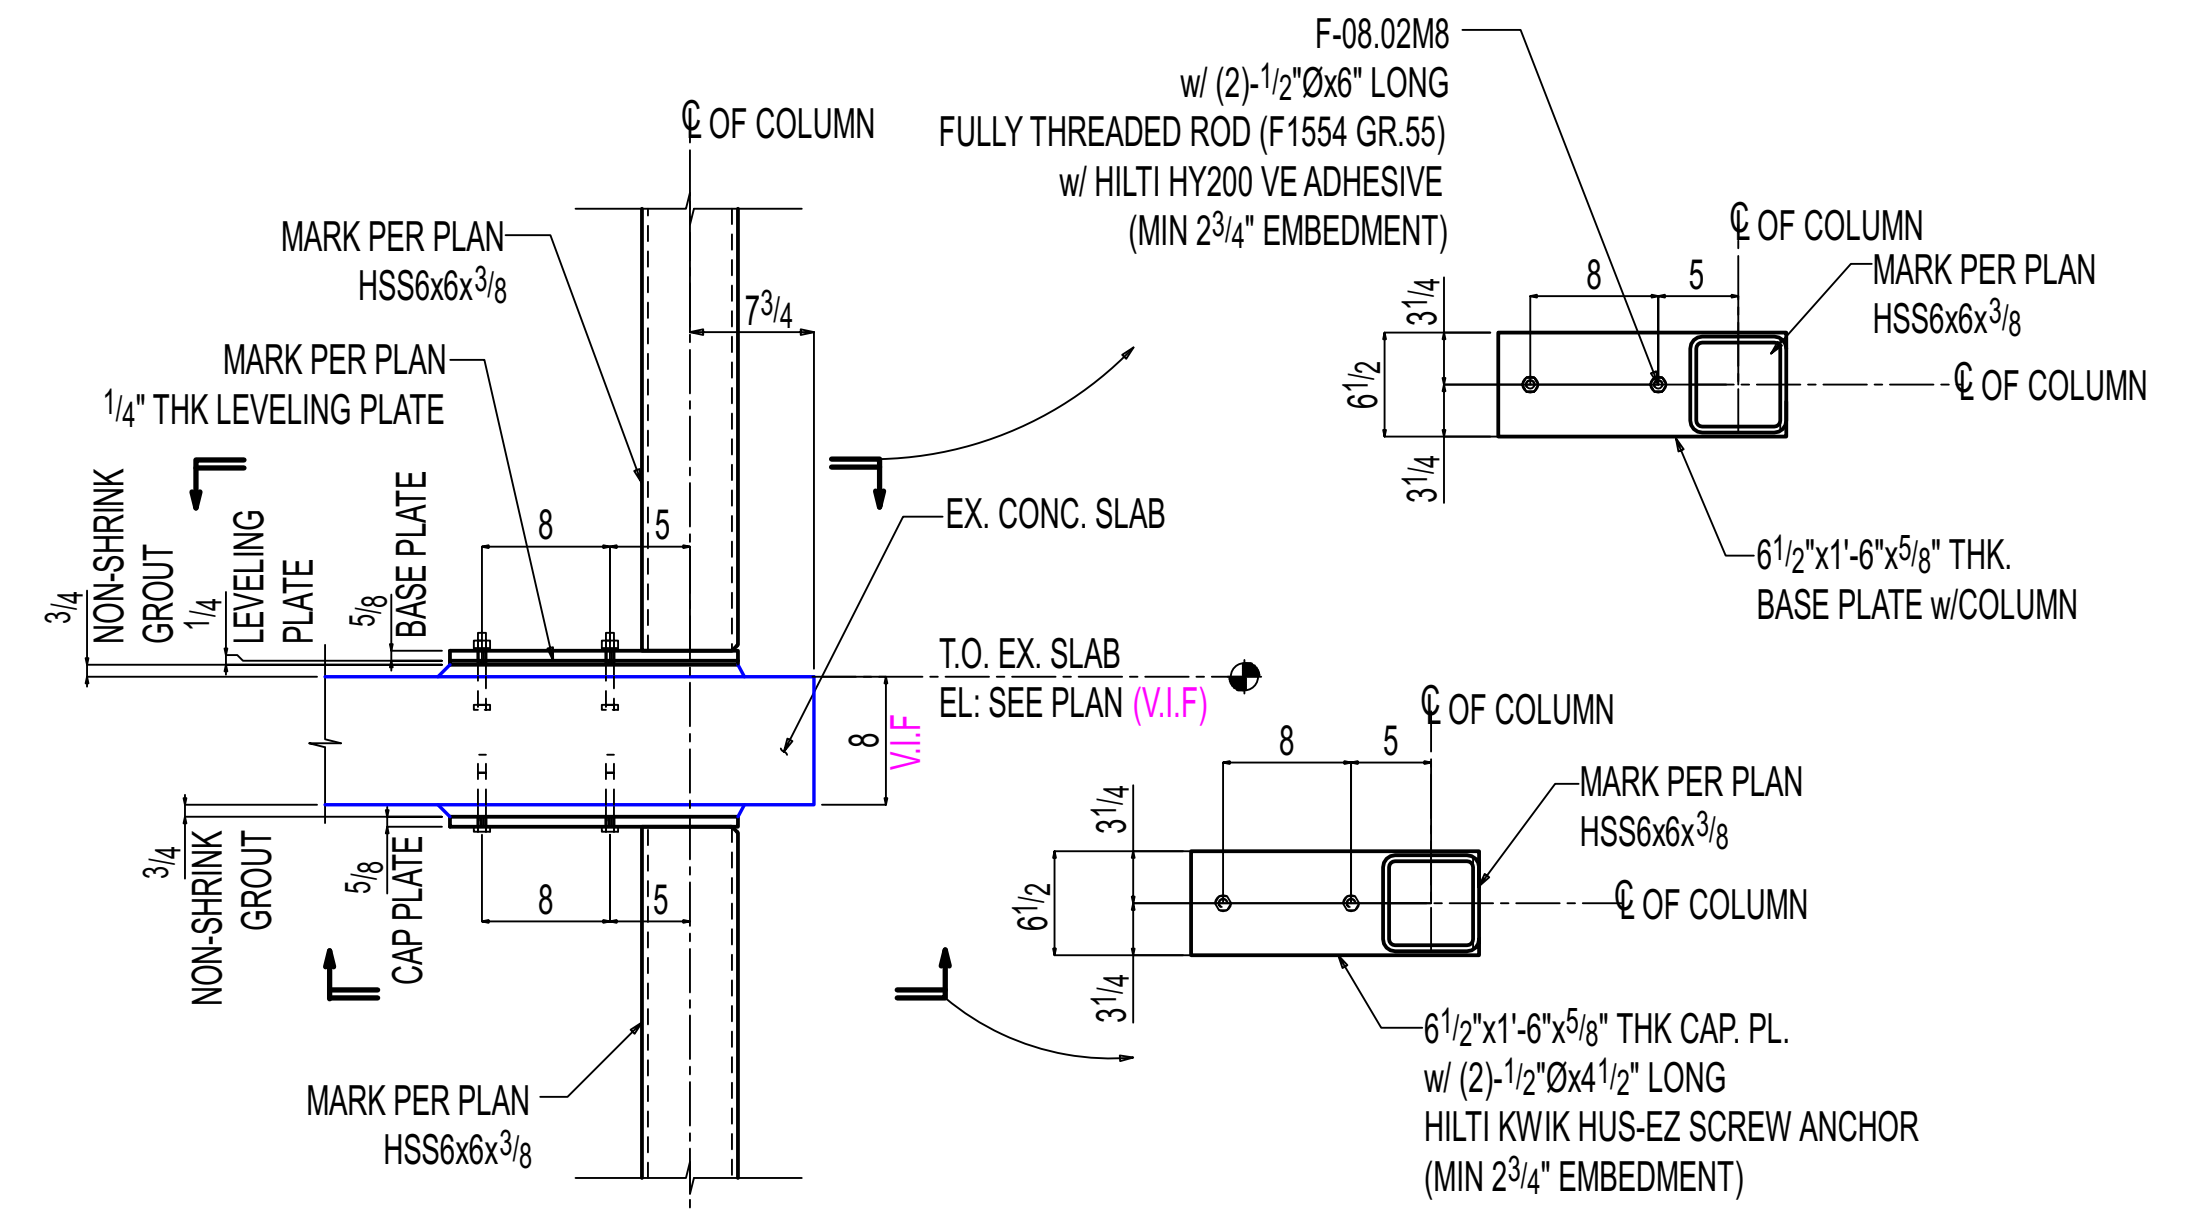

ERECTOR NOTE:
1"NSx6" WIDTH GROUT @ PRECAST BEARING POINT ONLY
CO-ORDINATE BEARING POINT LOCATION WITH
PRECAST MANUFACTURER.

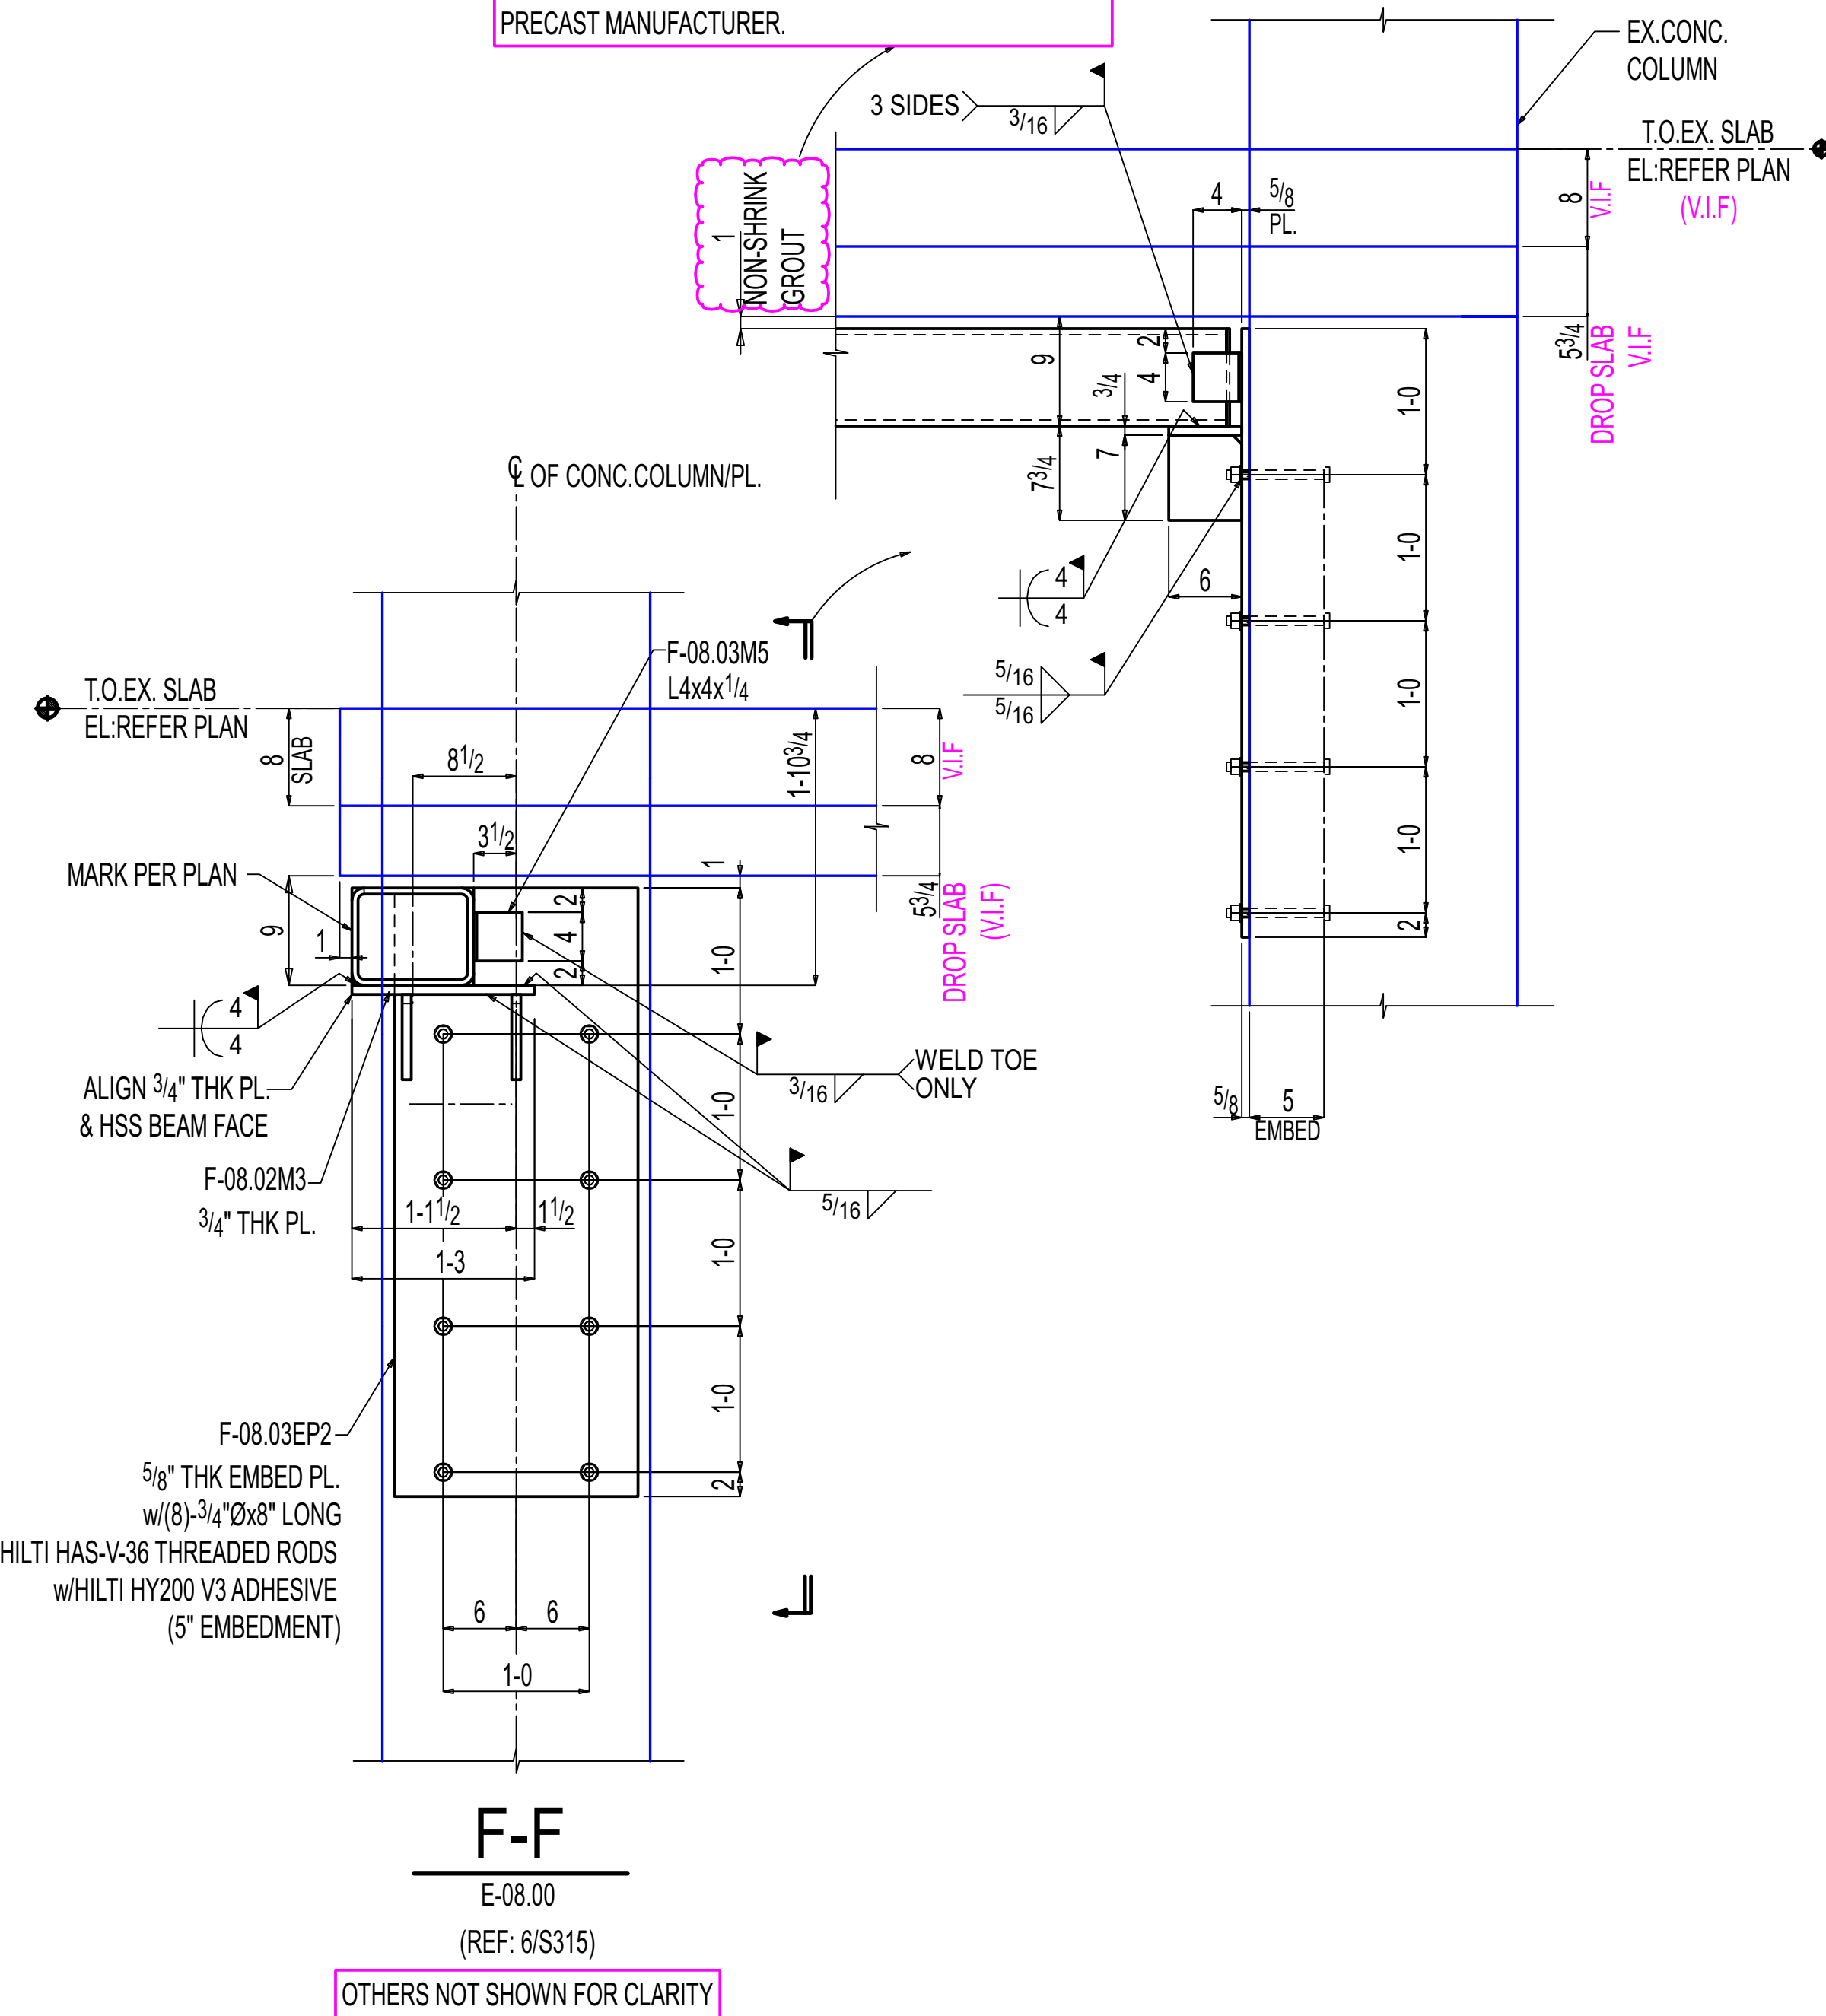

G-G
E-12.00
(REF: 3/S317)
OTHERS NOT SHOWN FOR CLARITY

General Notes			
*Structural steel shall conform to ASTM-A992.			
*Structural SQR/RND tubing conform to ASTM A500 Grade C			
*Pipe shall conform to ASTM A53, Grade B.			
*Channels, Angles and plates shall conform to A36.			
*All bolts shall be 3/4" High strength in accordance with ASTM A325 (UNO)			
*Welding Electrodes for Carbon steel :E70xx			
5	0	For Construction	11-03-2025
4	D	For Re-Approval	10-24-2025
3	C	For Re-Approval	09-19-2025
2	B	NOT IN USE	06-23-2025
1	A	For Approval	02-25-2025
# of Copies	Revision/ Issue	Destination	Date

IRON FABRICATION SERVICES, LLC.

3029 M. Street, NW, Suite 202
Washington, DC 20007
Tel: 202-800-5599
Fax: 202-478-0303

Project Name and Address
MARYLAND AVENUE

Location: **1250 MARYLAND AVENUE SW
WASHINGTON, DC 20024**

Contractor:
BALFOUR BEATTY

Approved for Fabrication by: _____
Signature

Contract #	224009	Drawing #	E-08.02
Contract Item:	LEVEL-02 SLAB EXTENSION		
Ref:	SOW-08:3,4,5&6 / S307		
Date	01/20/2025	Drawing Title:	SOW #08 LEVEL-02 NEW SLAB EXTENSION SUPPORT SECTIONS
Scale	VARIES		