
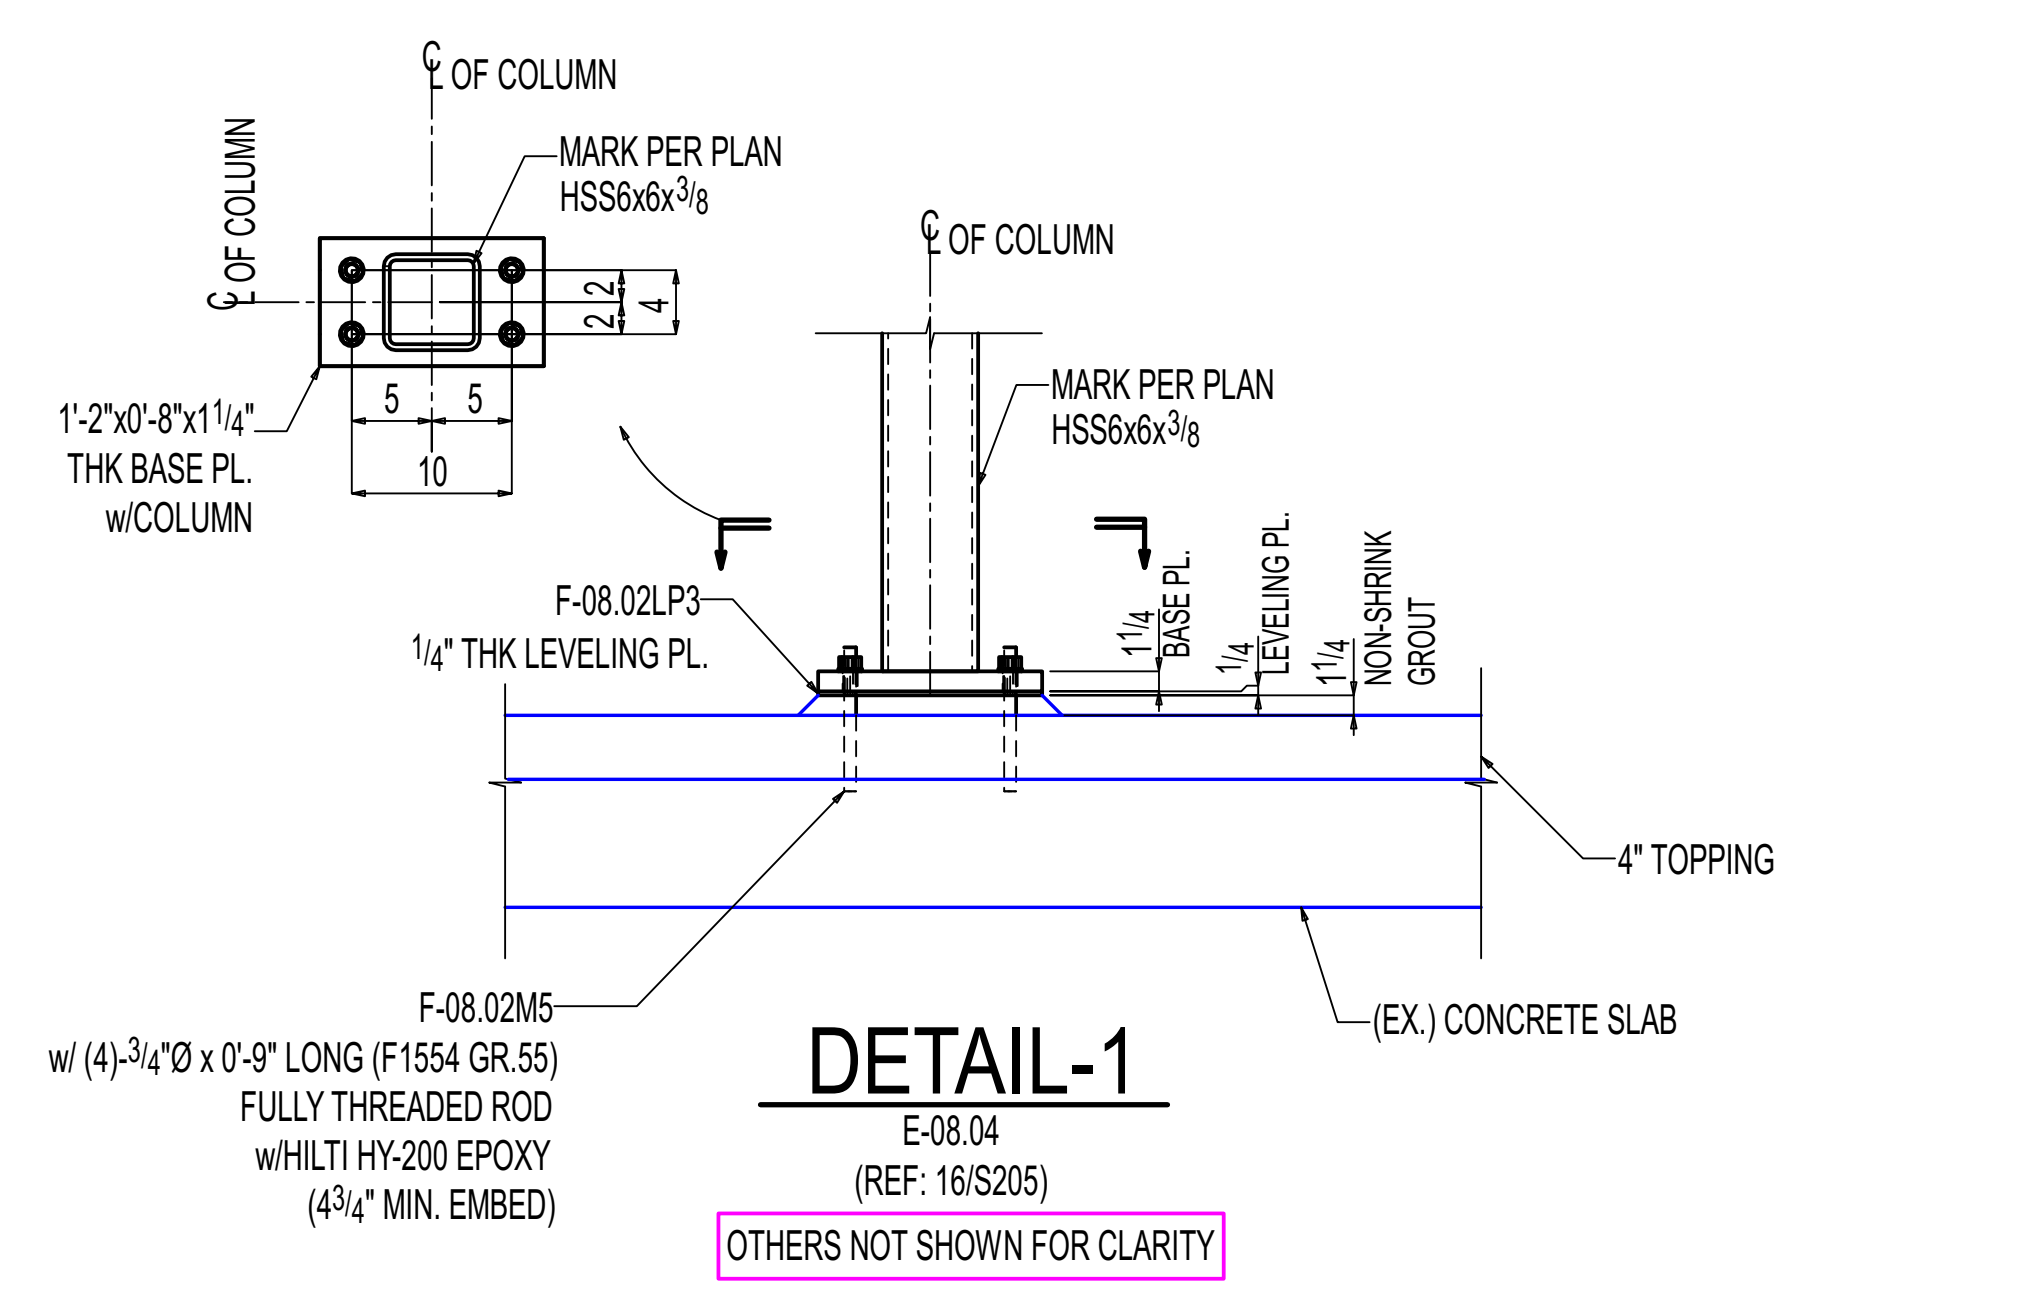
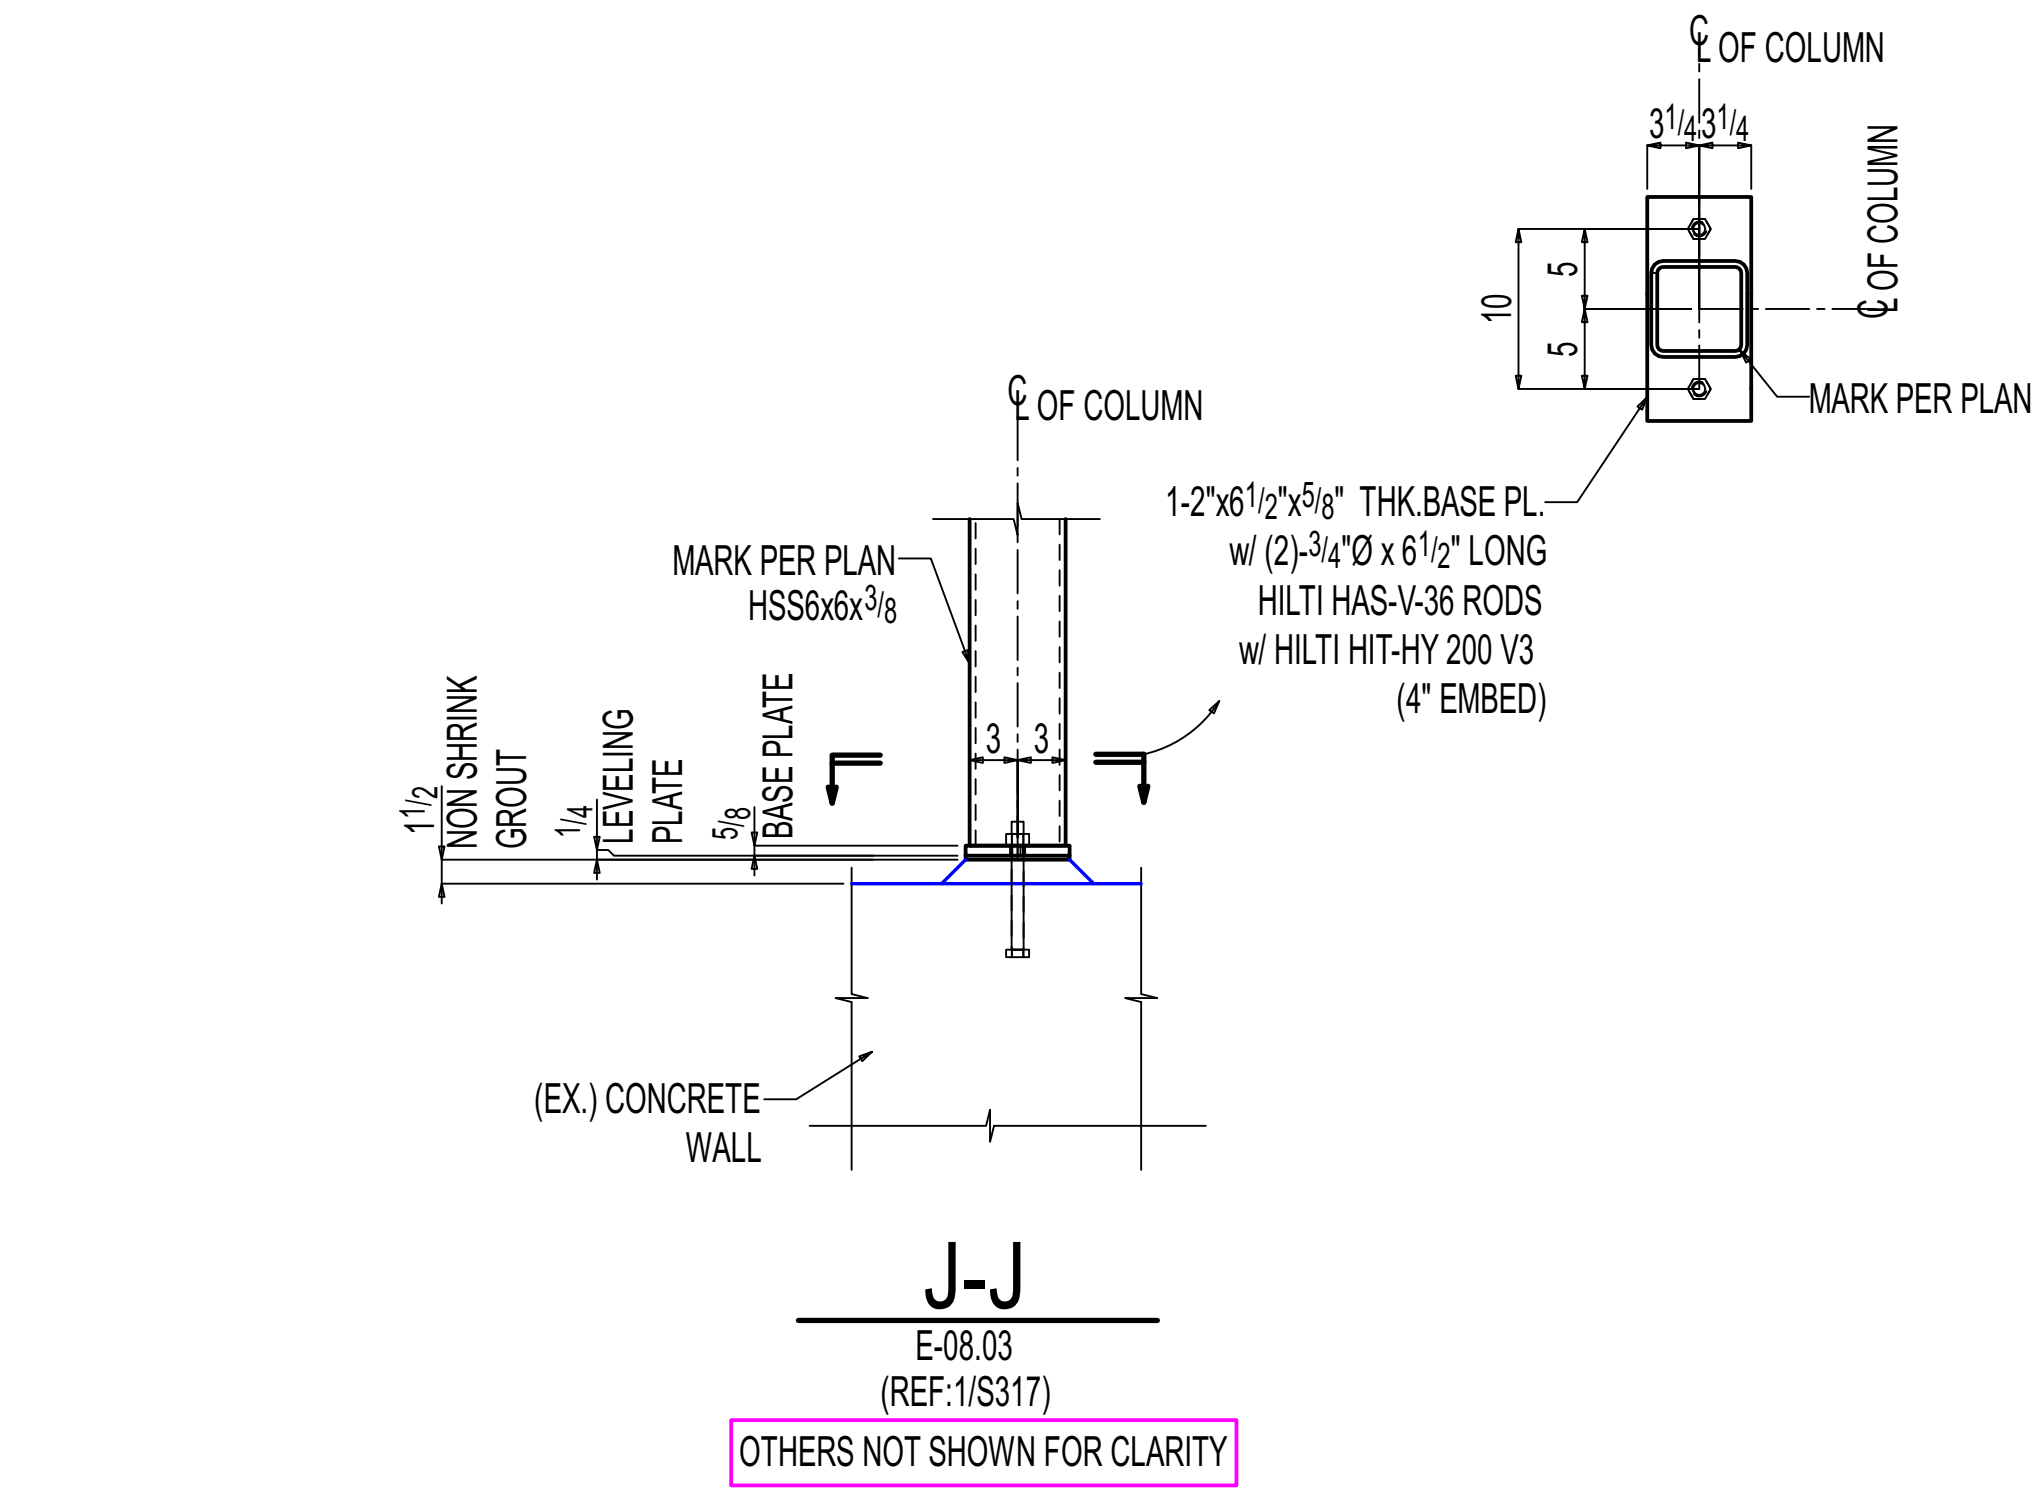
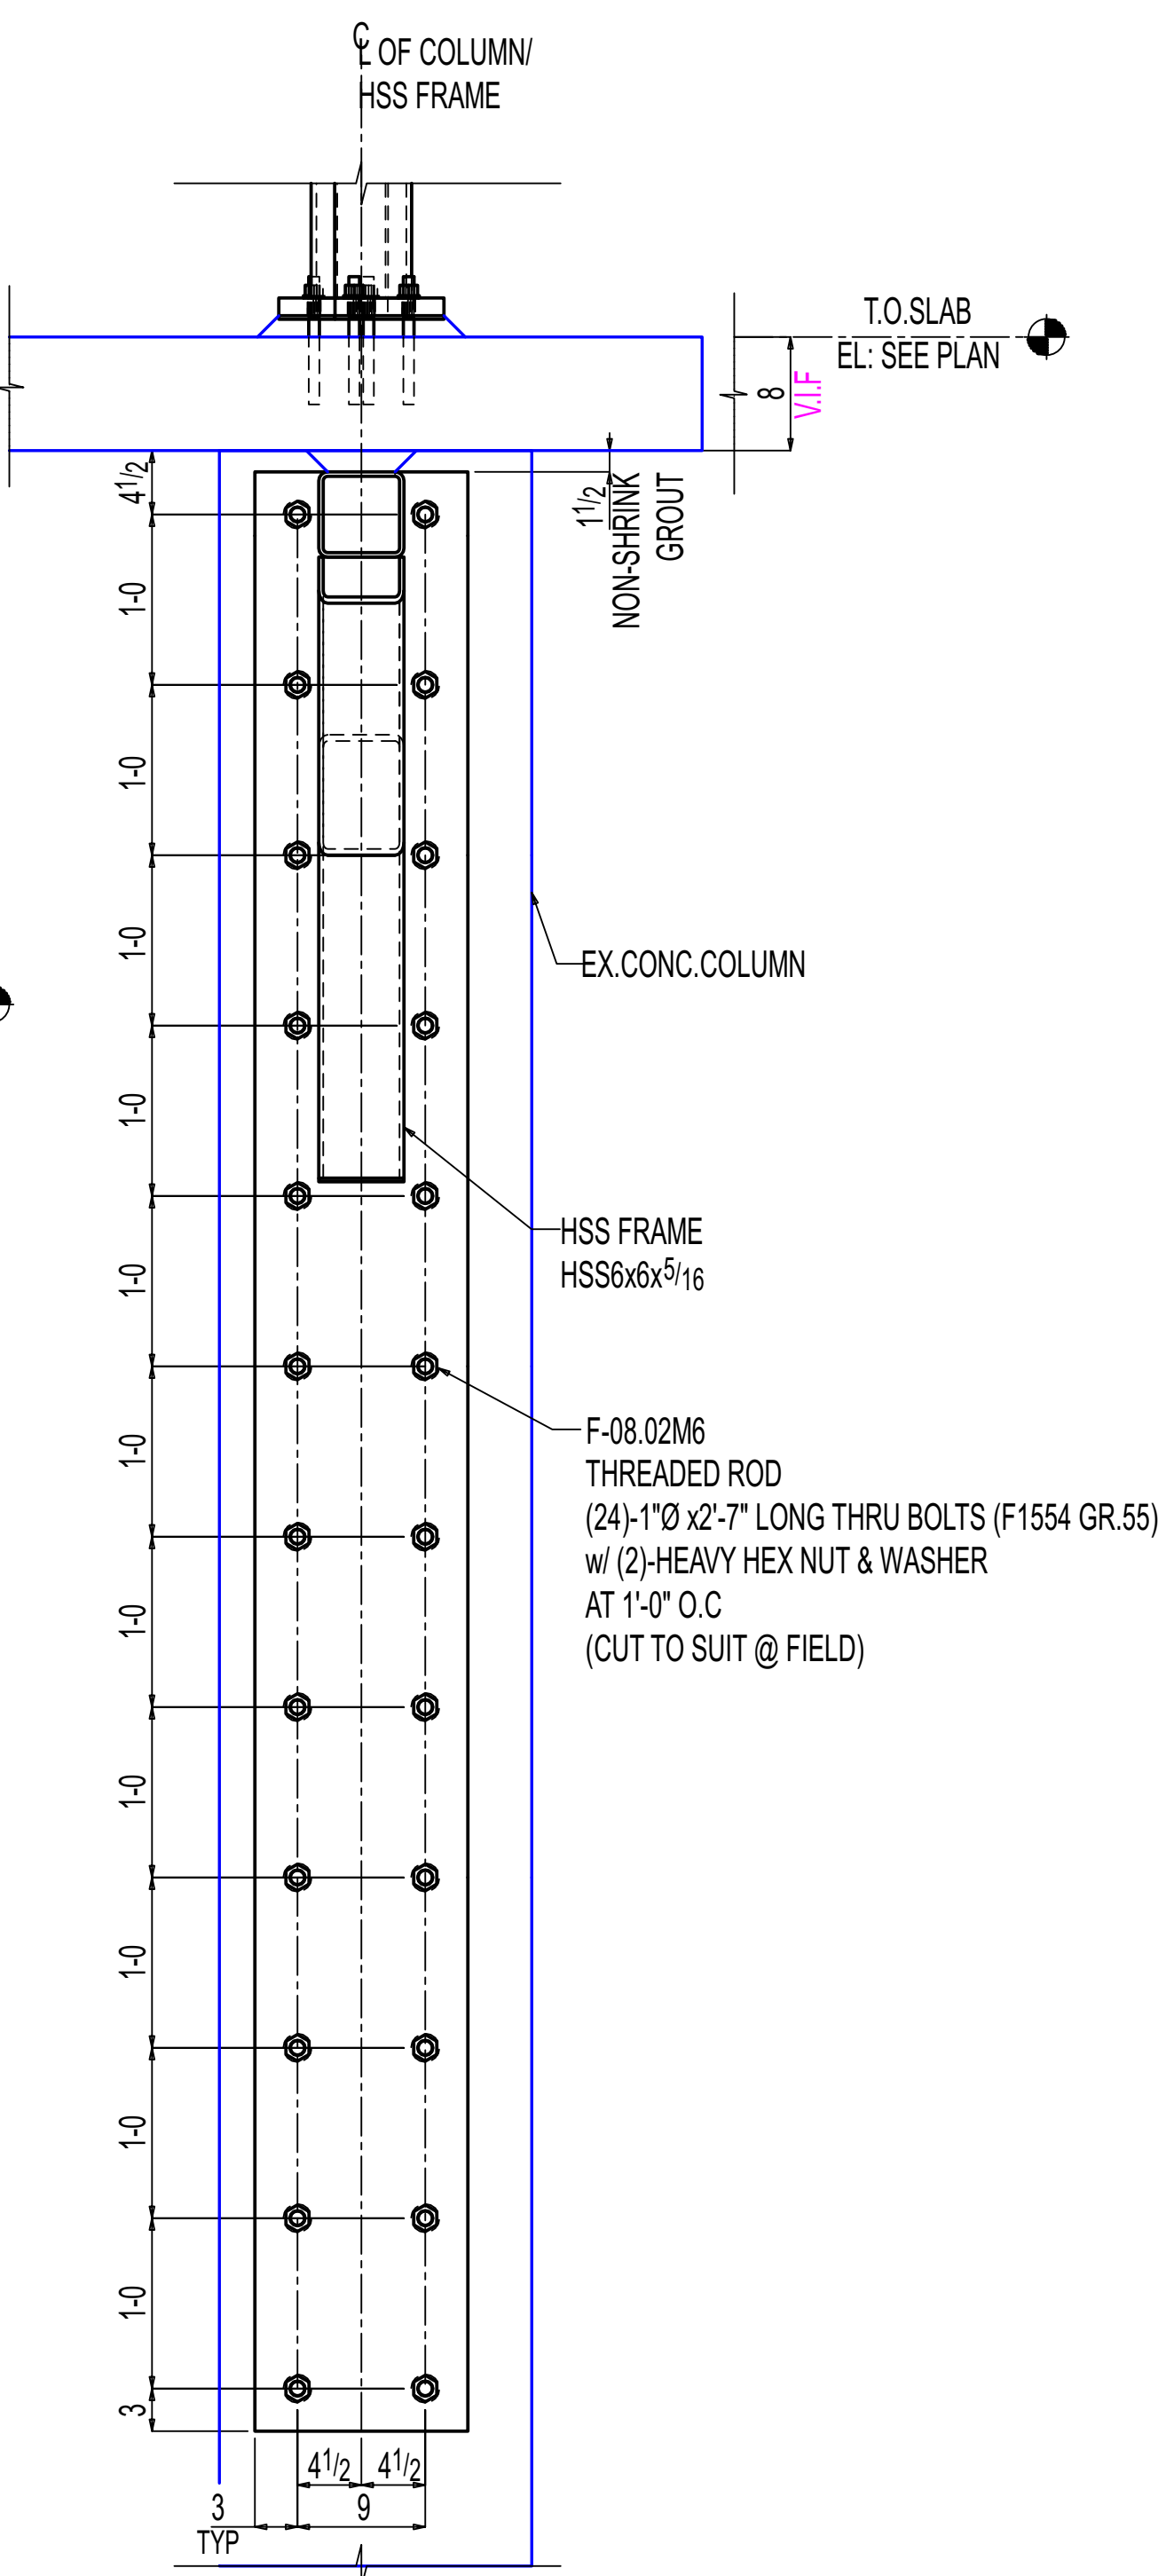


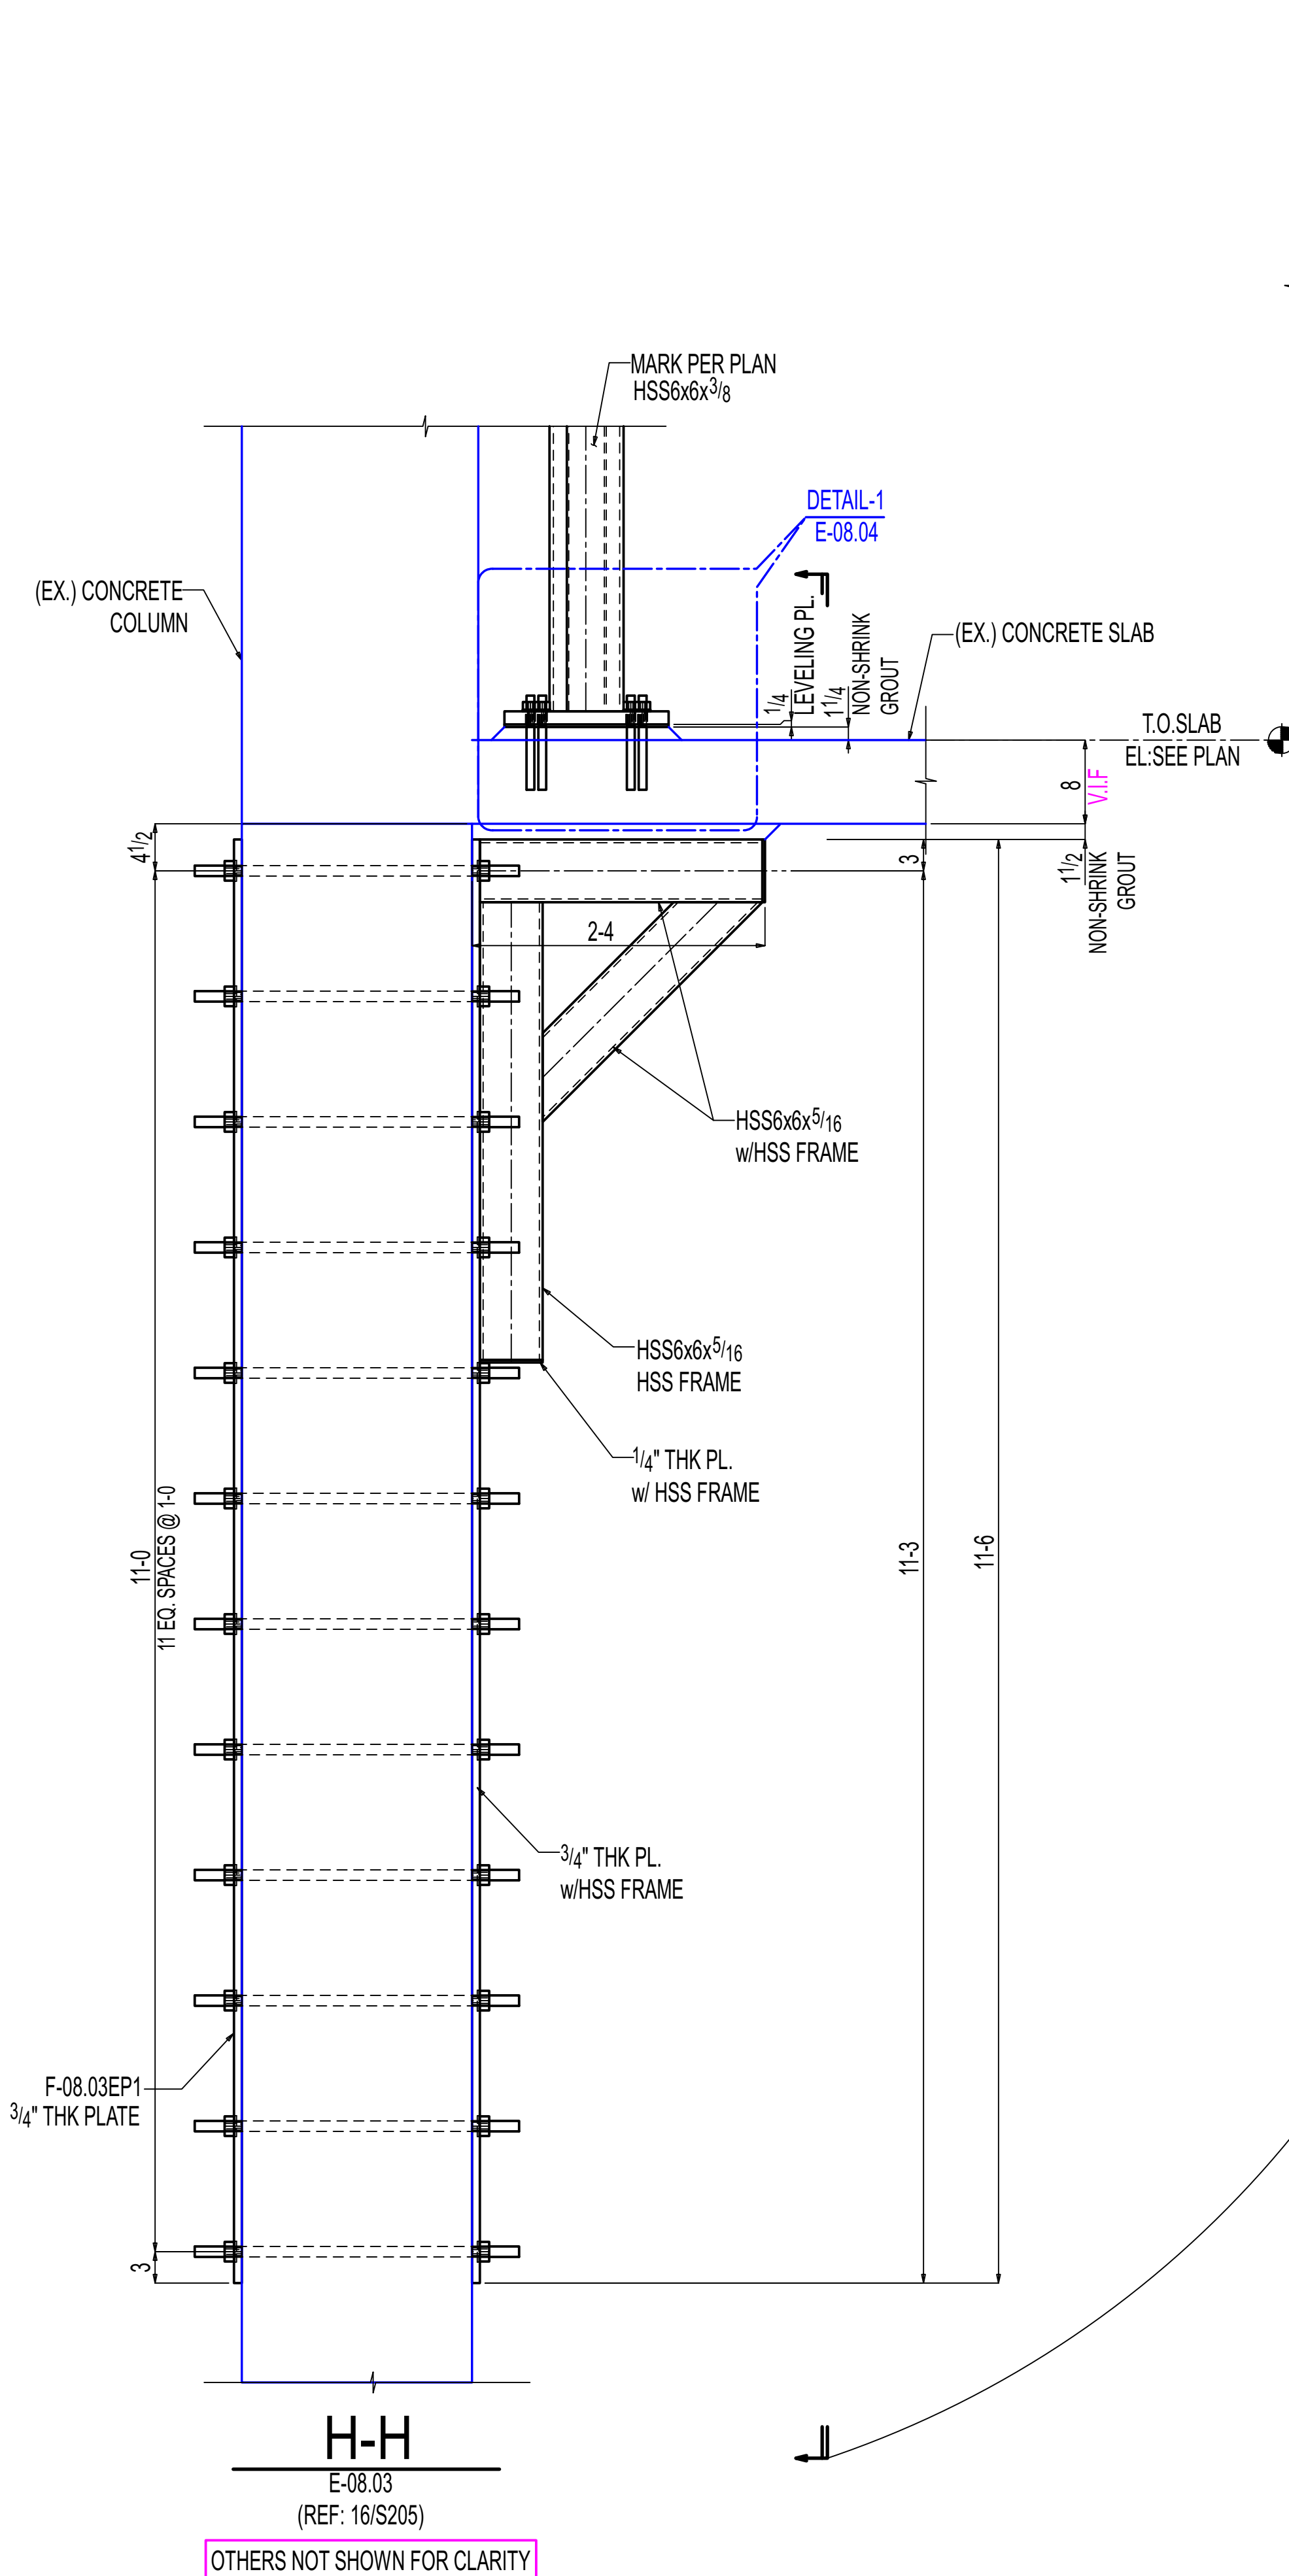

SHOP / ERECTOR NOTE:
LOCATE EXISTING REBAR PRIOR TO FABRICATION OF PLATE.
DO NOT DRILL THROUGH REBAR.

General Notes

*Structural steel shall conform to ASTM-A992.

*Structural SQR/RND tubing conform to ASTM A500 Grade C.

*Pipe shall conform to ASTM A53, Grade B.

*Channels, Angles and plates shall conform to A36.

*All bolts shall be 3/4" High strength in accordance with ASTM A325 (UNO)

*Welding Electrodes for Carbon steel :E70xx

5	0	For Construction	11-03-2025
4	D	For Re-Approval	10-24-2025
3	C	For Re-Approval	09-19-2025
2	B	For Re-Approval	06-23-2025
1	A	For Approval	02-25-2025
# of Copies	Revision/ Issue	Destination	Date

IRON FABRICATION SERVICES, LLC.

3029 M. Street, NW, Suite 202
Washington, DC 20007
Tel: 202-800-5599
Fax: 202-478-0303

Project Name and Address

MARYLAND AVENUE

Location: 1250 MARYLAND AVENUE SW
WASHINGTON, DC 20024

Contractor:

BALFOUR BEATTY

Approved for Fabrication by:

Signature

Contract #

224009

Drawing #

E-08.04

Contract Item:

LEVEL-01
SLAB EXTENSION

Ref:

SOW-08:3,4,5&6 / S307

Date

01/20/2025

Drawing Title:

SOW #08 LEVEL-01 NEW
SLAB EXTENSION SUPPORT
SECTIONS

Scale

VARIES