


BILL OF MATERIAL							
LINE #	QTY	PC	MARK	DESCRIPTION	LENGTH	REMARKS	ADVANCE MILL #
ONE	F-09.00FR1	FRAME					248
1	F-09.00FR1	HSS6x6x ⁵ / ₁₆		3	5 ³ / ₄	A500C	81
1	w2764	W8x31		1	4	A992	41
1	p346	PL ¹ / ₂ x16		4	6	A36	123
1	p688	PL ¹ / ₄ x6		0	6	A36	3
5	F-09.00FR3	FRAME					1193
5	F-09.00FR3	HSS6x6x ⁵ / ₁₆		3	5 ³ / ₄	A500C	406
5	w2769	W8x31		1	0 ¹ / ₂	A992	161
5	p346	PL ¹ / ₂ x16		4	6	A36	613
5	p688	PL ¹ / ₄ x6		0	6	A36	13
ONE	F-09.00FR4	FRAME					366
1	F-09.00FR4	HSS6x6x ⁵ / ₁₆		3	7 ³ / ₄	A500C	85
1	hss3770	HSS6x6x ⁵ / ₁₆		3	6 ³ / ₄	A500C	83
1	hss1544	HSS6x6x ⁵ / ₁₆		3	0 ¹ / ₄	A500C	70
1	p346	PL ¹ / ₂ x16		4	6	A36	123
2	p688	PL ¹ / ₄ x6		0	6	A36	5
ONE	F-09.00FR5	FRAME					372
1	F-09.00FR5	HSS6x6x ⁵ / ₁₆		3	7 ³ / ₄	A500C	85
1	hss235	HSS6x6x ⁵ / ₁₆		3	8 ⁹ / ₁₆	A500C	87
1	hss234	HSS6x6x ⁵ / ₁₆		3	1 ¹ / ₂	A500C	73
1	p346	PL ¹ / ₂ x16		4	6	A36	123
2	p688	PL ¹ / ₄ x6		0	6	A36	5
2	F-09.00FR6	FRAME					500
2	F-09.00FR6	HSS6x6x ⁵ / ₁₆		3	5 ³ / ₄	A500C	162
2	w125	W8x31		1	5	A992	88
2	p346	PL ¹ / ₂ x16		4	6	A36	245
2	p688	PL ¹ / ₄ x6		0	6	A36	5


Total weight : 2679

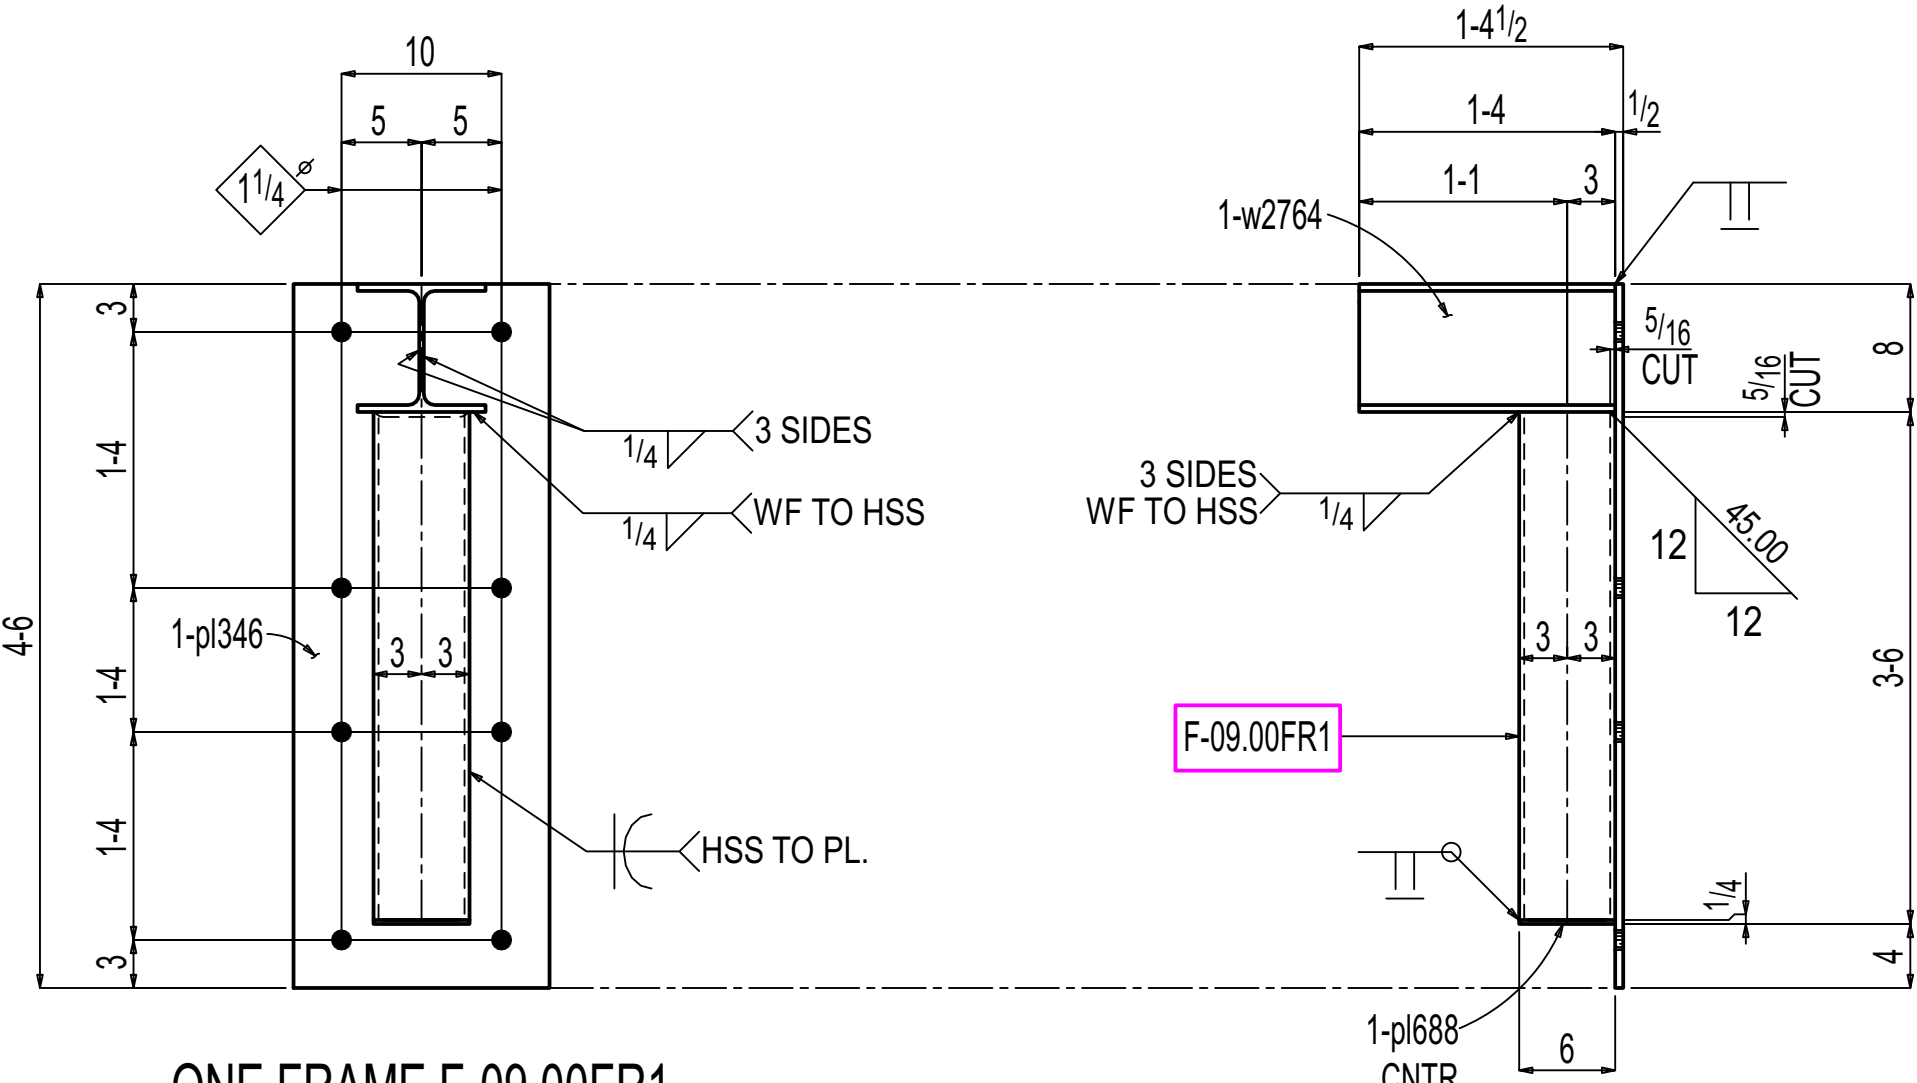


ONE FRAME F-09.00FR1

THIS PIECEMARK COMBINED
WITH F-09.00FR3


ONE FRAME F-09.00FR2

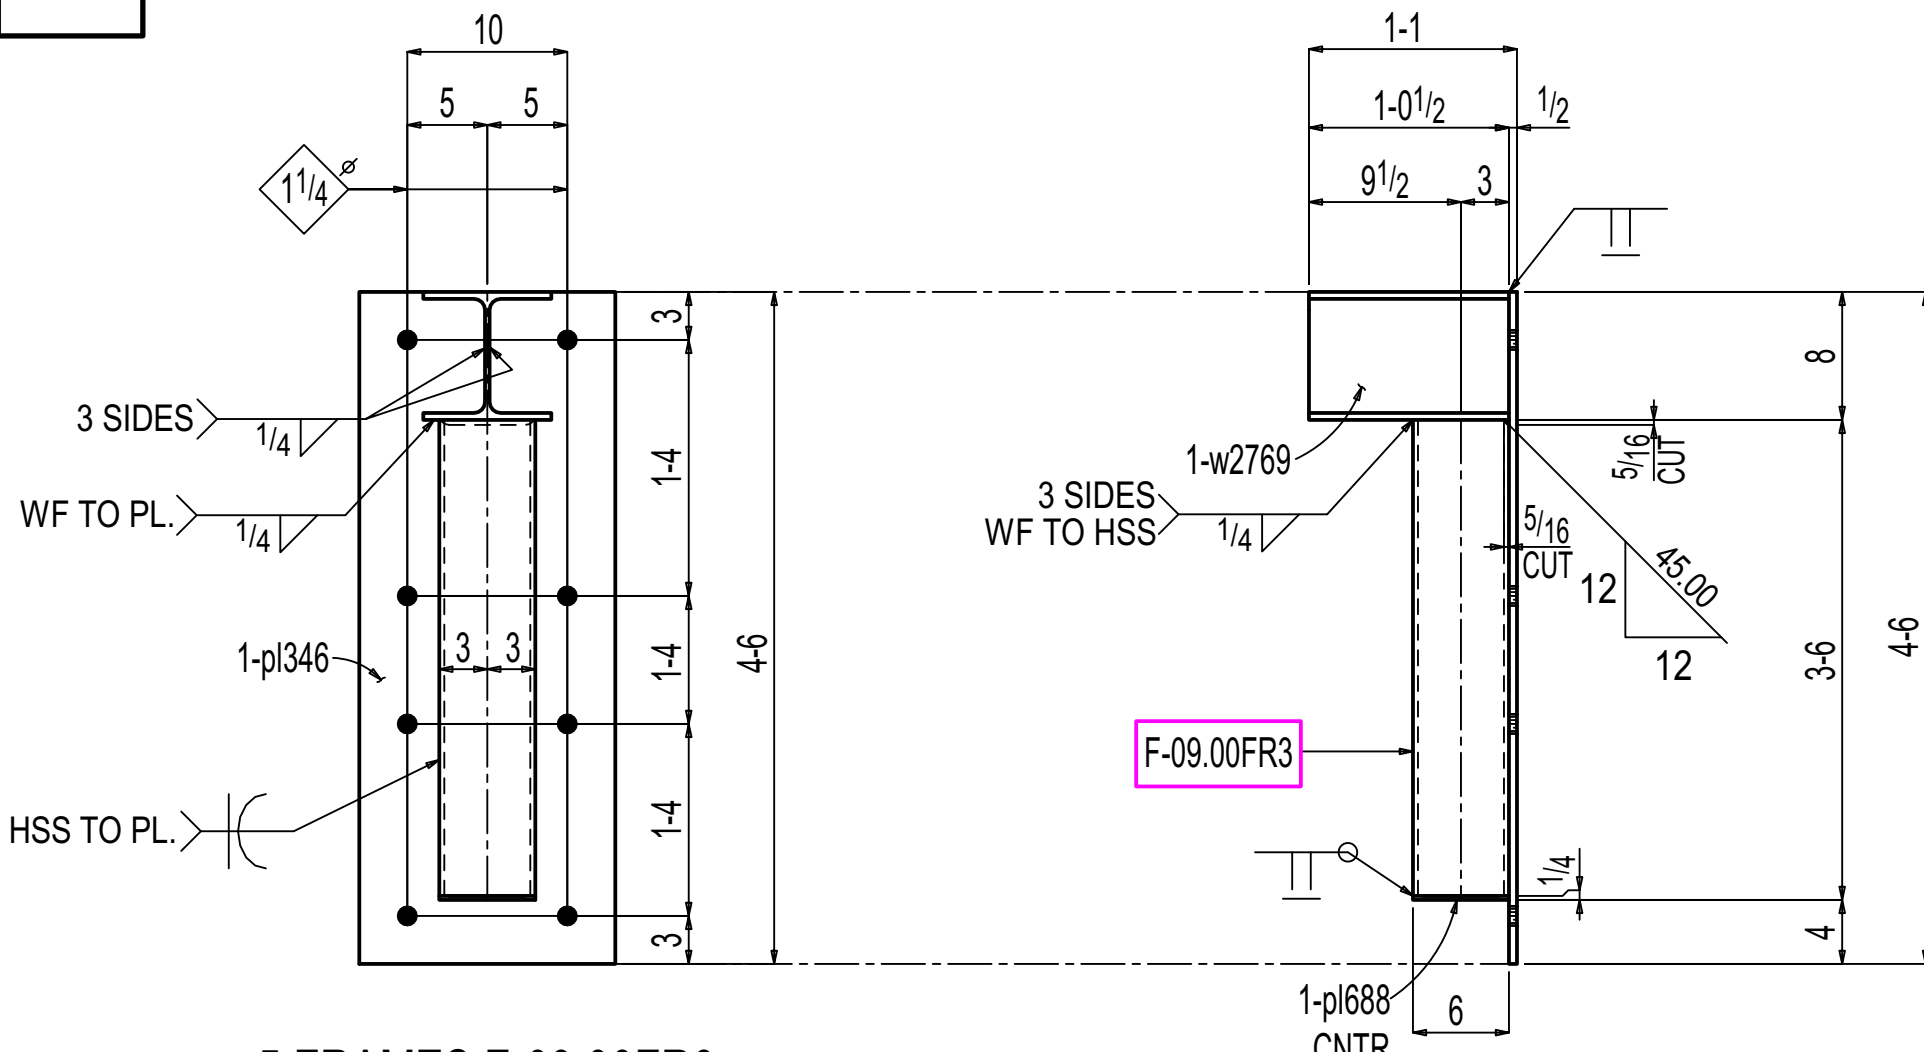


5 FRAMES F-09.00FR3

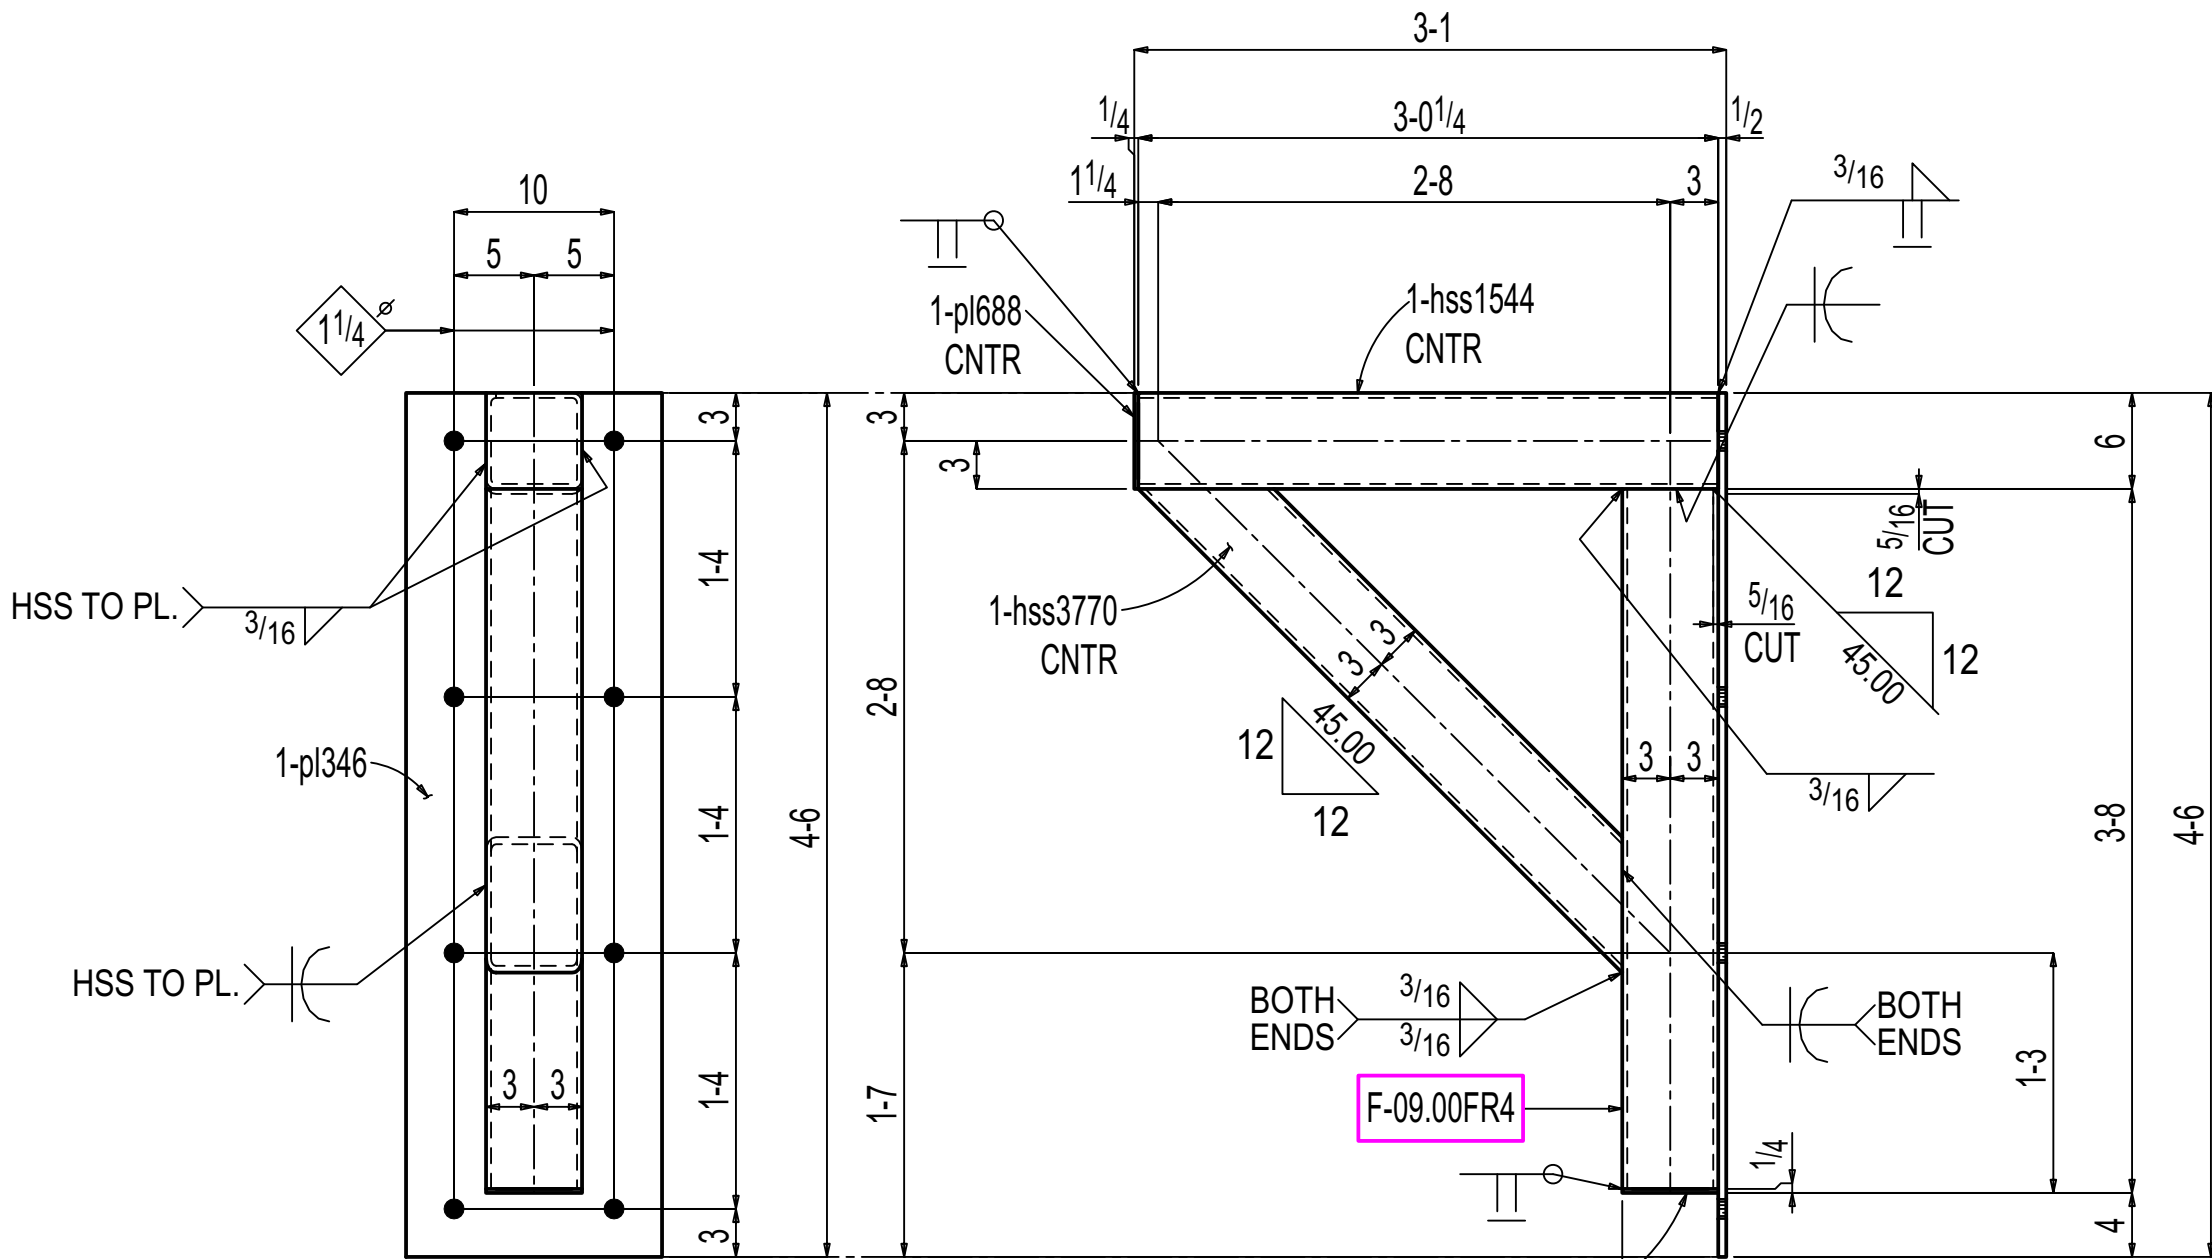

ONE FRAME F-09.00FR4

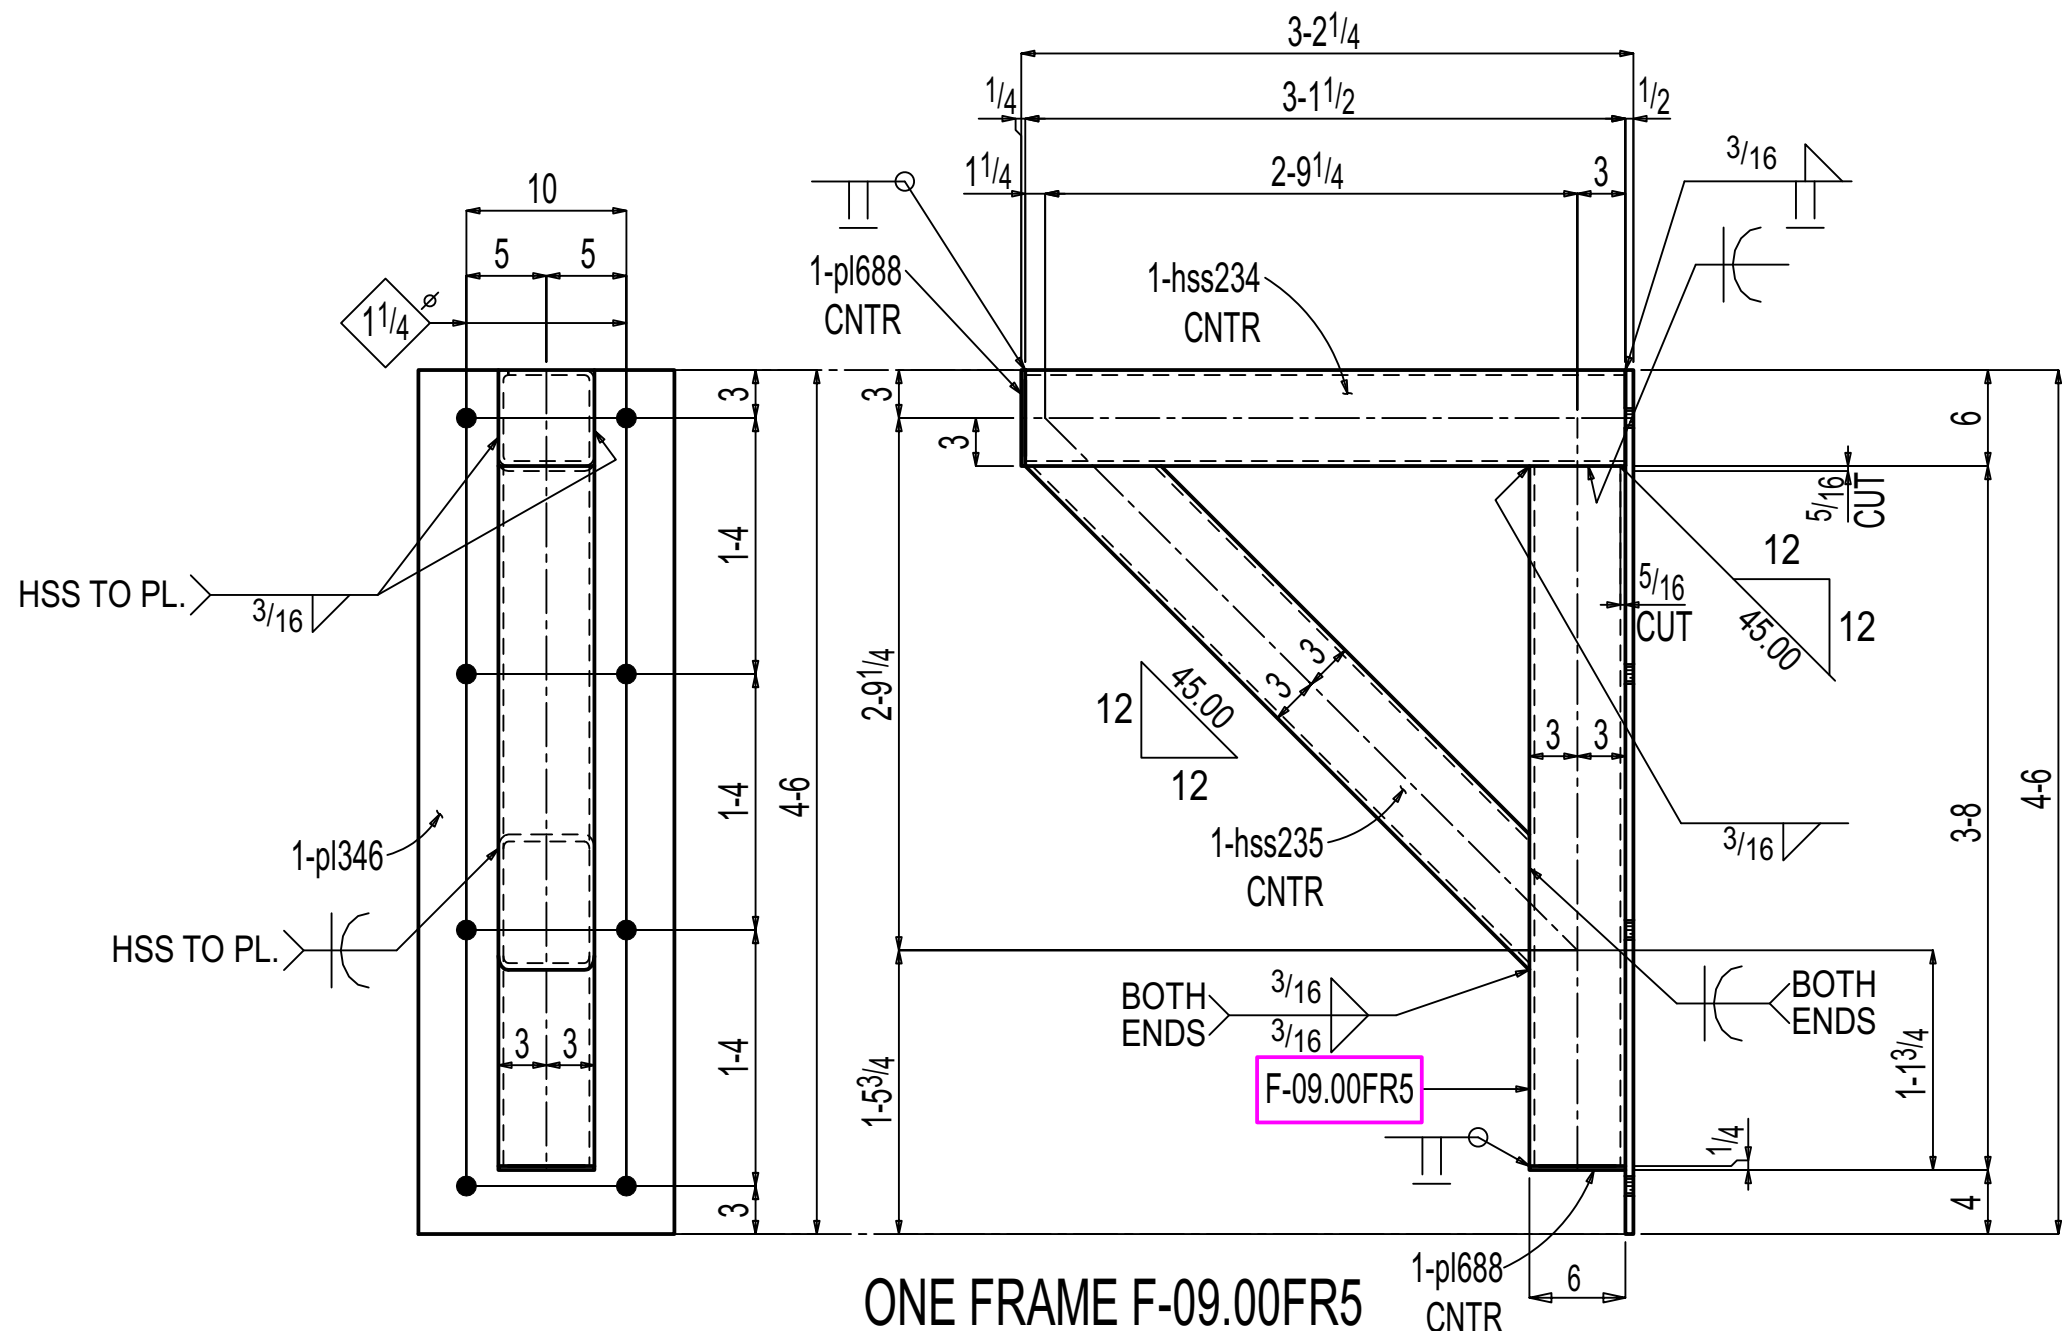

ONE FRAME F-09.00FR5

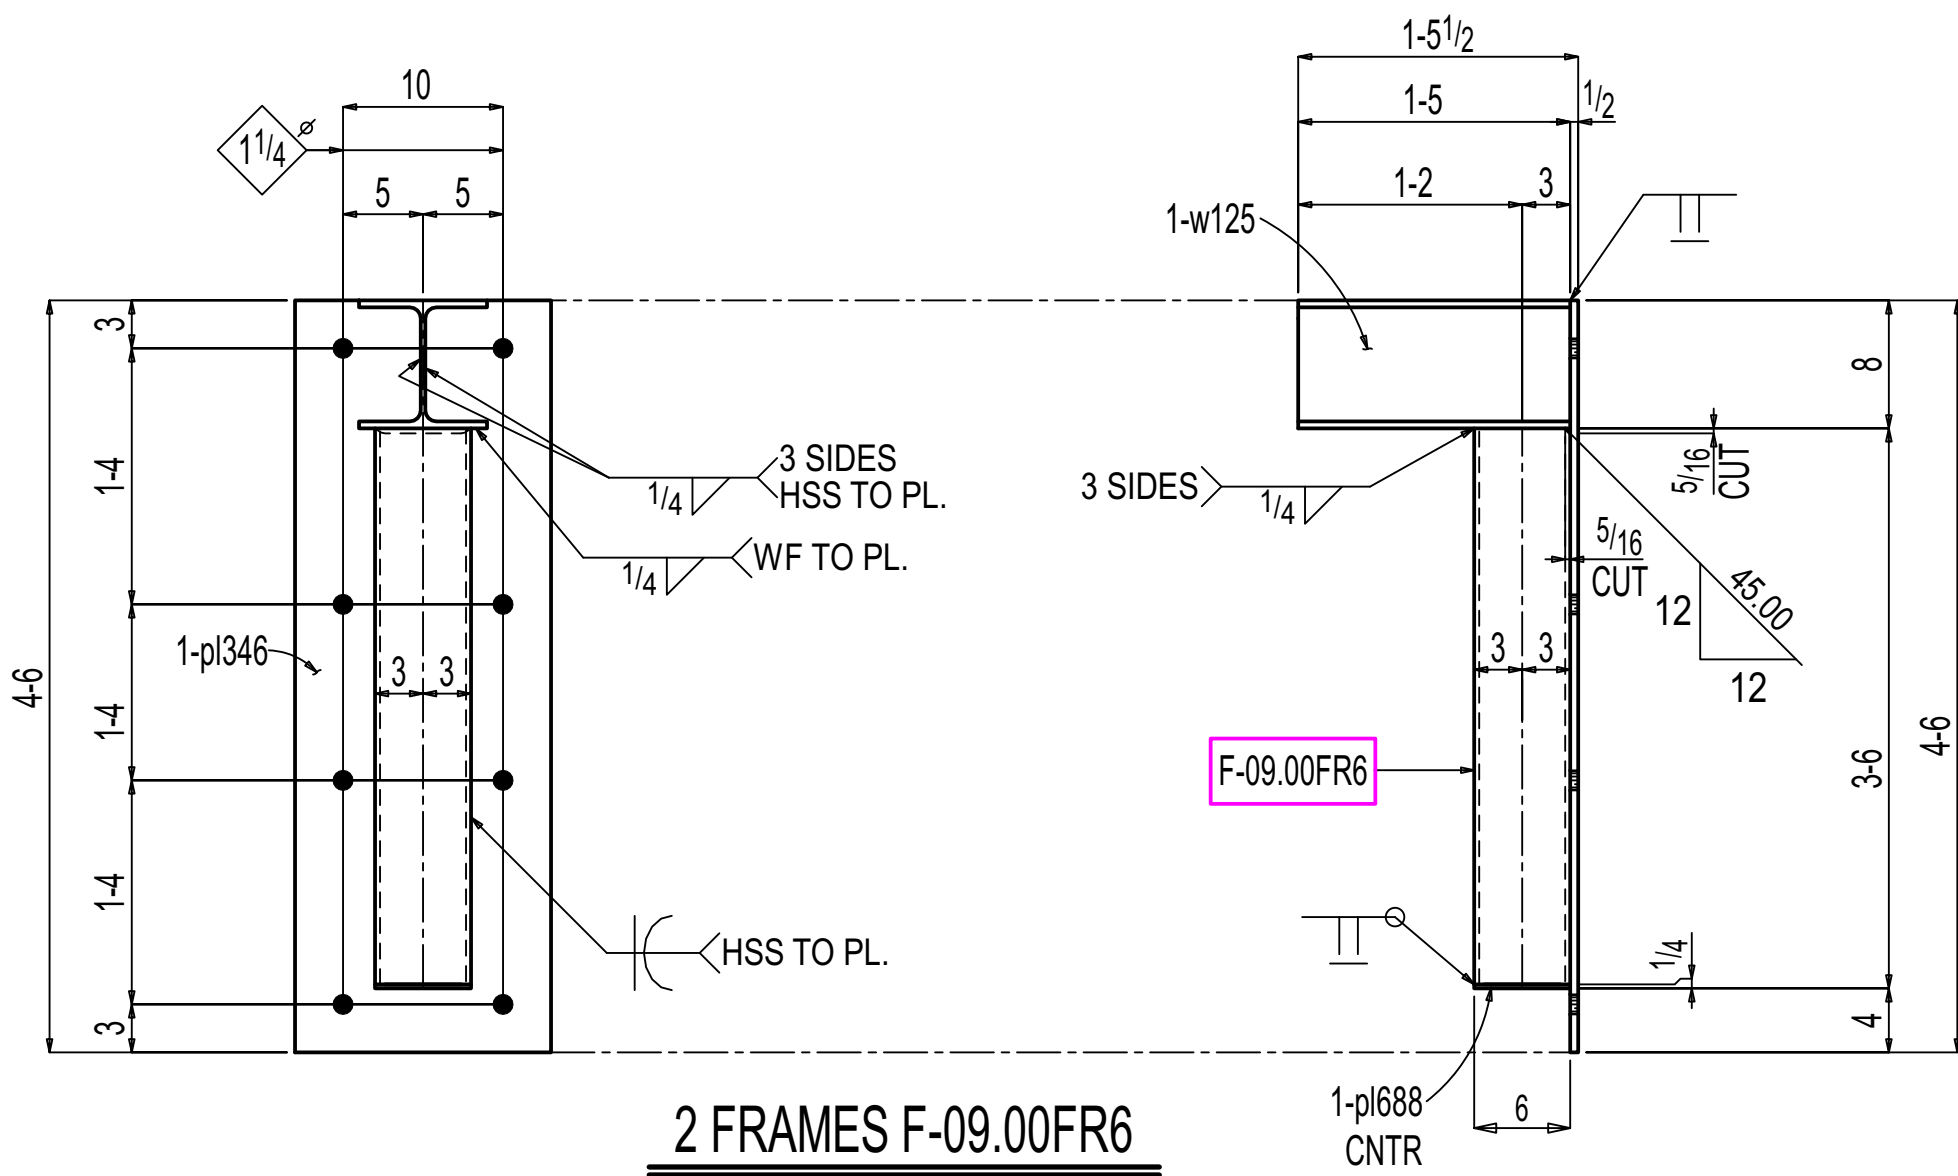

2 FRAMES F-09.00FR6

PAINT :NO PAINT
PREPARATION :SSPC-SP3

General Notes			
*Structural steel shall conform to ASTM-A992.			
*Structural SQR/RND,tubing conform to ASTM A500 Grade C			
*Pipe shall conform to ASTM A53, Grade B.			
*Channels, Angles and plates shall conform to A36.			
*All bolts shall be 3/4" High strength in accordance with ASTM A325 (UNO)			
*Welding Electrodes for Carbon steel :E70xx			
5	0	For Fabrication	11-14-2025
4	D	For Re-Approval	10-24-2025
3	C	For Re-Approval	09-19-2025
2	B	For Re-Approval	06-23-2025
1	A	For Approval	02-25-2025
# of Copies	Revision/ Issue	Destination	Date

IRON FABRICATION SERVICES, LLC.

3029 M. Street, NW, Suite 202
Washington, DC 20007
Tel: 202-800-5599
Fax: 202-478-0303

Project Name and Address
MARYLAND AVENUE
Location: **1250 MARYLAND AVENUE SW
WASHINGTON, DC 20024**

Contractor:
BALFOUR BEATTY

Approved for Fabrication by: Signature

Contract # **224009** Drawing # **F-09.00**

Contract Item: **FRAME**

Ref:
SOW - 09: E-09.00 - E-09.02

Date
01/ 23/ 2025
Scale
VARIES

Drawing Title:
FRAME DETAIL