
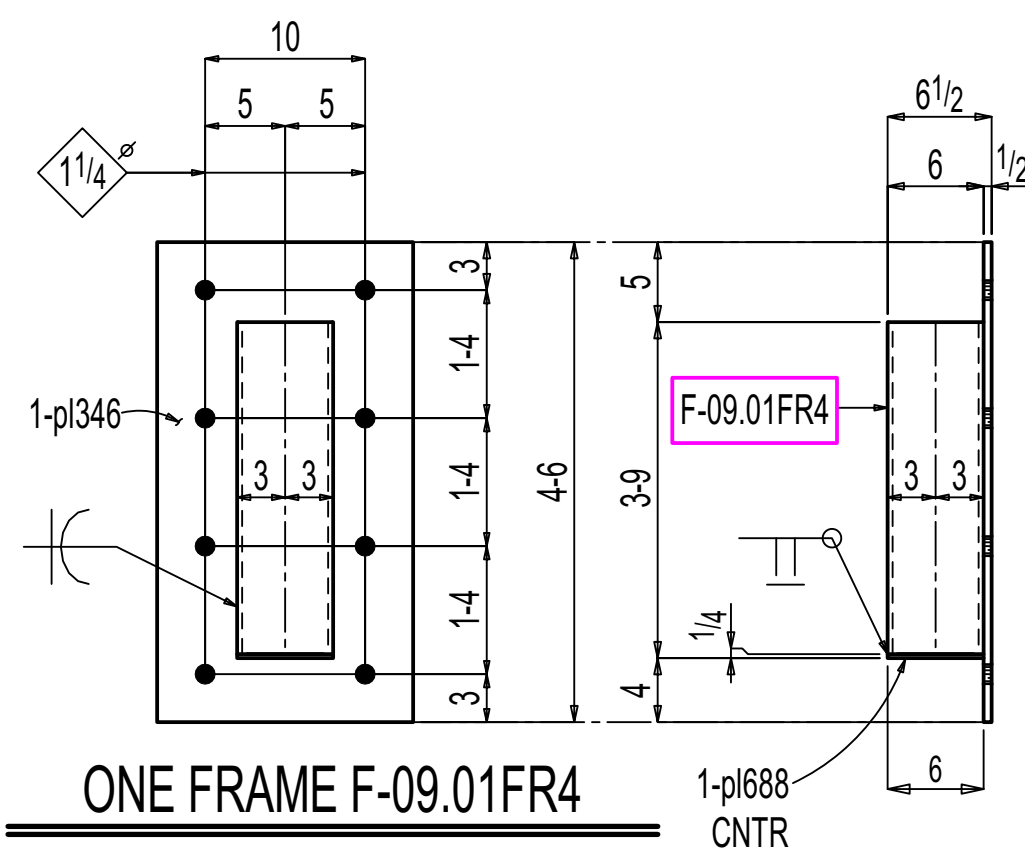
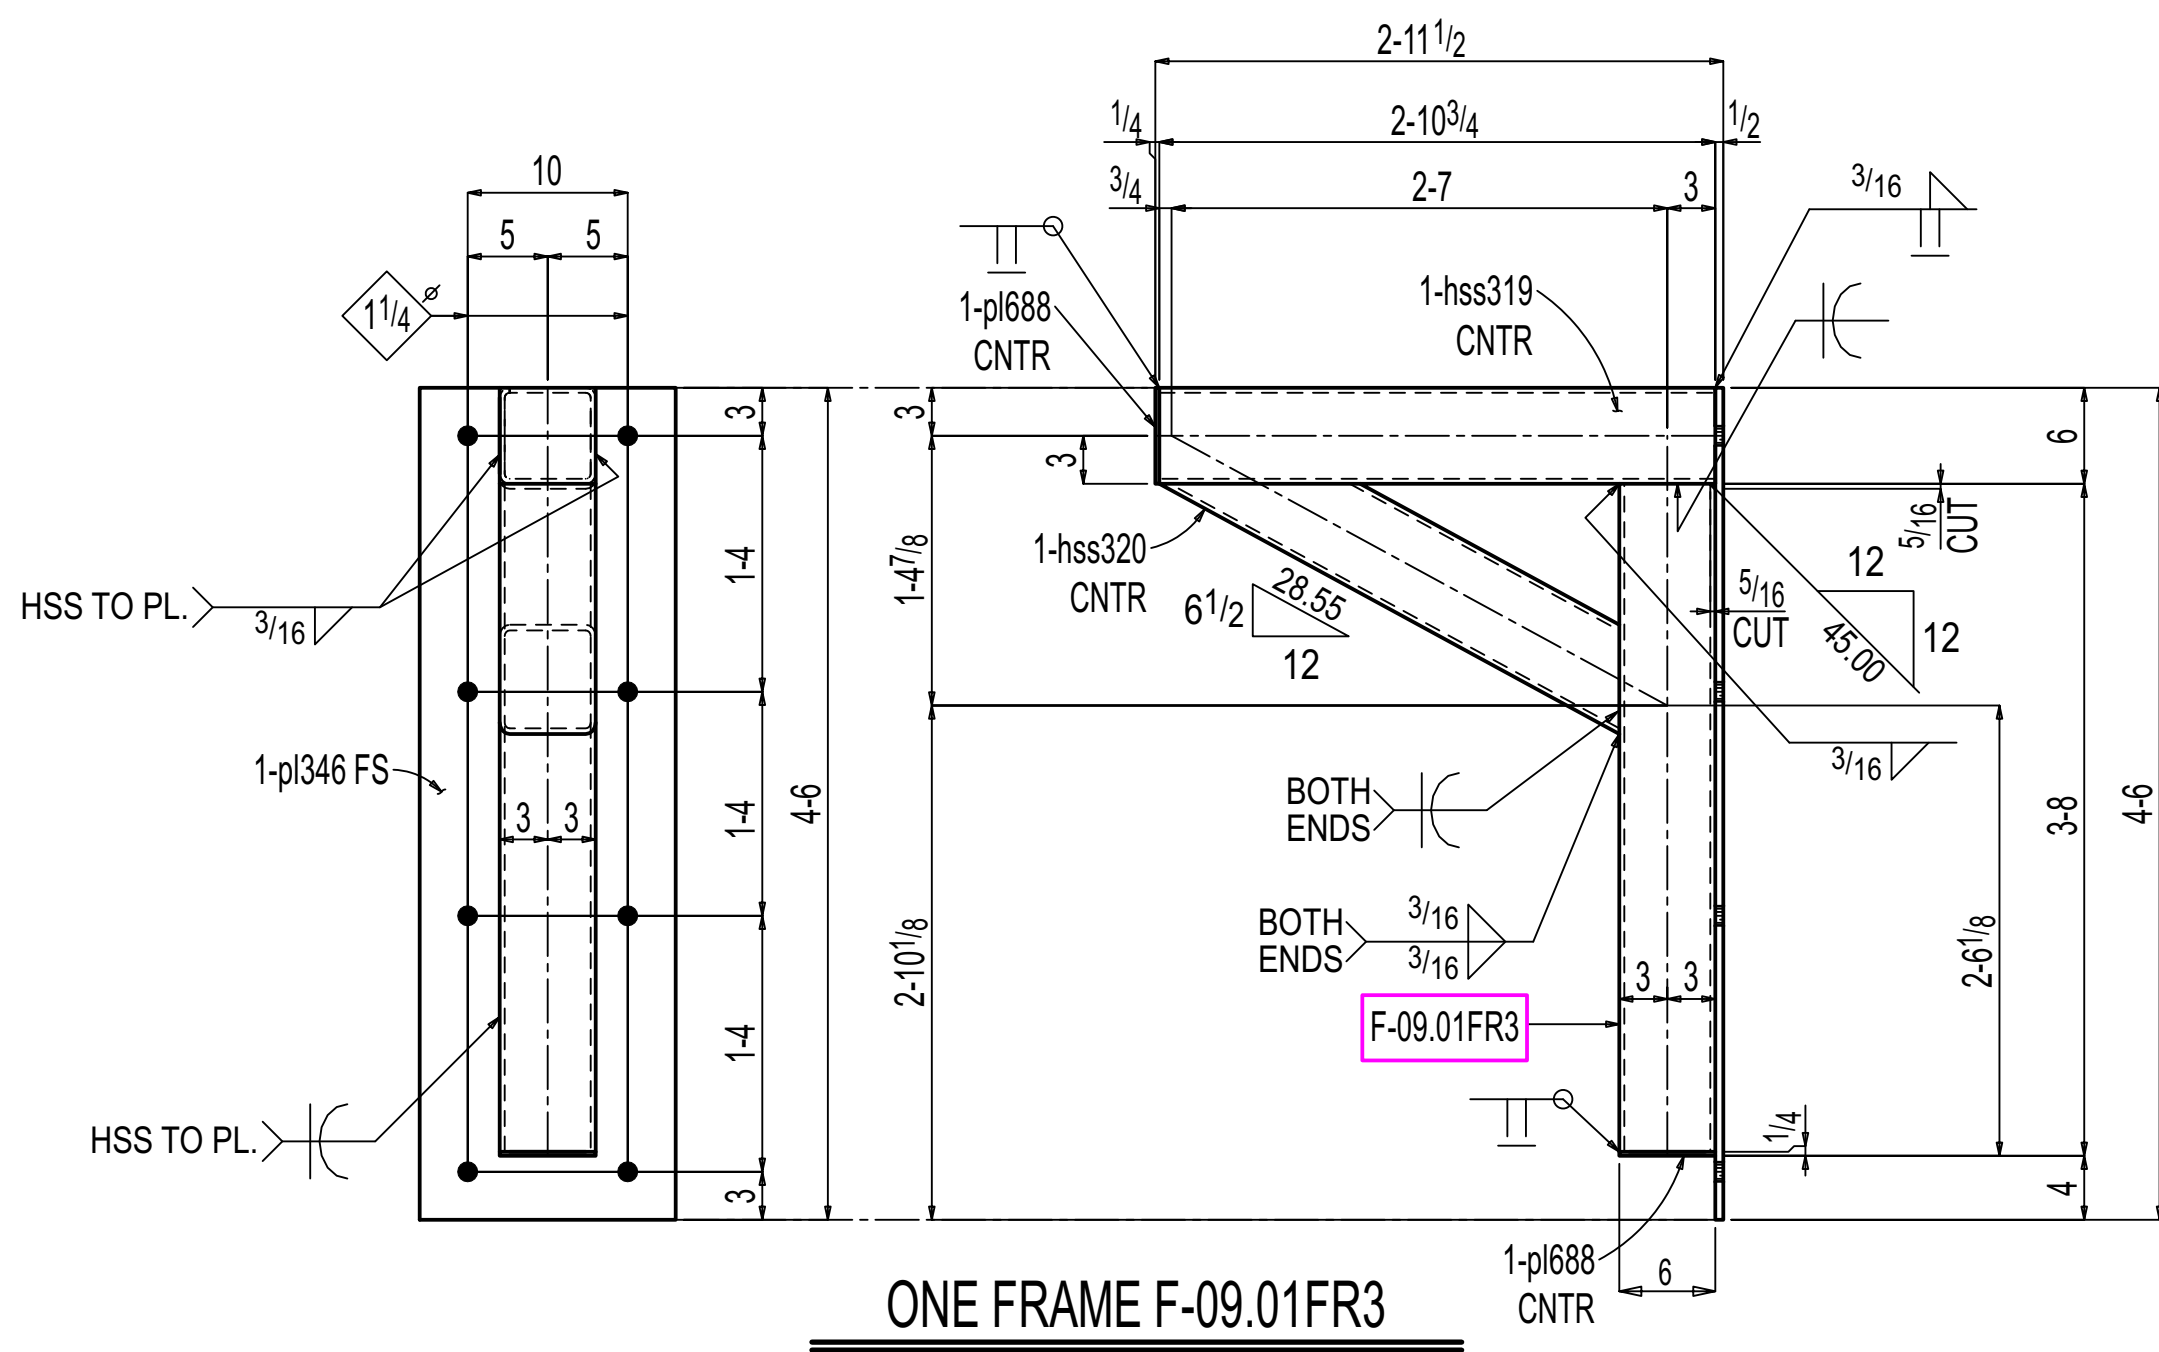
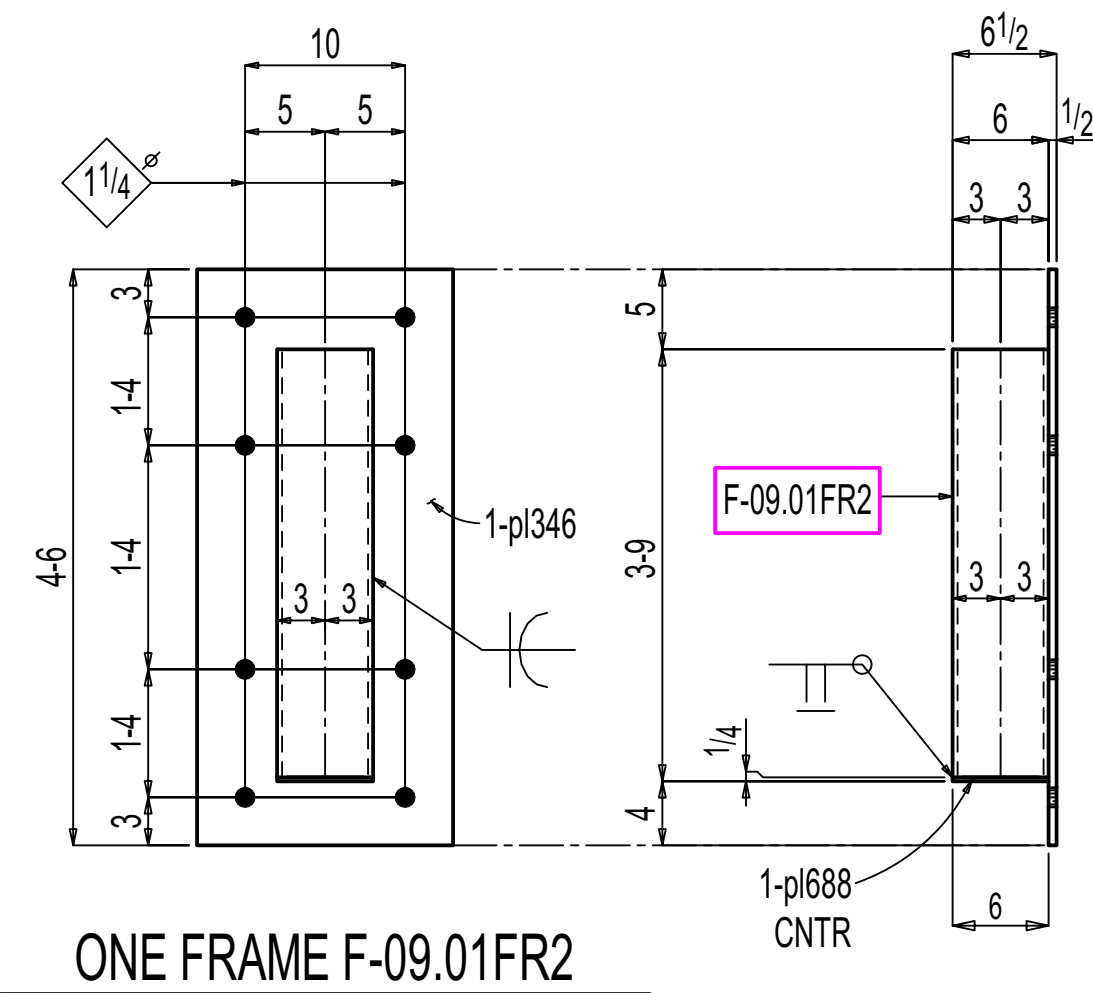


BILL OF MATERIAL							
LINE #	QTY	PC	MARK	DESCRIPTION	LENGTH	WEIGHT	ADVANCE
	TOTAL					TOTAL	MILL #
	ONE	F-09.01FR1		FRAME			
	1	F-09.01FR1		HSS6x2x5/16	4	89 1/16	A500C
	1	p347		PL1/2x9	5	6	A36
	1	p3034		PL1/4x2	0	6	A36
	ONE	F-09.01FR2		FRAME			
	1	F-09.01FR2		HSS6x6x5/16	3	81 1/16	A500C
	1	p346		PL1/2x16	4	6	A36
	1	p688		PL1/4x6	0	6	A36
	ONE	F-09.01FR3		FRAME			
	1	F-09.01FR3		HSS6x6x5/16	3	73 1/4	A500C
	1	hss319		HSS6x6x5/16	2	103 1/4	A500C
	1	hss320		HSS6x6x5/16	2	83 1/4	A500C
	1	p346		PL1/2x16	4	6	A36
	2	p688		PL1/4x6	0	6	A36
	ONE	F-09.01FR4		FRAME			
	1	F-09.01FR4		HSS6x6x5/16	3	83 1/4	A500C
	1	p346		PL1/2x16	4	6	A36
	1	p688		PL1/4x6	0	6	A36

Total weight : 923

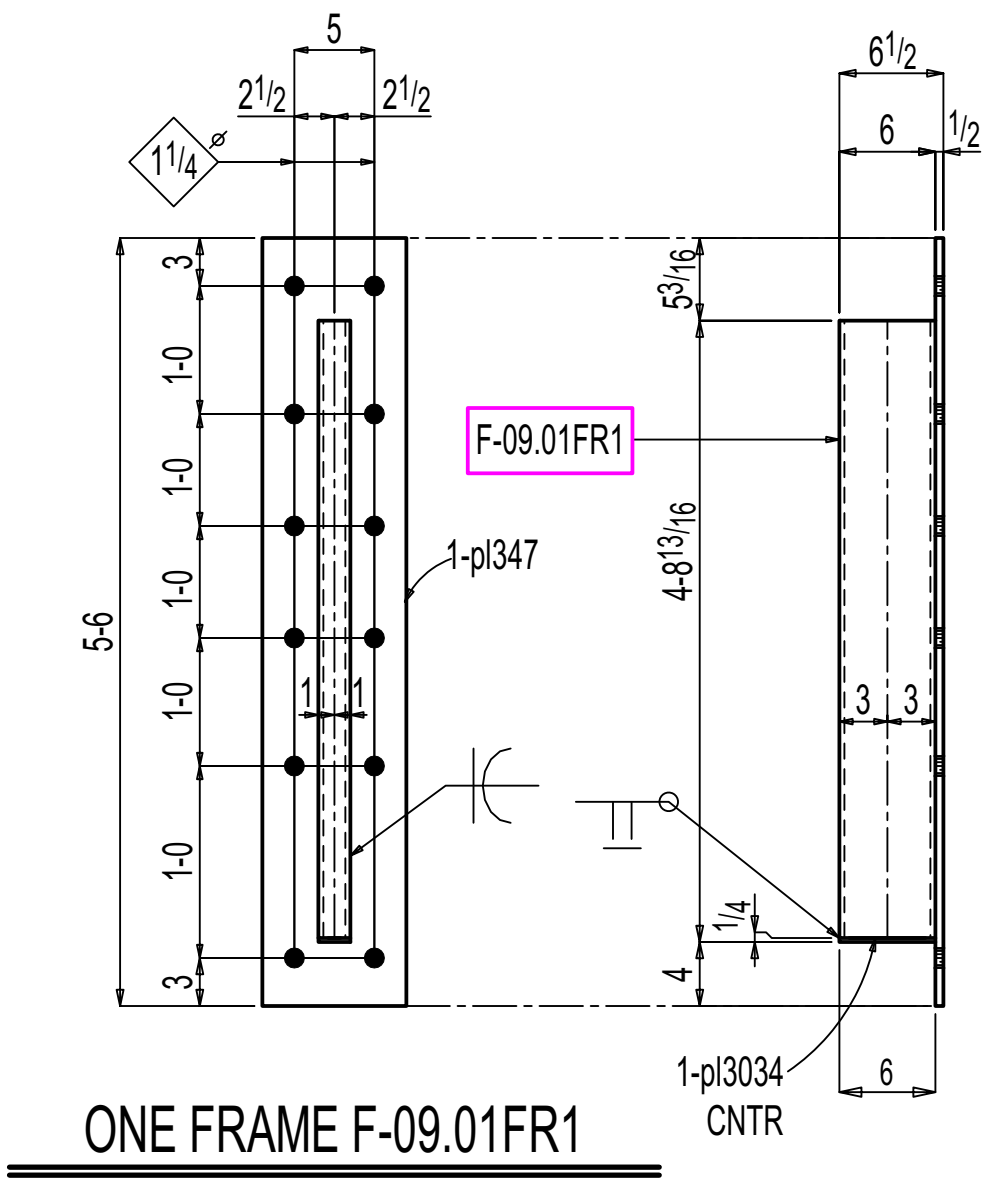

PAINT :NO PAINT
PREPARATION :SSPC-SP3

General Notes			
*Structural steel shall conform to ASTM-A992.			
*Structural SQR/RND,tubing conform to ASTM A500 Grade C			
*Pipe shall conform to ASTM A53, Grade B.			
*Channels, Angles and plates shall conform to A36.			
*All bolts shall be 3/4" High strength in accordance with ASTM A325 (UNO)			
*Welding Electrodes for Carbon steel :E70xx			
5	0	For Fabrication	11-14-2025
4	D	For Re-Approval	10-24-2025
3	C	For Re-Approval	09-19-2025
2	B	For Re-Approval	06-23-2025
1	A	For Approval	02-25-2025
# of Copies	Revision/ Issue	Destination	Date

IRON FABRICATION SERVICES, LLC.

3029 M. Street, NW, Suite 202
Washington, DC 20007
Tel: 202-800-5599
Fax: 202-478-0303

Project Name and Address
MARYLAND AVENUE
Location: **1250 MARYLAND AVENUE SW
WASHINGTON, DC 20024**

Contractor:
BALFOUR BEATTY

Approved for Fabrication by: Signature

Contract #	224009	Drawing #	F-09.01
Contract Item:	FRAME		
Ref:	SOW - 09: E-09.00 - E-09.02		
Date	01/ 23/ 2025	Drawing Title:	FRAME DETAIL
Scale	VARIES		