



BILL OF MATERIAL							
LINE #	QTY	PC	MARK	DESCRIPTION	LENGTH	REMARKS	WEIGHT
	TOTAL						TOTAL
							ADVANCE
	ONE	F-09.02FR1	FRAME				212
	1	F-09.02FR1	HSS6x6x ⁵ / ₁₆	3	8 ¹ / ₂	A500C	87
	1	p246	PL ¹ / ₂ x16	4	6	A36	123
	1	p688	PL ¹ / ₄ x6	0	6	A36	3
	ONE	F-09.02FR2	FRAME				394
	1	F-09.02FR2	HSS6x6x ⁵ / ₁₆	3	7 ³ / ₄	A500C	85
	1	hss379	HSS6x6x ⁵ / ₁₆	4	1 ¹ / ₁₆	A500C	95
	1	hss375	HSS6x6x ⁵ / ₁₆	3	8 ¹ / ₄	A500C	86
	1	p246	PL ¹ / ₂ x16	4	6	A36	123
	2	p688	PL ¹ / ₄ x6	0	6	A36	5
	ONE	F-09.02M1	PLATE				189
	1	F-09.02M1	PL1x18	2	1	A36	128
	1	p248	PL1x8	1	6	A36	41
	3	p287	PL ¹ / ₂ x7	0	7	A36	21
	ONE	F-09.02M2	HSS				153
	1	F-09.02M2	HSS6x6x ³ / ₈	5	5	A500C	149
	1	p2494	PL ¹ / ₄ x6	0	10	A36	4
	ONE	F-09.02M3	HSS				201
	1	F-09.02M3	HSS6x6x ³ / ₈	6	1	A500C	167
	1	a156	L5x5x ⁵ / ₁₆	0	10	A36	9
	1	p245	PL ¹ / ₂ x6	1	8	A36	17
	2	p688	PL ¹ / ₄ x6	0	6	A36	5
	2		3/4 Dia A325N	0	7 ¹ / ₂	+1HD WASH	3
	2		FIELD BOLTS				
			1/2 Dia HILTI K8-TZ2	0	7		
			EXPANSION ANCHOR		(5 ¹ / ₂ " EMBEDMENT)		
	ONE	F-09.02M4	PLATE				54
	1	F-09.02M4	PL ³ / ₄ x6	2	4 ¹ / ₂	A36	36
	2	p2380	PL ³ / ₄ x6	0	7	A36	18
	ONE	F-09.02M5	PLATE				117
	1	F-09.02M5	PL ⁵ / ₈ x22	2	6	A36	117
	6		FIELD BOLTS				
			3/4 Dia HILTI HAS V-36	0	8		
			w/ HILTI HIT HY-200 V3		(5" EMBEDMENT)		
			ADHESIVE				
	ONE	F-09.02M6	PLATE				30
	1	F-09.02M6	PL ¹ / ₂ x9	1	4	A36	20
	1	a3197	L6x6x ³ / ₈	0	8	A36	10
	2		FIELD BOLTS				
			3/4 Dia HILTI HAS V-36	0	10		
			w/ HILTI HIT HY-200 V3		(8" EMBEDMENT)		
			ADHESIVE				


Total weight : 1350

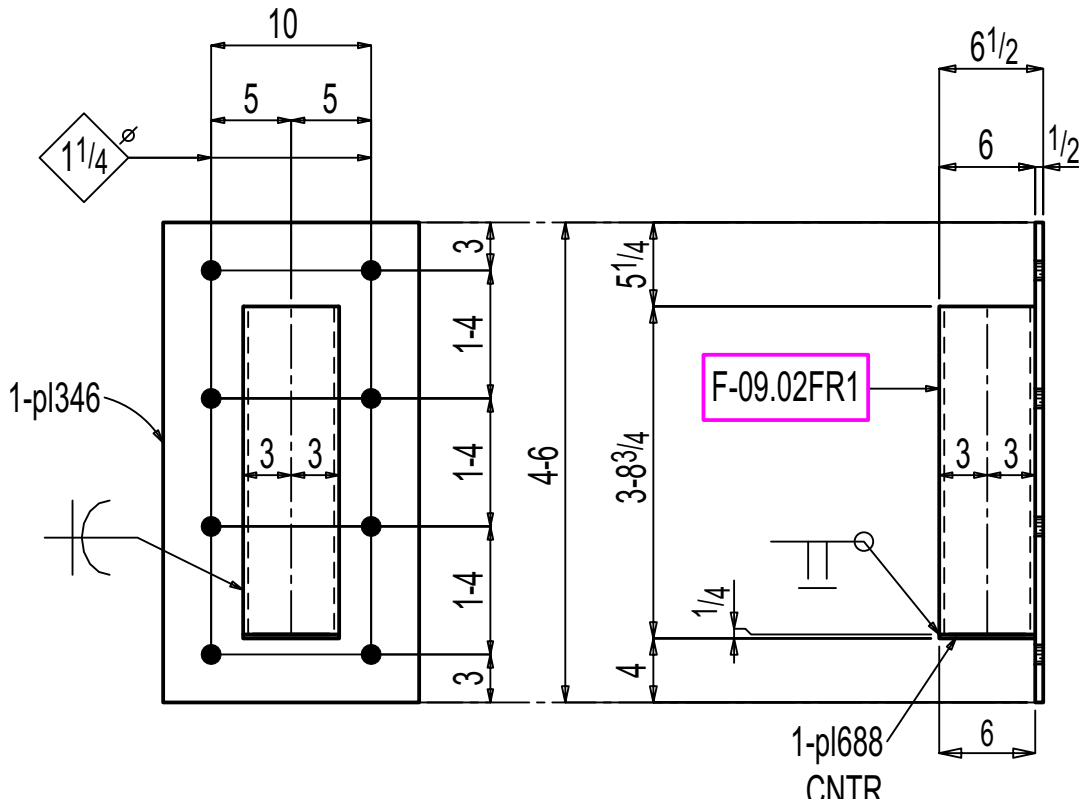


ONE FRAME F-09.02FR1

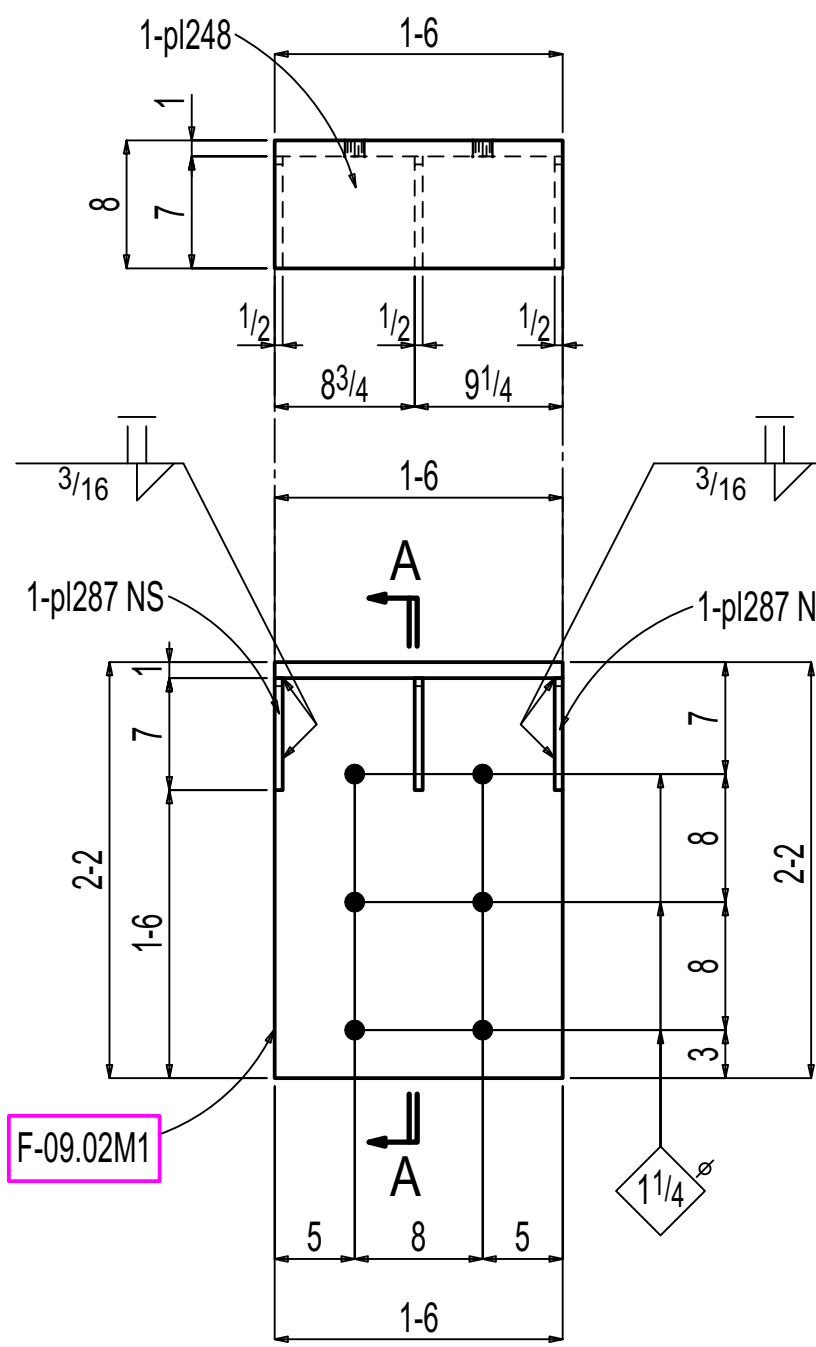


ONE PLATE F-09.02M1

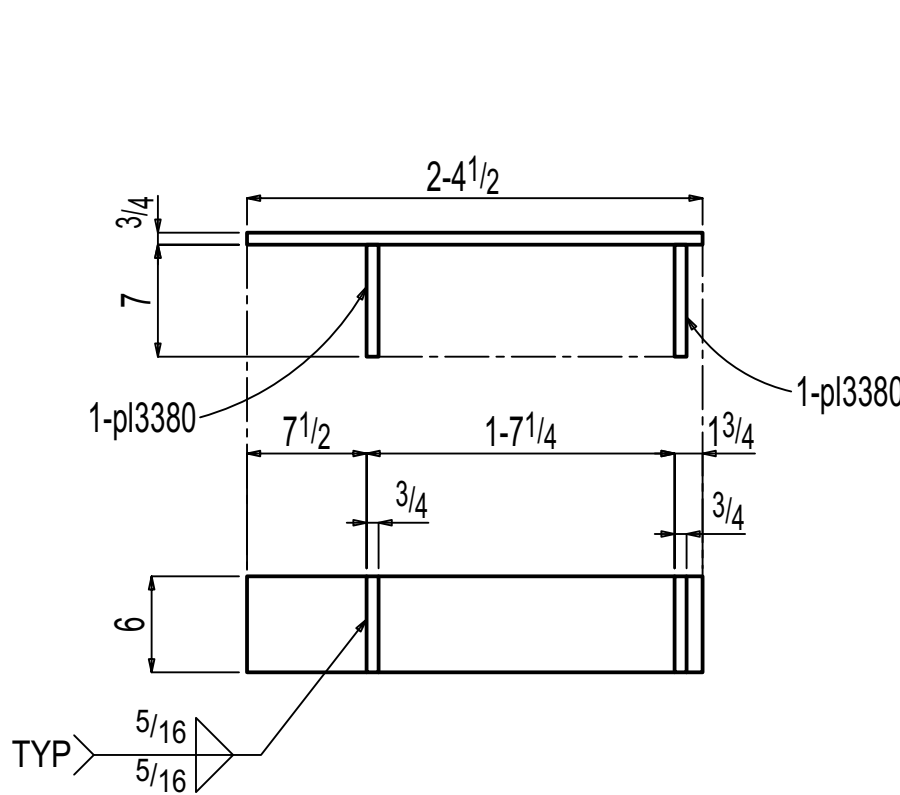


ONE PLATE F-09.02M4

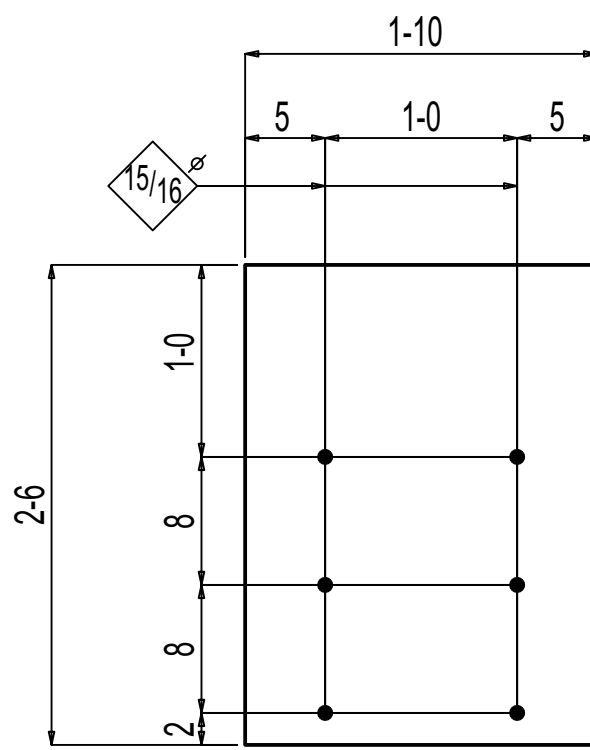

ONE PLATE F-09.02M5

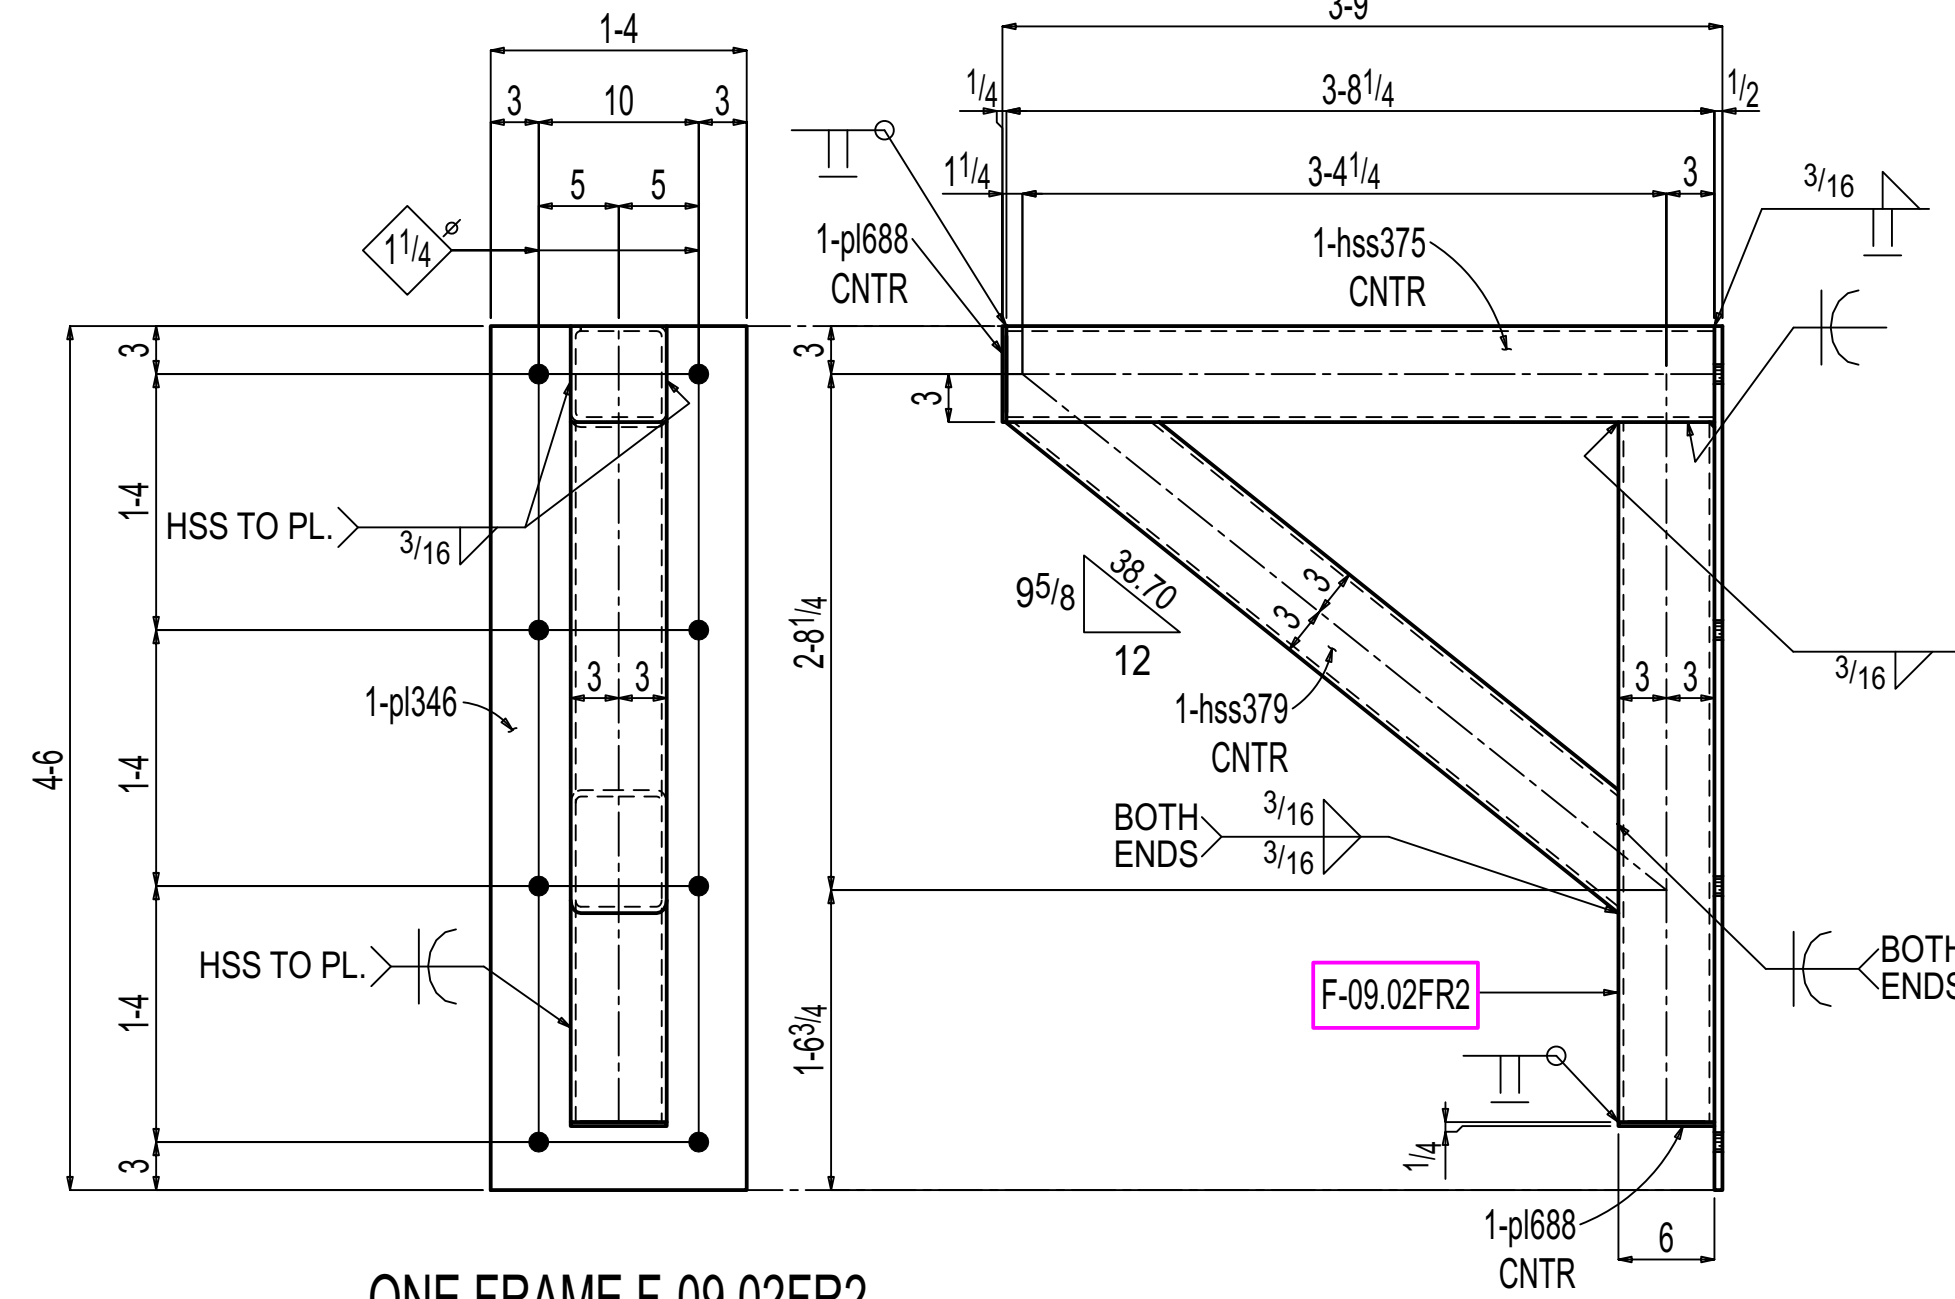


ONE FRAME F-09.02FR2

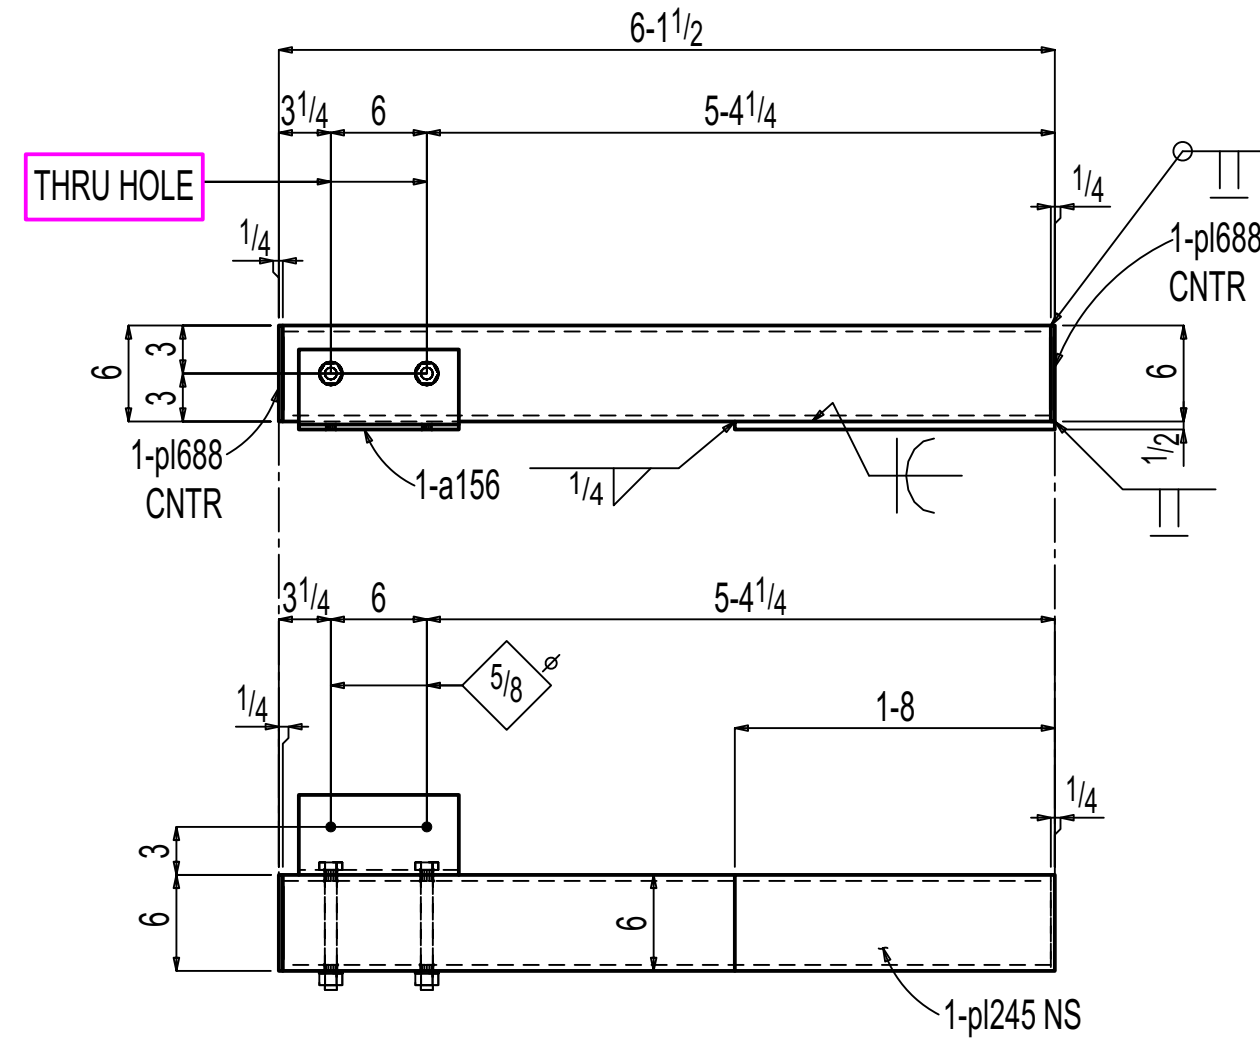

ONE HSS F-09.02M3

SHOP BOLTS:
2-3/4Diax7 1/2 A325N

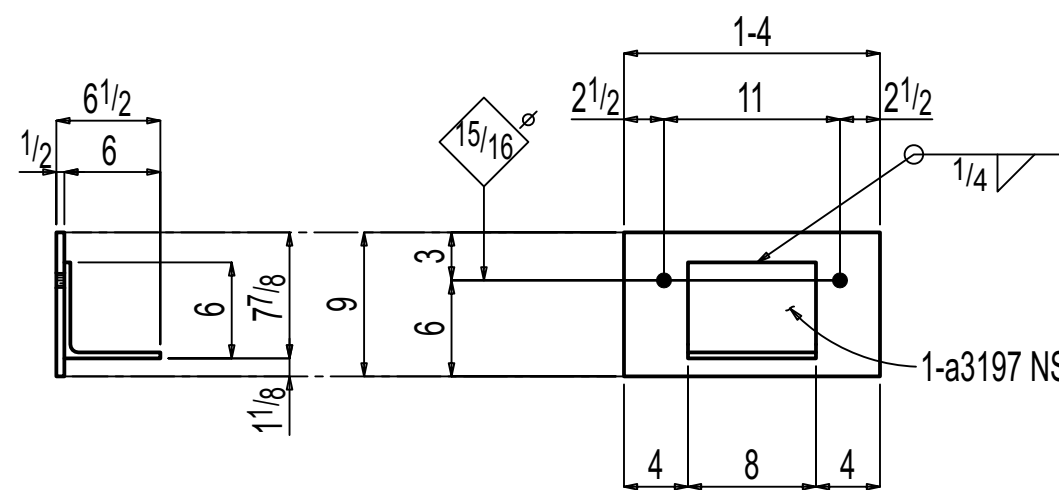

ONE PLATE F-09.02M6

PAINT PREPARATION :NO PAINT
PREPARATION :SSPC-SP3

General Notes			
*Structural steel shall conform to ASTM-A992.			
*Structural SQR/RND,tubing conform to ASTM A500 Grade C			
*Pipe shall conform to ASTM A53, Grade B.			
*Channels, Angles and plates shall conform to A36.			
*All bolts shall be 3/4" High strength in accordance with ASTM A325 (UNO)			
*Welding Electrodes for Carbon steel :E70xx			
5	0	For Fabrication	11-14-2025
4	D	For Re-Approval	10-24-2025
3	C	For Re-Approval	09-19-2025
2	B	For Re-Approval	06-23-2025
1	A	For Approval	02-25-2025
# of Copies	Revision/ Issue	Destination	Date

IRON FABRICATION SERVICES, LLC.

3029 M. Street, NW, Suite 202
Washington, DC 20007
Tel: 202-800-5599
Fax: 202-478-0303

Project Name and Address
MARYLAND AVENUE

Location: **1250 MARYLAND AVENUE SW
WASHINGTON, DC 20024**

Contractor:
BALFOUR BEATTY

Approved for Fabrication by: Signature

Contract # **224009** Drawing # **F-09.02**

Contract Item: **FRAME**

Ref:
SOW - 09: E-09.00 - E-09.02

Date **01/ 23/ 2025** Drawing Title:
Scale **VARIES** **FRAME & MISCELLANEOUS
DETAIL**