



BILL OF MATERIAL							
LINE #	QTY	PC	MARK	DESCRIPTION	LENGTH	REMARKS	WEIGHT TOTAL ADVANCE MILL #
	ONE	F-09.03C1		COLUMN			329
	1	F-09.03C1	HSS6x6x ³ / ₈		10 4	A500C	284
	1	p11965	PL1 ¹ / ₂ x7		1 6	A36	45
				FIELD BOLTS			
	2			³ / ₄ Dia HILTI HAS V-36	0 8	(³ / ₄ " EMBEDMENT)	
				w/ HILTI HIT HY-200 EPOXY			
	ONE	F-09.03C2		COLUMN			313
	1	F-09.03C2	HSS6x6x ³ / ₈		9 10 ³ / ₄	A500C	272
	2	p13368	PL ³ / ₈ x6 ¹ / ₂		1 6	A36	41
				FIELD BOLTS			
	2			³ / ₄ Dia HILTI Kwik HUS-EZ	0 4 ¹ / ₂	(² / ₃ " EMBEDMENT)	
				SCREW ANCHOR			
	ONE	F-09.03B1		BEAM			716
	1	F-09.03B1	HSS10x8x ¹ / ₄		18 9 ¹ / ₈	A500C	548
	1	bp122	PL ¹ / ₄ x9 ¹ / ₂		10 0	BENT A36	81
	1	bp123	PL ¹ / ₄ x9 ¹ / ₂		8 10 ³ / ₄	BENT A36	72
	2	p13418	PL ¹ / ₄ x8		0 10	A36	11
	1	p13489	PL ¹ / ₄ x4		1 1	A36	4
	ONE	F-09.03B2		BEAM			863
	1	F-09.03B2	HSS10x8x ³ / ₁₆		19 4 ⁷ / ₈	A500C	701
	2	p13526	PL ¹ / ₄ x8		0 10	A36	11
	1	fb25	FL ¹ / ₄ x9 ³ / ₁₆		7 11 ³ / ₄	A36	35
	1	fb37	FL ¹ / ₄ x9 ³ / ₁₆		3 4 ¹ / ₄	A36	17
	1	fb26	FL ¹ / ₄ x9 ³ / ₁₆		8 0	A36	28
	1	p13532	PL ¹ / ₄ x4		1 4 ¹ / ₈	A36	5
	1	p1443	PL ¹ / ₄ x4		1 3 ³ / ₄	A36	4
	1	fb143	FL ¹ / ₄ x9 ³ / ₁₆		8 0	A36	26
	1	fb154	FL ¹ / ₄ x9 ³ / ₁₆		7 11 ³ / ₈	A36	25
	1	fb15	FL ¹ / ₄ x9 ³ / ₁₆		3 3 ⁵ / ₁₆	A36	11

Total weight : 2221

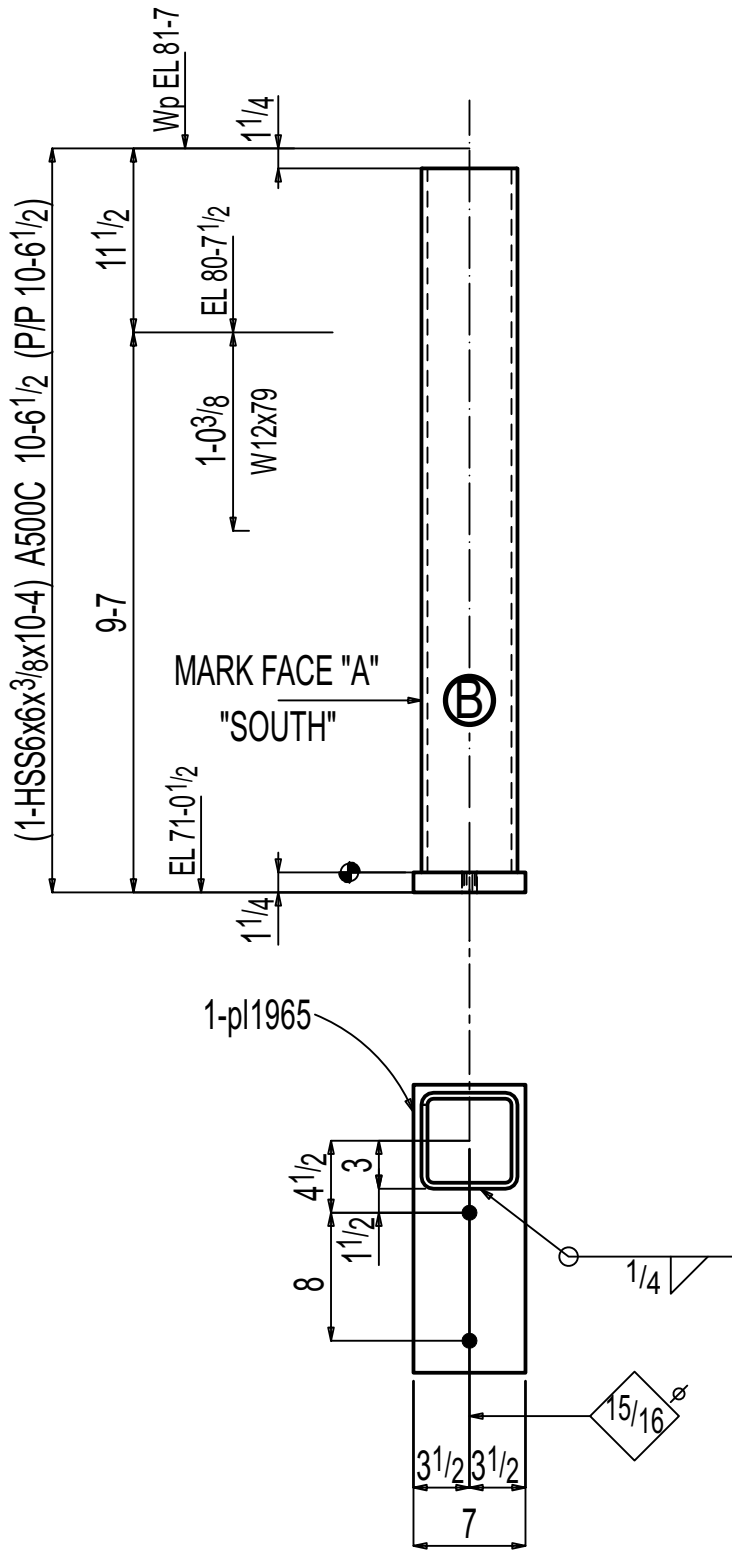


ONE COLUMN F-09.03C1

AT GRID:
EE & A

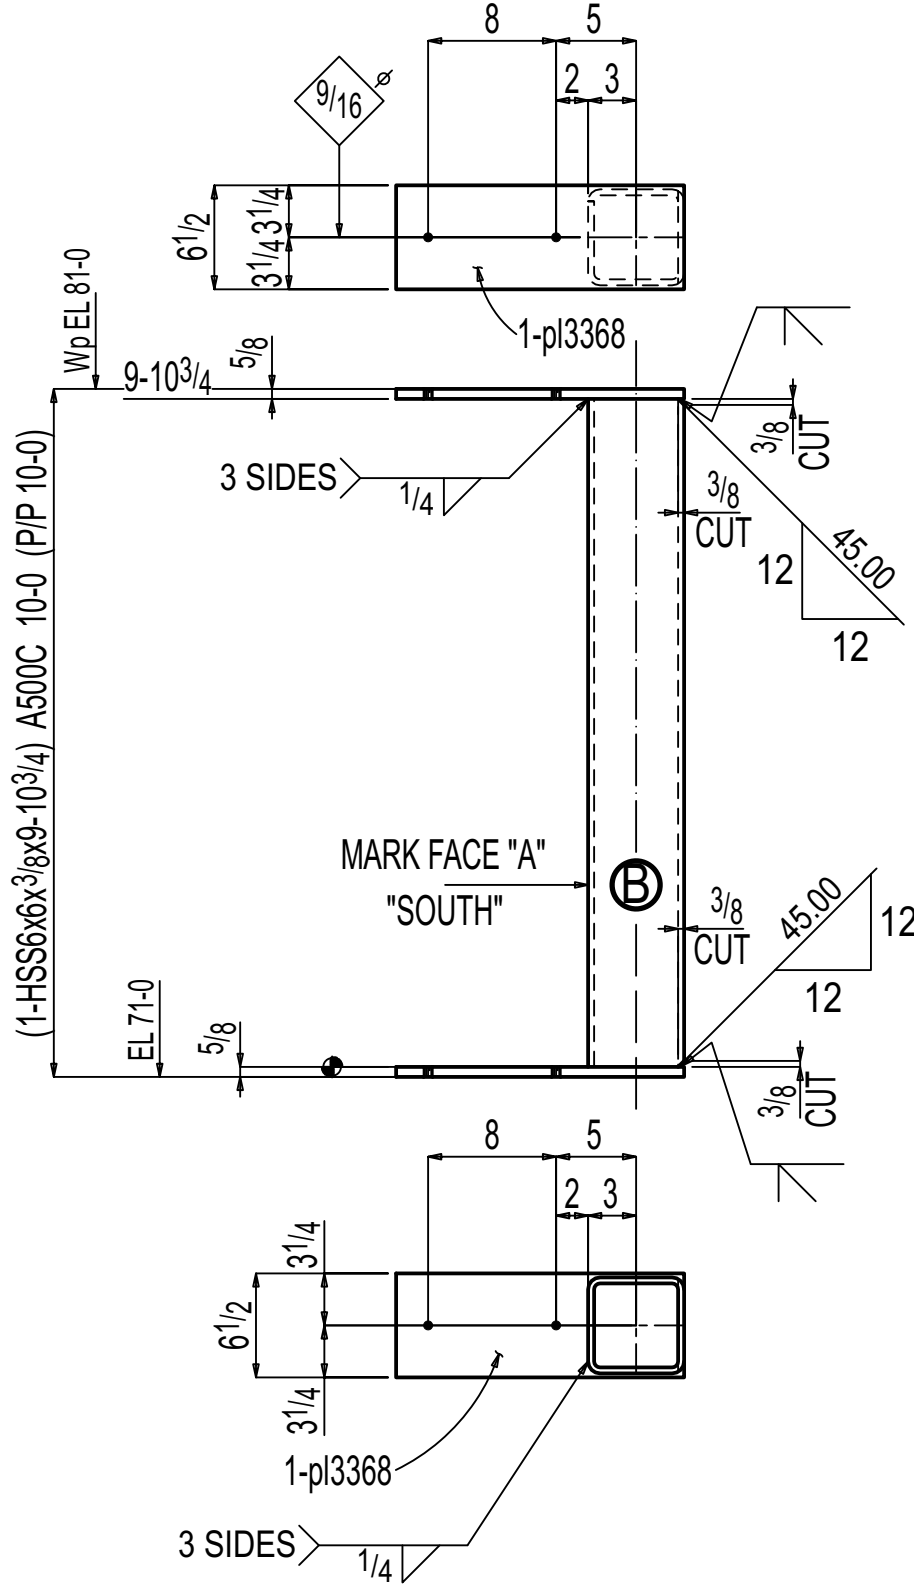


ONE COLUMN F-09.03C2


AT GRID:
AA & K

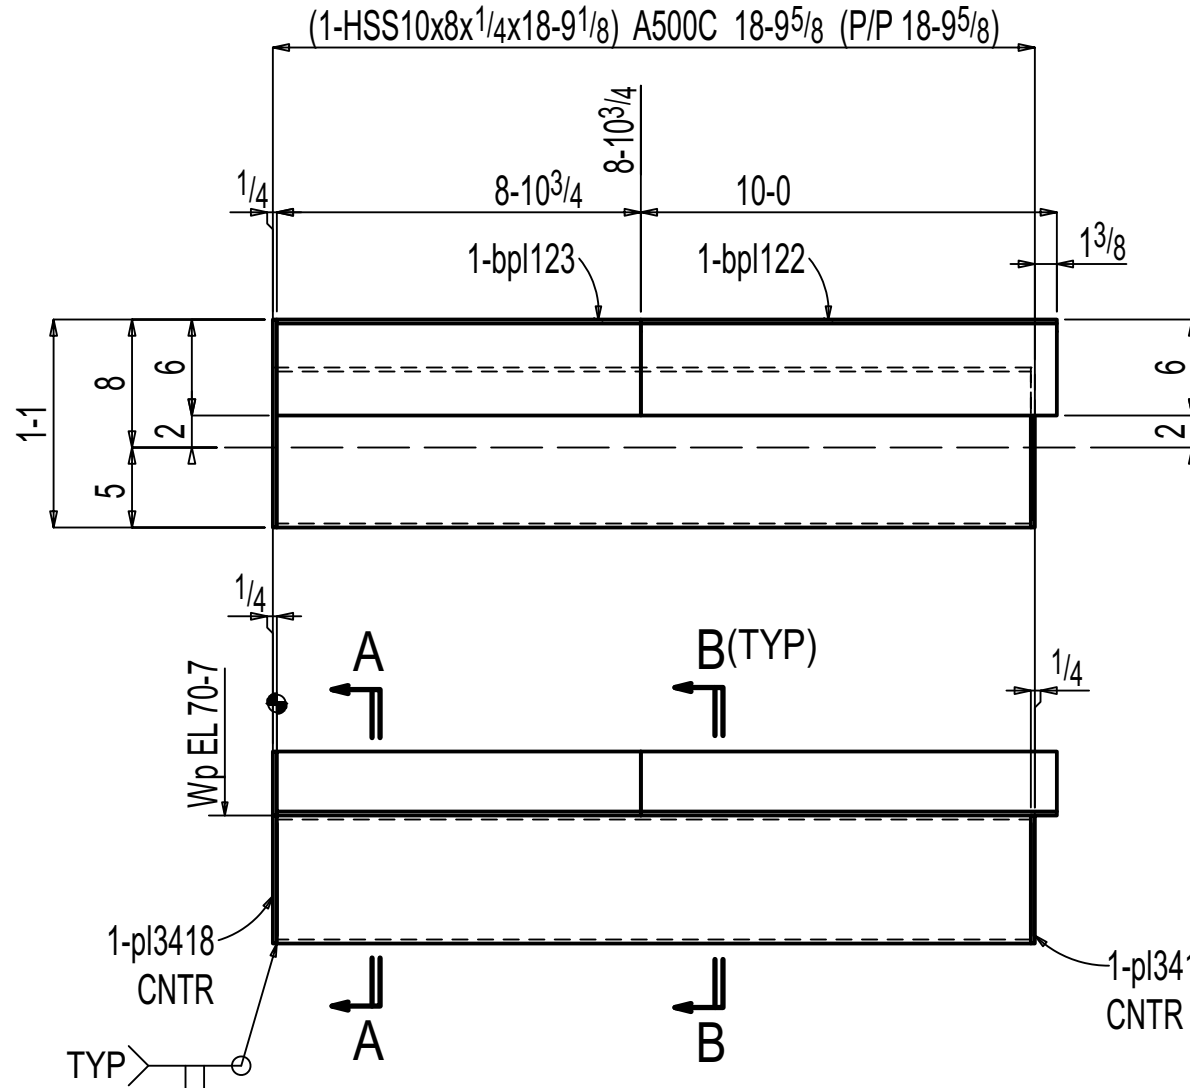

ONE BEAM F-09.03B1

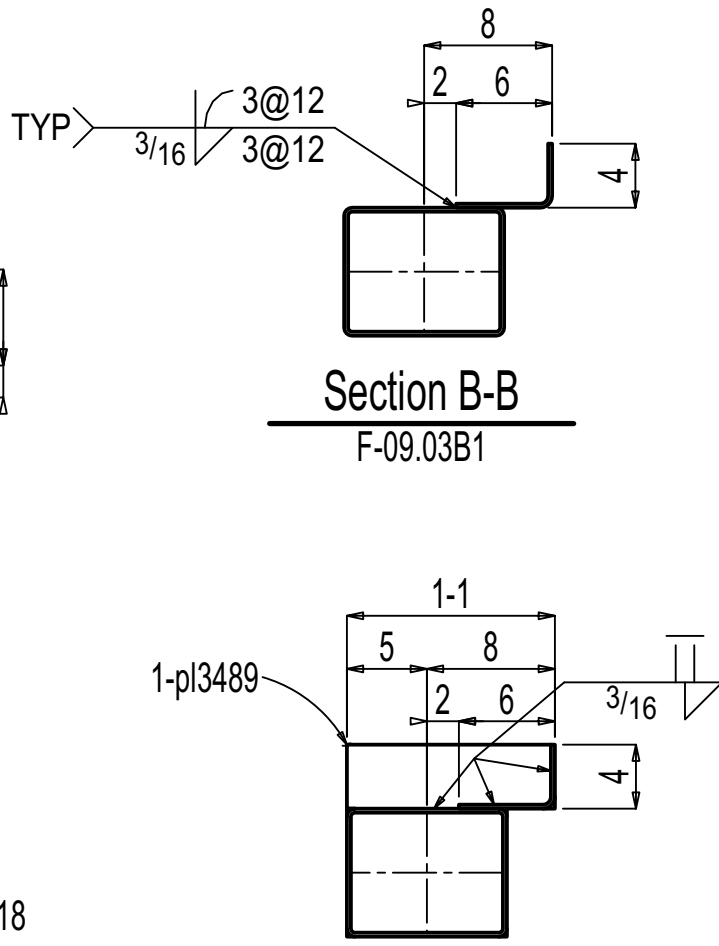


Section A-A
F-09.03B1

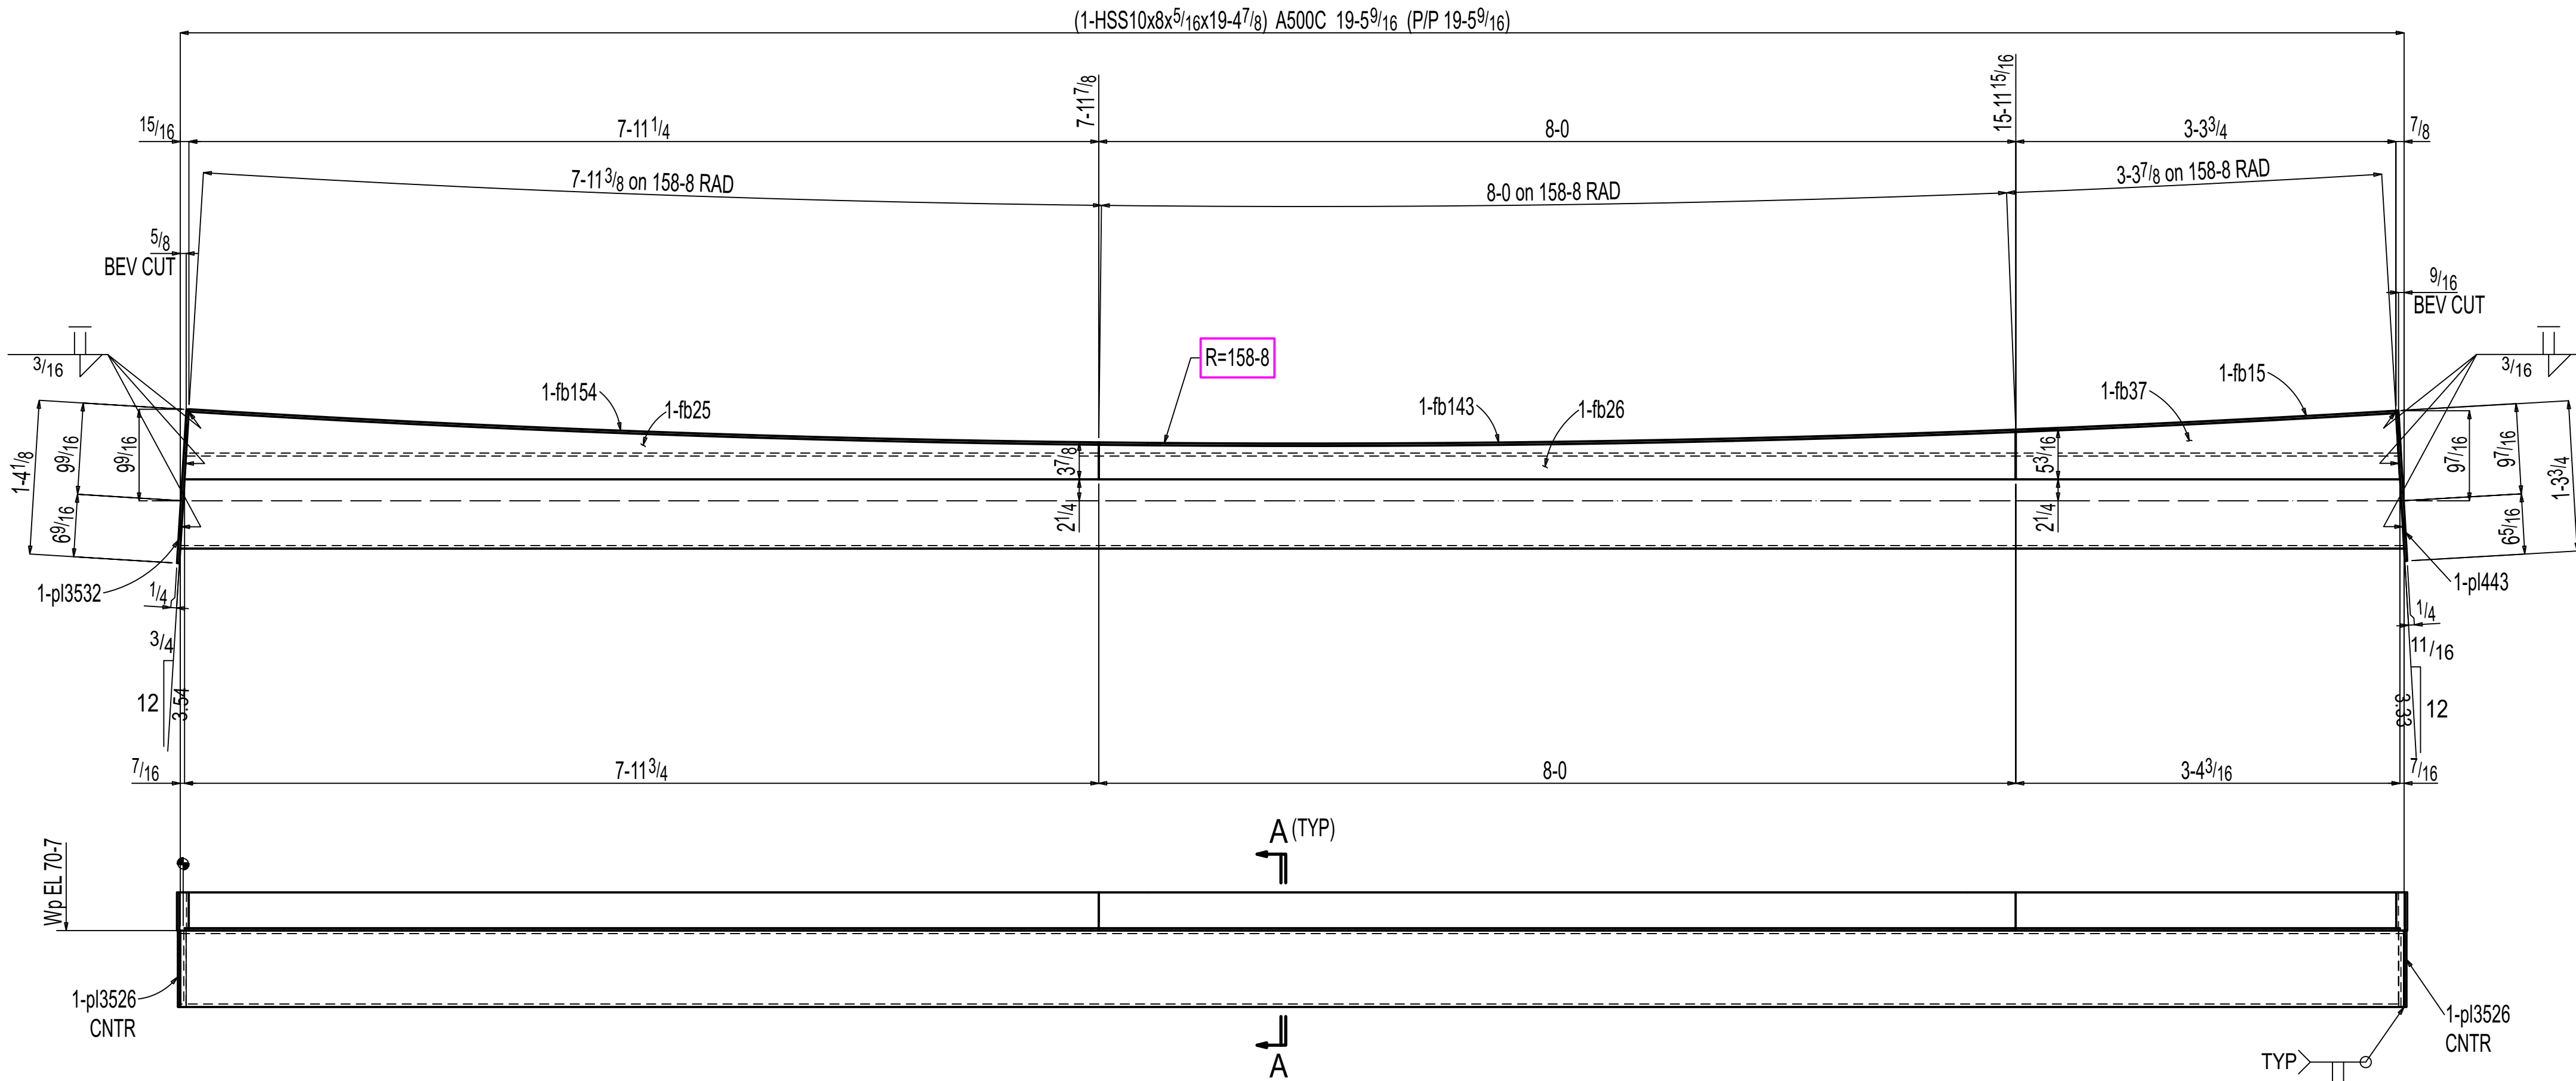

ONE BEAM F-09.03B2

AT GRID:
A

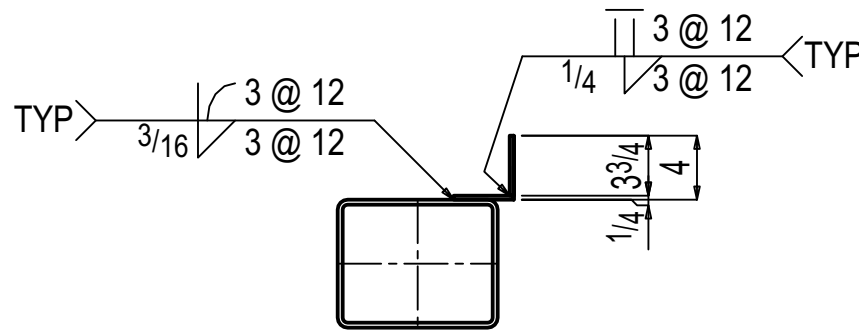

Section A-A
F-09.03B2

PAINT PREPARATION :NO PAINT
:SSPC-SP3

General Notes			
*Structural steel shall conform to ASTM-A992.			
*Structural SQR/RND,tubing conform to ASTM A500 Grade C			
*Pipe shall conform to ASTM A53, Grade B.			
*Channels, Angles and plates shall conform to A36.			
*All bolts shall be ³ / ₄ " High strength in accordance with ASTM A325 (UNO)			
*Welding Electrodes for Carbon steel :E70xx			
5	0	For Fabrication	11-14-2025
4	D	For Re-Approval	10-24-2025
3	C	For Re-Approval	09-19-2025
2	B	For Re-Approval	06-23-2025
1	A	For Approval	02-25-2025
# of Copies	Revision/ Issue	Destination	Date

IRON FABRICATION SERVICES, LLC.

3029 M. Street, NW, Suite 202
Washington, DC 20007
Tel: 202-800-5599
Fax: 202-478-0303

Project Name and Address
MARYLAND AVENUE

Location: **1250 MARYLAND AVENUE SW
WASHINGTON, DC 20024**

Contractor:
BALFOUR BEATTY

Approved for Fabrication by: Signature

Contract # **224009** Drawing # **F-09.03**

Contract Item: **BEAM**

Ref:
SOW - 09: E-09.00 - E-09.02

Date **01/ 23/ 2025** Drawing Title: **BEAM & COLUMN DETAIL**
Scale VARIES