
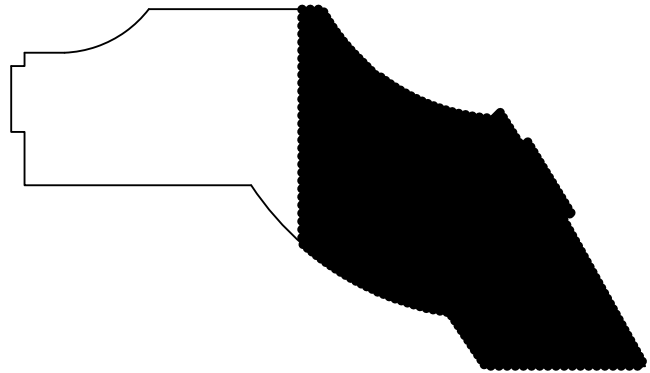


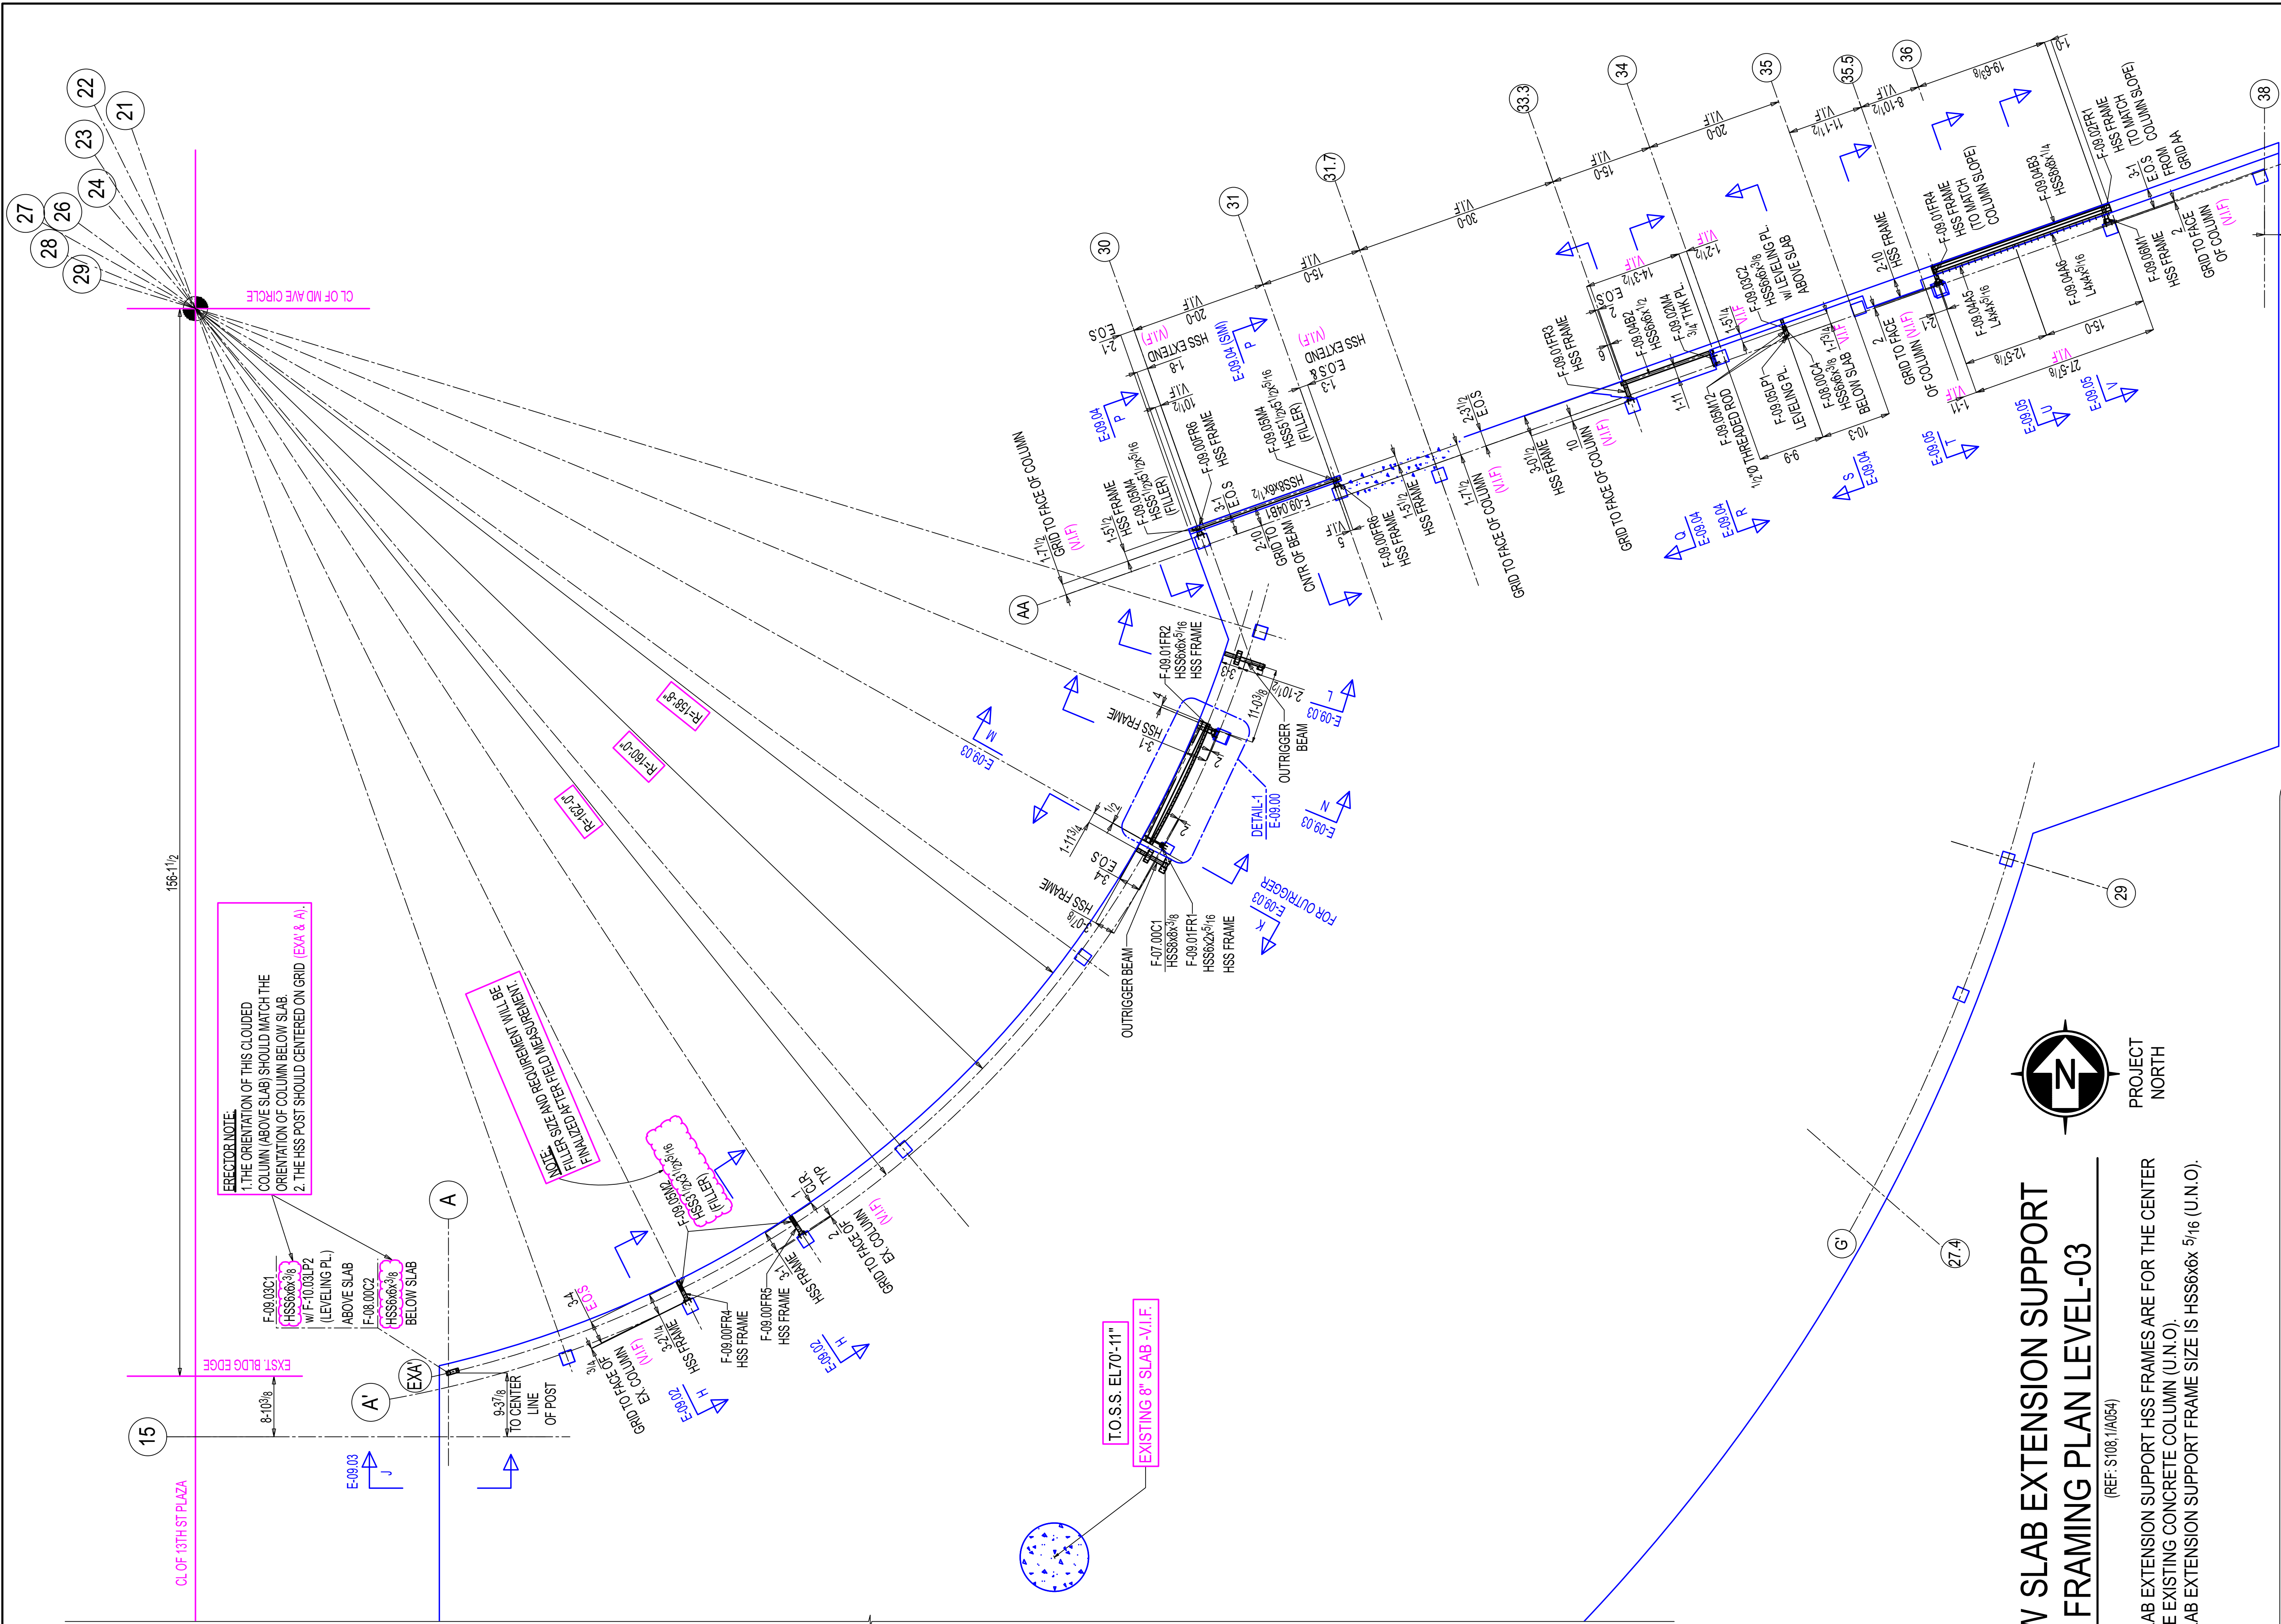

KEY PLAN

General Notes

- *Structural steel shall conform to ASTM-A992.
- *Structural SQR/RND tubing conform to ASTM A500 Grade C.
- *Pipe shall conform to ASTM A53, Grade B.
- *Channels, Angles and plates shall conform to A36.
- *All bolts shall be 3/4" High strength in accordance with ASTM A325 (UNO).
- *Welding Electrodes for Carbon steel :E70xx

# of Copies	Revision/ Issue	Destination	Date
3	0	For Construction	11-14-2025
2	B	For Re-Approval	10-24-2025
1	A	For Approval	09-19-2025

IRON FABRICATION SERVICES, LLC.

3029 M. Street, NW, Suite 202
Washington, DC 20007
Tel: 202-800-5599
Fax: 202-478-0303

Project Name and Address
MARYLAND AVENUE

Location: **1250 MARYLAND AVENUE SW
WASHINGTON, DC 20024**

Contractor:
BALFOUR BEATTY

Approved for Fabrication by: Signature

Contract # **224009** Drawing # **E-09.00A**

Contract Item: **LEVEL-03
SLAB EXTENSION**

Ref:
SOW-09: (S108,1/A054)

Date
01/20/2025
Scale
VARIES


Drawing Title:
**SOW #09 LEVEL-03 NEW
SLAB EXTENSION SUPPORT
FRAMING PLAN**

NEW SLAB EXTENSION SUPPORT
FRAMING PLAN LEVEL-03

(REF: S108,1/A054)

NOTE:

- ALL SLAB EXTENSION SUPPORT HSS FRAMES ARE FOR THE CENTER OF THE EXISTING CONCRETE COLUMN (U.N.O.).
- ALL SLAB EXTENSION SUPPORT FRAME SIZE IS HSS6x6x 5/16 (U.N.O.).

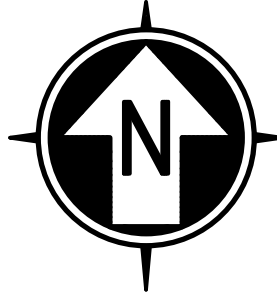

PROJECT
NORTH