


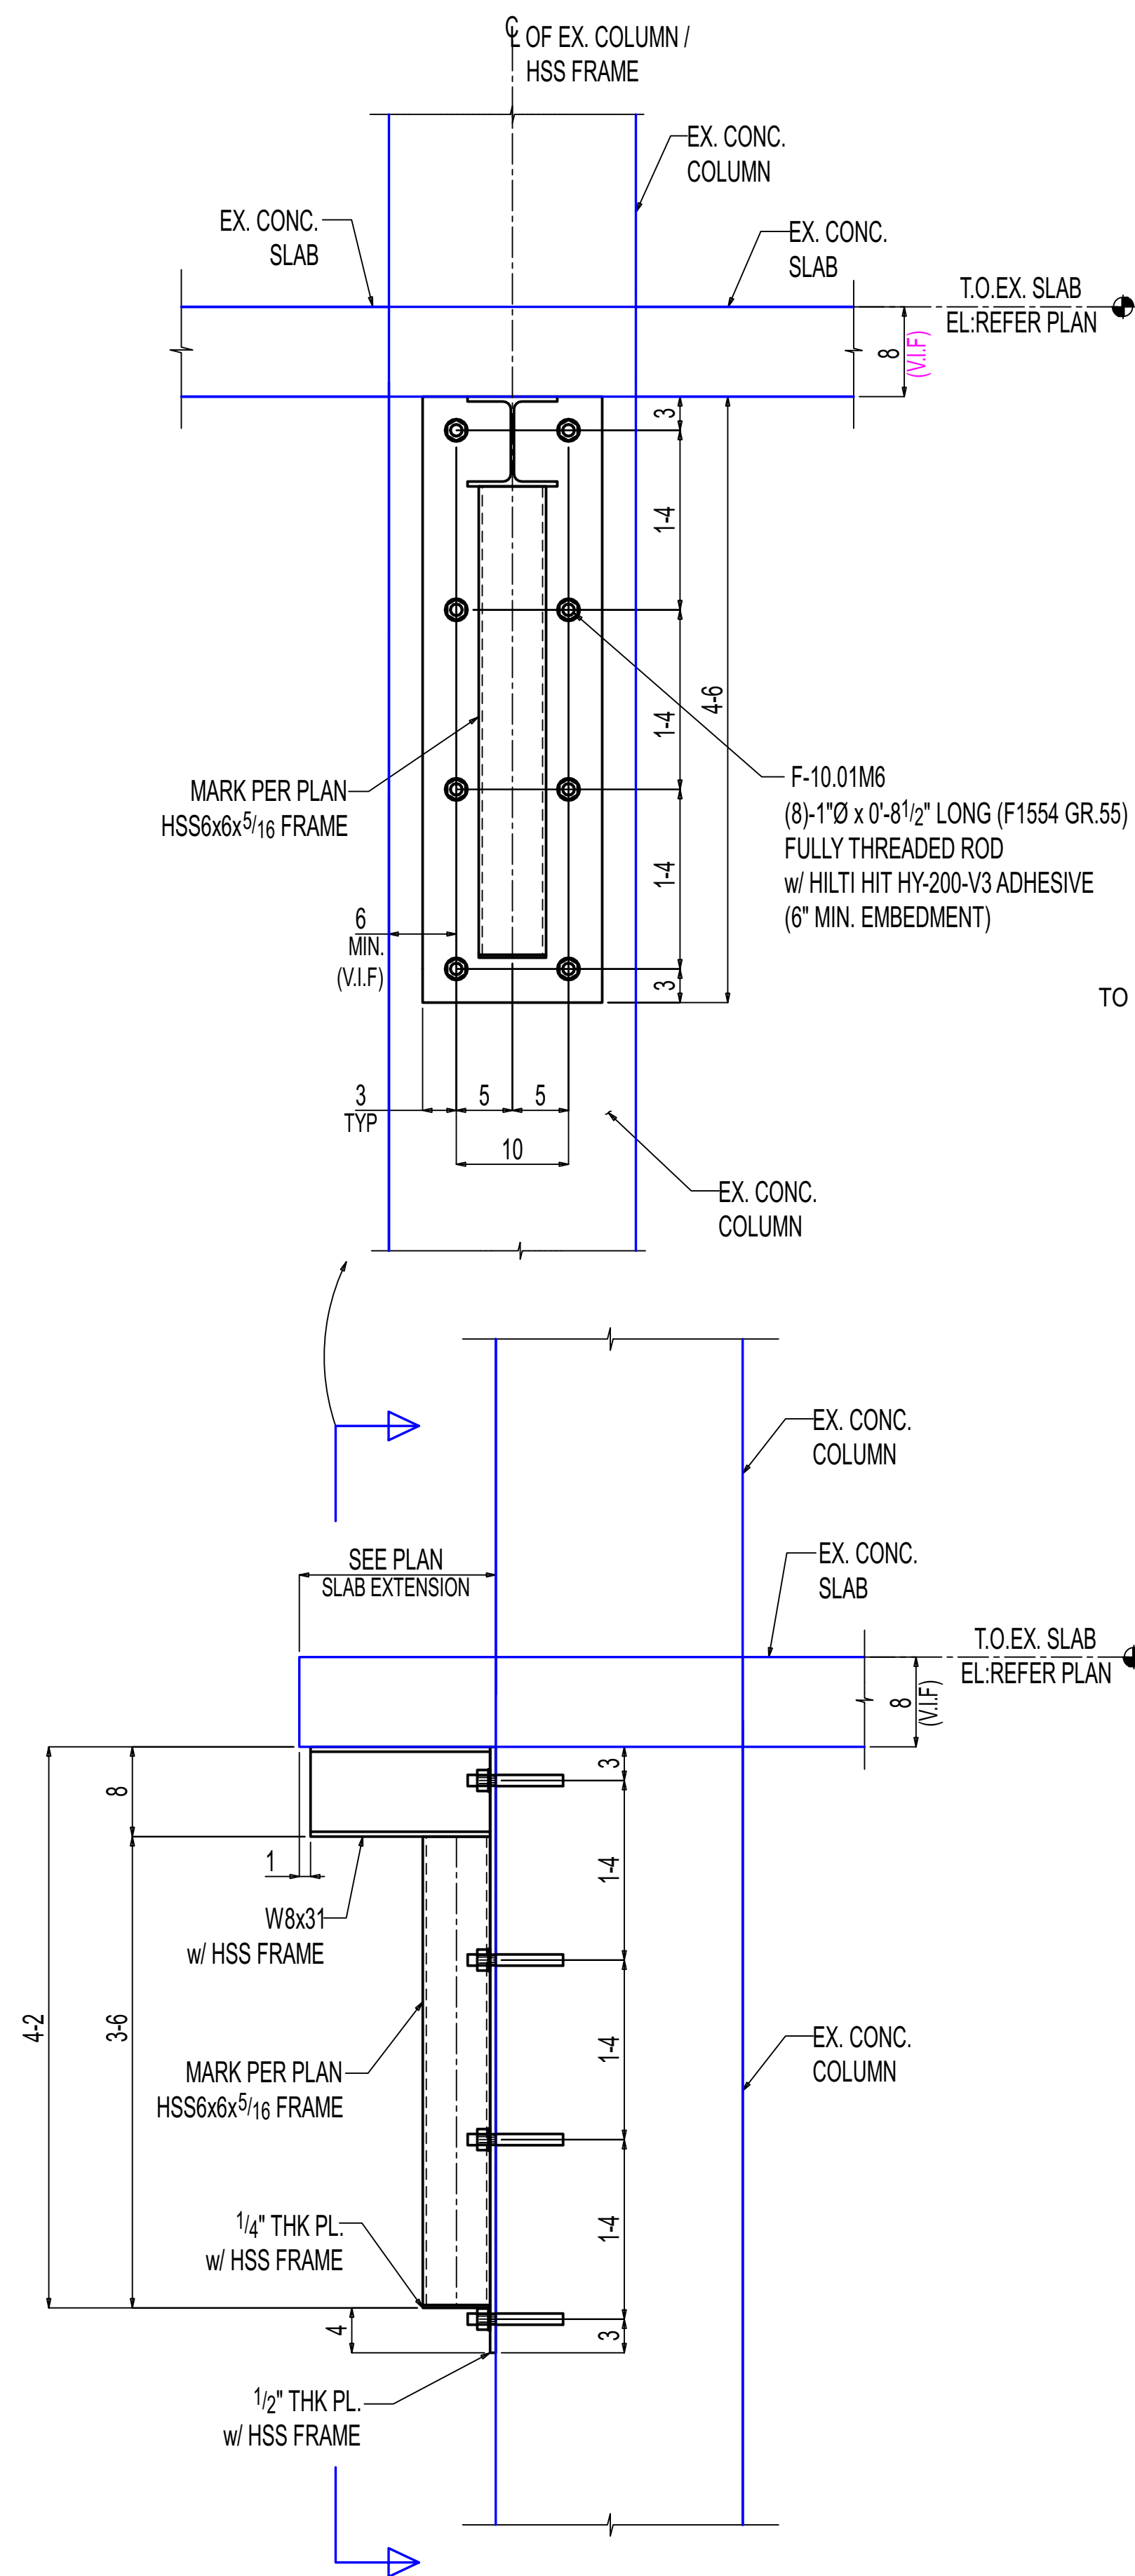


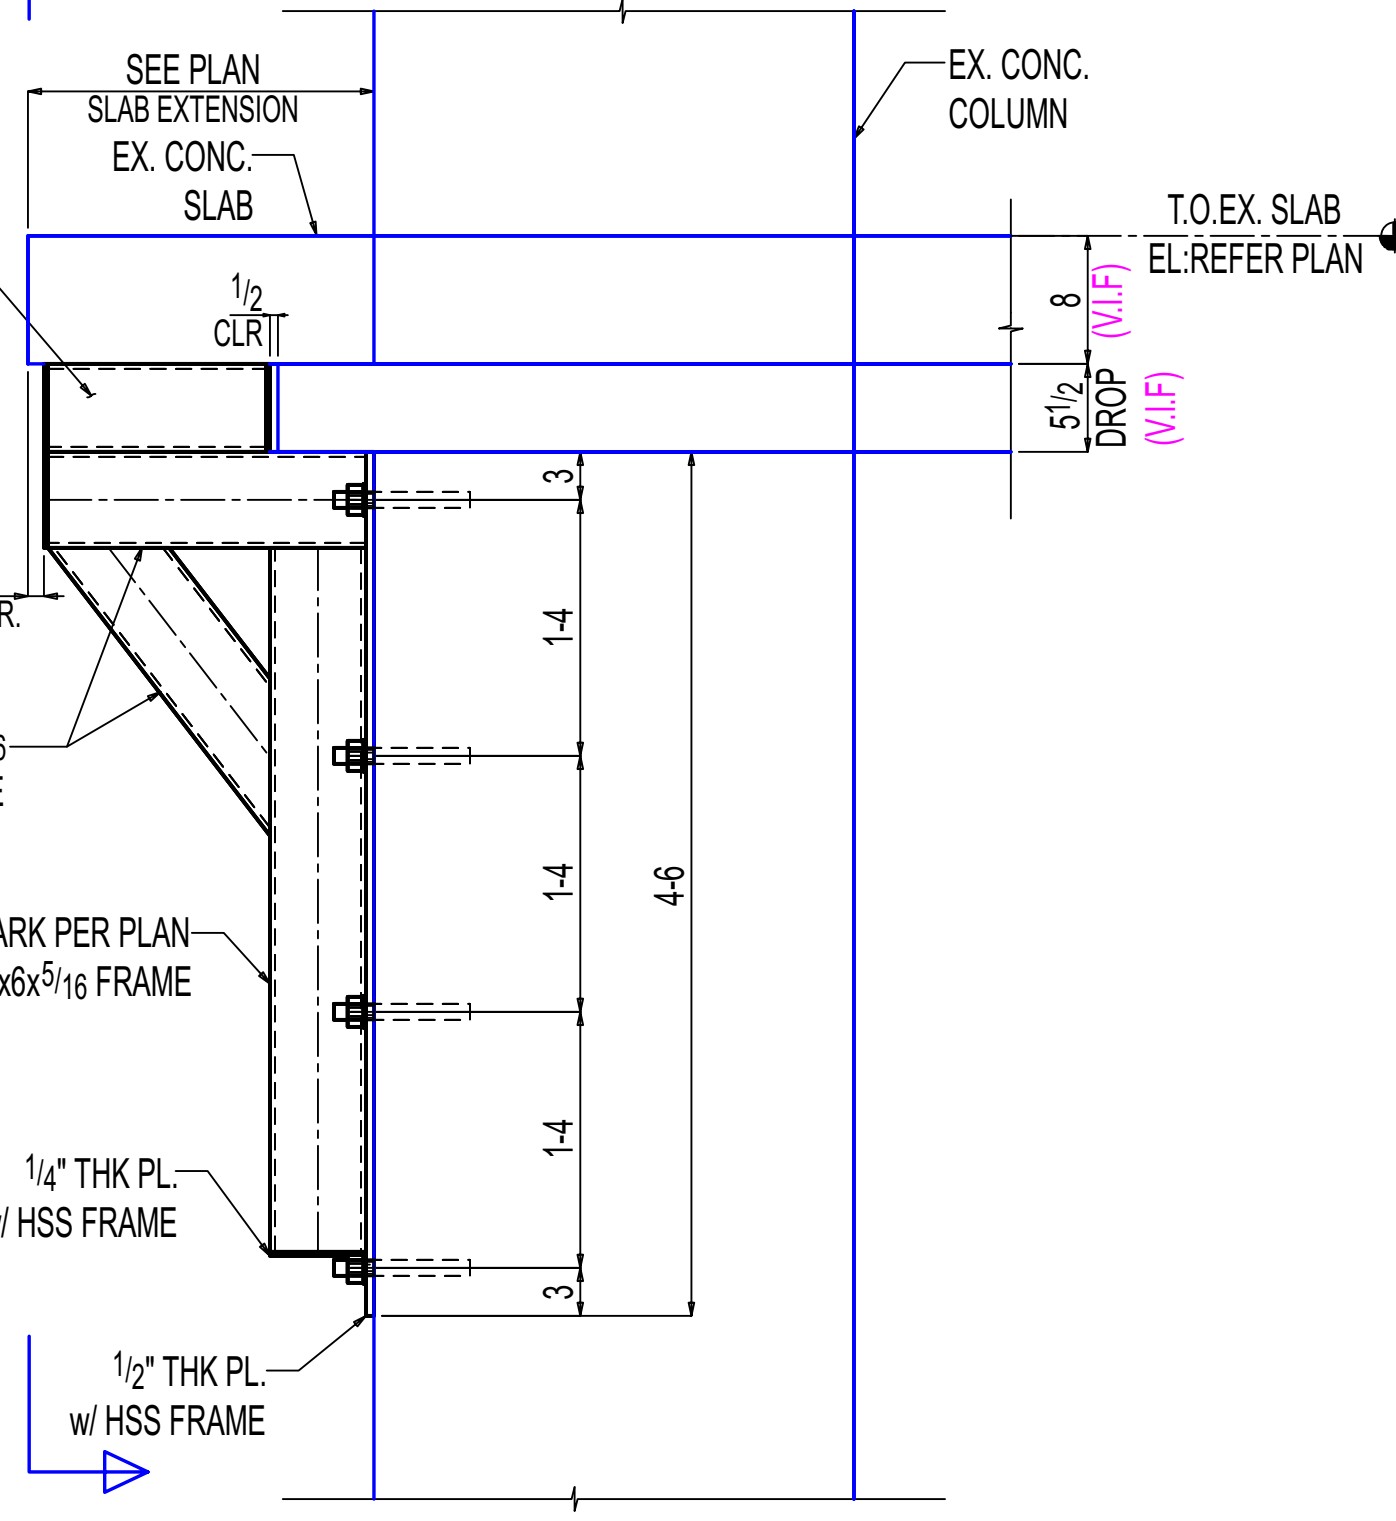

A-A
(NEW SLAB EXTENSION SUPPORT 1'-6" TO 3'-1")
E-10.00
(REF:11/S314)
OTHERS NOT SHOWN FOR CLARITY

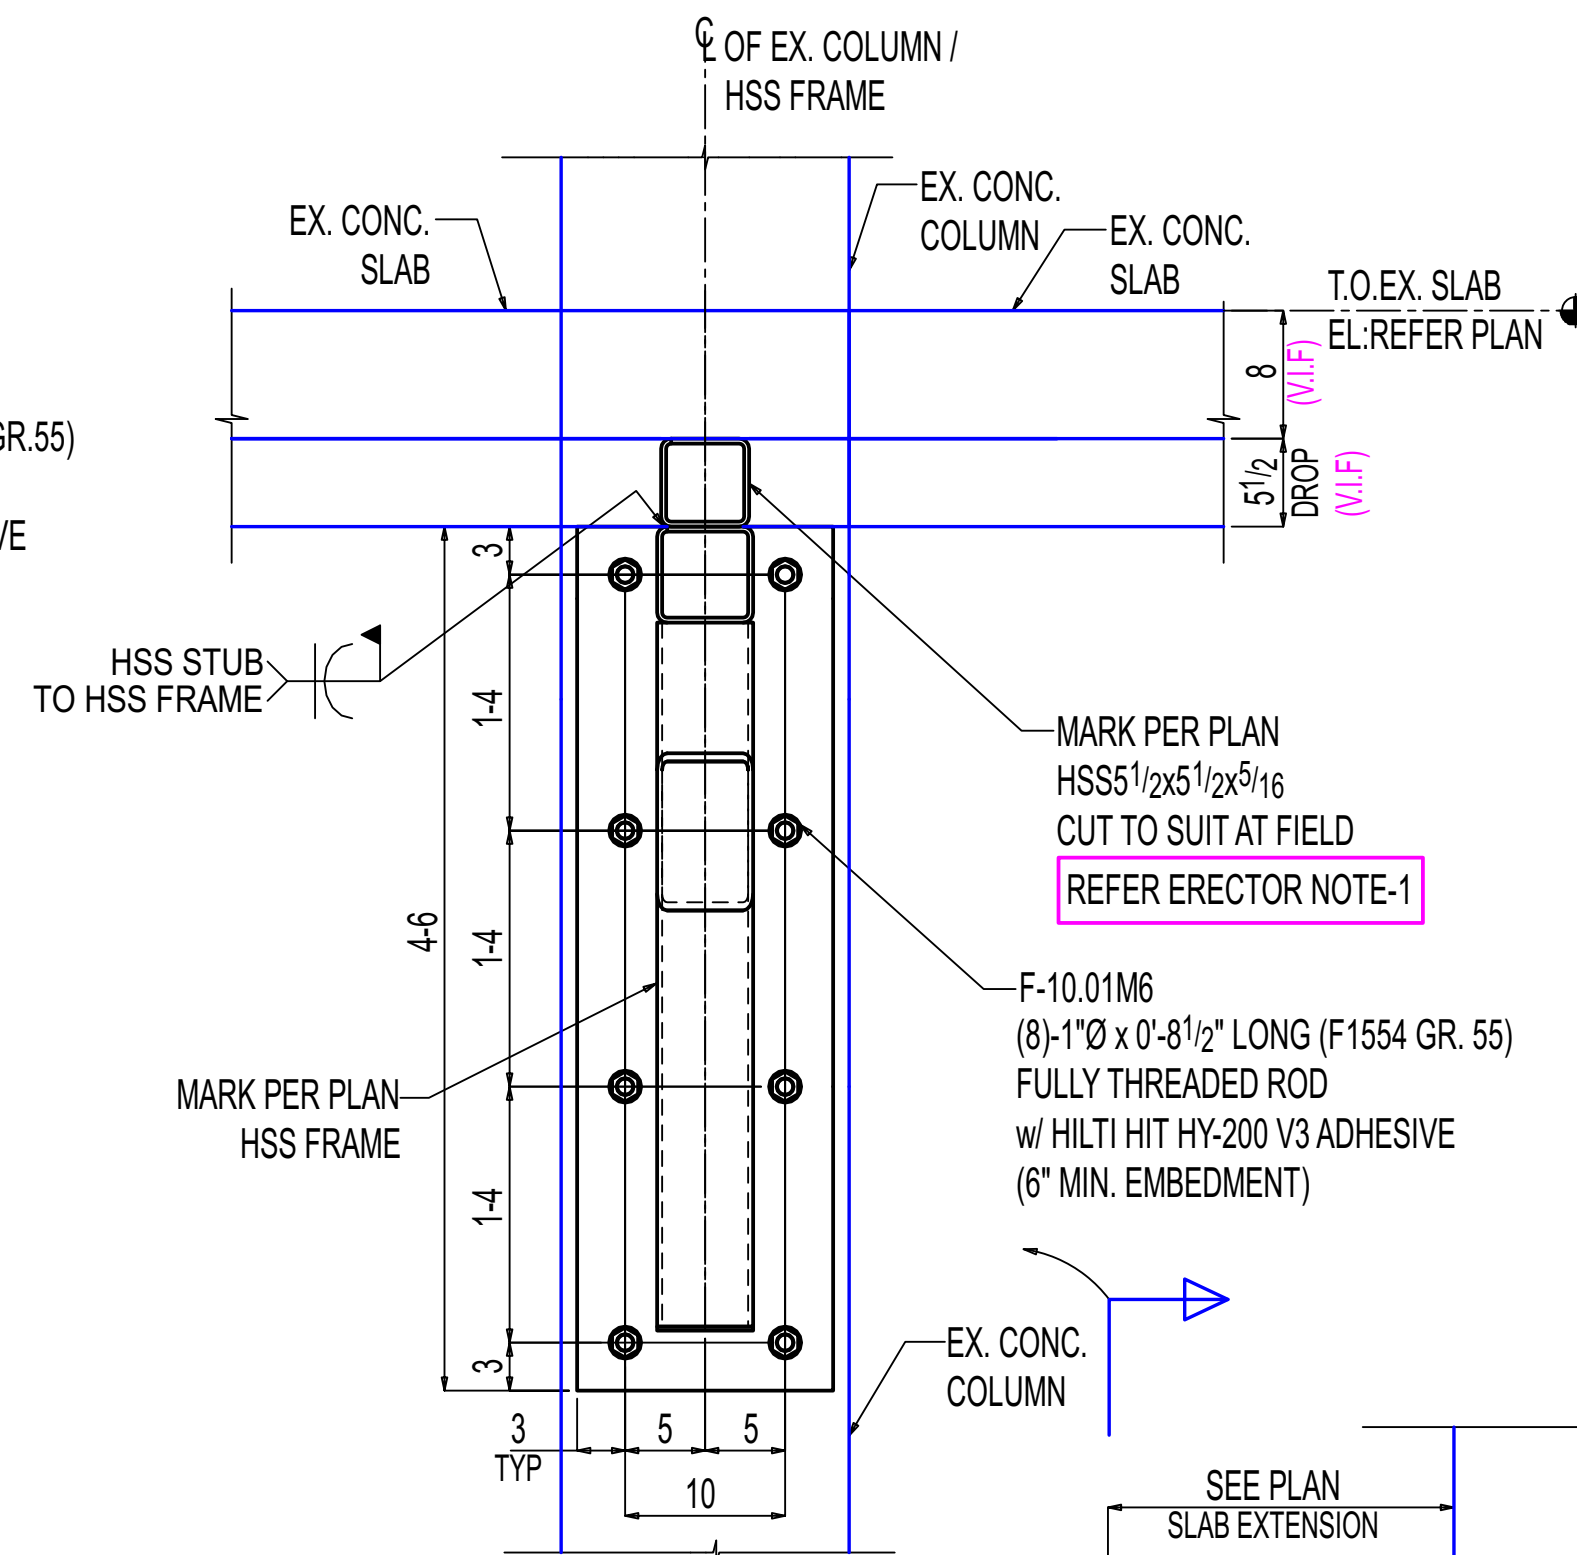

B-B
E-10.00
(REF: 3 & 4/S307)
OTHERS NOT SHOWN FOR CLARITY

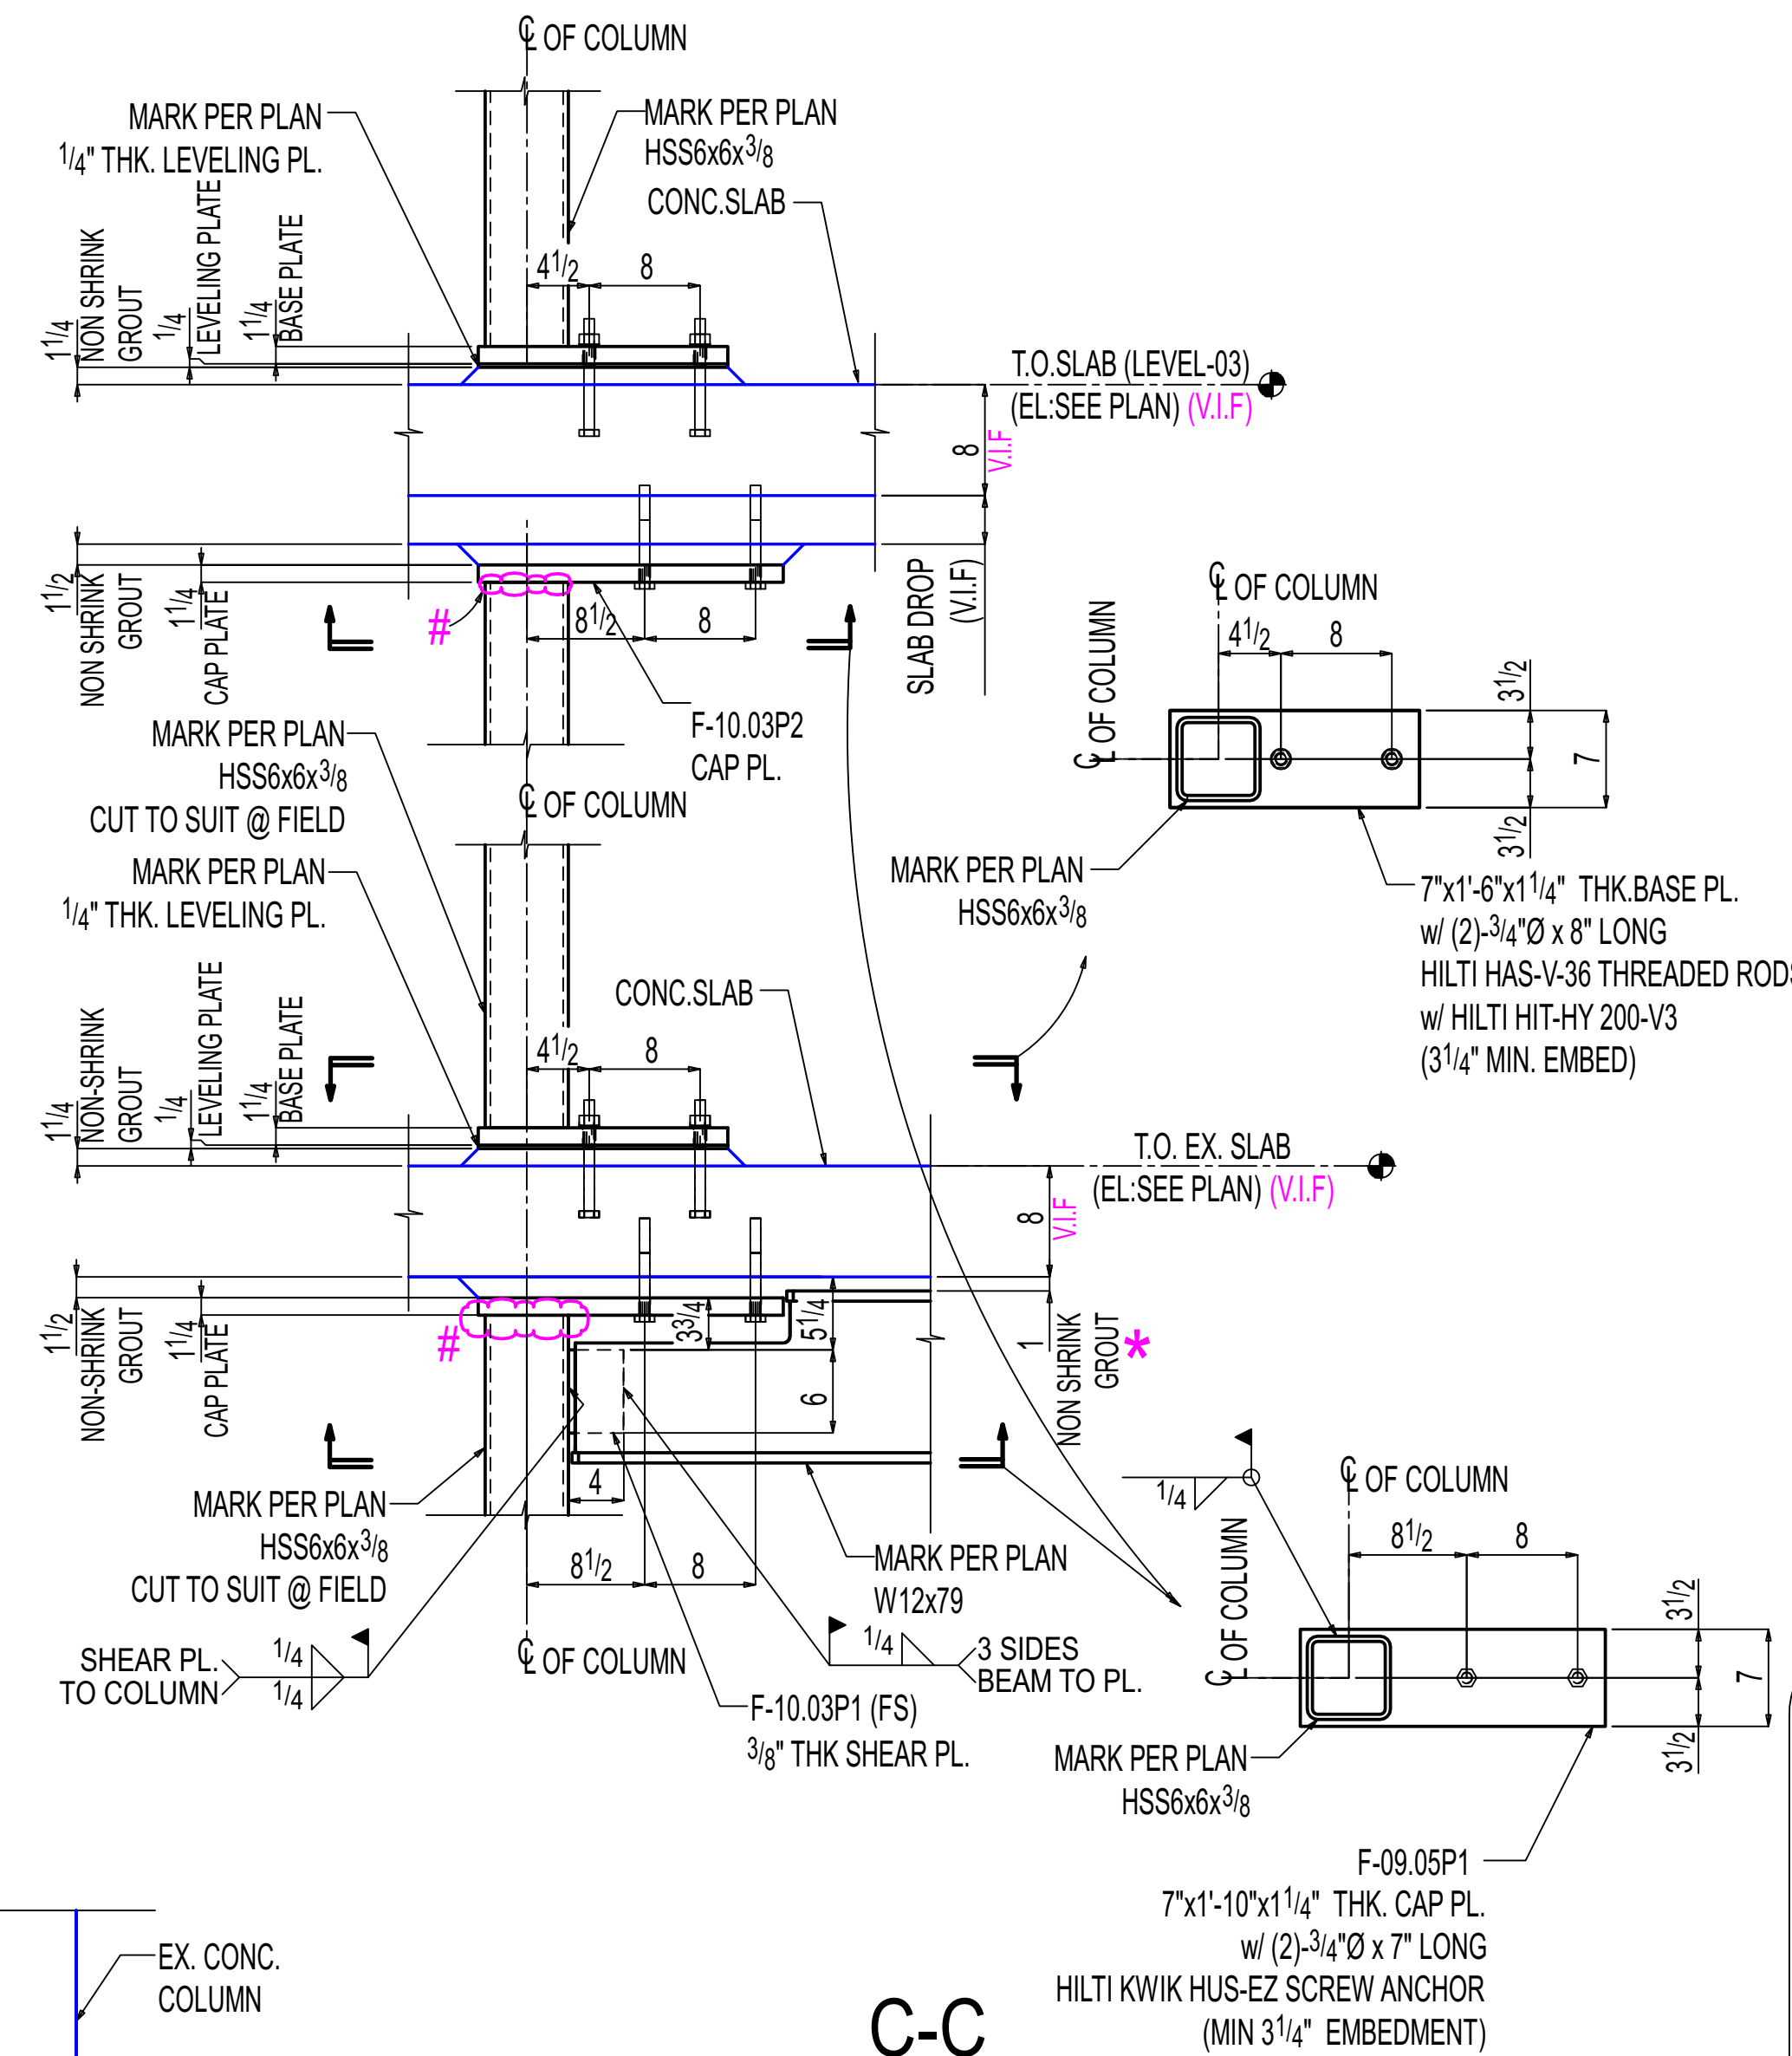

C-C
E-10.00
(REF:7/S314)
OTHERS NOT SHOWN FOR CLARITY

ERECTOR NOTE:
ALL # INDICATED COLUMN ENDS TO BE CUT TO SUIT @ FIELD
BASED ON FLOOR TO FLOOR CLEARANCE AND WELD IT TO THE CAP PLATE.

*** - ERECTOR NOTE:**
PROVIDE 1" NON-SHRINK GROUT x 12" LONG
CENTERED BENEATH AT PRECAST
ATTACHMENT POINTS.

General Notes

- *Structural steel shall conform to ASTM-A992.
- *Structural SQR/RND tubing conform to ASTM A500 Grade C
- *Pipe shall conform to ASTM A53, Grade B.
- *Channels, Angles and plates shall conform to A36.
- *All bolts shall be 3/4" High strength in accordance with ASTM A325 (UNO)
- *Welding Electrodes for Carbon steel :E70xx

# of Copies	Revision/ Issue	Destination	Date
5	0	For Construction	11-14-2025
4	D	For Re-Approval	10-24-2025
3	C	For Re-Approval	09-19-2025
2	B	For Re-Approval	06-23-2025
1	A	For Approval	02-25-2025

IRON FABRICATION SERVICES, LLC.

3029 M. Street, NW, Suite 202
Washington, DC 20007
Tel: 202-800-5599
Fax: 202-478-0303

Project Name and Address
MARYLAND AVENUE

Location: **1250 MARYLAND AVENUE SW
WASHINGTON, DC 20024**

Contractor:
BALFOUR BEATTY

Approved for Fabrication by:	Signature
------------------------------	-----------

Contract # **224009** Drawing # **E-10.01**

Contract Item: **LEVEL-04
SLAB EXTENSION**

Ref: **SOW-10: 3,4,5&6 / S307**

Date 01/20/2025	Drawing Title: SOW #10 LEVEL-04 NEW SLAB EXTENSION SUPPORT SECTIONS
Scale VARIES	