

BILL OF MATERIAL							
LINE	QTY	PC		LENGTH		WEIGHT	ADVANCE
#	TOTAL	MARK	DESCRIPTION			REMARKS	MILL #
	13	F-11.00FR1	FRAME				3101
	13	F-11.00FR1	HSS6x6x ⁹ / ₁₆	3	5 ³ / ₄	A500C	1056
	13	w2771	W8x31	1	0 ¹ / ₂	A992	420
	13	p818	PL ¹ / ₂ x16	4	6	A36	1593
	13	p696	PL ¹ / ₄ x6	0	6	A36	33
	ONE	F-11.00FR2	FRAME				395
	1	F-11.00FR2	HSS6x6x ⁹ / ₁₆	3	7 ³ / ₄	A500C	85
	1	hss3667	HSS6x6x ⁹ / ₁₆	4	1 ¹ / ₈	A500C	96
	1	hss3666	HSS6x6x ⁹ / ₁₆	3	8 ³ / ₈	A500C	86
	1	p818	PL ¹ / ₂ x16	4	6	A36	123
	2	p696	PL ¹ / ₄ x6	0	6	A36	5
	2	F-11.00FR4	FRAME				340
	2	F-11.00FR4	HSS6x2x ⁹ / ₁₆	4	7 ³ / ₄	A500C	138
	2	hss3831	HSS6x2x ⁹ / ₁₆	1	0 ¹ / ₄	A500C	30
	2	p342	PL ¹ / ₂ x9	5	6	A36	168
	4	p3040	PL ¹ / ₄ x2	0	6	A36	3

Technical drawing showing two frames, F-11.00FR4, with dimensions and material specifications.

Front View (Left):

- Overall width: 5.6
- Overall height: 5.6
- Top flange width: 5
- Top flange thickness: $2\frac{1}{2}$
- Top flange offset: $1\frac{1}{4}$
- Web thickness: $\frac{3}{16}$
- Web height: 2.6
- Bottom flange thickness: 1
- Bottom flange offset: 1
- Bottom flange width: 2.6
- Bottom flange height: 3
- Material: HSS TO PL.
- Frame designation: F-11.00FR4

Side View (Right):

- Overall width: 5.6
- Overall height: 4.8
- Top flange width: 1-1
- Top flange thickness: $1\frac{1}{4}$
- Top flange offset: $1\frac{1}{4}$
- Web thickness: $\frac{3}{16}$
- Web height: 6
- Bottom flange thickness: $\frac{3}{16}$
- Bottom flange offset: $\frac{1}{4}$
- Bottom flange width: 6
- Bottom flange height: 4
- Material: 1-p/3040 CNTR
- Frame designation: F-11.00FR4

PAINT	:NO PAINT
PREPARATION	:SSPC-SP3

Drawing Title:
FRAME DETAIL

[illegible]

Technical drawing of a 3-Frame 5-11-04FR1, showing front and side views with dimensions and material specifications.

Front View (Left):

- Overall width: 10
- Overall height: 4-6
- Top flange thickness: $1\frac{1}{4}$
- Top flange width: 5 (centered)
- Web thickness: $\frac{3}{16}$
- Web height: 3-1
- Bottom flange thickness: $\frac{3}{16}$
- Bottom flange width: 5 (centered)
- Material: 1-pl818
- Material: HSS TO PL.

Side View (Right):

- Overall width: 3-1
- Overall height: 4-6
- Top flange thickness: $1\frac{1}{4}$
- Top flange width: 3-0 $\frac{1}{4}$
- Web thickness: $\frac{3}{16}$
- Web height: 3-1
- Bottom flange thickness: $\frac{3}{16}$
- Bottom flange width: 3
- Material: 1-hss1607 CNTR
- Material: 1-hss349 CNTR
- Material: 1-pl696 CNTR
- Material: HSS TO PL.
- Material: BOTH ENDS
- Material: F-11.01FR1

[illegible]








Technical drawing of a 1-pipe 1818 pipe fitting. The drawing shows a side view with dimensions: total length 46, four segments of length 14, and a top flange with a 10mm outer diameter and 5mm inner diameter. A 1 1/4 inch diameter hole is shown on the top flange. The pipe has a 3mm wall thickness and a 1-pipe 1818 specification.

F-11.01FR3

Scale
VARIES

BILL OF MATERIAL							
LINE #	QTY	PC	MARK	DESCRIPTION	LENGTH	WEIGHT	ADVANCE
	TOTAL					TOTAL	MILL #
	2	F-11.02FR1		FRAME		505	
	2	F-11.02FR1	HSS6x2x ³ / ₁₆		4 7 ³ / ₄	A500C	138
	2	hss3773	HSS6x2x ³ / ₁₆		3 6 ³ / ₄	A500C	106
	2	hss3675	HSS6x2x ³ / ₁₆		3 0 ¹ / ₄	A500C	90
	2	p1343	PL 1/2x2		5 6	A36	168
	4	p13040	PL 1/4x2		0 6	A36	3
	ONE	F-11.02FR2		FRAME		366	
	1	F-11.02FR2	HSS6x6x ³ / ₁₆		3 7 ³ / ₄	A500C	85
	1	hss3829	HSS6x6x ³ / ₁₆		3 6 ³ / ₄	A500C	83
	1	hss1607	HSS6x6x ³ / ₁₆		3 0 ¹ / ₄	A500C	70
	1	p1818	PL 1/2x16		4 6	A36	123
	2	p1696	PL 1/4x6		0 6	A36	5
	ONE	F-11.02FR3		FRAME		349	
	1	F-11.02FR3	HSS6x6x ³ / ₁₆		3 7 ³ / ₄	A500C	85
	1	hss1607	HSS6x6x ³ / ₁₆		3 0 ¹ / ₄	A500C	70
	1	hss3714	HSS6x6x ³ / ₁₆		2 10	A500C	66
	1	p1818	PL 1/2x16		4 6	A36	123
	2	p1696	PL 1/4x6		0 6	A36	5
	2	F-11.02FR4		FRAME		495	
	2	F-11.02FR4	HSS6x6x ³ / ₁₆		3 5 ³ / ₄	A500C	162
	2	w2792	WB6x31		1 4	A992	83
	2	p1818	PL 1/2x16		4 6	A36	245
	2	p1696	PL 1/4x6		0 6	A36	5
	36	F-11.02M1		THREADED ROD		88	
	36	F-11.02M1	1" Ø THREADED ROD		0 11	F1554 GR. 55	88
			w/ HILTI HIT HY-200 V3			(8" EMBEDMENT)	
			ADHESIVE				
	36		1 NUT			HHNT A563	
	36		1 WASHER			HD F436	
	208	F-11.02M2		THREADED ROD		394	
	208	F-11.02M2	1" Ø THREADED ROD		0 8 ¹ / ₂	F1554 GR. 55	394
			w/ HILTI HIT HY-200 V3			(6" EMBEDMENT)	
			ADHESIVE				
	208		1 NUT			HHNT A563	
	208		1 WASHER			HD F436	
	6	F-11.02M3		THREADED ROD		16	
	6	F-11.02M3	1" Ø THREADED ROD		1 0	F1554 GR. 55	16
			w/ HILTI HIT HY-200 V3			(8" EMBEDMENT)	
			ADHESIVE				
			FIELD BOLTS				
	6		1 NUT			HHNT A563	

Total weight : 2214

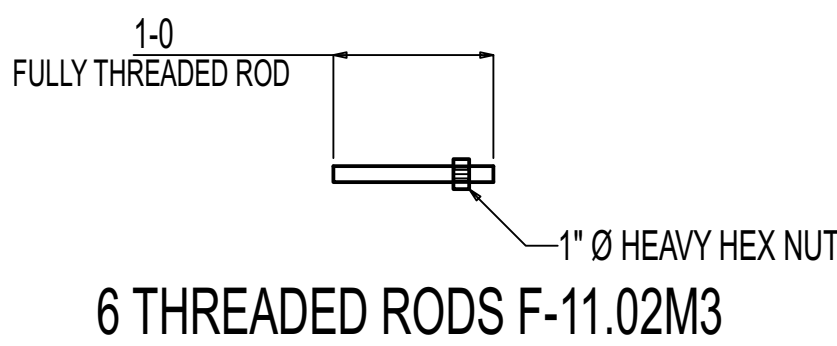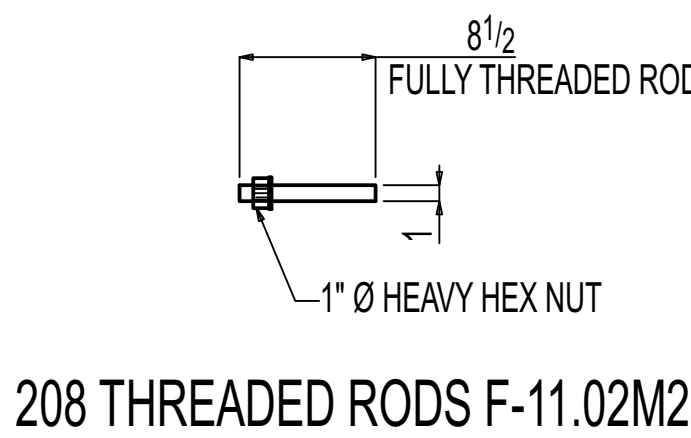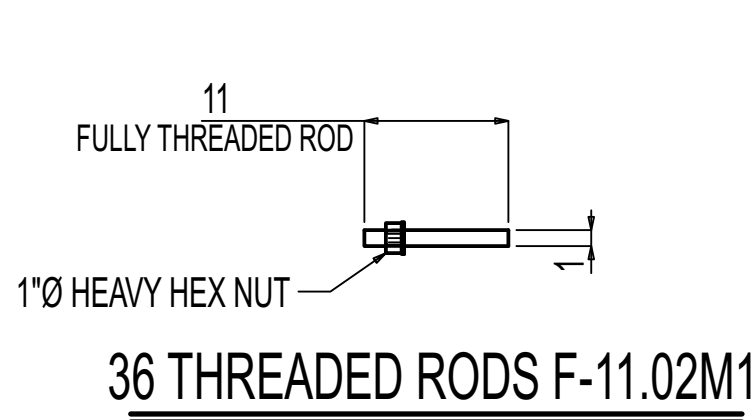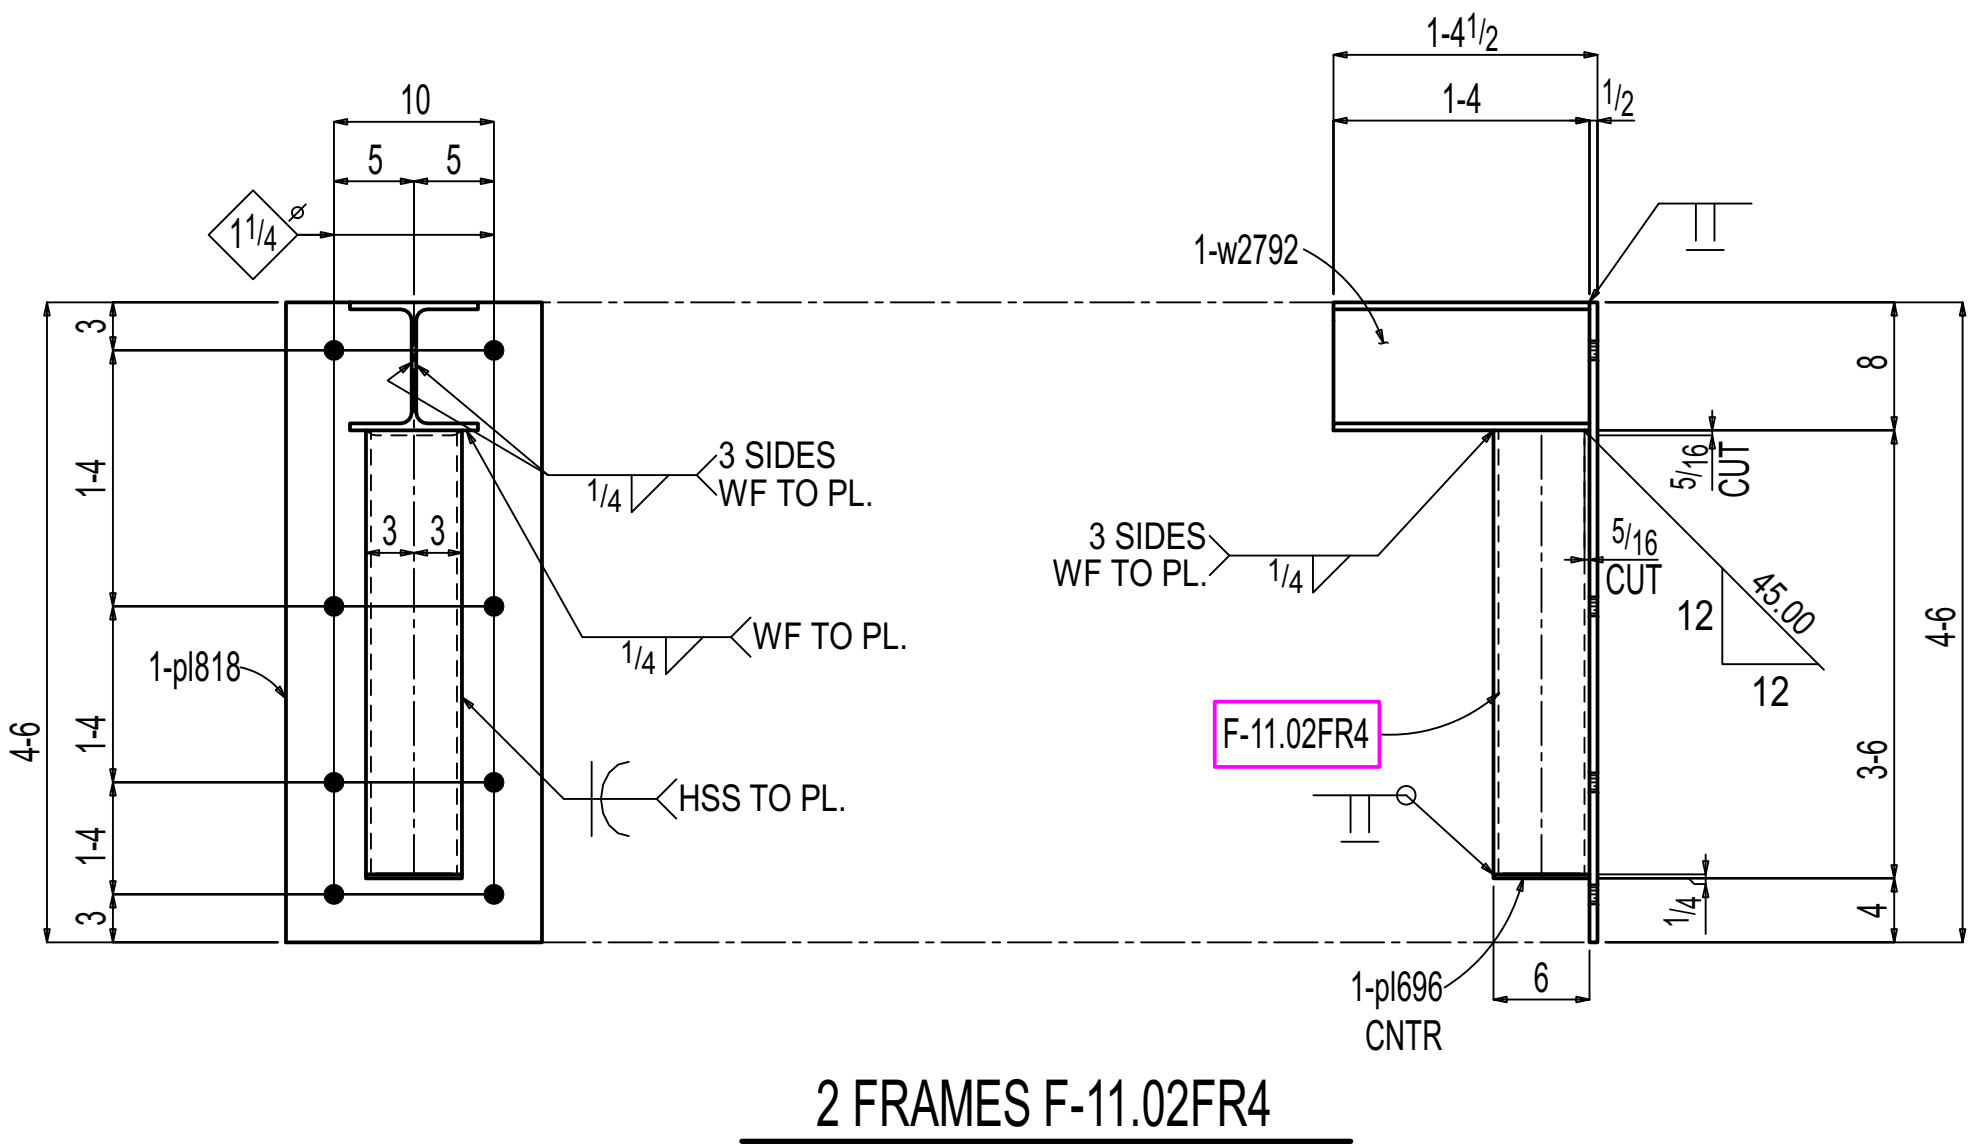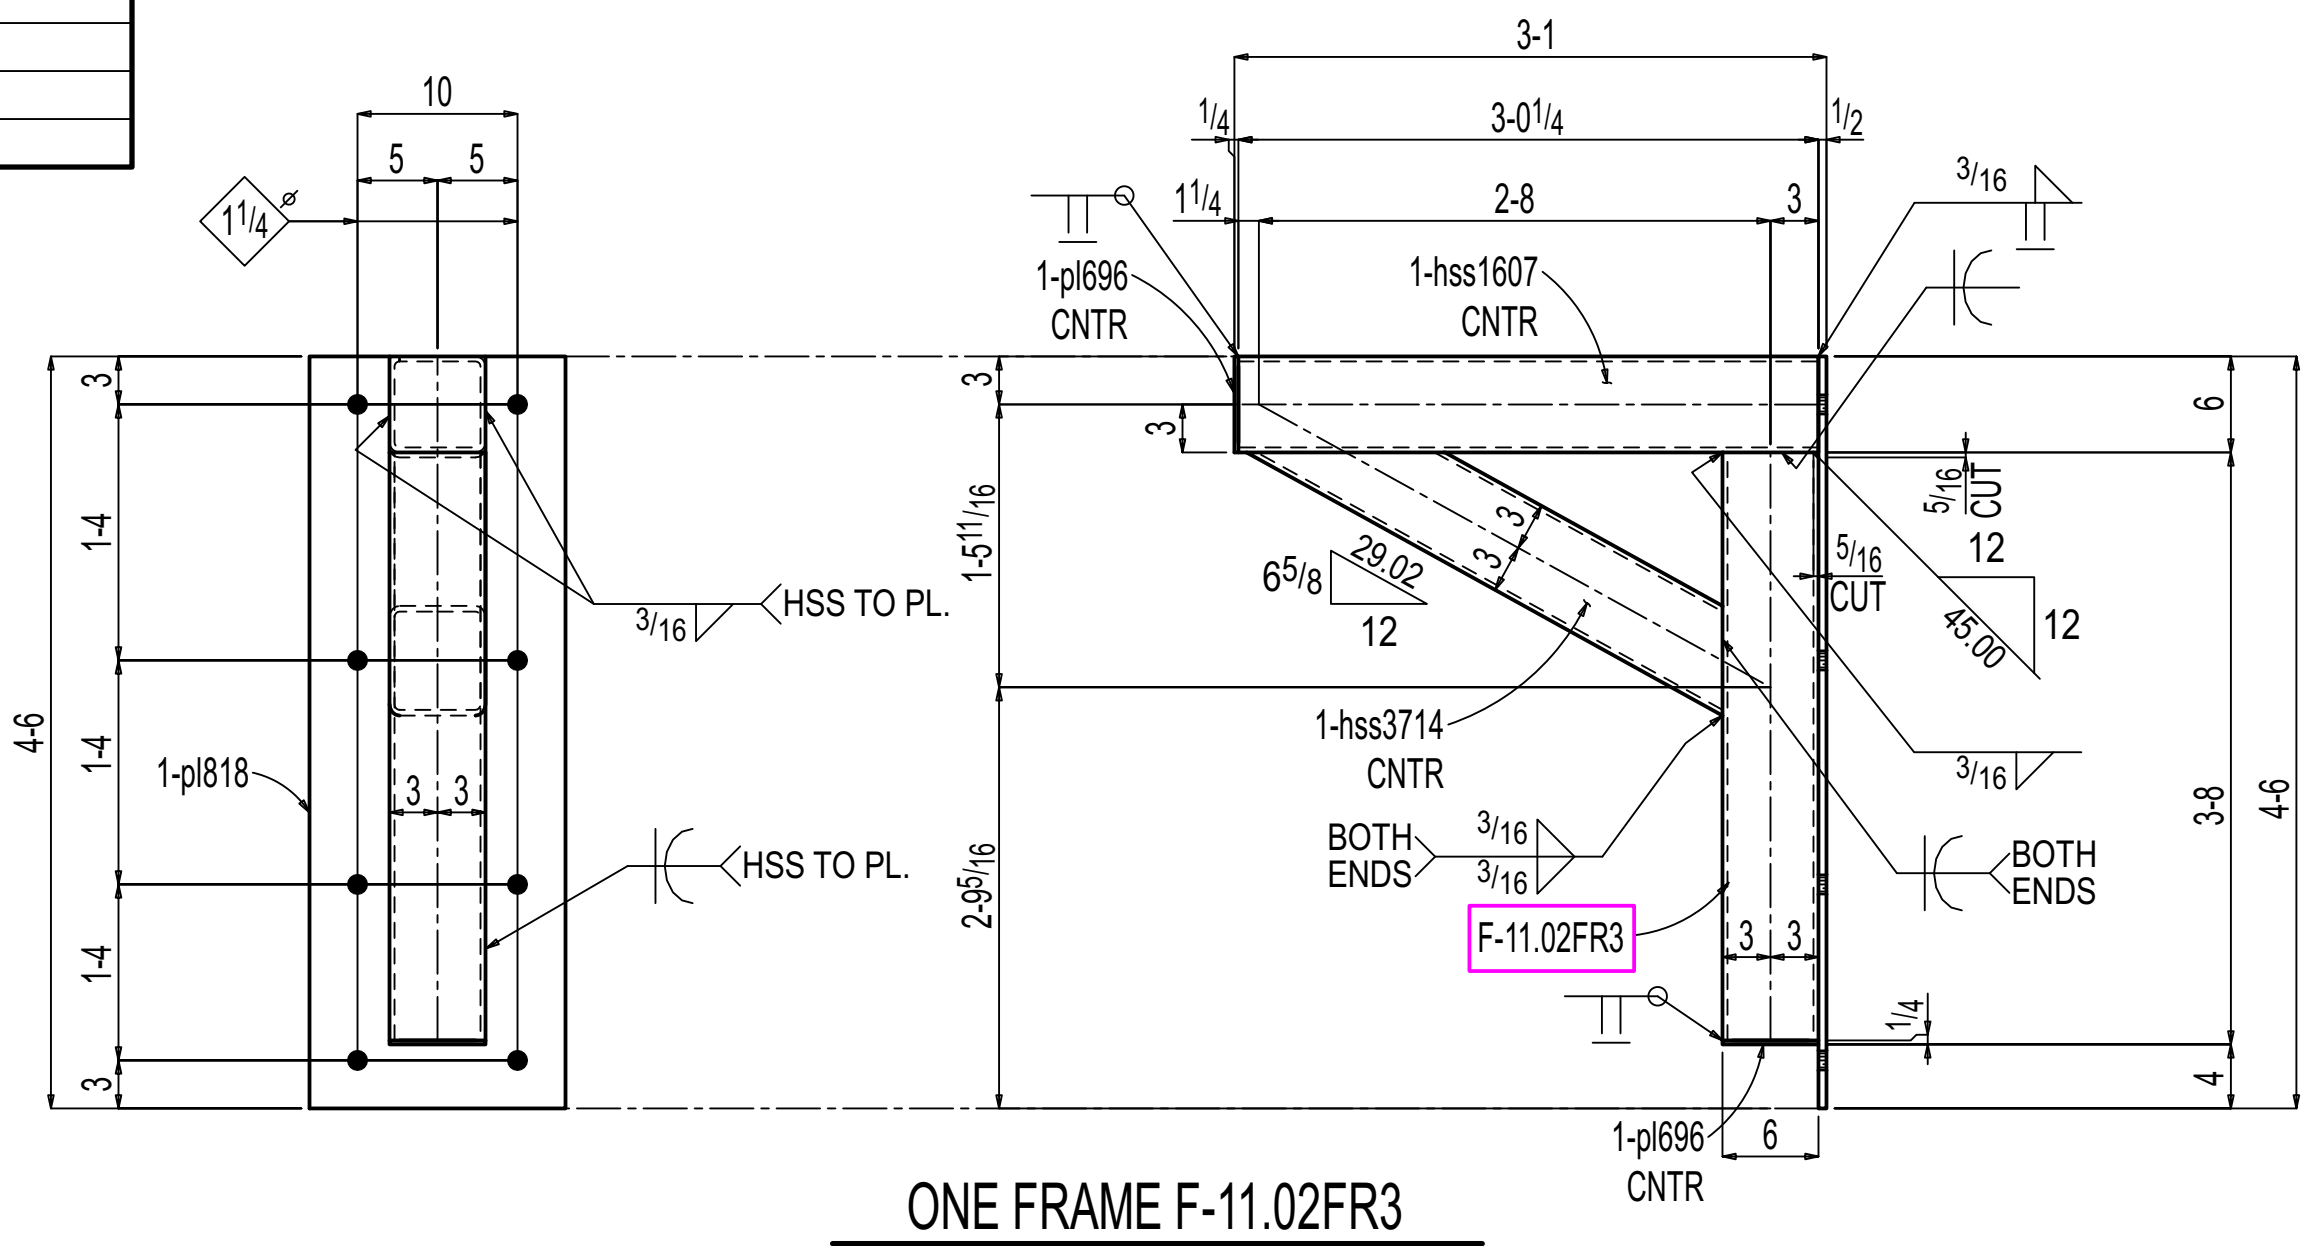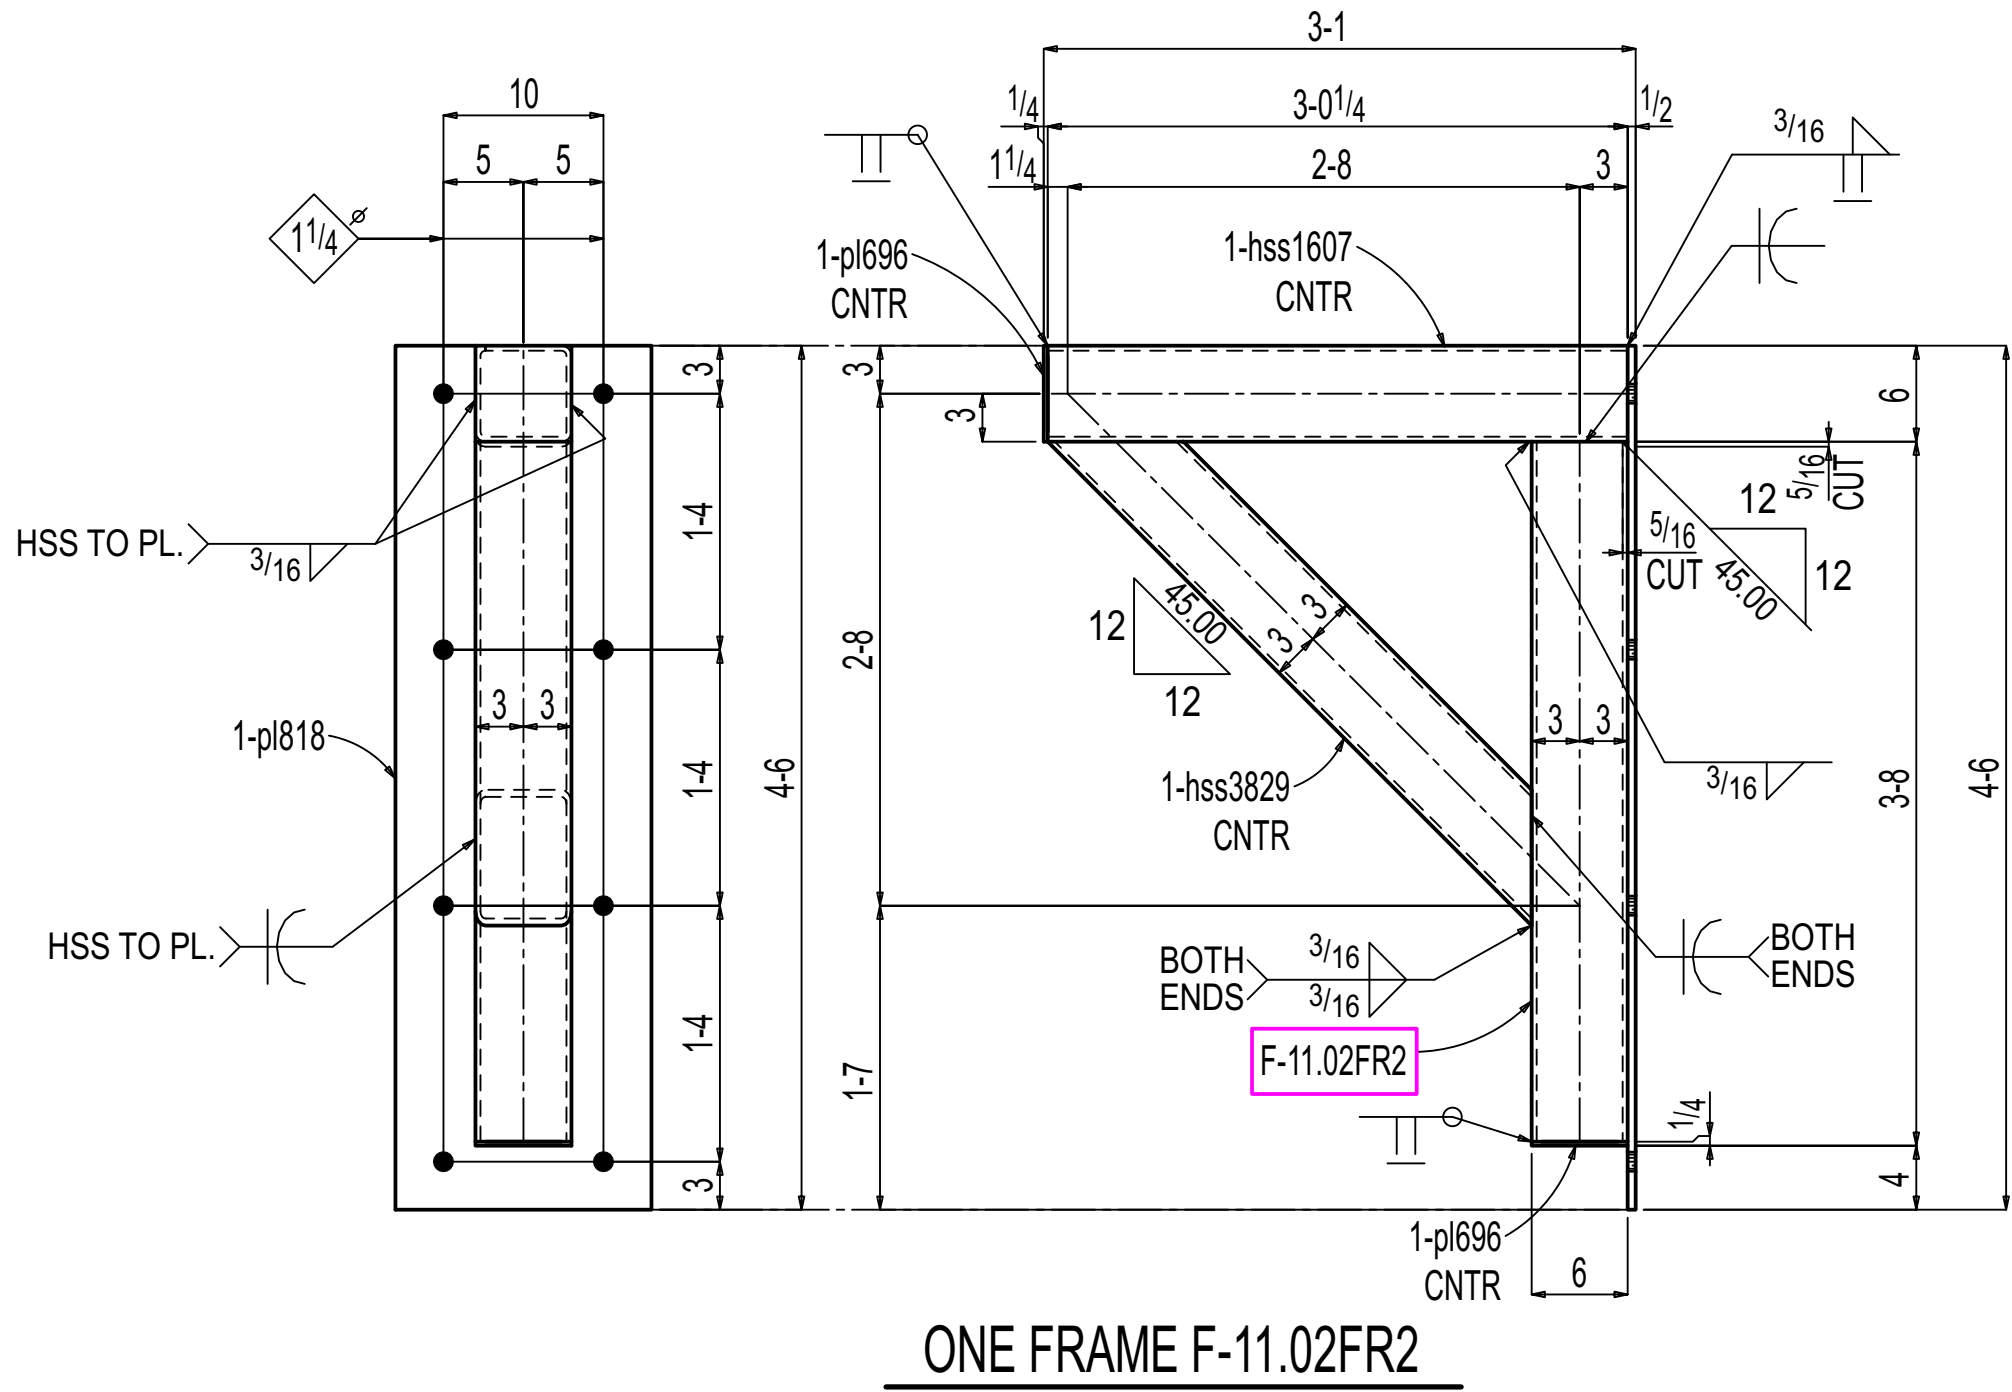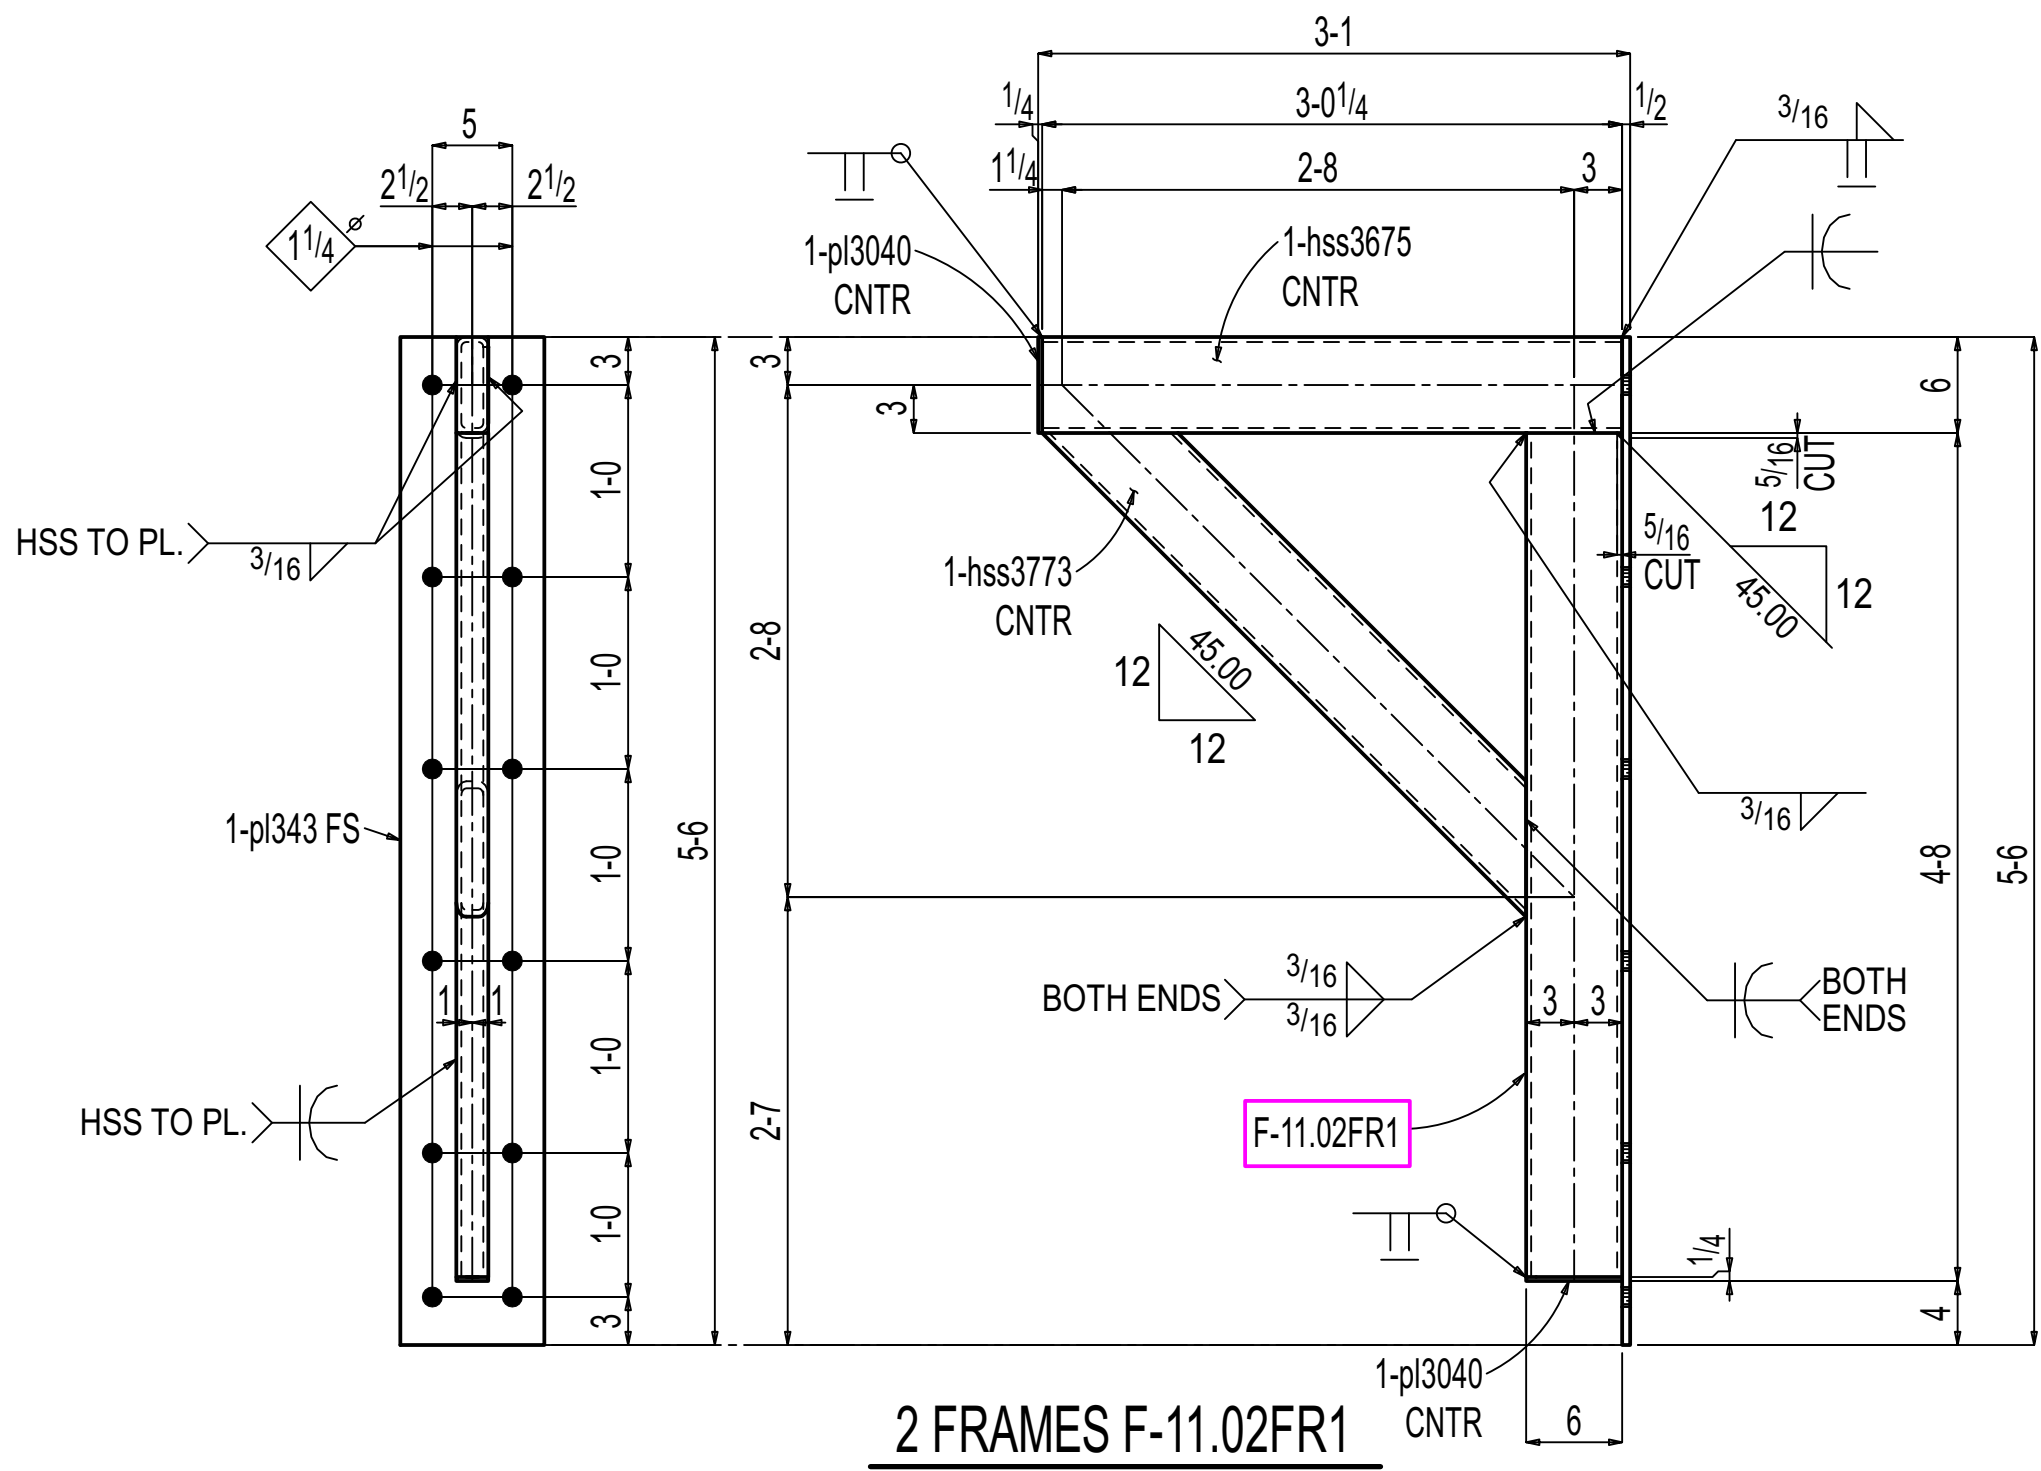

PAINT :NO PAINT
PREPARATION :SSPC-SP3

General Notes			
*Structural steel shall conform to ASTM-A992.			
*Structural SQR/RND,tubing conform to ASTM A500 Grade C			
*Pipe shall conform to ASTM A53, Grade B.			
*Channels, Angles and plates shall conform to A36.			
*All bolts shall be 3/4" High strength in accordance with ASTM A325 (UNO)			
*Welding Electrodes for Carbon steel :E70xx			
5	0	For Fabrication	11-14-2025
4	D	For Re-Approval	10-24-2025
3	C	For Re-Approval	09-19-2025
2	B	For Re-Approval	06-23-2025
1	A	For Approval	02-25-2025
# of Copies	Revision/ Issue	Destination	Date

IRON FABRICATION SERVICES, LLC.

3029 M. Street, NW, Suite 202
Washington, DC 20007
Tel: 202-800-5599
Fax: 202-478-0303

Project Name and Address

MARYLAND AVENUE
Location: **1250 MARYLAND AVENUE SW**
WASHINGTON, DC 20024

Contractor:

BALFOUR BEATTY

Approved for Fabrication by:	Signature
------------------------------	-----------

Contract #	224009	Drawing #	F-11.02
Contract Item:	FRAME & THREADED ROD		
Ref:	SOW - 11: E-11.00 - E-11.02		
Date	01/ 23/ 2025	Drawing Title:	FRAME DETAIL
Scale	VARIES		

BILL OF MATERIAL							
LINE	QTY	PC		LENGTH		WEIGHT	ADVANCE
#	TOTAL	MARK	DESCRIPTION		REMARKS	TOTAL	MILL #
	ONE	F-11.03FR1	FRAME			438	
	1	F-11.03FR1	HSS6x6x9/16	3 79/16	A500C	85	
	1	hss350	HSS6x6x9/16	4 115/16	A500C	115	
	1	hss351	HSS6x6x9/16	4 87/16	A500C	110	
	1	p818	PL1/2x16	4 6	A36	123	
	1	p3416	PL1/4x6	0 77/16	A36	3	
	1	p696	PL1/4x6	0 6	A36	3	
	ONE	F-11.03M1	PLATE			189	
	1	F-11.03M1	PL1x18	2 1	A36	128	
	1	p128	PL1x8	1 6	A36	41	
	3	p1240	PL1/2x7	0 7	A36	21	
	ONE	F-11.03M2	PLATE			37	
	1	F-11.03M2	PL3/4x6	1 3	A36	19	
	2	p3640	PL3/4x6	0 7	A36	18	
	ONE	F-11.03M3	PLATE			55	
	1	F-11.03M3	PL3/4x6	2 53/8	A36	38	
	2	p599	PL3/4x6	0 7	A36	18	
	ONE	F-11.03M4	HSS			41	
	1	F-11.03M4	HSS8x8x9/16	1 0	A500C	32	
	2	p3643	PL1/4x8	0 8	A36	9	
	ONE	F-11.03M5	HSS			33	
	1	F-11.03M5	HSS10x10x5/16	0 51/2	A500C	18	
	2	p538	PL1/4x10	0 10	A36	14	
	2	F-11.03M6	HSS			35	
	2	F-11.03M6	HSS51/2x51/2x5/16	0 71/2	A500C	27	
	4	p698	PL1/4x51/2	0 51/2	A36	9	
	6	F-11.03M10	PLATE WASHER			8	
	6	F-11.03M10	PL1/2x3	0 3	A36	8	
	ONE	F-11.03EP1	EMBED PLATE			230	
	1	F-11.03EP1	PL5/8x22	4 11	A36	230	
	10		FIELD BOLTS 3/4 Dia HILTI HAS V-36 w/ HILTI HIT HY-200 V3 ADHESIVE	0 8	+1HD WASH (5" EMBEDMENT)		
	ONE	F-11.03EP2	EMBED PLATE			117	
	1	F-11.03EP2	PL5/8x22	2 6	A36	117	
	6		FIELD BOLTS 3/4 Dia HILTI HAS V-36 w/ HILTI HIT HY-200 V3 ADHESIVE	0 8	(5" EMBEDMENT)		
	ONE	F-11.03LP1	LEVELING PLATE			9	
	1	F-11.03LP1	PL1/4x7	1 6	A36	9	
	ONE	F-11.03LP2	LEVELING PLATE			8	
	1	F-11.03LP2	PL1/4x61/2	1 6	A36	8	


Total weight : 1201



Drawing Title:
**FRAME & MISCELLANEOUS
DETAIL**


BILL OF MATERIAL							
LINE #	QTY	PC MARK	DESCRIPTION	LENGTH		WEIGHT	ADVANCE
	TOTAL	MARK	DESCRIPTION		REMARKS	TOTAL	MILL #
ONE	F-11.04C1	COLUMN				329	
1	F-11.04C1	HSS6x6x3/8		10	4	S2E A500C	284
1	p1971	PL11/4x7		1	6	A36	45
			FIELD BOLTS				
2		3/4 Dia HILTI HAS V-36		0	8	+1HD WASH	
		w/ HILTI HIT HY-200 V3				(3 1/4" EMBEDMENT)	
		ADHESIVE					
ONE	F-11.04C2	COLUMN				313	
1	F-11.04C2	HSS6x6x3/8		9	10 1/2	S2E A500C	271
1	p358	PL5/8x6 1/2		1	6	A36	21
1	p3371	PL5/8x6 1/2		1	6	A36	21
			FIELD BOLTS				
2		1/2 Dia HILTI KWIK HUS-EZ		0	4 1/2		
		SCREW ANCHOR				(2 3/4" EMBEDMENT)	
ONE	F-11.04B1	BEAM				2397	
1	F-11.04B1	HSS12x12x3/4		21	7 1/2	A500C	2377
2	p3644	PL1/4x12		1	0	A36	20
2	F-11.04B2	BEAM				1090	
2	F-11.04B2	HSS8x8x1/4		20	9	A500C	1072
4	p567	PL1/4x8		0	8	A36	18
2	F-11.04M1	THREADED ROD				1	
2	F-11.04M1	1/2" Ø THREADED ROD		0	6	F1554 GR. 55	1
2		1/2 NUT				HHNT A563	
2		1/2 WASHER				HD F436	
ONE	F-11.04M2	HSS				265	
1	F-11.04M2	HSS5x5x5/16		13	8 1/2	A500C	262
2	p567	PL1/4x5		0	5	A36	4
ONE	F-11.04M3	HSS				145	
1	F-11.04M3	HSS5x3x5/16		9	7 1/2	A500C	143
2	p570	PL1/4x3		0	5	A36	2
ONE	F-11.04A1	ANGLE				7	
1	F-11.04A1	L4x4x1/4		1	0	A36	7
ONE	F-11.04A2	ANGLE				2	
1	F-11.04A2	L4x4x1/4		0	4	A36	2
2	F-11.04P1	PLATE				18	
2	F-11.04P1	PL1/2x8		0	8	A36	18
ONE	F-11.04P2	PLATE				55	
1	F-11.04P2	PL11/4x7		1	10	A36	55
		FIELD BOLTS					
2		3/4 Dia HILTI KWIK HUS-EZ		0	7		
		SCREW ANCHOR					

Total weight : 4621

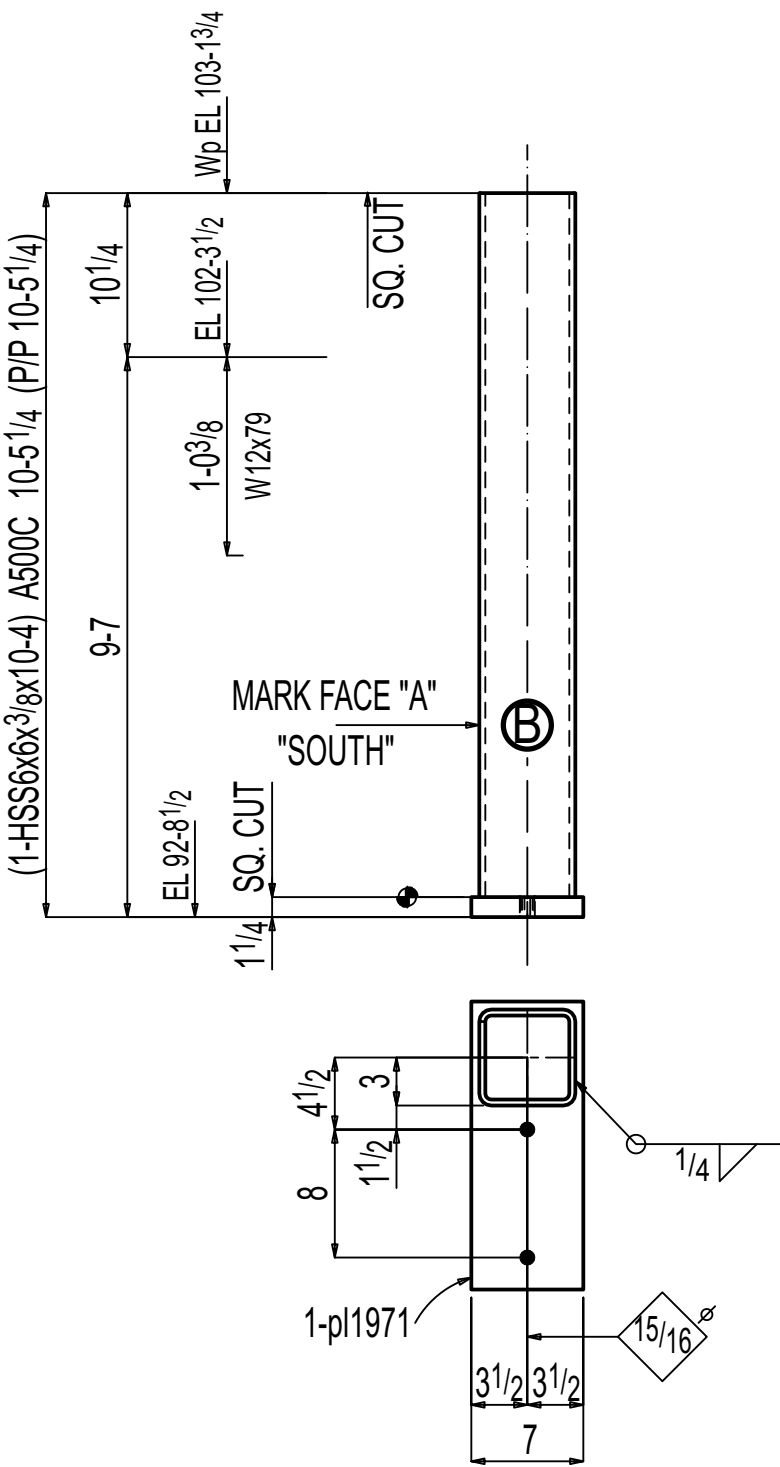


ONE COLUMN F-11.04C1


AT GRID:
EE & A

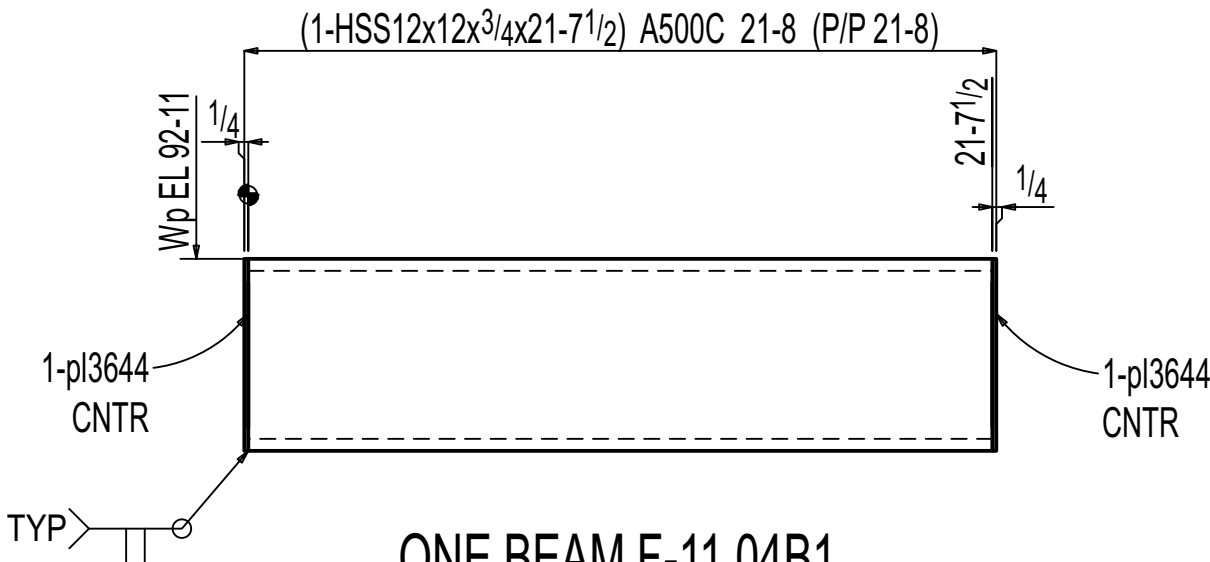


ONE BEAM F-11.04B1

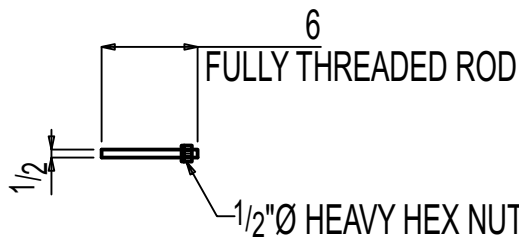


2 THREADED RODS F-11.04M1

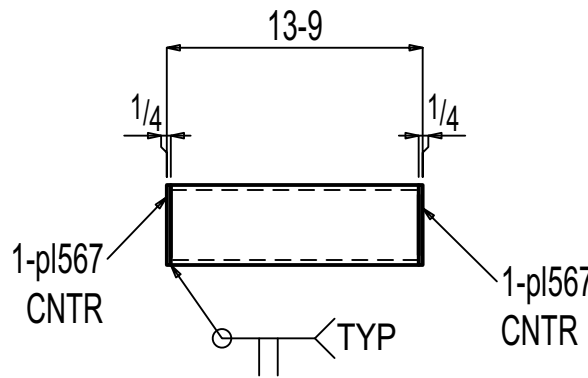

ONE HSS F-11.04M2

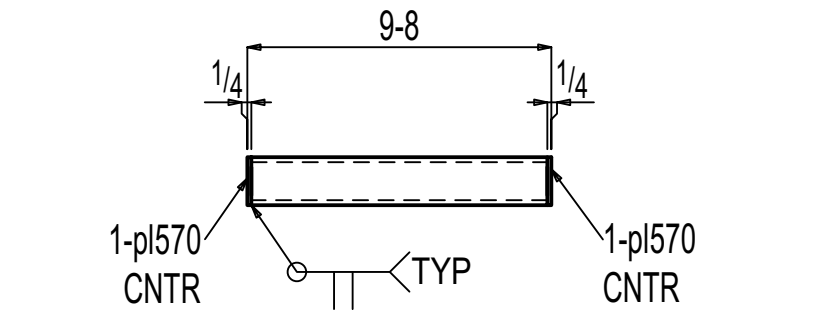


ONE HSS F-11.04M3

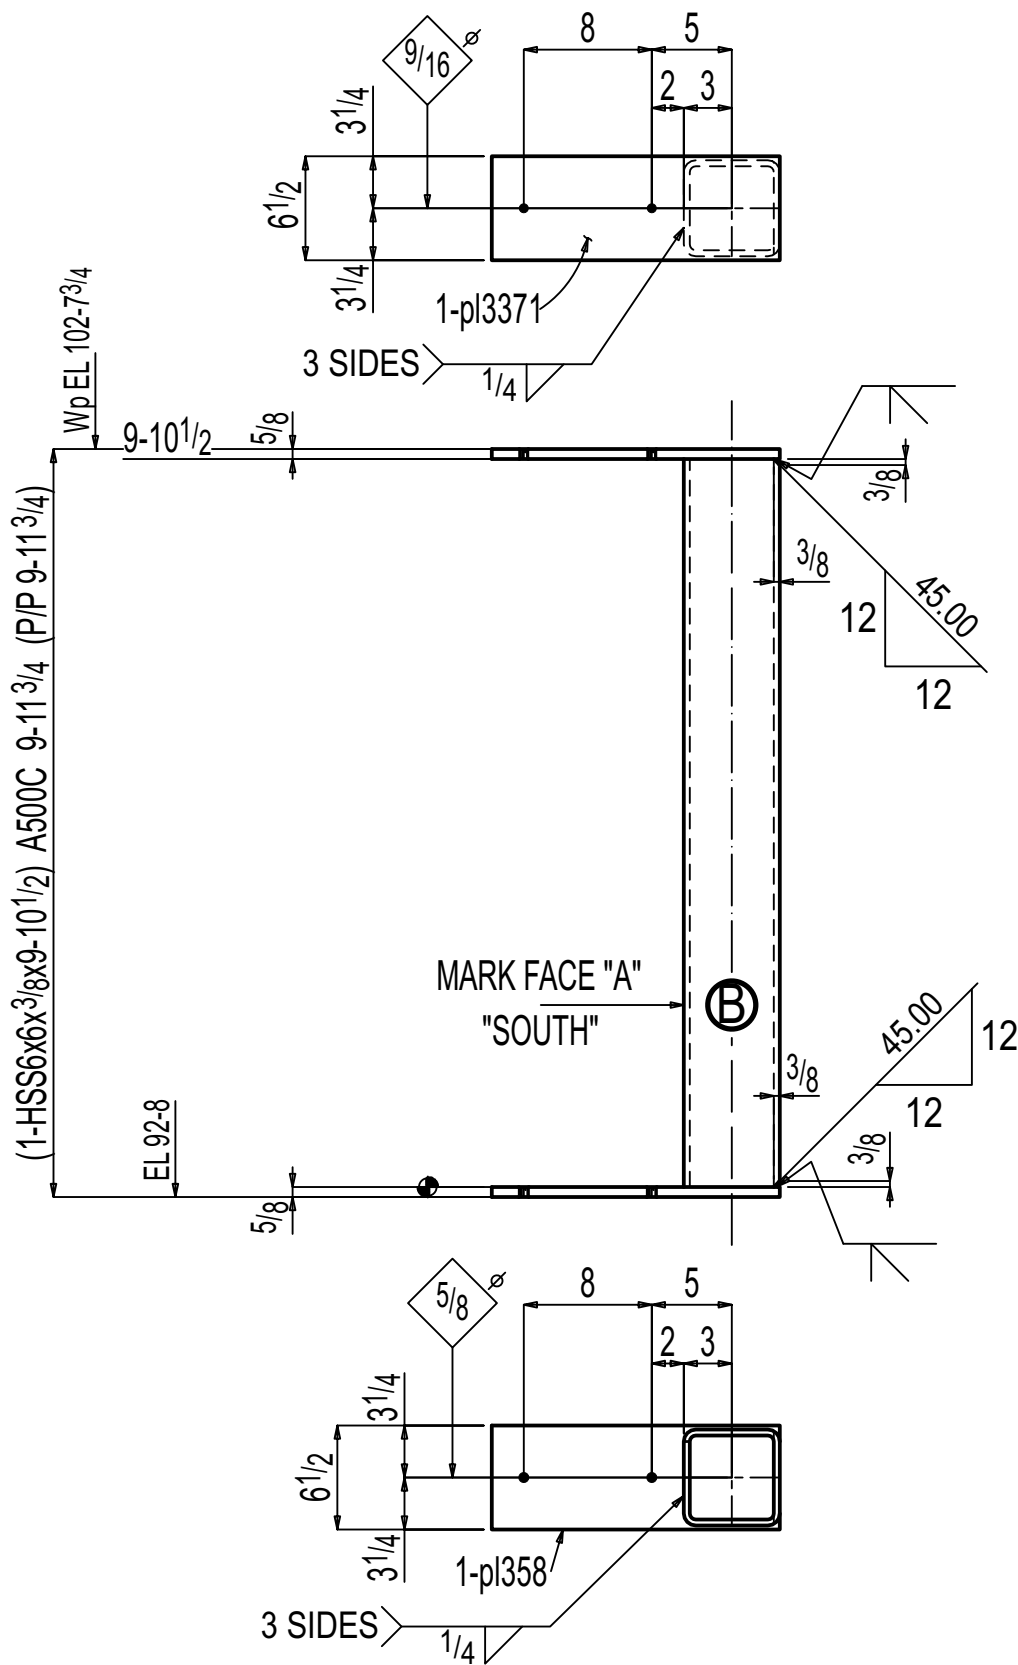


ONE COLUMN F-11.04C2


AT GRID:
AA & K

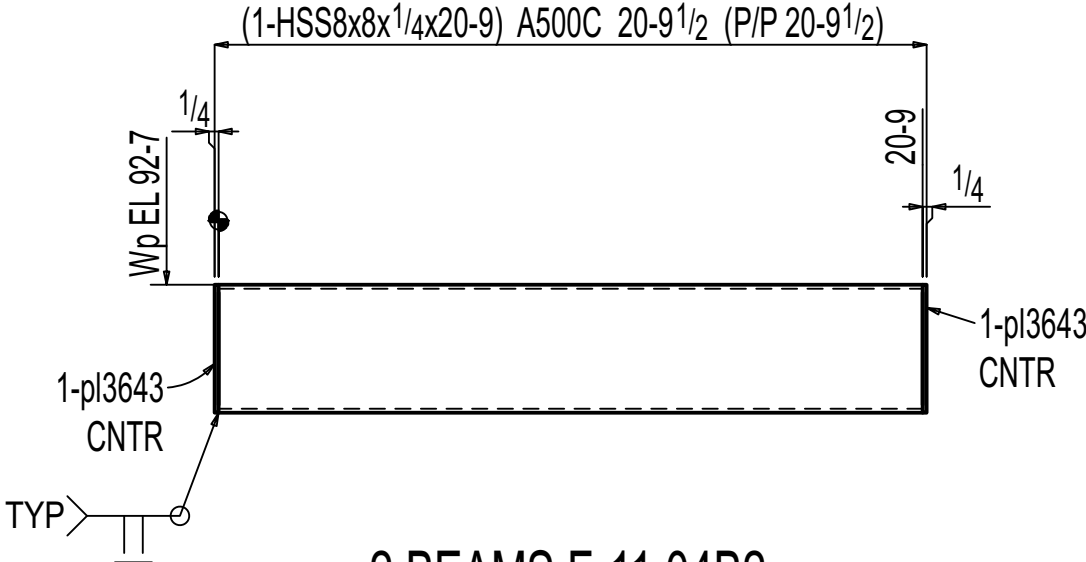


2 BEAMS F-11.04B2

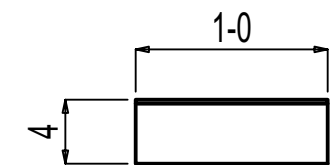


ONE ANGLE F-11.04A1

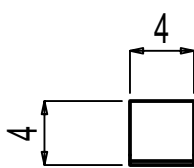

ONE ANGLE F-11.04A2

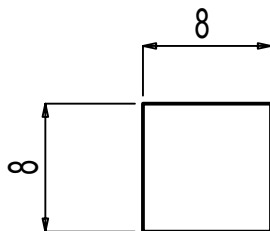

2 PLATES F-11.04P1

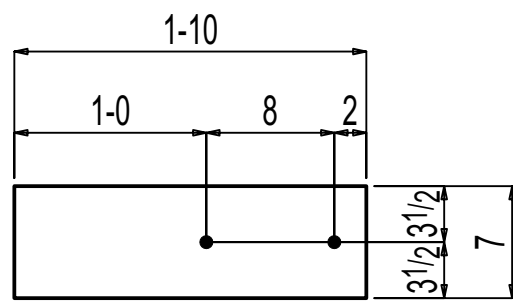

ONE PLATE F-11.04P2

PAINT PREPARATION :NO PAINT
:SSPC-SP3

General Notes			
*Structural steel shall conform to ASTM-A992.			
*Structural SQR/RND,tubing conform to ASTM A500 Grade C			
*Pipe shall conform to ASTM A53, Grade B.			
*Channels, Angles and plates shall conform to A36.			
*All bolts shall be 3/4" High strength in accordance with ASTM A325 (UNO)			
*Welding Electrodes for Carbon steel :E70xx			
5	0	For Fabrication	11-14-2025
4	D	For Re-Approval	10-24-2025
3	C	For Re-Approval	09-19-2025
2	B	For Re-Approval	06-23-2025
1	A	For Approval	02-25-2025
# of Copies	Revision/ Issue	Destination	Date

IRON FABRICATION SERVICES, LLC.

3029 M. Street, NW, Suite 202
Washington, DC 20007
Tel: 202-800-5599
Fax: 202-478-0303

Project Name and Address
MARYLAND AVENUE

Location: **1250 MARYLAND AVENUE SW
WASHINGTON, DC 20024**

Contractor:
BALFOUR BEATTY

Approved for Fabrication by:	Signature
------------------------------	-----------

Contract # 224009	Drawing # F-11.04
--------------------------	--------------------------



Contract Item: **FRAME**

Ref:
SOW - 11: E-11.00 - E-11.02

Date 01/ 23/ 2025	Drawing Title: COLUMN & BEAM DETAIL
Scale VARIES	



BILL OF MATERIAL							
LINE #	QTY	PC MARK	DESCRIPTION	LENGTH	REMARKS	WEIGHT TOTAL	ADVANCE MILL #
ONE F-11.05B1 BEAM						906	
1	F-11.05B1	HSS10x8x5/16		19 10 13/16	A500C	718	
1	p385	PL 1/4x8 7/16		9 10 1/2	A36	71	
1	p3538	PL 1/4x8		0 10	A36	6	
1	p3417	PL 1/4x8		0 10	A36	6	
1	p386	PL 1/4x8 15/16		9 11 7/8	A36	42	
1	fb175	FL 1/4x3 3/4		9 11 3/4	A36	32	
1	fb163	FL 1/4x3 3/4		9 10	A36	31	
ONE F-11.05B2 BEAM						896	
1	F-11.05B2	HSS10x8x5/16		19 0 1/2	A500C	687	
1	p395	PL 1/4x8 7/16		8 11 7/8	A36	65	
1	p394	PL 1/4x8 7/16		10 0 3/16	A36	72	
2	p3538	PL 1/4x8		0 10	A36	11	
1	fb174	FL 1/4x3 3/4		9 11 13/16	A36	32	
1	fb181	FL 1/4x3 3/4		8 11 7/16	A36	29	

Total weight : 1801

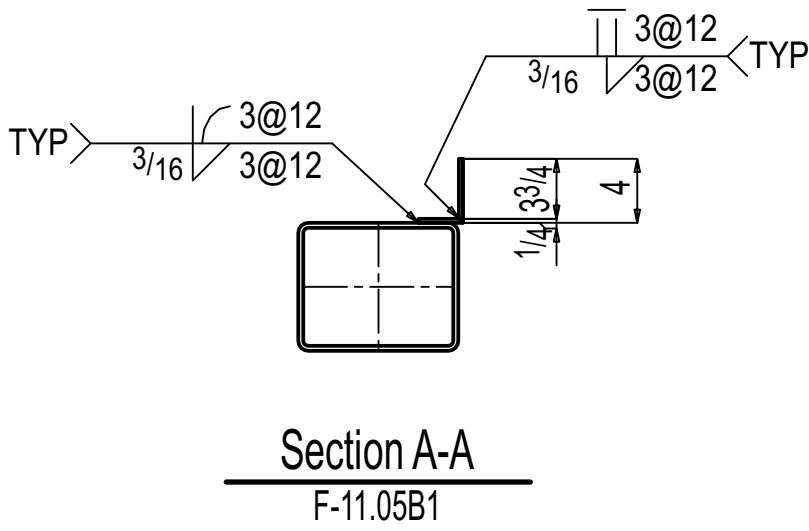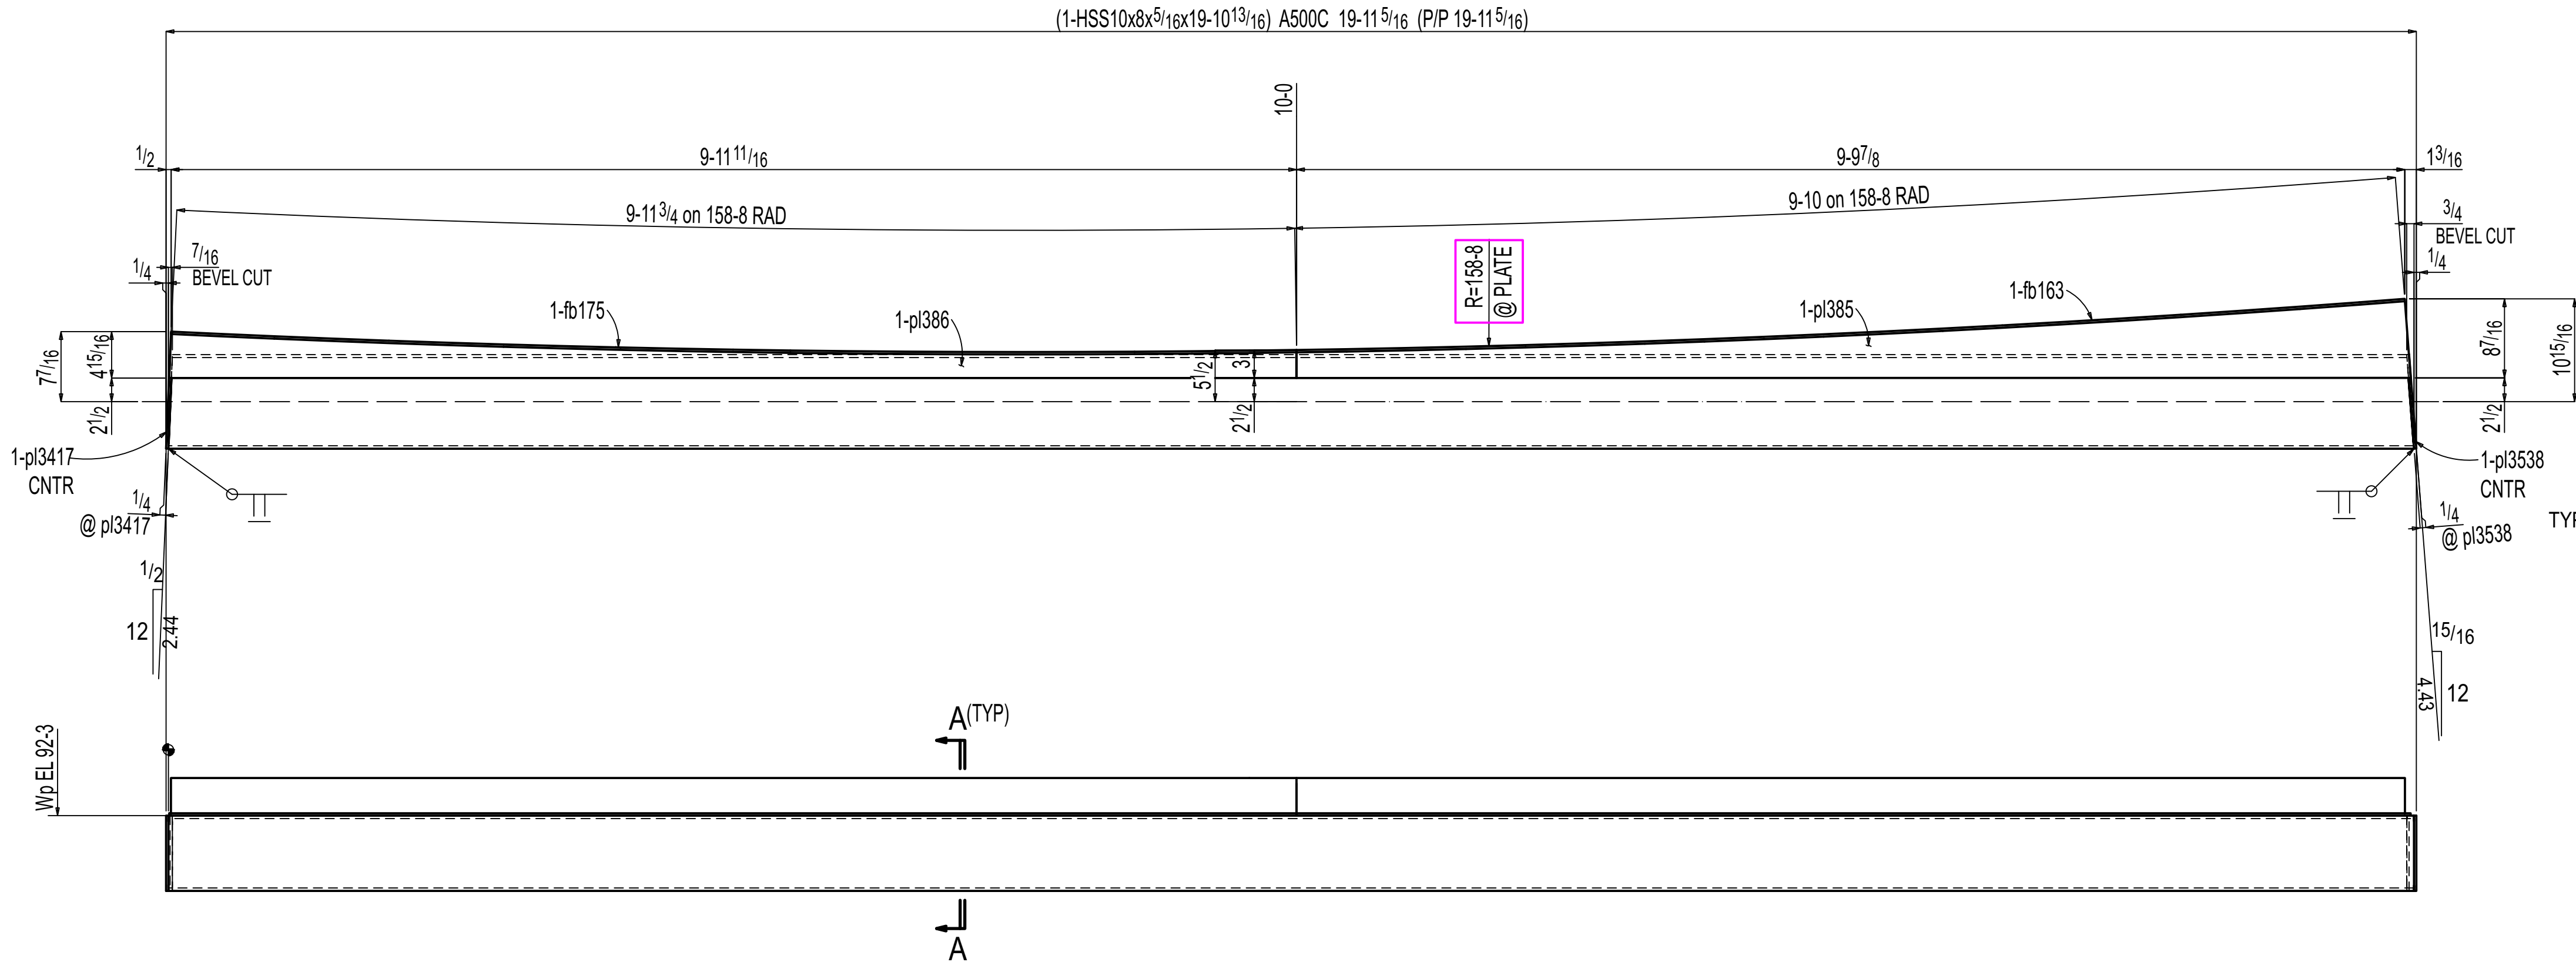

PAINT :NO PAINT
PREPARATION :SSPC-SP3

ONE BEAM F-11.05B1

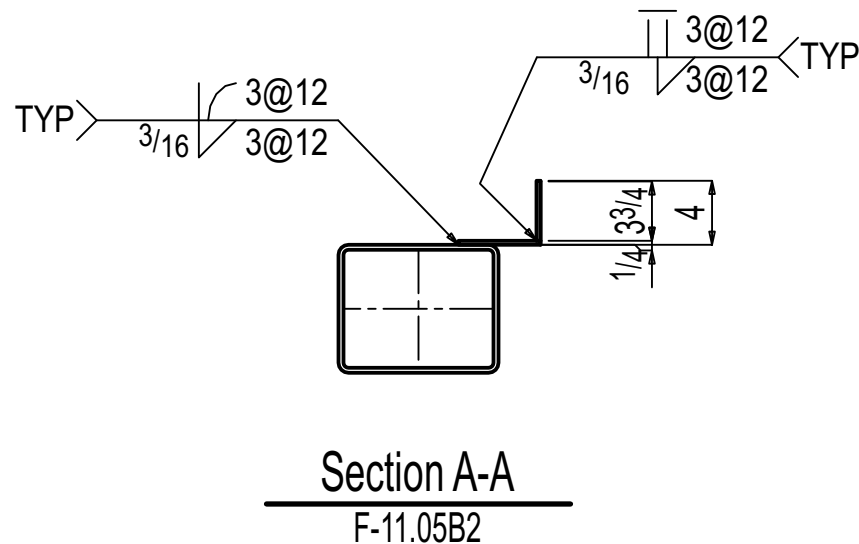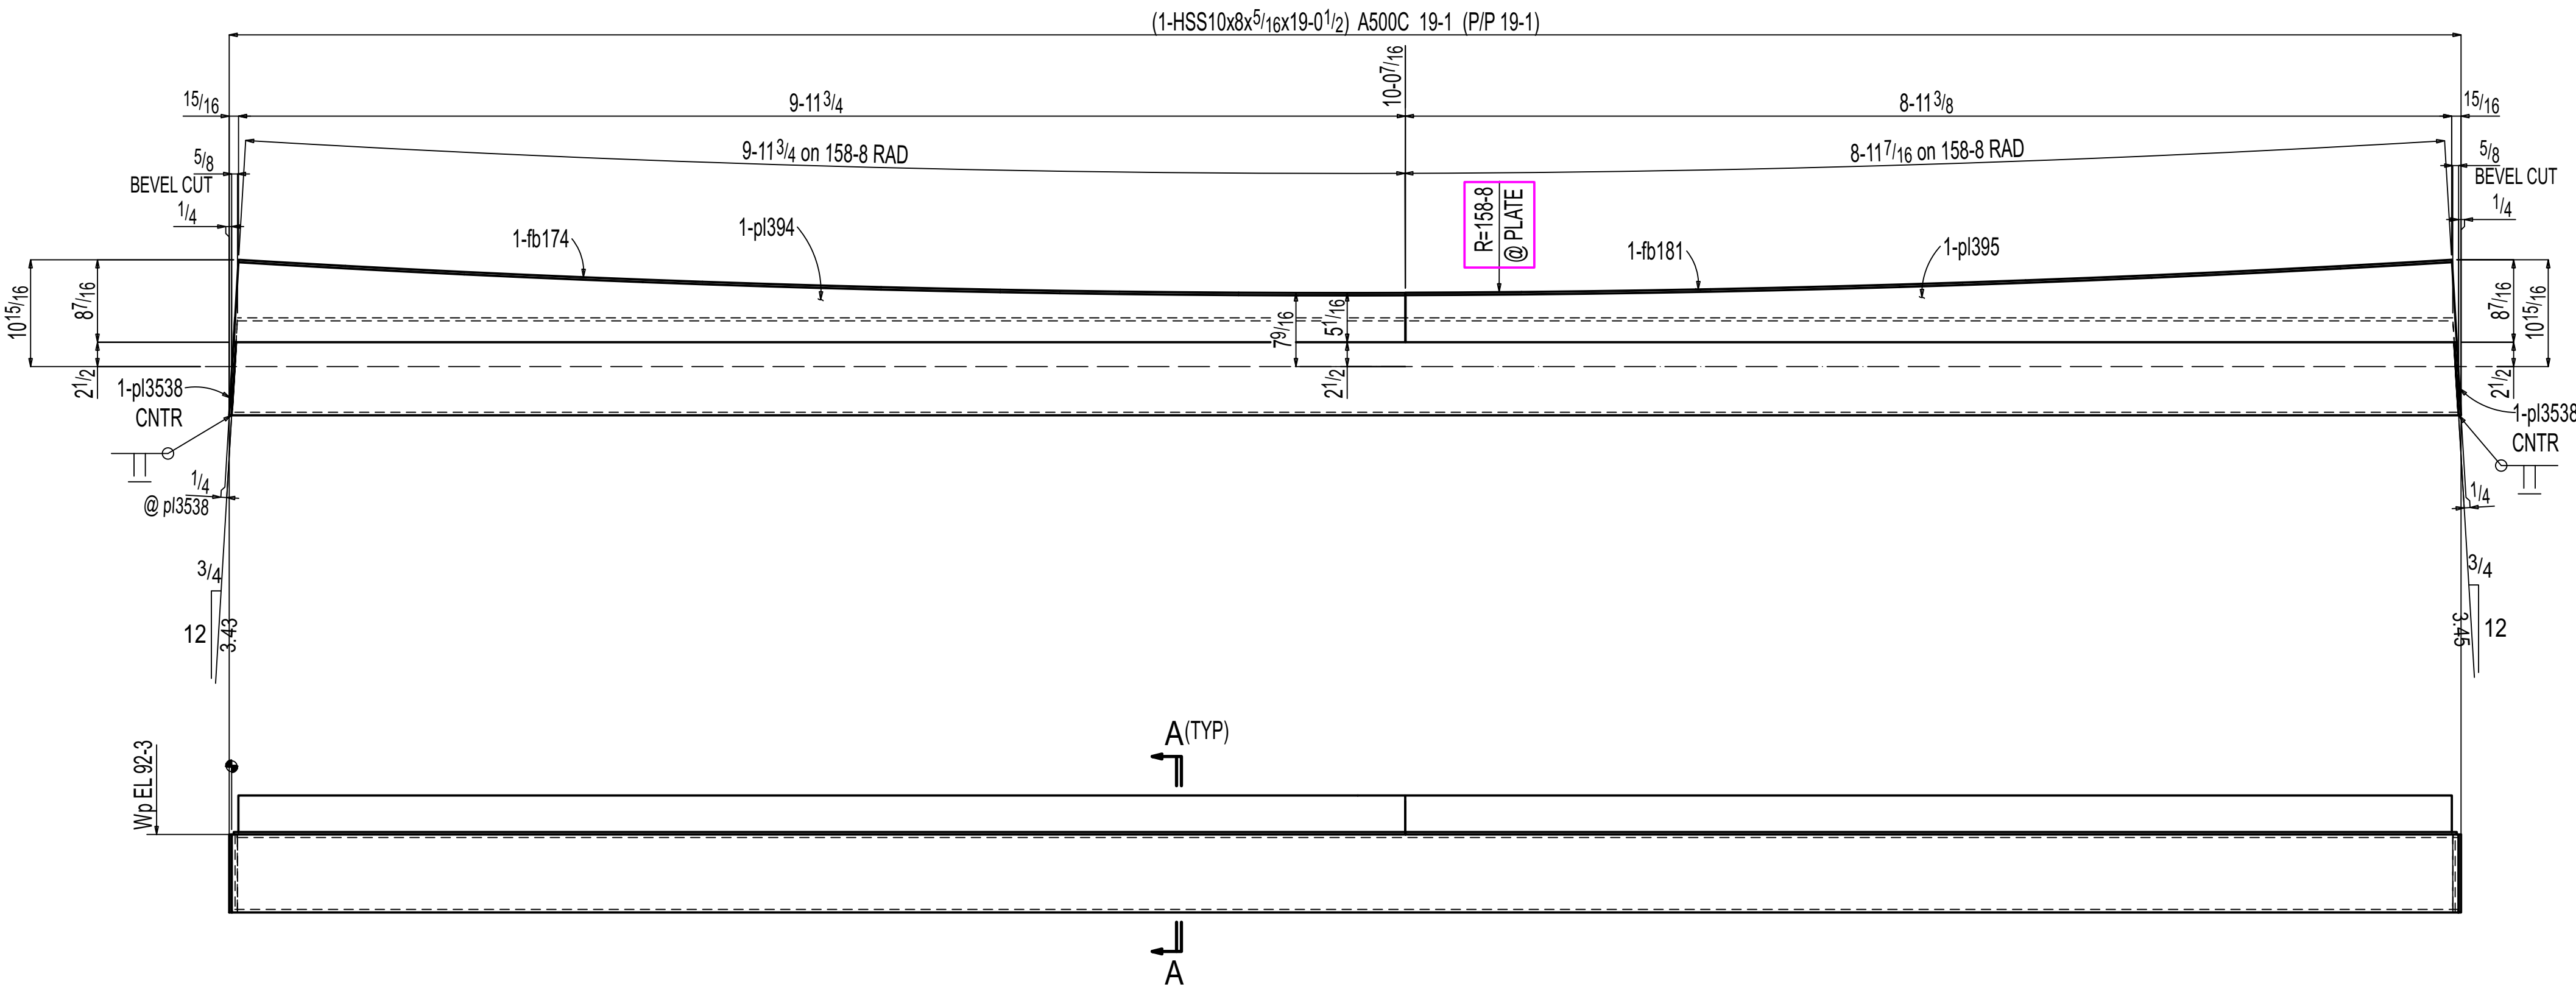

ONE BEAM F-11.05B2

General Notes			
*Structural steel shall conform to ASTM-A992.			
*Structural SQR/RND,tubing conform to ASTM A500 Grade C			
*Pipe shall conform to ASTM A53, Grade B.			
*Channels, Angles and plates shall conform to A36.			
*All bolts shall be 3/4" High strength in accordance with ASTM A325 (UNO)			
*Welding Electrodes for Carbon steel :E70xx			
# of Copies	Revision/ Issue	Destination	Date
5	0	For Fabrication	11-14-2025
4	D	For Re-Approval	10-24-2025
3	C	For Re-Approval	09-19-2025
2	B	For Re-Approval	06-23-2025
1	A	For Approval	02-25-2025

IRON FABRICATION SERVICES, LLC.

3029 M. Street, NW, Suite 202
Washington, DC 20007
Tel: 202-800-5599
Fax: 202-478-0303

Project Name and Address
MARYLAND AVENUE

Location: **1250 MARYLAND AVENUE SW
WASHINGTON, DC 20024**

Contractor:
BALFOUR BEATTY

Approved for Fabrication by: Signature

Contract # **224009** Drawing # **F-11.05**

Contract Item: **BEAM**


Ref:
SOW - 11: E-11.00 - E-11.02

Date
01/ 23/ 2025 Drawing Title:
BEAM DETAIL

Scale
VARIES

BILL OF MATERIAL							
LINE #	QTY	PC MARK	DESCRIPTION	LENGTH	REMARKS	WEIGHT TOTAL	ADVANCE MILL #
	ONE	F-11.0681	BEAM			769	
	1	F-11.0681	HSS10x8x3/16	16	1 15/16	A500C	584
	1	p13679	PL1/4x18 11/16	2	5 1/8	A36	39
	1	p1400	PL1/4x8 7/16	10	0 1/8	A36	72
	2	p13417	PL1/4x8	0	10	A36	11
	1	p1401	PL1/4x7 9/16	2	10 3/8	A36	18
	1	f614	FL1/4x4	2	10 1/2	A36	9
	1	f6177	FL1/4x3 1/4	9	11 3/4	A36	32
	1	p13673	PL1/4x3 1/4	1	6	A36	5
	ONE	F-11.0682	BEAM			287	
	1	F-11.0682	HSS8x4x5/16	12	1 3/8	A500C	283
	2	p13424	PL1/4x4	0	8	A36	5
	ONE	F-11.0683	BEAM			969	
	1	F-11.0683	HSS8x6x1 1/2	22	10 1/2	A500C	962
	2	p1467	PL1/4x6	0	8	A36	7
	ONE	F-11.06P1	PLATE			9	
	1	F-11.06P1	PL3/8x8	0	10	A36	9
	ONE	F-11.06P2	PLATE			9	
	1	F-11.06P2	PL3/8x8	0	10	A36	9
	2	F-11.06P3	PLATE			8	
	2	F-11.06P3	FL3/8x4	0	10	A36	8
	ONE	F-11.06P4	PLATE			6	
	1	F-11.06P4	PL3/8x6	0	10	A36	6
	ONE	F-11.06P5	PLATE			3	
	1	F-11.06P5	FL3/8x4	0	10 7/16	A36	3

Total weight : 2060

 

IRON FABRICATION SERVICES, LLC.

3029 M. Street, NW, Suite 202
Washington, DC 20007
Tel: 202-800-5599
Fax: 202-478-0303

Contractor: **BALFOUR BEATTY**


Contract Item: BEAM DETAIL
Ref:

Scale VARIES	
-----------------	--


100

BILL OF MATERIAL							
LINE #	QTY	PC MARK	DESCRIPTION	LENGTH	REMARKS	WEIGHT	ADVANCE
	TOTAL	MARK	DESCRIPTION			TOTAL	MILL #
	ONE	F-11.07B1	BEAM			516	
1		F-11.07B1	HSS6x6x $\frac{1}{2}$	14	5 $\frac{13}{16}$ A500C	511	
2		p696	PL $\frac{1}{4}$ x6	0	6 A36	5	
6		F-11.07M1	PLATE			68	
6		F-11.07M1	PL $\frac{1}{2}$ x8	0	10 A36	68	
6		F-11.07M2	PLATE			34	
6		F-11.07M2	FL $\frac{1}{2}$ x4	0	10 A36	34	
ONE		F-11.07A1	ANGLE			145	
1		F-11.07A1	L4x4x $\frac{3}{16}$	17	8 $\frac{5}{8}$ A36	145	
			FIELD BOLTS				
27			$\frac{1}{2}$ " Ø HILTI HAS V-36	0	4 $\frac{1}{2}$ (2 $\frac{3}{4}$ " EMBEDMENT)		
			w/ HILTI HIT HY-200 V3				
			ADHESIVE				
ONE		F-11.07A2	ANGLE			126	
1		F-11.07A2	L4x4x $\frac{3}{16}$	15	4 $\frac{9}{16}$ A36	126	
			FIELD BOLTS				
24			$\frac{1}{2}$ " Ø HILTI HAS V-36	0	4 $\frac{1}{2}$ (2 $\frac{3}{4}$ " EMBEDMENT)		
			w/ HILTI HIT HY-200 V3				
			ADHESIVE				
ONE		F-11.07A3	ANGLE			136	
1		F-11.07A3	L4x4x $\frac{3}{16}$	16	7 $\frac{1}{16}$ A36	136	
			FIELD BOLTS				
25			$\frac{1}{2}$ " Ø HILTI HAS V-36	0	4 $\frac{1}{2}$ (2 $\frac{3}{4}$ " EMBEDMENT)		
			w/ HILTI HIT HY-200 V3				
			ADHESIVE				


Total weight : 1025

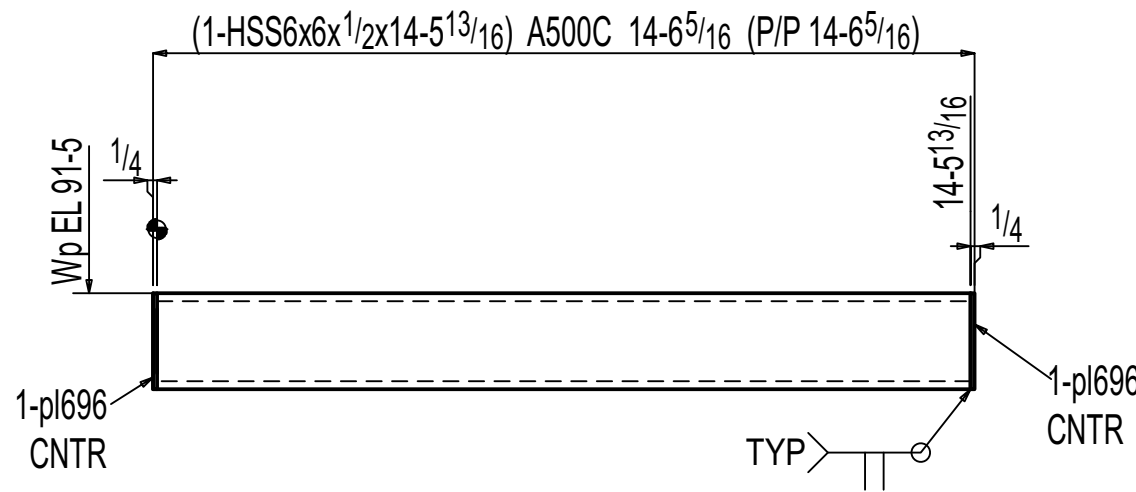

ONE BEAM F-11.07B1

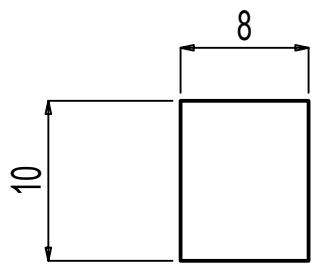


6 PLATES F-11.07M1

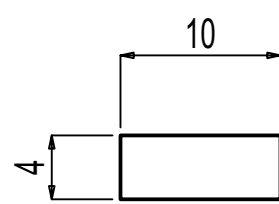


6 PLATES F-11.07M2

NOT IN USE


ONE HSS F-11.07M3

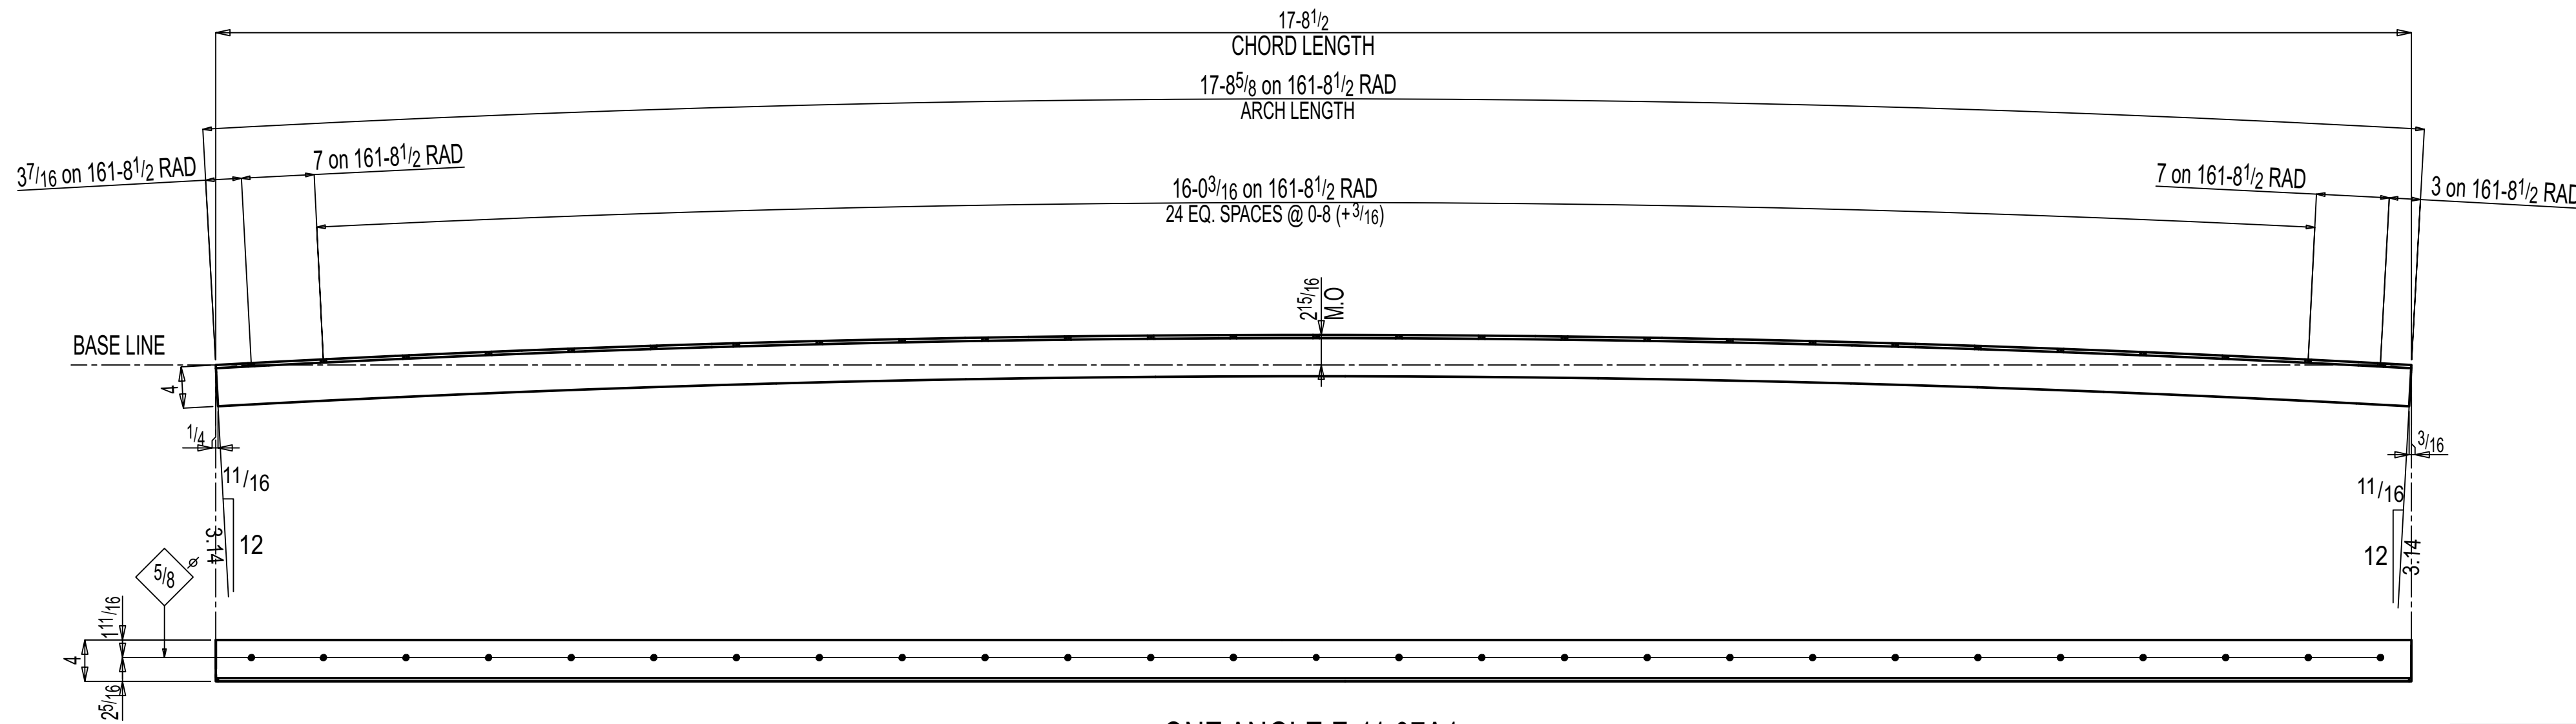

ONE ANGLE F-11.07A1

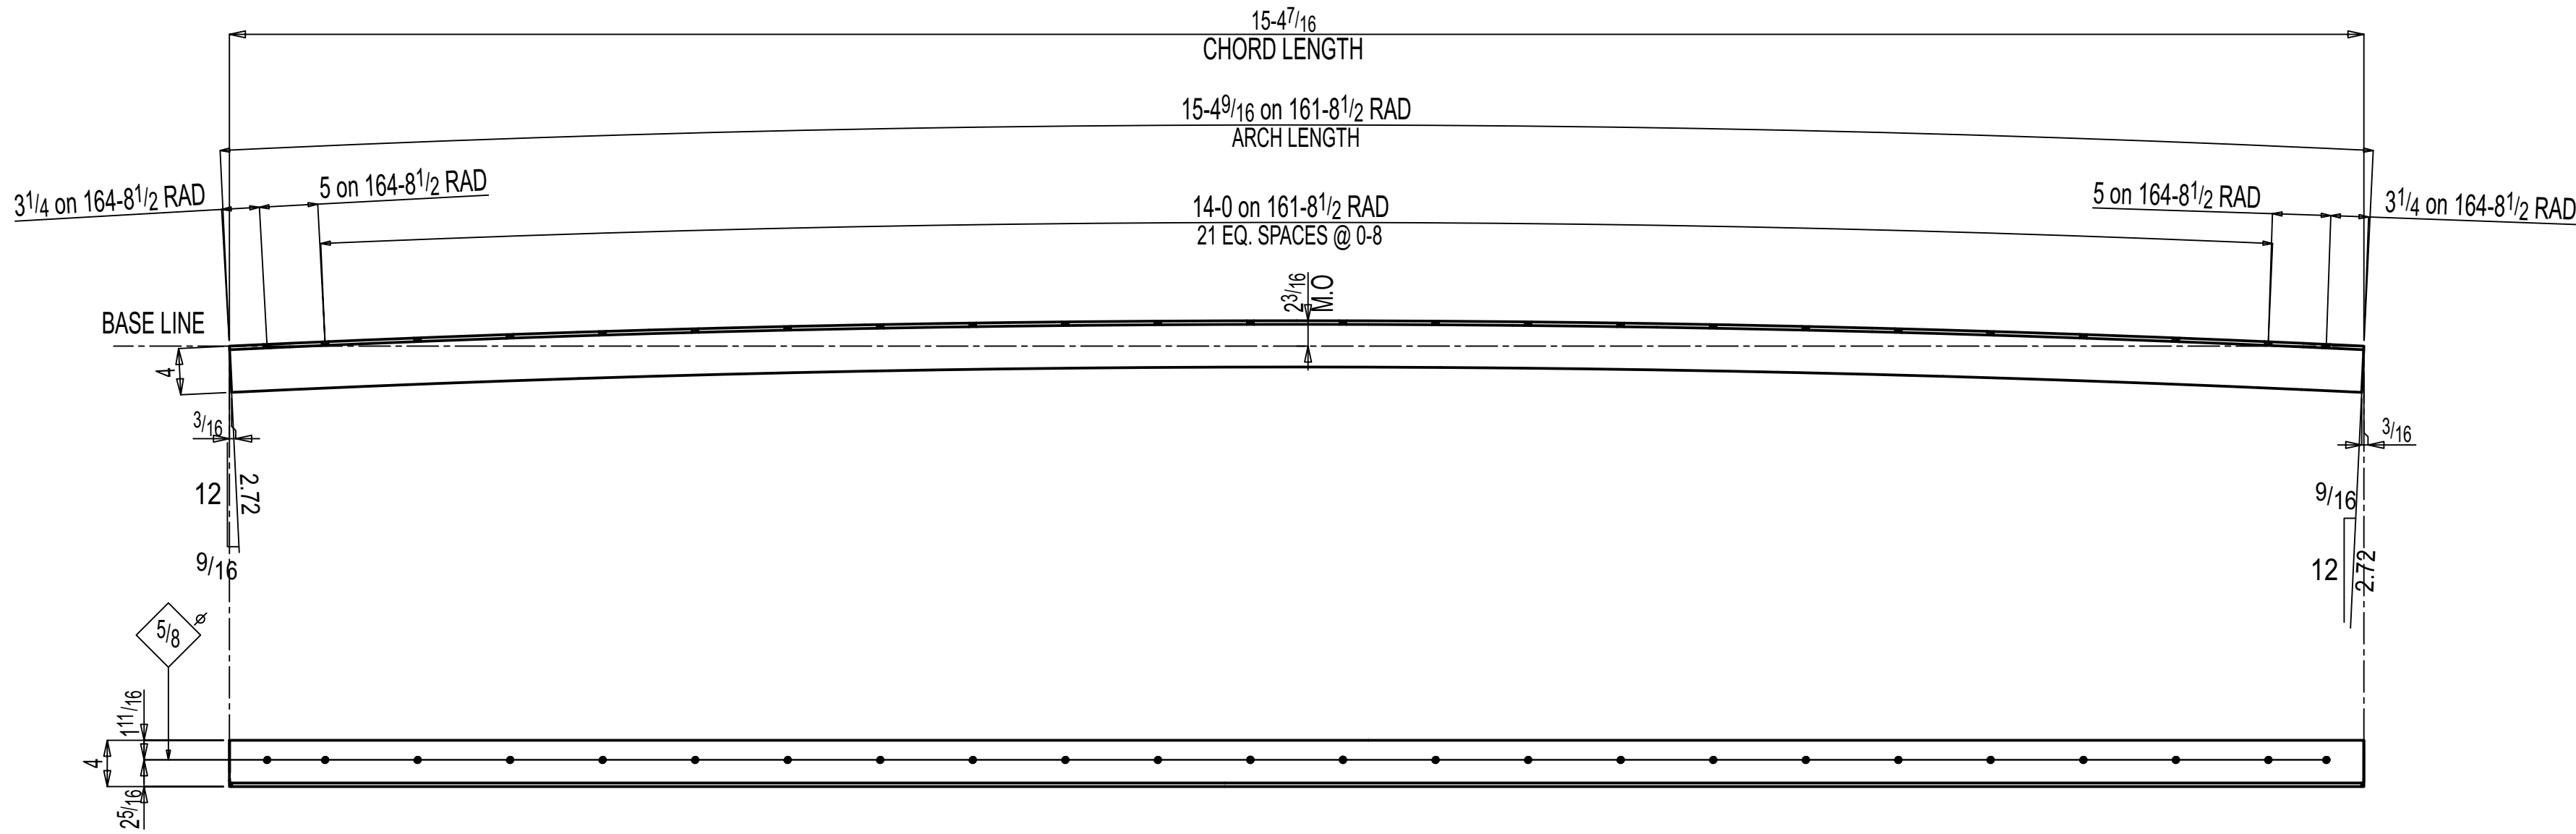

ONE ANGLE F-11.07A2

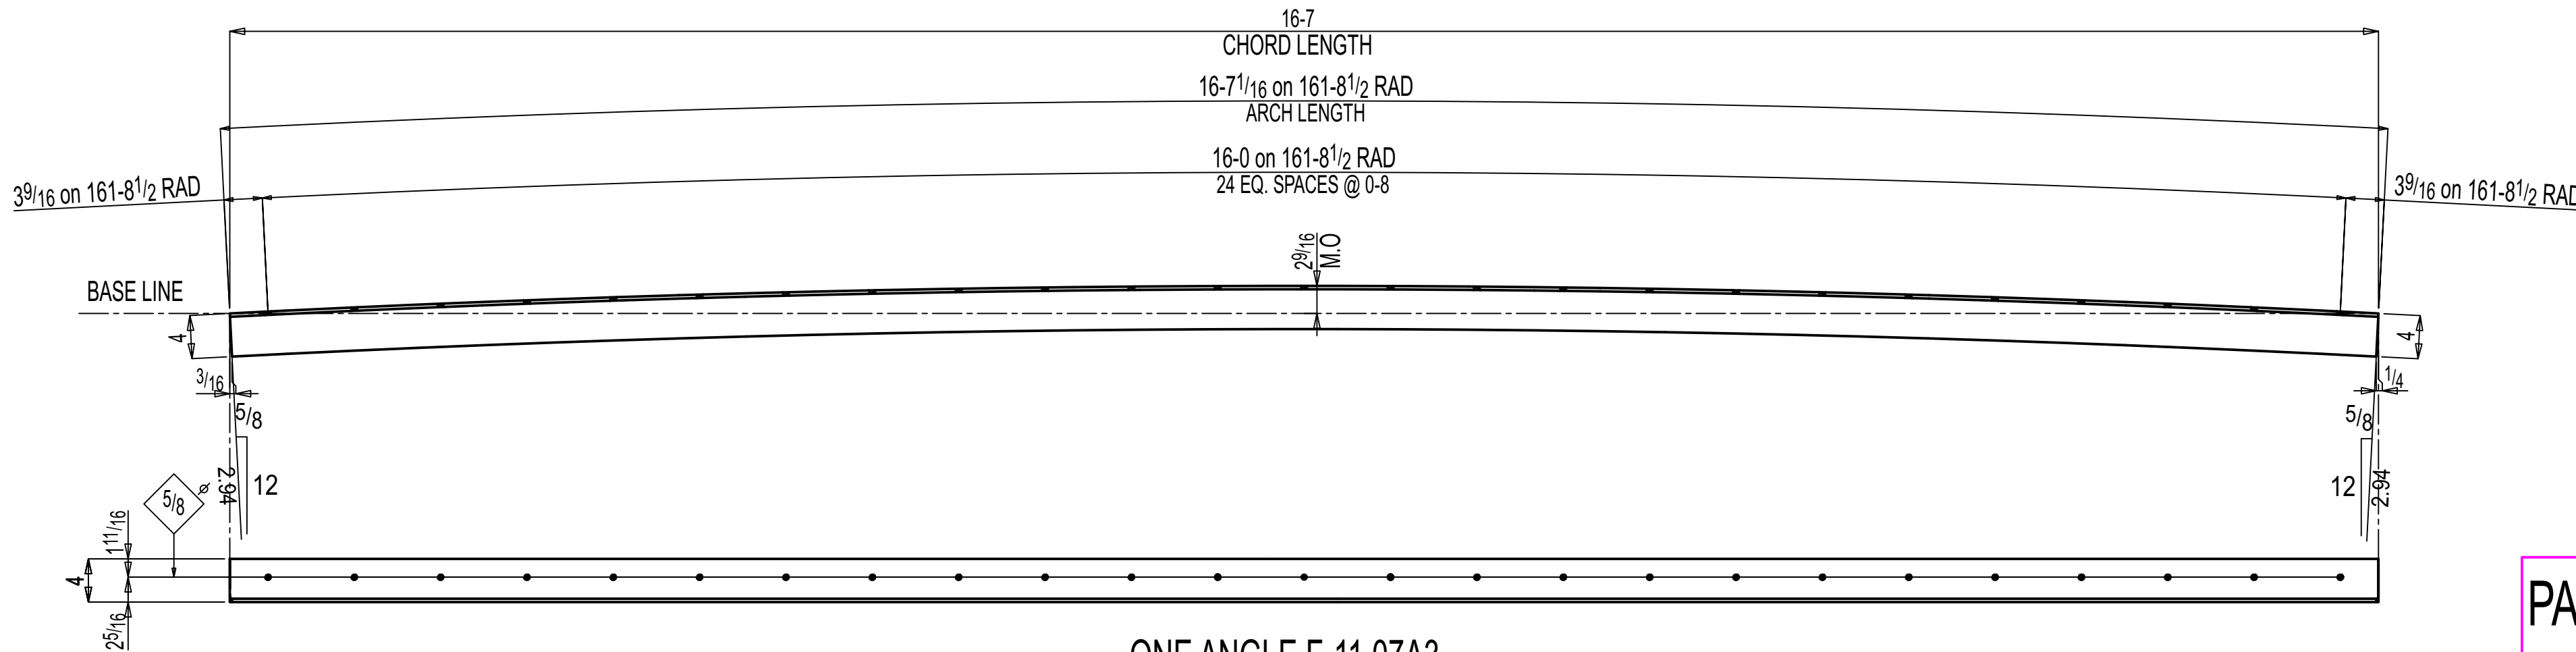

ONE ANGLE F-11.07A3

PAINT PREPARATION :NO PAINT :SSPC-SP3

General Notes

- *Structural steel shall conform to ASTM-A992.
- *Structural SQR/RND,tubing conform to ASTM A500 Grade C
- *Pipe shall conform to ASTM A53, Grade B.
- *Channels, Angles and plates shall conform to A36.
- *All bolts shall be $\frac{3}{4}$ " High strength in accordance with ASTM A325 (UNO)
- *Welding Electrodes for Carbon steel :E70xx

# of Copies	Revision/ Issue	Destination	Date
4	0	For Fabrication	11-14-2025
3	C	For Re-Approval	10-24-2025
2	B	For Re-Approval	09-19-2025
1	A	For Approval	06-23-2025

IRON FABRICATION SERVICES, LLC.

3029 M. Street, NW, Suite 202
Washington, DC 20007
Tel: 202-800-5599
Fax: 202-478-0303

Project Name and Address

MARYLAND AVENUE
Location: **1250 MARYLAND AVENUE SW**
WASHINGTON, DC 20024

Contractor:

BALFOUR BEATTY

Approved for Fabrication by:	Signature
------------------------------	-----------

Contract # 224009	Drawing # F-11.07
--------------------------	--------------------------

Contract Item:

FRAME

Ref:

SOW - 11: E-11.00 - E-11.02

Date 01/23/2025	Drawing Title: BEAM & MISCELLANEOUS DETAIL
Scale VARIES	