
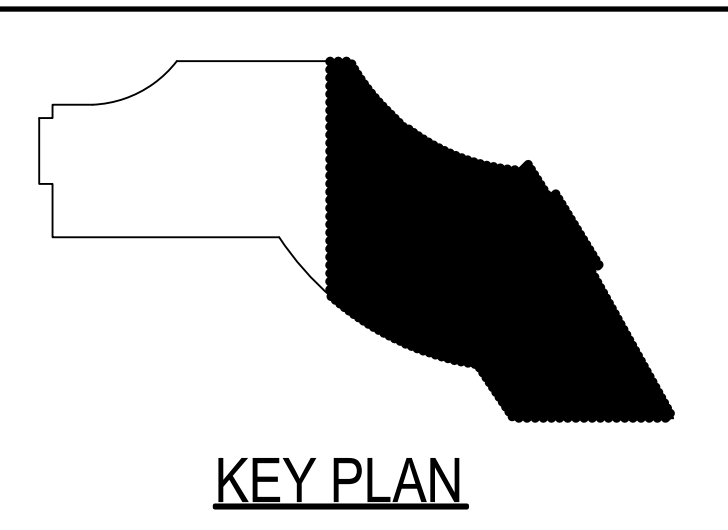


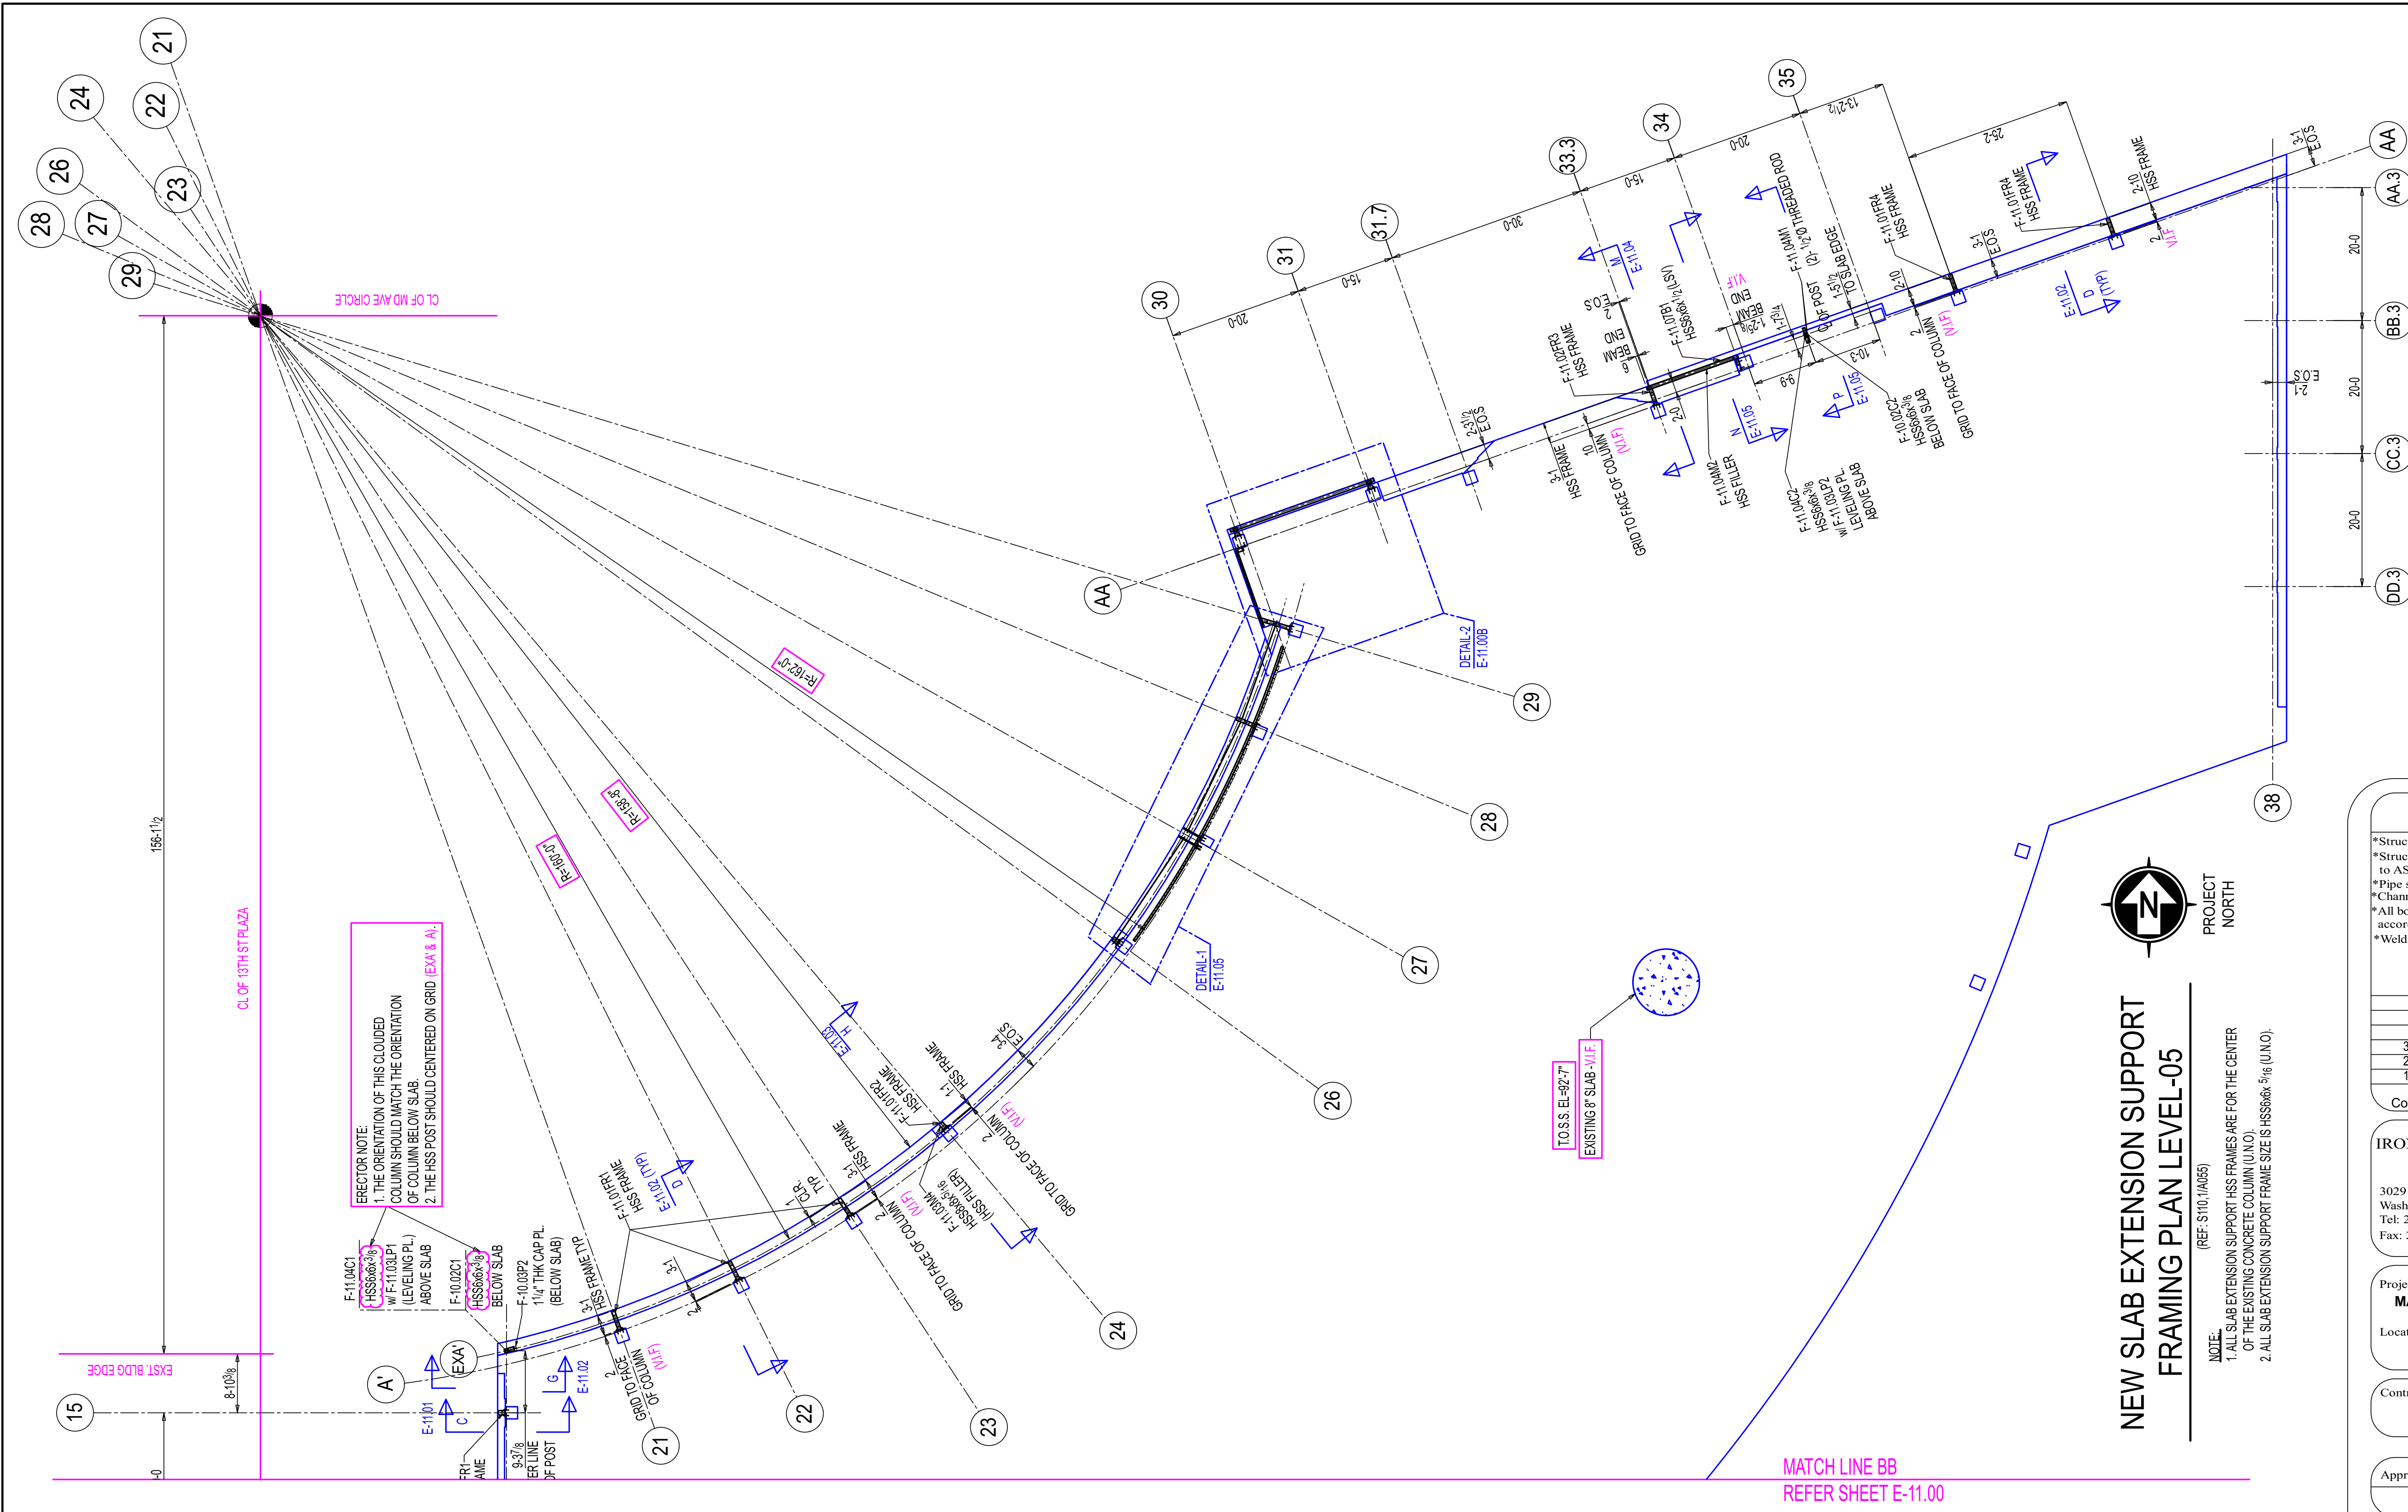

NEW SLAB EXTENSION SUPPORT
FRAMING PLAN LEVEL-05

NOTE:
1. ALL SLAB EXTENSION SUPPORT HSS FRAMES ARE FOR THE CENTER OF THE EXISTING CONCRETE COLUMN (U.N.O.).
2. ALL SLAB EXTENSION SUPPORT FRAME SIZE IS HSS60x5 1/6 (U.N.O.).

General Notes

- *Structural steel shall conform to ASTM-A992.
- *Structural SQR/RND.tubing conform to ASTM A500 Grade C
- *Pipe shall conform to ASTM A53, Grade B.
- *Channels, Angles and plates shall conform to A36.
- *All bolts shall be 3/4" High strength in accordance with ASTM A325 (UNO)
- *Welding Electrodes for Carbon steel :E70xx

# of Copies	Revision/ Issue	Destination	Date
3	0	For Construction	11-14-2025
2	B	For Re-Approval	10-24-2025
1	A	For Approval	09-19-2025

IRON FABRICATION SERVICES, LLC.

3029 M. Street, NW, Suite 202
Washington, DC 20007
Tel: 202-800-5599
Fax: 202-478-0303

Project Name and Address
MARYLAND AVENUE

Location: **1250 MARYLAND AVENUE SW
WASHINGTON, DC 20024**

Contractor:
BALFOUR BEATTY

Approved for Fabrication by: _____
Signature

Contract # 224009	Drawing # E-11.00A
Contract Item: LEVEL-05 SLAB EXTENSION	
Ref: SOW-11: (S110,1/A055)	
Date 01/20/2025	Drawing Title: SOW #11 LEVEL-05 NEW SLAB EXTENSION SUPPORT FRAMING PLAN
Scale VARIES	