


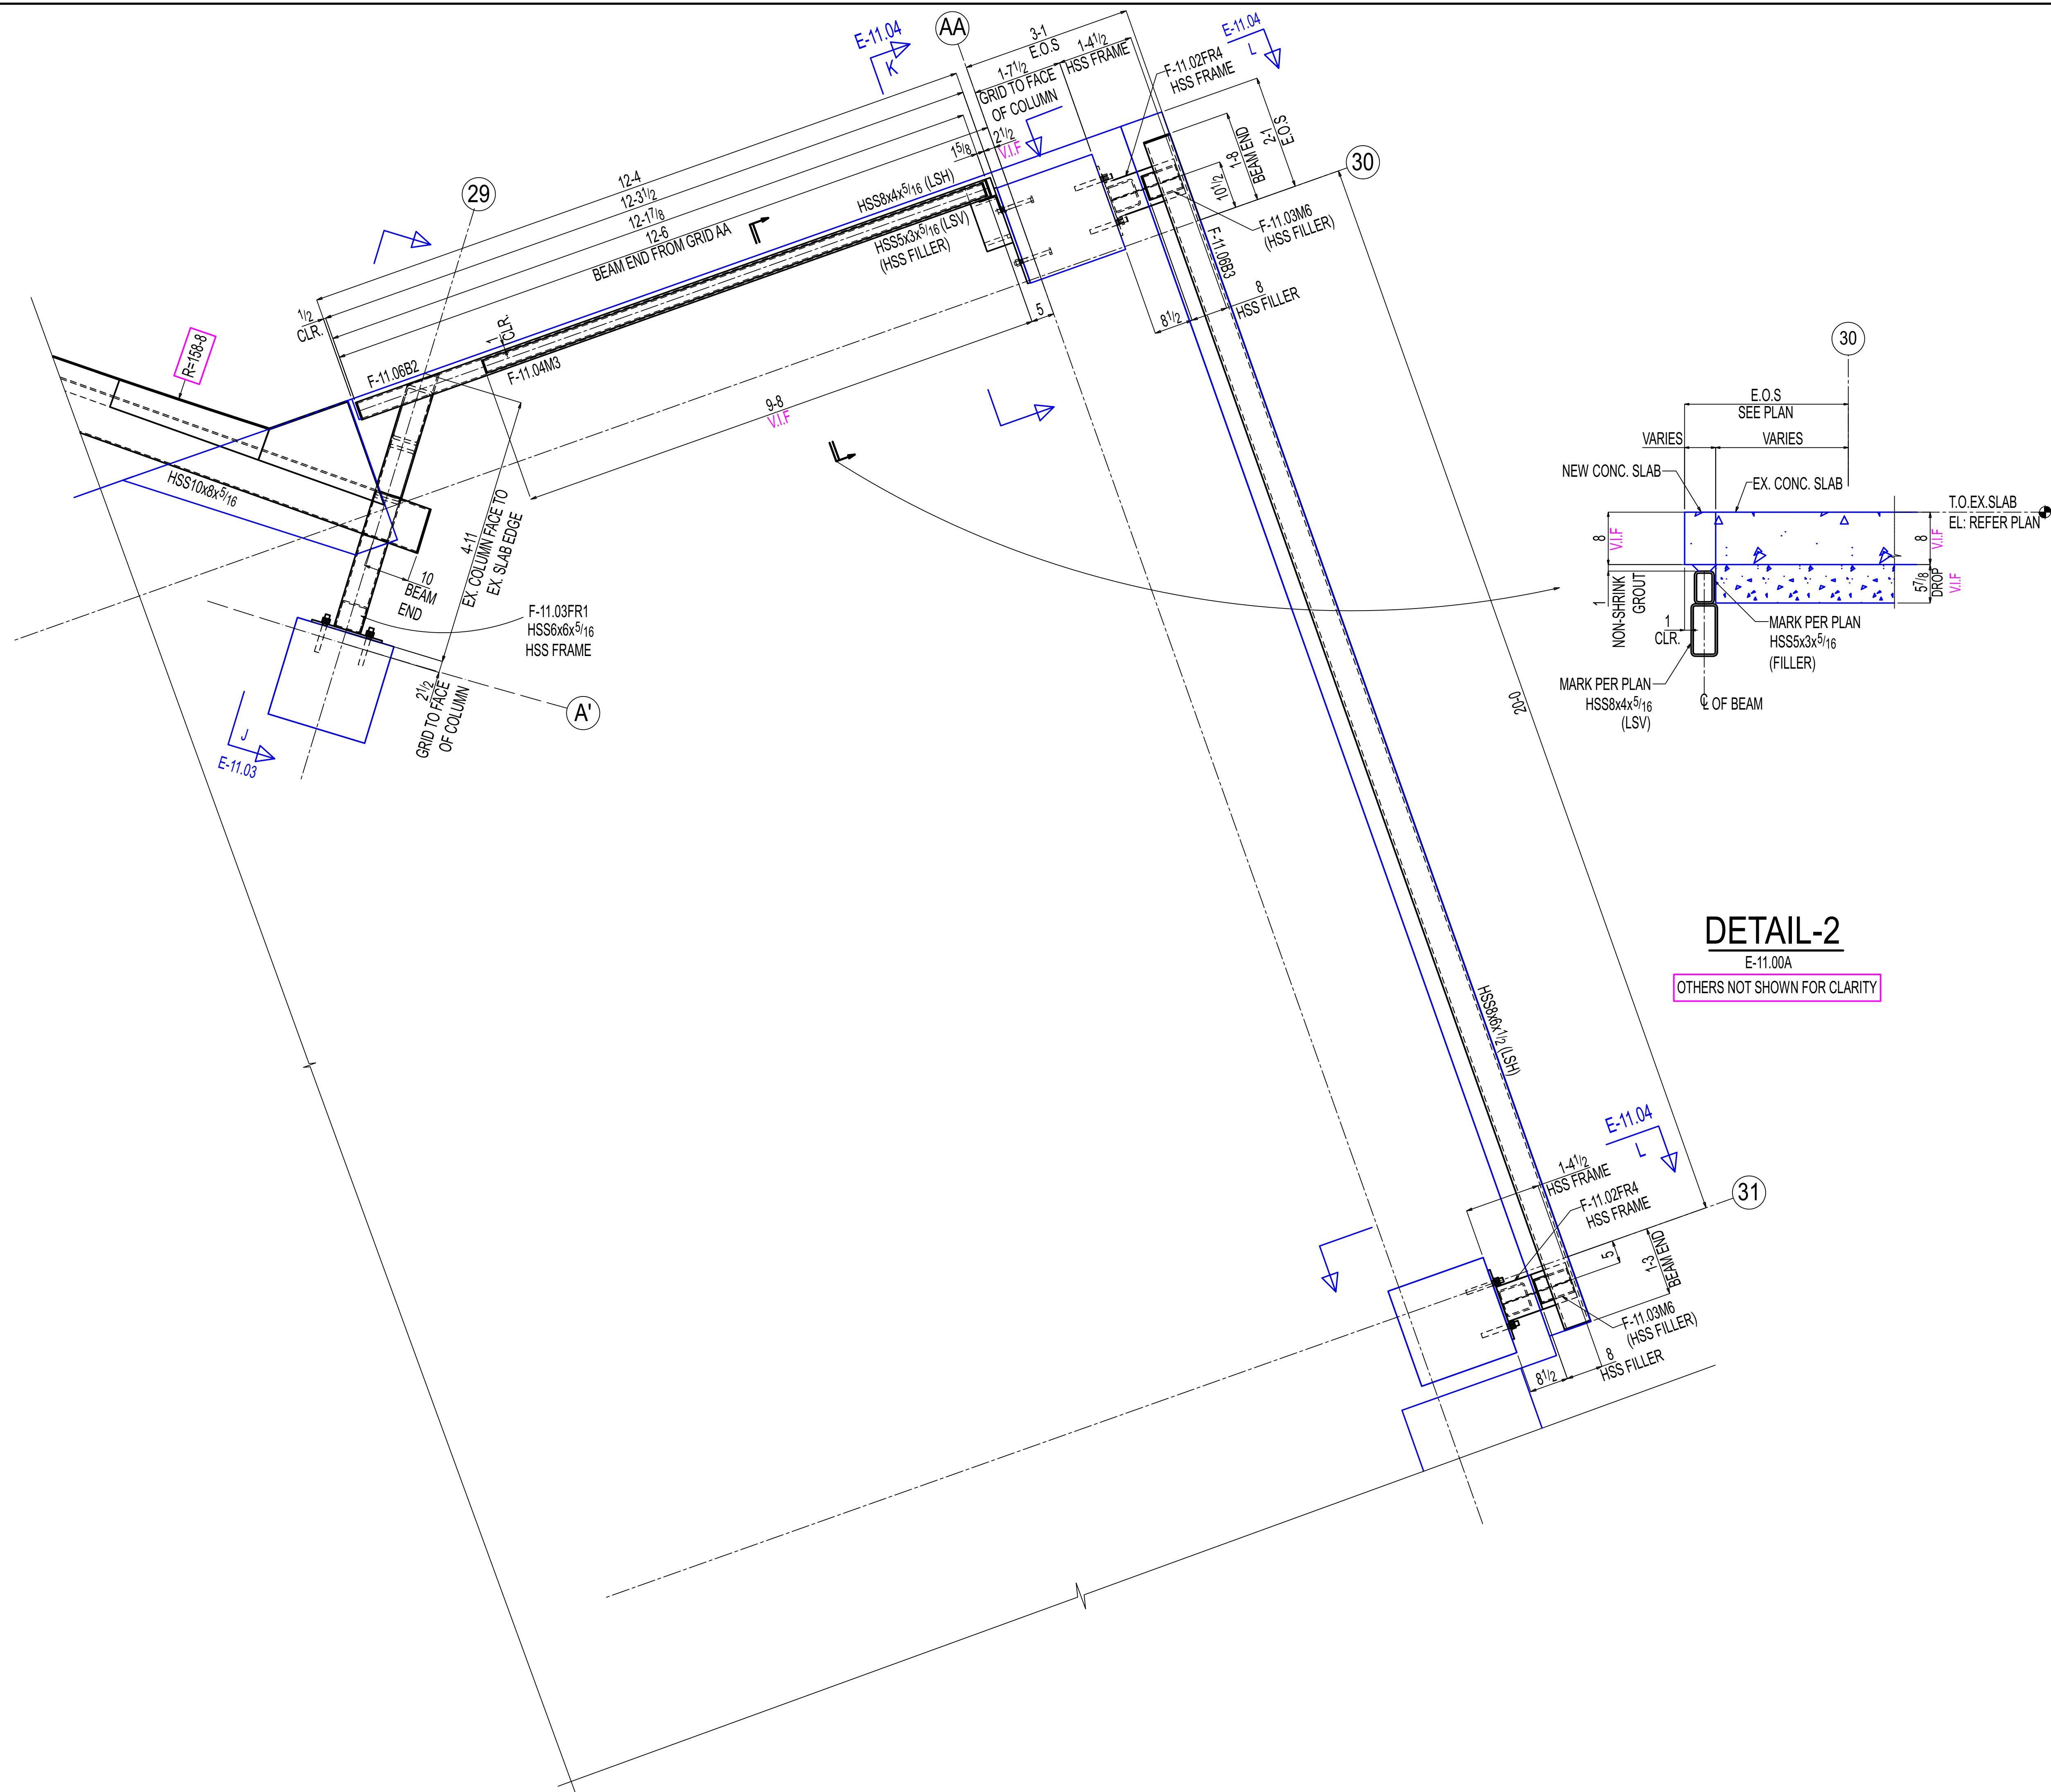

E-11.00A

OTHERS NOT SHOWN FOR CLARITY

- *Structural steel shall conform to ASTM-A992.
- *Structural SQR/RND.tubing conform to ASTM A500 Grade C
- *Pipe shall conform to ASTM A53, Grade B.
- *Channels, Angles and plates shall conform to A36.
- *All bolts shall be $\frac{3}{4}$ " High strength in accordance with ASTM A325 (UNO)
- *Welding Electrodes for Carbon steel :E70xx

1	0	For Construction	11-14-2025
# of Copies	Revision/ Issue	Destination	Date

3029 M. Street, NW, Suite 202
Washington, DC 20007
Tel: 202-800-5599
Fax: 202-478-0303

Location: **1250 MARYLAND AVENUE SW**
WASHINGTON, DC 20024

Approved for Fabrication by:	Signature
------------------------------	-----------

Contract # 224009		Drawing # E-11.00B
Contract Item: LEVEL-05 SLAB EXTENSION		
Ref: SOW-11: (S110,1/A055)		
Date 01/20/2025	Drawing Title: SOW #11 LEVEL-05 DETAIL VIEW	
Scale VARIABLES		