


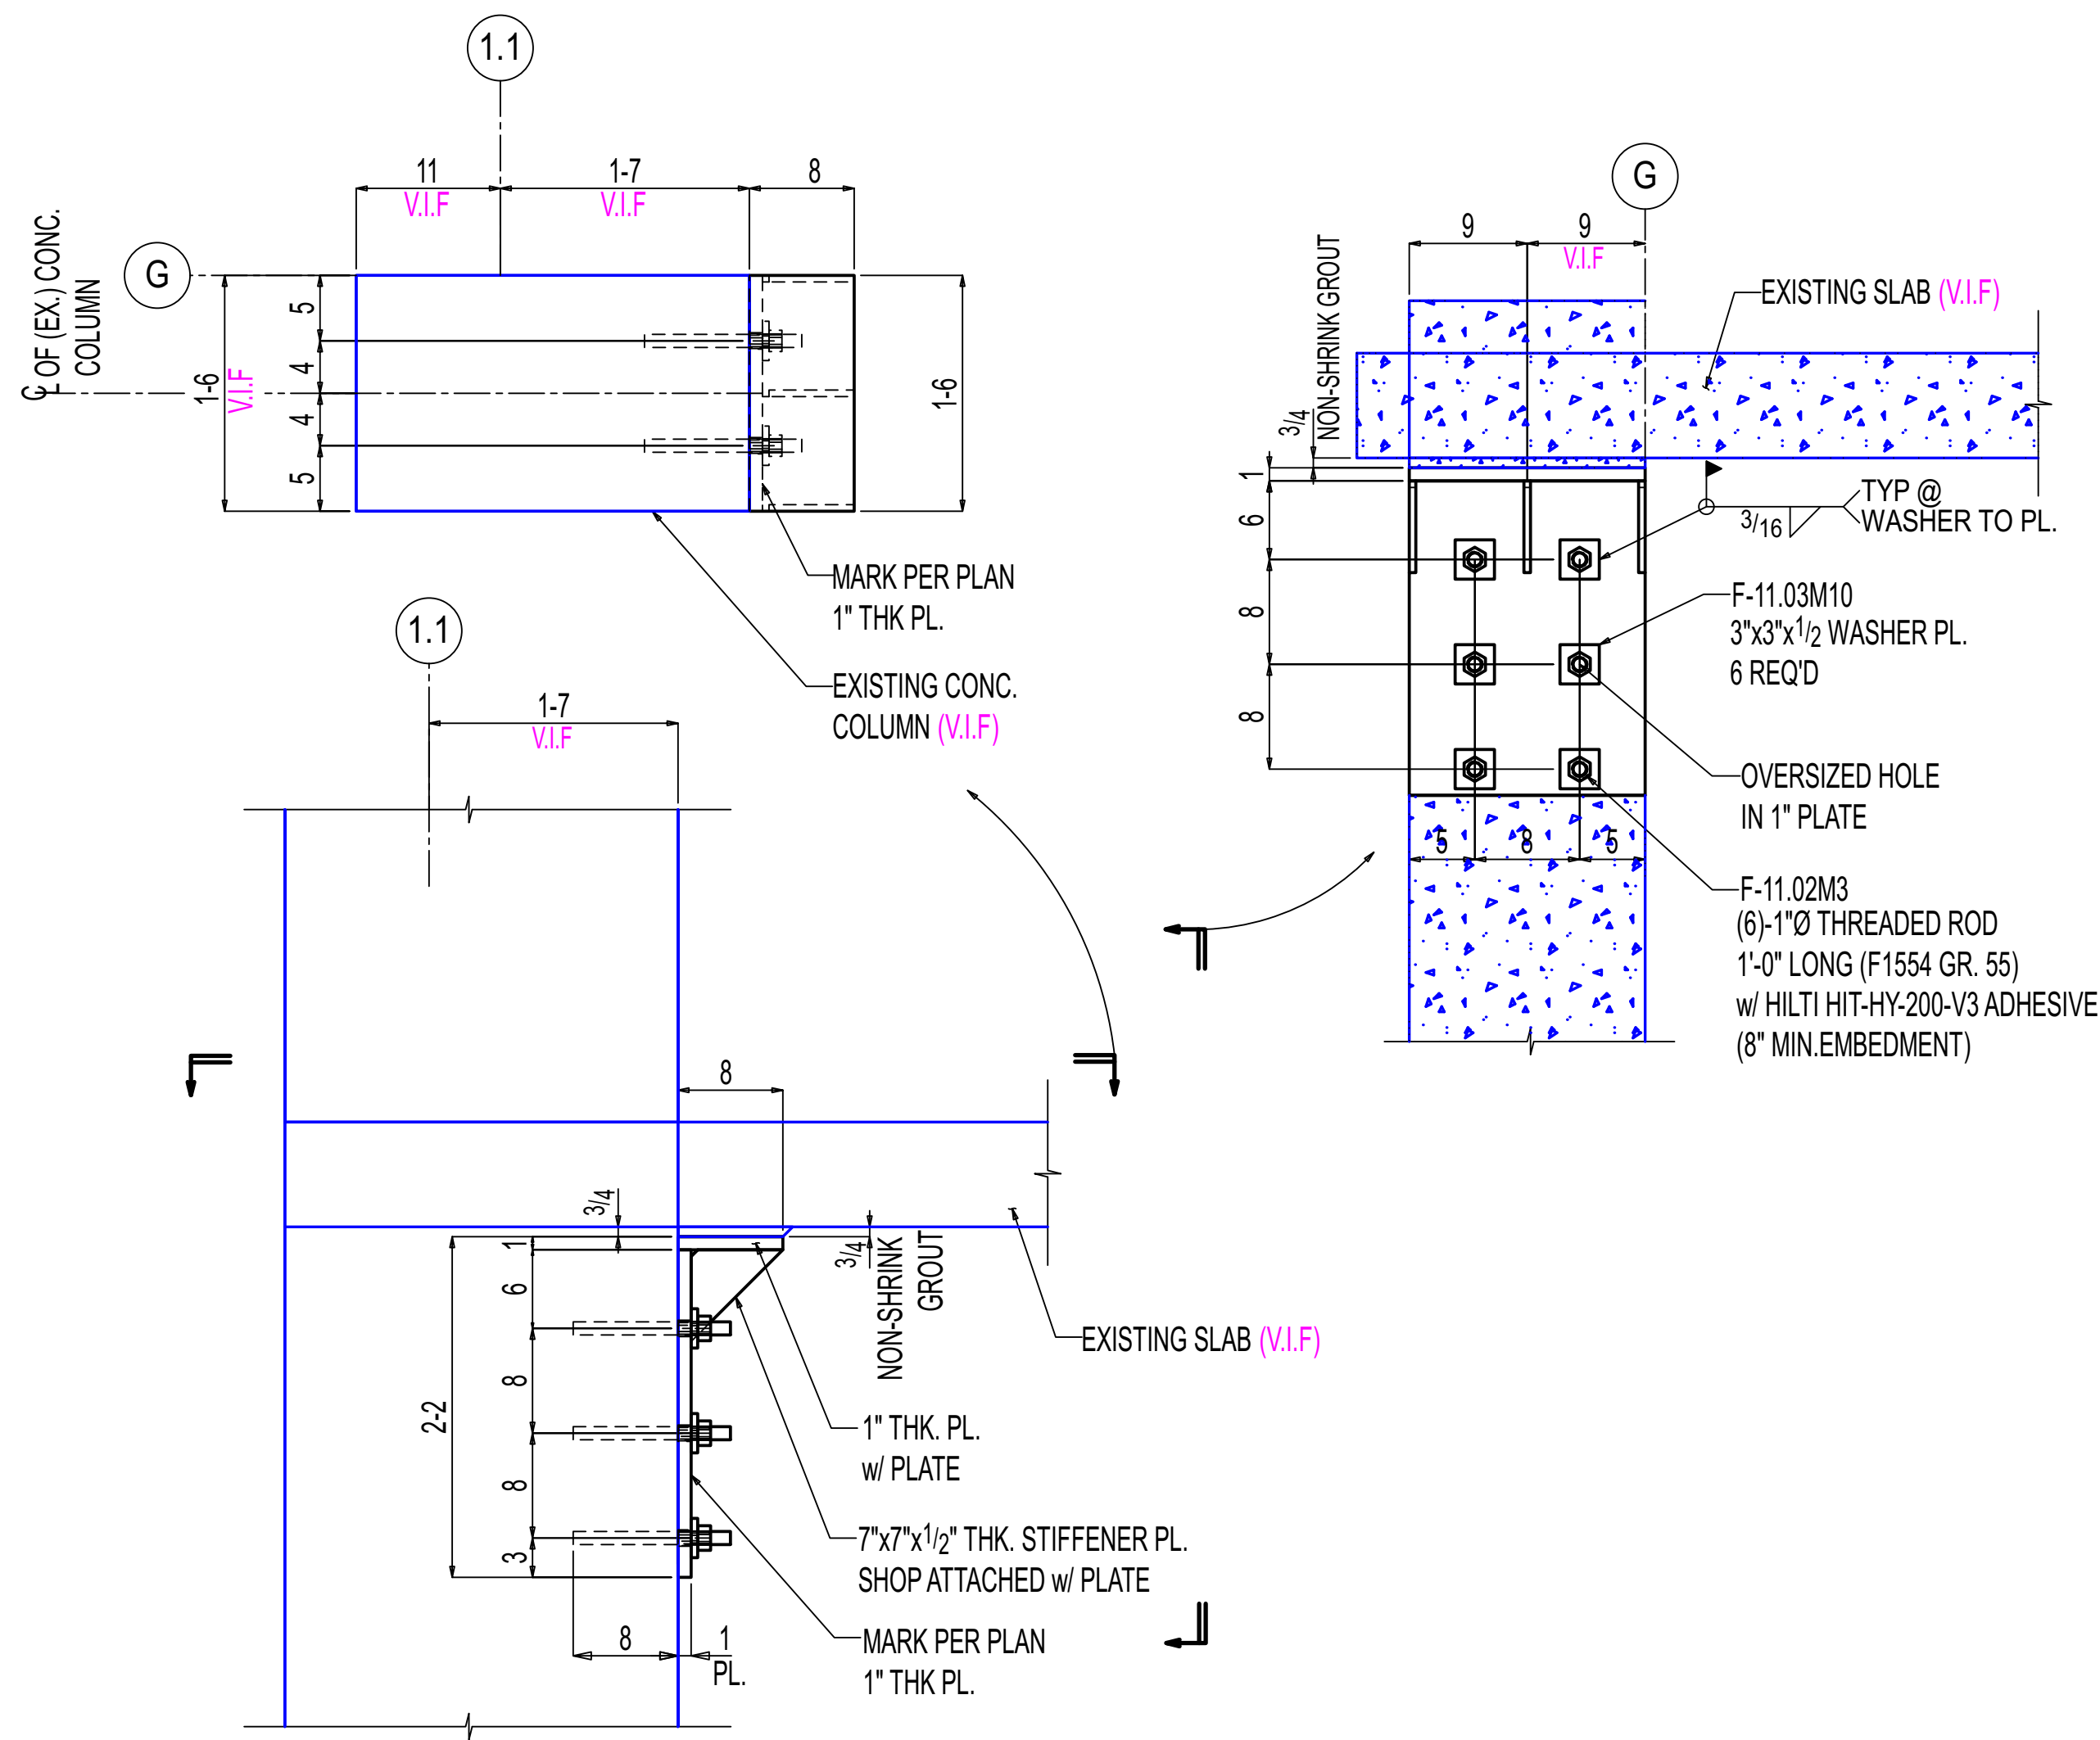

A-A

E-11.00
(REF: 4/S317)

OTHERS NOT SHOWN FOR CLARITY

NOTE:


- DO NOT CUT EXISTING REBAR WHEN DRILLING FOR NEW BOLTS. GPR CONCRETE TO LOCATE REBAR PRIOR TO FINAL STEEL FABRICATION AND DRILLING. SPACING OF HOLES SHALL BE COORDINATED BY CONTRACTOR WITH RGA FOR EXISTING FIELD CONDITIONS.
- INSTALL WASHER PLATE SO TOP OF THREADED ROD IS IN BEARING WITH WASHER PRIOR TO WELDING AND NON-SHRINK GROUT PLACEMENT.
- AFTER THREADED ROD IS INSERTED, PRESSURE INJECT DURAL 452LV OR APPROVED ALTERNATIVE FULL WIDTH OF COLUMN.

NOT IN USE

B-B

E-11.00

OTHERS NOT SHOWN FOR CLARITY

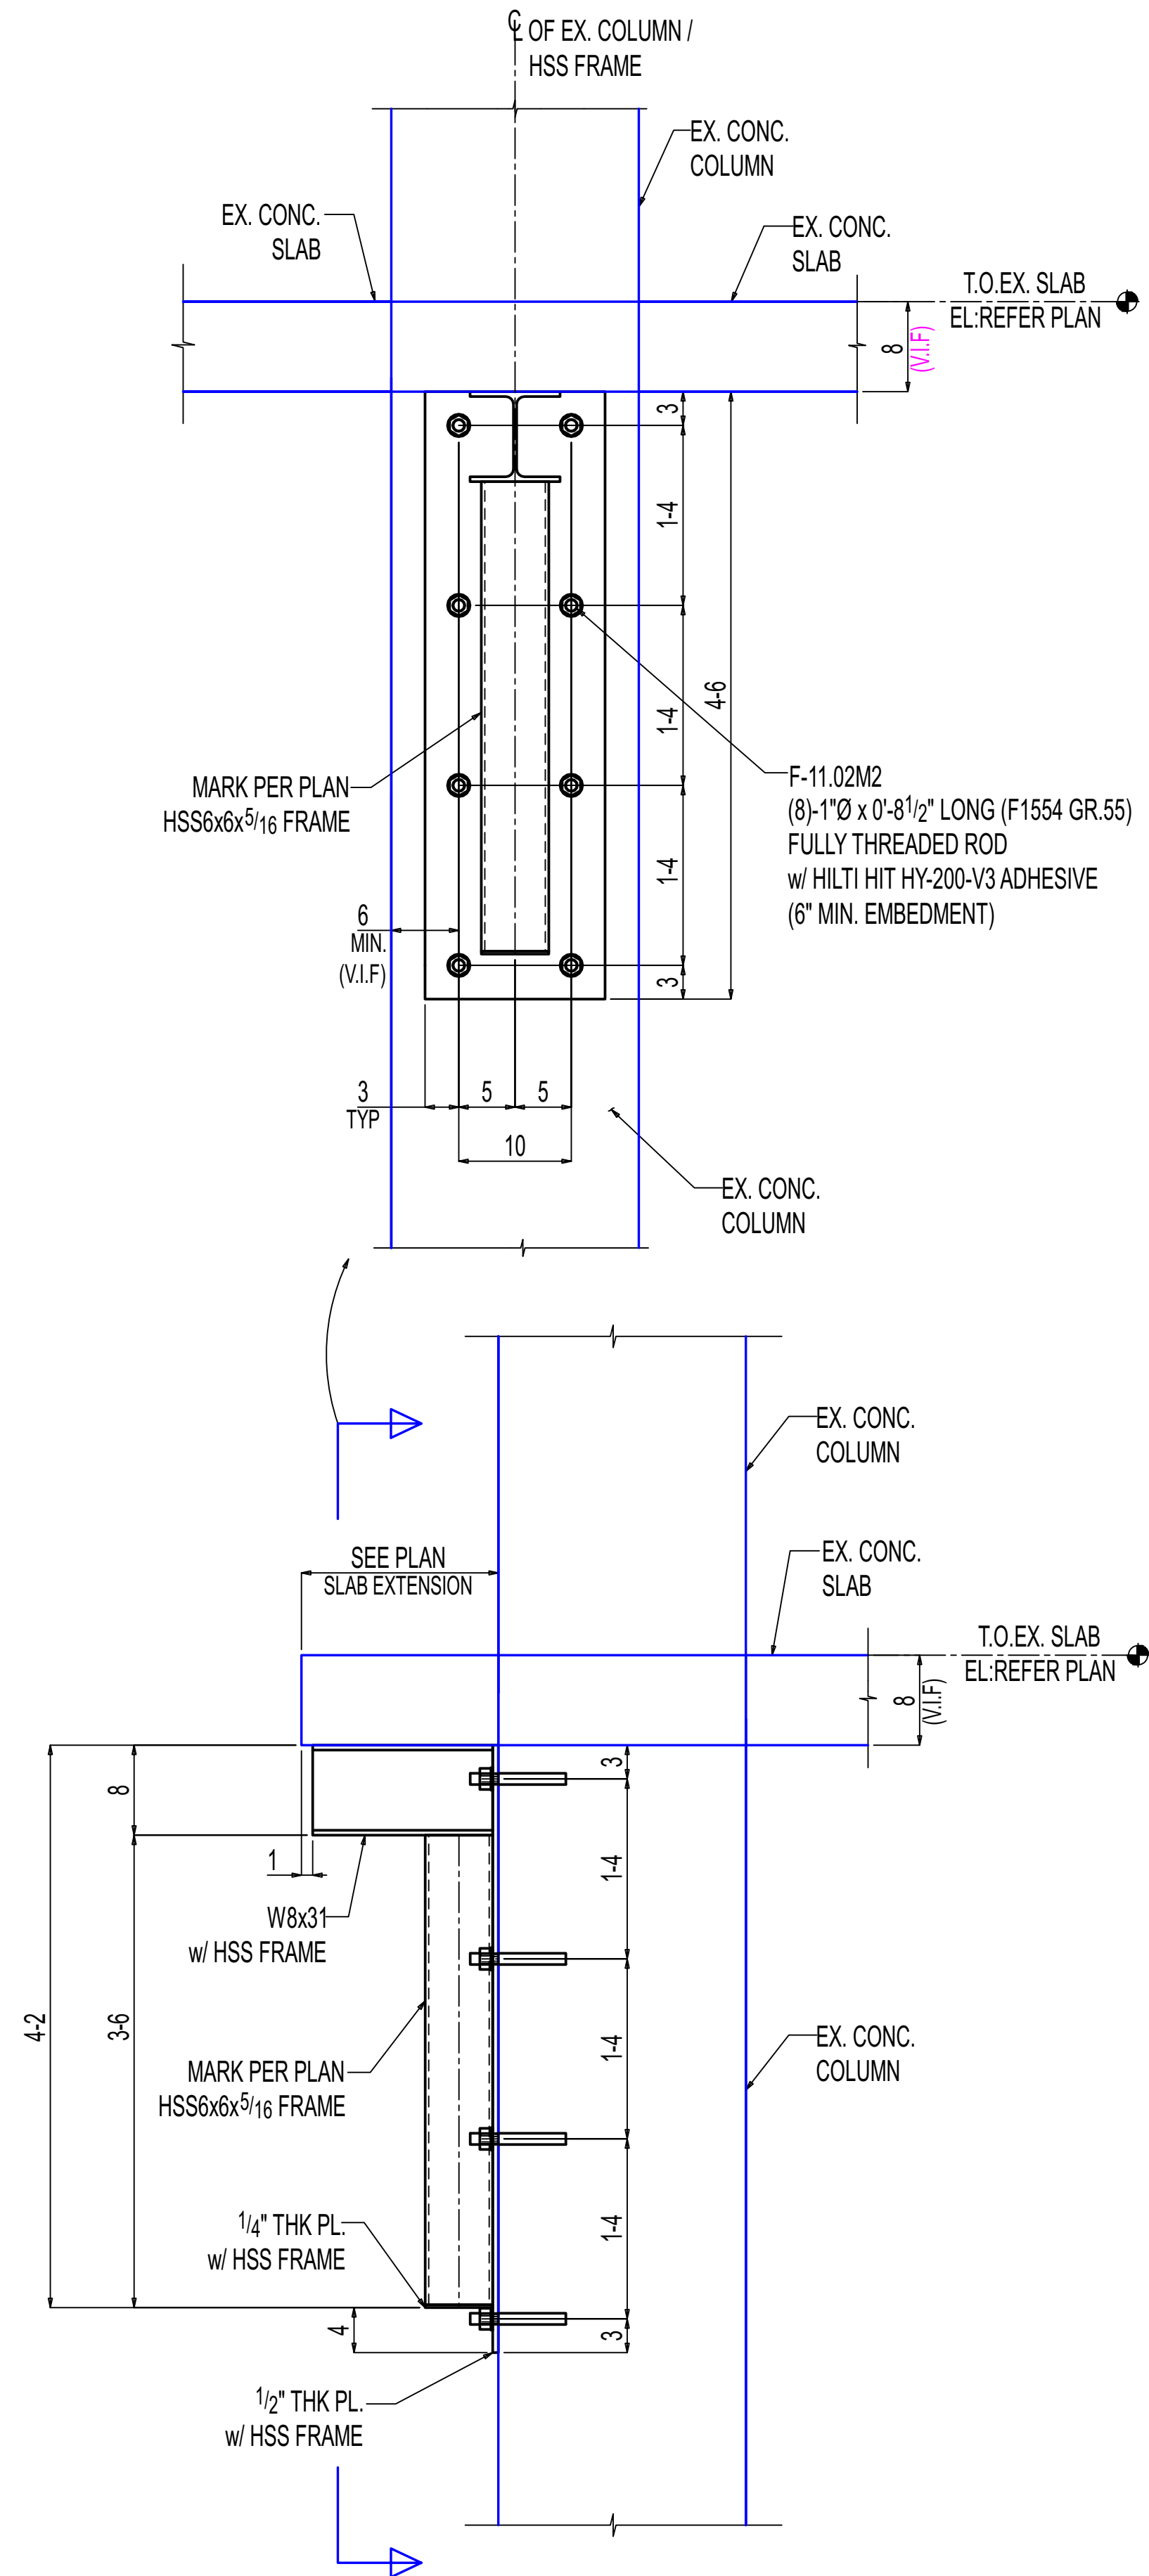

C-C

E-11.00
(REF: 11/S314)

OTHERS NOT SHOWN FOR CLARITY

General Notes

- *Structural steel shall conform to ASTM-A992.
- *Structural SQR/RND tubing conform to ASTM A500 Grade C
- *Pipe shall conform to ASTM A53, Grade B.
- *Channels, Angles and plates shall conform to A36.
- *All bolts shall be 3/4" High strength in accordance with ASTM A325 (UNO)
- *Welding Electrodes for Carbon steel :E70xx

# of Copies	Revision/ Issue	Destination	Date
5	0	For Construction	11-14-2025
4	D	For Re-Approval	10-24-2025
3	C	For Re-Approval	09-19-2025
2	B	For Re-Approval	06-23-2025
1	A	For Approval	02-25-2025

IRON FABRICATION SERVICES, LLC.

3029 M. Street, NW, Suite 202
Washington, DC 20007
Tel: 202-800-5599
Fax: 202-478-0303

Project Name and Address

MARYLAND AVENUE

Location: **1250 MARYLAND AVENUE SW
WASHINGTON, DC 20024**

Contractor:

BALFOUR BEATTY

Approved for Fabrication by:

Signature

Contract # **224009**

Drawing # **E-11.01**

Contract Item: **LEVEL-05
SLAB EXTENSION**

Ref: **SOW-11: 3,4,5&6 / S307**

Date

01/ 20/ 2025

Drawing Title:

**SOW #11 LEVEL-05 NEW
SLAB EXTENSION SUPPORT
SECTIONS**

Scale

VARIES