


[illegible]

Total weight : 1284

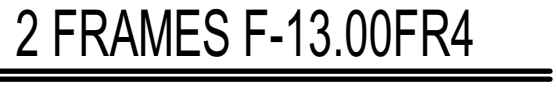

PAINT	:NO PAINT
PREPARATION	:SSPC-SP3

General Notes			
*Structural steel shall conform to ASTM-A992. *Structural SQR/RND,tubing conform to ASTM A500 Grade C *Pipe shall conform to ASTM A53, Grade B. *Channels, Angles and plates shall conform to A36. *All bolts shall be $\frac{3}{4}$" High strength in accordance with ASTM A325 (UNO) *Welding Electrodes for Carbon steel :E70xx			
5	0	For Fabrication	11-17-2025
4	D	For Re-Approval	10-24-2025
3	C	For Re-Approval	09-19-2025
2	B	For Re-Approval	06-23-2025
1	A	For Approval	02-25-2025
# of Copies	Revision/ Issue	Destination	Date

5	0	For Fabrication	11-17-2025
4	D	For Re-Approval	10-24-2025
3	C	For Re-Approval	09-19-2025
2	B	For Re-Approval	06-23-2025
1	A	For Approval	02-25-2025
# of Copies	Revision/Issue	Destination	Date

IRON FABRICATION SERVICES, LLC.

3029 M. Street, NW, Suite 202
Washington, DC 20007
Tel: 202-800-5599
Fax: 202-478-0303

Project Name and Address
MARYLAND AVENUE

Location: **1250 MARYLAND AVENUE SW**
WASHINGTON, DC 20024

Contractor: **BALFOUR BEATTY**

Approved for Fabrication by:	Signature
------------------------------	-----------

Contract # 224009	Drawing # F-13.00
--------------------------	--------------------------

Contract Item: **FRAME**

Ref:

SOW - 13: E-13.00 - E-13.02

Date 01/ 23/ 2025	Drawing Title: FRAME DETAIL
Scale VARIES	

BILL OF MATERIAL							
LINE	QTY	PC		LENGTH		WEIGHT	ADVANCE
#	TOTAL	MARK	DESCRIPTION			REMARKS	MILL #
	2	F-13.01FR1	FRAME				420
	2	F-13.01FR1	HSS6x6x3/16	3	73/4	A500C	170
	2	p817	PL1/2x16	4	6	A36	245
	2	p704	PL1/4x6	0	6	A36	5
	2	F-13.01FR2	FRAME				737
	2	F-13.01FR2	HSS6x6x3/16	3	73/4	A500C	170
	2	hss311	HSS6x2x3/16	3	71/2	A500C	169
	2	hss309	HSS6x6x3/16	3	03/4	A500C	143
	2	p817	PL1/2x16	4	6	A36	245
	4	p704	PL1/4x6	0	6	A36	10
	2	F-13.01FR3	FRAME				505
	2	F-13.01FR3	HSS6x2x3/16	4	73/4	A500C	138
	2	hss3834	HSS6x2x3/16	3	63/4	A500C	106
	2	hss3833	HSS6x2x3/16	3	01/4	A500C	90
	2	p360	PL1/2x9	5	6	A36	168
	4	p3098	PL1/4x2	0	6	A36	3

Total weight : 1663



- *Structural steel shall conform to ASTM-A992.
- *Structural SQR/RND.tubing conform to ASTM A500 Grade C
- *Pipe shall conform to ASTM A53, Grade B.
- *Channels, Angles and plates shall conform to A36.
- *All bolts shall be 3/4" High strength in accordance with ASTM A325 (UNO)
- *Welding Electrodes for Carbon steel :E70xx

IRON FABRICATION SERVICES, LLC.

Project Name and Address
MARYLAND AVENUE

Location: **1250 MARYLAND AVENUE SW**
WASHINGTON, DC 20024

Contractor: **BALFOUR BEATTY**

Contract # 224009	Drawing # F-13.01
--------------------------	--------------------------

Contract Item: **FRAME**

Ref:


SOW - 13: E-13.00 - E-13.02

Date 01/ 23/ 2025	Drawing Title: FRAME DETAIL
Scale VARIES	

PAINT	:NO PAINT
PREPARATION	:SSPC-SP3


BILL OF MATERIAL									
LINE #	QTY	PC	MARK	DESCRIPTION		LENGTH	REMARKS		ADVANCE
	TOTAL								MILL #
ONE		F-13.02C1		COLUMN					329
1		F-13.02C1		HSS6x6x ³ / ₈		10 4	SIZE A500C		284
1		pl1976		PL1 ¹ / ₂ x7		1 6	A36		45
				FIELD BOLTS					
2				³ / ₄ " Dia HILTI HAS V-36		0 8	+1HD WASH		
				w/ HILTI HY-200 V3			(3 ¹ / ₄ " EMBEDMENT)		
				ADHESIVE					
ONE		F-13.02B1		BEAM					810
1		F-13.02B1		HSS10x8x ⁵ / ₁₆		17 6 ⁷ / ₁₆	A500C		633
1		pl364		PL1 ¹ / ₂ x7 ¹ / ₈		8 9 ¹ / ₈	A36		53
2		pl3649		PL1 ¹ / ₂ x8		0 10	A36		11
1		pl328		PL1 ¹ / ₂ x7 ⁵ / ₈		8 8 ⁵ / ₁₆	A36		57
1		fb13		FL1 ¹ / ₂ x3 ³ / ₄		8 8 ³ / ₄	A36		28
1		fb12		FL1 ¹ / ₂ x3 ³ / ₄		8 8 ³ / ₈	A36		28

Total weight : 1139

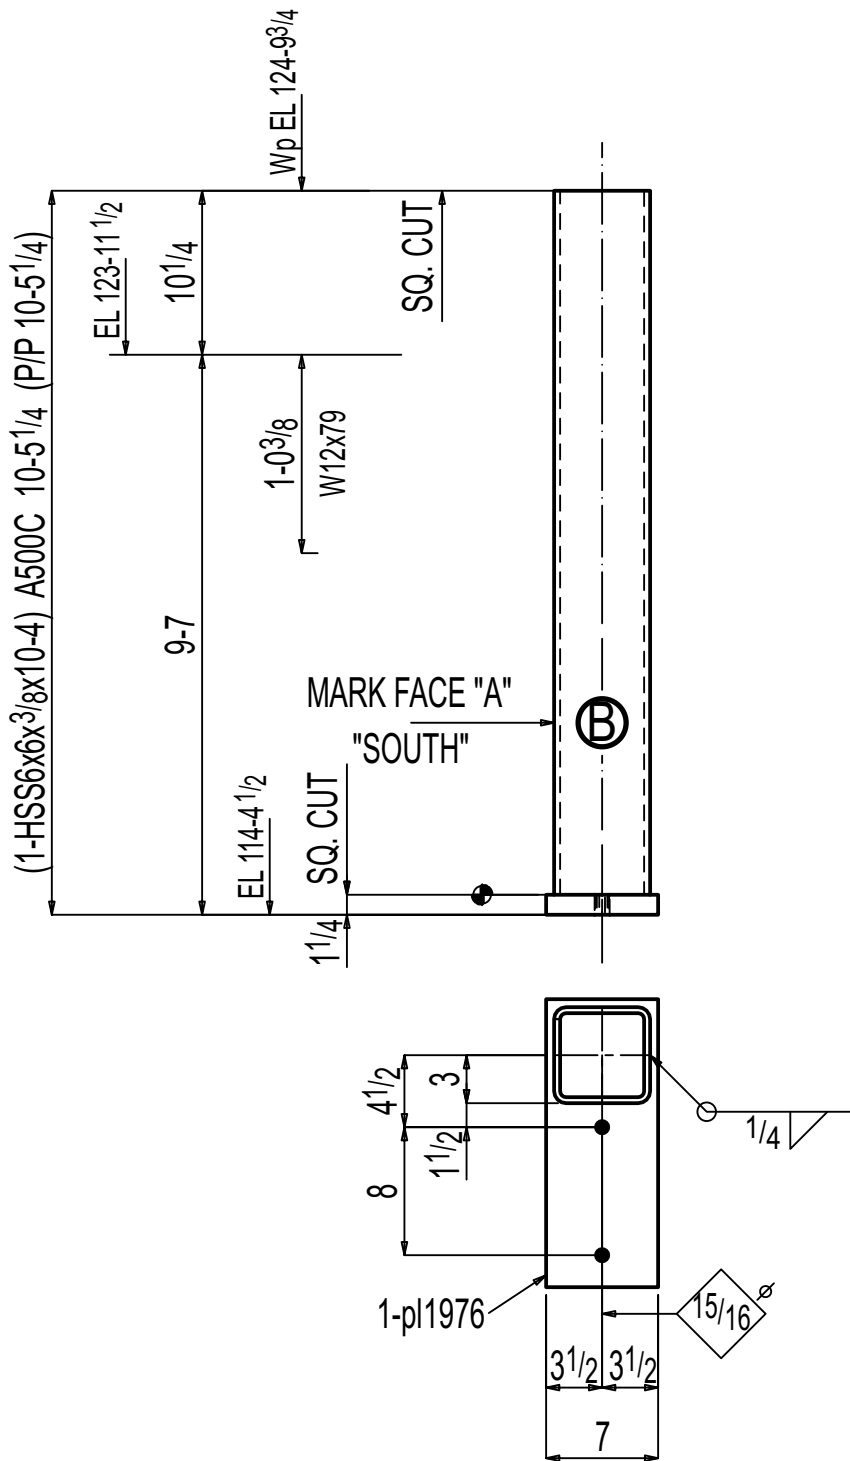


ONE COLUMN F-13.02C1

AT GRID:
EE & A

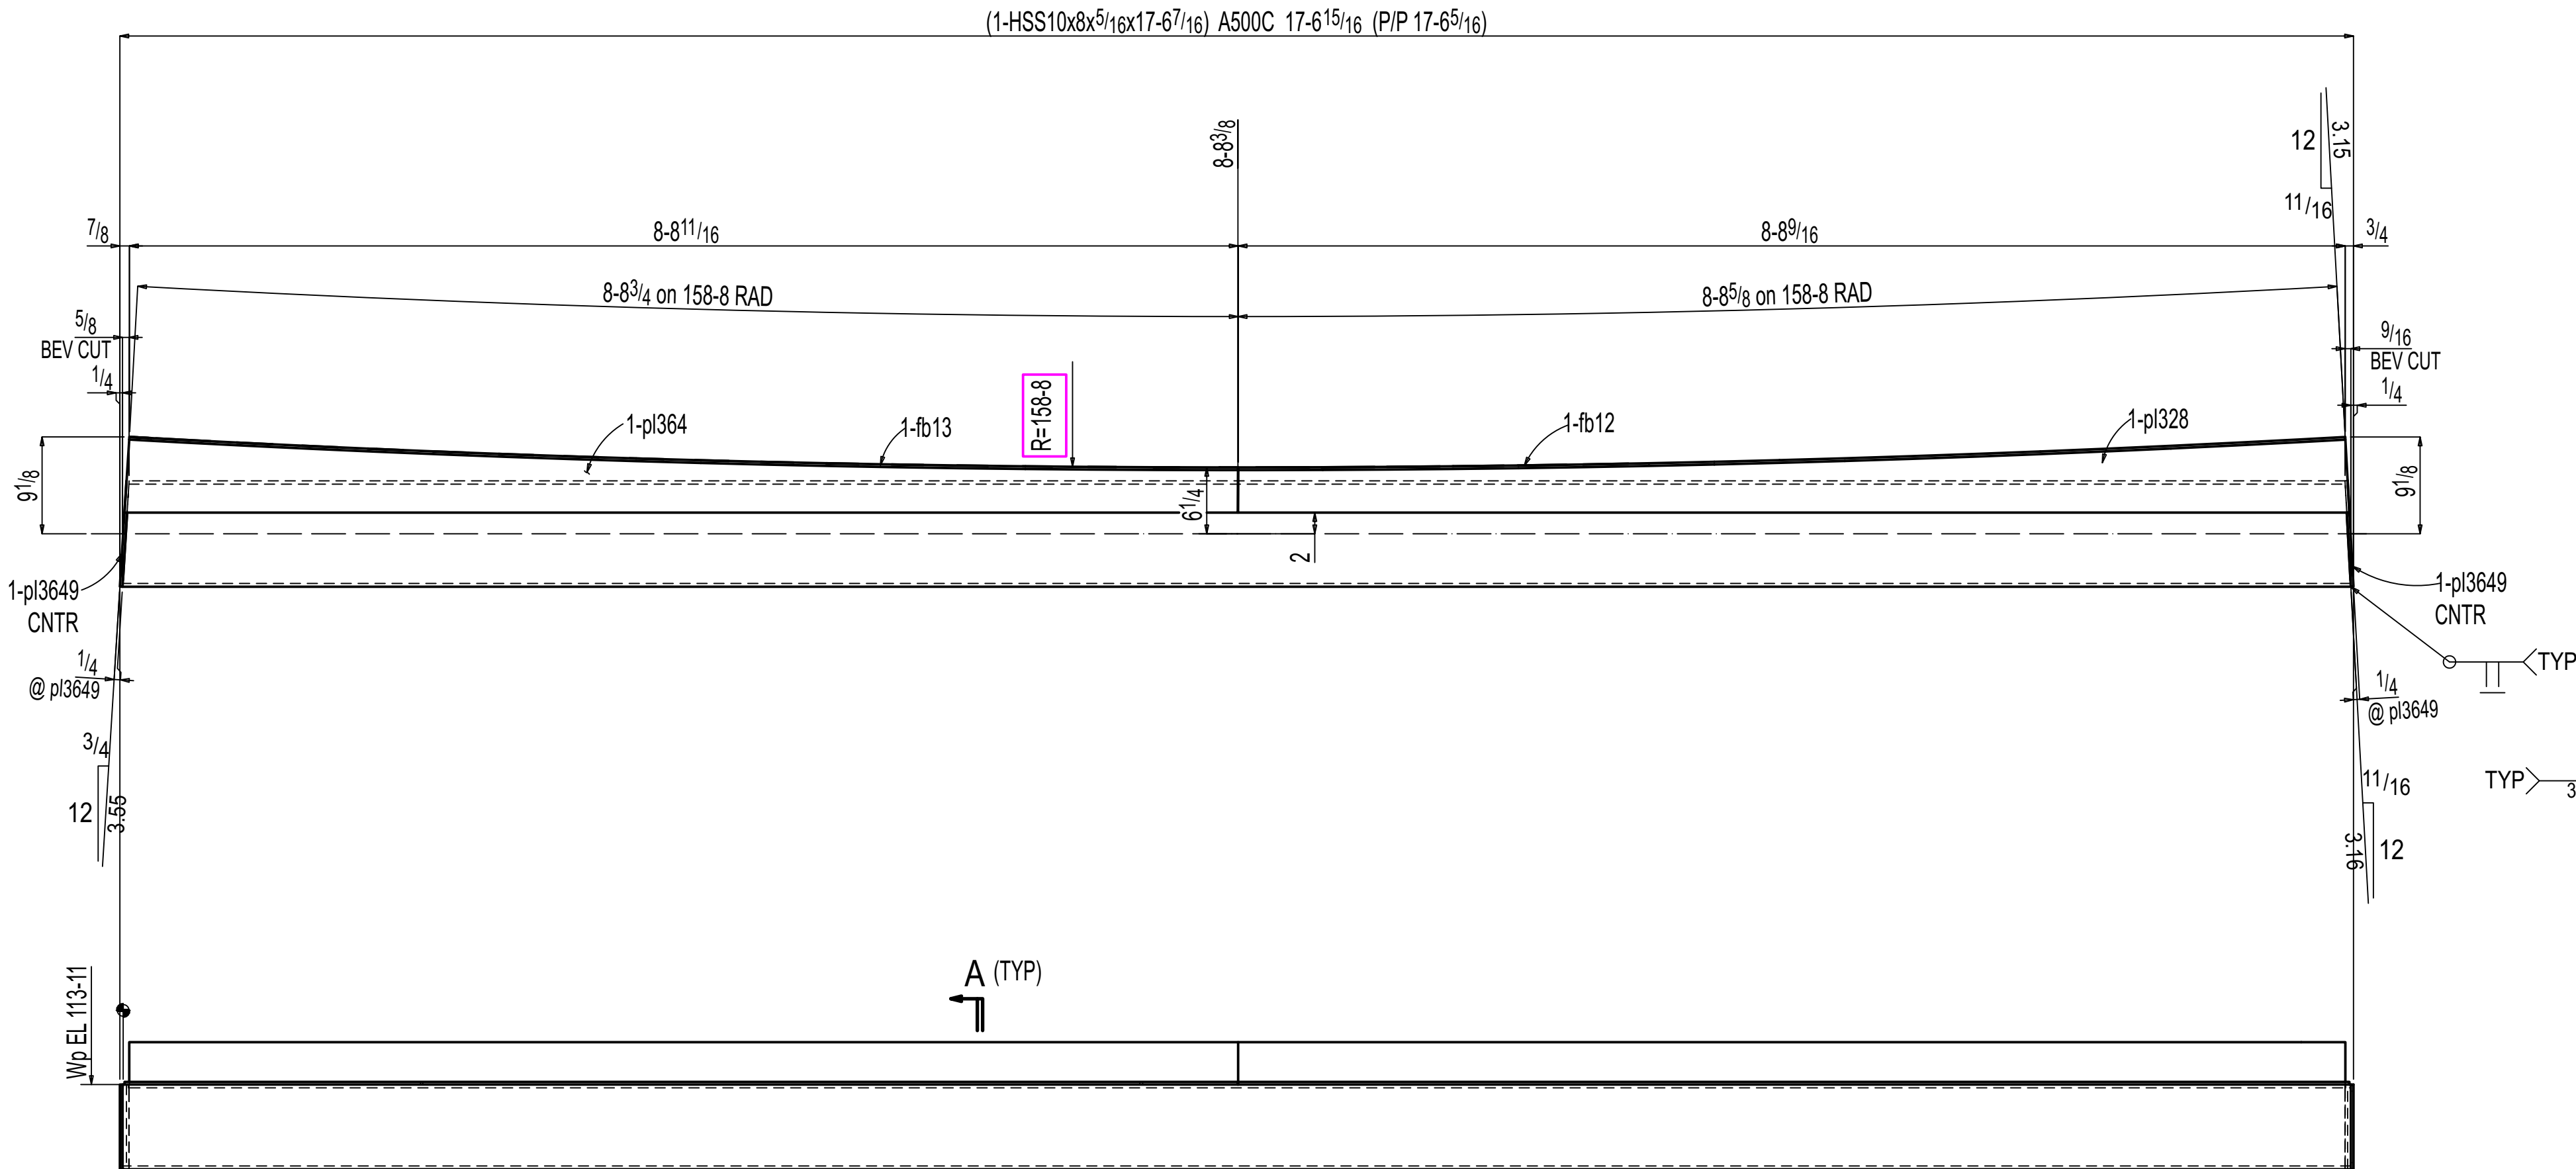

ONE BEAM F-13.02B1

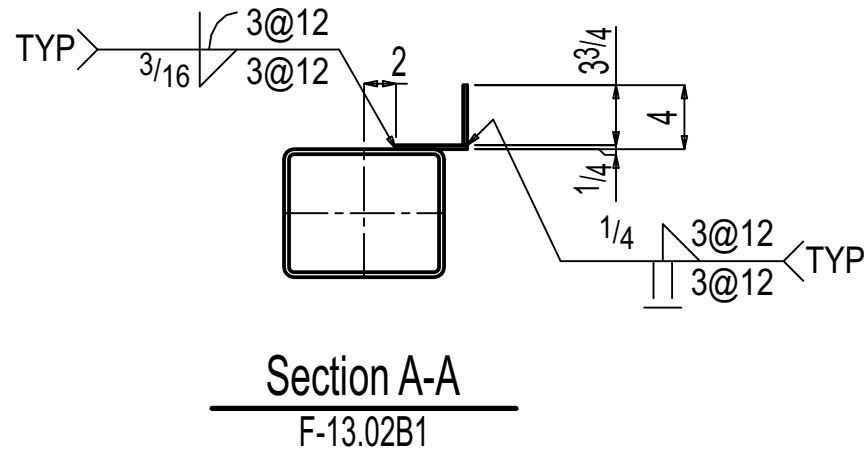

PAINT :NO PAINT
PREPARATION :SSPC-SP3

General Notes			
*Structural steel shall conform to ASTM-A992.			
*Structural SQR/RND,tubing conform to ASTM A500 Grade C			
*Pipe shall conform to ASTM A53, Grade B.			
*Channels, Angles and plates shall conform to A36.			
*All bolts shall be ³ / ₄ " High strength in accordance with ASTM A325 (UNO)			
*Welding Electrodes for Carbon steel :E70xx			
5	0	For Fabrication	11-17-2025
4	D	For Re-Approval	10-24-2025
3	C	For Re-Approval	09-19-2025
2	B	For Re-Approval	06-23-2025
1	A	For Approval	02-25-2025
# of Copies	Revision/ Issue	Destination	Date

IRON FABRICATION SERVICES, LLC.

3029 M. Street, NW, Suite 202
Washington, DC 20007
Tel: 202-800-5599
Fax: 202-478-0303

Project Name and Address
MARYLAND AVENUE

Location: **1250 MARYLAND AVENUE SW
WASHINGTON, DC 20024**


Contractor:
BALFOUR BEATTY

Approved for Fabrication by: Signature


Contract #	224009	Drawing #	F-13.02
Contract Item: COLUMN & BEAM			
Ref: SOW - 13: E-13.00 - E-13.02			
Date 01/ 23/ 2025	Drawing Title: COLUMN & BEAM DETAIL		
Scale VARIES			

BILL OF MATERIAL									
LINE #	QTY	PC MARK	DESCRIPTION	LENGTH	REMARKS	WEIGHT	ADVANCE		
	TOTAL					TOTAL	MILL #		
ONE	F-13.03B1	BEAM				919			
1	F-13.03B1	HSS10x8x ⁵ / ₁₆		19 10 ¹³ / ₁₆	A500C	718			
2	p13649	PL ¹ / ₄ x8		0 10	A36	11			
1	p1368	PL ¹ / ₄ x7 ¹³ / ₁₆		9 11 ¹ / ₄	A36	66			
1	p13652	PL ¹ / ₄ x7 ¹ / ₈		9 11 ¹ / ₄	A36	60			
1	fb229	FL ¹ / ₄ x3 ³ / ₄		9 10 ⁷ / ₈	A36	32			
1	fb230	FL ¹ / ₄ x3 ³ / ₄		9 10 ⁷ / ₈	A36	32			
ONE	F-13.03B2	BEAM				969			
1	F-13.03B2	HSS8x6x ¹ / ₂		22 10 ¹ / ₂	A500C	962			
2	p1476	PL ¹ / ₄ x6		0 8	A36	7			
ONE	F-13.03B3	BEAM				495			
1	F-13.03B3	HSS6x6x ¹ / ₂		13 10 ⁷ / ₈	A500C	490			
2	p1704	PL ¹ / ₄ x6		0 6	A36	5			
ONE	F-13.03M1	HSS				110			
1	F-13.03M1	HSS6x6x ³ / ₁₆		4 7 ¹ / ₂	A500C	108			
1	p1704	PL ¹ / ₄ x6		0 6	A36	3			
ONE	F-13.03M2	HSS				117			
1	F-13.03M2	HSS6x6x ³ / ₁₆		5 0	A500C	117			
2	F-13.03M3	HSS				200			
2	F-13.03M3	HSS6x6x ³ / ₁₆		4 3 ¹ / ₂	A500C	200			
2	F-13.03M4	HSS				180			
2	F-13.03M4	HSS6x6x ³ / ₁₆		3 9	A500C	175			
2	p1704	PL ¹ / ₄ x6		0 6	A36	5			
ONE	F-13.03A1	ANGLE				7			
1	F-13.03A1	L4x4x ¹ / ₄		1 0	A36	7			
ONE	F-13.03P2	PLATE				55			
1	F-13.03P2	PL ¹ / ₄ x7		1 10	A36	55			
		FIELD BOLTS							
2		3/4 Dia HILTI KWIK HUS-EZ		0 7	(3 ¹ / ₄ " EMBEDMENT)				
		SCREW ANCHOR							


Total weight : 3052

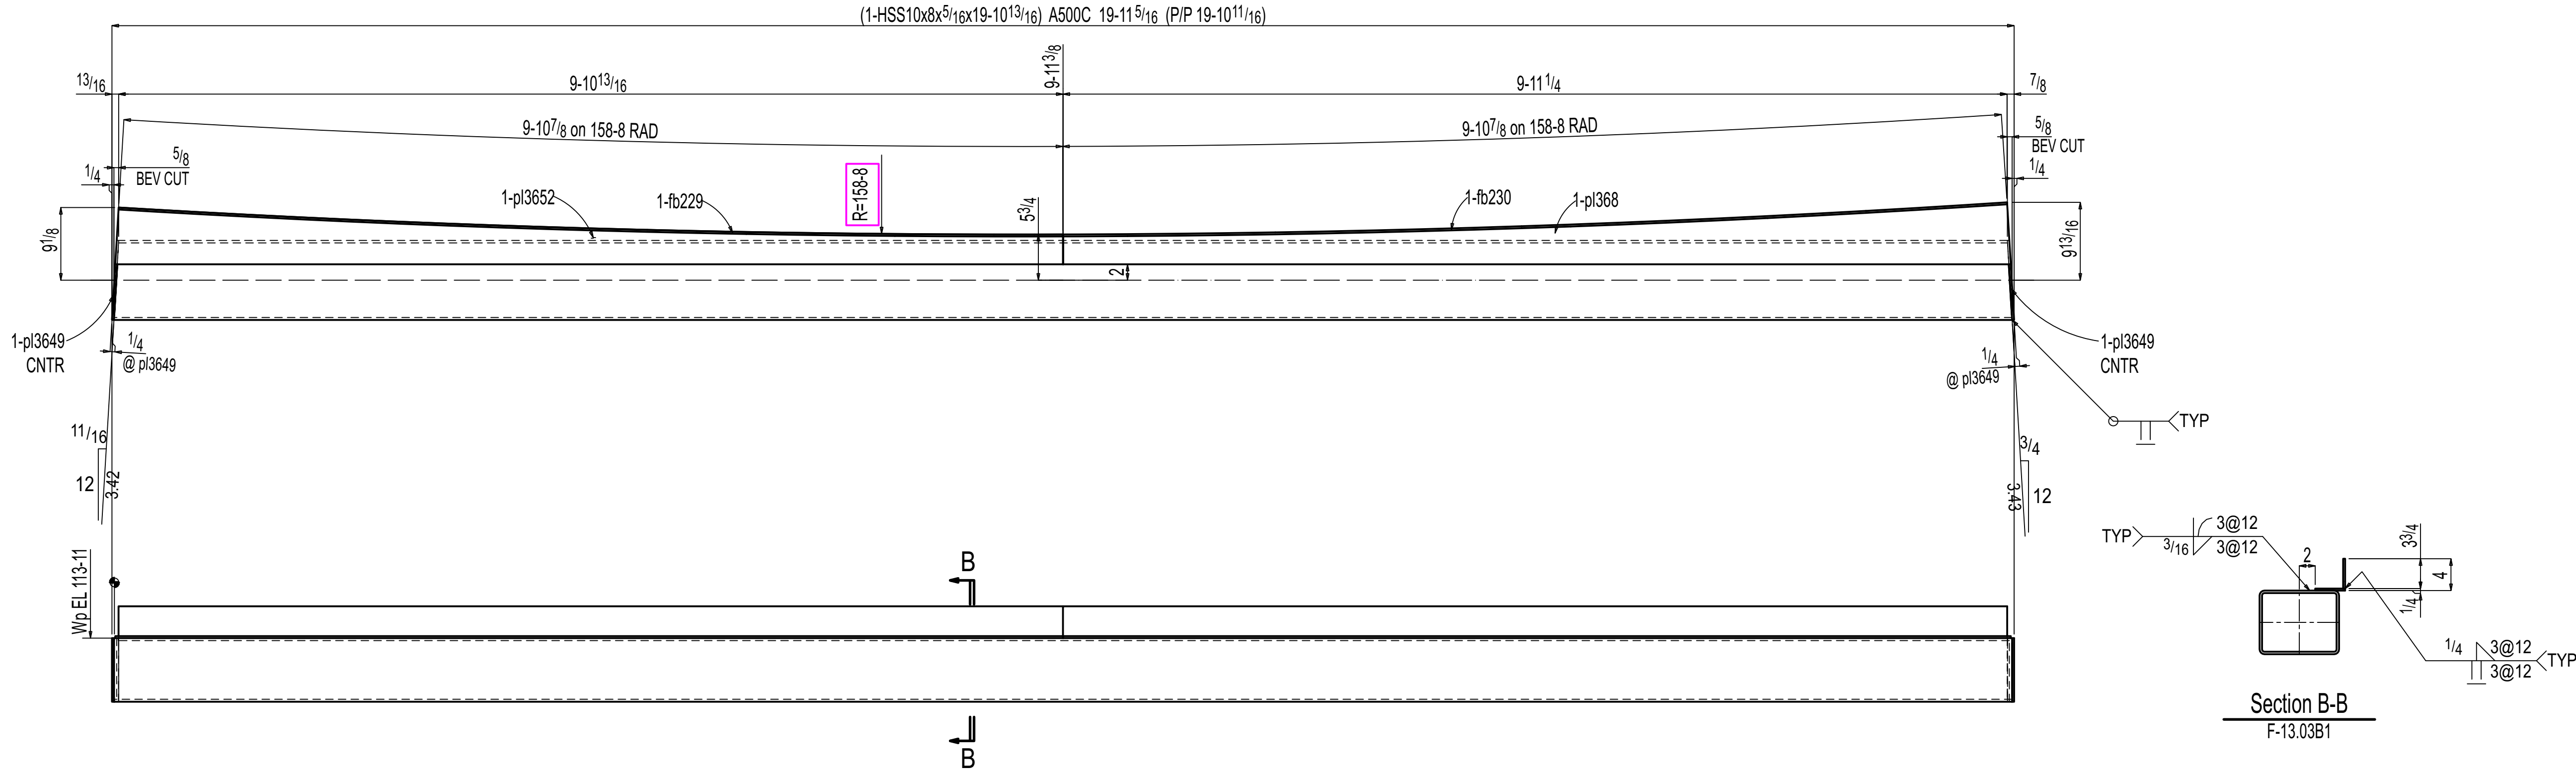


ONE BEAM F-13.03B1

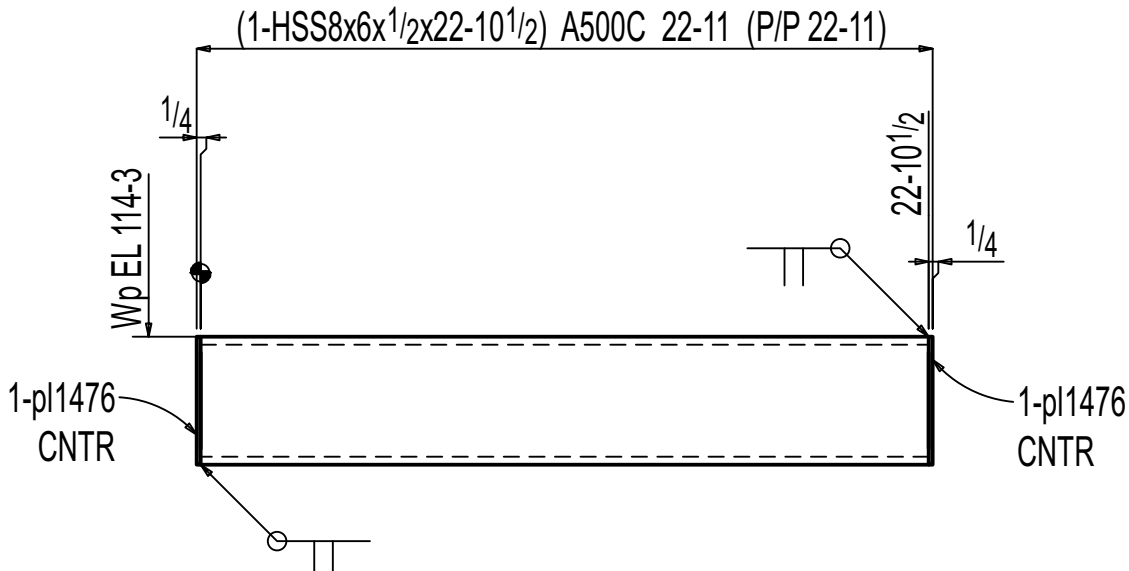


ONE BEAM F-13.03B2

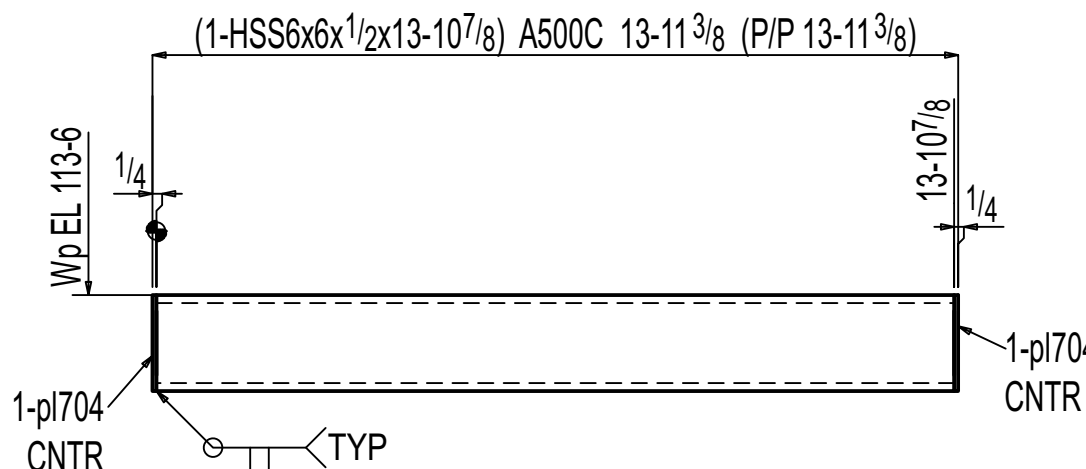


ONE BEAM F-13.03B3

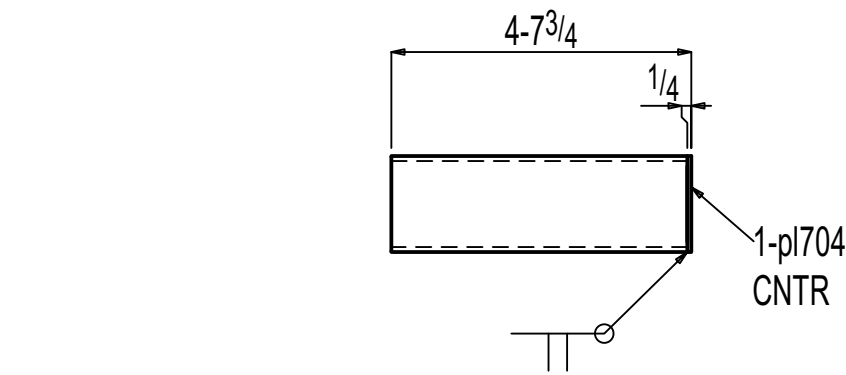


ONE HSS F-13.03M1

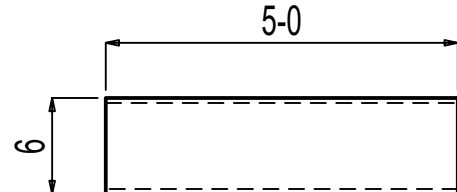


ONE HSS F-13.03M2

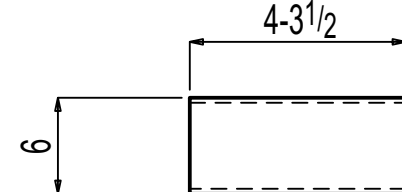


2 HSES F-13.03M3

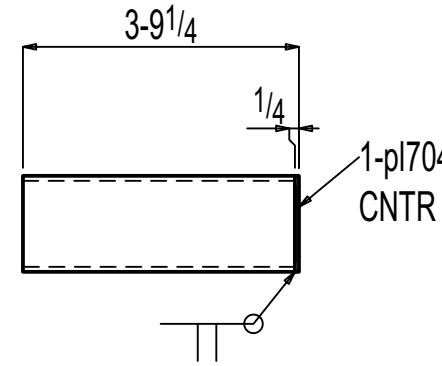

2 HSES F-13.03M4

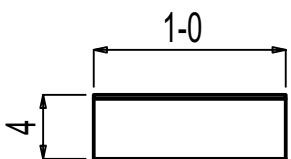

ONE ANGLE F-13.03A1

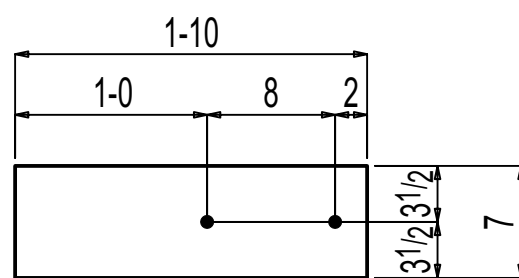

ONE PLATE F-13.03P2

PAINT PREPARATION :NO PAINT :SSPC-SP3

General Notes			
*Structural steel shall conform to ASTM-A992.			
*Structural SQR/RND,tubing conform to ASTM A500 Grade C			
*Pipe shall conform to ASTM A53, Grade B.			
*Channels, Angles and plates shall conform to A36.			
*All bolts shall be 3/4" High strength in accordance with ASTM A325 (UNO)			
*Welding Electrodes for Carbon steel :E70xx			
5	0	For Fabrication	11-17-2025
4	D	For Re-Approval	10-24-2025
3	C	For Re-Approval	09-19-2025
2	B	For Re-Approval	06-23-2025
1	A	For Approval	02-11-2025
# of Copies	Revision/ Issue	Destination	Date

IRON FABRICATION SERVICES, LLC.

3029 M. Street, NW, Suite 202
Washington, DC 20007
Tel: 202-800-5599
Fax: 202-478-0303

Project Name and Address
MARYLAND AVENUE
Location: **1250 MARYLAND AVENUE SW
WASHINGTON, DC 20024**

Contractor:
BALFOUR BEATTY

Approved for Fabrication by: Signature






Contract # **224009** Drawing # **F-13.03**

Contract Item: **FRAME**


Ref:
SOW - 13: E-13.00 - E-13.02

Date **01/ 23/ 2025** Drawing Title:
Scale **VARIES** **BEAM & MISCELLANEOUS DETAIL**

BILL OF MATERIAL									
LINE #	QTY	PC	MARK	DESCRIPTION	LENGTH	REMARKS	WEIGHT	ADVANCE	
	TOTAL		MARK	DESCRIPTION			TOTAL	MILL #	
ONE		F-13.04B1		BEAM			828		
1		F-13.04B1		HSS8x8x1/4	25	10	A500C	667	
2		p359		PL1/4x4	1	2	A36	8	
2		p3697		PL1/4x8	0	8	A36	9	
3		bp11987		PL1/4x691/16	8	0	BENT A36	134	
1		bp176		PL1/4x691/16	1	10	BENT A36	10	
ONE		F-13.04A1		ANGLE			145		
1		F-13.04A1		L4x4x3/16	17	89/16	A36	145	
				FIELD BOLTS					
27				1/2 Dia HILTI HAS V-36	0	41/2	+1HD WASH		
				w/ HILTI HY-200 V3 EPOXY			(23/4" EMBEDMENT)		
ONE		F-13.04A2		ANGLE			82		
1		F-13.04A2		L4x4x3/16	10	09/16	A36	82	
				FIELD BOLTS					
16				1/2 Dia HILTI HAS V-36	0	41/2	+1HD WASH		
				w/ HILTI HY-200 V3 EPOXY			(23/4" EMBEDMENT)		
ONE		F-13.04A3		ANGLE			82		
1		F-13.04A3		L4x4x3/16	10	09/16	A36	82	
				FIELD BOLTS					
16				1/2 Dia HILTI HAS V-36	0	41/2	+1HD WASH		
				w/ HILTI HY-200 V3 EPOXY			(23/4" EMBEDMENT)		
ONE		F-13.04A4		ANGLE			107		
1		F-13.04A4		L4x4x3/16	12	111/4	A36	106	
1		p3699		PL1/4x211/16	0	4	A36	1	
				FIELD BOLTS					
13				1/2 Dia HILTI HAS V-36	0	41/2	+1HD WASH		
				w/ HILTI HY-200 V3 EPOXY			(23/4" EMBEDMENT)		
2		F-13.04A5		ANGLE			47		
2		F-13.04A5		L8x8x1/2	0	10	A36	44	
2		p601		PL5/16x3	0	51/2	A36	3	
				FIELD BOLTS					
2				3/4 Dia A325N	0	9	+2HD WASH		
4				3/4 Dia HILTI K8-T22	0	7	+1HD WASH		
				EXPANSION ANCHOR			(49/4" EMBEDMENT)		
ONE		F-13.04A7		ANGLE			107		
1		F-13.04A7		L4x4x3/16	12	111/4	A36	106	
1		p3699		PL1/4x211/16	0	4	A36	1	
				FIELD BOLTS					
13				1/2 Dia HILTI HAS V-36	0	41/2	+1HD WASH		
				w/HILTI HY-200 V3 EPOXY			(23/4" EMBEDMENT)		

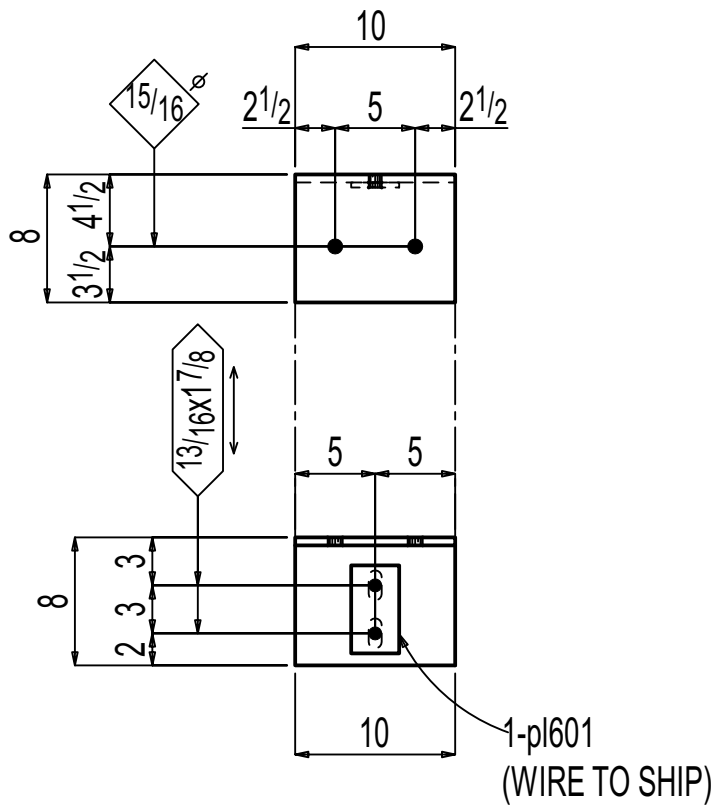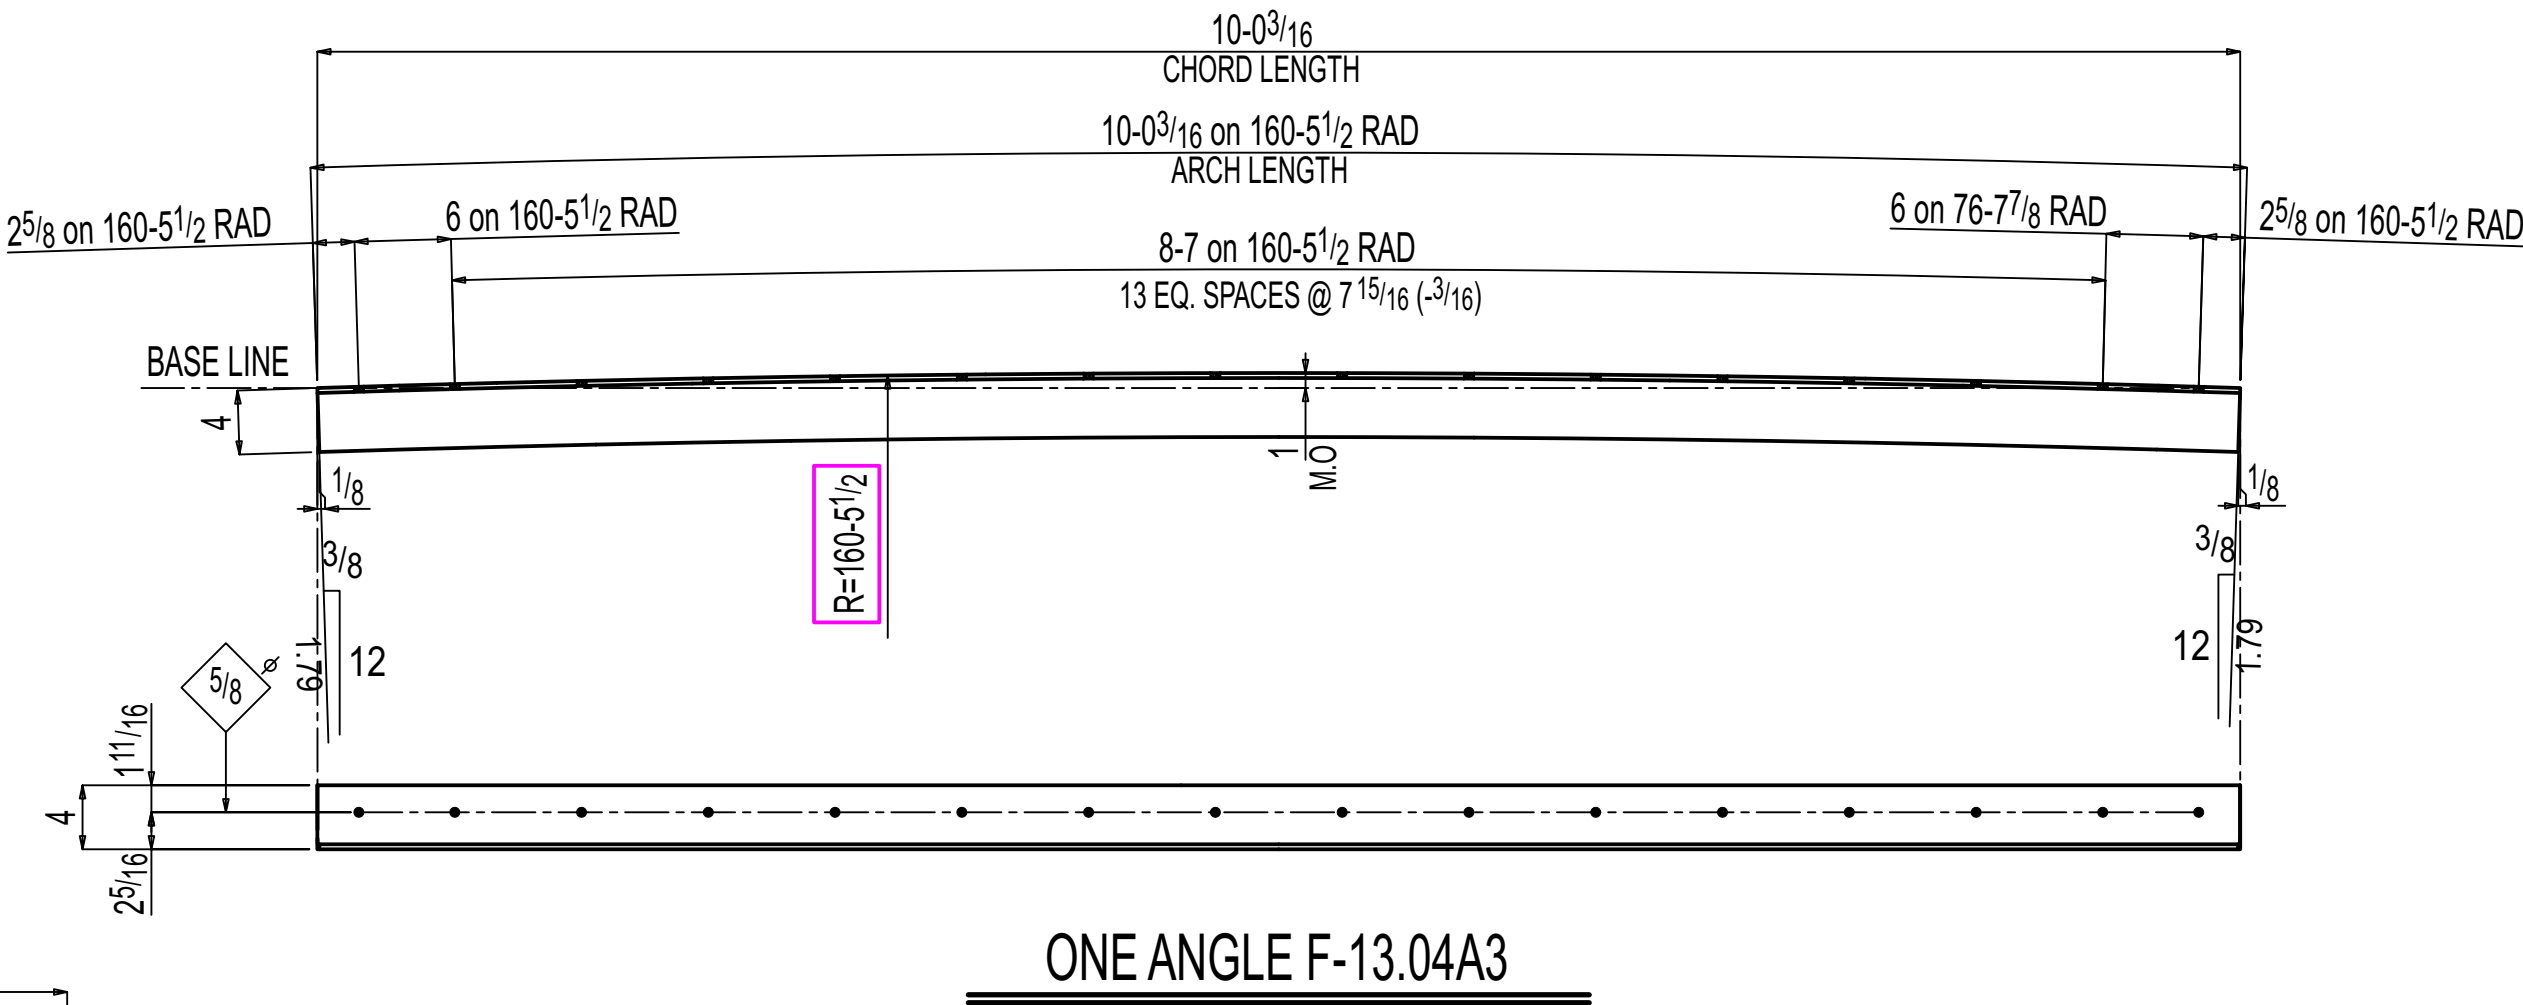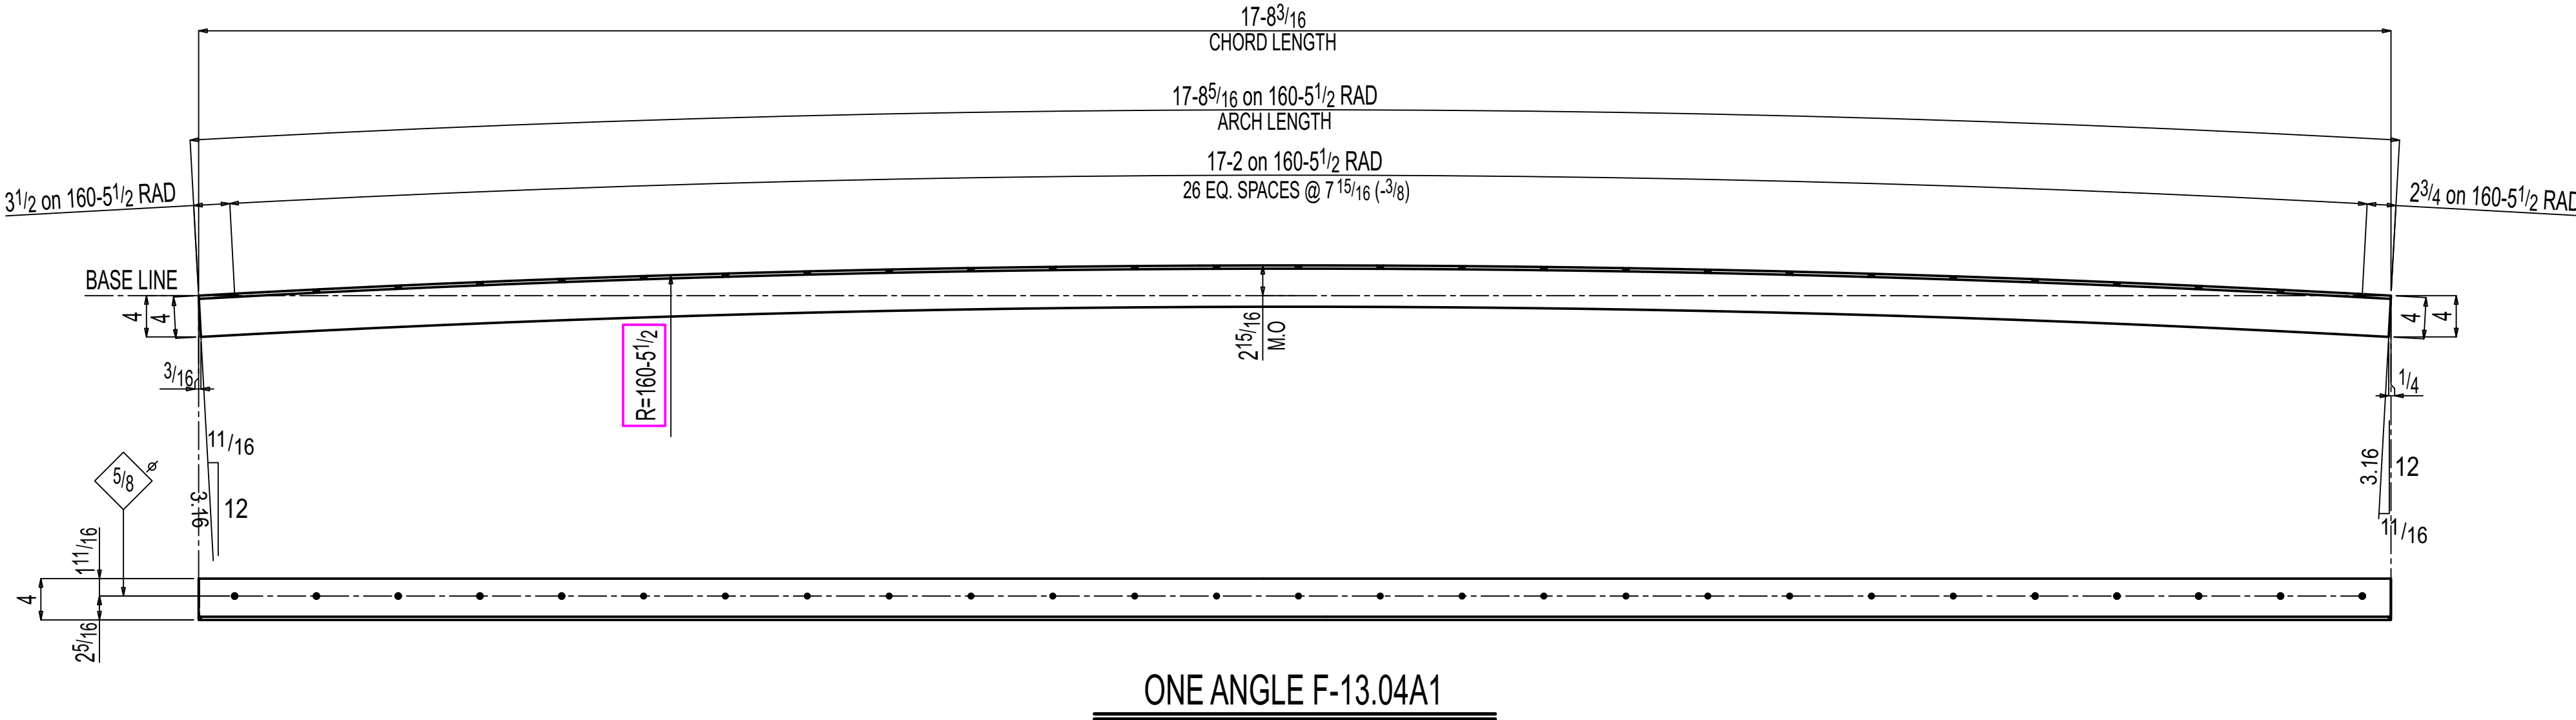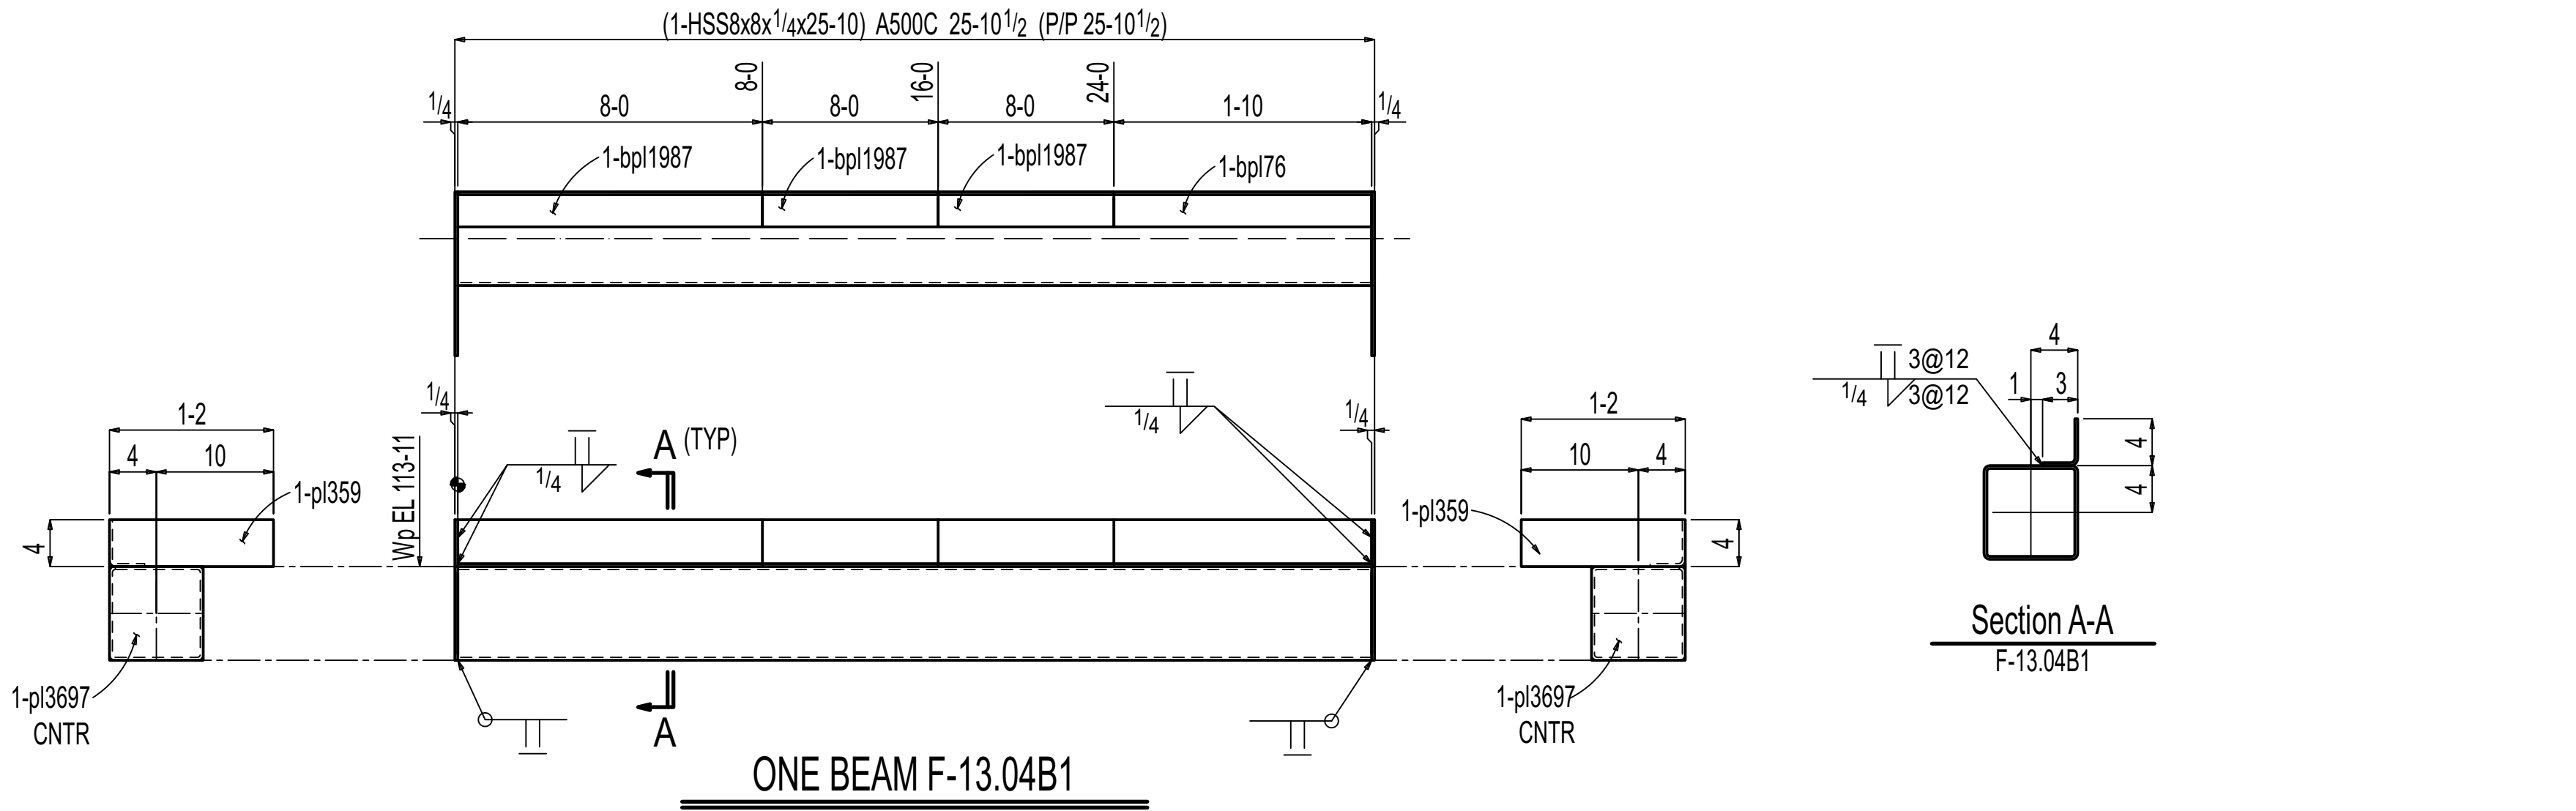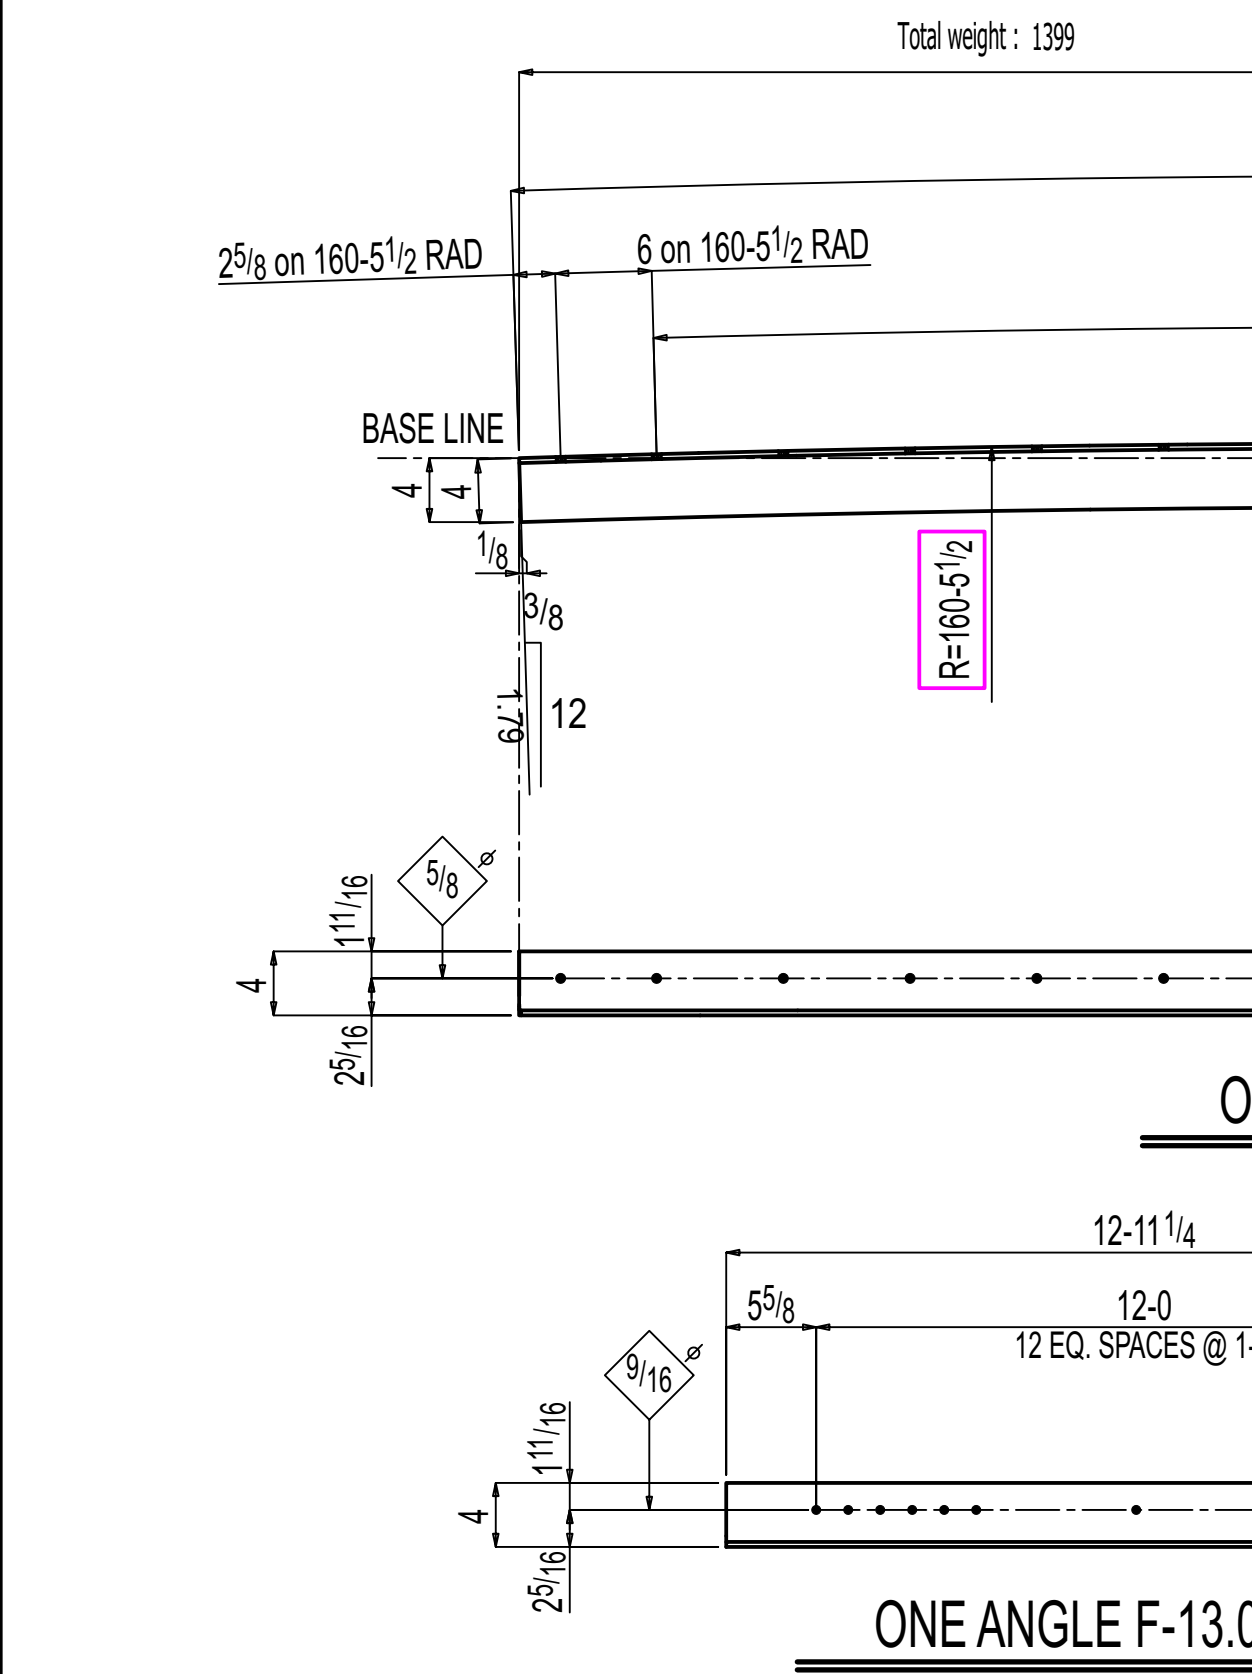

THIS PCMK COMBINED WITH F-13.04A5

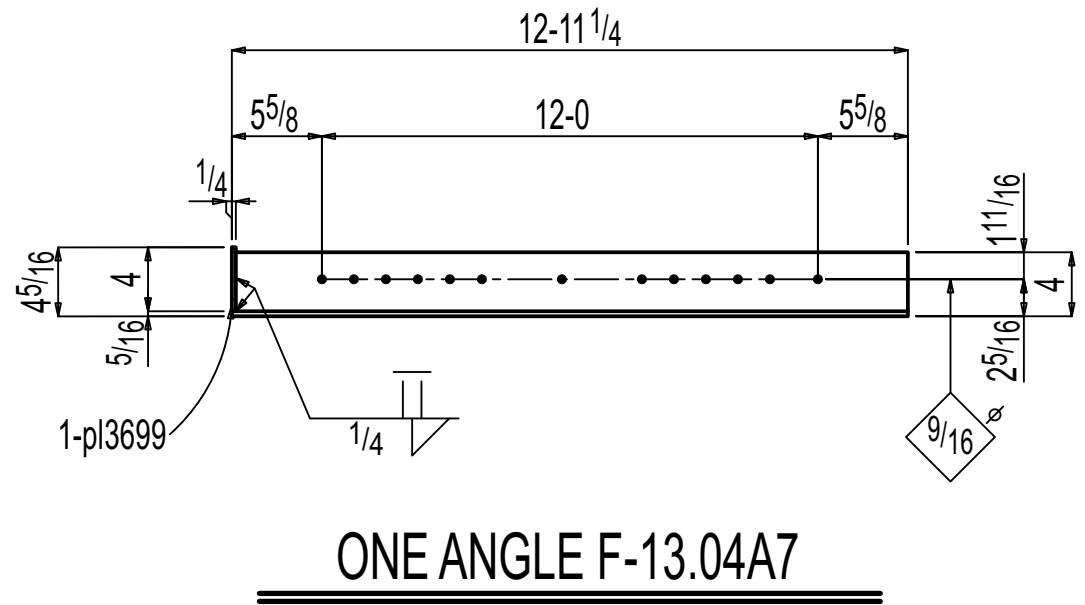

PAINT PREPARATION :NO PAINT :SSPC-SP3

General Notes

- *Structural steel shall conform to ASTM-A992.
- *Structural SQR/RND,tubing conform to ASTM A500 Grade C
- *Pipe shall conform to ASTM A53, Grade B.
- *Channels, Angles and plates shall conform to A36.
- *All bolts shall be 3/4" High strength in accordance with ASTM A325 (UNO)
- *Welding Electrodes for Carbon steel :E70xx

# of Copies	Revision/ Issue	Destination	Date
5	0	For Fabrication	11-17-2025
4	D	For Re-Approval	10-24-2025
3	C	For Re-Approval	09-19-2025
2	B	For Re-Approval	06-23-2025
1	A	For Approval	02-11-2025

IRON FABRICATION SERVICES, LLC.

3029 M. Street, NW, Suite 202
Washington, DC 20007
Tel: 202-800-5599
Fax: 202-478-0303

Project Name and Address
MARYLAND AVENUE
Location: **1250 MARYLAND AVENUE SW WASHINGTON, DC 20024**

Contractor:
BALFOUR BEATTY

Approved for Fabrication by: Signature

Contract # **224009** Drawing # **F-13.04**

Contract Item: **BEAM,ANGLE & BENT PLATE**

Ref:
SOW - 13: E-13.00 - E-13.02

Date **01/ 23/ 2025** Drawing Title: **BEAM & MISCELLANEOUS DETAIL**
Scale **VARIES**

