
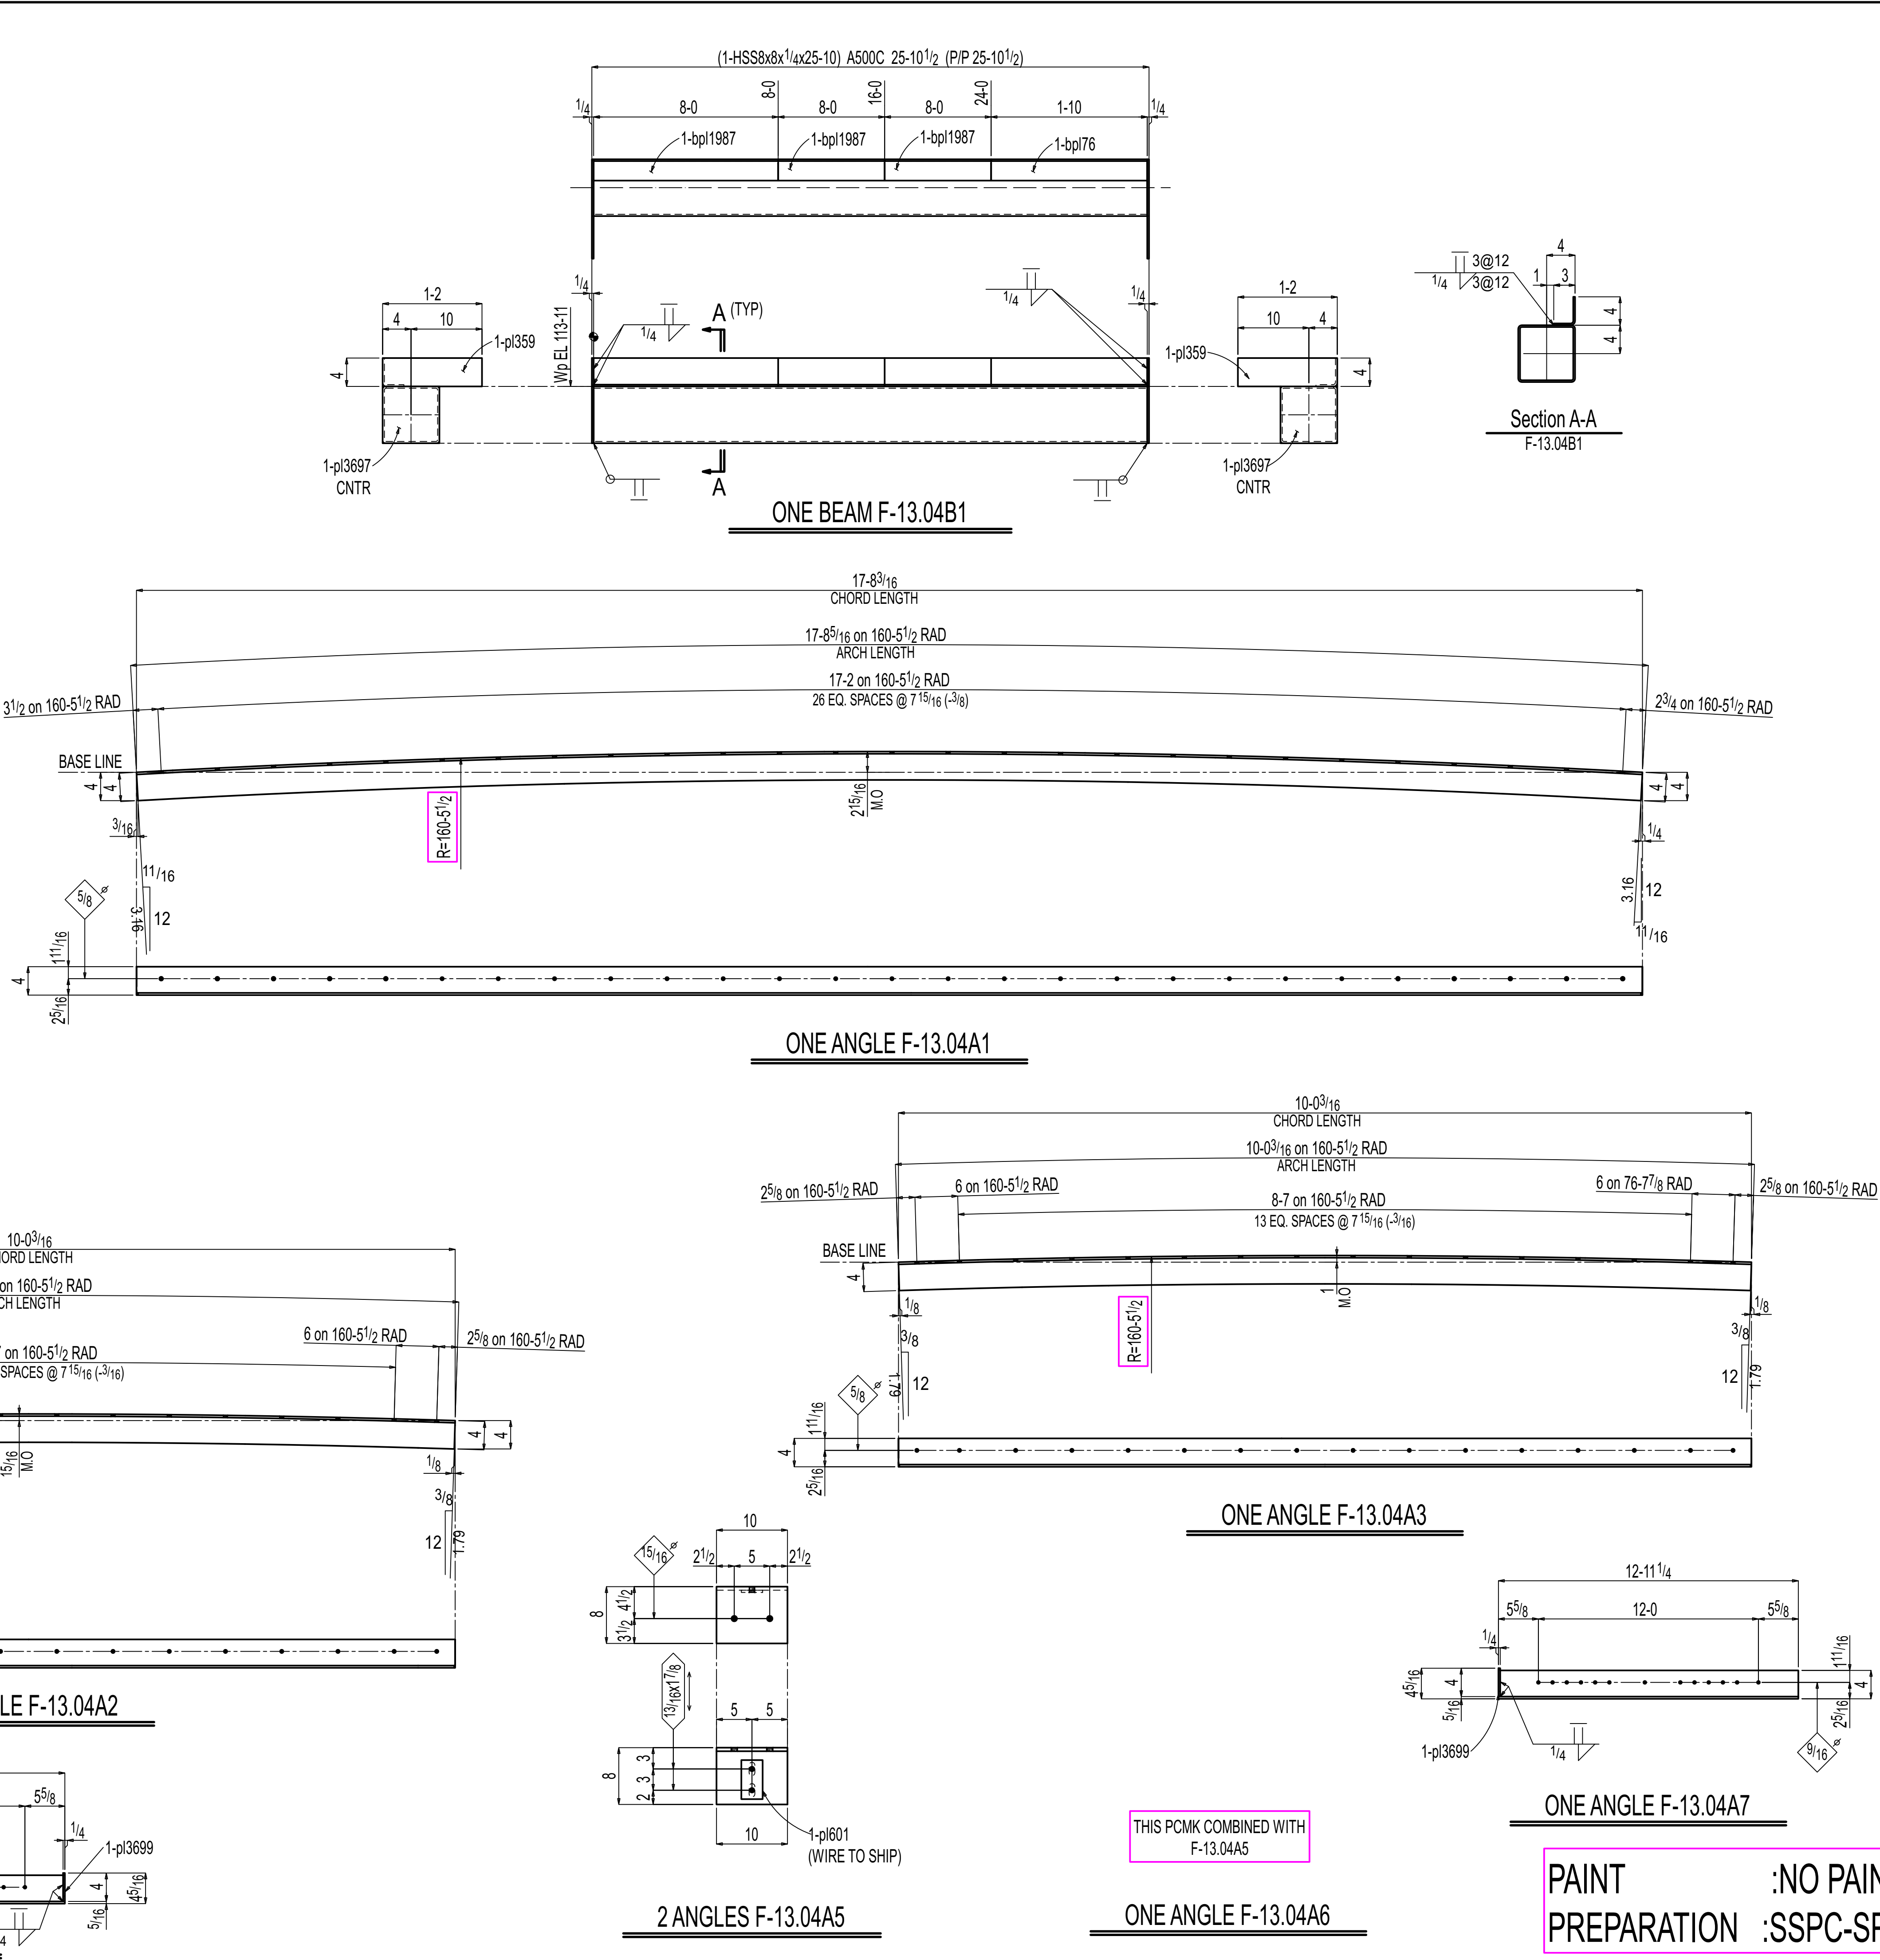


BILL OF MATERIAL									
LINE #	QTY	PC	MARK	DESCRIPTION	LENGTH	REMARKS	WEIGHT	ADVANCE	
	TOTAL		MARK	DESCRIPTION			TOTAL	MILL #	
ONE		F-13.04B1		BEAM			828		
1		F-13.04B1		HSS8x8x1/4	25	10	A500C	667	
2		p359		PL1/4x4	1	2	A36	8	
2		p3697		PL1/4x8	0	8	A36	9	
3		bp11987		PL1/4x691/16	8	0	BENT A36	134	
1		bp176		PL1/4x691/16	1	10	BENT A36	10	
ONE		F-13.04A1		ANGLE			145		
1		F-13.04A1		L4x4x3/16	17	89/16	A36	145	
				FIELD BOLTS					
27				1/2 Dia HILTI HAS V-36	0	41/2	+1HD WASH		
				w/ HILTI HY-200 V3 EPOXY			(23/4" EMBEDMENT)		
ONE		F-13.04A2		ANGLE			82		
1		F-13.04A2		L4x4x3/16	10	09/16	A36	82	
				FIELD BOLTS					
16				1/2 Dia HILTI HAS V-36	0	41/2	+1HD WASH		
				w/ HILTI HY-200 V3 EPOXY			(23/4" EMBEDMENT)		
ONE		F-13.04A3		ANGLE			82		
1		F-13.04A3		L4x4x3/16	10	09/16	A36	82	
				FIELD BOLTS					
16				1/2 Dia HILTI HAS V-36	0	41/2	+1HD WASH		
				w/ HILTI HY-200 V3 EPOXY			(23/4" EMBEDMENT)		
ONE		F-13.04A4		ANGLE			107		
1		F-13.04A4		L4x4x3/16	12	111/4	A36	106	
1		p3699		PL1/4x211/16	0	4	A36	1	
				FIELD BOLTS					
13				1/2 Dia HILTI HAS V-36	0	41/2	+1HD WASH		
				w/ HILTI HY-200 V3 EPOXY			(23/4" EMBEDMENT)		
2		F-13.04A5		ANGLE			47		
2		F-13.04A5		L8x8x1/2	0	10	A36	44	
2		p601		PL5/16x3	0	51/2	A36	3	
				FIELD BOLTS					
2				3/4 Dia A325N	0	9	+2HD WASH		
4				3/4 Dia HILTI KB-T22	0	7	+1HD WASH		
				EXPANSION ANCHOR			(49/4" EMBEDMENT)		
ONE		F-13.04A7		ANGLE			107		
1		F-13.04A7		L4x4x3/16	12	111/4	A36	106	
1		p3699		PL1/4x211/16	0	4	A36	1	
				FIELD BOLTS					
13				1/2 Dia HILTI HAS V-36	0	41/2	+1HD WASH		
				w/HILTI HY-200 V3 EPOXY			(23/4" EMBEDMENT)		

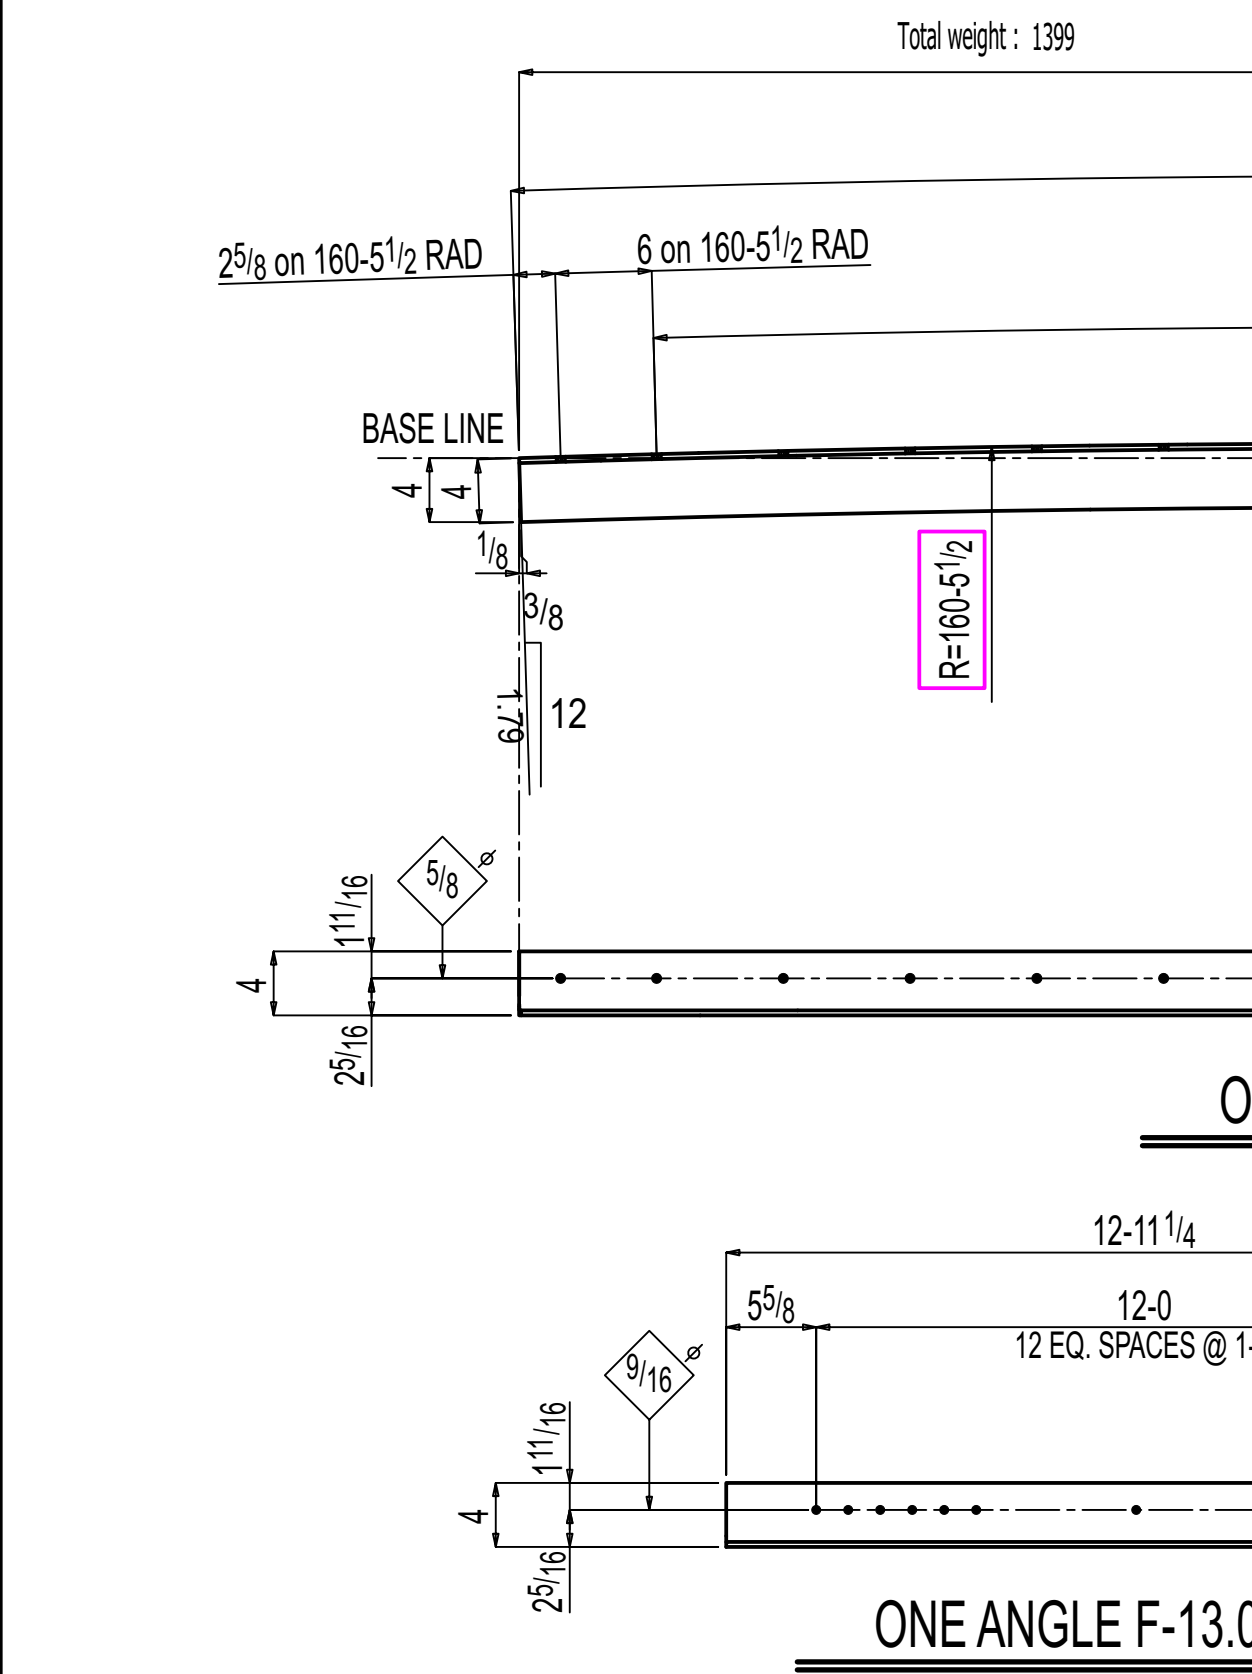

General Notes

- *Structural steel shall conform to ASTM-A992.
- *Structural SQR/RND,tubing conform to ASTM A500 Grade C
- *Pipe shall conform to ASTM A53, Grade B.
- *Channels, Angles and plates shall conform to A36.
- *All bolts shall be 3/4" High strength in accordance with ASTM A325 (UNO)
- *Welding Electrodes for Carbon steel :E70xx

# of Copies	Revision/ Issue	Destination	Date
5	0	For Fabrication	11-17-2025
4	D	For Re-Approval	10-24-2025
3	C	For Re-Approval	09-19-2025
2	B	For Re-Approval	06-23-2025
1	A	For Approval	02-11-2025

IRON FABRICATION SERVICES, LLC.

3029 M. Street, NW, Suite 202
Washington, DC 20007
Tel: 202-800-5599
Fax: 202-478-0303

Project Name and Address
MARYLAND AVENUE
Location: **1250 MARYLAND AVENUE SW
WASHINGTON, DC 20024**

Contractor:
BALFOUR BEATTY

Approved for Fabrication by: Signature

Contract # **224009** Drawing # **F-13.04**

Contract Item: **BEAM,ANGLE & BENT PLATE**

Ref:
SOW - 13: E-13.00 - E-13.02

Date
01/ 23/ 2025
Drawing Title:
**BEAM & MISCELLANEOUS
DETAIL**
Scale
VARIES