
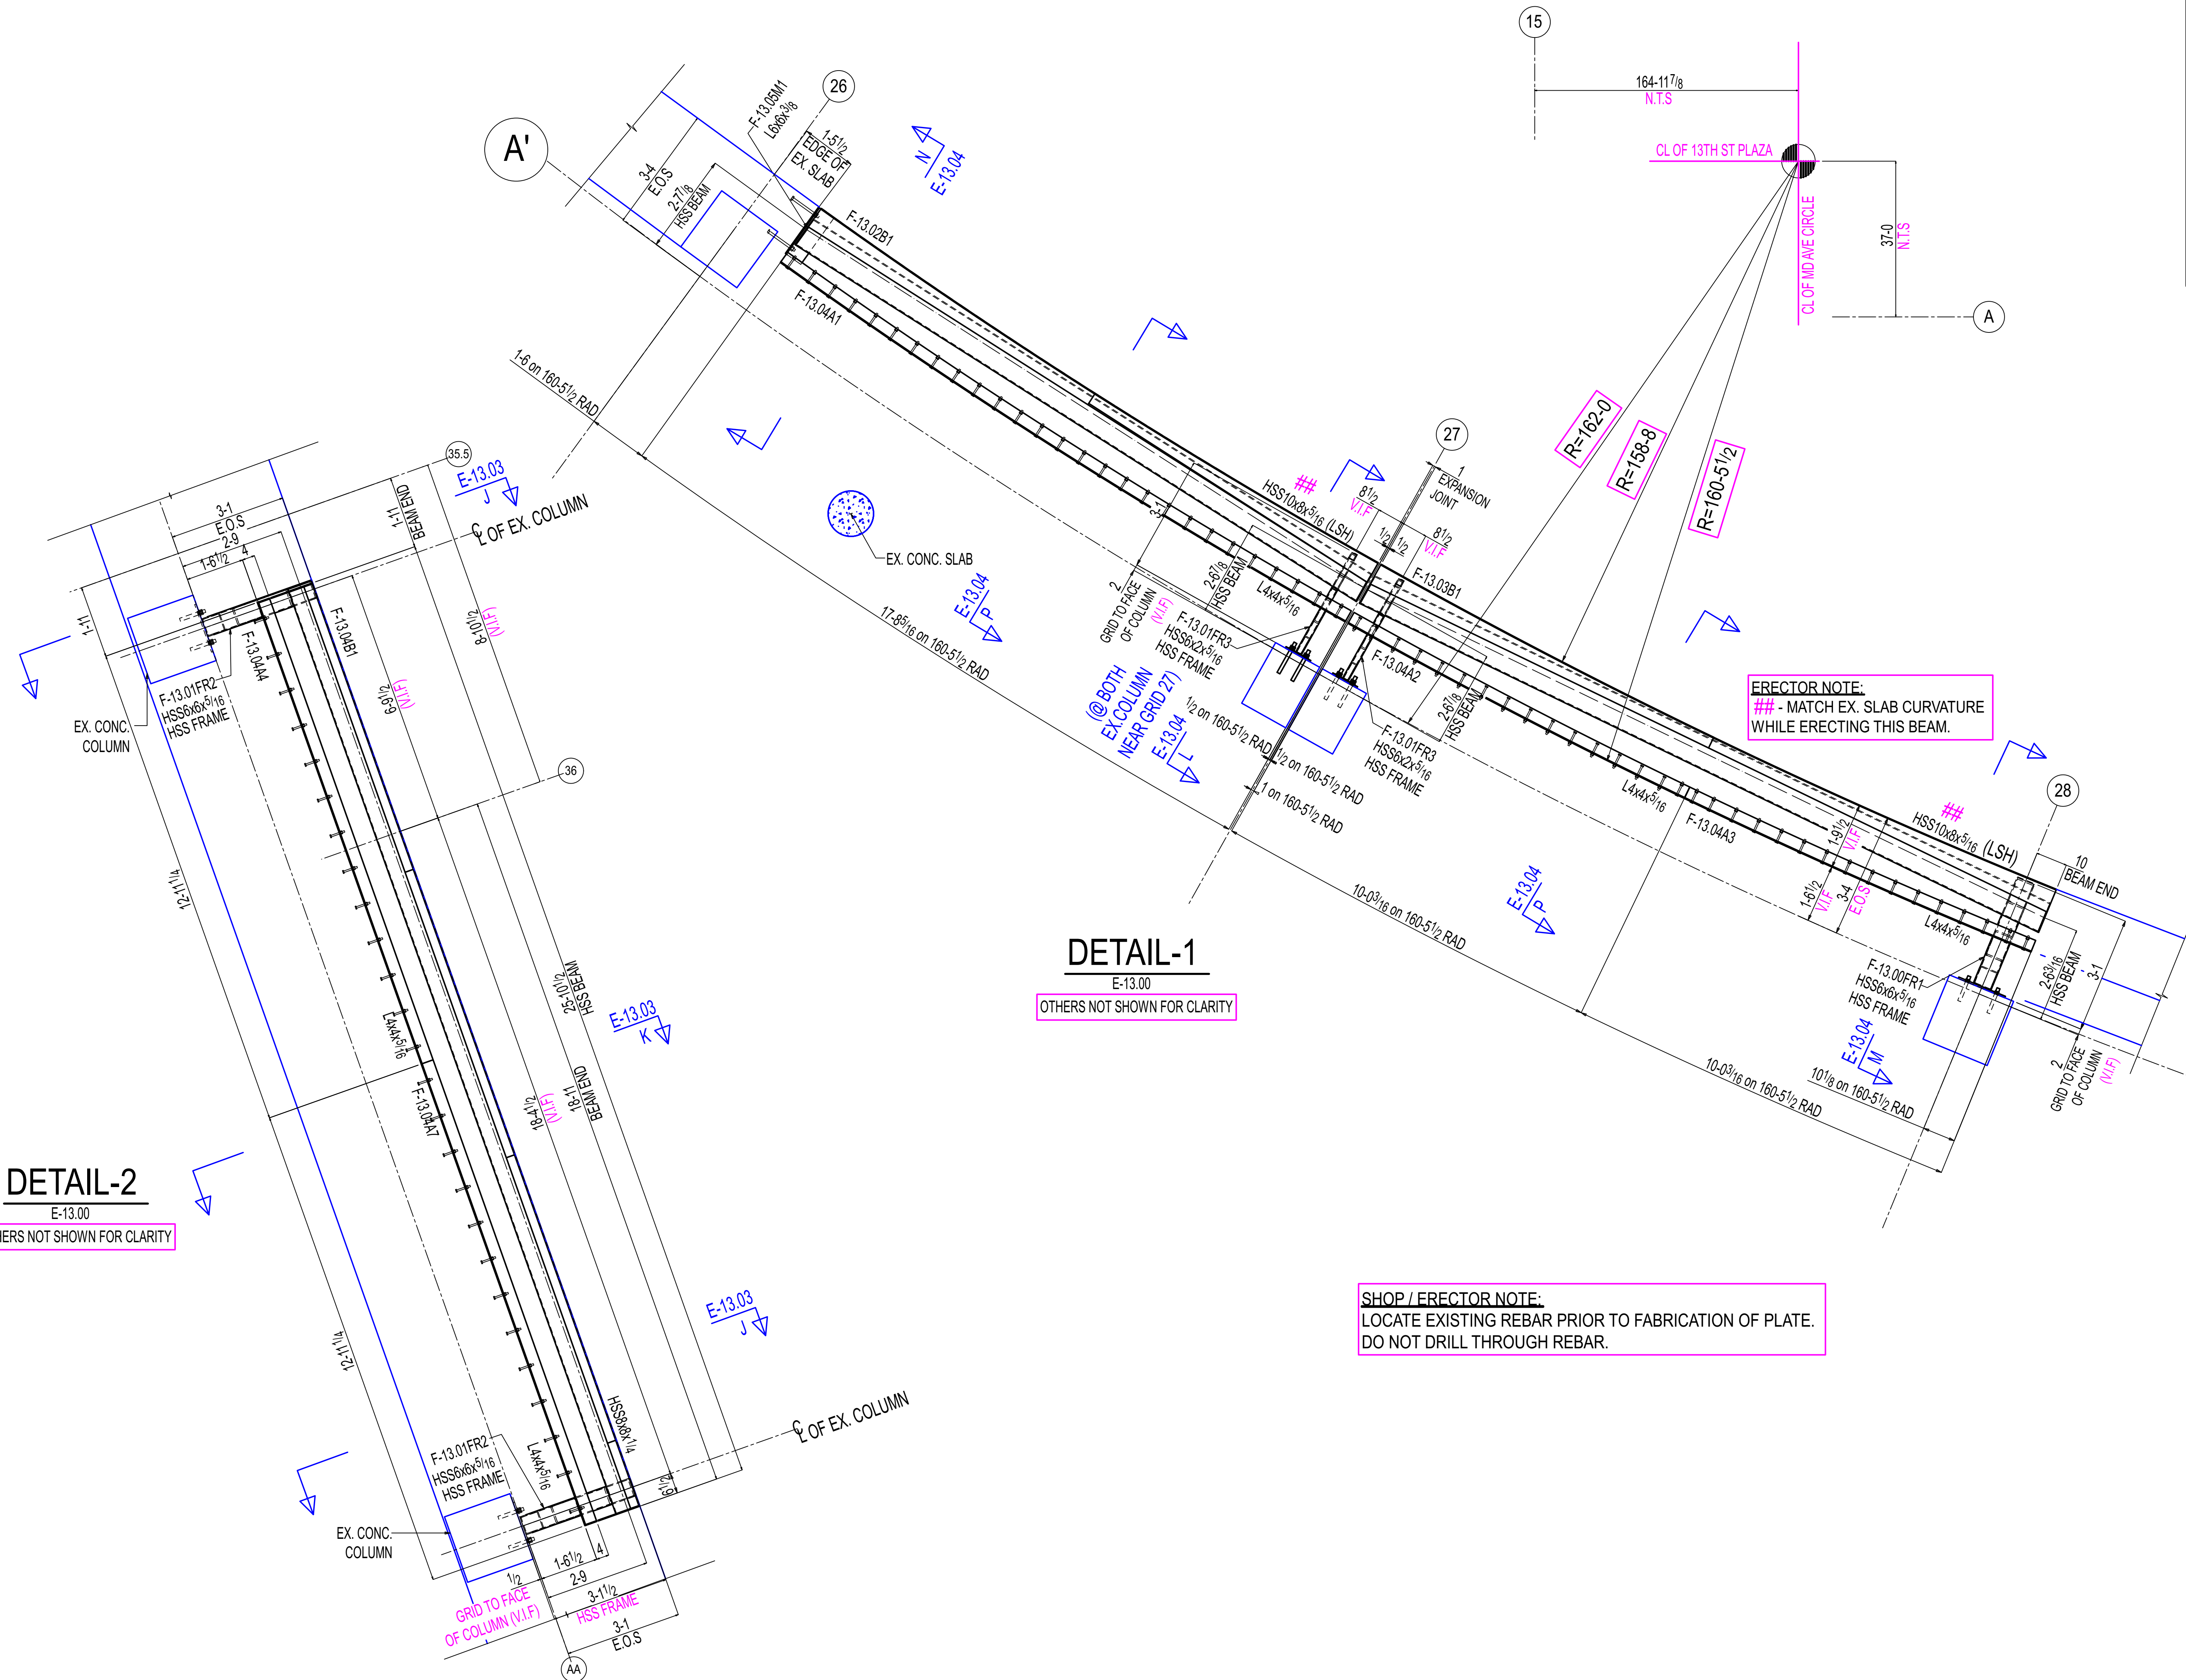


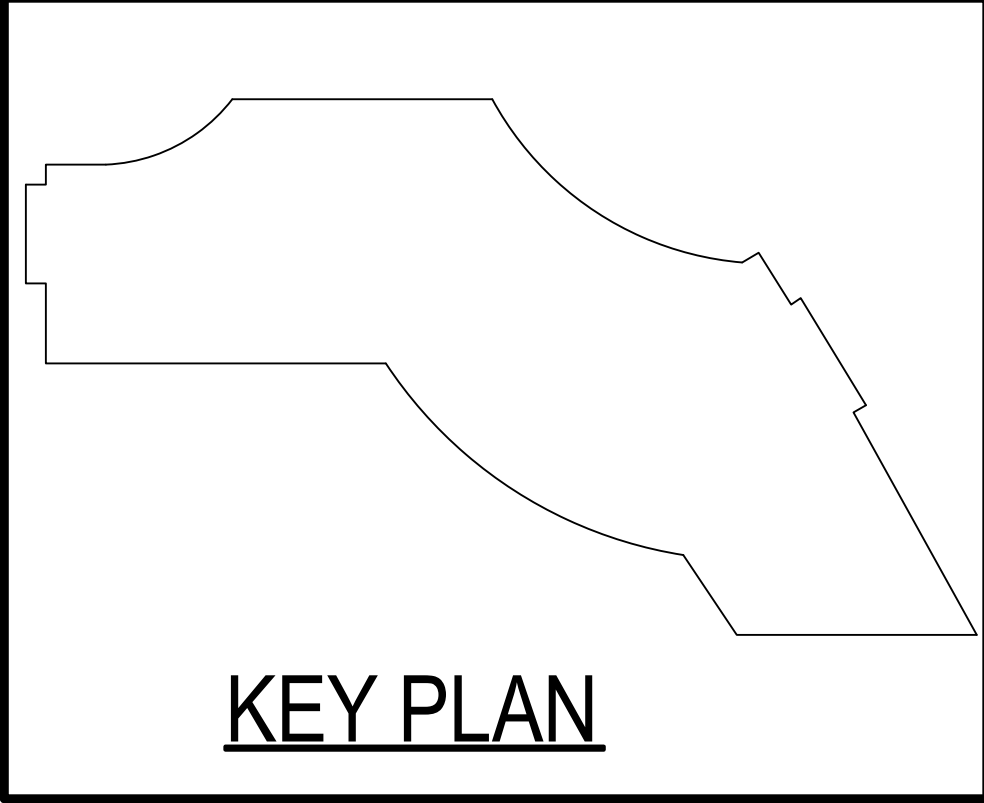

General Notes			
*Structural steel shall conform to ASTM-A992.			
*Structural SQR/RND tubing conform to ASTM A500 Grade C.			
*Pipe shall conform to ASTM A53, Grade B.			
*Channels, Angles and plates shall conform to A36.			
*All bolts shall be 3/4" High strength in accordance with ASTM A325 (UNO).			
*Welding Electrodes for Carbon steel :E70xx			
# of Copies	Revision/ Issue	Destination	Date
3	0	For Construction	11-17-2025
2	B	For Re-Approval	10-24-2025
1	A	For Approval	09-19-2025

IRON FABRICATION SERVICES, LLC.

3029 M. Street, NW, Suite 202
Washington, DC 20007
Tel: 202-800-5599
Fax: 202-478-0303

Project Name and Address
MARYLAND AVENUE

Location: **1250 MARYLAND AVENUE SW
WASHINGTON, DC 20024**

Contractor:
BALFOUR BEATTY

Approved for Fabrication by: _____
Signature: _____

Contract #	224009	Drawing #	E-13.00A
Contract Item:	LEVEL-07 SLAB EXTENSION		
Ref:	SOW-13: (S112,1/A056)		
Date	01/20/2025	Drawing Title:	SOW #13 LEVEL-07 NEW SLAB EXTENSION SUPPORT FRAMING PLAN
Scale	VARIES		