
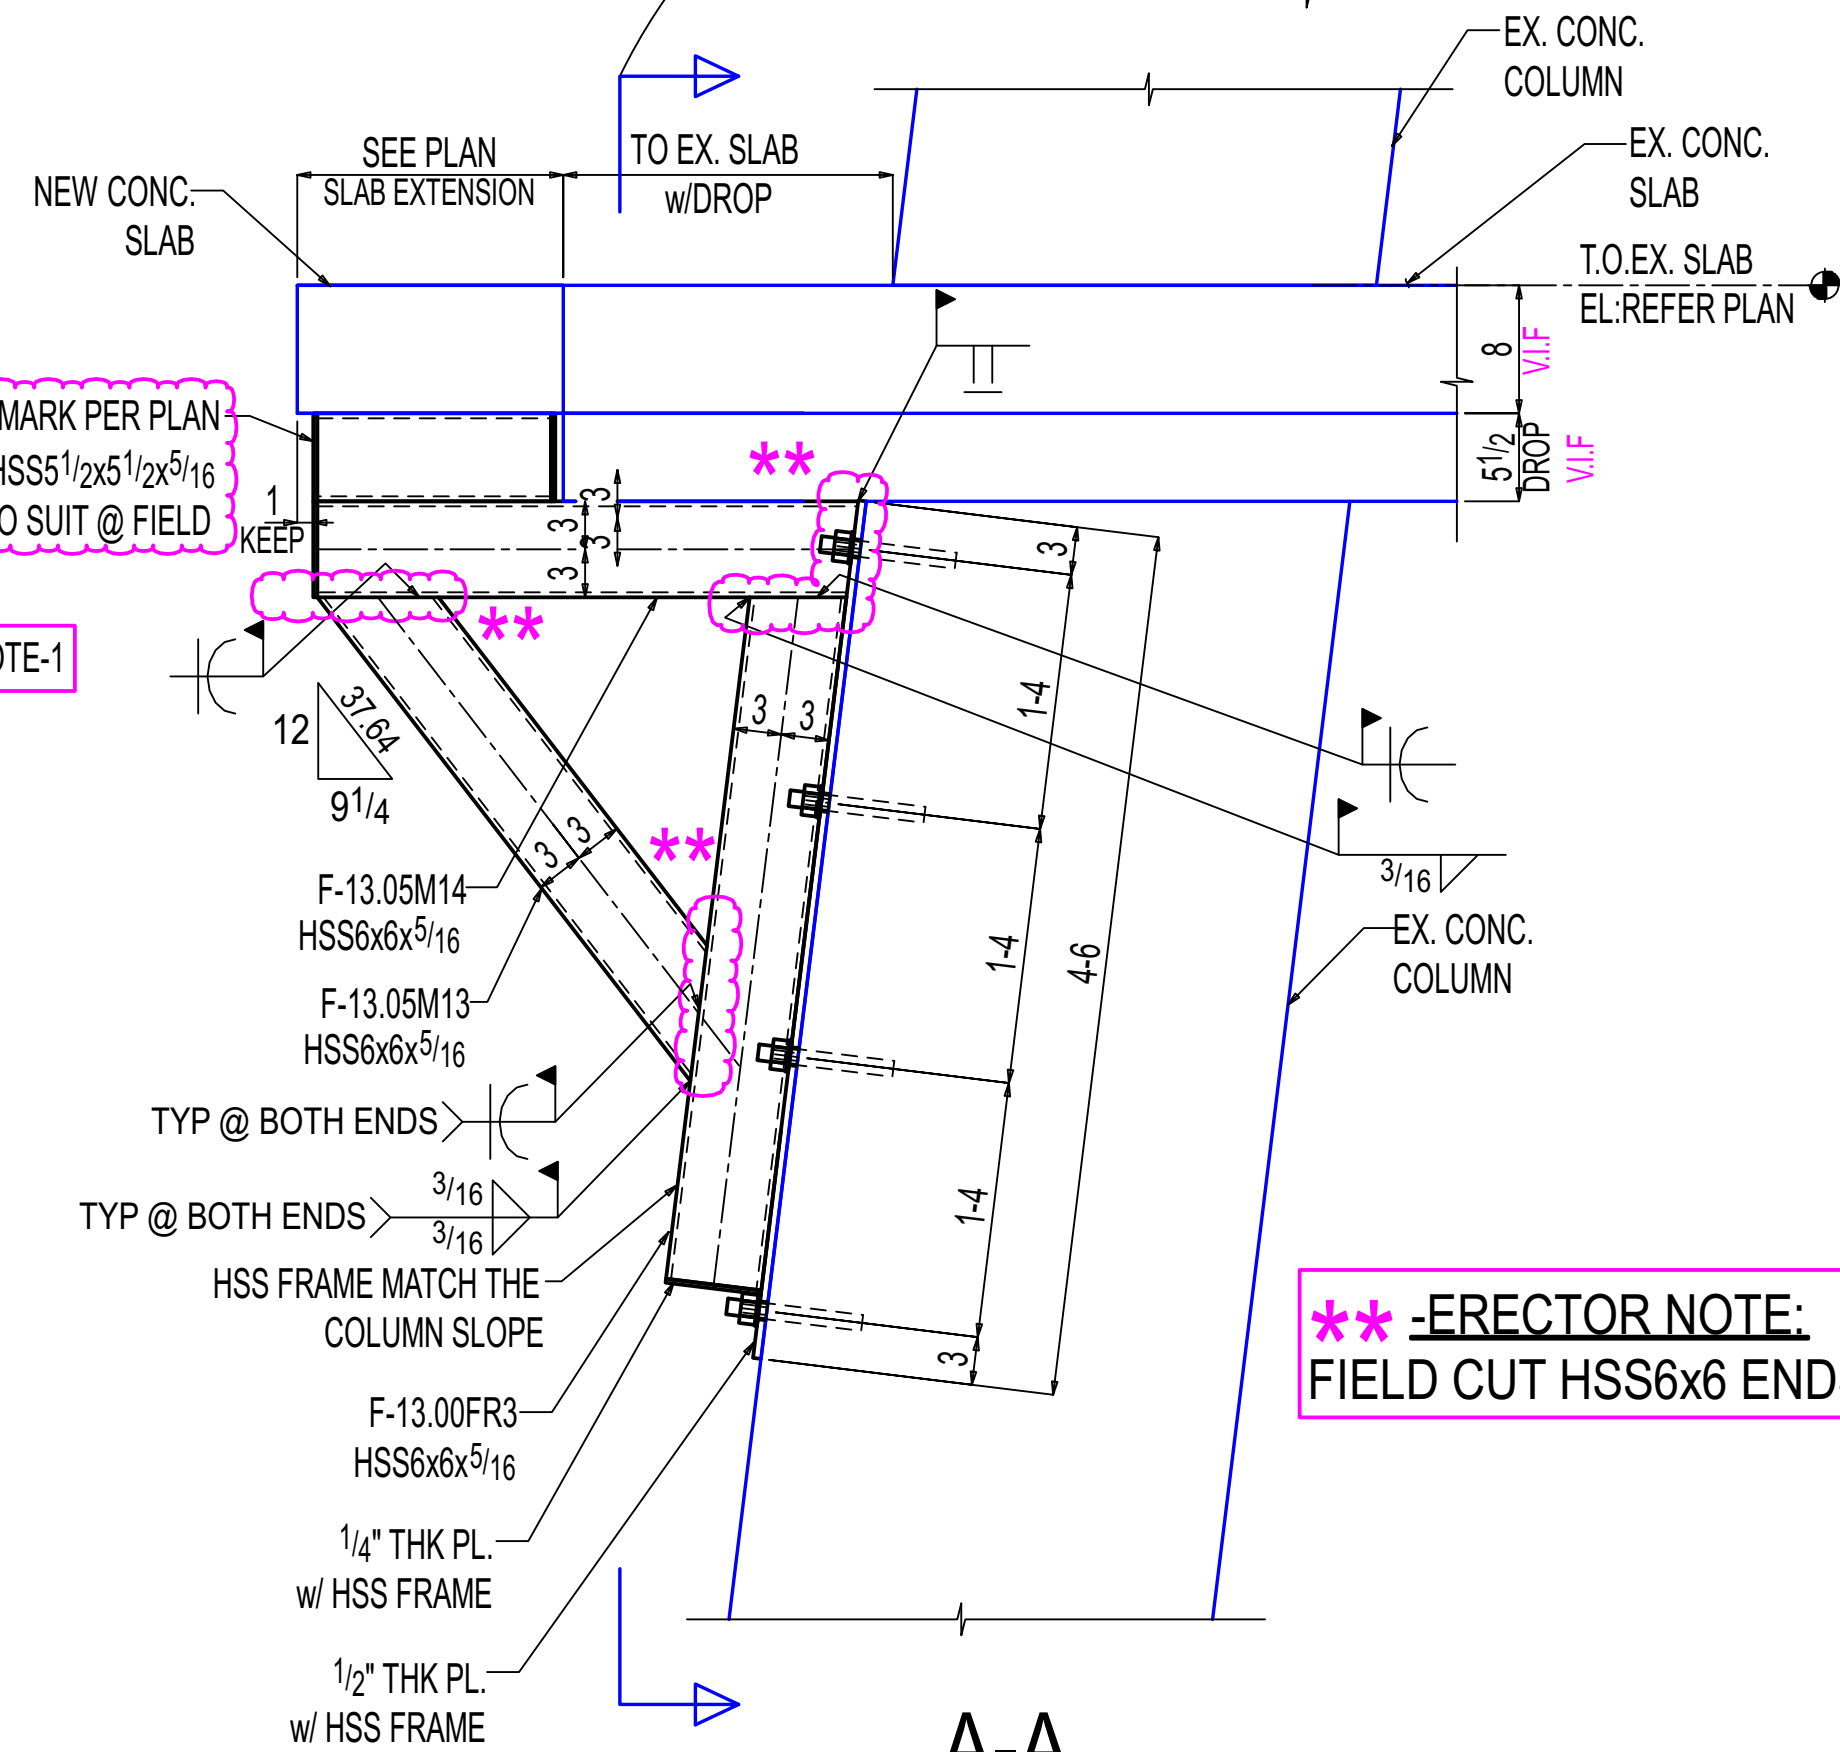


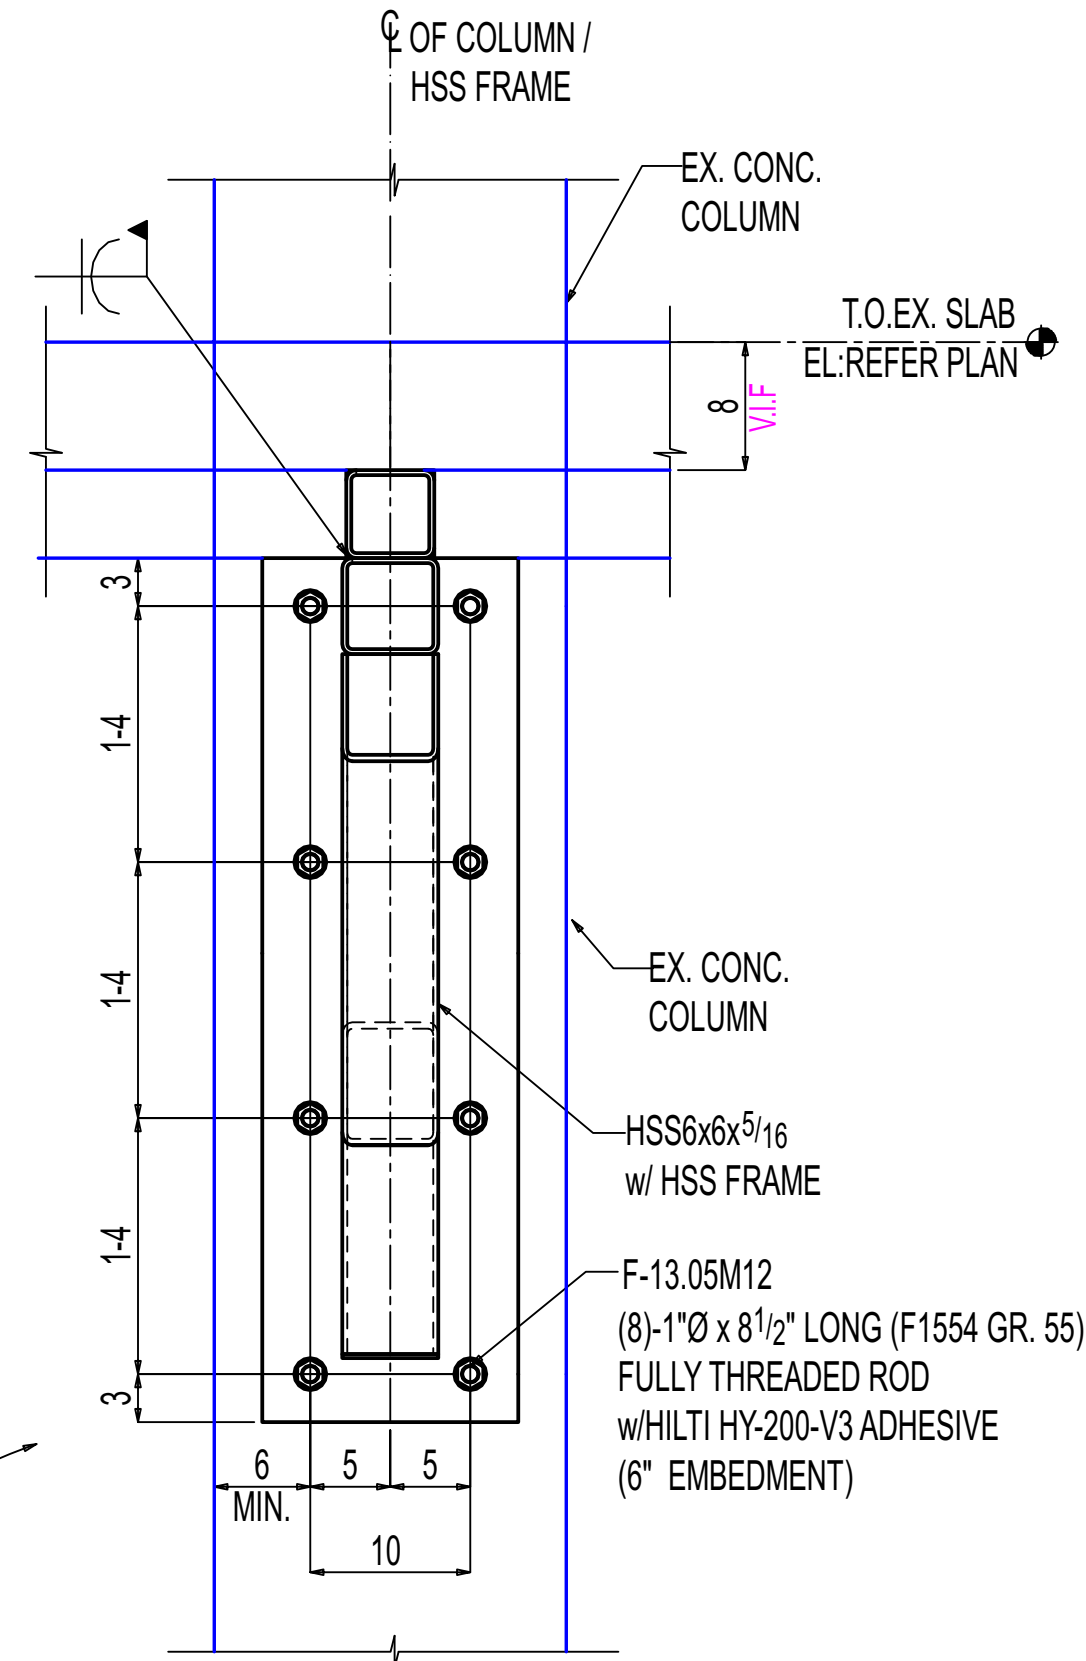

A-A


E-13.00
(REF: 9/S315)

OTHERS NOT SHOWN FOR CLARITY

**** -ERECTOR NOTE:**
FIELD CUT HSS6x6 ENDS TO SUIT AT EXISTING COLUMN SLOPE.

SHOP / ERECTOR NOTE:
LOCATE EXISTING REBAR PRIOR TO FABRICATION OF PLATE.
DO NOT DRILL THROUGH REBAR.


ERECTOR NOTE-1:
ADJUST HSS FILLER DEPTH IN FIELD BY CUT THE HSS FILLER TO MATCH
EXISTING SLAB DROP THICKNESS, AND WELD TO THE
TOP OF HSS FRAME AT SITE PRIOR TO ERECTING THE HSS FRAME.

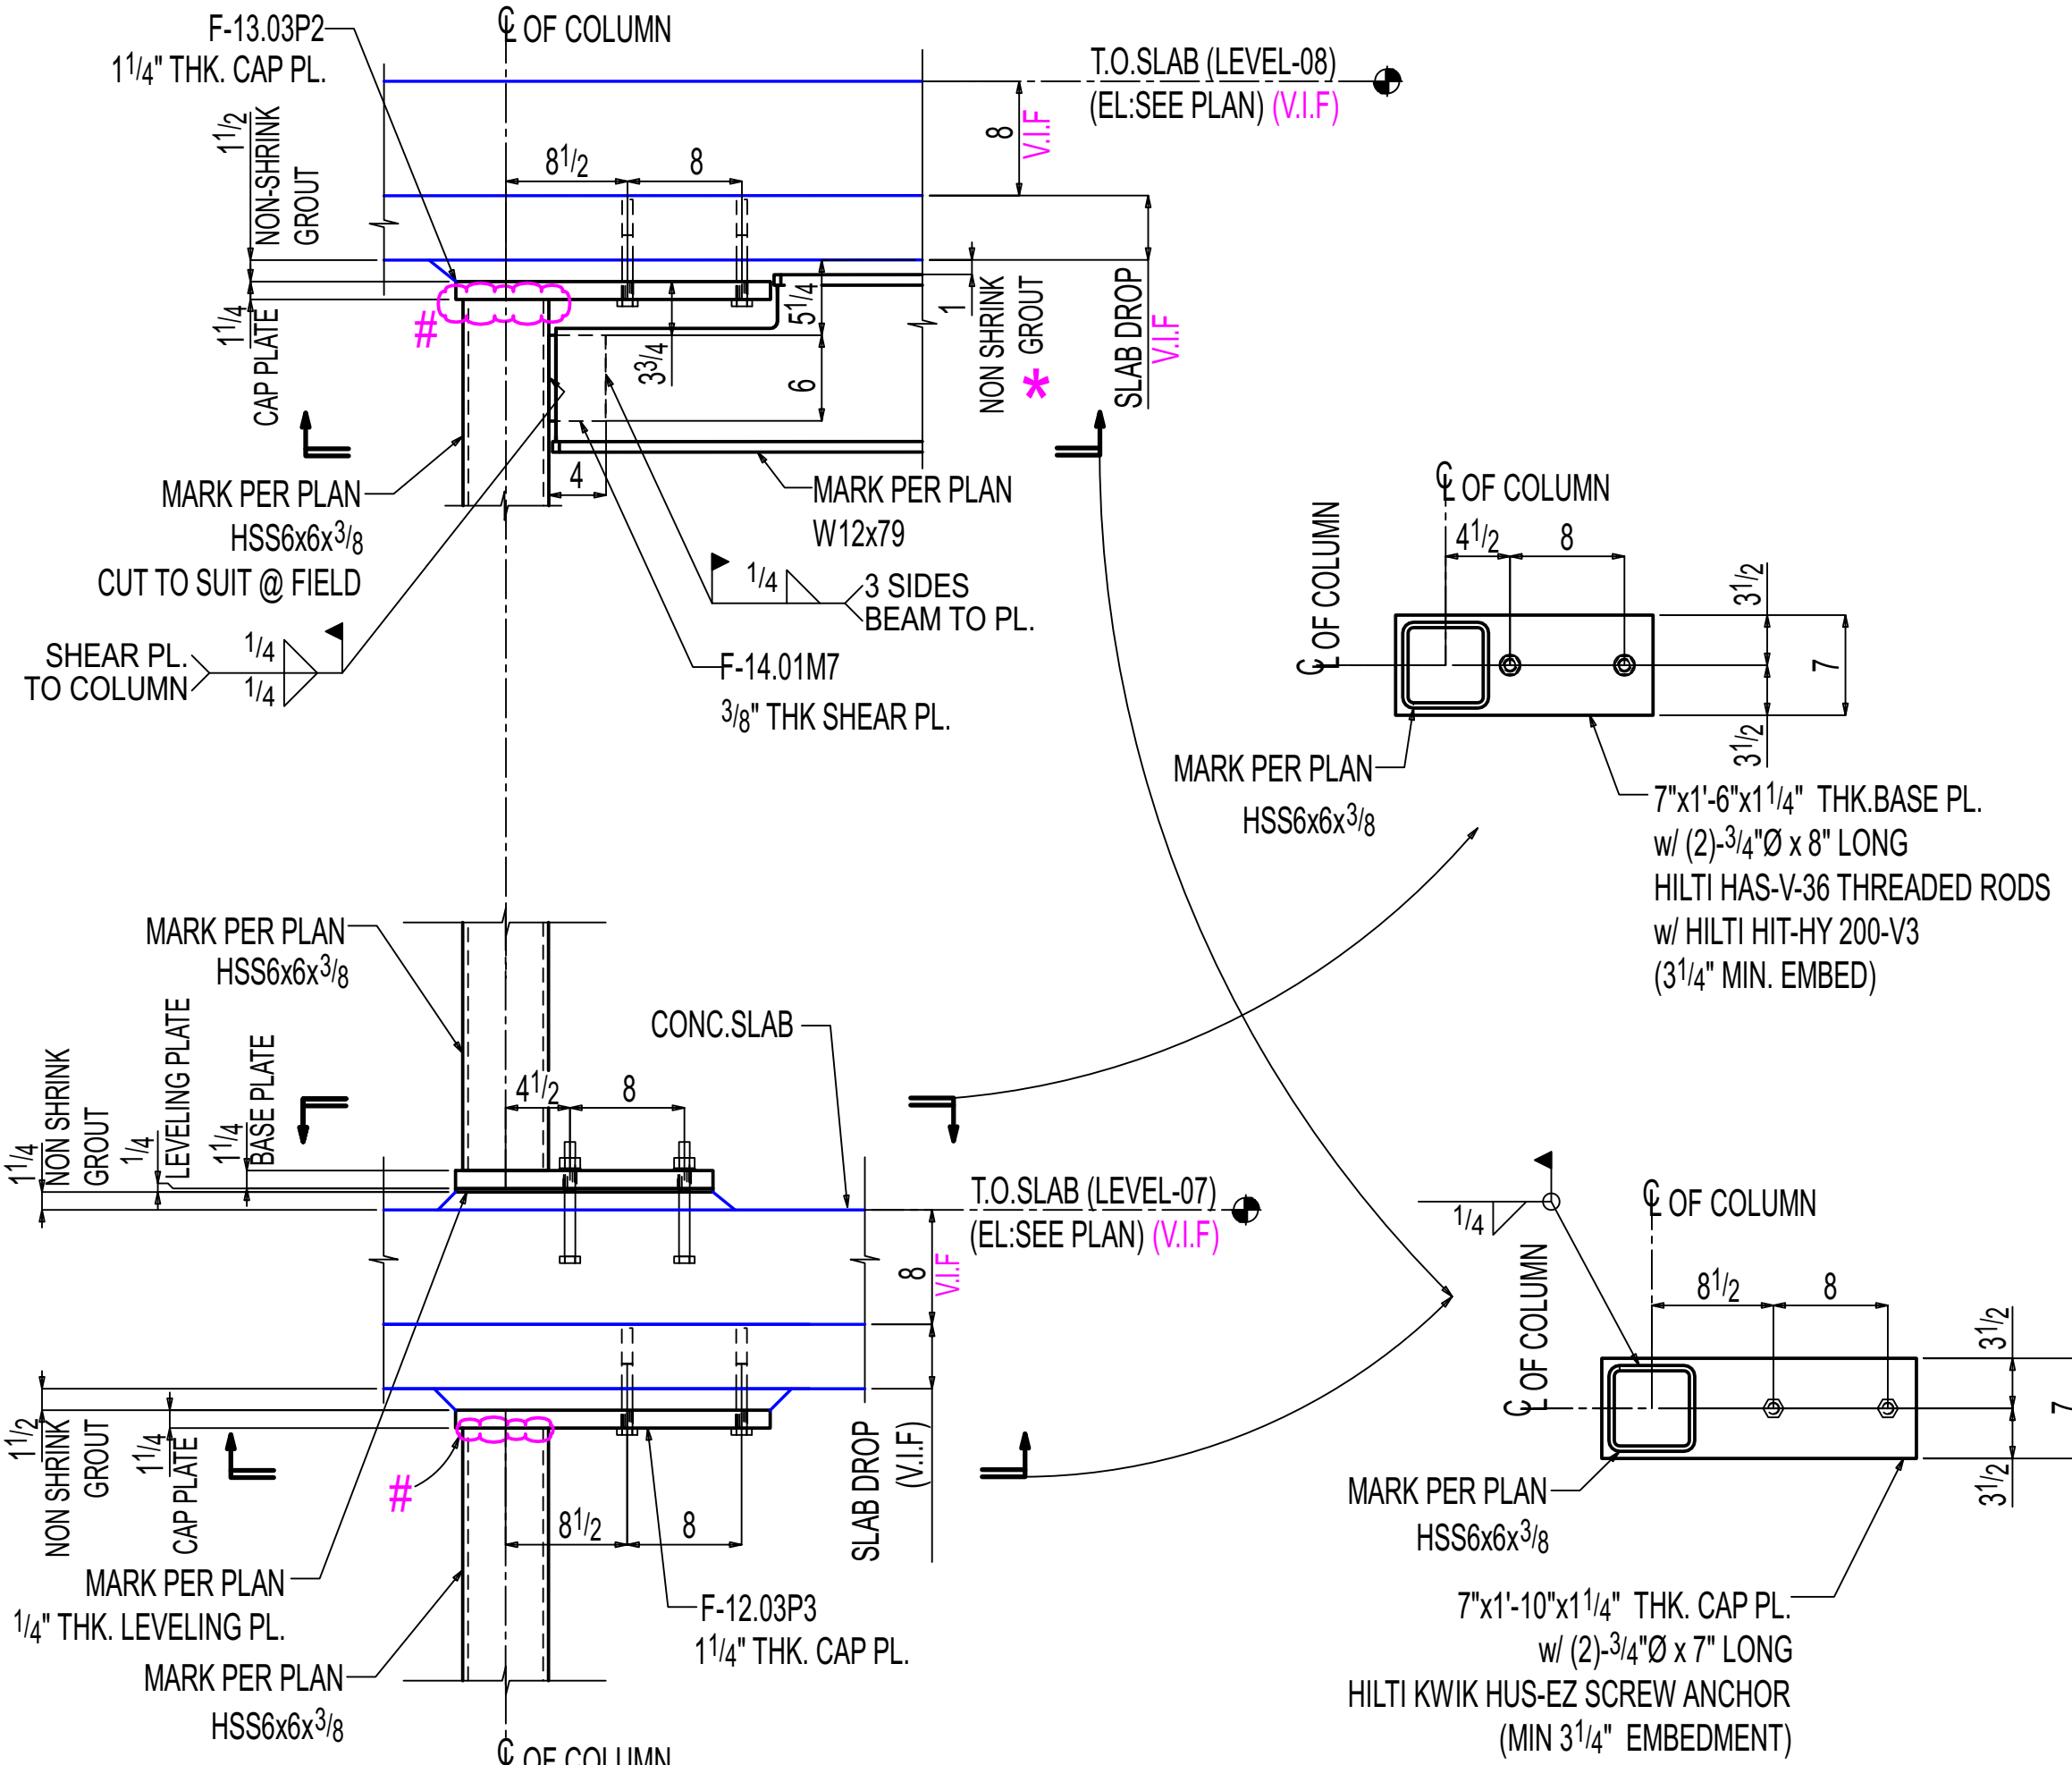

B-B

E-13.00
(REF: 5,6/S314)

OTHERS NOT SHOWN FOR CLARITY

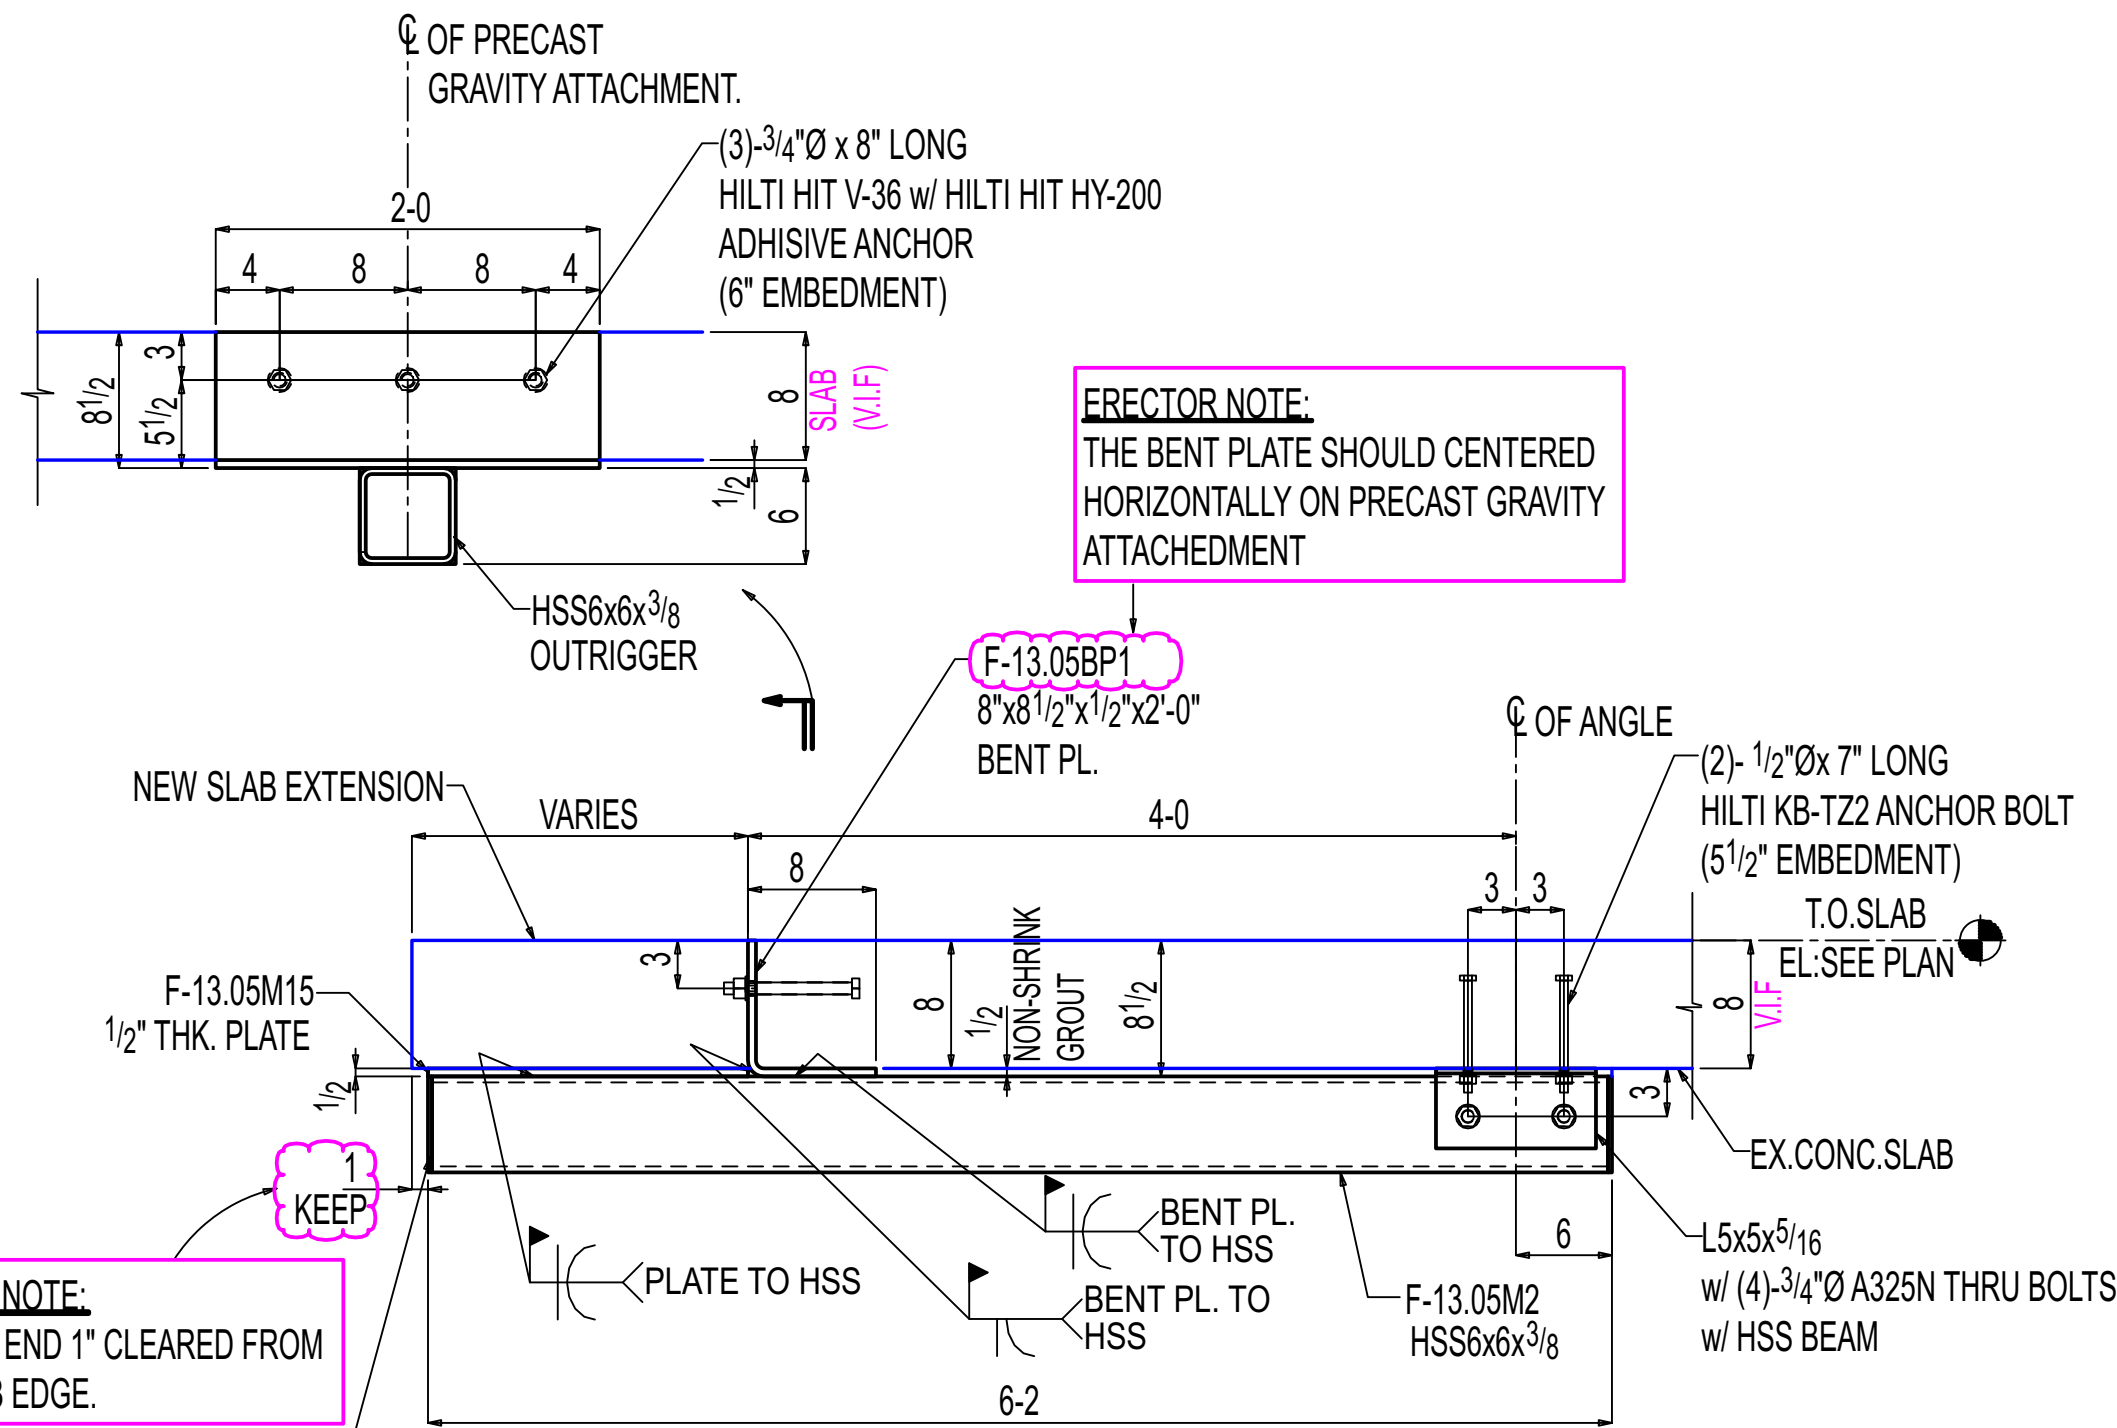

C-C

E-13.00
(REF: 3/S316)

OTHERS NOT SHOWN FOR CLARITY

*** -ERECTOR NOTE:**
PROVIDE 1" NON -SHRINK GROUT x 12" LONG
CENTERED BENEATH AT PRECAST
ATTACHMENT POINTS.

ERECTOR NOTE:
ALL # INDICATED COLUMN ENDS TO BE
CUT TO SUIT @ FIELD BASED ON FLOOR
TO FLOOR CLEARANCE AND WELD IT TO
THE CAP PLATE.

General Notes

- *Structural steel shall conform to ASTM-A992.
- *Structural SQR/RND tubing conform to ASTM A500 Grade C
- *Pipe shall conform to ASTM A53, Grade B.
- *Channels, Angles and plates shall conform to A36.
- *All bolts shall be 3/4" High strength in accordance with ASTM A325 (UNO)
- *Welding Electrodes for Carbon steel :E70xx

# of Copies	Revision/ Issue	Destination	Date
5	0	For Construction	11-17-2025
4	D	For Re-Approval	10-24-2025
3	C	For Re-Approval	09-19-2025
2	B	For Re-Approval	06-23-2025
1	A	For Approval	02-25-2025

IRON FABRICATION SERVICES, LLC.

3029 M. Street, NW, Suite 202
Washington, DC 20007
Tel: 202-800-5599
Fax: 202-478-0303

Project Name and Address
MARYLAND AVENUE

Location: **1250 MARYLAND AVENUE SW
WASHINGTON, DC 20024**

Contractor:
BALFOUR BEATTY

Approved for Fabrication by: _____
Signature

Contract # **224009** Drawing # **E-13.01**

Contract Item: **LEVEL-07
SLAB EXTENSION**

Ref: **SOW-13: 3,4,5&6 / S307**

Date **01/20/2025** Drawing Title:
**SOW #13 LEVEL-07 NEW
SLAB EXTENSION SUPPORT
SECTIONS**

Scale
VARIES