



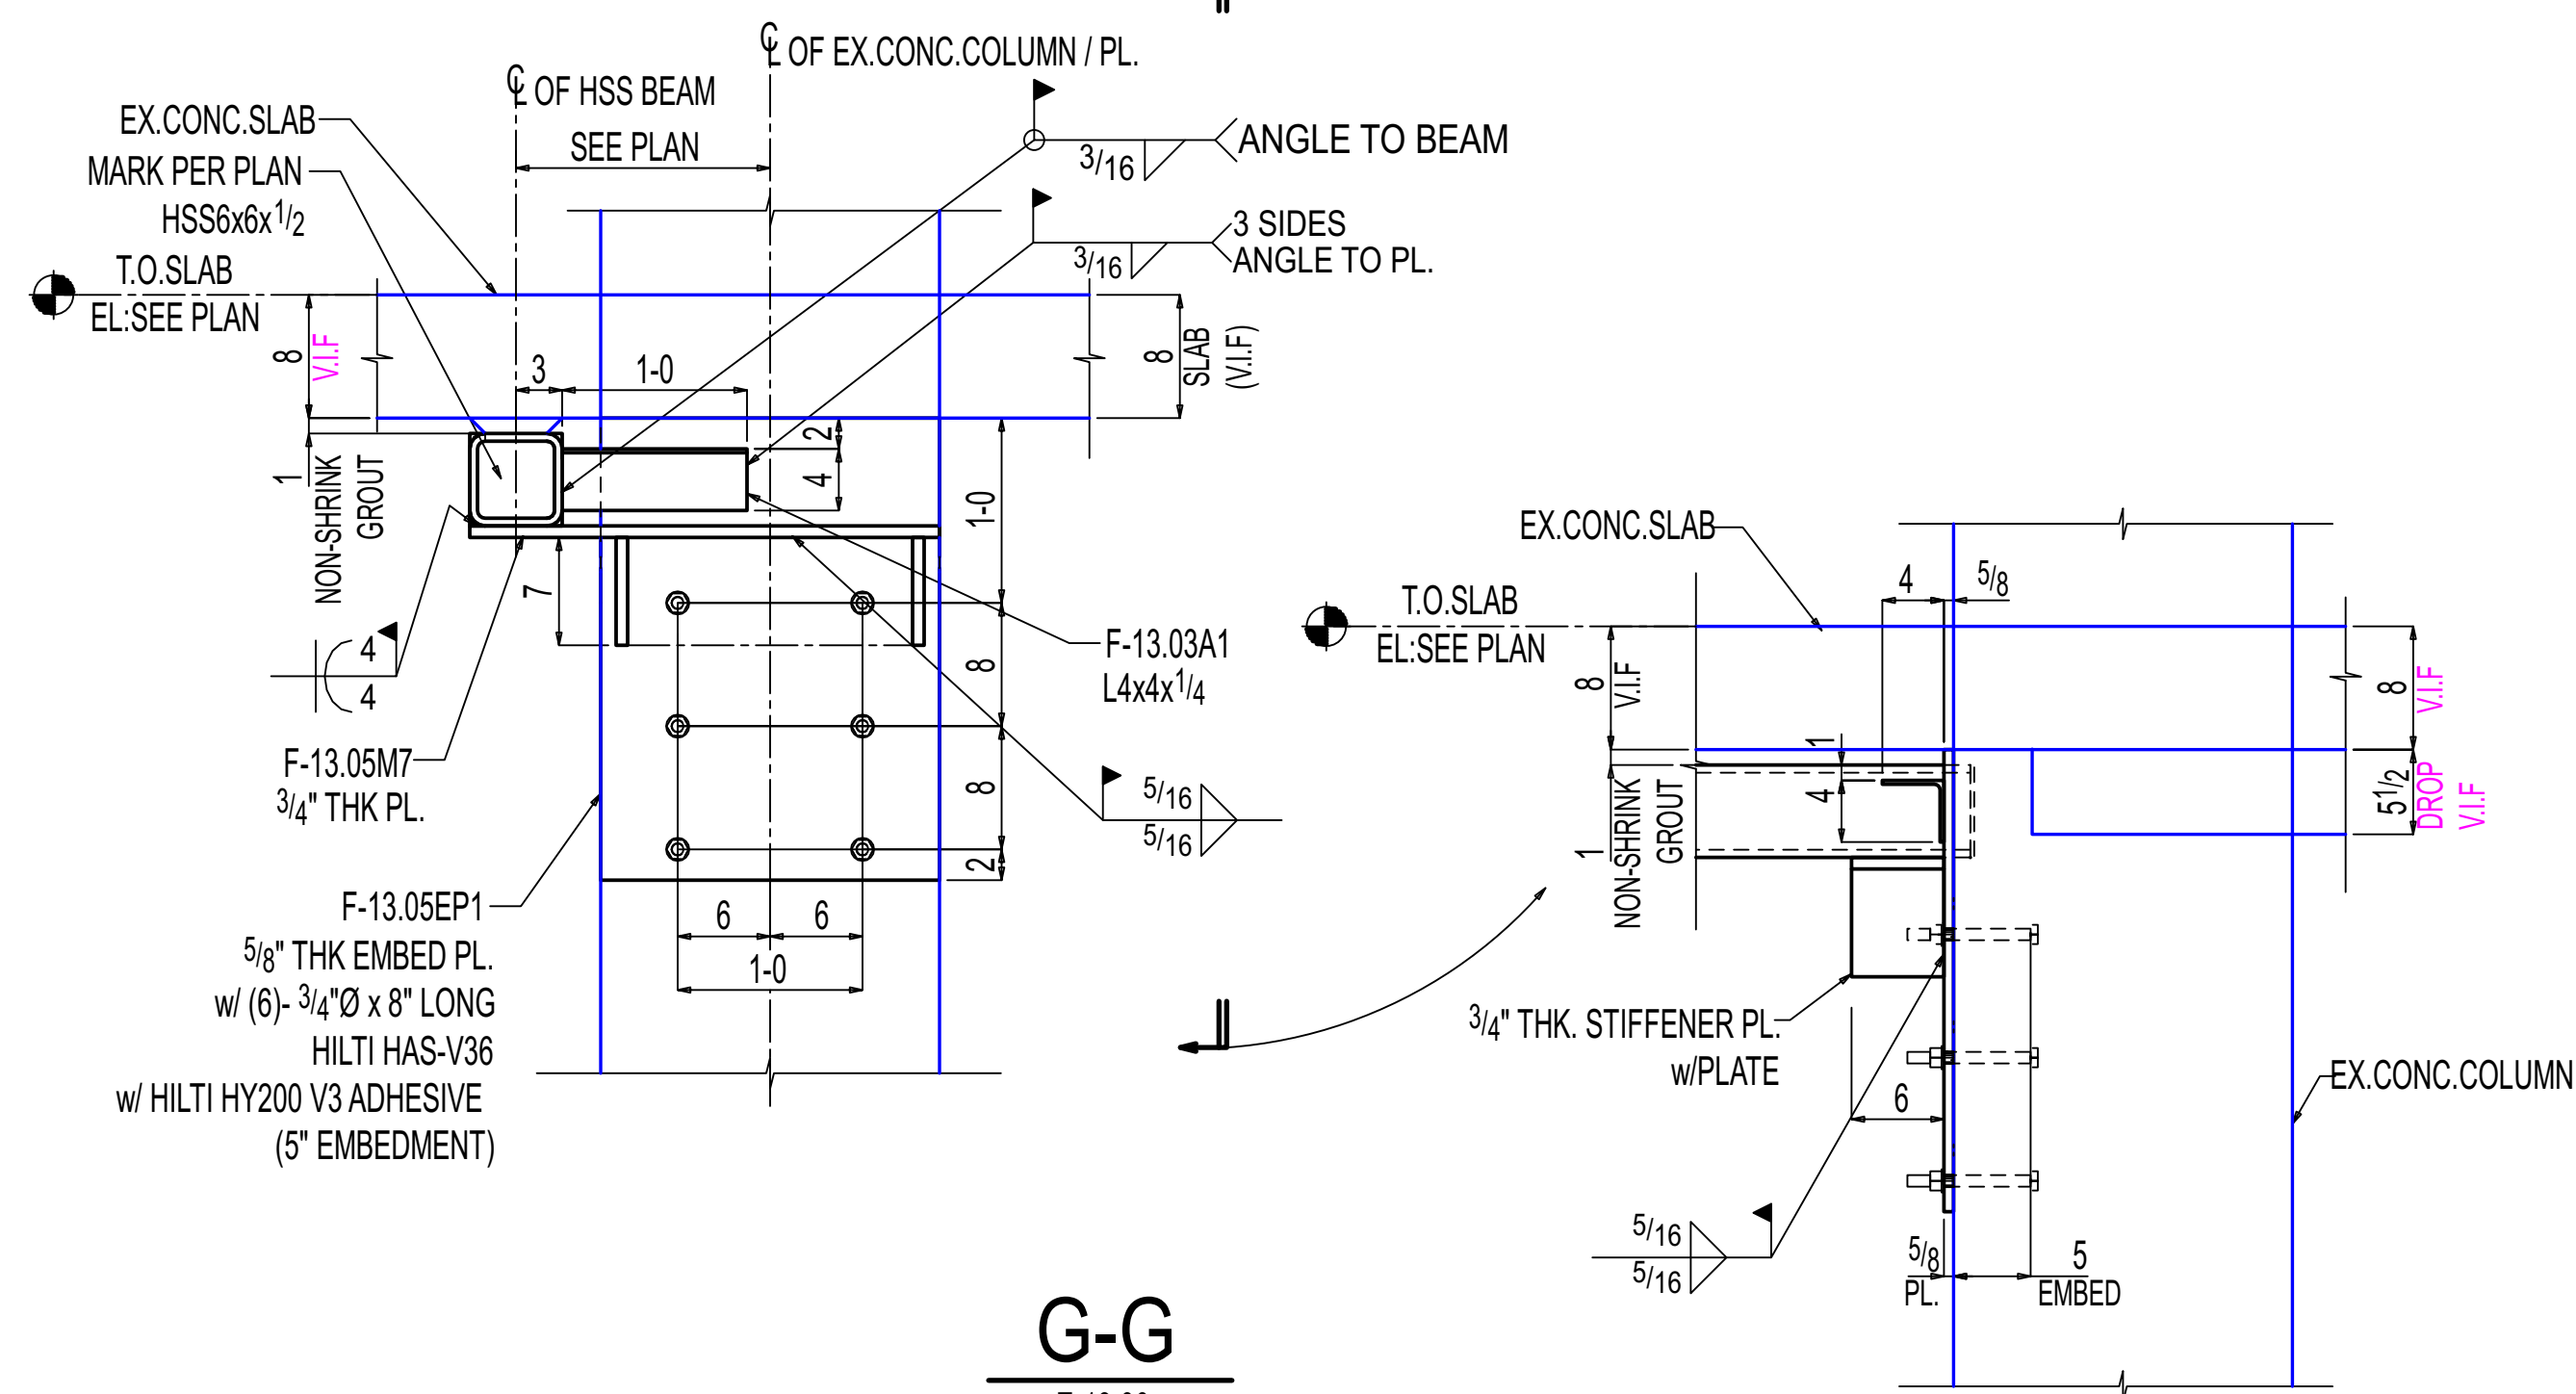

G-G

E-13.00
(REF: 7/S316)


OTHERS NOT SHOWN FOR CLARITY

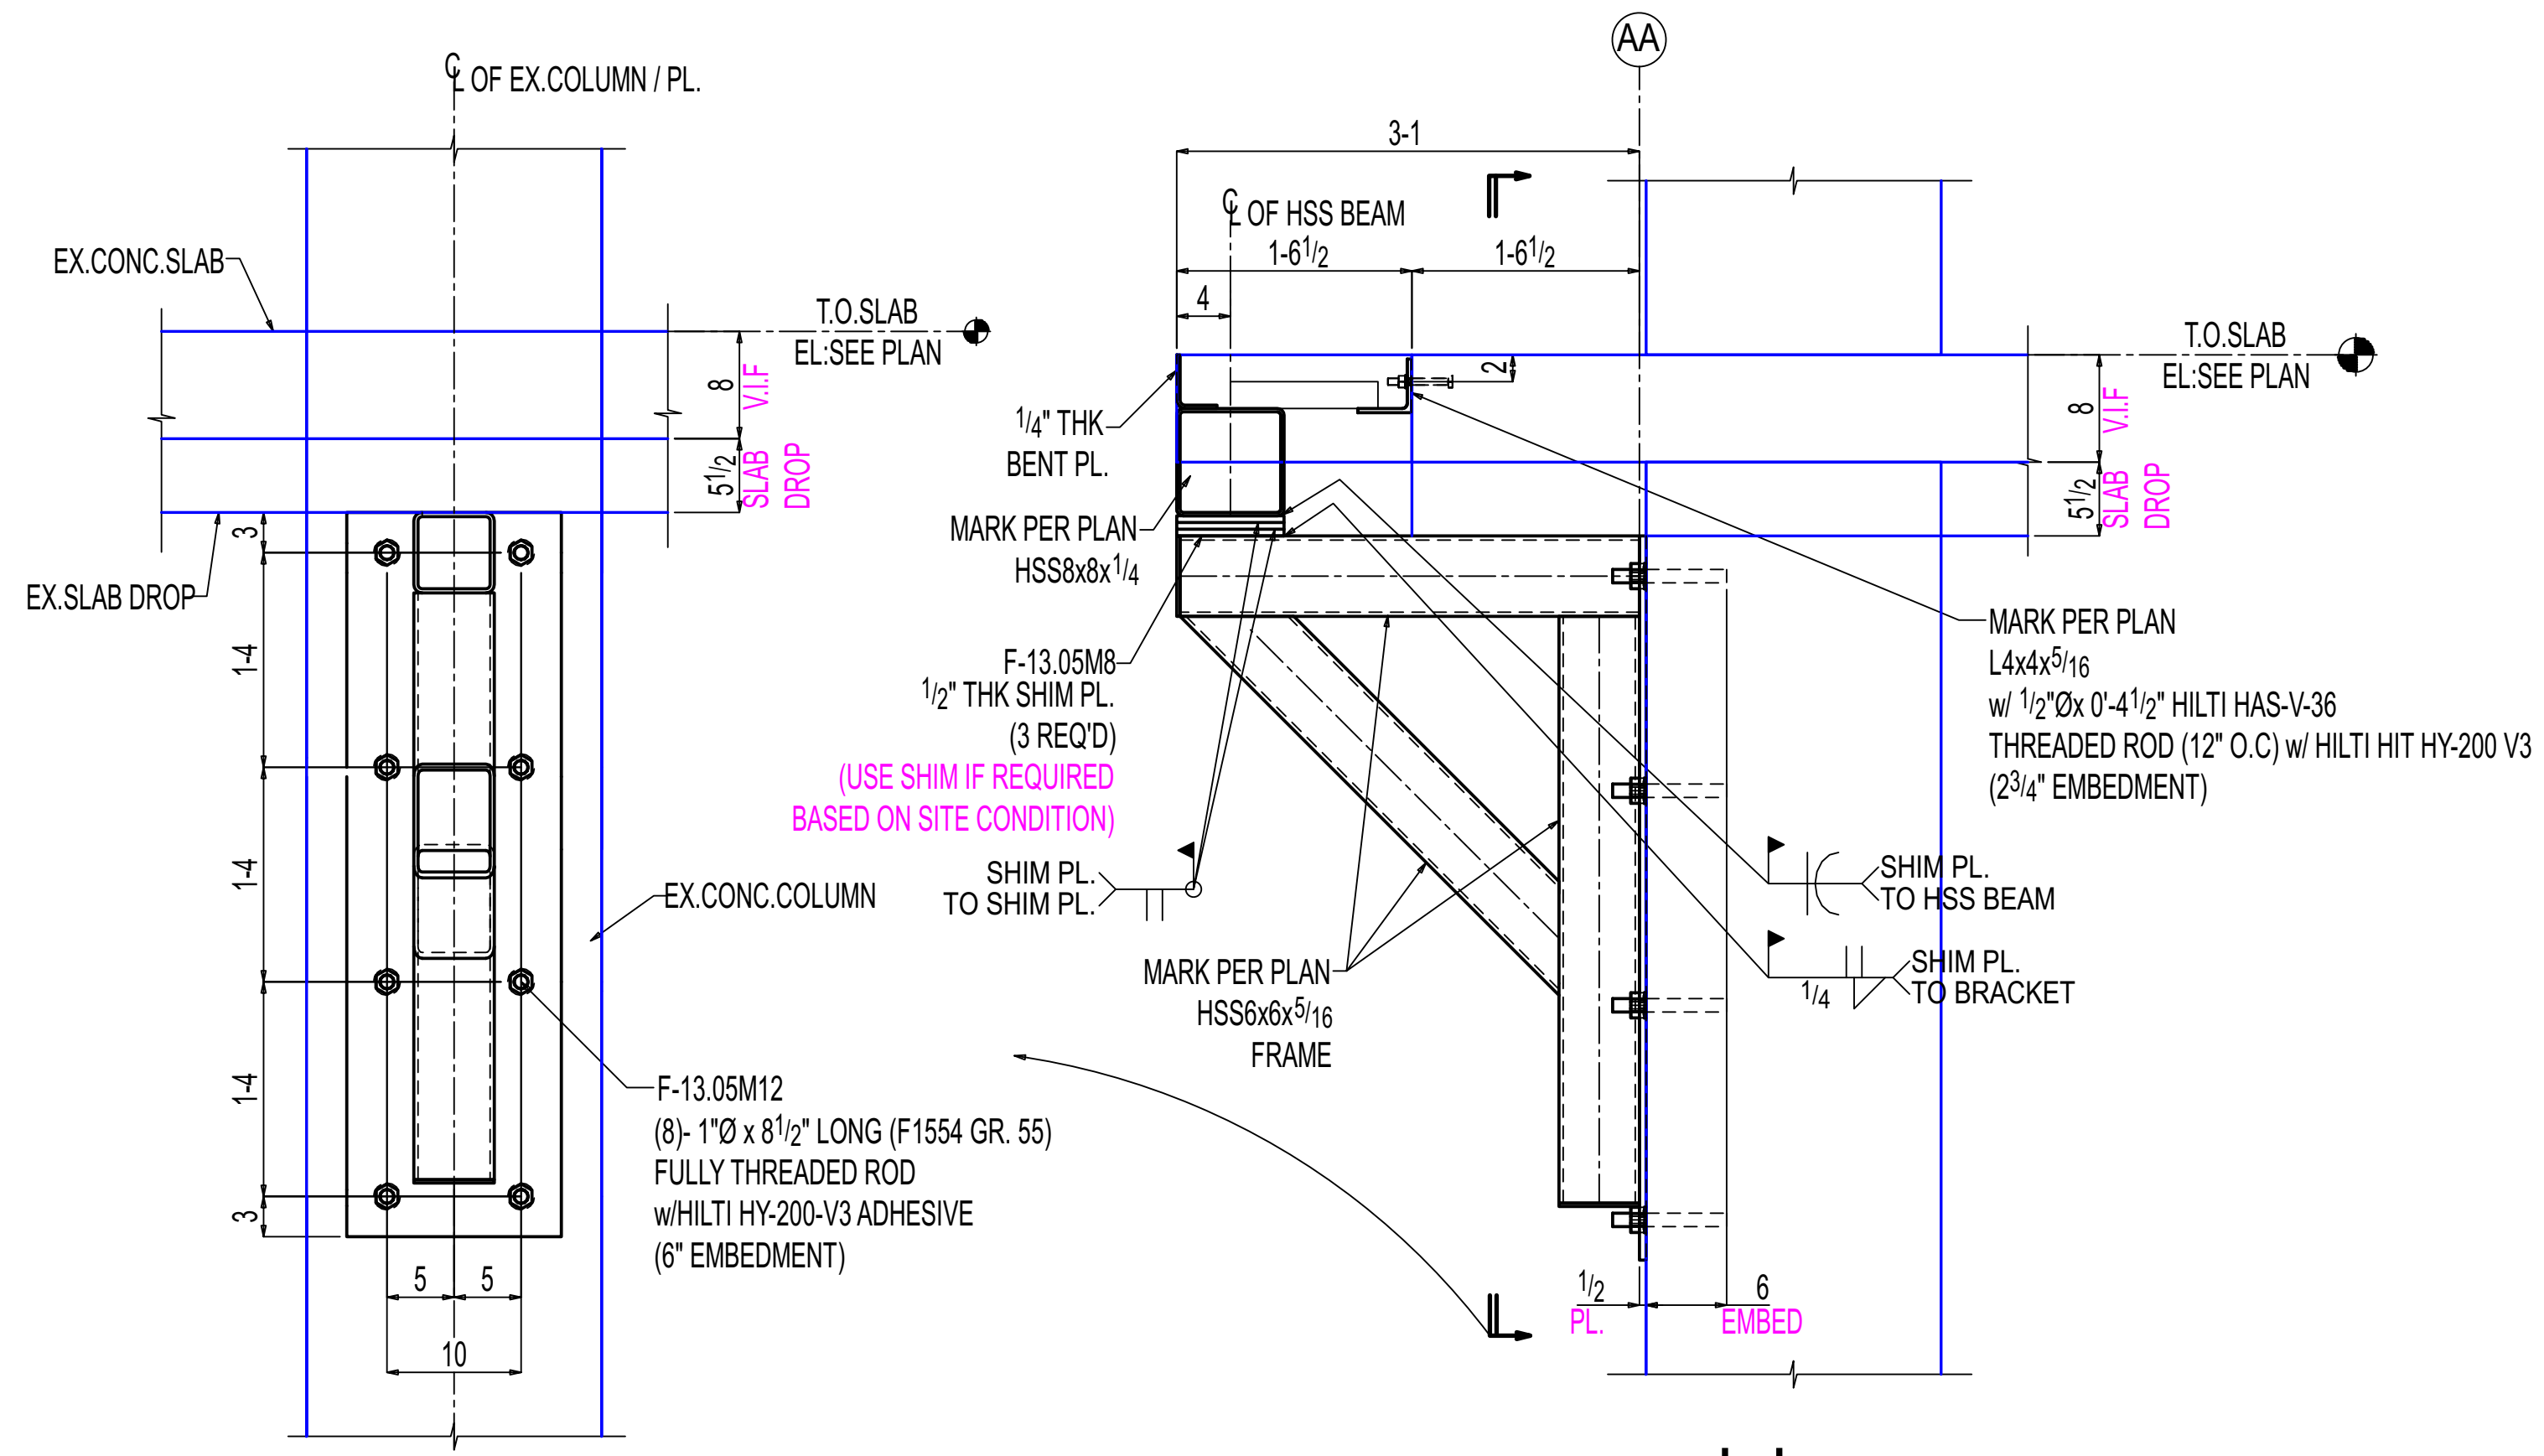

J-J

E-13.00
(REF: 5/S316)


OTHERS NOT SHOWN FOR CLARITY

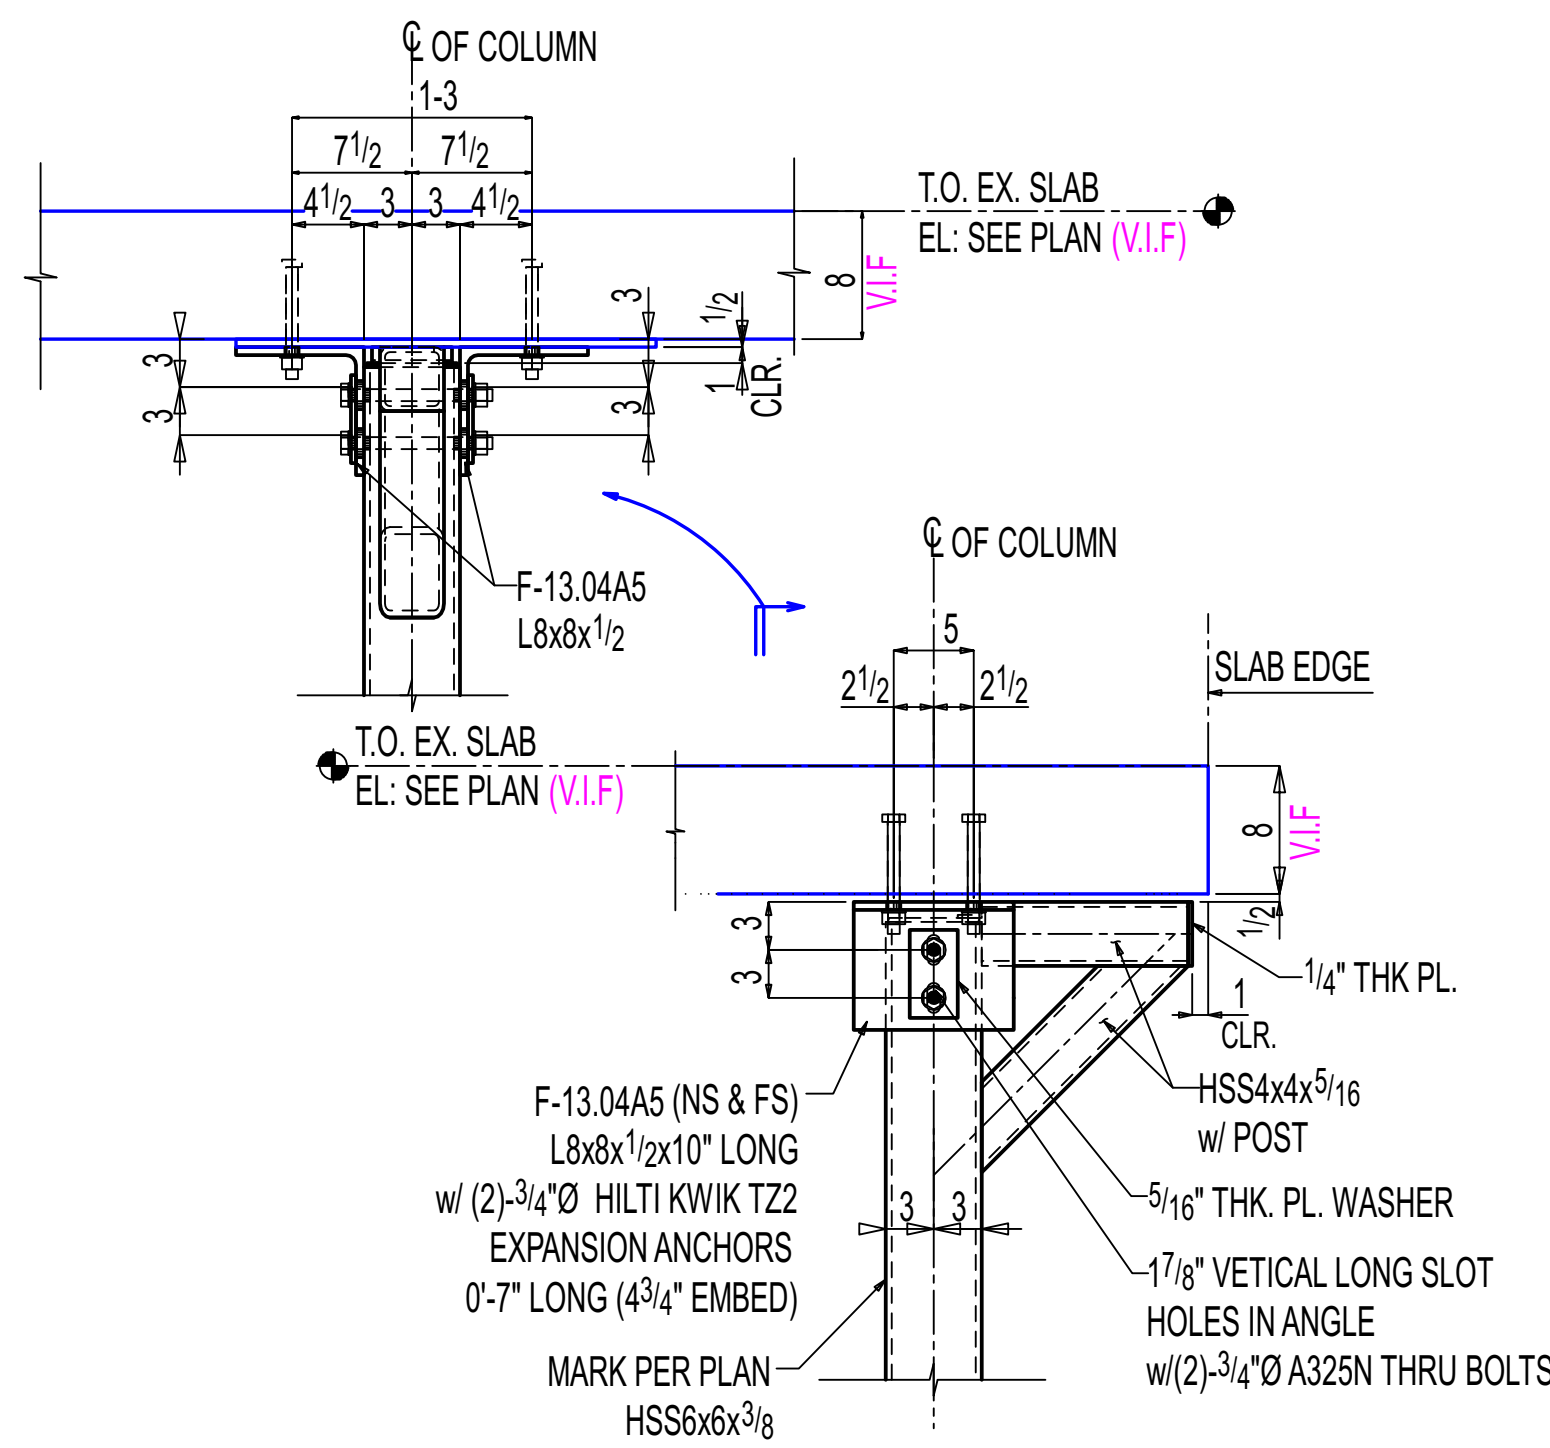

H-H

E-13.00
(REF: 1 & 2/S317)

OTHERS NOT SHOWN FOR CLARITY

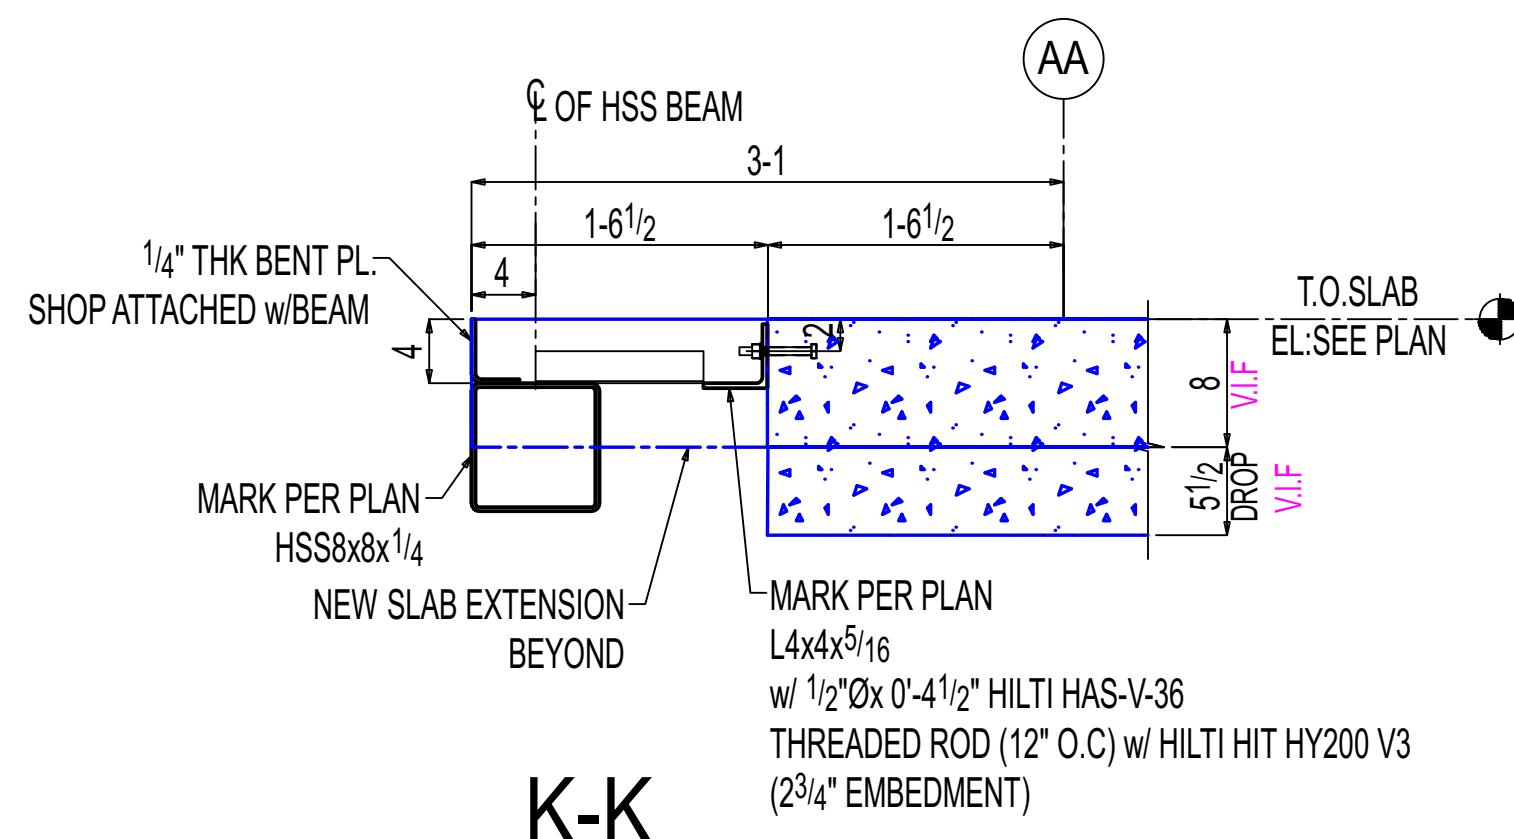

K-K

E-13.00A
(REF: 8/S315)

OTHERS NOT SHOWN FOR CLARITY

General Notes

- *Structural steel shall conform to ASTM-A992.
- *Structural SQR/RND tubing conform to ASTM A500 Grade C.
- *Pipe shall conform to ASTM A53, Grade B.
- *Channels, Angles and plates shall conform to A36.
- *All bolts shall be 3/4" High strength in accordance with ASTM A325 (UNO).
- *Welding Electrodes for Carbon steel :E70xx

# of Copies	Revision/ Issue	Destination	Date
4	0	For Construction	11-17-2025
3	C	For Re-Approval	10-24-2025
2	B	For Re-Approval	09-19-2025
1	A	For Approval	06-23-2025

IRON FABRICATION SERVICES, LLC.

3029 M. Street, NW, Suite 202
Washington, DC 20007
Tel: 202-800-5599
Fax: 202-478-0303

Project Name and Address

MARYLAND AVENUE

Location: **1250 MARYLAND AVENUE SW
WASHINGTON, DC 20024**

Contractor:

BALFOUR BEATTY

Approved for Fabrication by:

Signature

Contract # **224009**

Drawing # **E-13.03**

Contract Item: **LEVEL-07
SLAB EXTENSION**

Ref: **SOW-13: 3,4,5&6 / S307**

Date

01/20/2025

Scale

VARIES

Drawing Title:

**SOW #13 LEVEL-07 NEW
SLAB EXTENSION SUPPORT
SECTIONS**