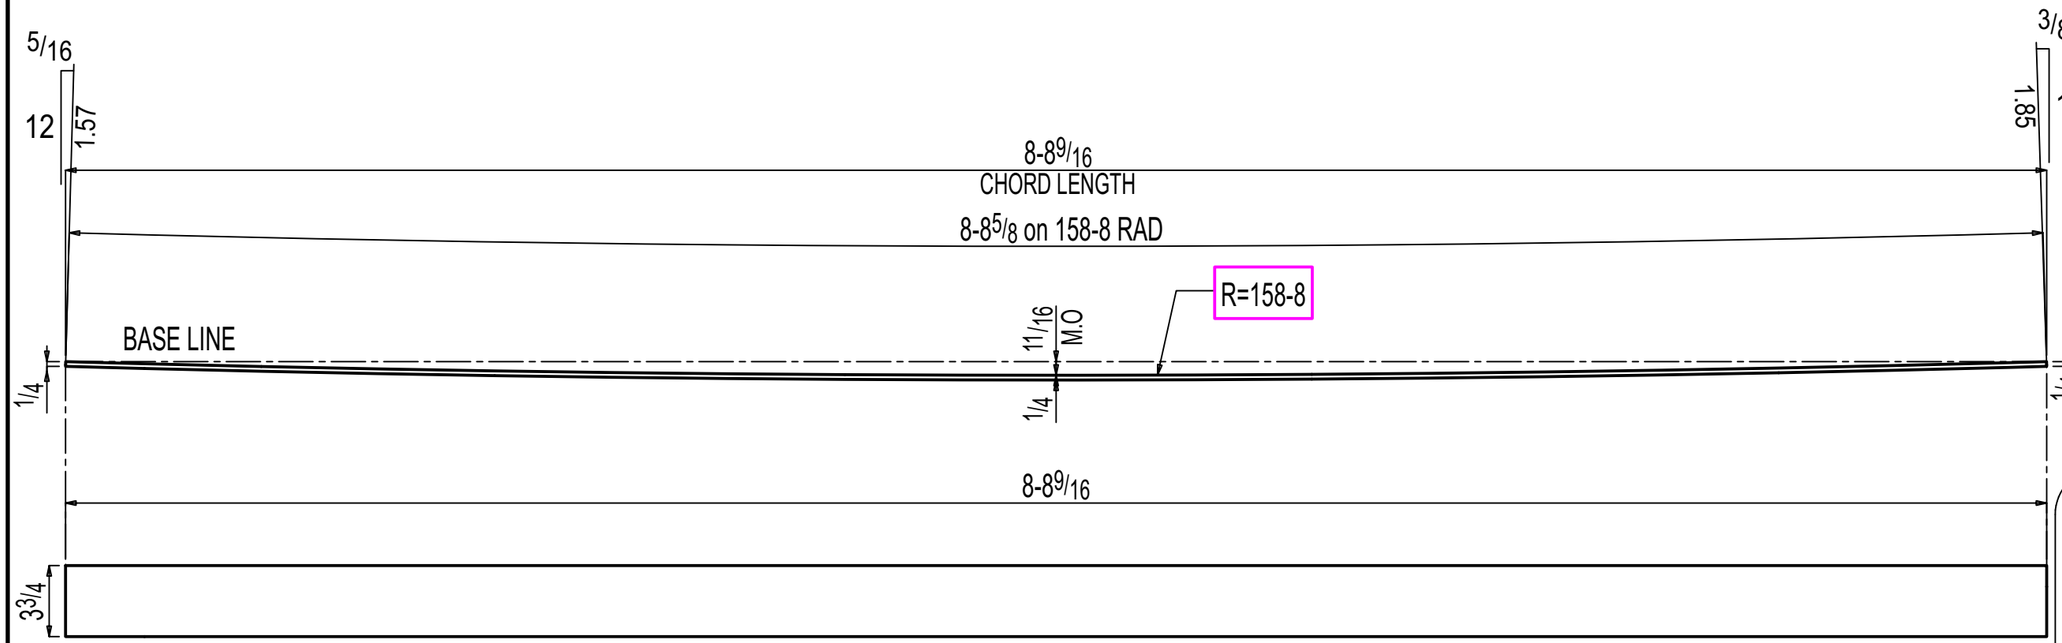

ONE FL 1/4x3 3/4x8-8 5/8 fb12

GRADE: A36

HOLE: 13/16 Ø (U.N.O)

General Notes

*Structural steel shall conform to ASTM-A992.
*Structural SQR/RND.tubing conform to ASTM A500 Grade C
*Pipe shall conform to ASTM A53, Grade B.
*Channels, Angles and plates shall conform to A36.
*All bolts shall be 3/4" High strength in accordance with ASTM A325 (UNO)
*Welding Electrodes for Carbon steel :E70xx
*Structural members are to be shop primer (U.N.O).
*Surface Preparation-SSPC-SP3 UNO.
*If welds exposed to view, should be ground smooth.

# of Copies	Revision/ Issue	Destination	Date
1	0	FOR FABRICATION	11-17-2025

IRON FABRICATION SERVICES, LLC.

3029 M. Street, NW, Suite 202
Washington, DC 20007
Tel: 202-800-5599
Fax: 202-478-0303

Project Name and Address
MARYLAND AVENUE

Location: **1250 MARYLAND AVENUE SW WASHINGTON, DC 20024**

Contractor:
BALFOUR BEATTY

Approved for Fabrication by:	Signature

Contract # **224009** | Drawing # **fb12**

Contract Item: **PLATE**

Ref:
SOW -13:F-13.00-F-13.05

Date **01/ 23/ 2025**

Scale VARIES

Drawing Title: **PLATE**