

1250 Maryland Avenue
1250 MARYLAND AVENUE SW
WASHINGTON, DC 20024

**BEYER
BLINDER
BELLE**
3307 M Street Northwest, Suite 301
Washington, DC 20007
202 333 8000

MECHANICAL & PLUMBING
HURST ENGINEERS
703-534-7872

ELECTRICAL
POWER DESIGN INC.
727-497-9811

STRUCTURAL
RATHGEBER GOSS ASSOCIATES
301-590-0071

CIVIL
GORDON DC
202-869-1600

LANDSCAPE
OVS
202-546-7575

INTERIORS
KTOY SIDG
312-274-0707

LIGHTING
CM KLING + ASSOCIATES
703-684-6270

KEY PLAN

STAMP

4	6/6/25	ISSUED FOR CONSTRUCTION
2	DATE	ADDENDUM 02
NO	DATE	DESCRIPTION

REVISIONS

SUBMITTAL


**ISSUED FOR
CONSTRUCTION**

DRAWING TITLE

SLAB EDGE - LEVEL 09 TO
10

SCALE _____ As indicated
DATE 05/16/25
PROJECT NUMBER 6415.00
DRAWING NUMBER

A057

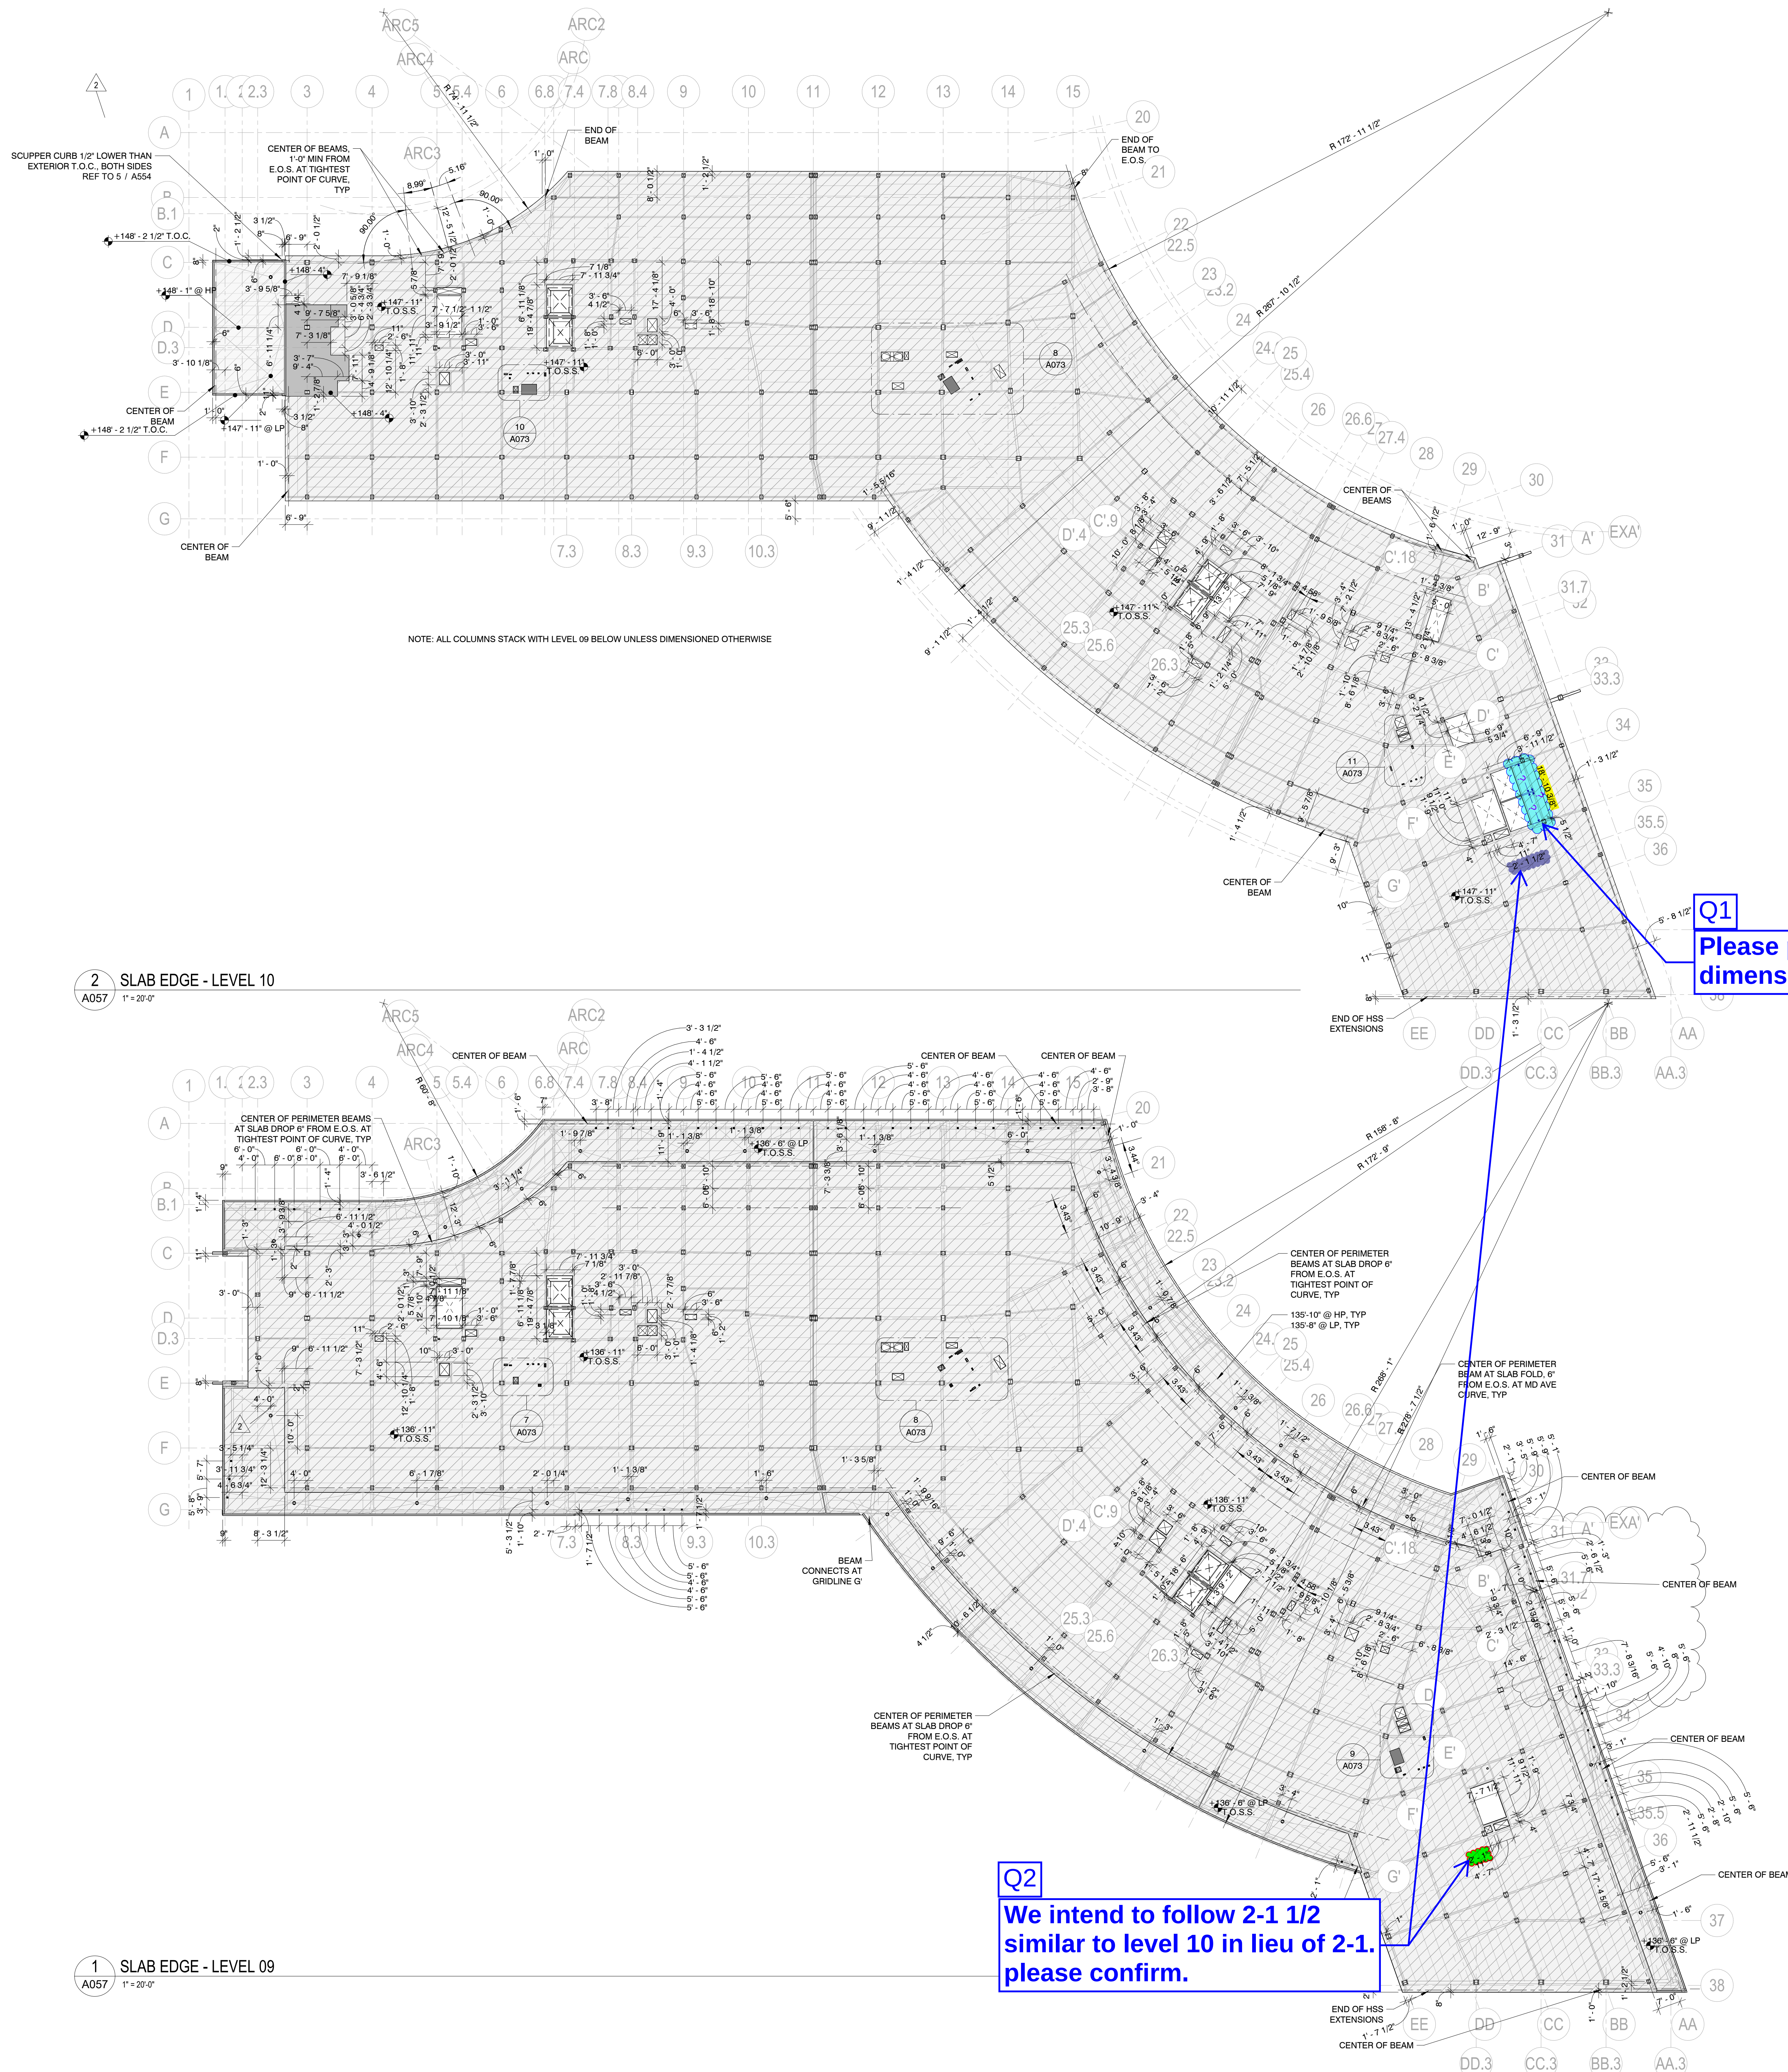

Q2
We intend to follow 2-1 1/2 similar to level 10 in lieu of 2-1. please confirm.


NEW FLOOR STEEL STRUCTURE NOTES:
1. SEE STRUCTURAL DRAWINGS FOR STEEL SIZING & LOCATIONS
2. NEW STEEL COLUMNS ALIGNED W/ EXISTING CONCRETE COLUMNS BELOW UNLESS NOTED OTHERWISE. DIMENSIONS PROVIDED FOR COLUMNS NOT ALIGNED W/ BELOW.
3. SEE STRUCTURAL DRAWINGS FOR STEEL COLUMN SIZING & SHAPE. RECTANGULAR GRAPHIC SHOWN IN ARCHITECTURAL PLANS ALSO REPRESENTS GYPSUM FURRING NEEDED FOR RATING.

LEGEND
NEW STEEL COLUMN, ALIGNED WITH COLUMN BELOW
NEW STEEL COLUMN, SUPPORTED BY BEAM BELOW. SEE DIMENSIONS

SLAB EDGE DRAWING NOTES:
1. SLAB DRAWINGS ARE BASED ON ORIGINAL EXISTING DRAWINGS. ALL LOCATIONS, DIMENSIONS, JOINTS, VERIFI, NOTIF, OPENI, DRAWI, INFILL.
2. SEE D NEW Q DEMO, ARCH, 10.
3. SEE A DEMO, ELEVAT.
4. NEW # EXTER, ADJAC, NOTED.
5. SEE A00# SERIES FOR ENLARGED PERIMETER PLANS. DIMENSIONS OF PERIMETER OMITTED FROM THIS DRAWING FOR CLARITY.

LEGEND
EXISTING SLAB, TO BE DEMO

SK#25
7 pages
11 Queries
Date: 07-14-2025

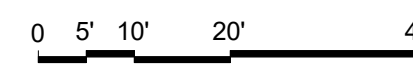

250 Maryland Avenue
250 MARYLAND AVENUE SW
WASHINGTON, DC 20024

**BEYER
BLINDER
BELLE**
307 M Street Northwest, Suite 301
Washington, DC, 20007
202 333 8000

MECHANICAL & PLUMBING
FIRST ENGINEERS
03-534-7872

ELECTRICAL
POWER DESIGN INC.
27-497-9811

STRUCTURAL
KATHGEHR GOSS ASSOCIATES
01-590-0071


IVIL
GORDON DC
02-869-1600

LANDSCAPE
IVS
02-546-7575

INTERIORS
TGYSDDG
12-274-0707

LIGHTING
M KLING + ASSOCIATES
03-684-6270

KEY PLAN

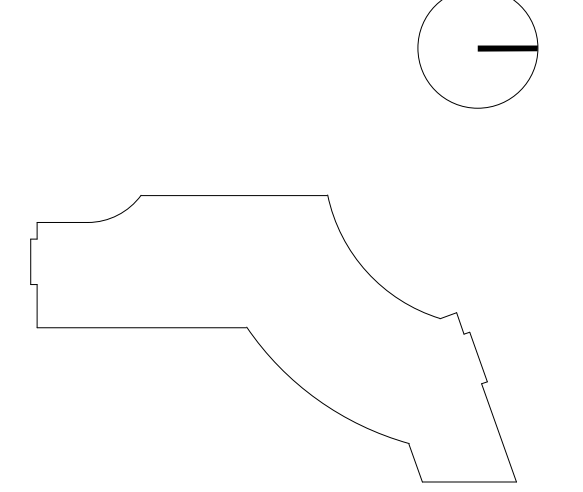

TAMP

NO	DATE	DESCRIPTION
4	6/6/25	ISSUED FOR CONSTRUCTION

REVISIONS

SUBMITTAL


ISSUED FOR
CONSTRUCTION

DRAWING TITLE


ENLARGED SLAB EDGE PLANS

SCALE	1/4" = 1'-0"
DATE	05/16/25
PROJECT NUMBER	6415.00
DRAWING NUMBER	

of

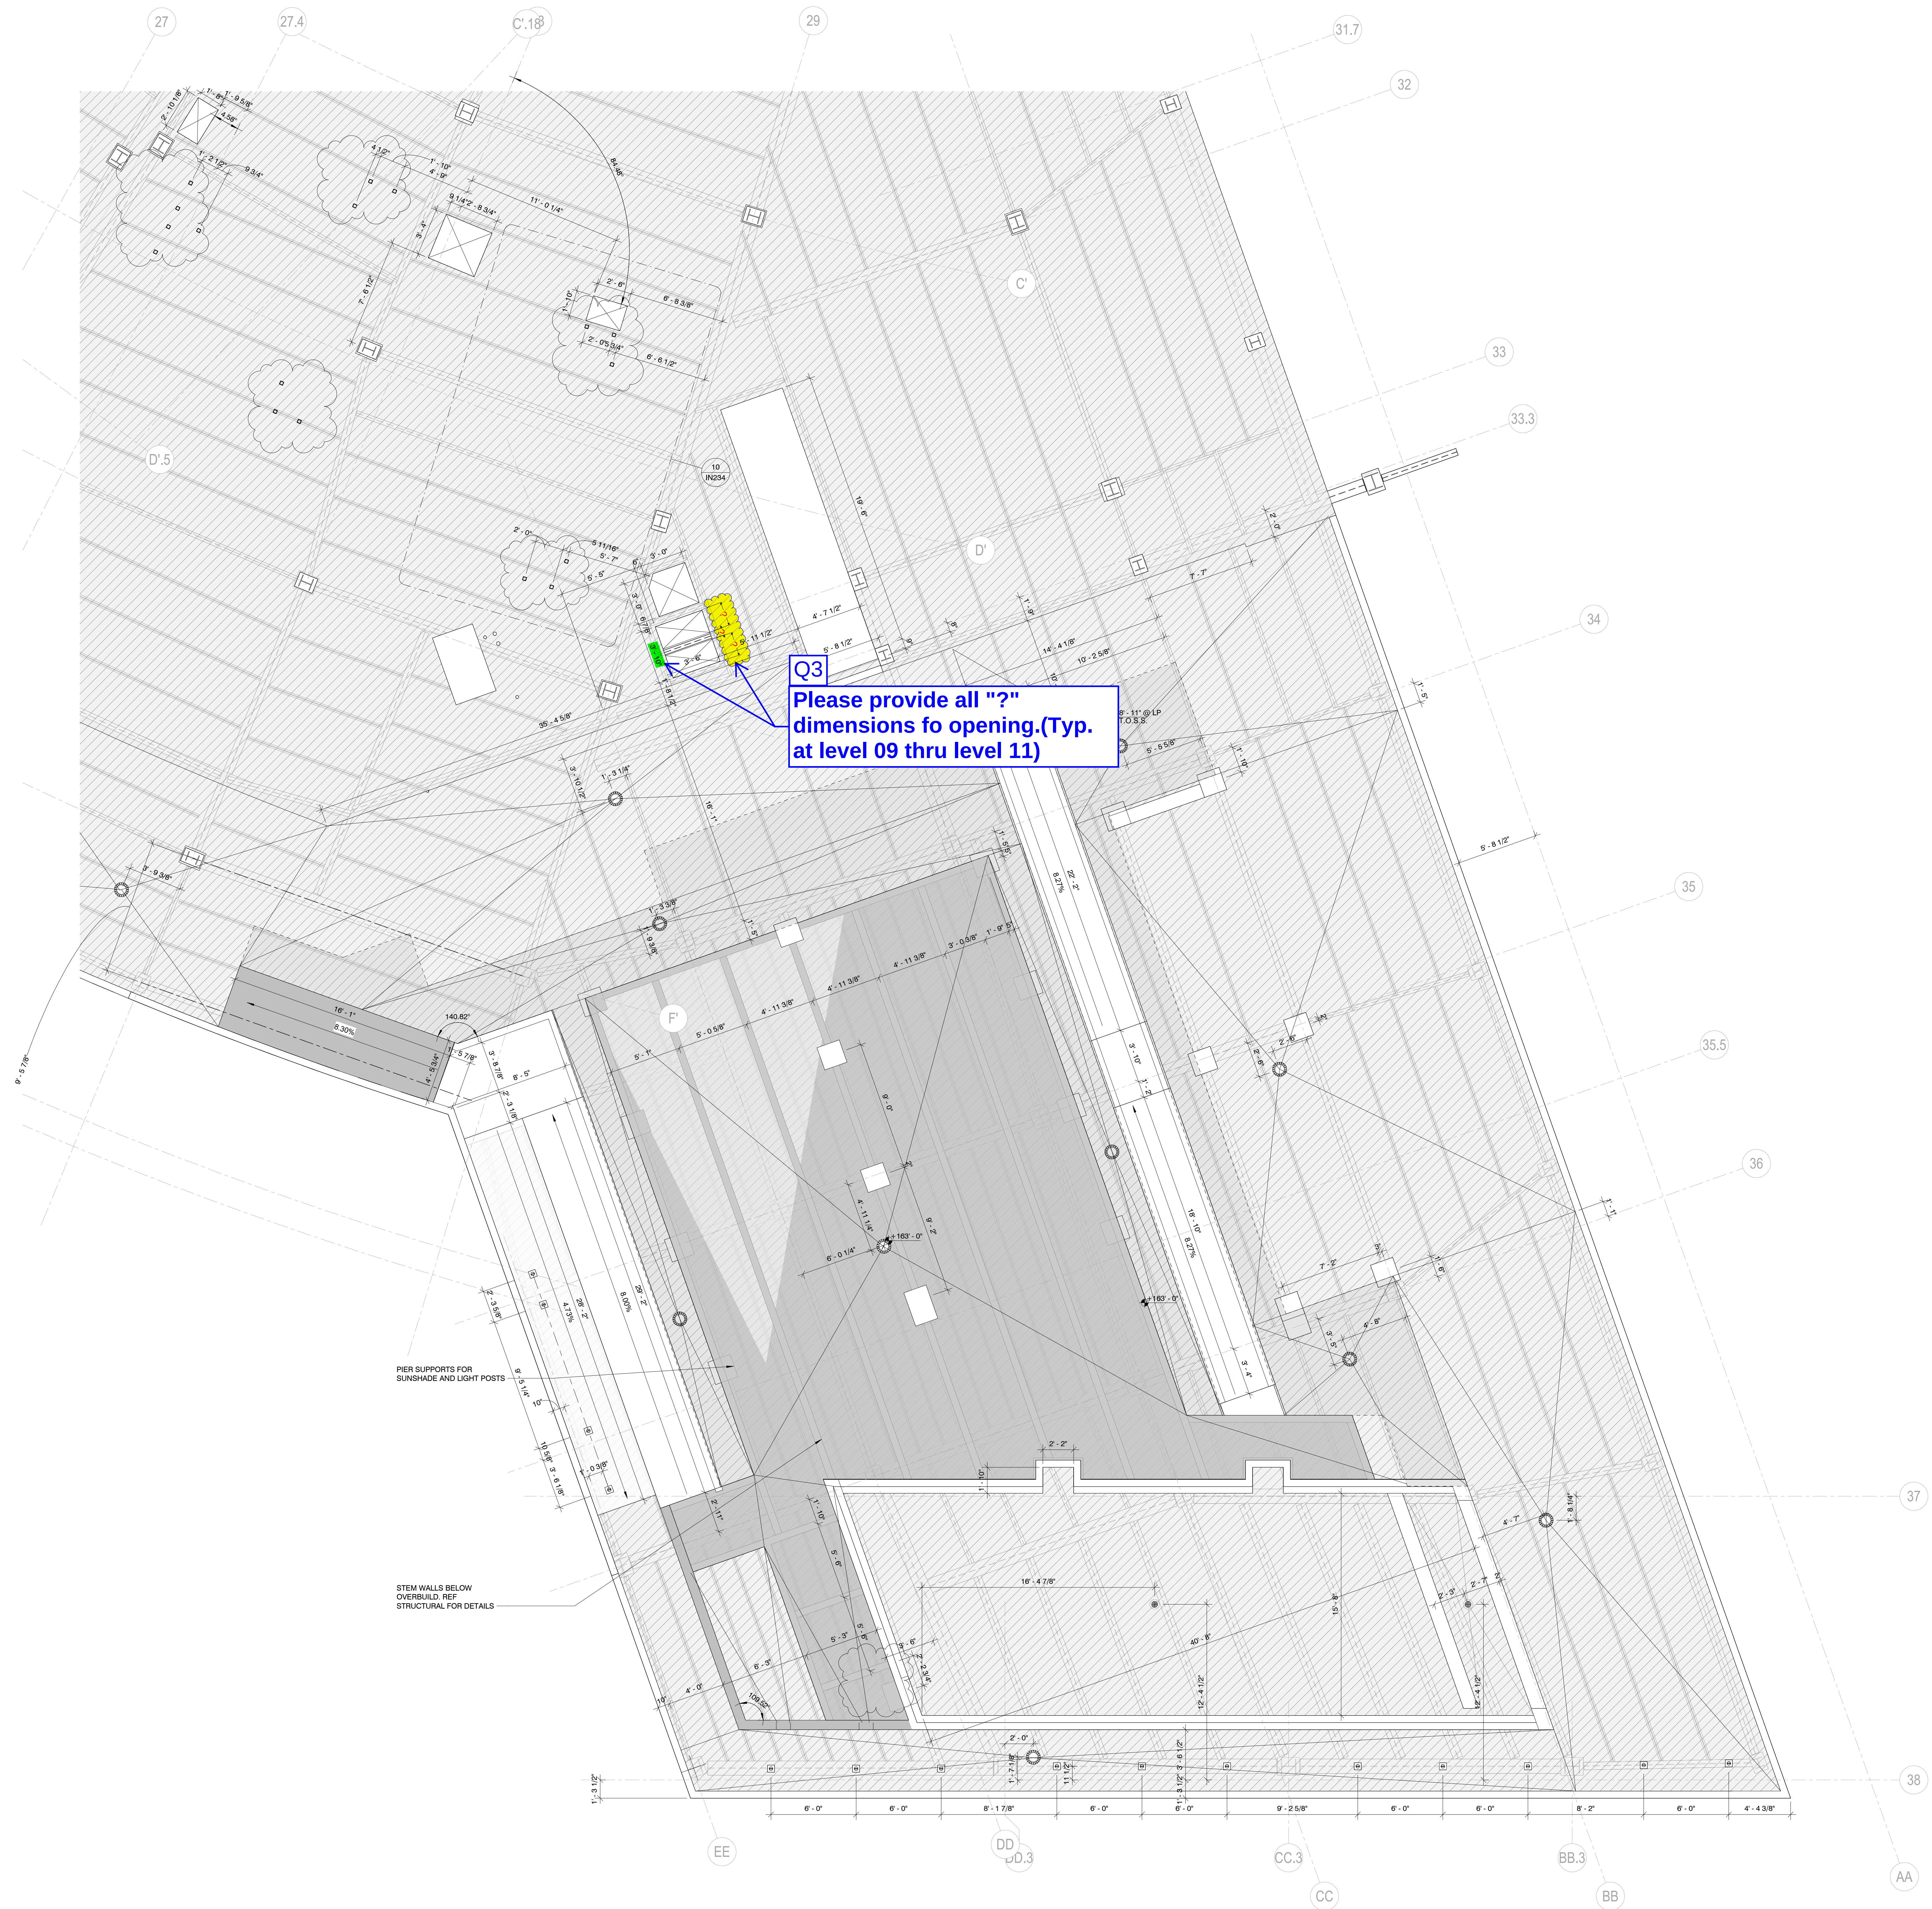

1 SLAB EDGE - ENLARGED PLAN LEVEL 11
A071 1/4" = 1'-0"

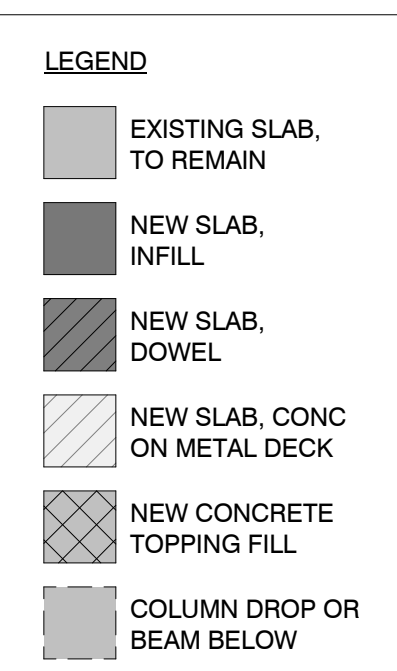

Snap from Arch. drawing 8/A073

1250 Maryland Avenue

1250 MARYLAND AVENUE SW
WASHINGTON, DC 20024BEYER
BLINDER
BELLE3307 M Street Northwest, Suite 301
Washington, DC 20007
202 333 8000MECHANICAL & PLUMBING
HURST ENGINEERS
703-534-7872ELECTRICAL
POWER DESIGN INC.
727-497-9811STRUCTURAL
RATHGEBER GOSS ASSOCIATES
301-590-0071CIVIL
GORDON DC
202-869-1600LANDSCAPE
OVS
202-546-7575INTERIORS
KTOY SIDG
312-274-0707LIGHTING
CM KLING + ASSOCIATES
703-684-6270

KEY PLAN

STAMP

4 6/6/25 ISSUED FOR CONSTRUCTION
2 2/4/25 ADDENDUM 02
NO DATE DESCRIPTION

REVISIONS

SUBMITTAL


ISSUED FOR
CONSTRUCTION

DRAWING TITLE

SLAB EDGE - LEVEL 09 TO
10SCALE As indicated
DATE 05/16/25
PROJECT NUMBER 6415.00
DRAWING NUMBER

A057

of

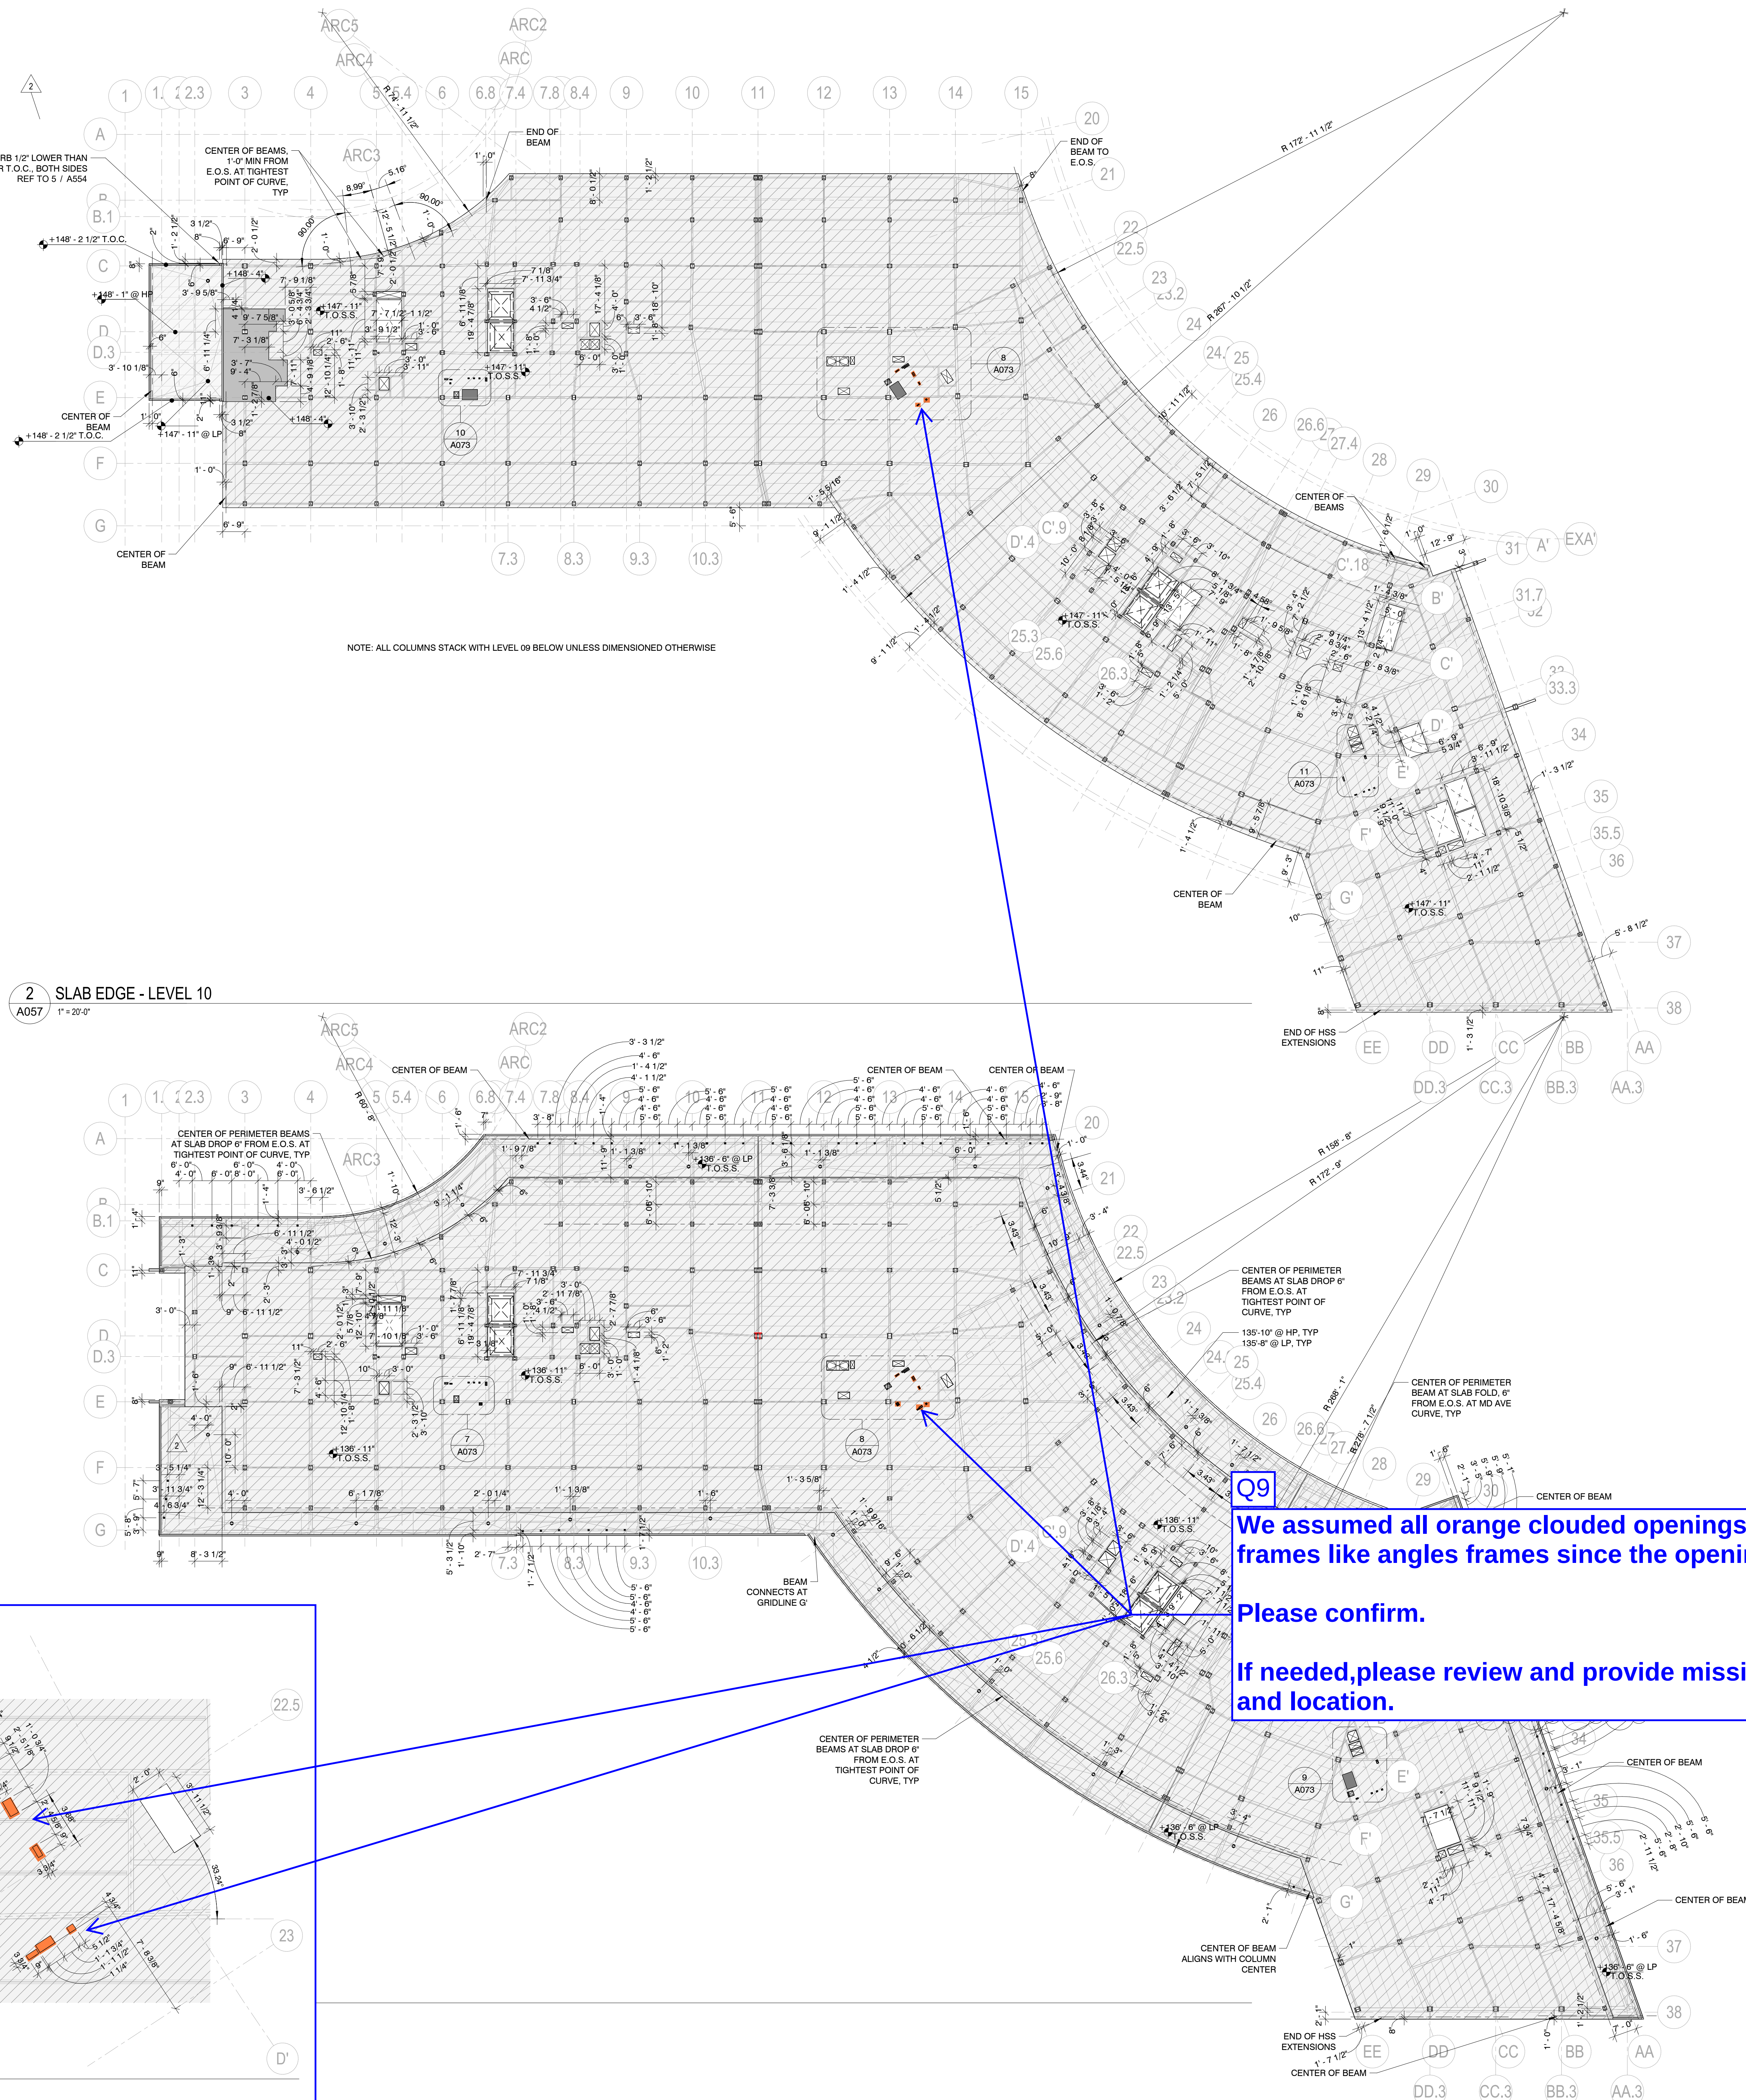

We assumed all orange clouded openings will NOT required support frames like angles frames since the opening sizes are small (less than 1-2).

Please confirm.

If needed, please review and provide missing dimension for opening size and location.

1. SEE STRUCTURAL DRAWINGS FOR STEEL SIZING & LOCATIONS BELOW
2. NEW STEEL COLUMNS ALIGNED W/ EXISTING CONCRETE COLUMNS BELOW UNLESS NOTED OTHERWISE. DIMENSIONS PROVIDED FOR COLUMNS NOT ALIGNED W/ BELOW.
3. SEE STRUCTURAL DRAWINGS FOR STEEL COLUMN SIZING & SHAPE. RECTANGULAR GRAPHIC SHOWN IN ARCHITECTURAL PLANS ALSO REPRESENTS GYPSUM FURRING NEEDED FOR RATING.

ADDED WITH COLUMN BELOW
NEW STEEL COLUMN
SUPPORTED BY BEAM
BELOW. SEE DIMENSIONS

- SLAB EDGE DRAWING NOTES:
1. SLAB DRAWINGS ARE BASED ON ORIGINAL EXISTING DRAWINGS. ALL LOCATIONS & DIMENSIONS TO BE VERIFIED IN FIELD. CONTRACTOR TO NOTIFY ARCHITECT OF ANY OPENINGS NOT SHOWN ON DRAWINGS. OPENINGS MAY REQUIRE INFILL.
 2. SEE DEMOLITION DRAWINGS FOR NEW OPENINGS. STRUCTURAL DEMOLITION, & SLAB EDGES THAT ARE TO BE CUT BACK.
 3. SEE ADDITIONAL NOTES ON DEMOLITION DRAWINGS FOR ELEVATOR PITS IN PARKING GARAGE.
 4. NEW INFILLS AT OPENINGS & SLAB EXTENSIONS ARE TO MATCH ADJACENT SLAB LEVEL UNLESS NOTED OTHERWISE.
 5. SEE A00# SERIES FOR ENLARGED PERIMETER PLANS. DIMENSIONS OF PERIMETER OMITTED FROM THIS DRAWING FOR CLARITY.

LEGEND

- EXISTING SLAB, TO REMAIN
- NEW SLAB, INFILL
- NEW SLAB, DOVEL
- NEW SLAB, CONC ON METAL DECK
- NEW CONCRETE TOPPING FILL
- COLUMN DROP OR BEAM BELOW

2 SLAB EDGE - LEVEL 10

A057 1" = 20'-0"

8 ENLARGED SLAB EDGE - LEVEL 9-2 (LEVEL 10 SIM)

A073 1/4" = 1'-0"

Snap from Arch. drawing 8/A073

NOTE: IF THIS SHEET IS NOT 36" X 48", THEN IT IS NOT THE INTENDED SIZE. IN ALL CASES, REFER TO PROJECT DIMENSIONS.

1250 Maryland Avenue
1250 MARYLAND AVENUE SW
WASHINGTON, DC 20024

**BEYER
BLINDER
BELLE**

3307 M Street Northwest, Suite 301
Washington, DC 20007
202 333 8000

MECHANICAL & PLUMBING
HURST ENGINEERS
703-534-7872

ELECTRICAL
POWER DESIGN INC.
727-497-9811

STRUCTURAL
RATHGEBER GOSS ASSOCIATES
301-590-0071

CIVIL
GORDON DC
202-869-1600

LANDSCAPE
OVS
202-546-7575

INTERIORS
KTOY SIDGG
312-274-0707

LIGHTING
CM KLING + ASSOCIATES
703-684-6270

KEY PLAN



STAMP

**ISSUED FOR
CONSTRUCTION**

DRAWING TITLE
**SLAB EDGE - LEVEL 11 TO
ROOF**

SCALE As indicated
DATE 05/16/25
PROJECT NUMBER 6415.00
DRAWING NUMBER

A058

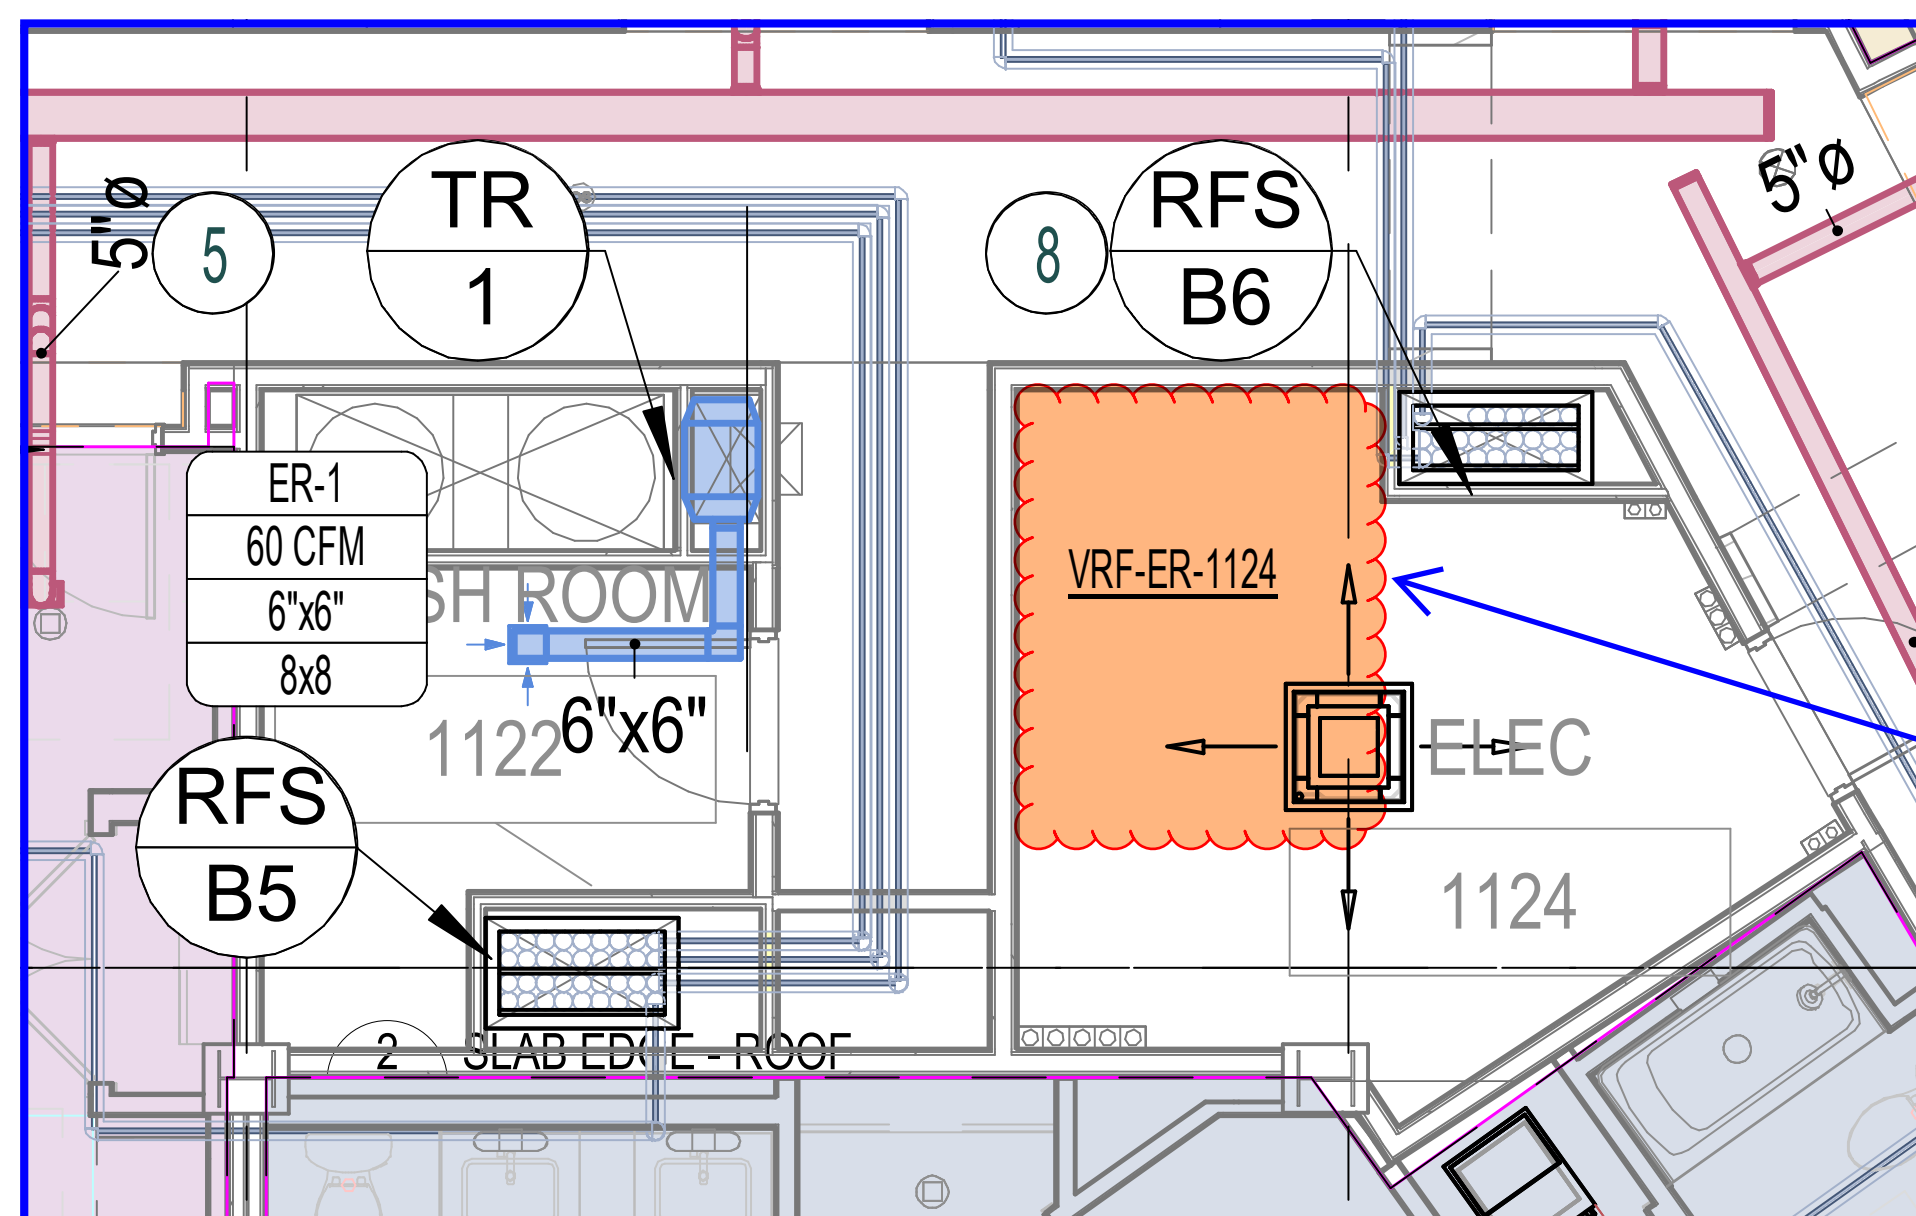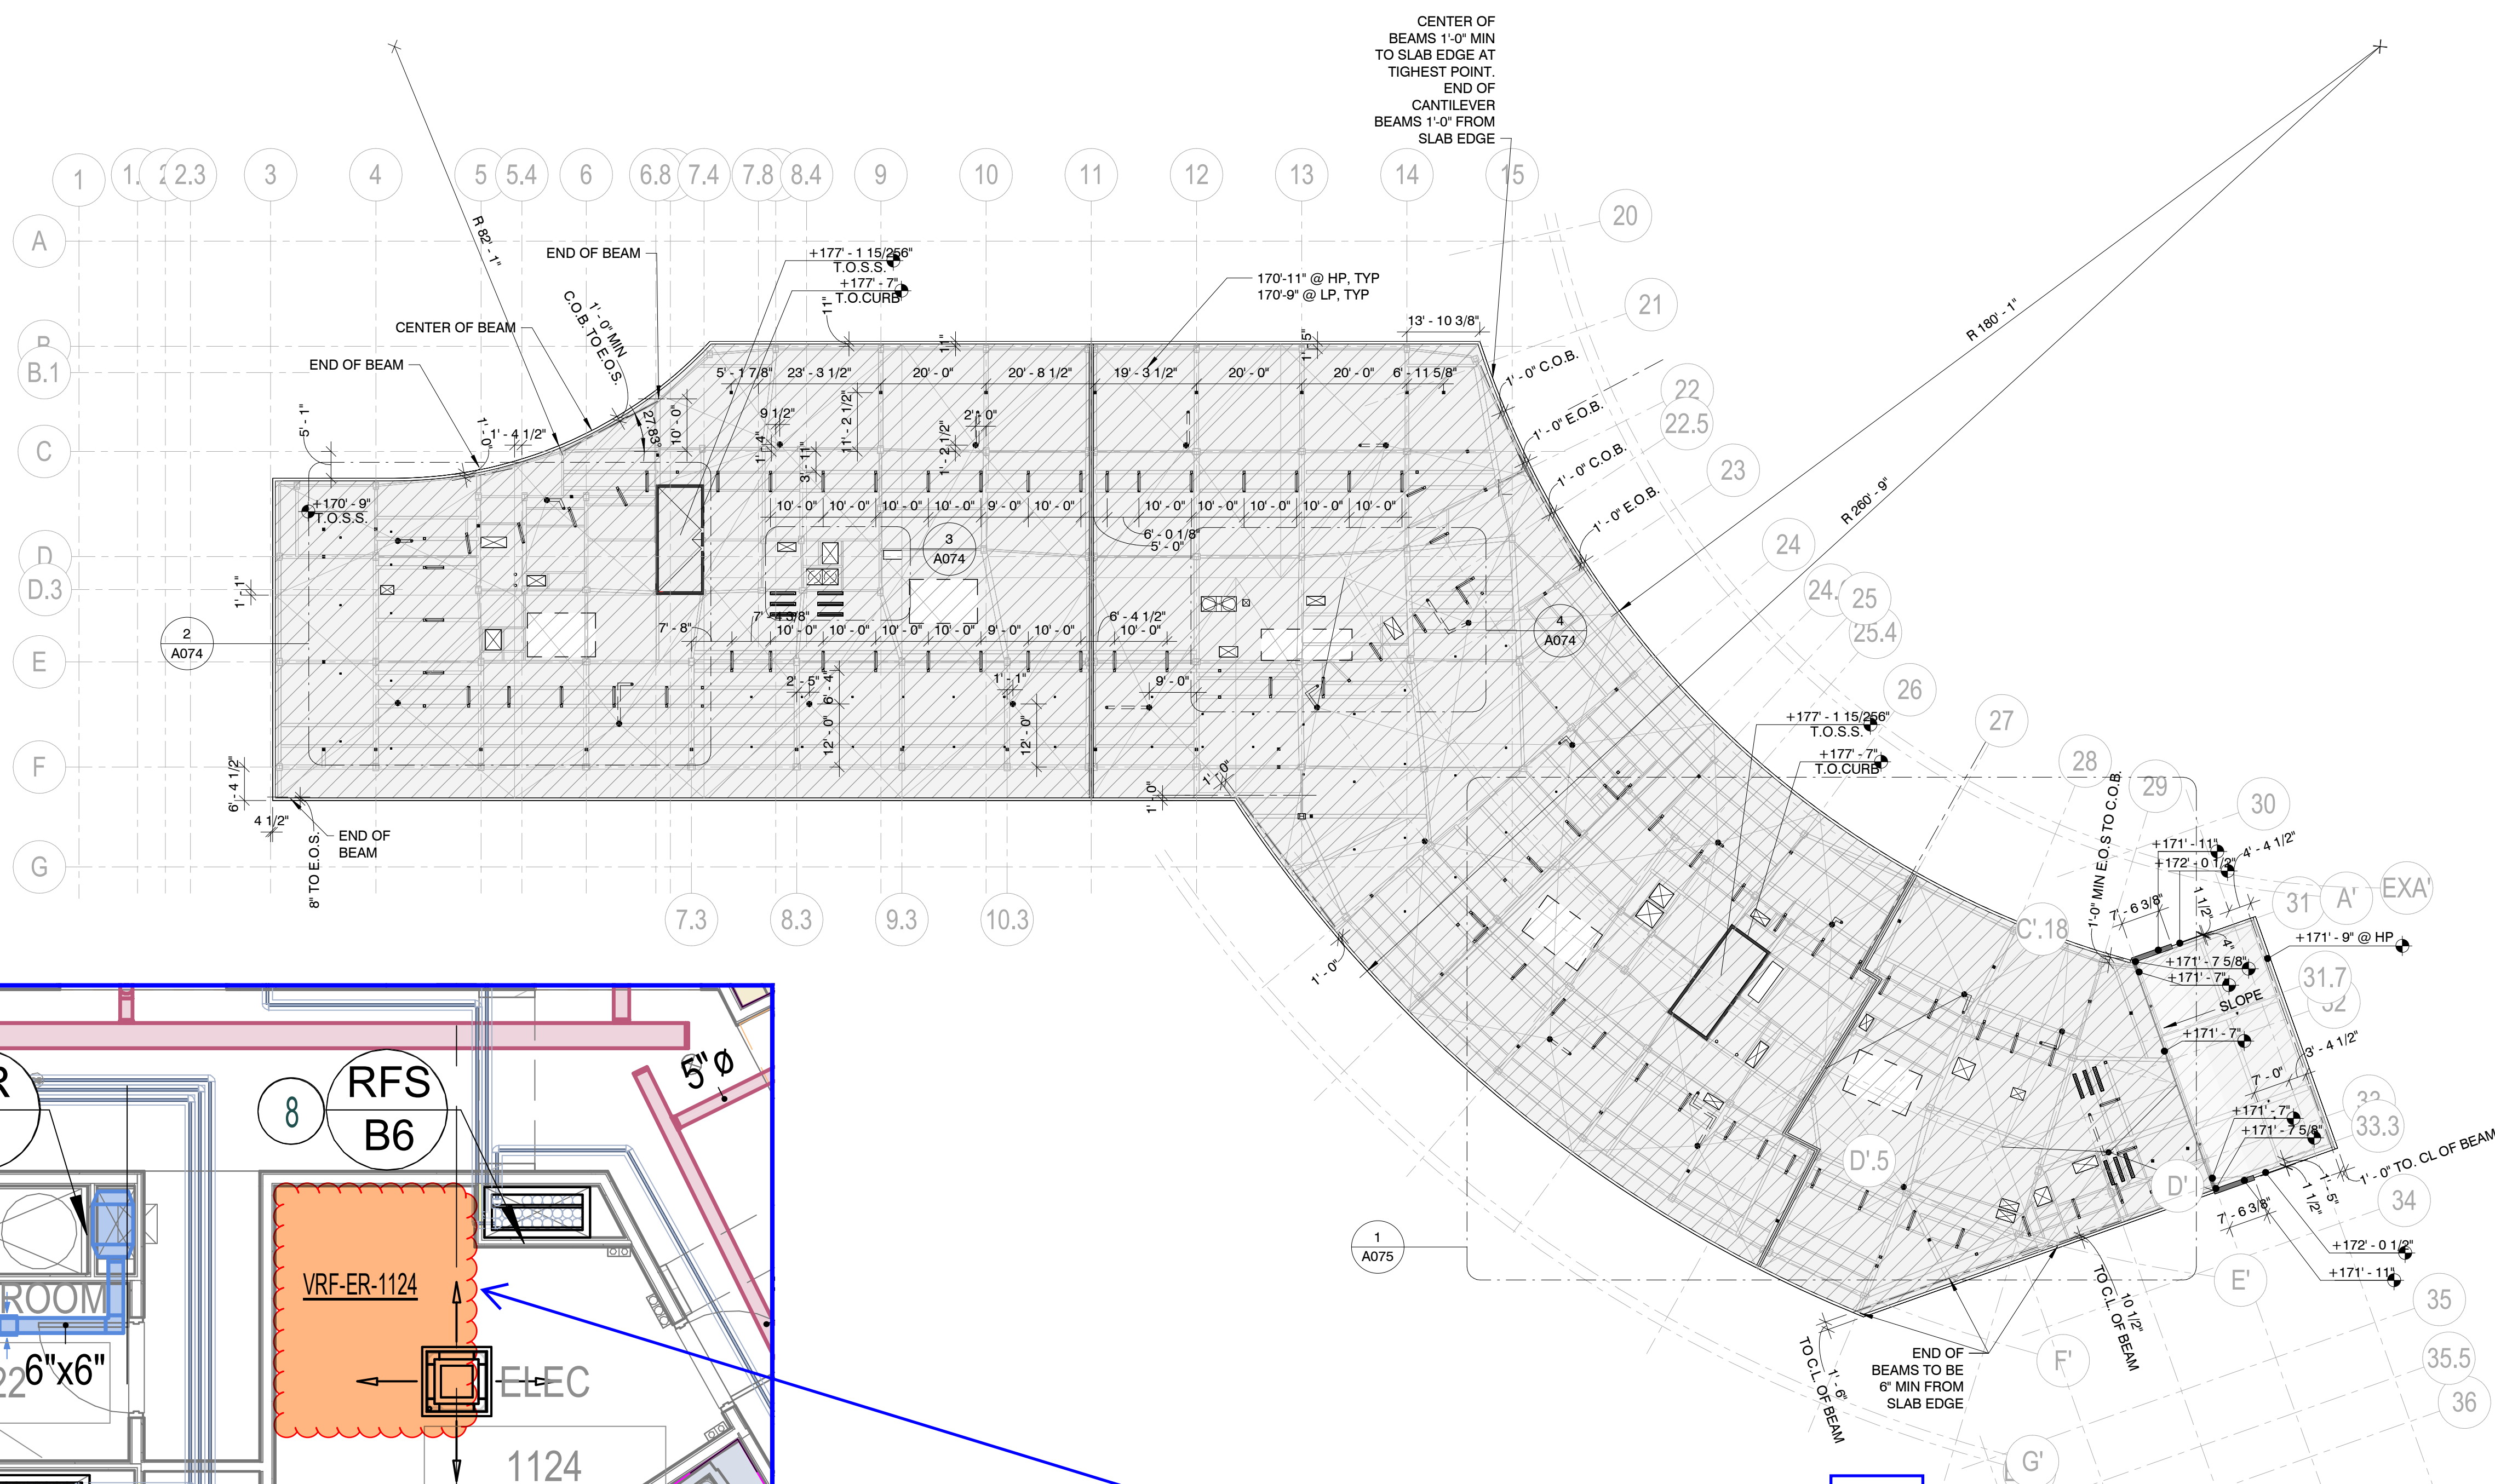


**Snap from Mech. drawing M116
LEVEL 11 MECHANICAL PLAN**

Q10

These yellow clouded openings are not shown in Mechanical drawings. Please review and advise if the opening are necessary?

If yes, the opening extends into the beam location for magenta clouded dimension. Please review and advise.

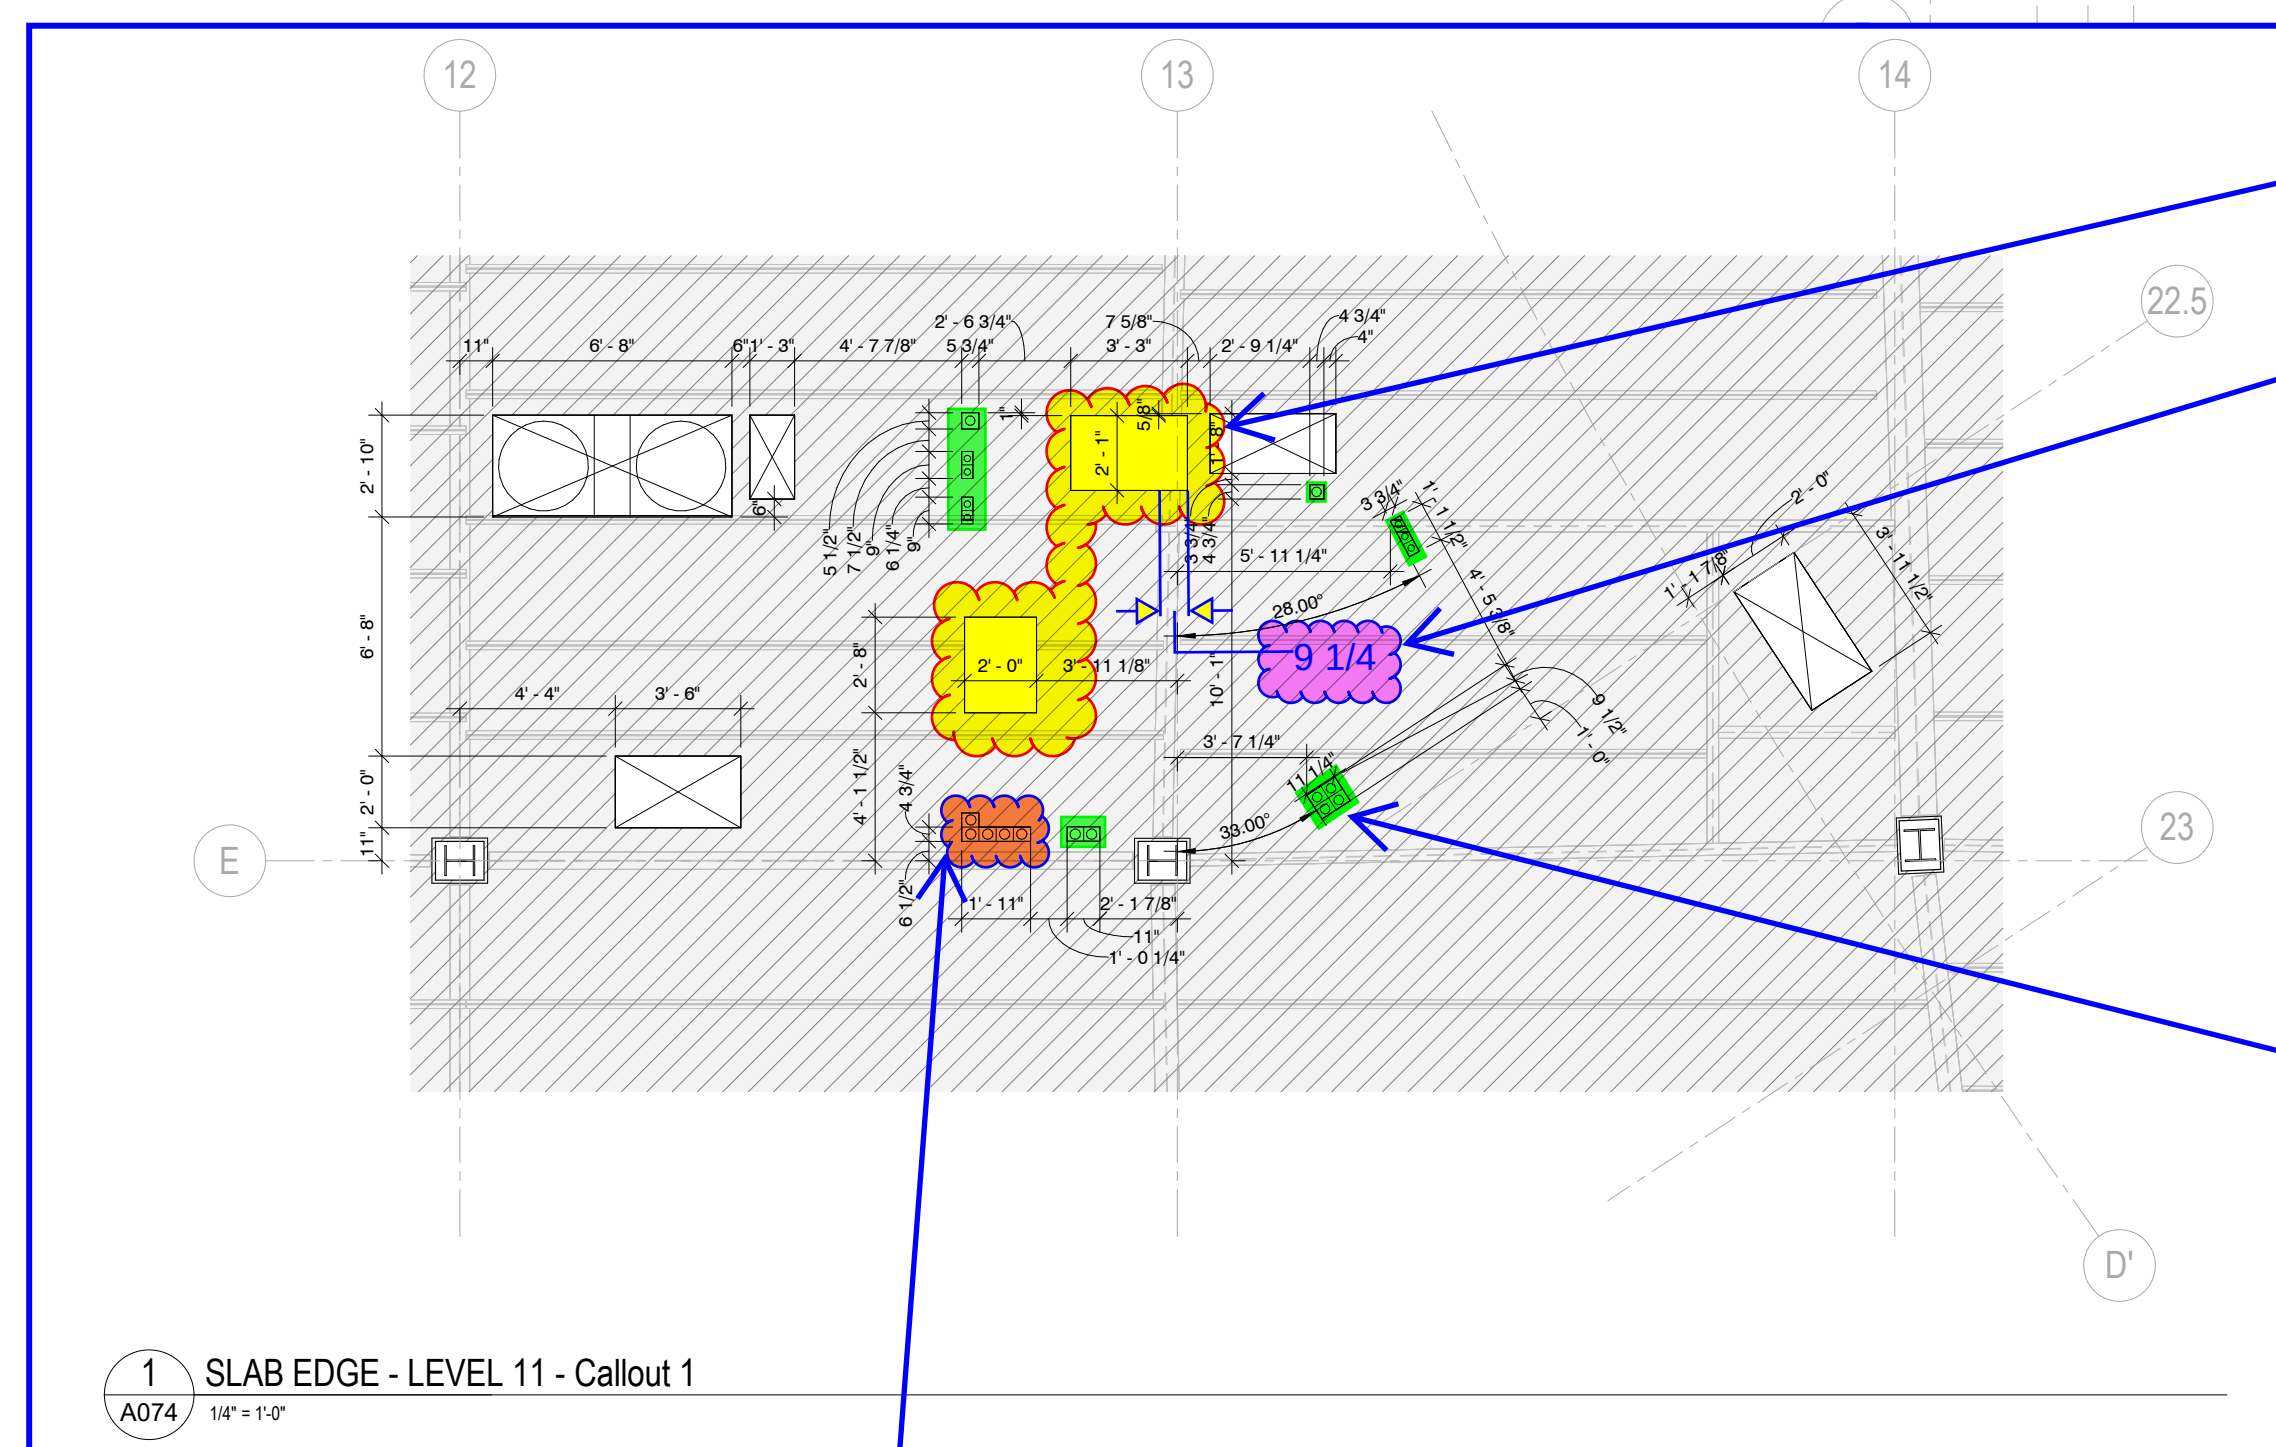

Snap from Arch. drawing 1/A074

Q12

We assumed the clouded openings will NOT required support frames like angles frames since the opening sizes are small.

Please confirm.

If needed, please review and provide missing dimension for opening size.

Q11

We assumed all green clouded openings will NOT required support frames like angles frames since the opening sizes are small (less than 1-2).

Please confirm.

If needed, please review and provide missing dimension for opening size and location.

NEW FLOOR STEEL STRUCTURE NOTES:

- SEE STRUCTURAL DRAWINGS FOR STEEL SIZING & LOCATIONS
- NEW STEEL COLUMNS ALIGNED W/ EXISTING CONCRETE COLUMNS BELOW UNLESS NOTED OTHERWISE. DIMENSIONS PROVIDED FOR COLUMNS NOT ALIGNED W/ BELOW.
- SEE STRUCTURAL DRAWINGS FOR STEEL COLUMN SIZING & SHAPE. RECTANGULAR GRAPHIC SHOWN IN ARCHITECTURAL PLANS ALSO REPRESENTS GYPSUM FURRING NEEDED FOR RATING.

LEGEND

- NEW STEEL COLUMN, ALIGNED WITH COLUMN BELOW
- NEW STEEL COLUMN, SUPPORTED BY BEAM BELOW, SEE DIMENSIONS

SLAB EDGE DRAWING NOTES:

- SLAB DRAWINGS ARE BASED ON ORIGINAL EXISTING DRAWINGS. ALL LOCATIONS & DIMENSIONS TO BE VERIFIED IN FIELD. CONTRACTOR TO NOTIFY ARCHITECT OF ANY OPENINGS NOT SHOWN ON DRAWINGS. OPENINGS MAY REQUIRE INFILL.
- SEE DEMOLITION DRAWINGS FOR NEW OPENINGS. STRUCTURAL DEMOLITION, & SLAB EDGES THAT ARE TO BE CUT BACK.
- SEE ADDITIONAL NOTES ON DEMOLITION DRAWINGS FOR ELEVATOR PITTS IN PARKING GARAGE.
- NEW INFILLS AT OPENINGS & SLAB EXTENSIONS ARE TO MATCH ADJACENT SLAB LEVEL UNLESS NOTED OTHERWISE.
- SEE A06# SERIES FOR ENLARGED PERIMETER PLANS. DIMENSIONS OF PERIMETER OMITTED FROM THIS DRAWING FOR CLARITY.

LEGEND

- EXISTING SLAB, TO REMAIN
- NEW SLAB, INFILL
- NEW SLAB, DOWEL
- NEW SLAB, CONC ON METAL DECK
- NEW CONCRETE TOPPING FILL
- COLUMN DROP OR BEAM BELOW

0 5' 10' 20' 40'

at

NOTE: IF THIS SHEET IS NOT 36" x 48", THEN IT IS NOT THE INTENDED SIZE. SMALL CANNOT BE USED FOR DIMENSIONS.