



BILL OF MATERIAL							
LINE #	QTY	PC	MARK	DESCRIPTION	LENGTH	REMARKS	WEIGHT
							ADVANCE
							MILL #
ONE	F-08.00C1	COLUMN					417
1	F-08.00C1	HSS6x6x3/8		11	9	SIZE A500C	323
1	bp1002	PL11/4x8		1	2	A36	40
1	p3065	PL11/4x7		1	10	A36	55
FIELD BOLTS							
2		3/4 Dia HILTI KWIK HUS-EZ		0	7	(3/4" EMBED)	
SCREW ANCHOR							
ONE	F-08.00C2	COLUMN					356
1	F-08.00C2	HSS6x6x3/8		9	4	SIZE A500C	256
1	p3065	PL11/4x7		1	10	A36	55
1	p1964	PL11/4x7		1	6	A36	45
FIELD BOLTS							
2		3/4 Dia HILTI HAS V-36		0	8	(3/4" EMBED)	
w/HILTI HY-200 EPOXY							
2		3/4 Dia HILTI KWIK HUS-EZ		0	7	(3/4" EMBED)	
SCREW ANCHOR							
B	ONE	F-08.00C3	COLUMN				396
1	F-08.00C3	HSS6x6x3/8		13	03/4	SIZE A500C	359
1	p3367	PL3/8x61/2		1	6	A36	21
1	p230	PL3/8x61/2		1	2	A36	16
FIELD BOLTS							
2		3/4 Dia HILTI HAS V-36		0	8	(4" EMBED)	
THREADED ROD							
w/ HILTI HY-200 EPOXY							
2		1/2 Dia HILTI KWIK HUS-EZ		0	41/2	(3/4" EMBED)	
SCREW ANCHOR							
ONE	F-08.00C4	COLUMN					354
1	F-08.00C4	HSS6x6x3/8		9	101/2	A500C	271
1	hss70	HSS4x4x3/16		1	63/4	A500C	23
1	hss69	HSS4x4x3/16		1	1	A500C	16
1	a155	L11/2x1x3/16		0	5	A36	1
1	p404	PL3/8x61/2		1	6	A36	21
1	p3367	PL3/8x61/2		1	6	A36	21
1	p3632	PL1/4x4		0	4	A36	1
FIELD BOLTS							
2		3/4 Dia HILTI KWIK HUS-EZ		0	41/2	(3/4" EMBED)	
SCREW ANCHOR							
ONE	F-08.00B1	BEAM					688
1	F-08.00B1	HSS10x8x1/2		12	17/8	A500C	677
2	p3657	PL1/4x8		0	10	A36	11

Total weight : 2211

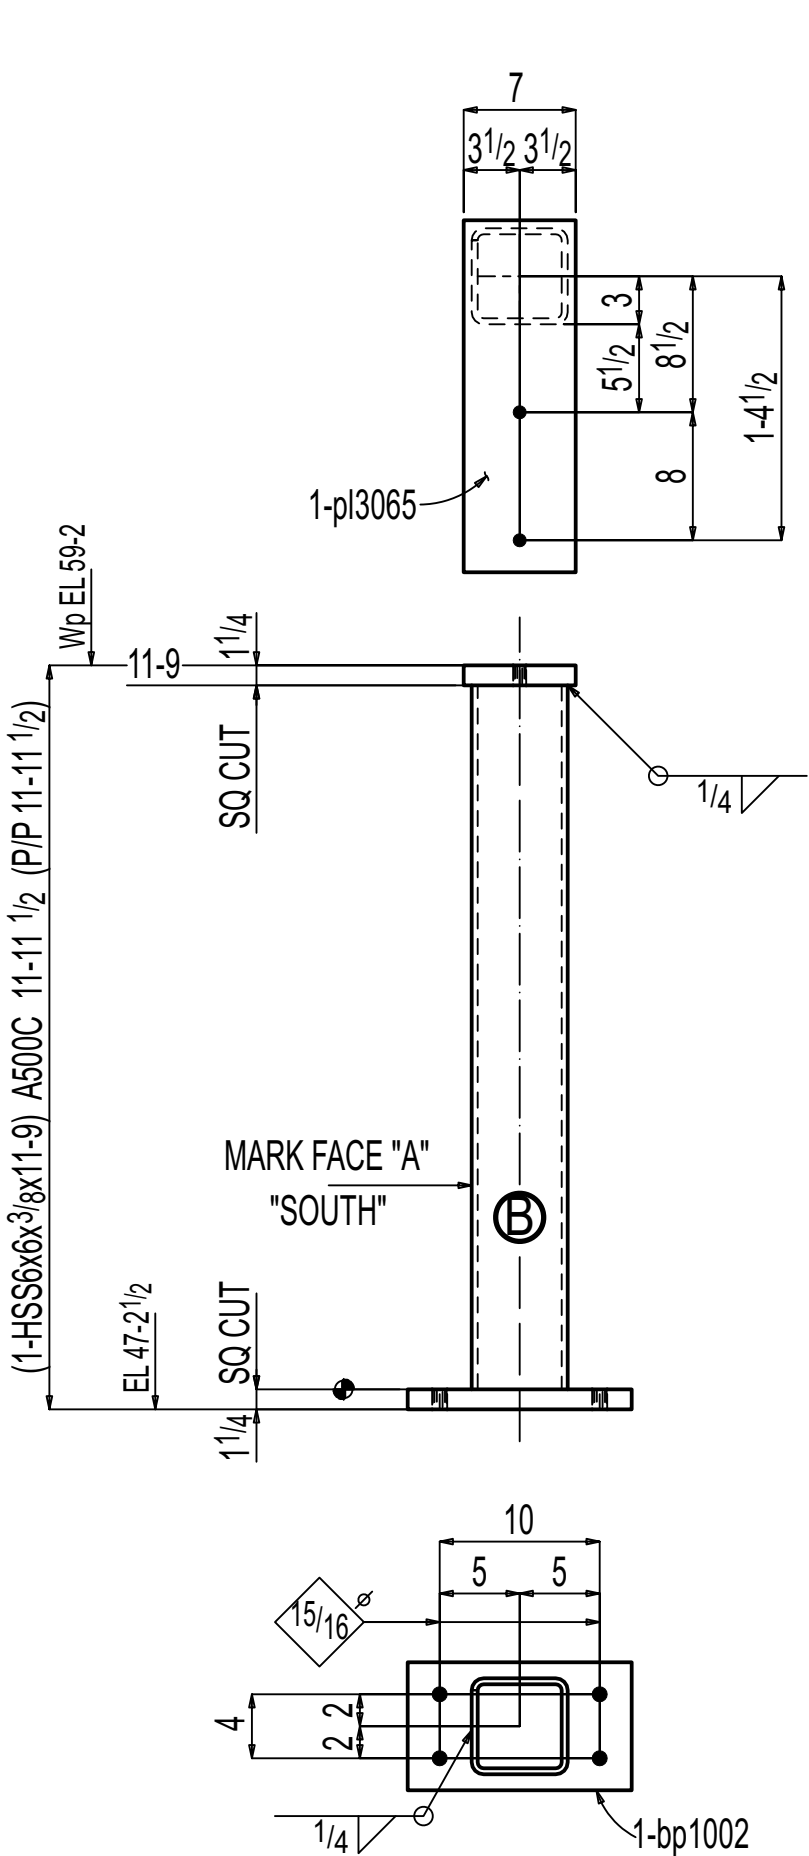


AT GRID:
EE & A

ONE COLUMN F-08.00C1

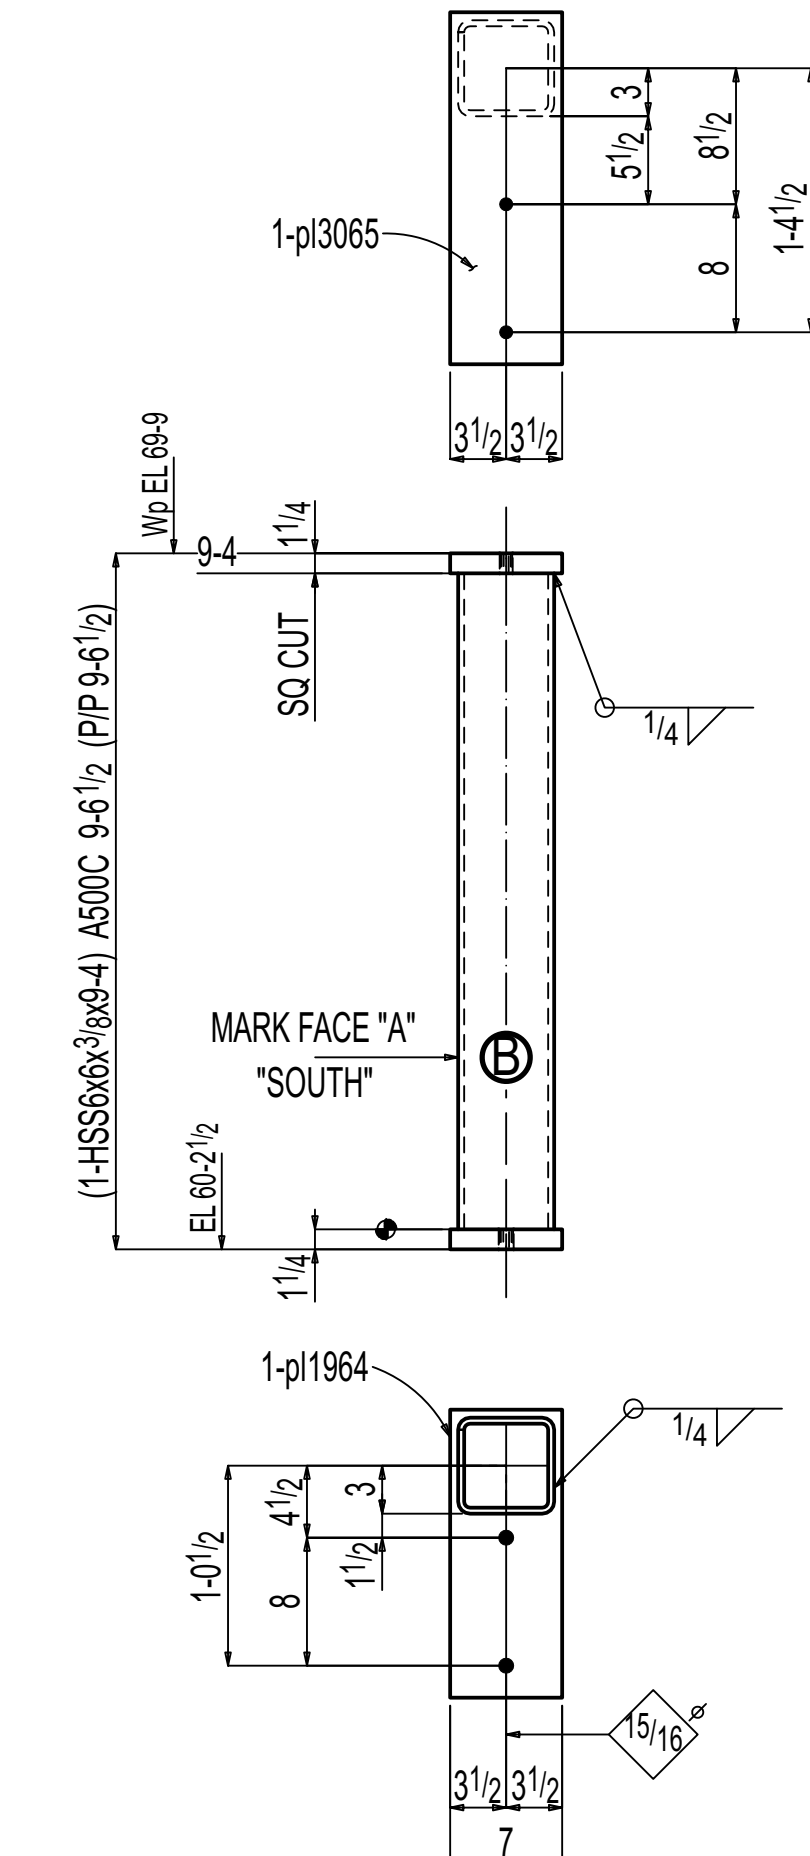


AT GRID:
EE & A

ONE COLUMN F-08.00C2

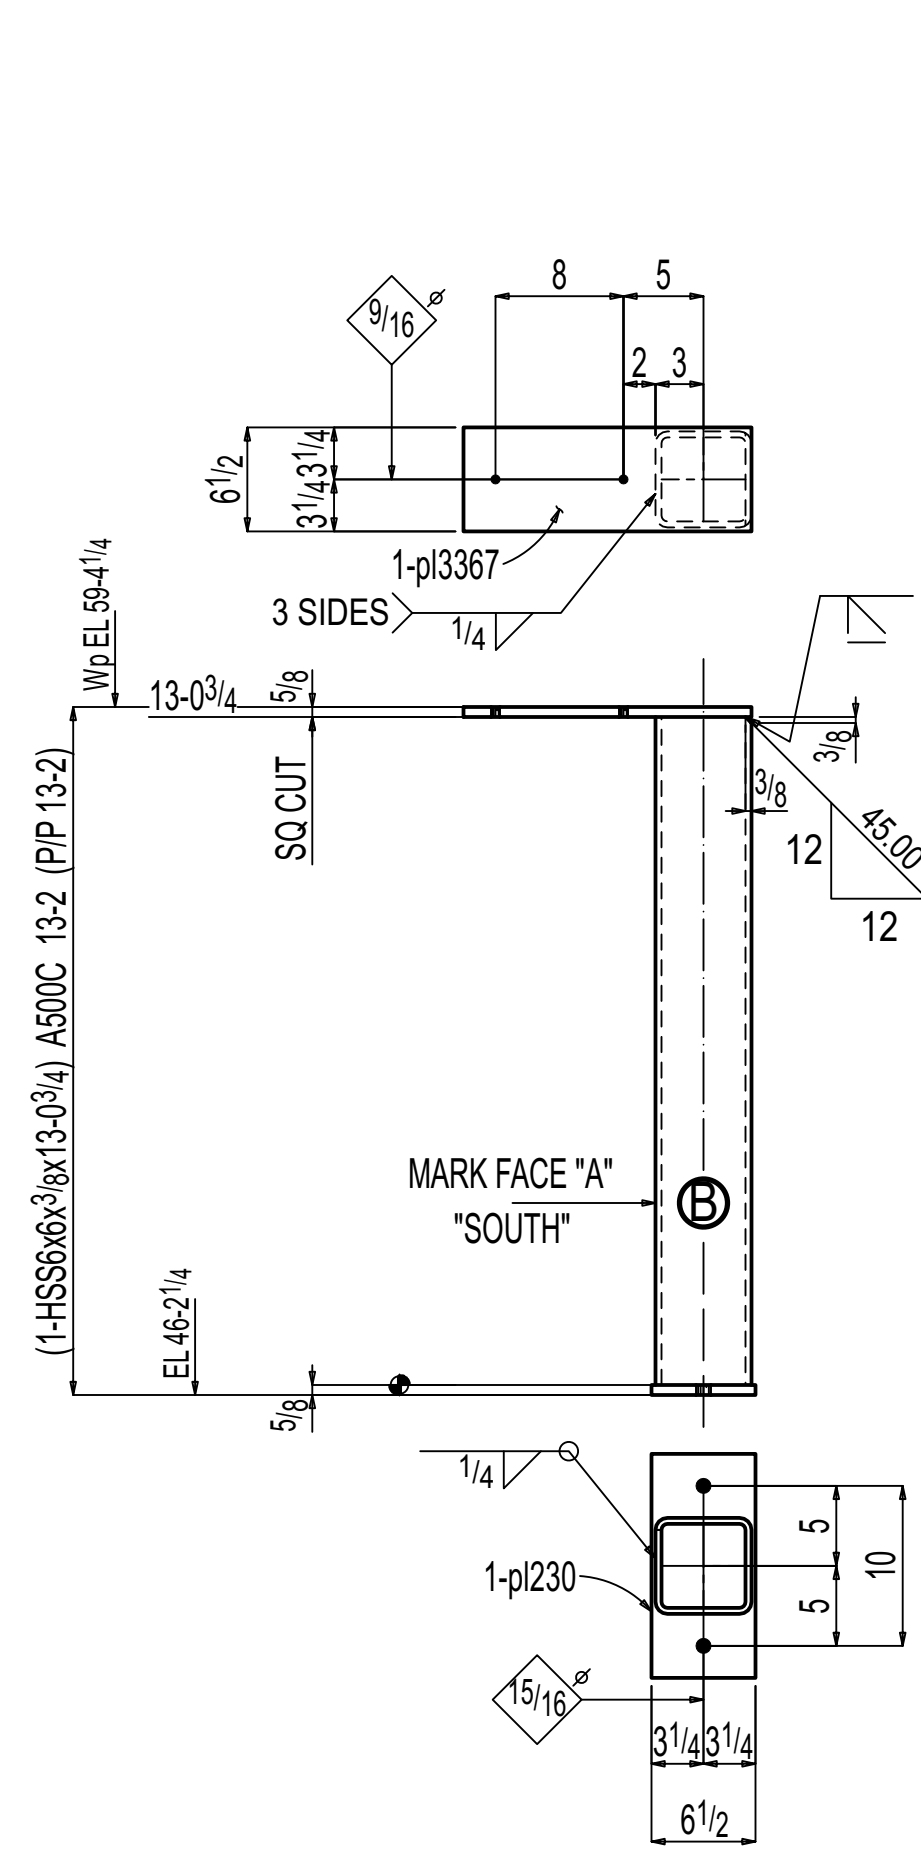


AT GRID:
AA & K

ONE COLUMN F-08.00C3

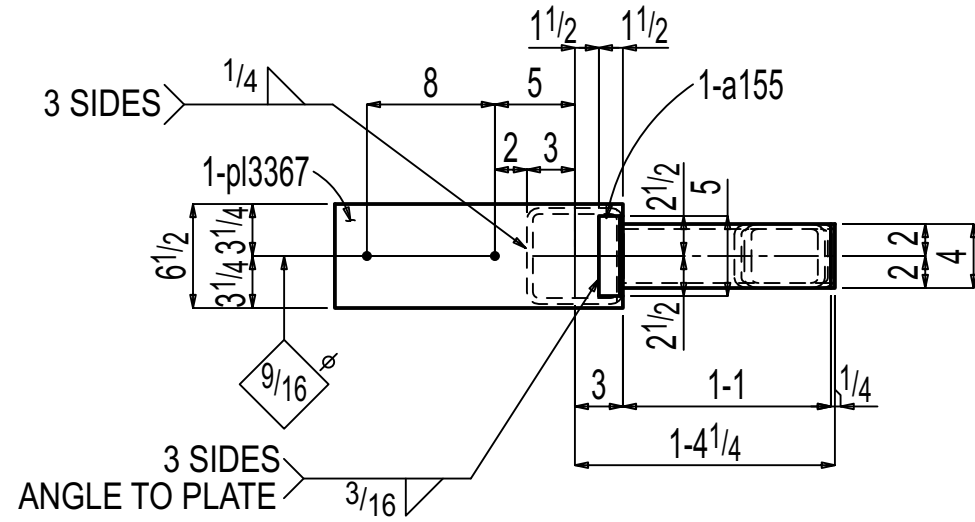

AT GRID:
AA & K

ONE COLUMN F-08.00C4

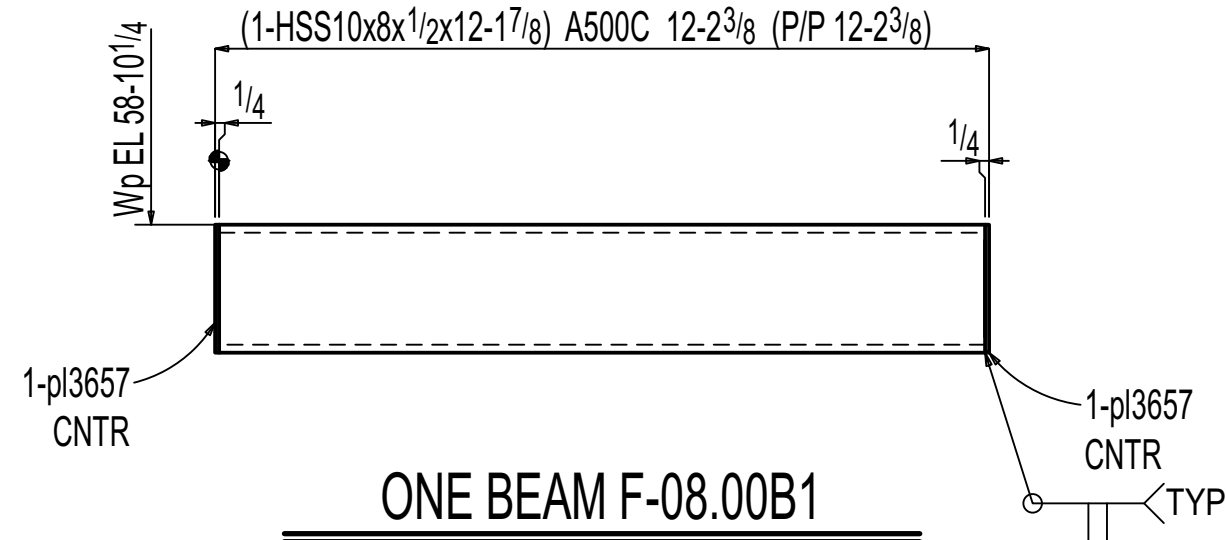

ONE BEAM F-08.00B1

PAINT :NO PAINT
PREPARATION :SSPC-SP3

General Notes

- *Structural steel shall conform to ASTM-A992.
- *Structural SQR/RND,tubing conform to ASTM A500 Grade C
- *Pipe shall conform to ASTM A53, Grade B.
- *Channels, Angles and plates shall conform to A36.
- *All bolts shall be 3/4" High strength in accordance with ASTM A325 (UNO)
- *Welding Electrodes for Carbon steel :E70xx

# of Copies	Revision/ Issue	Destination	Date
5	0	For Fabrication	11-03-2025
4	D	For Re-Approval	10-24-2025
3	C	For Re-Approval	09-19-2025
2	B	For Re-Approval	06-23-2025
1	A	For Approval	02-25-2025

IRON FABRICATION SERVICES, LLC.

3029 M. Street, NW, Suite 202
Washington, DC 20007
Tel: 202-800-5599
Fax: 202-478-0303

Project Name and Address

MARYLAND AVENUE

Location: **1250 MARYLAND AVENUE SW
WASHINGTON, DC 20024**

Contractor:

BALFOUR BEATTY

Approved for Fabrication by:	Signature
------------------------------	-----------

Contract #	224009	Drawing #	F-08.00
------------	---------------	-----------	----------------

Contract Item: **COLUMN ,BEAM**

Ref:

SOW - 08: E-08.00 - E-08.04

Date 01/ 23/ 2025	Drawing Title: COLUMN & BEAM DETAIL
Scale VARIES	

BILL OF MATERIAL							
LINE	QTY	PC		LENGTH		WEIGHT	ADVANCE
#	TOTAL	MARK	DESCRIPTION		REMARKS	TOTAL	MILL #
	ONE	F-08.01FR1	FRAME			248	
	1	F-08.01FR1	HSS6x6x9/16	3	53/4	A500C	81
	1	w2762	W8x31	1	4	A992	41
	1	p403	PL1/2x16	4	6	A36	123
	1	p685	PL1/4x6	0	6	A36	3
	ONE	F-08.01FR2	FRAME			296	
	1	F-08.01FR2	HSS6x6x9/16	3	73/4	A500C	85
	1	hss3616	HSS6x6x9/16	1	103/4	A500C	44
	1	hss3605	HSS6x6x9/16	1	77/8	A500C	39
	1	p403	PL1/2x16	4	6	A36	123
	2	p685	PL1/4x6	0	6	A36	5
	ONE	F-08.01FR3	FRAME			515	
	1	F-08.01FR3	HSS6x6x9/16	3	73/4	A500C	85
	1	hss284	HSS6x6x9/16	6	81/8	A500C	156
	1	hss288	HSS6x6x9/16	6	33/16	A500C	146
	1	p403	PL1/2x16	4	6	A36	123
	1	p3187	PL1/4x6	0	77/16	A36	3
	1	p685	PL1/4x6	0	6	A36	3
	ONE	F-08.01FR4	FRAME			641	
	1	F-08.01FR4	HSS6x6x9/16	3	73/4	A500C	85
	1	hss3982	HSS6x6x9/16	2	511/16	A500C	58
	1	hss3981	HSS6x6x9/16	2	3	A500C	53
	1	p410	PL3/4x15	11	6	A36	440
	2	p685	PL1/4x6	0	6	A36	5

Total weight : 1699



PAINT	:NO PAINT
PREPARATION	:SSPC-SP3

- *Structural steel shall conform to ASTM-A992.
- *Structural SQR/RND.tubing conform to ASTM A500 Grade C
- *Pipe shall conform to ASTM A53, Grade B.
- *Channels, Angles and plates shall conform to A36.
- *All bolts shall be 3/4" High strength in accordance with ASTM A325 (UNO)
- *Welding Electrodes for Carbon steel :E70xx

5	0	For Fabrication	11-03-2025
4	D	For Re-Approval	10-24-2025
3	C	For Re-Approval	09-19-2025
2	B	For Re-Approval	06-24-2025
1	A	For Approval	02-25-2025
# of Copies	Revision/ Issue	Destination	Date

3029 M. Street, NW, Suite 202
Washington, DC 20007
Tel: 202-800-5599
Fax: 202-478-0303

Location: **1250 MARYLAND AVENUE SW**
WASHINGTON, DC 20024

Approved for Fabrication by:	Signature
------------------------------	-----------

Contract # 224009	Drawing # F-08.01
--------------------------	--------------------------


Ref:

SOW - 08: E-08.00 - E-08.04


Date 01/ 23/ 2025	Drawing Title: FRAME DETAIL
Scale VARIES	

BILL OF MATERIAL								
LINE #	QTY	PC MARK	DESCRIPTION	LENGTH		REMARKS	WEIGHT TOTAL	ADVANCE MILL #
	ONE	F-08.02LP1	LEVELING PLATE				9	
	1	F-08.02LP1	PL 1/4x7	1	6	A36	9	
	ONE	F-08.02LP2	LEVELING PLATE				6	
	1	F-08.02LP2	PL 1/4x6 1/2	1	2	A36	6	
	ONE	F-08.02LP3	LEVELING PLATE				8	
	1	F-08.02LP3	PL 1/4x8	1	2	A36	8	
	ONE	F-08.02LP4	LEVELING PLATE				8	
	1	F-08.02LP4	PL 1/4x6 1/2	1	6	A36	8	
	ONE	F-08.02M1	HSS				54	
	1	F-08.02M1	HSS 7/8x1 1/2	1	1 1/2	A500C	47	
	2	p3667	PL 1/4x7	0	7	A36	7	
	ONE	F-08.02M2	SHIM PLATE				13	
	1	F-08.02M2	PL 1/2x7	1	1 1/2	A36	13	
	ONE	F-08.02M3	PLATE				37	
	1	F-08.02M3	PL 3/4x6	1	3	A36	19	
	2	p3659	PL 3/4x6	0	7	A36	18	
	8	F-08.02M4	THREADED ROD				12	
	8	F-08.02M4	1" Ø FULLY THREADED ROD w/ HILTI HIT-HY 200 V3 ADHESIVE	0	6 1/2	F1554 GR. 55	12	
	8		1 NUT			HHNT A563		
	8		1 WASHER			HD F436		
	4	F-08.02M5	THREADED ROD				5	
	4	F-08.02M5	3/4" Ø THREADED ROD w/ HILTI HY-200 ADHESIVE	0	9	F1554 GR. 55	5	
	4		3/4 NUT			HHNT A563		
	4		3/4 WASHER			HD F436		
	24	F-08.02M6	THREADED ROD				166	
	24	F-08.02M6	1" Ø THREADED ROD	2	7	F1554 GR. 55	166	
	48		1 NUT			HHNT A563		
	48		1 WASHER			HD F436		
	16	F-08.02M7	THREADED ROD				30	
	16	F-08.02M7	1" Ø THREADED ROD w/ HILTI HIT-HY 200 V3 ADHESIVE	0	8 1/2	F1554 GR. 55	30	
	16		1 NUT			HHNT A563		
	16		1 WASHER			HD F436		
	2	F-08.02M8	THREADED ROD				1	
	2	F-08.02M8	1/2" Ø THREADED ROD w/HILTI HY 200 V3 ADHESIVE	0	6	F1554 GR. 55	1	
	2		1/2 NUT			HHNT A563		
	ONE	F-08.02M9	HSS				208	
	1	F-08.02M9	HSS 5 1/2x5 1/2x5 1/16	9	7 1/2	A500C	204	
	2	p407	PL 1/4x5 1/2	0	5 1/2	A36	4	


Total weight : 557

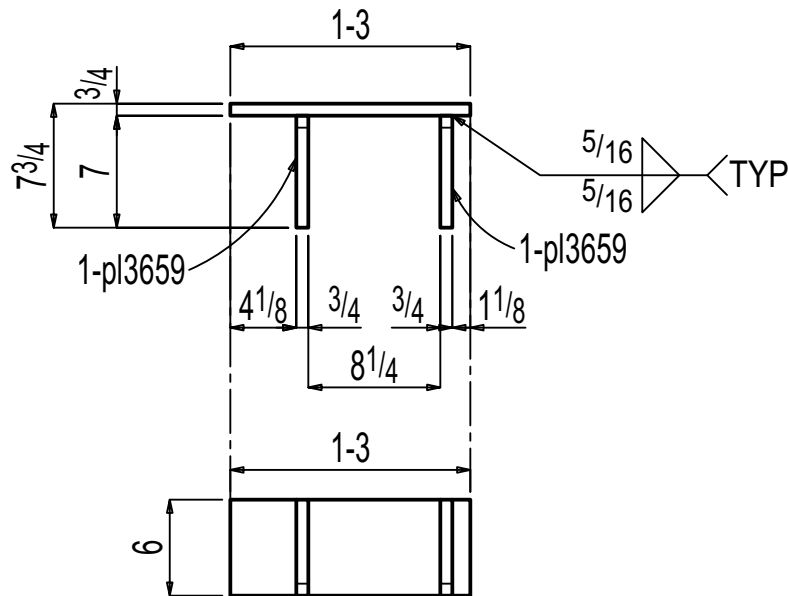


ONE PLATE F-08.02M3

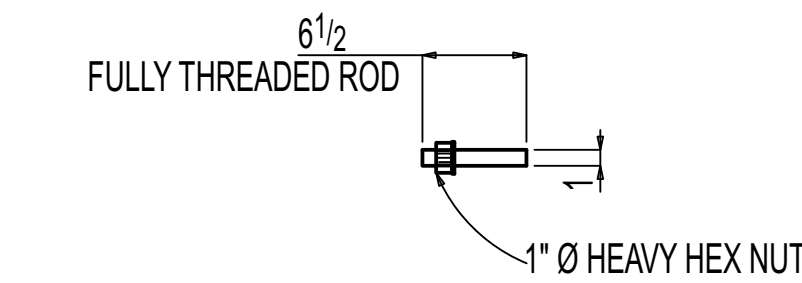


8 THREADED RODS F-08.02M4

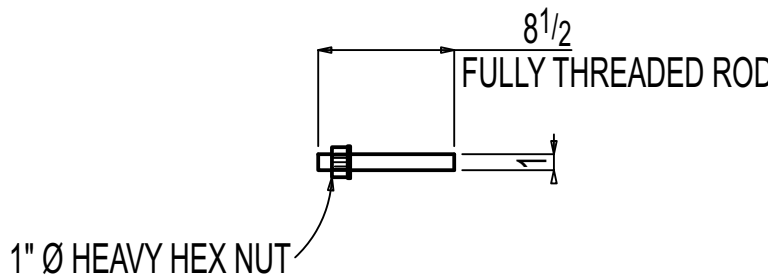


16 THREADED RODS F-08.02M7

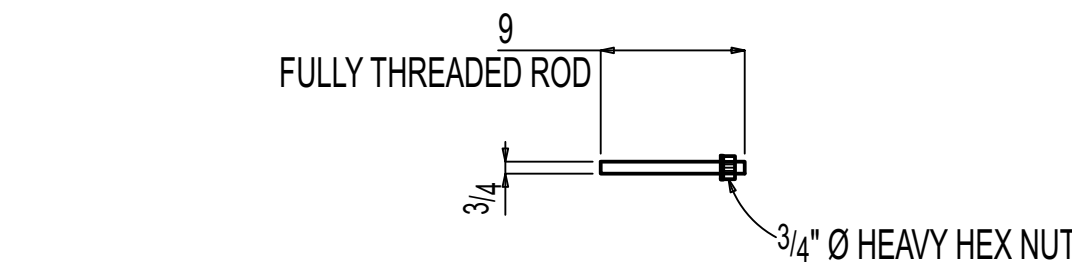


4 THREADED RODS F-08.02M5

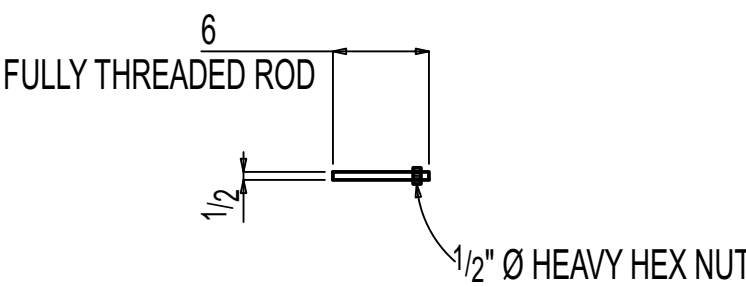


2 THREADED RODS F-08.02M8

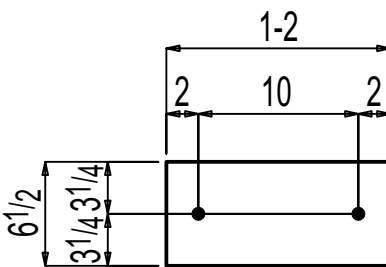


ONE LEVELING PLATE F-08.02LP2

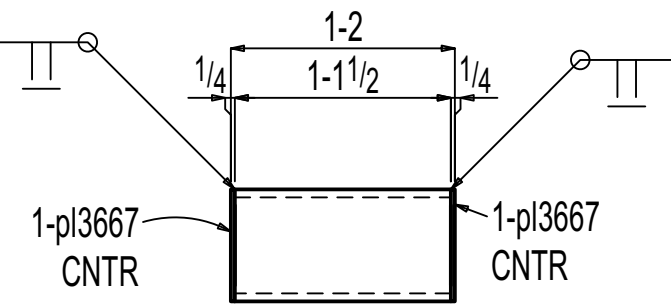


ONE HSS F-08.02M1

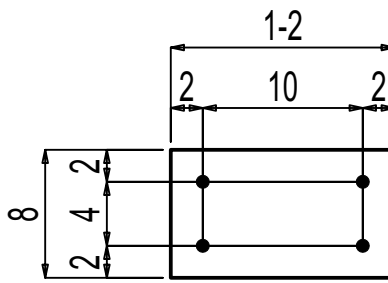


ONE LEVELING PLATE F-08.02LP3

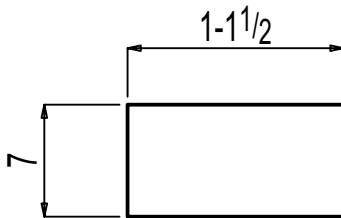

ONE SHIM PLATE F-08.02M2

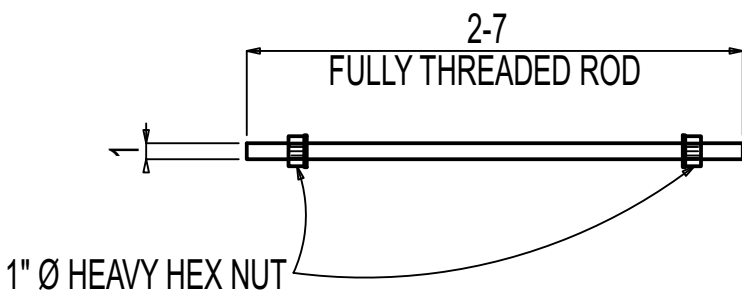

24 THREADED RODS F-08.02M6

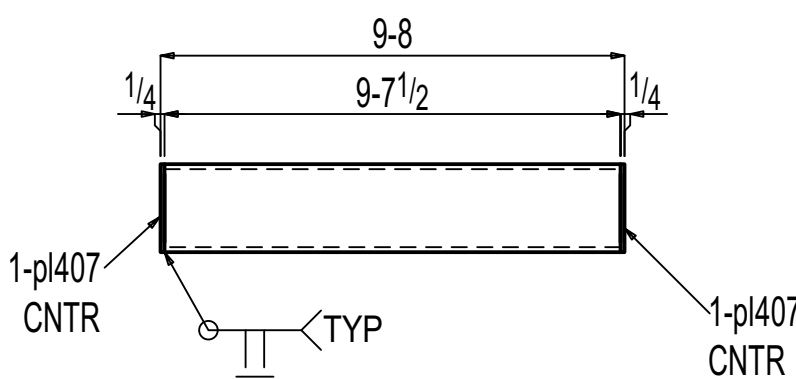

ONE HSS F-08.02M9

PAINT :NO PAINT
PREPARATION :SSPC-SP3

General Notes			
*Structural steel shall conform to ASTM-A992.			
*Structural SQR/RND,tubing conform to ASTM A500 Grade C			
*Pipe shall conform to ASTM A53, Grade B.			
*Channels, Angles and plates shall conform to A36.			
*All bolts shall be 3/4" High strength in accordance with ASTM A325 (UNO)			
*Welding Electrodes for Carbon steel :E70xx			
5	0	For Fabrication	11-03-2025
4	D	For Re-Approval	10-24-2025
3	C	For Re-Approval	09-19-2025
2	B	For Re-Approval	06-23-2025
1	A	For Approval	02-25-2025
# of Copies	Revision/ Issue	Destination	Date

IRON FABRICATION SERVICES, LLC.

3029 M. Street, NW, Suite 202
Washington, DC 20007
Tel: 202-800-5599
Fax: 202-478-0303

Project Name and Address

MARYLAND AVENUE

Location: 1250 MARYLAND AVENUE SW
WASHINGTON, DC 20024

Contractor:

BALFOUR BEATTY

Approved for Fabrication by:	Signature
------------------------------	-----------

Contract # 224009	Drawing # F-08.02
-------------------	-------------------

Contract Item: MISC DETAIL


Ref:

SOW - 08: E-08.00 - E-08.04


Date 01/ 23/ 2025	Drawing Title: MISCELLANEOUS DETAIL
Scale VARIES	

BILL OF MATERIAL							
LINE #	QTY	PC MARK	DESCRIPTION	LENGTH	REMARKS	WEIGHT TOTAL	ADVANCE MILL #
	ONE	F-08.03M1	BENT PLATE			53	
	1	F-08.03M1	PL1/2x1511/16	2 0	BENT A36	53	
			FIELD BOLTS				
	3		3/4 Dia HILTI HAS V-36	0 8	(6" EMBED)		
			THREADED ROD				
			w/HILTI HY-200				
	3	F-08.03M2	BENT PLATE			196	
	3	F-08.03M2	PL1/2x193/16	2 0	BENT A36	196	
			FIELD BOLTS				
	9		3/4 Dia HILTI HAS V-36	0 8	6" EMBED		
			THREADED ROD				
			w/HILTI HY-200				
	3	F-08.03M3	HSS			29	
	3	F-08.03M3	HSS31/2x31/2x5/16	0 71/2	A500C	24	
	6	p3257	PL1/4x31/2	0 31/2	A36	5	
	4	F-08.03M4	HSS			431	
	4	F-08.03M4	HSS5x5x3/8	4 2	A500C	373	
	4	a154	L5x5x3/16	0 10	A36	34	
	8	p3256	PL1/4x5	0 5	A36	14	
	8		3/4 Dia A325N	0 61/2	+1HD WASH	10	
			FIELD BOLTS				
	8		1/2 Dia HILTI K8-T22	0 7			
			EXPANSION ANCHOR		(51/2" EMBEDMENT)		
	ONE	F-08.03M5	ANGLE			2	
	1	F-08.03M5	L4x4x1/4	0 4	A36	2	
	ONE	F-08.03M6	PLATE			7	
	1	F-08.03M6	PL1/4x7	1 11/2	A36	7	
	ONE	F-08.03EP1	EMBED PLATE			440	
	1	F-08.03EP1	PL3/4x15	11 6	A36	440	
	ONE	F-08.03EP2	EMBED PLATE			177	
	1	F-08.03EP2	PL5/8x20	4 2	A36	177	
			FIELD BOLTS				
	8		3/4 Dia HILTI HAS V-36	0 8	(5" EMBEDMENT)		
			w/ HILTI HY-200 EPOXY				


Total weight : 1336

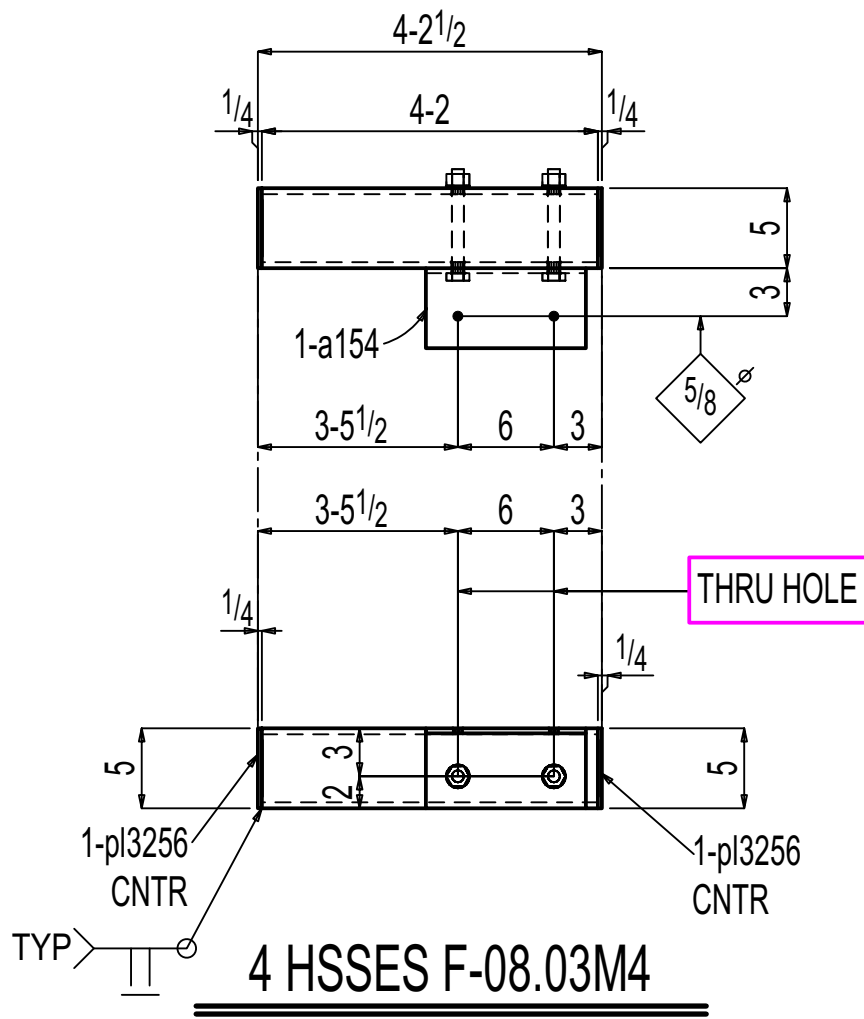


SHOP BOLTS:
2-3/4Diax61/2 A325N

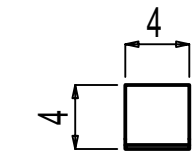


ONE ANGLE F-08.03M5

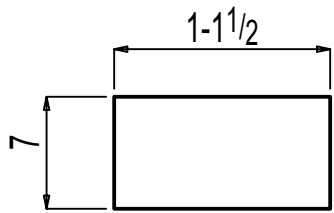

ONE PLATE F-08.03M6

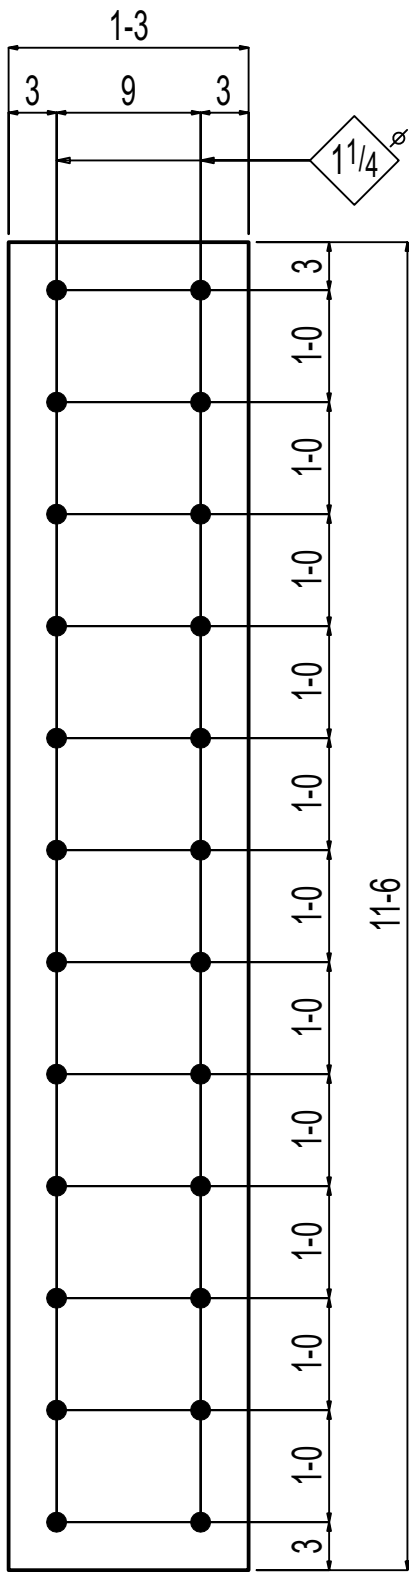


ONE EMBED PLATE F-08.03EP1

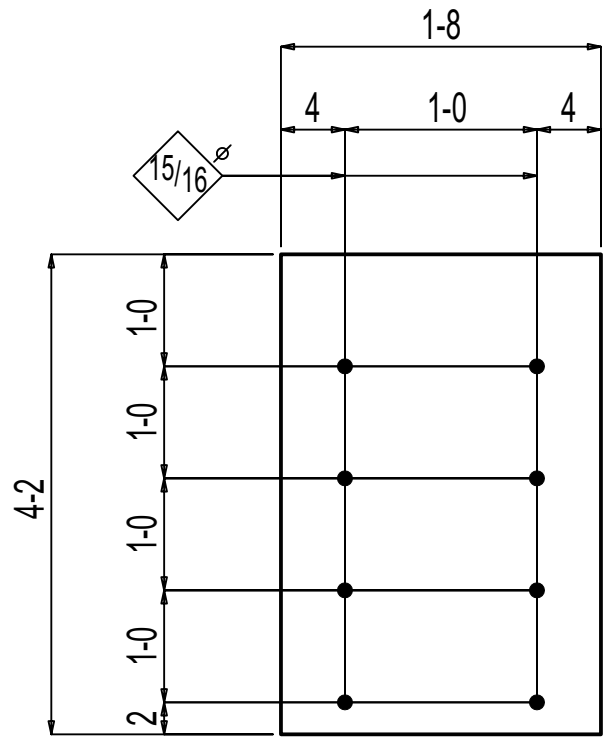


ONE EMBED PLATE F-08.03EP2


PAINT :NO PAINT
PREPARATION :SSPC-SP3

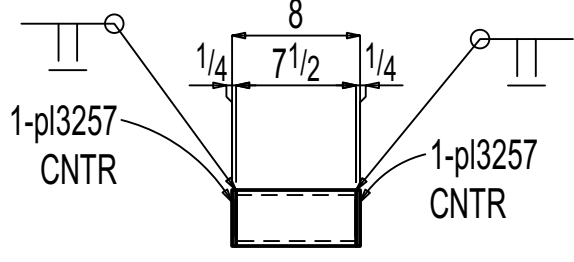

3 HSSes F-08.03M3

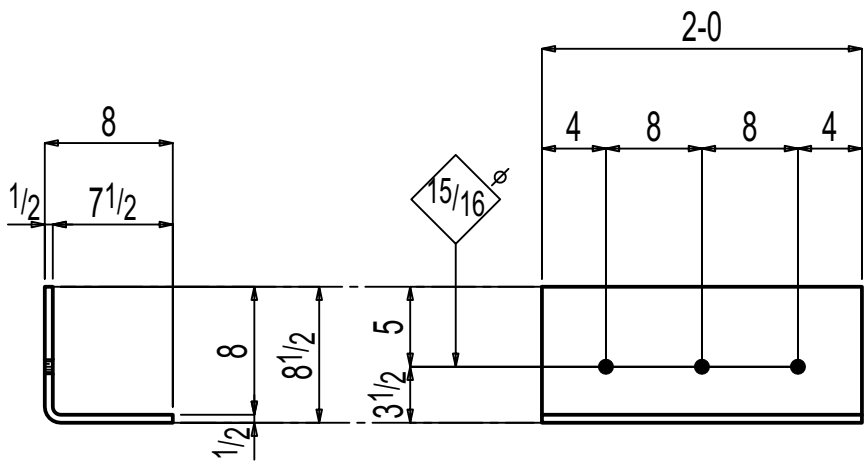

ONE BENT PLATE F-08.03M1

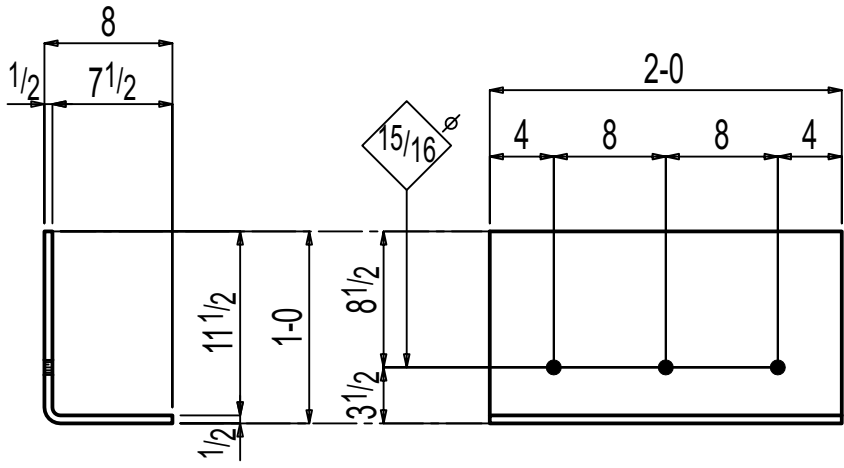

3 BENT PLATES F-08.03M2

General Notes			
*Structural steel shall conform to ASTM-A992.			
*Structural SQR/RND,tubing conform to ASTM A500 Grade C			
*Pipe shall conform to ASTM A53, Grade B.			
*Channels, Angles and plates shall conform to A36.			
*All bolts shall be 3/4" High strength in accordance with ASTM A325 (UNO)			
*Welding Electrodes for Carbon steel :E70xx			
5	0	For Fabrication	11-03-2025
4	D	For Re-Approval	10-24-2025
3	C	For Re-Approval	09-19-2025
2	B	Deleted	06-23-2025
1	A	For Approval	02-25-2025
# of Copies	Revision/ Issue	Destination	Date

IRON FABRICATION SERVICES, LLC.

3029 M. Street, NW, Suite 202
Washington, DC 20007
Tel: 202-800-5599
Fax: 202-478-0303

Project Name and Address

MARYLAND AVENUE

Location: **1250 MARYLAND AVENUE SW
WASHINGTON, DC 20024**

Contractor:

BALFOUR BEATTY

Approved for Fabrication by:

Signature

Contract # **224009**

Drawing # **F-08.03**

Contract Item: **PLATE & ANGLE DETAIL**

Ref:

SOW - 08: E-08.00 - E-08.04

Date

01/ 23/ 2025

Drawing Title:

MISCELLANEOUS DETAIL

Scale

VARIES