

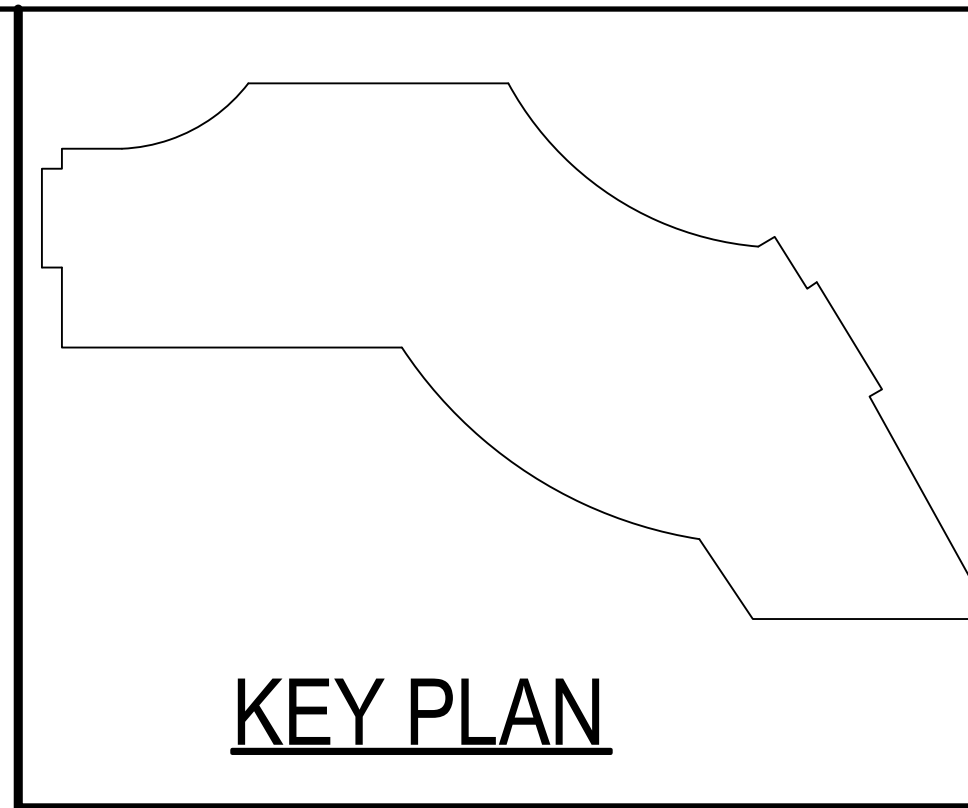


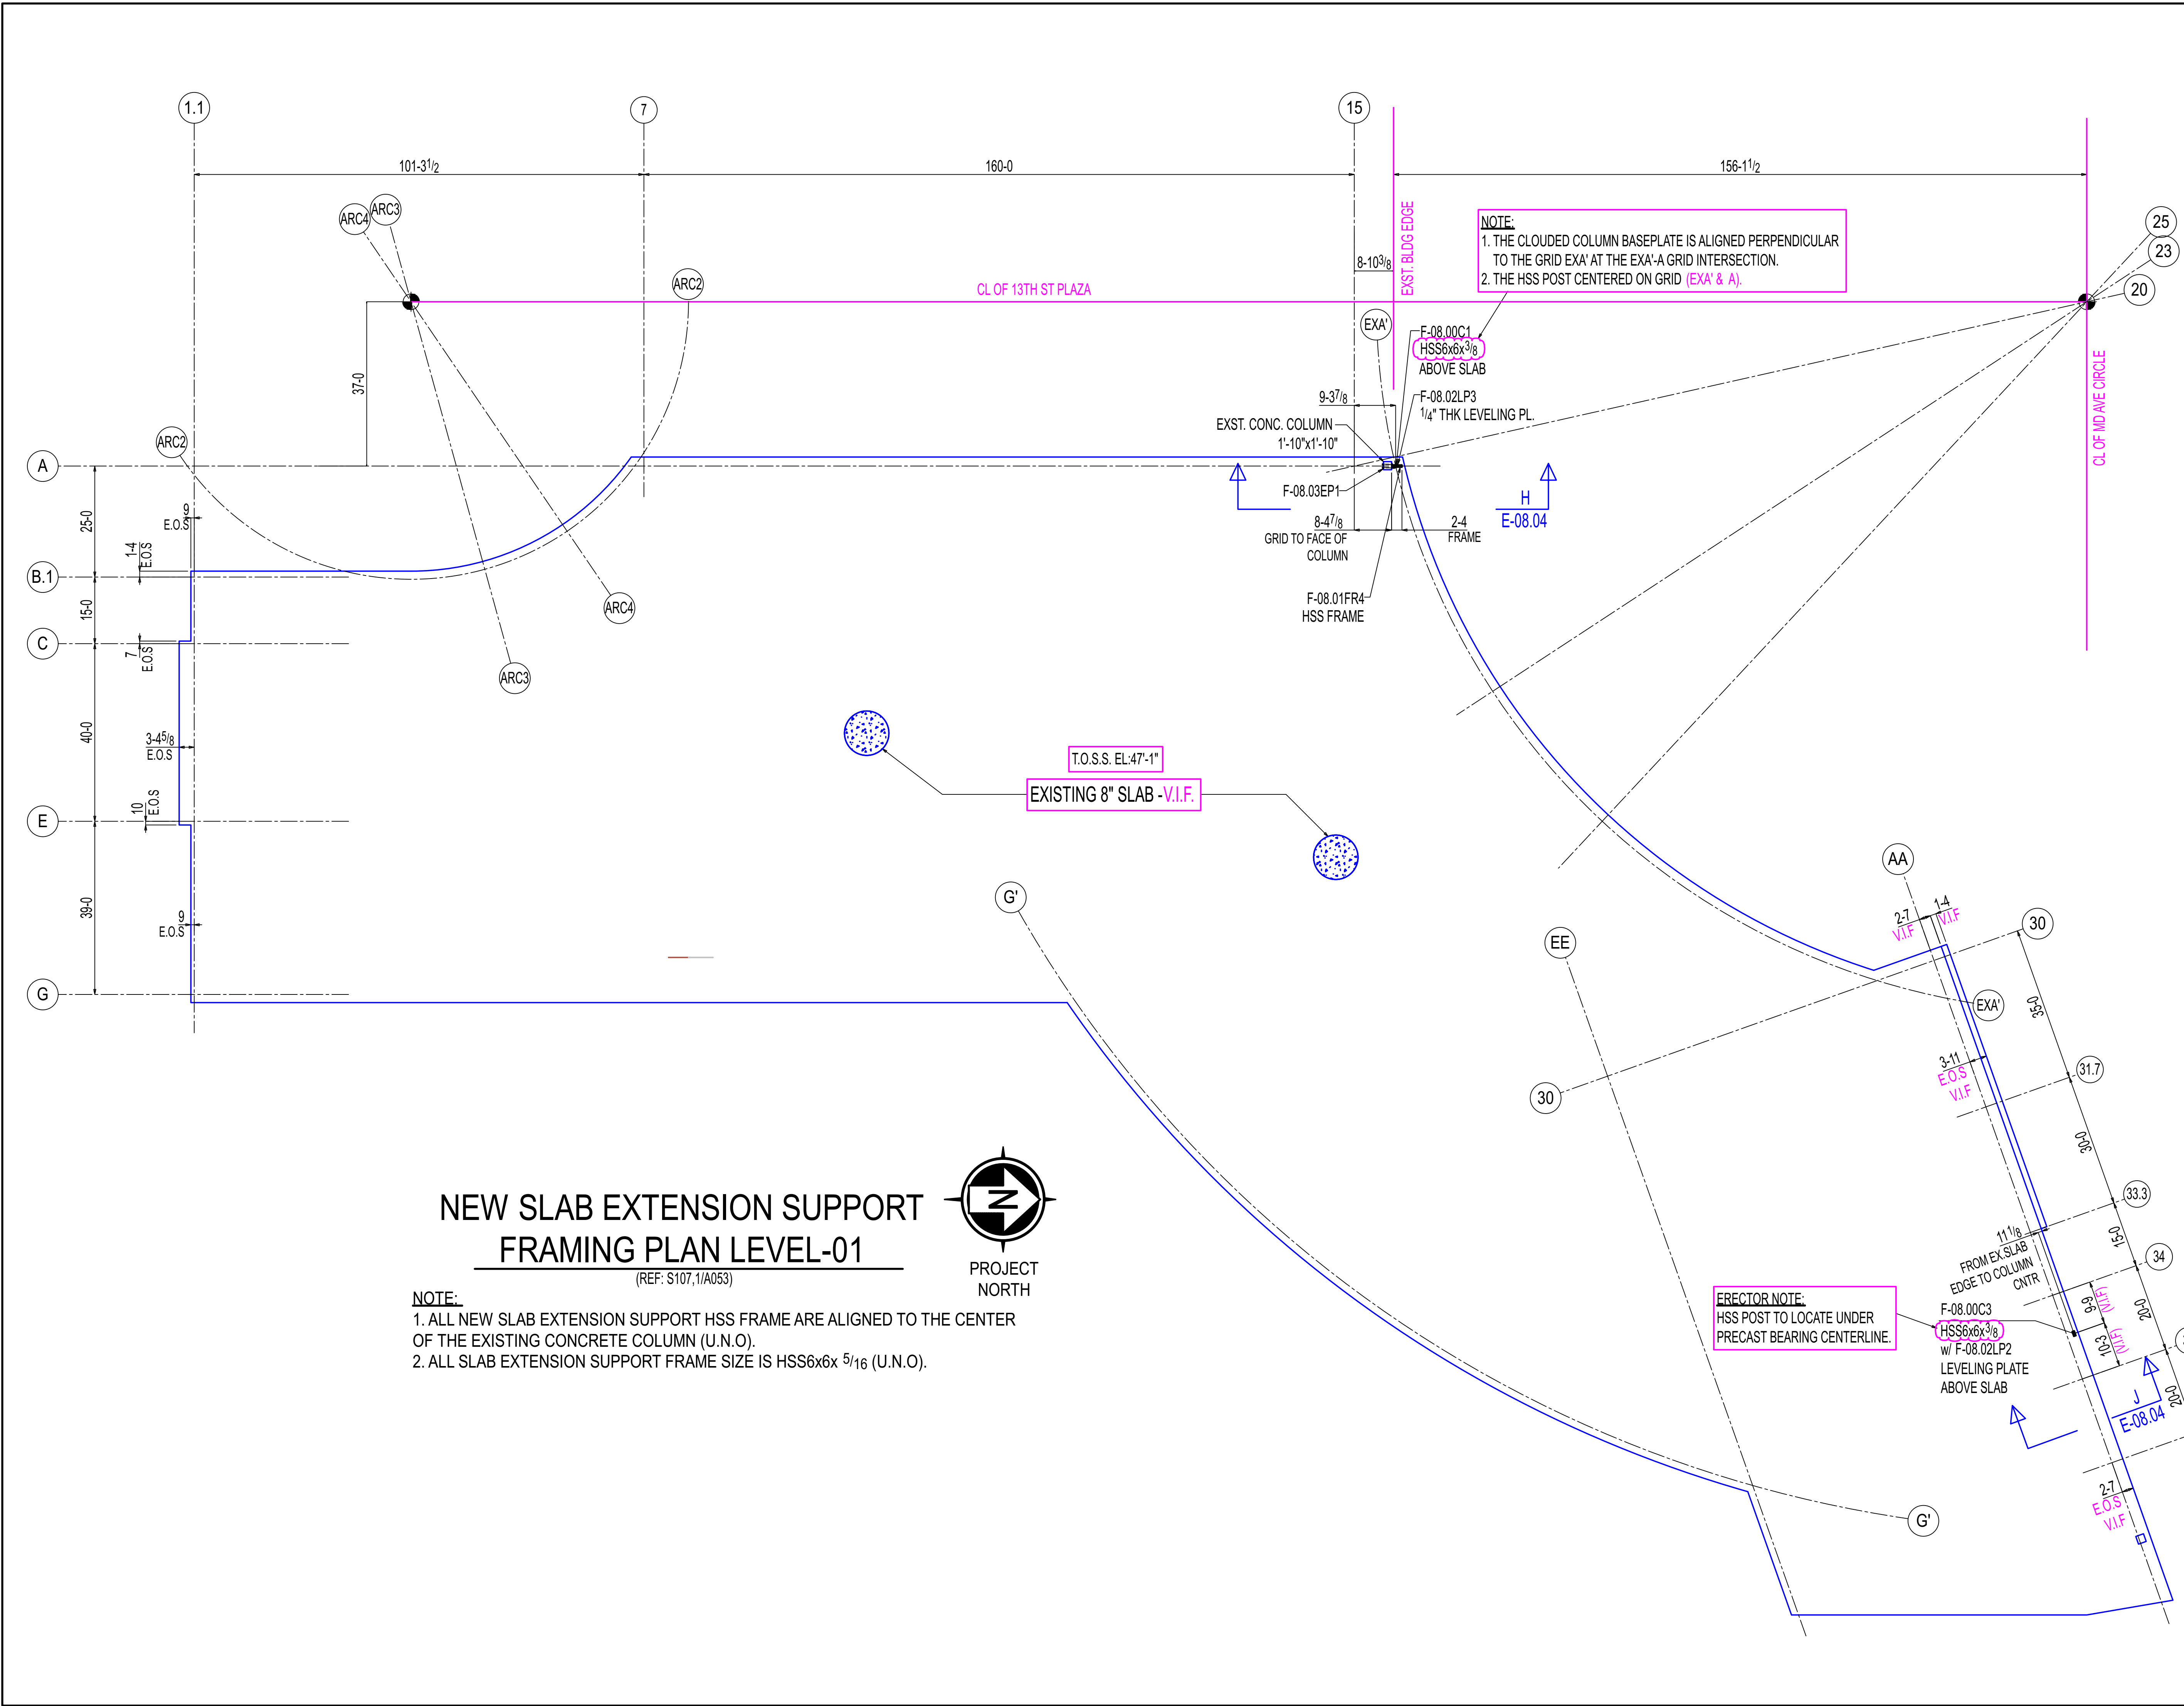

NEW SLAB EXTENSION SUPPORT FRAMING PLAN LEVEL-01

(REF: S107,1/A053)

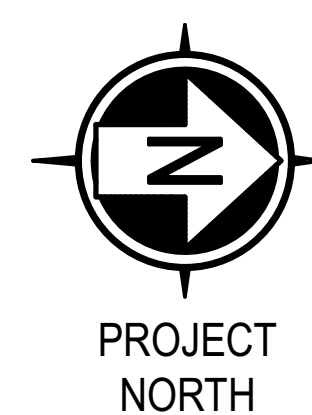

- NOTE:**
1. ALL NEW SLAB EXTENSION SUPPORT HSS FRAME ARE ALIGNED TO THE CENTER OF THE EXISTING CONCRETE COLUMN (U.N.O).
 2. ALL SLAB EXTENSION SUPPORT FRAME SIZE IS HSS6x6x $\frac{5}{16}$ (U.N.O).

General Notes

- *Structural steel shall conform to ASTM-A992.
- *Structural SQR/RND,tubing conform to ASTM A500 Grade C
- *Pipe shall conform to ASTM A53, Grade B.
- *Channels, Angles and plates shall conform to A36.
- *All bolts shall be $\frac{3}{4}$ " High strength in accordance with ASTM A325 (UNO)
- *Welding Electrodes for Carbon steel :E70xx

# of Copies	Revision/ Issue	Destination	Date
5	0	For Construction	11-03-2025
4	D	For Re-Approval	10-24-2025
3	C	For Re-Approval	09-19-2025
2	B	For Re-Approval	08-23-2025
1	A	For Approval	02-25-2025

IRON FABRICATION SERVICES, LLC.

3029 M. Street, NW, Suite 202
Washington, DC 20007
Tel: 202-800-5599
Fax: 202-478-0303

Project Name and Address
MARYLAND AVENUE

Location: **1250 MARYLAND AVENUE SW
WASHINGTON, DC 20024**

Contractor:
BALFOUR BEATTY

Approved for Fabrication by: _____

Signature _____

Contract # **224009** Drawing # **E-08.03**

Contract Item: **LEVEL-01
SLAB EXTENSION**

Ref: **SOW-08:3,4,5&6 / S307**

Date **01/ 20/ 2025** Drawing Title:
**SOW #08 LEVEL-01 NEW
SLAB EXTENSION SUPPORT
FRAMING**

Scale **VARIES**