




NOTE:

-

NOTE,
* - HSS POST LOCATION SHOULD BE CO-ORDINATE WITH
PRECAST MANUFACTURER FOR PRECAST BEARING LOCATION.

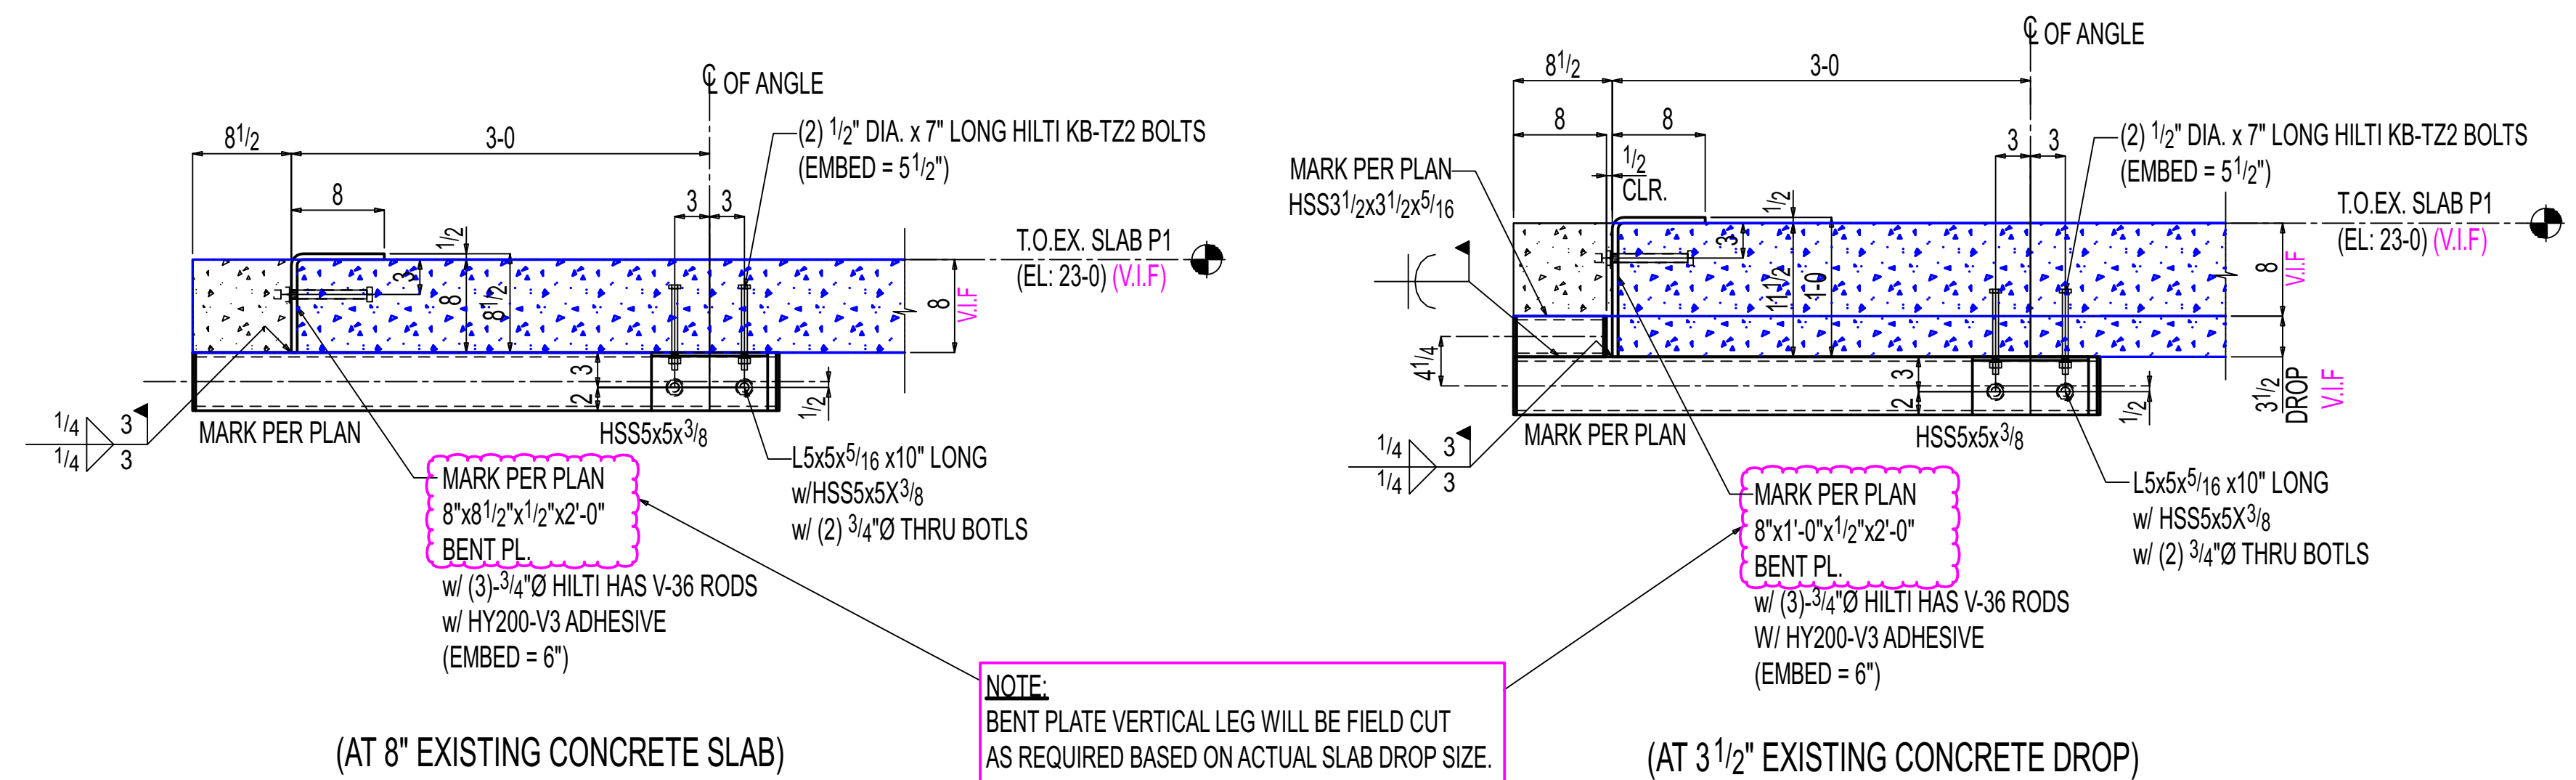

TYPICAL HSS OUTRIGGER SUPPORT PRECAST DETAIL

Date 01/ 20/ 2025	Drawing Title: SOW #08 LEVEL-P1 NEW SLAB EXTENSION SUPPORT PLAN & SECTIONS
Scale VARIES	

- *Structural steel shall conform to ASTM-A992.
- *Structural SQR/RND tubing conform to ASTM A500 Grade C
- *Pipe shall conform to ASTM A53, Grade B.
- *Channels, Angles and plates shall conform to A36.
- *All bolts shall be $\frac{3}{4}$ " High strength in accordance with ASTM A325 (UNO)
- *Welding Electrodes for Carbon steel :E70xx

3	0	For Construction	11-03-2025
2	B	For Re-Approval	10-24-2025
1	A	For Approval	09-19-2025
# of Copies	Revision/Issue	Destination	Date

3029 M. Street, NW, Suite 202
Washington, DC 20007
Tel: 202-800-5599
Fax: 202-478-0303

Project Name and Address
MARYLAND AVENUE

Location: **1250 MARYLAND AVENUE SW**
WASHINGTON, DC 20024

Contractor: **BALFOUR BEATTY**

Approved for Fabrication by:	Signature

Contract # 224009	Drawing # E-08.05
--------------------------	--------------------------

Contract Item:	LEVEL-P1 SLAB EXTENSION
----------------	------------------------------------

Ref: **SOW-08:S104,5/S315**

Date 01/ 20/ 2025	Drawing Title: SOW #08 LEVEL-P1 NEW SLAB EXTENSION SUPPORT PLAN & SECTIONS
Scale VARIES	