


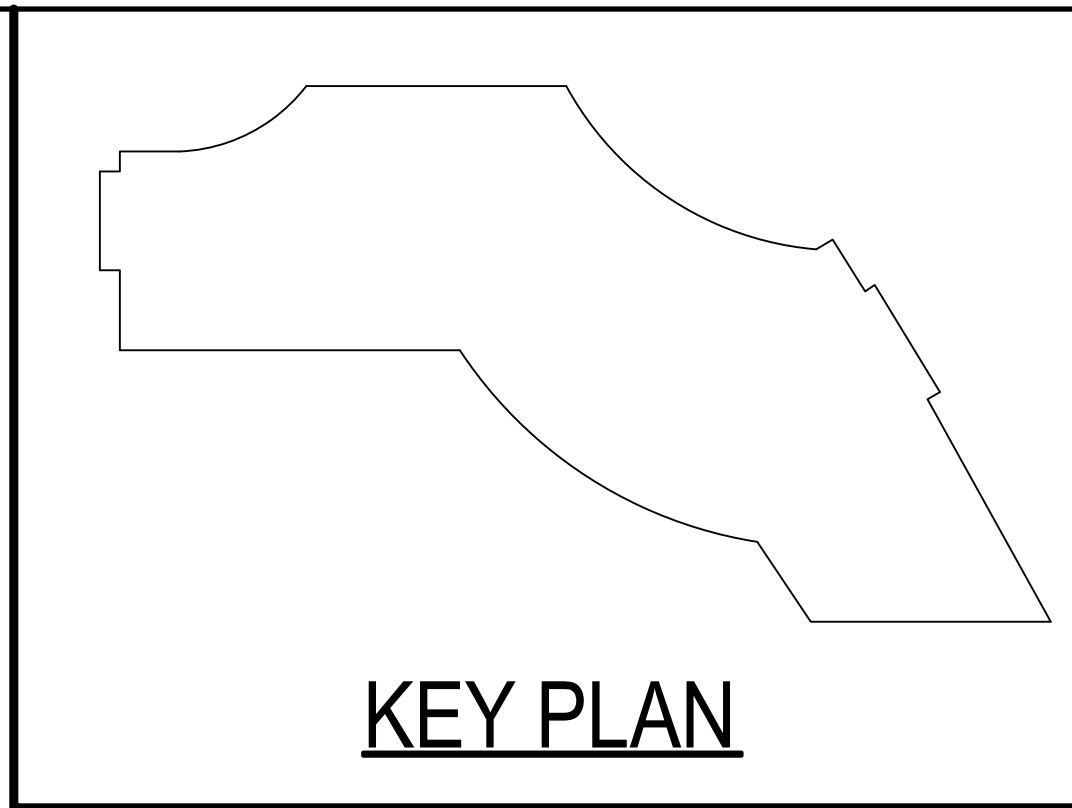

KEY PLAN

LEGEND:
V.I.F - VERIFY IN FIELD
LSH - LONG SIDE HORIZONTAL
E.O.S - EDGE OF SLAB
U.N.O - UNLESS NOTED OTHERWISE

General Notes			
*Structural steel shall conform to ASTM-A992.			
*Structural SQR/RND.tubing conform to ASTM A500 Grade C			
*Pipe shall conform to ASTM A53, Grade B.			
*Channels, Angles and plates shall conform to A36.			
*All bolts shall be 3/4" High strength in accordance with ASTM A325 (UNO)			
*Welding Electrodes for Carbon steel :E70xx			
# of Copies	Revision/ Issue	Destination	Date
5	0	For Construction	11-03-2025
4	D	For Re-Approval	10-24-2025
3	C	For Re-Approval	09-19-2025
2	B	For Re-Approval	08-23-2025
1	A	For Approval	02-25-2025

IRON FABRICATION SERVICES, LLC.

3029 M. Street, NW, Suite 202
Washington, DC 20007
Tel: 202-800-5599
Fax: 202-478-0303


Project Name and Address
MARYLAND AVENUE

Location: **1250 MARYLAND AVENUE SW
WASHINGTON, DC 20024**

Contractor:
BALFOUR BEATTY

Approved for Fabrication by: _____ Signature _____

Contract #	224009	Drawing #	E-08.00
Contract Item:	LEVEL-02 SLAB EXTENSION		
Ref:	SOW-08: (S107,1/A053)		
Date	01/20/2025	Drawing Title:	SOW #08 LEVEL-02 NEW SLAB EXTENSION SUPPORT FRAMING PLAN
Scale	VARIES		

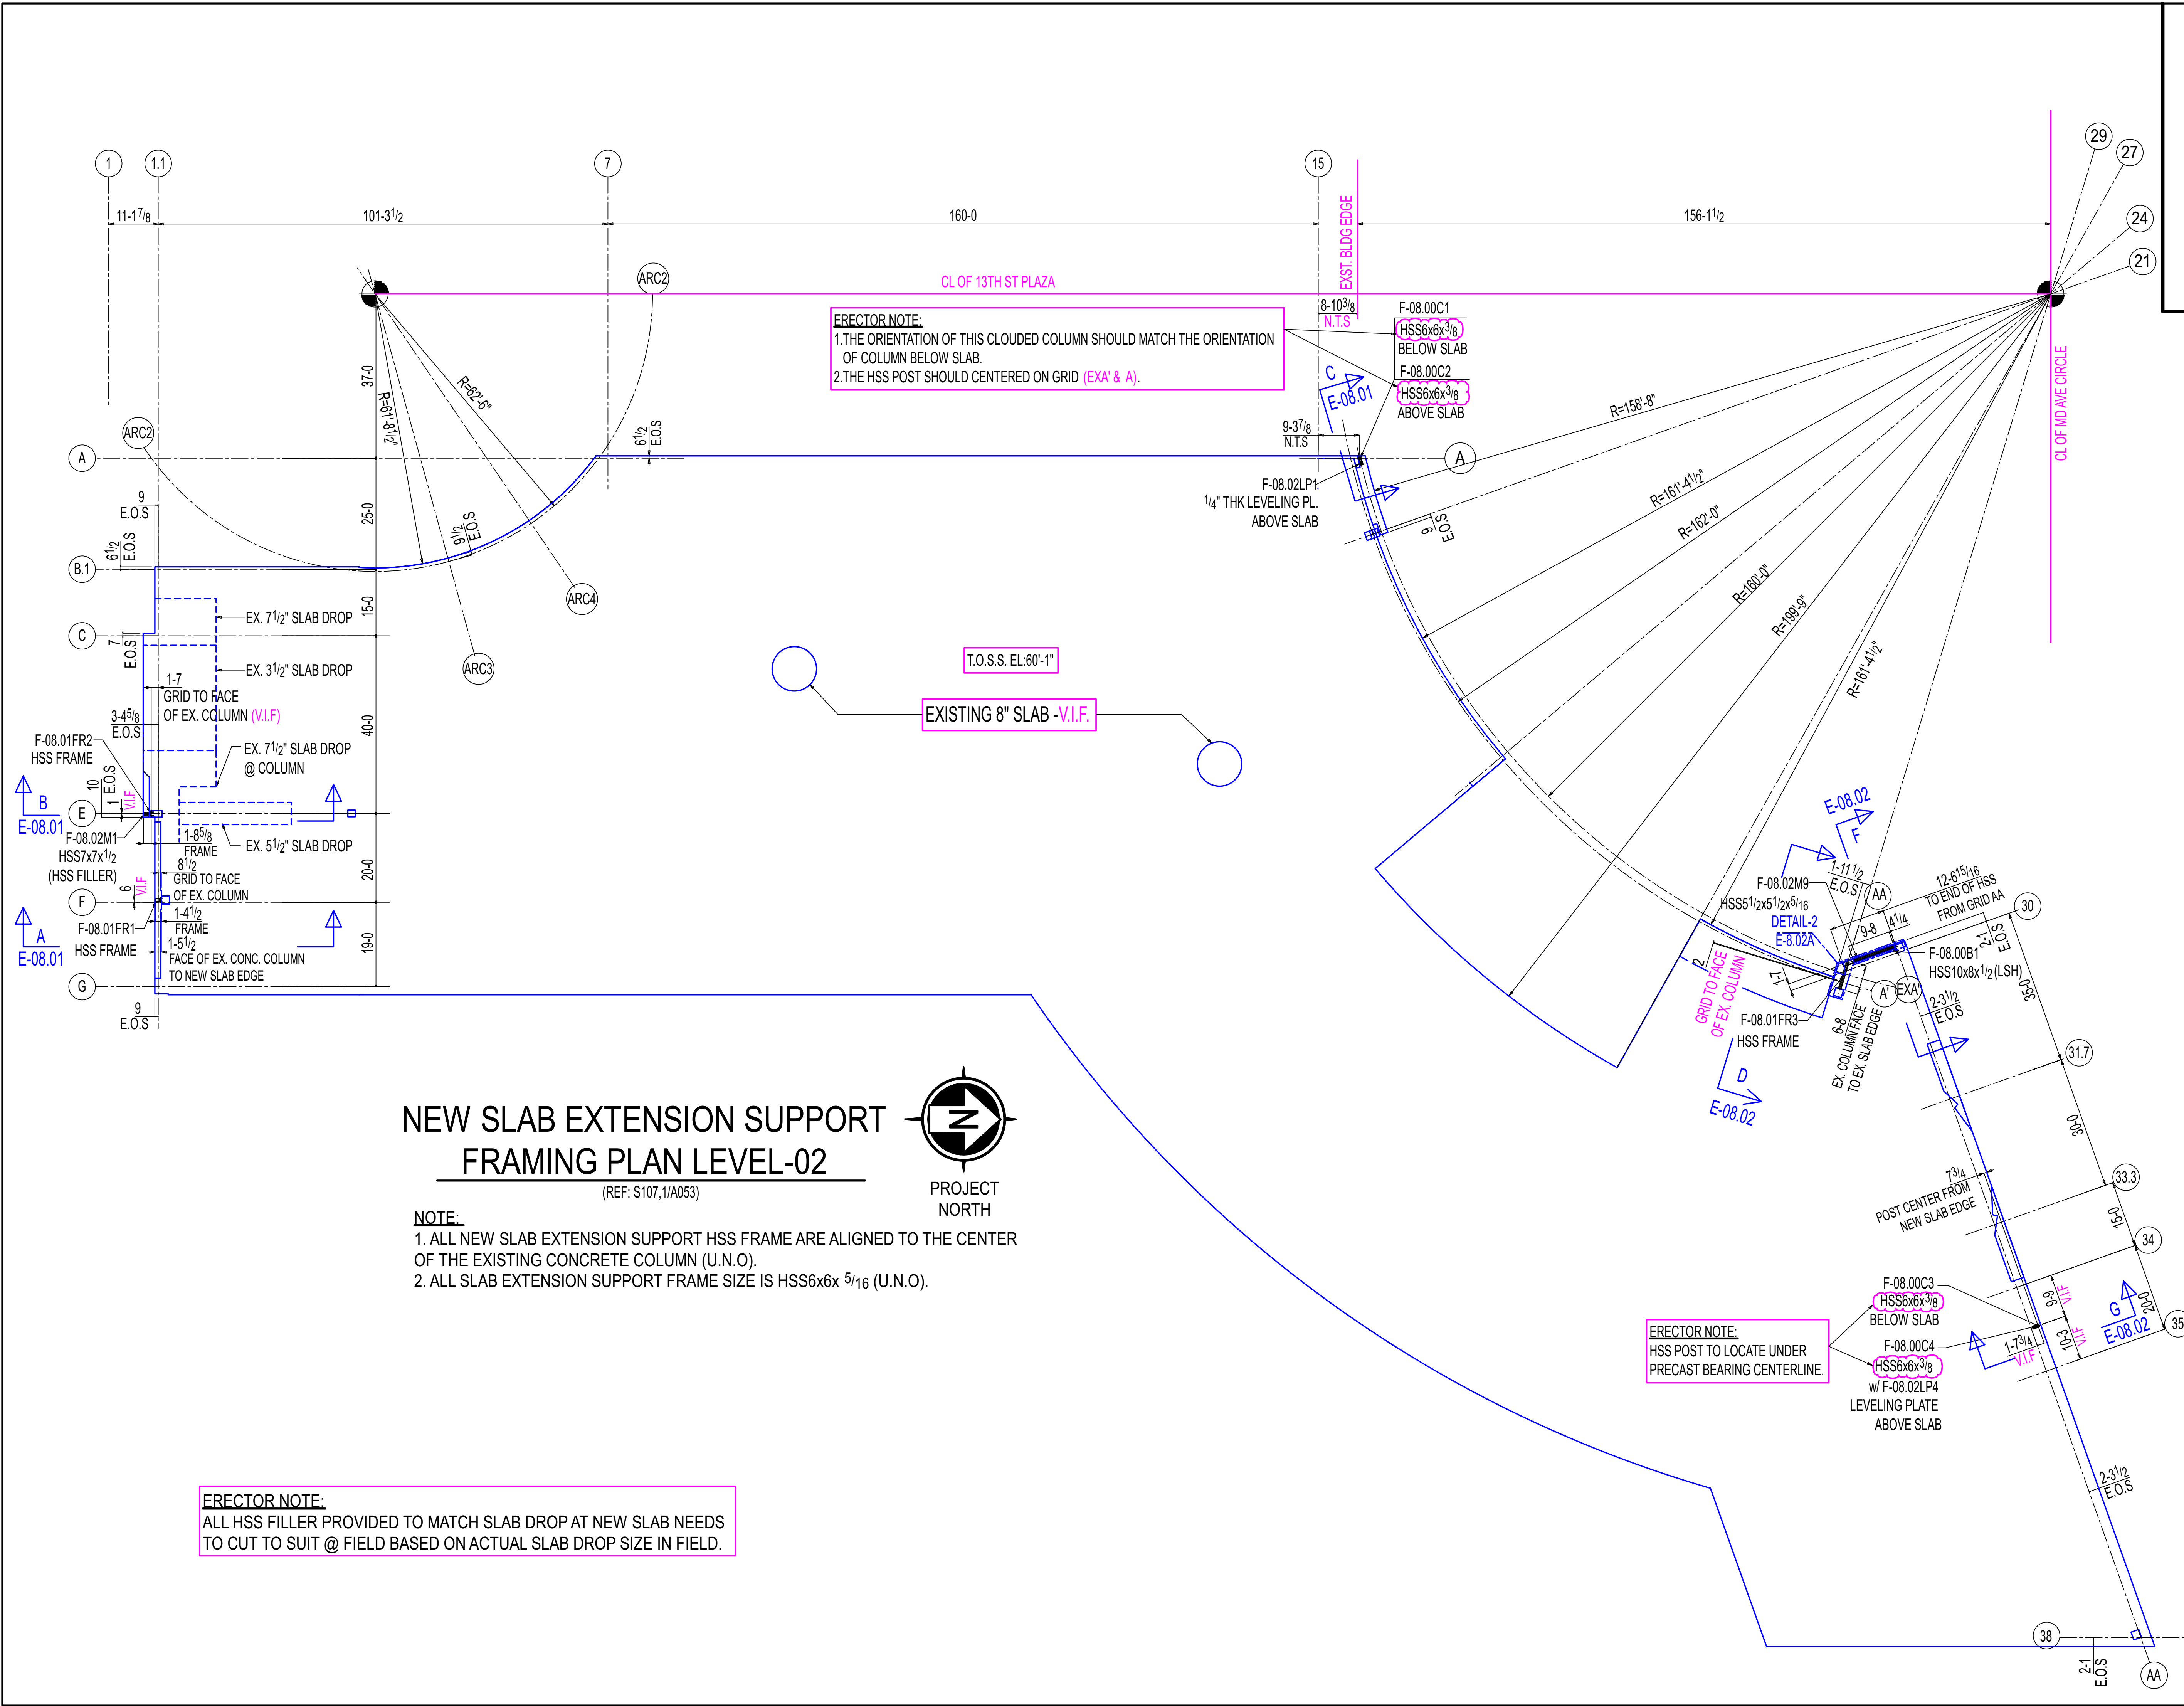


ERECTOR NOTE:
1. THE ORIENTATION OF THIS CLOUDED COLUMN SHOULD MATCH THE ORIENTATION OF COLUMN BELOW SLAB.
2. THE HSS POST SHOULD BE CENTERED ON GRID (EXA' & A).

ERECTOR NOTE:
HSS POST TO LOCATE UNDER PRECAST BEARING CENTERLINE.

NEW SLAB EXTENSION SUPPORT
FRAMING PLAN LEVEL-02


(REF: S107,1/A053)

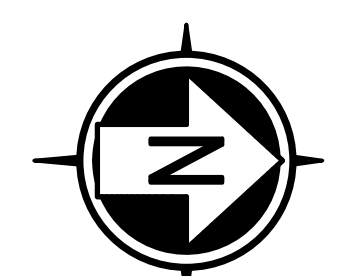

PROJECT
NORTH


NOTE:
1. ALL NEW SLAB EXTENSION SUPPORT HSS FRAME ARE ALIGNED TO THE CENTER OF THE EXISTING CONCRETE COLUMN (U.N.O).
2. ALL SLAB EXTENSION SUPPORT FRAME SIZE IS HSS6x6x 5/16 (U.N.O).

ERECTOR NOTE:
ALL HSS FILLER PROVIDED TO MATCH SLAB DROP AT NEW SLAB NEEDS TO CUT TO SUIT @ FIELD BASED ON ACTUAL SLAB DROP SIZE IN FIELD.

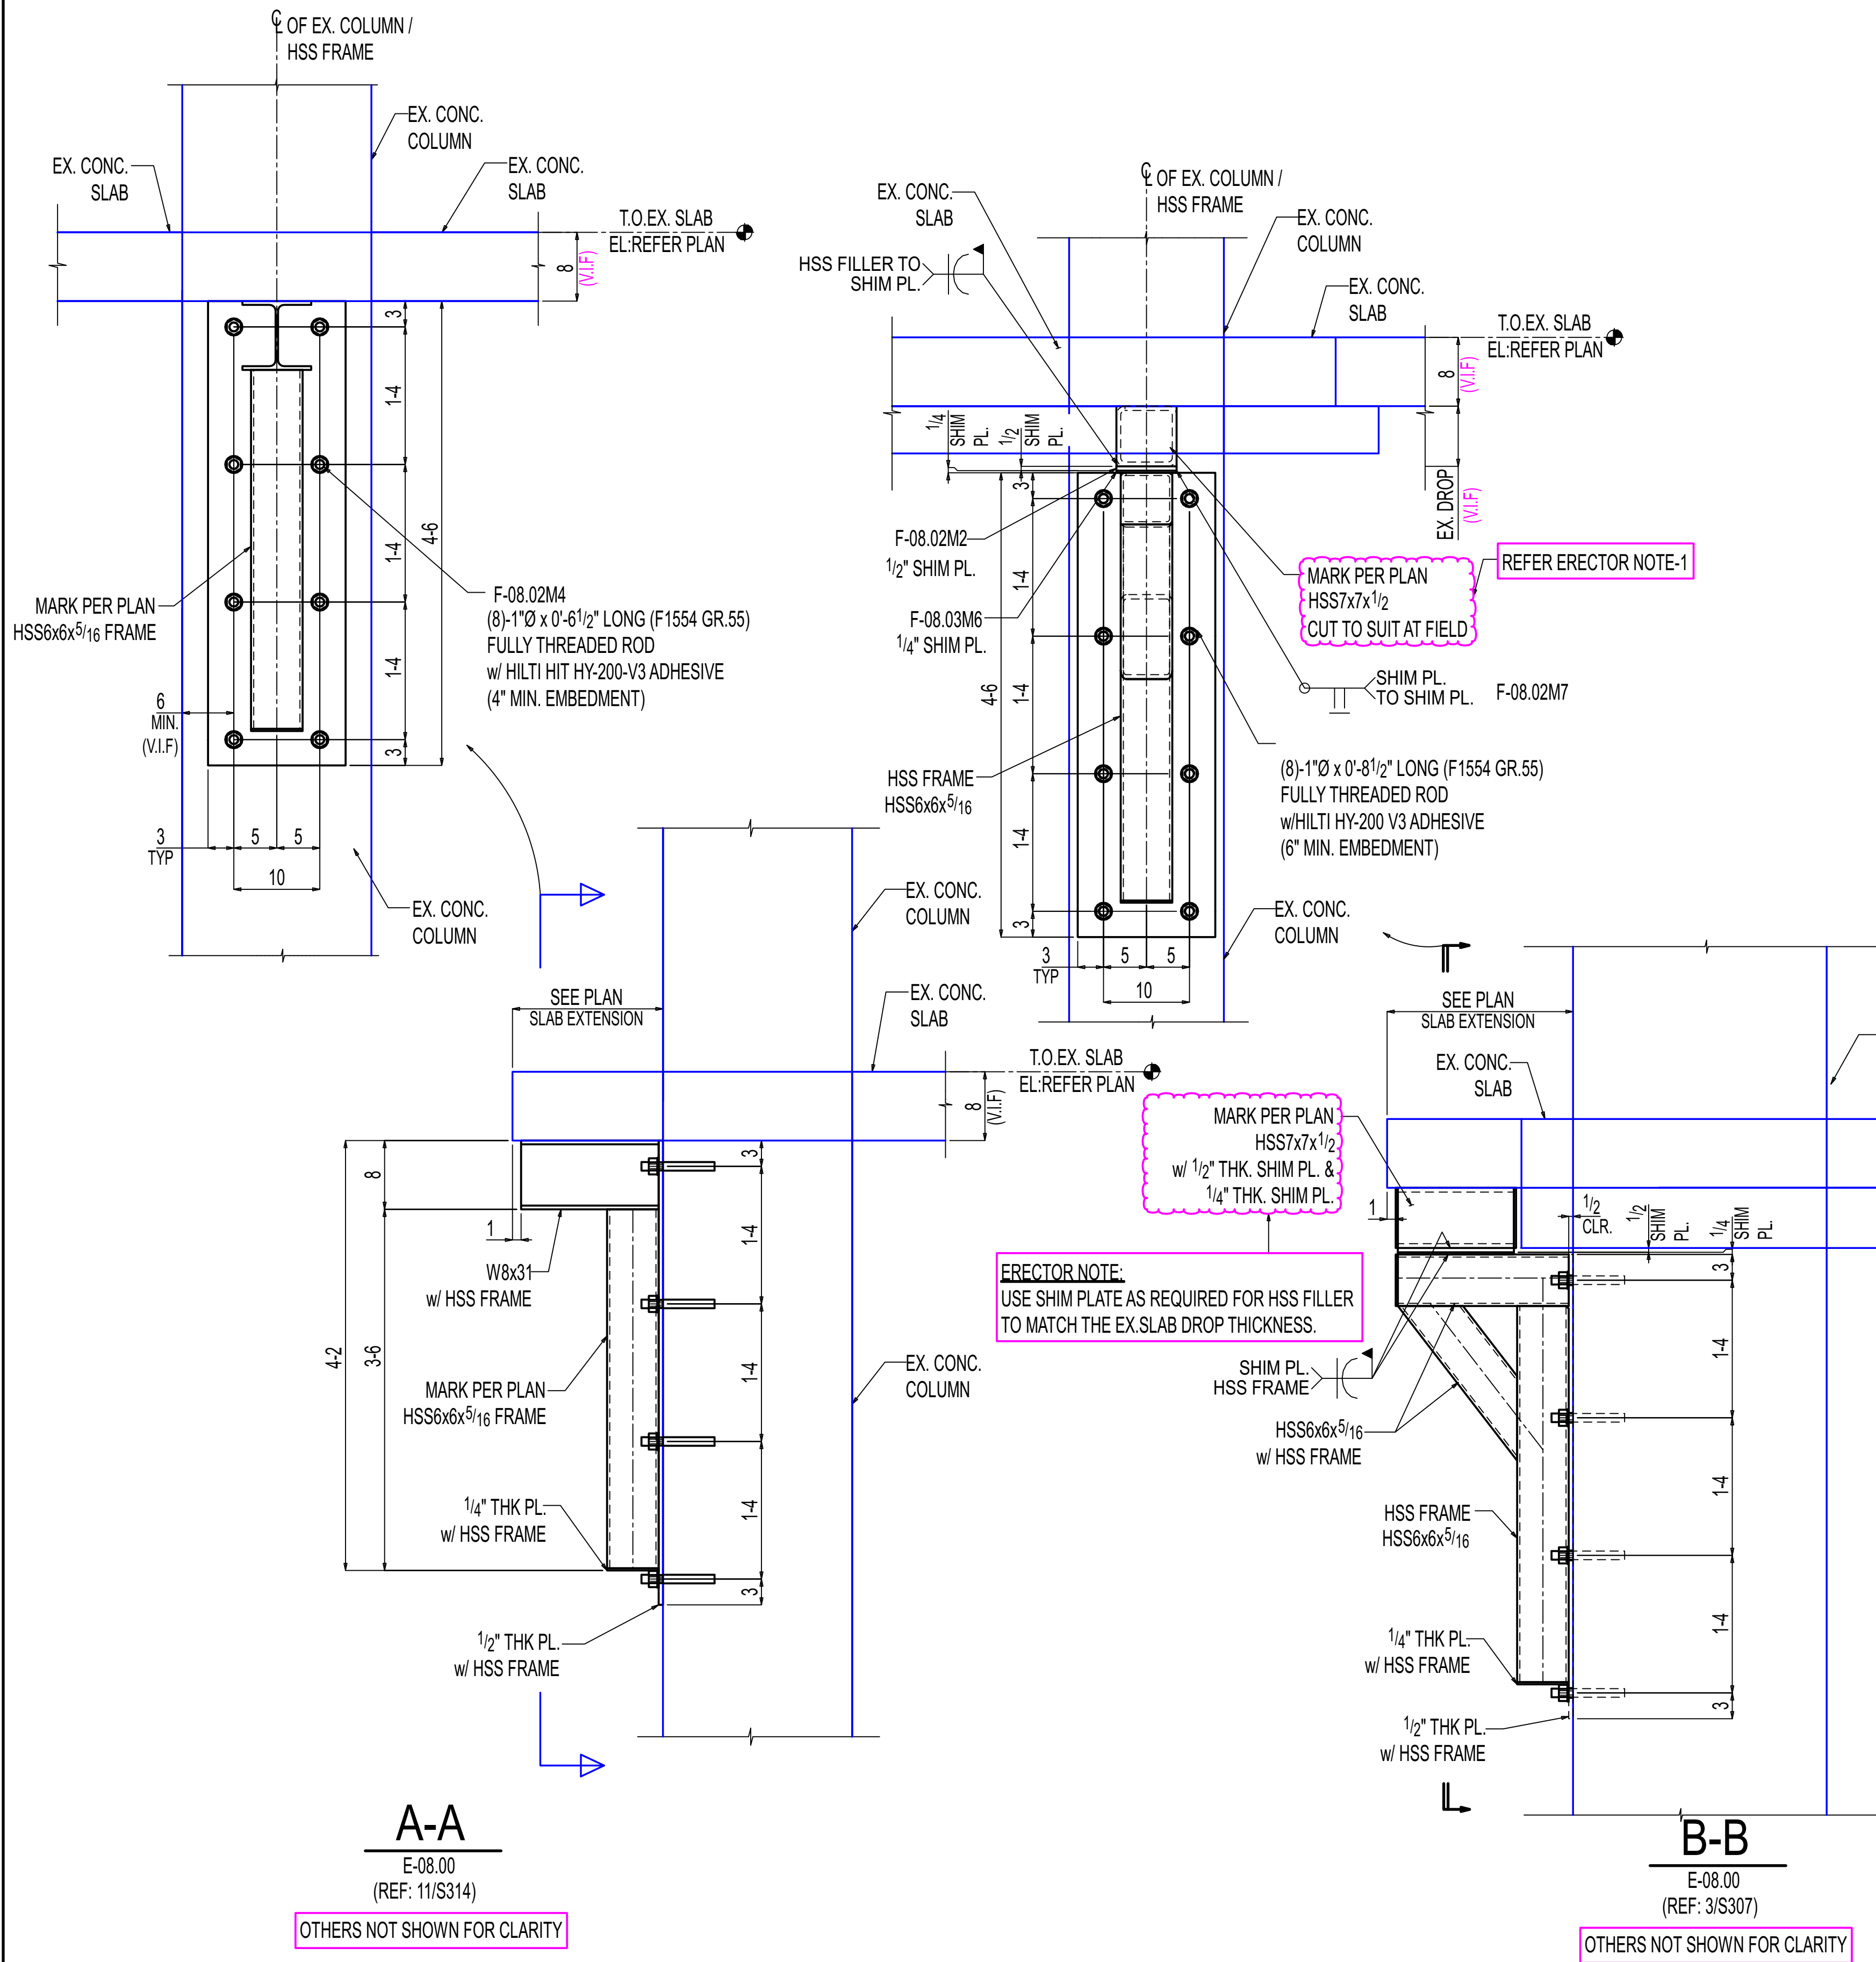

SHOP / ERECTOR NOTE:
LOCATE EXISTING REBAR PRIOR TO FABRICATION OF PLATE.
DO NOT DRILL THROUGH REBAR.

ERECTOR NOTE-1:
ADJUST HSS DEPTH IN FIELD BY CUT THE HSS TO MATCH
EXISTING SLAB DROP THICKNESS, AND WELD TO THE
TOP OF HSS FRAME AT SITE PRIOR TO ERECTING THE HSS FRAME.

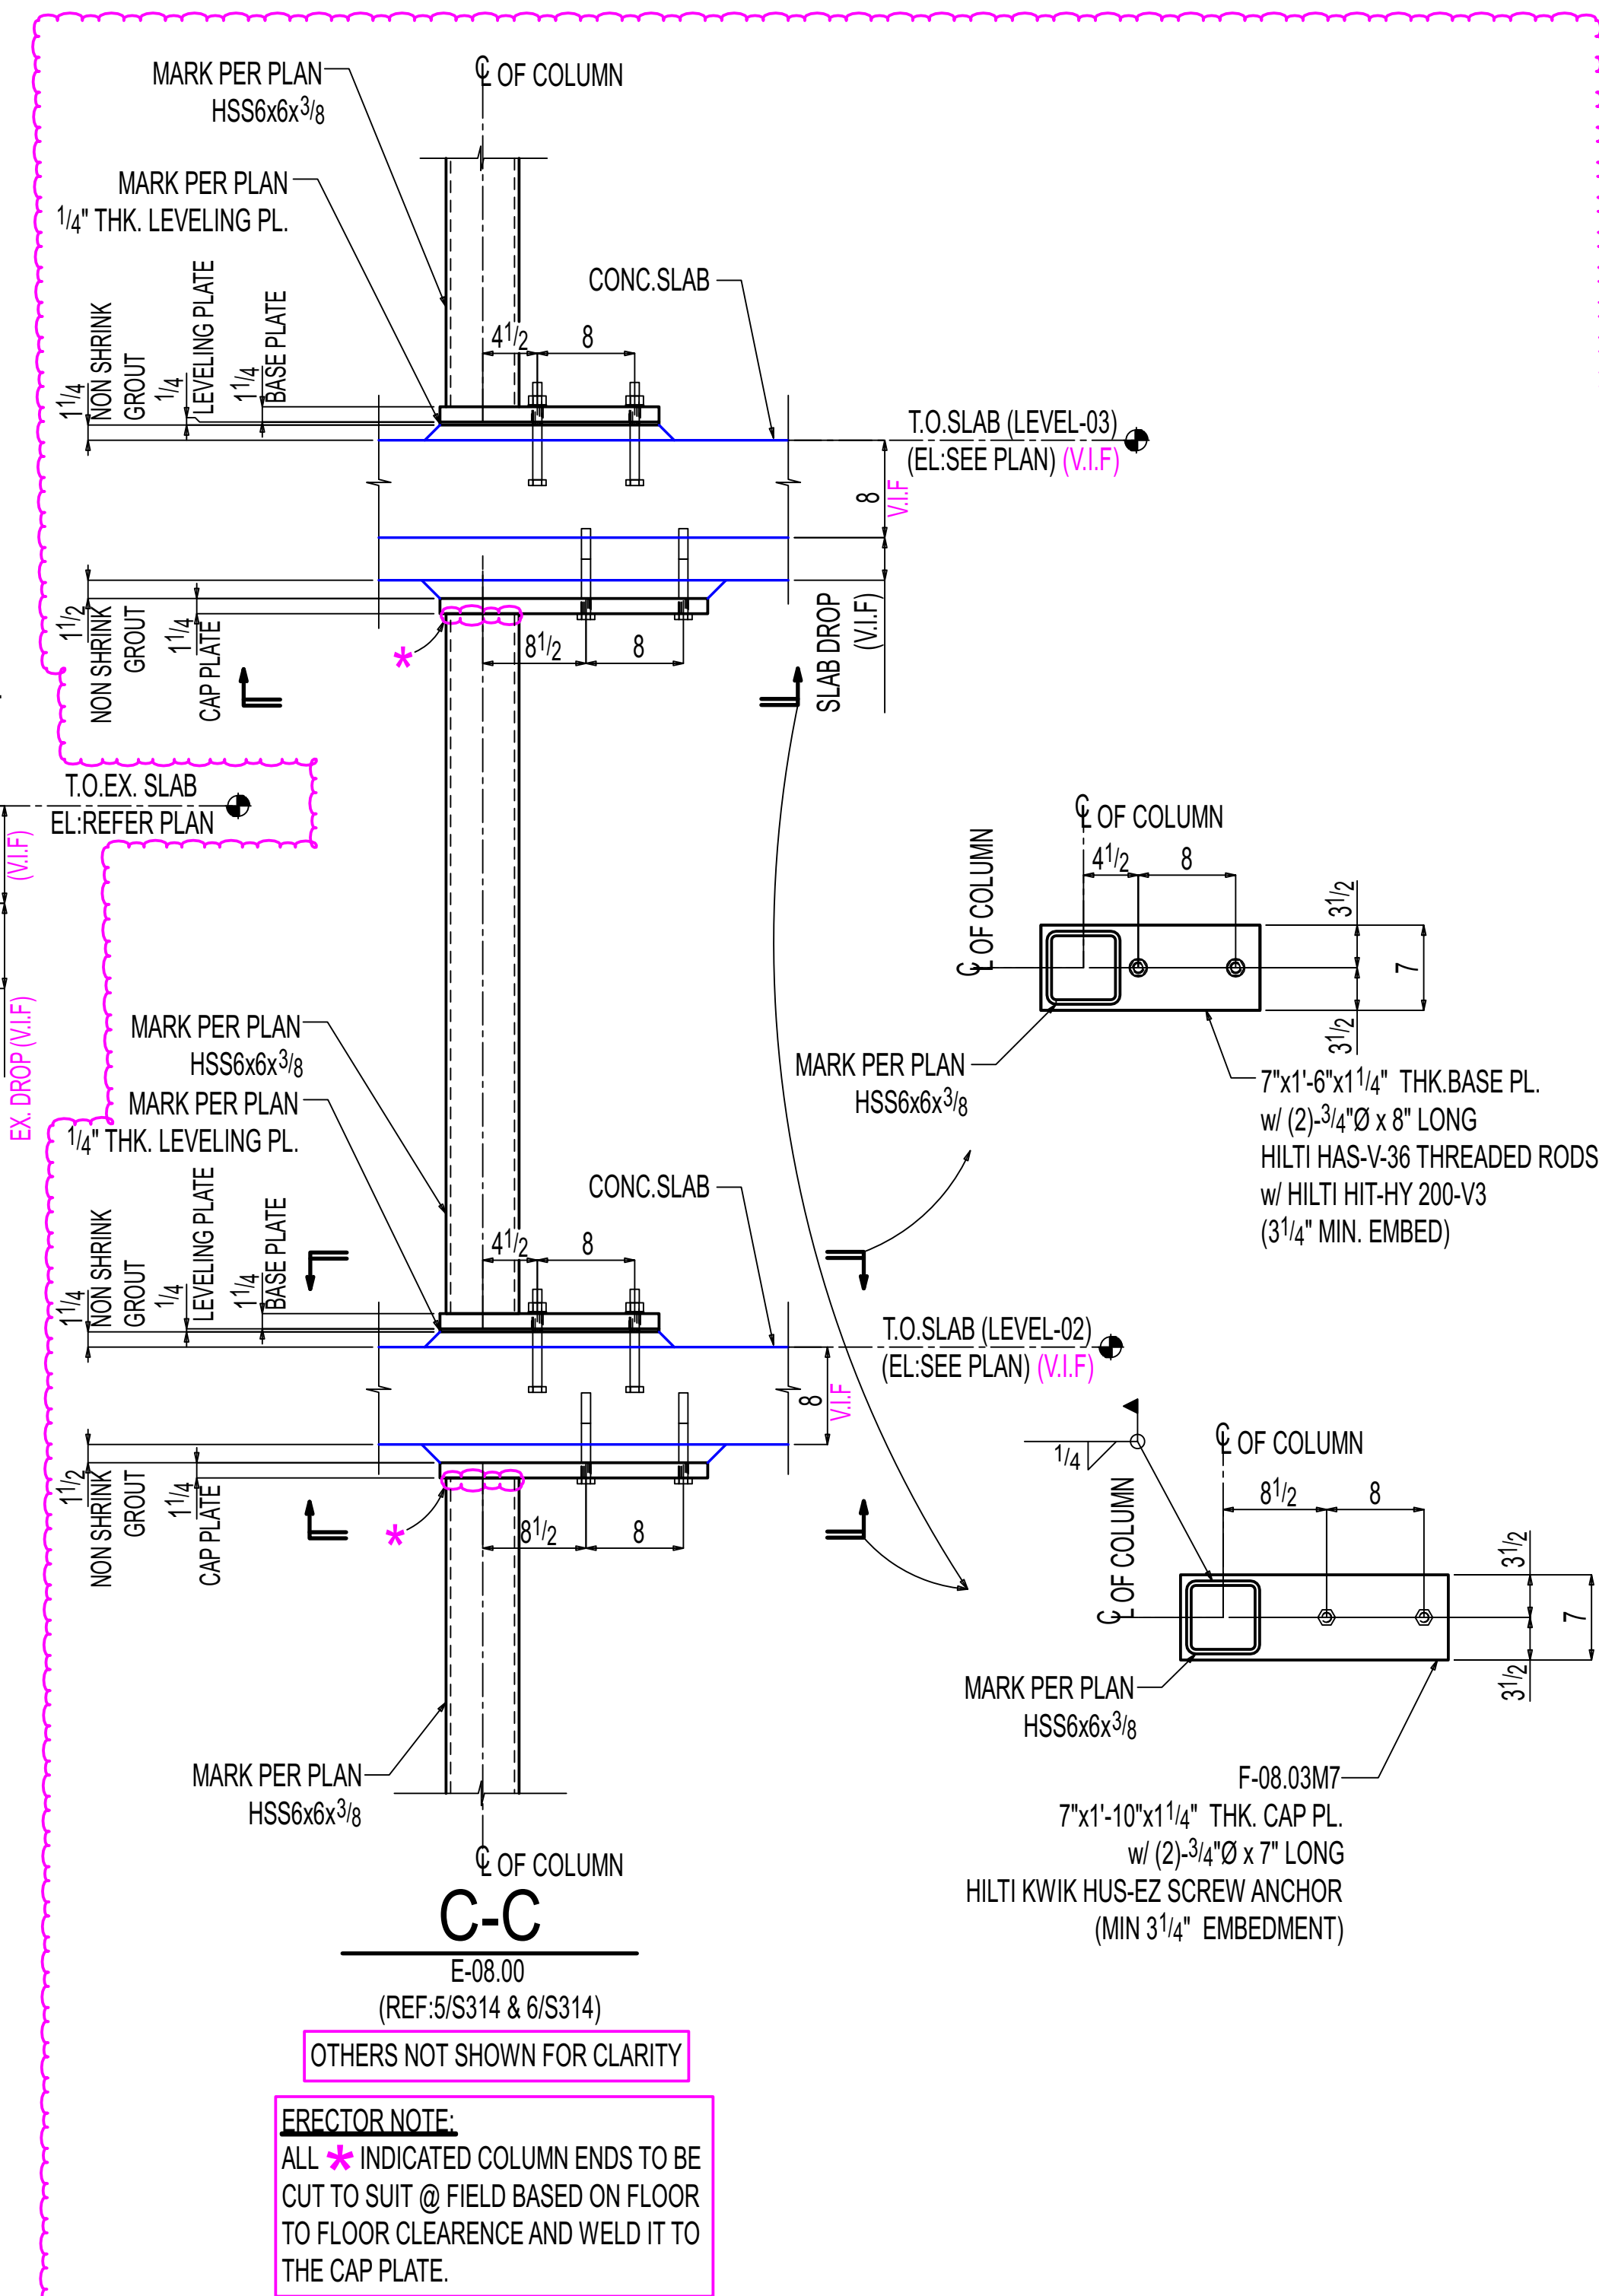

ERECTOR NOTE:
ALL * INDICATED COLUMN ENDS TO BE
CUT TO SUIT @ FIELD BASED ON FLOOR
TO FLOOR CLEARANCE AND WELD IT TO
THE CAP PLATE.

General Notes			
*Structural steel shall conform to ASTM-A992.			
*Structural SQR/RND.tubing conform to ASTM A500 Grade C			
*Pipe shall conform to ASTM A53, Grade B.			
*Channels, Angles and plates shall conform to A36.			
*All bolts shall be 3/4" High strength in accordance with ASTM A325 (UNO)			
*Welding Electrodes for Carbon steel :E70xx			
# of Copies	Revision/ Issue	Destination	Date
6	1	Revised as noted	11-11-2025
5	0	For Construction	11-03-2025
4	D	For Re-Approval	10-24-2025
3	C	For Re-Approval	09-19-2025
2	B	For Re-Approval	06-23-2025
1	A	For Approval	02-25-2025

IRON FABRICATION SERVICES, LLC.

3029 M. Street, NW, Suite 202
Washington, DC 20007
Tel: 202-800-5599
Fax: 202-478-0303

Project Name and Address
MARYLAND AVENUE
Location: **1250 MARYLAND AVENUE SW
WASHINGTON, DC 20024**


Contractor:
BALFOUR BEATTY

Approved for Fabrication by: _____
Signature

Contract # **224009** Drawing # **E-08.01**
Contract Item: **LEVEL-02
SLAB EXTENSION**
Ref: **SOW-08:3,4,5&6 / S307**

Date **01/20/2025** Drawing Title:
**SOW #08 LEVEL-02 NEW
SLAB EXTENSION SUPPORT
SECTIONS**
Scale **VARIES**

Date 01/ 20/ 2025	Drawing Title: SOW #08 LEVEL-02 NEW SLAB EXTENSION SUPPORT SECTIONS
Scale VARIES	

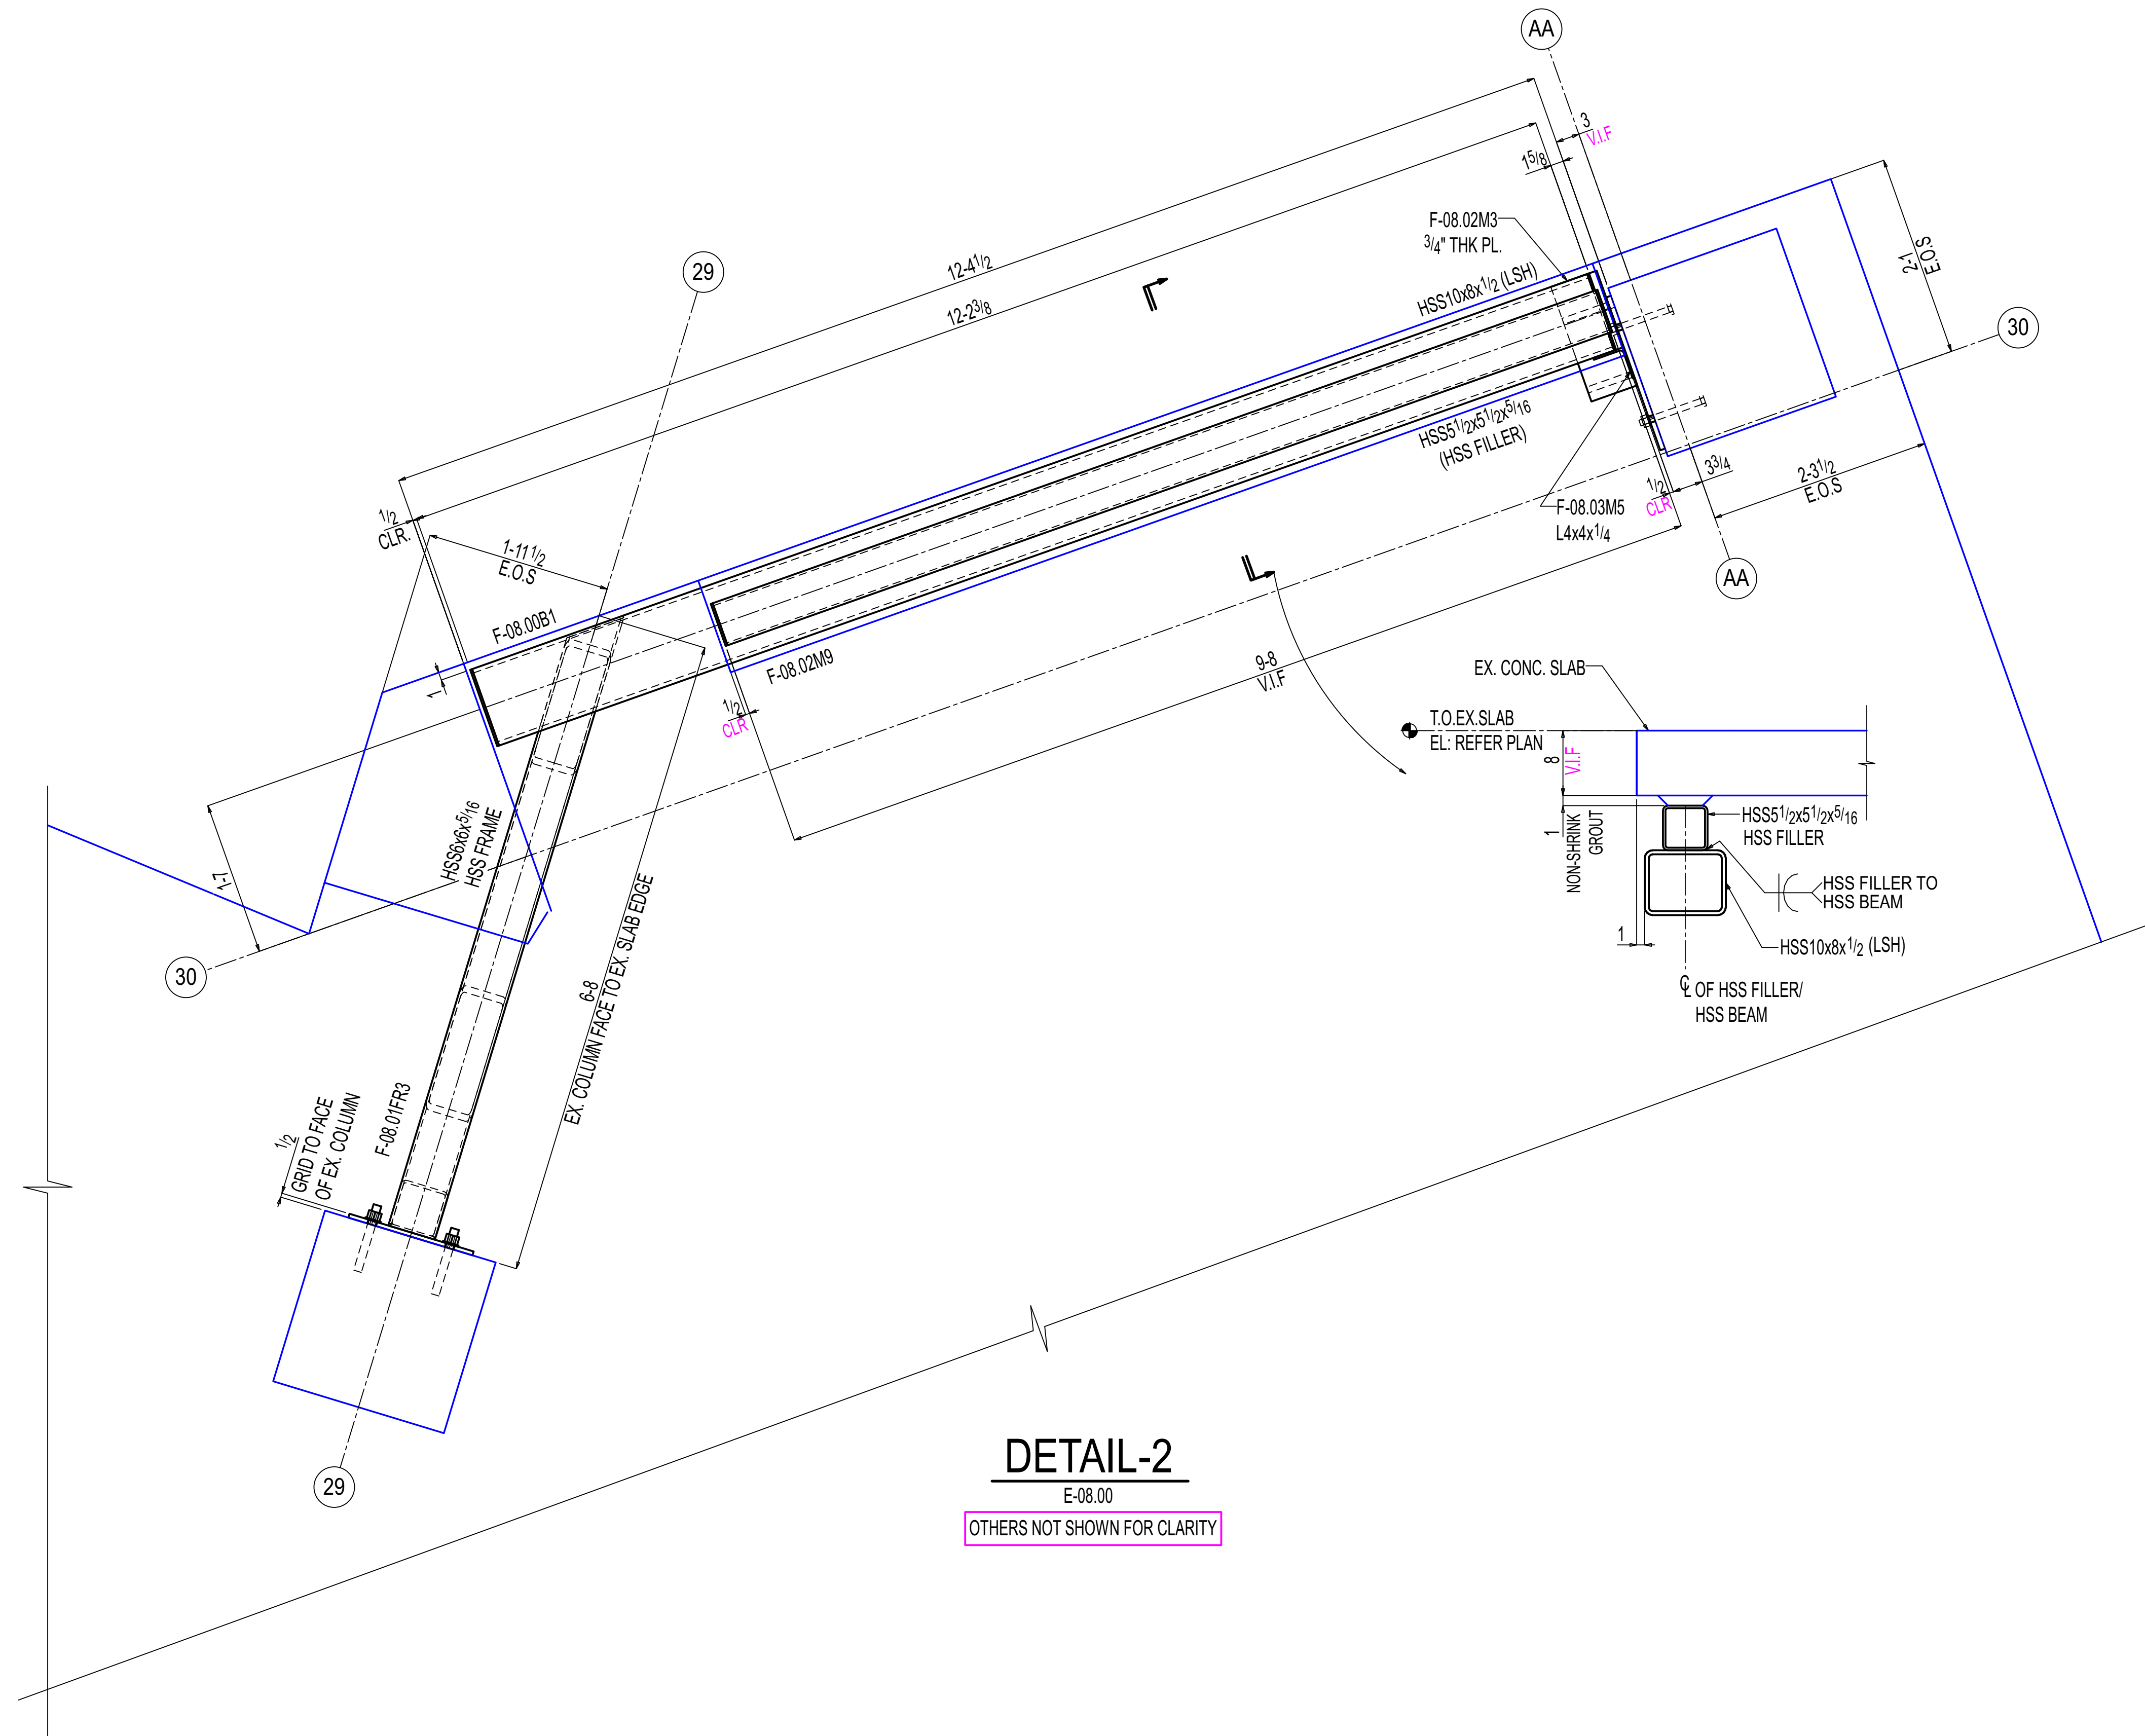

DETAIL-2

E-08.00

OTHERS NOT SHOWN FOR CLARITY

General Notes

- *Structural steel shall conform to ASTM-A992.
- *Structural SQR/RND.tubing conform to ASTM A500 Grade C
- *Pipe shall conform to ASTM A53, Grade B.
- *Channels, Angles and plates shall conform to A36.
- *All bolts shall be 3/4" High strength in accordance with ASTM A325 (UNO)
- *Welding Electrodes for Carbon steel :E70xx

# of Copies	Revision/ Issue	For Construction Destination	11-03-2025 Date
1	0	For Construction	11-03-2025

IRON FABRICATION SERVICES, LLC.

3029 M. Street, NW, Suite 202
Washington, DC 20007
Tel: 202-800-5599
Fax: 202-478-0303



Project Name and Address
MARYLAND AVENUE

Location: **1250 MARYLAND AVENUE SW
WASHINGTON, DC 20024**

Contractor:
BALFOUR BEATTY


Approved for Fabrication by:	Signature
------------------------------	-----------

Contract # 224009	Drawing # E-08.02A
Contract Item: LEVEL-02 SLAB EXTENSION	
Ref: SOW-08:3,4,5&6 / S307	
Date 01/ 20/ 2025	Drawing Title: SOW #08 LEVEL-02 DETAIL VIEW
Scale VARIES	

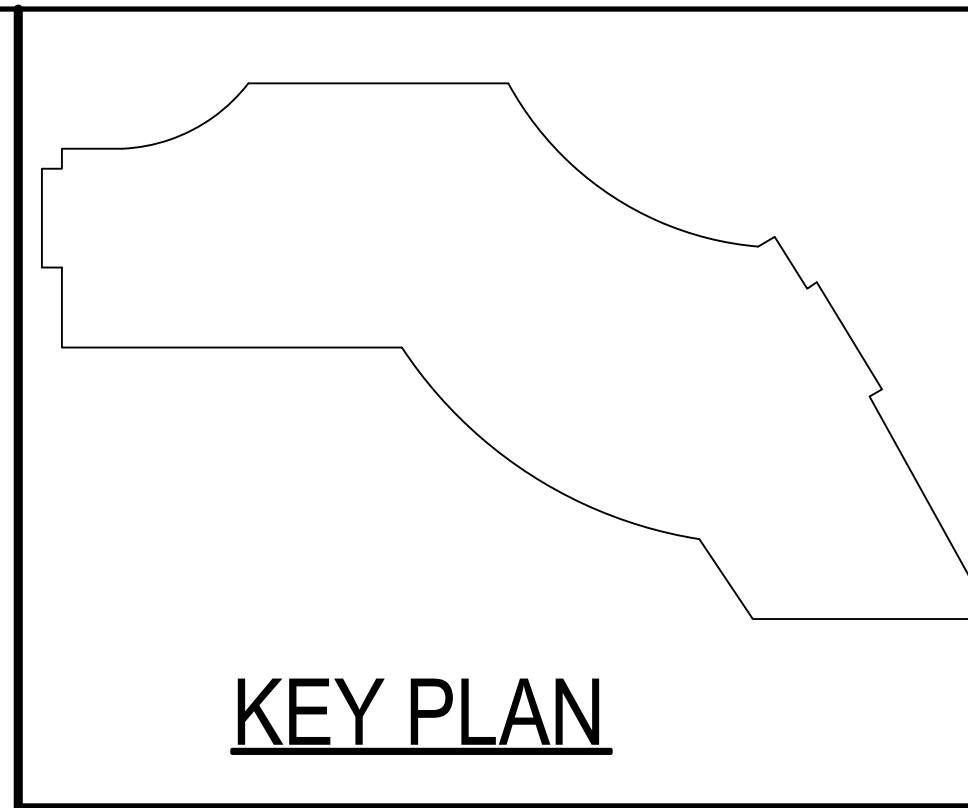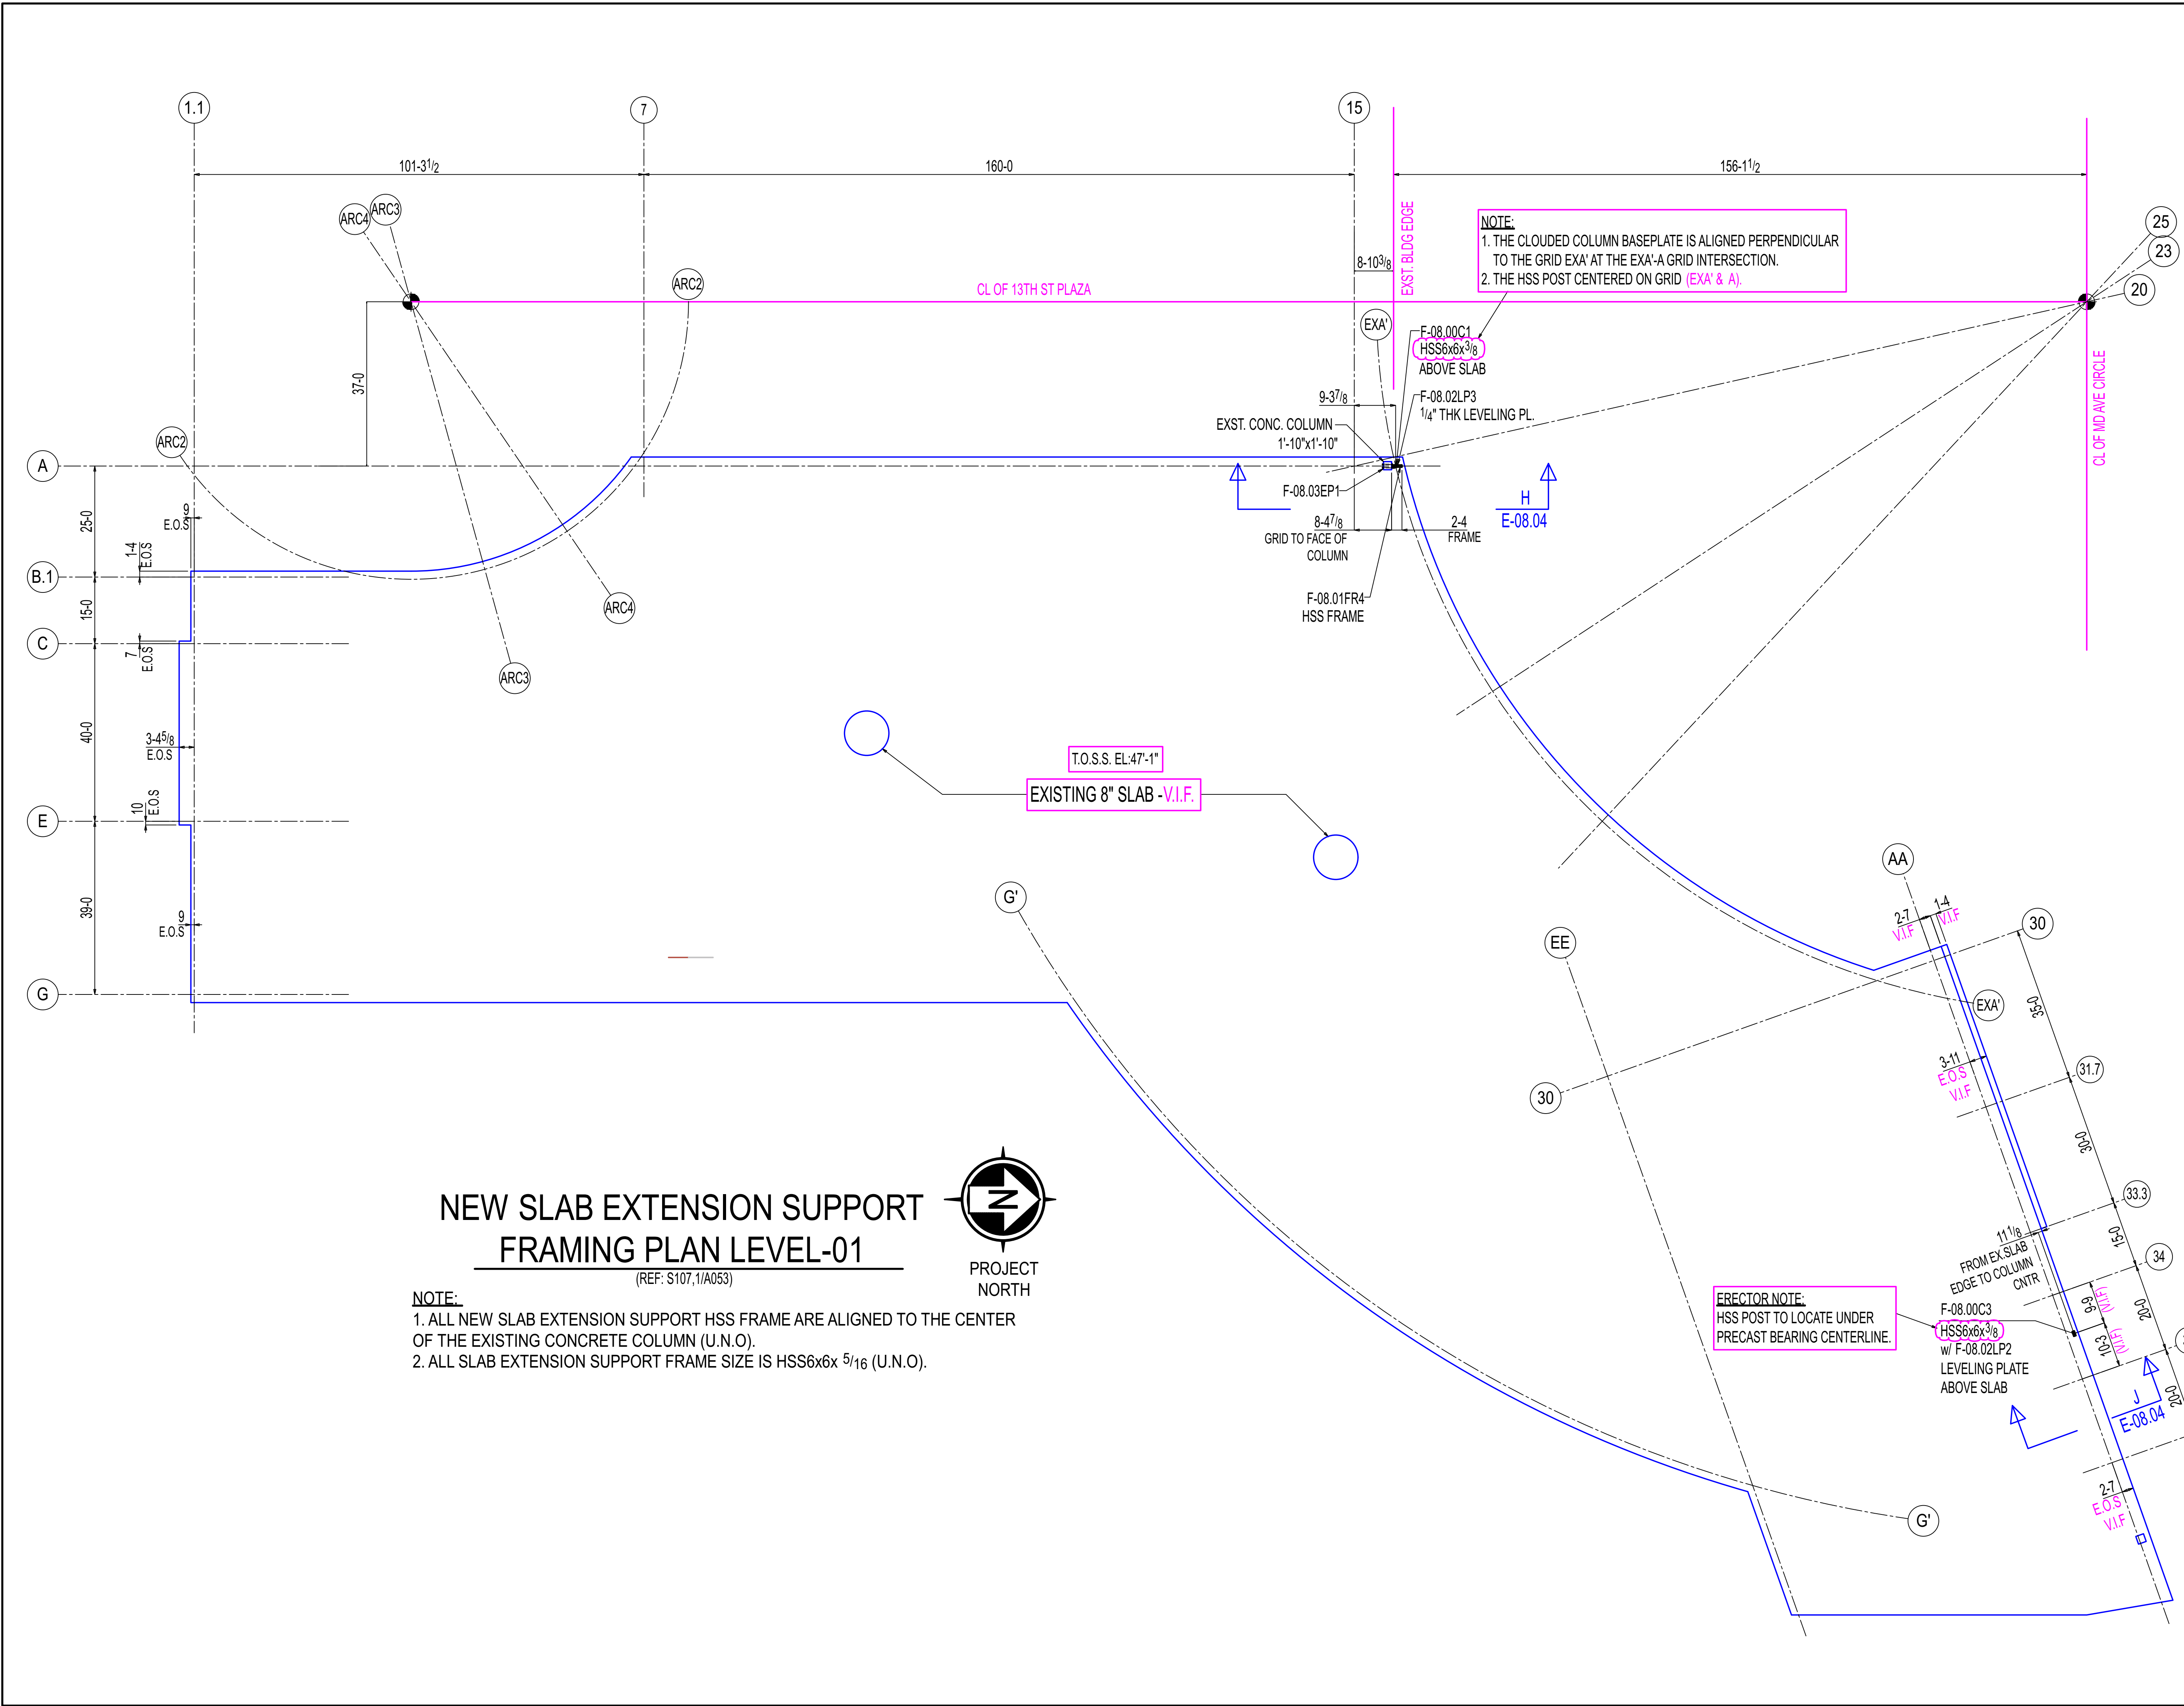

NEW SLAB EXTENSION SUPPORT FRAMING PLAN LEVEL-01

(REF: S107, 1/A053)

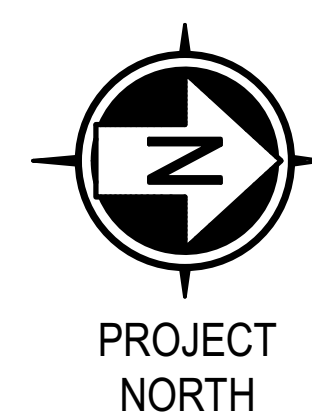

- NOTE:**
1. ALL NEW SLAB EXTENSION SUPPORT HSS FRAME ARE ALIGNED TO THE CENTER OF THE EXISTING CONCRETE COLUMN (U.N.O).
 2. ALL SLAB EXTENSION SUPPORT FRAME SIZE IS HSS6x6x 5/16 (U.N.O).

General Notes

- *Structural steel shall conform to ASTM-A992.
- *Structural SQR/RND.tubing conform to ASTM A500 Grade C
- *Pipe shall conform to ASTM A53, Grade B.
- *Channels, Angles and plates shall conform to A36.
- *All bolts shall be 3/4" High strength in accordance with ASTM A325 (UNO)
- *Welding Electrodes for Carbon steel :E70xx

# of Copies	Revision/ Issue	Destination	Date
5	0	For Construction	11-03-2025
4	D	For Re-Approval	10-24-2025
3	C	For Re-Approval	09-19-2025
2	B	For Re-Approval	08-23-2025
1	A	For Approval	02-25-2025

IRON FABRICATION SERVICES, LLC.

3029 M. Street, NW, Suite 202
Washington, DC 20007
Tel: 202-800-5599
Fax: 202-478-0303

Project Name and Address
MARYLAND AVENUE

Location: **1250 MARYLAND AVENUE SW
WASHINGTON, DC 20024**

Contractor:
BALFOUR BEATTY

Approved for Fabrication by: _____

Signature _____

Contract # **224009** Drawing # **E-08.03**





Contract Item: **LEVEL-01
SLAB EXTENSION**

Ref: **SOW-08:3,4,5&6 / S307**

Date
01/ 20/ 2025

Scale
VARIES

Drawing Title:
**SOW #08 LEVEL-01 NEW
SLAB EXTENSION SUPPORT
FRAMING**

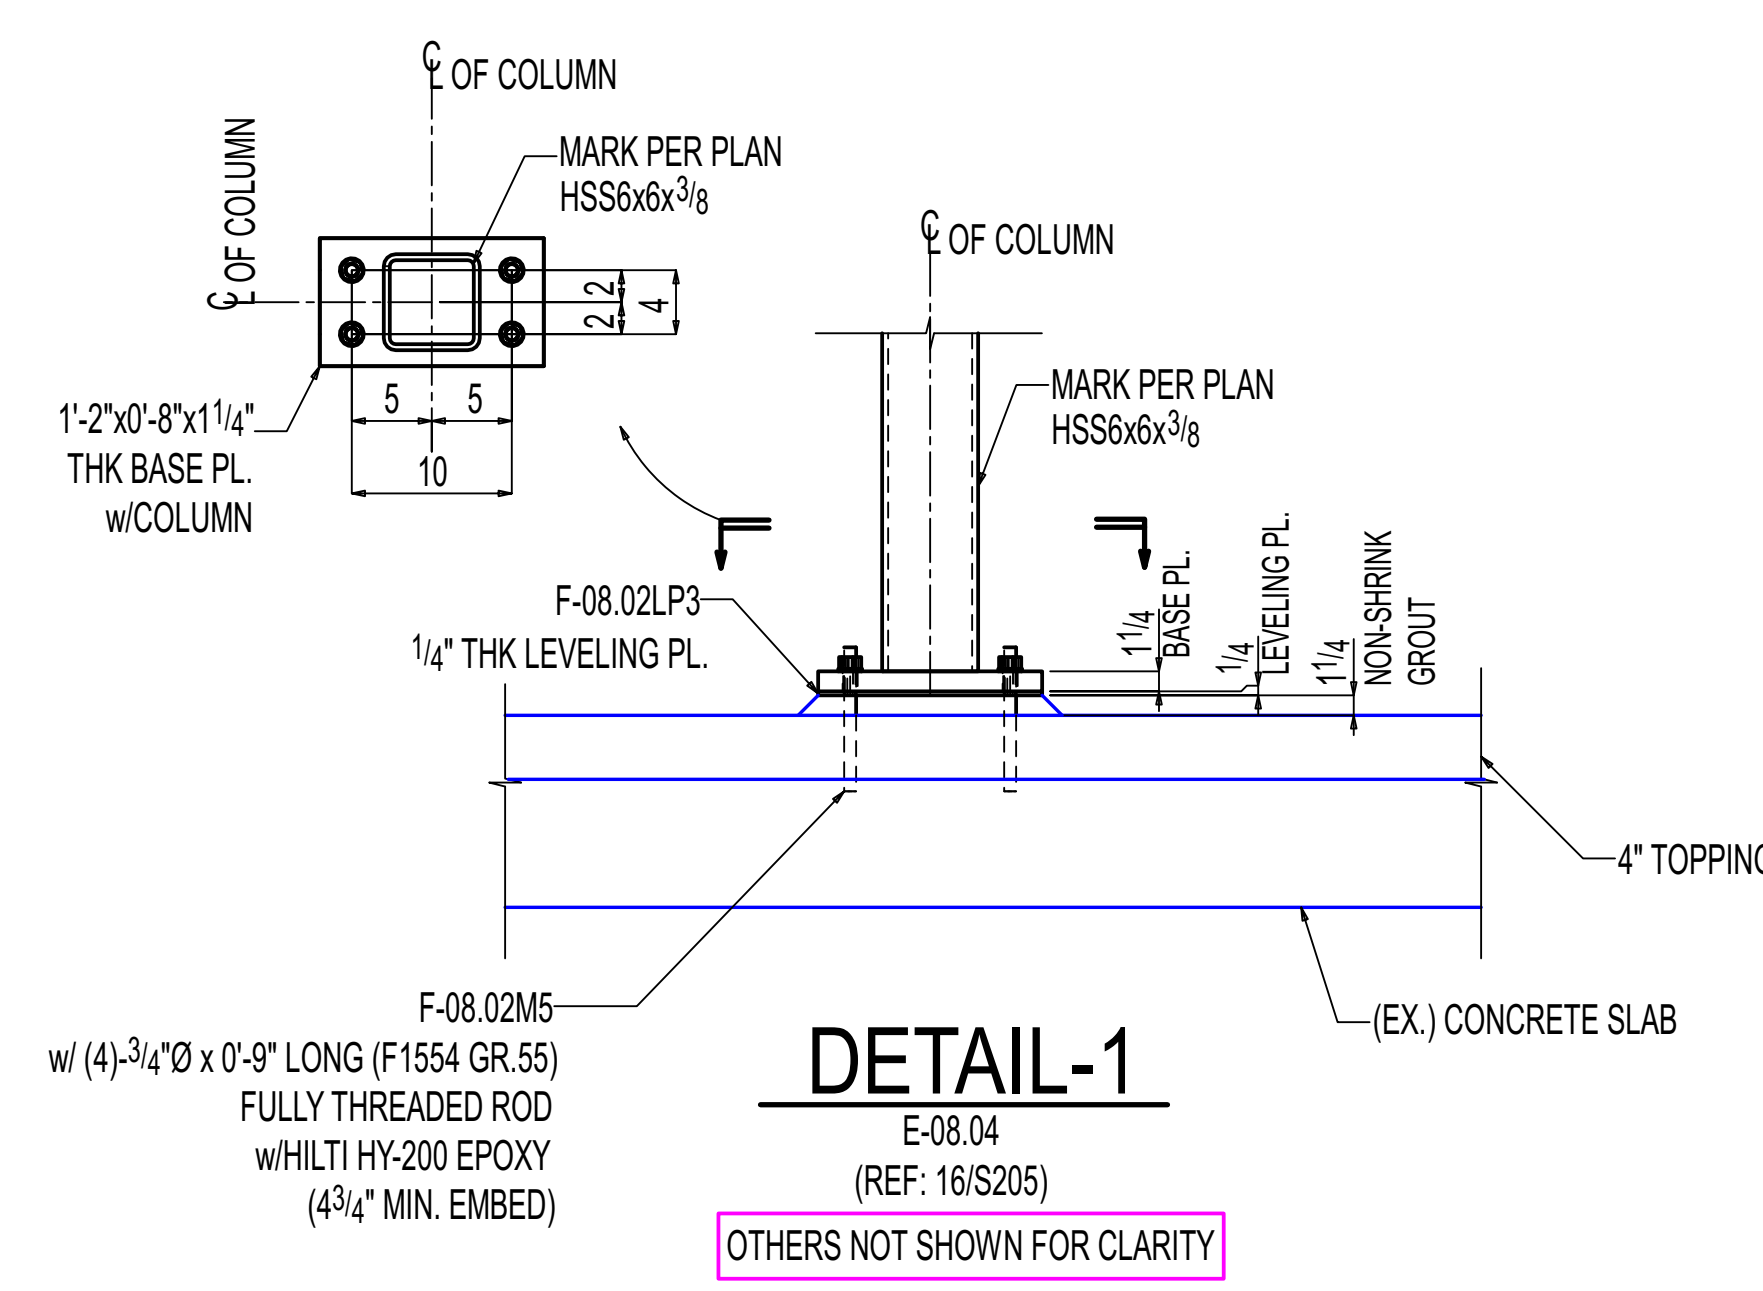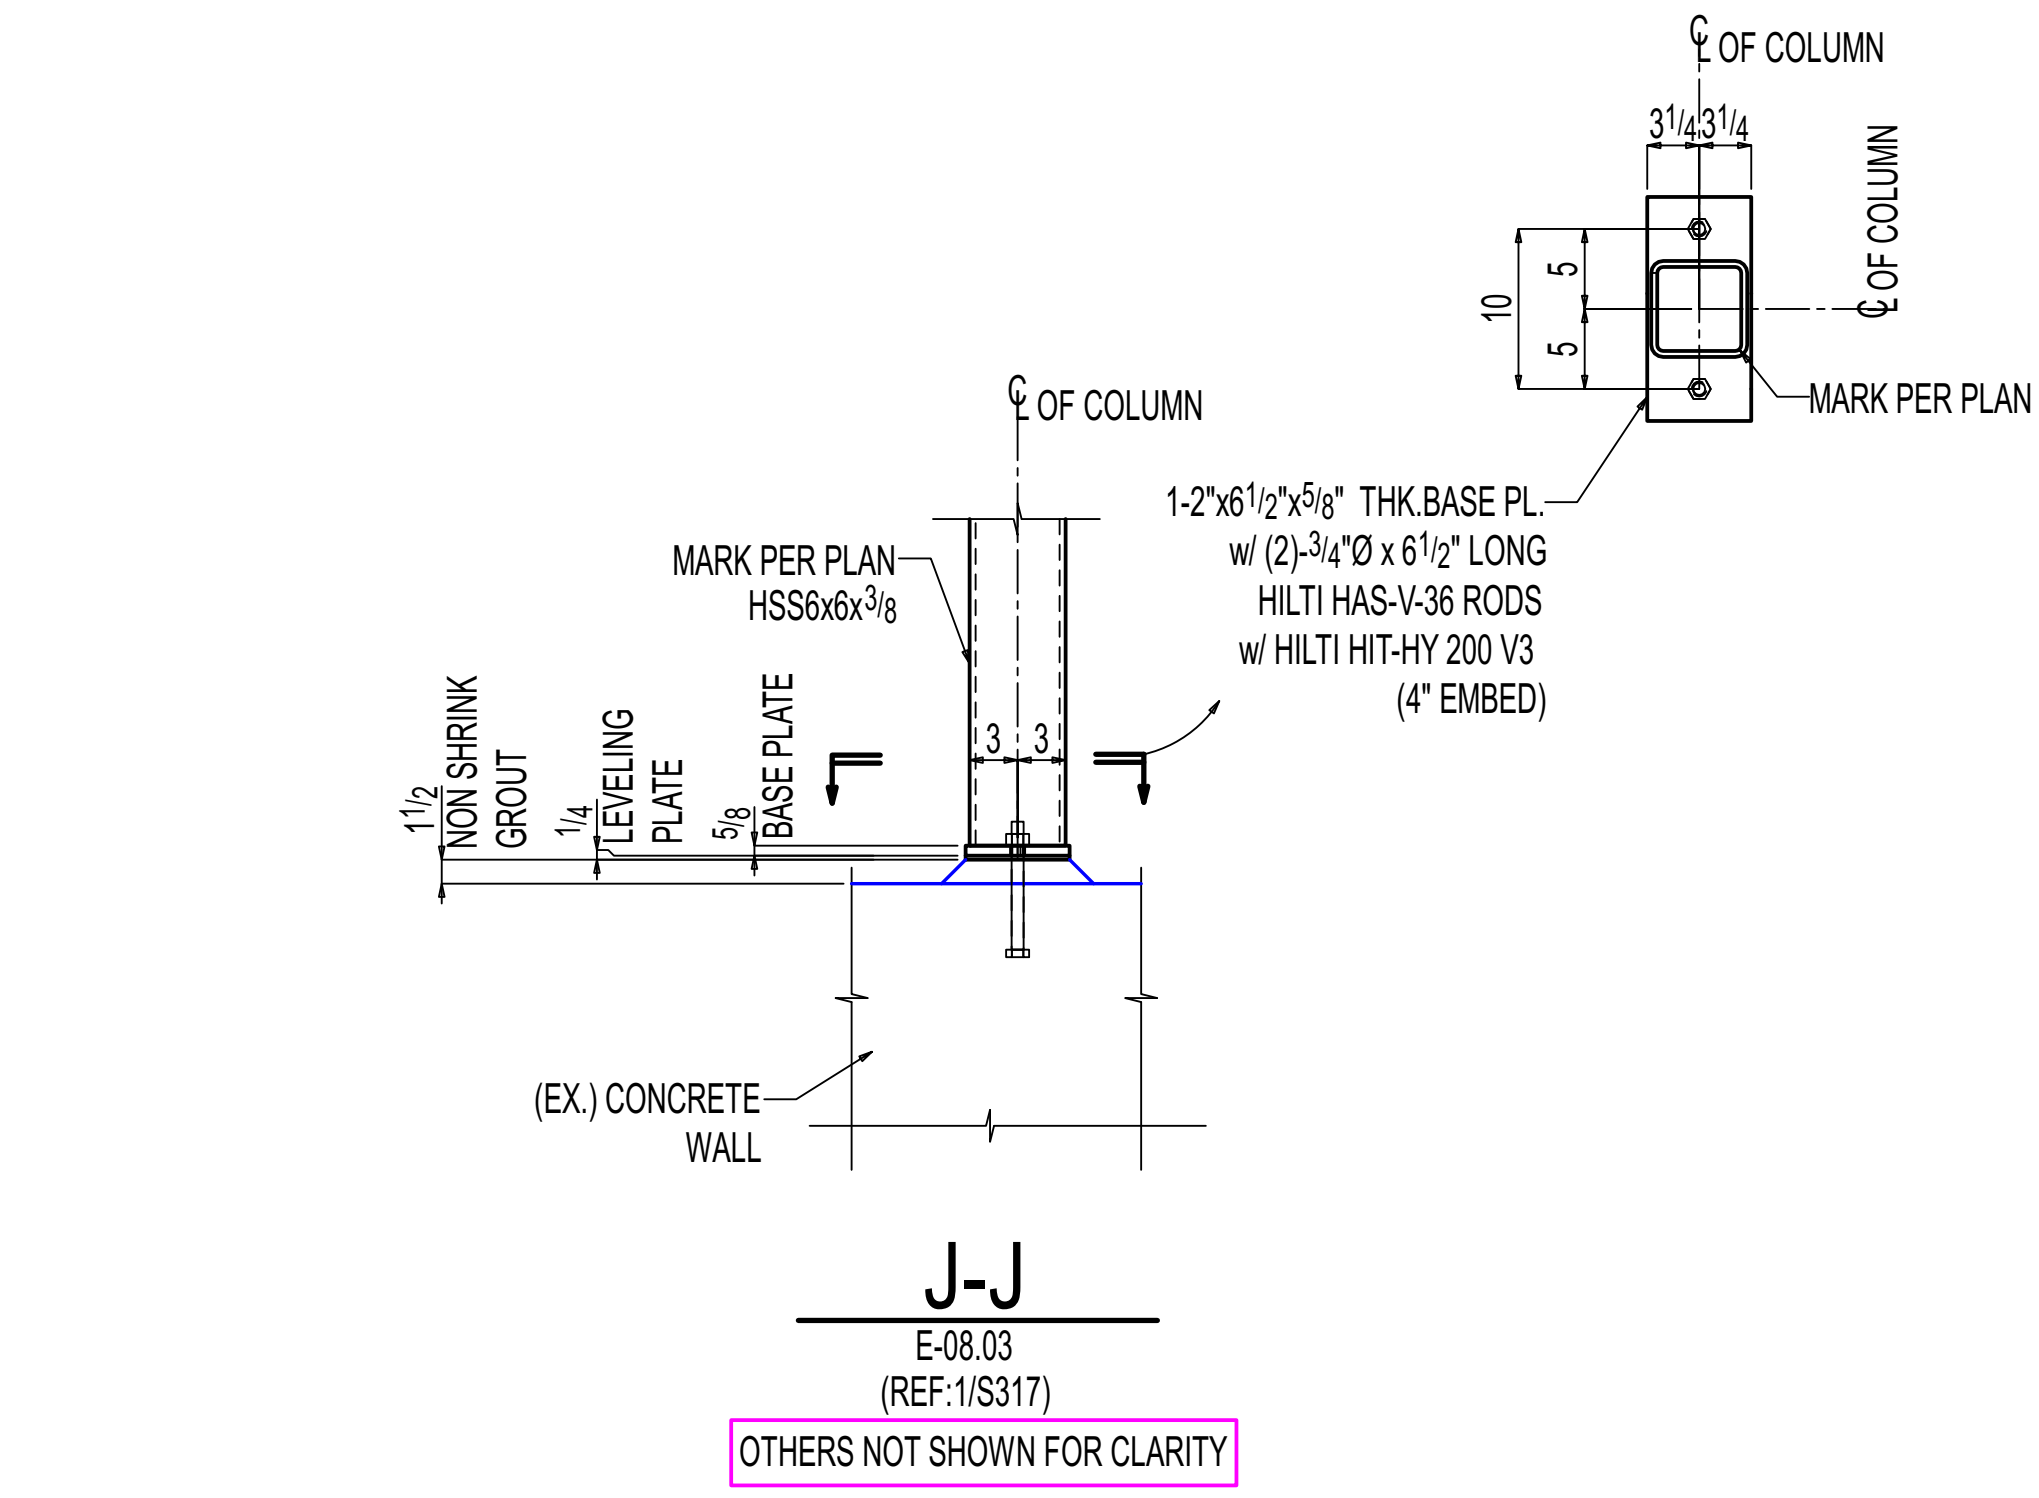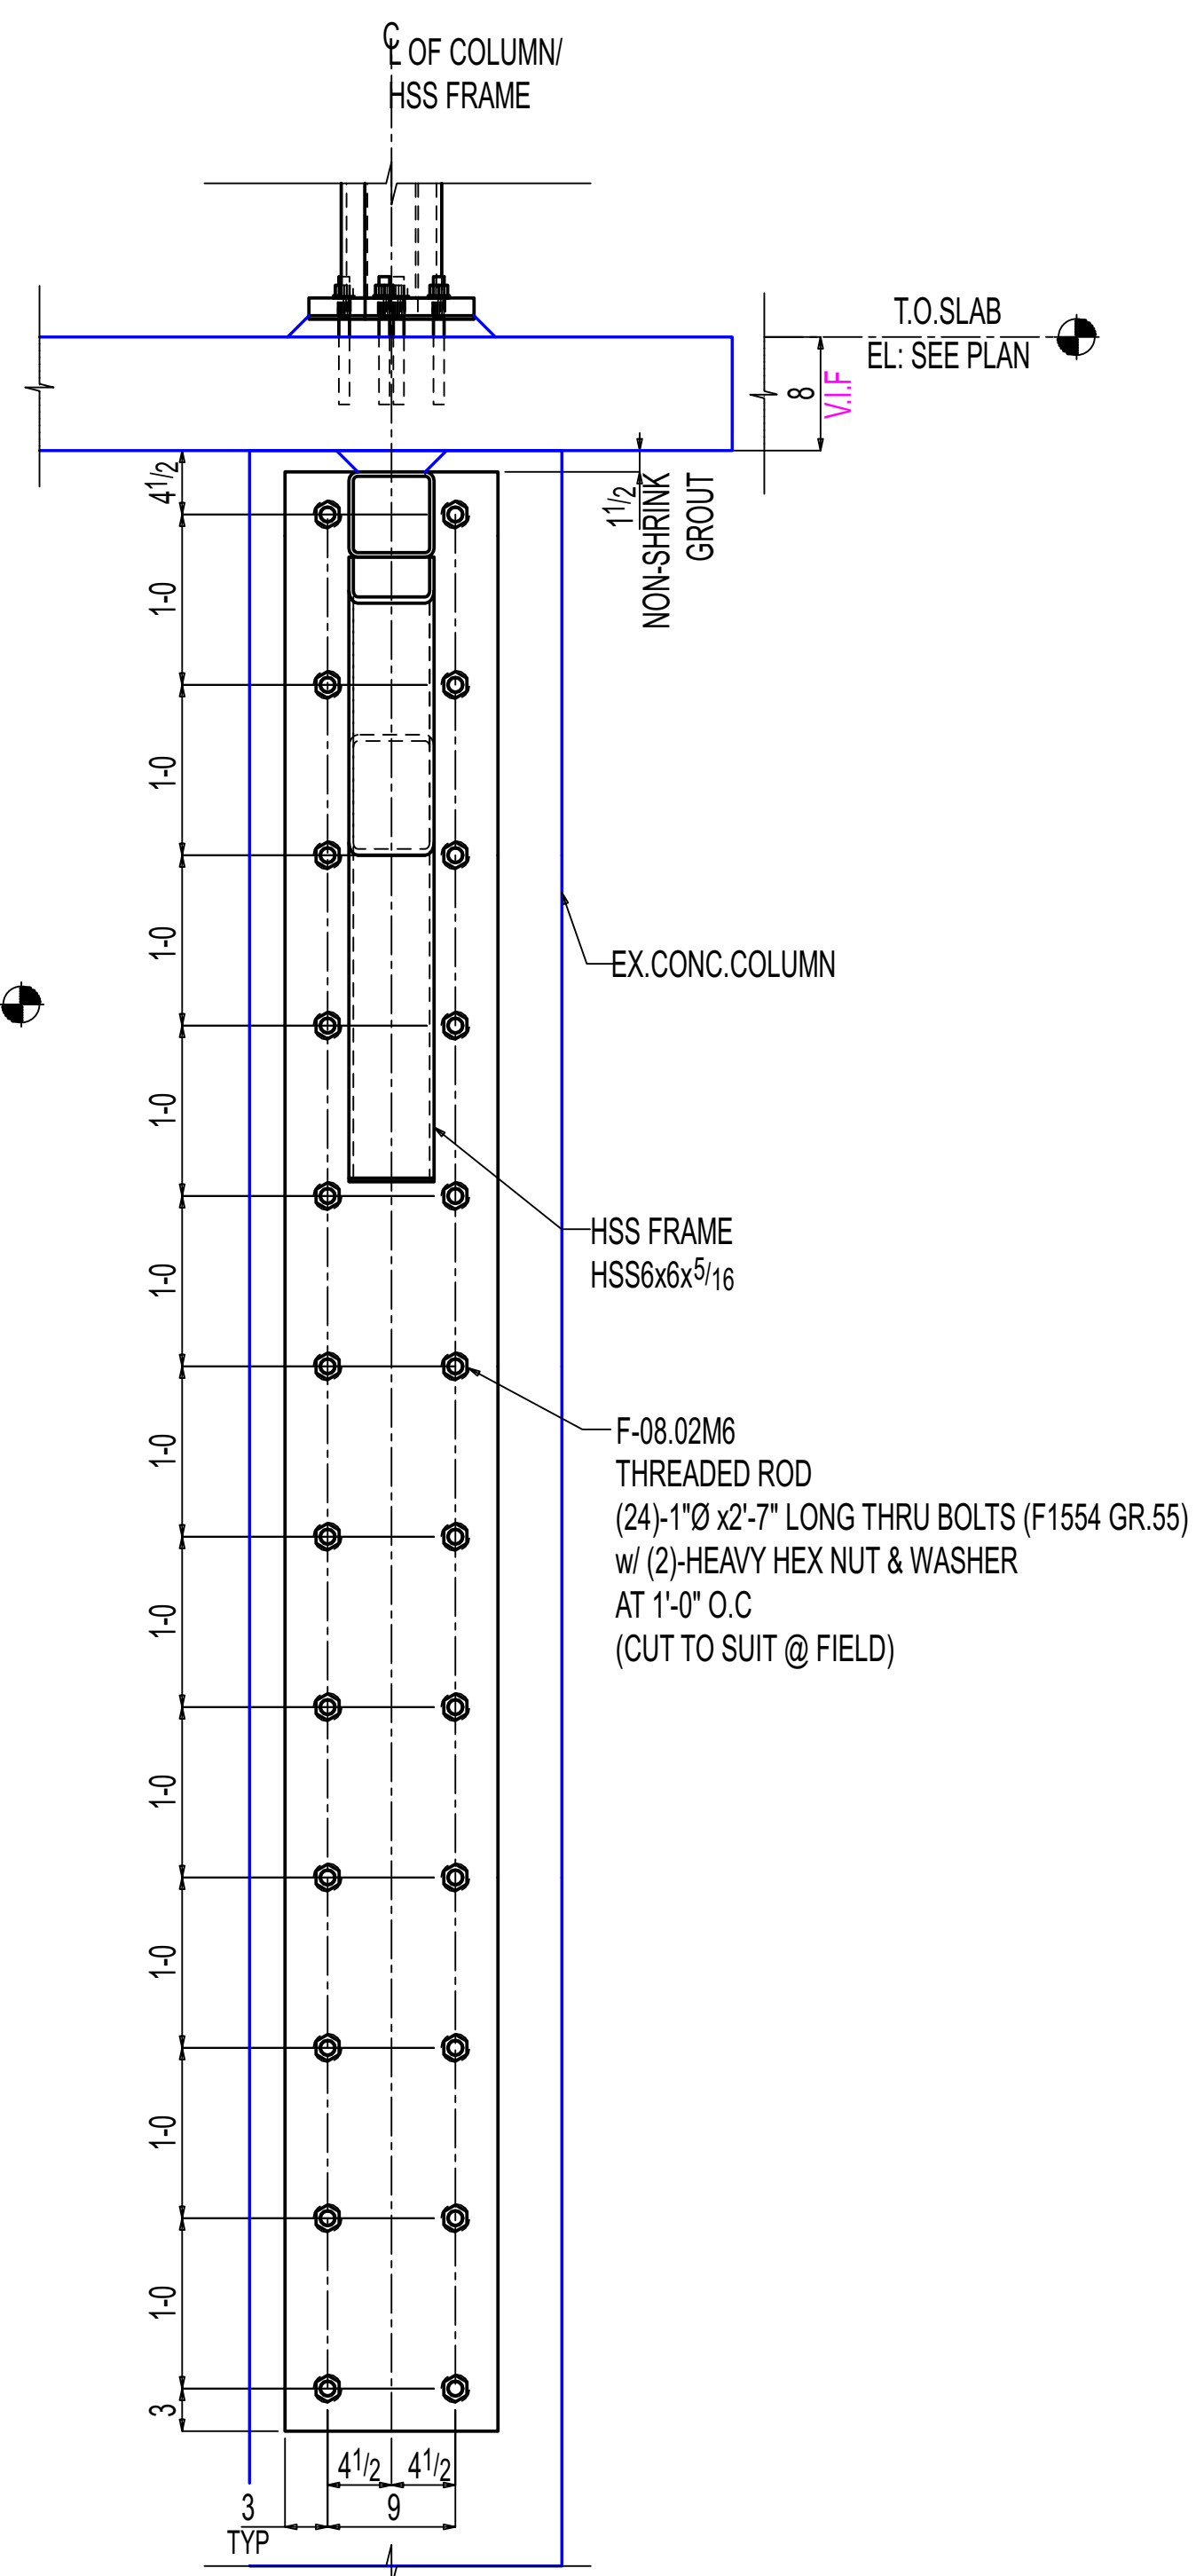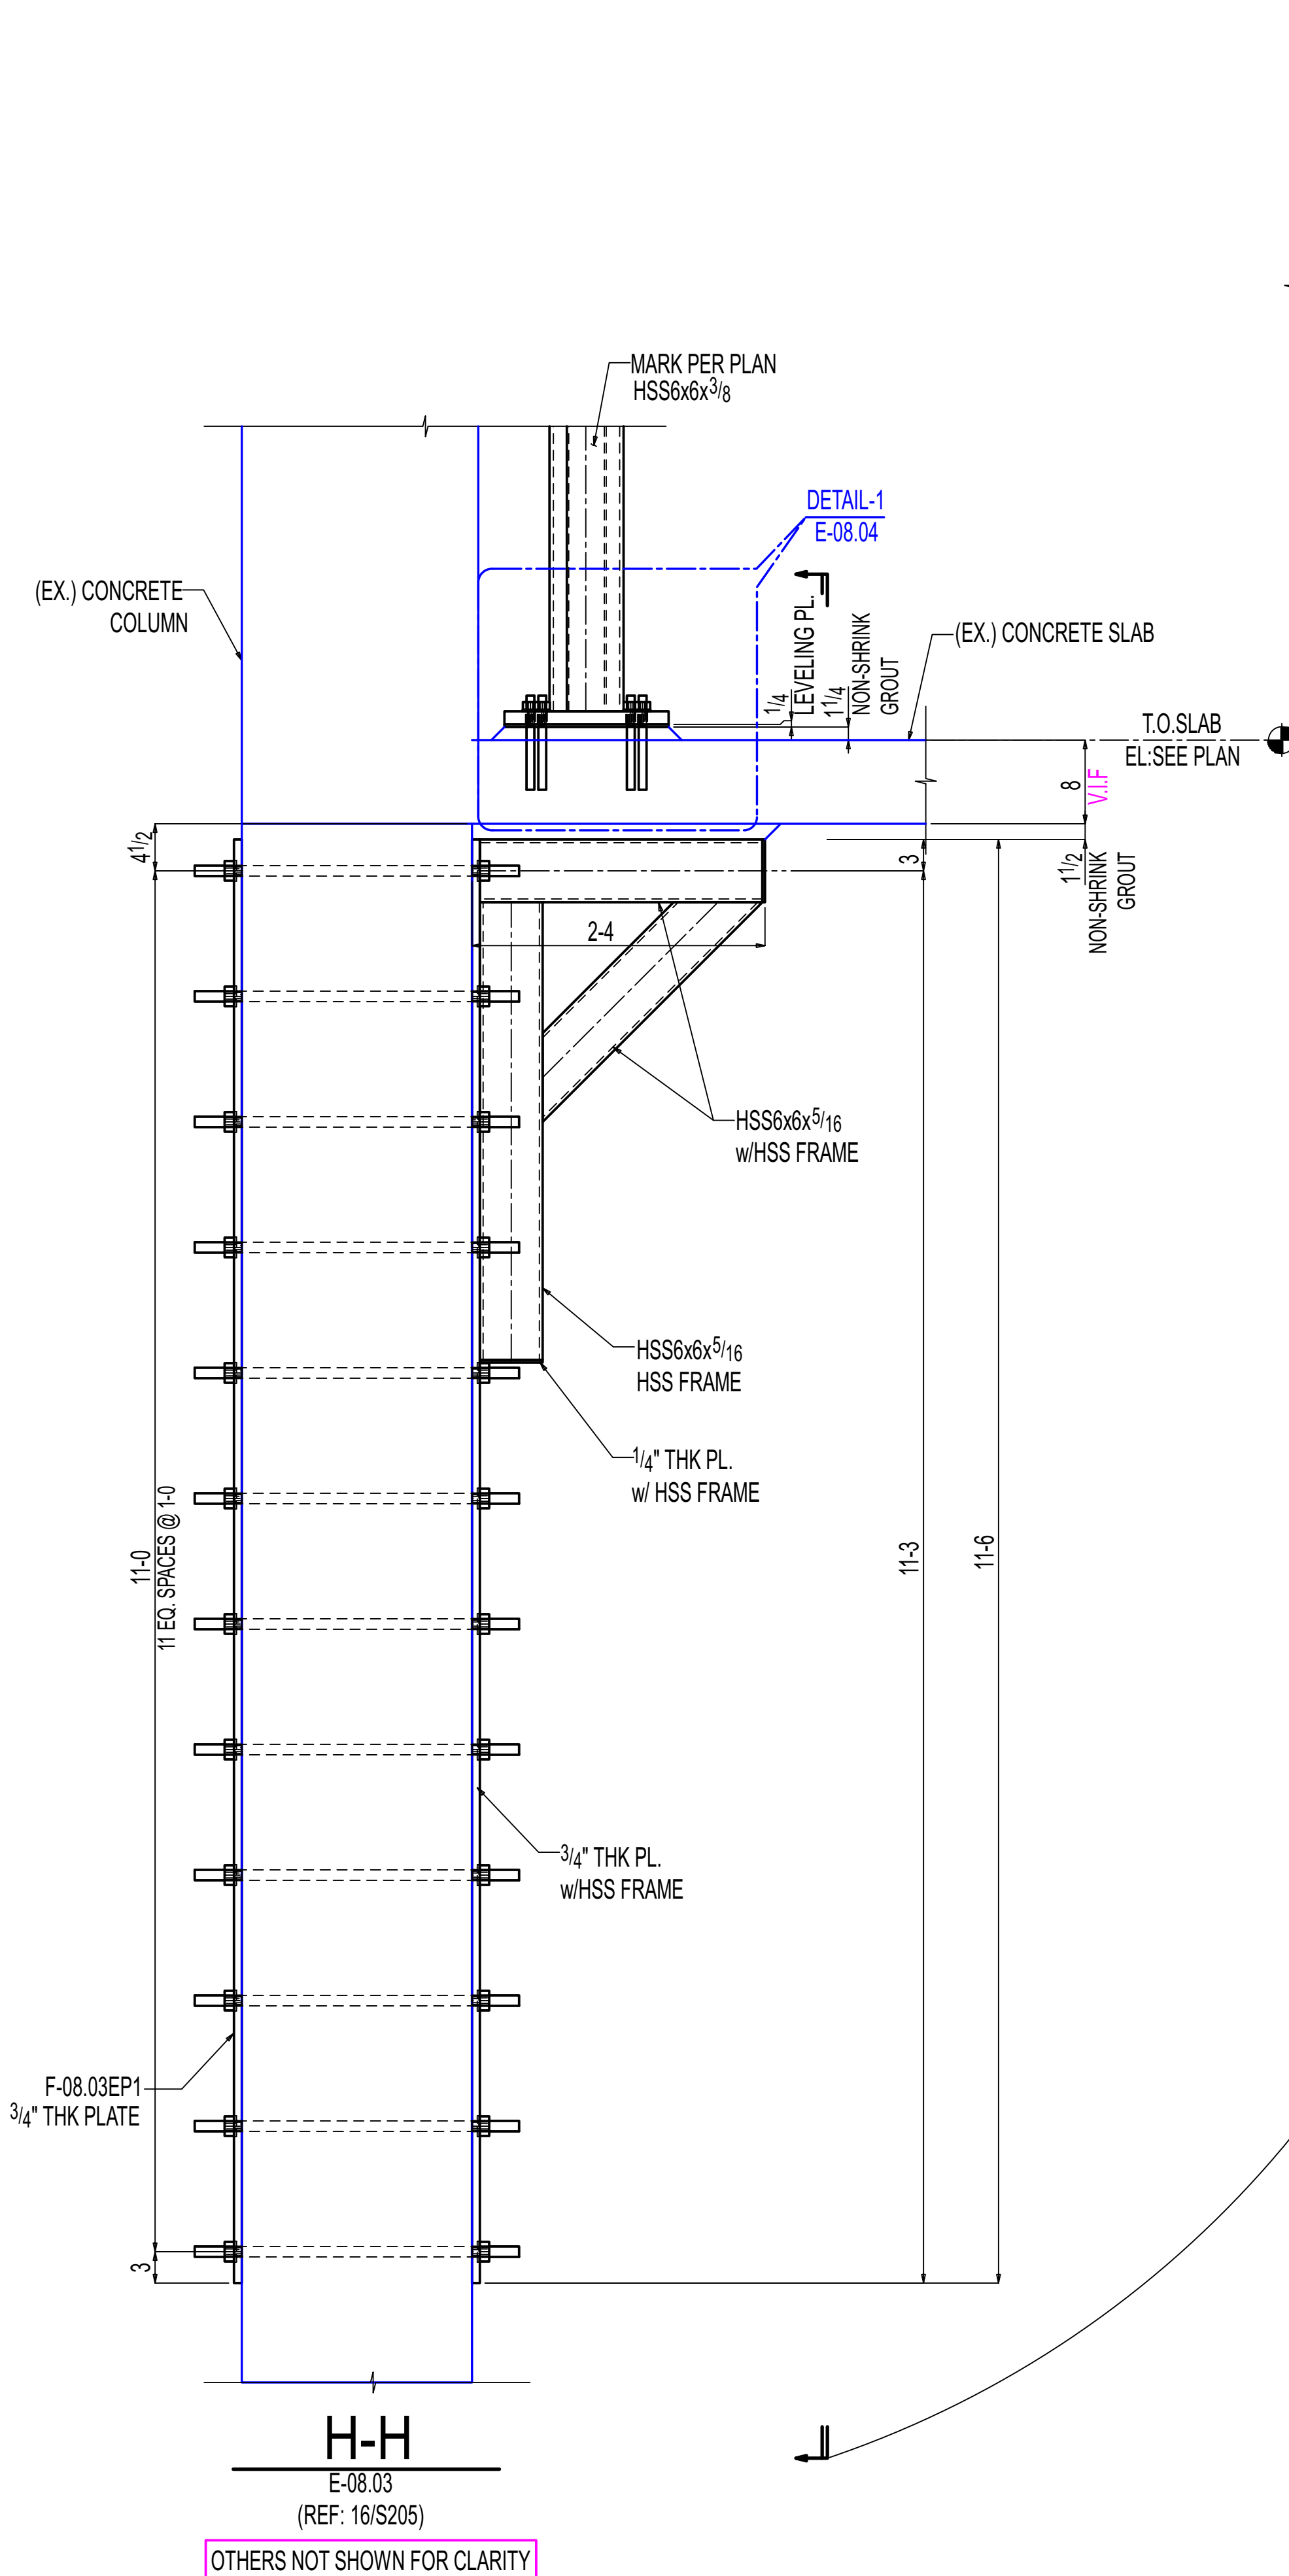

SHOP / ERECTOR NOTE:
LOCATE EXISTING REBAR PRIOR TO FABRICATION OF PLATE.
DO NOT DRILL THROUGH REBAR.

General Notes

*Structural steel shall conform to ASTM-A992.

*Structural SQR/RND,tubing conform to ASTM A500 Grade C

*Pipe shall conform to ASTM A53, Grade B.

*Channels, Angles and plates shall conform to A36.

*All bolts shall be 3/4" High strength in accordance with ASTM A325 (UNO)

*Welding Electrodes for Carbon steel :E70xx

5	0	For Construction	11-03-2025
4	D	For Re-Approval	10-24-2025
3	C	For Re-Approval	09-19-2025
2	B	For Re-Approval	06-23-2025
1	A	For Approval	02-25-2025
# of Copies	Revision/ Issue	Destination	Date

IRON FABRICATION SERVICES, LLC.

3029 M. Street, NW, Suite 202
Washington, DC 20007
Tel: 202-800-5599
Fax: 202-478-0303

Project Name and Address

MARYLAND AVENUE

Location: 1250 MARYLAND AVENUE SW
WASHINGTON, DC 20024

Contractor:

BALFOUR BEATTY

Approved for Fabrication by:

Signature

Contract #

224009

Drawing #

E-08.04

Contract Item:

LEVEL-01
SLAB EXTENSION

Ref:

SOW-08:3,4,5&6 / S307

Date

01/20/2025

Drawing Title:

SOW #08 LEVEL-01 NEW
SLAB EXTENSION SUPPORT
SECTIONS

Scale

VARIES




NOTE:

1. ALL SLAB EXTENSION SUPPORT HSS FRAMES ARE FOR THE CENTER OF THE EXISTING CONCRETE COLUMN (U.N.O).
2. ALL SLAB EXTENSION SUPPORT FRAME SIZE IS HSS5x5x $\frac{3}{8}$ (U.N.O).



NOTE

* - HSS POST LOCATION SHOULD BE CO-ORDINATE WITH PRECAST MANUFACTURER FOR PRECAST BEARING LOCATION

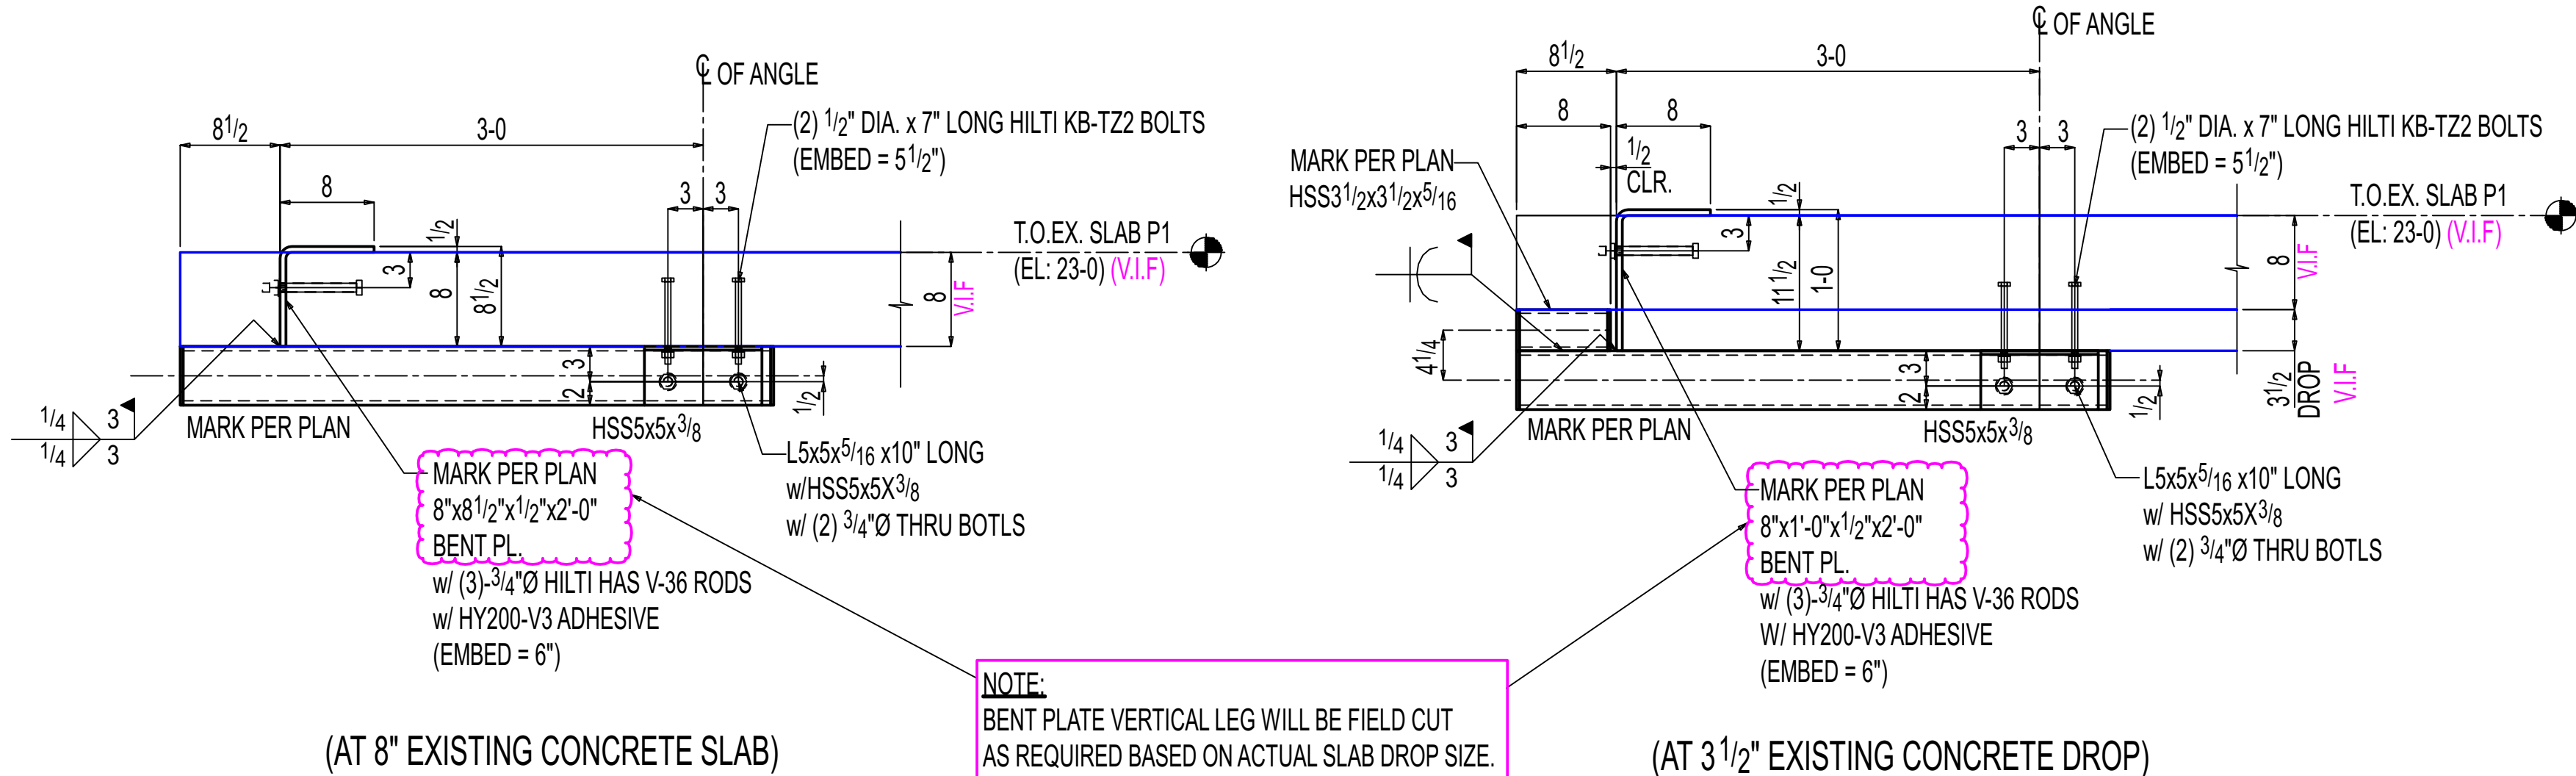

TYPICAL HSS OUTRIGGER SUPPORT PRECAST DETAIL

General Notes			
*Structural steel shall conform to ASTM-A992.			
*Structural SQR/RND.tubing conform to ASTM A500 Grade C			
*Pipe shall conform to ASTM A53, Grade B.			
*Channels, Angles and plates shall conform to A36.			
*All bolts shall be 3/4" High strength in accordance with ASTM A325 (UNO)			
*Welding Electrodes for Carbon steel :E70xx			
3	0	For Construction	11-03-2025
2	B	For Re-Approval	10-24-2025
1	A	For Approval	09-19-2025
# of Copies	Revision/ Issue	Destination	Date

IRON FABRICATION SERVICES, LLC.

3029 M. Street, NW, Suite 202
Washington, DC 20007
Tel: 202-800-5599
Fax: 202-478-0303

Project Name and Address
MARYLAND AVENUE

Location: **1250 MARYLAND AVENUE SW**
WASHINGTON, DC 20024

Contractor:

BALFOUR BEATTY

Approved for Fabrication by _____

Signature

Contract # **224009**Drawing # **E-08.05**

Contract Item:	LEVEL-P1 SLAB EXTENSION
----------------	------------------------------------

Ref: **SOW-08:S104,5/S315**

Date	01/20/2025
Scale	

Drawing Title:

**SOW #08 LEVEL-P1 NEW
SLAB EXTENSION SUPPORT
PLAN & SECTIONS**