


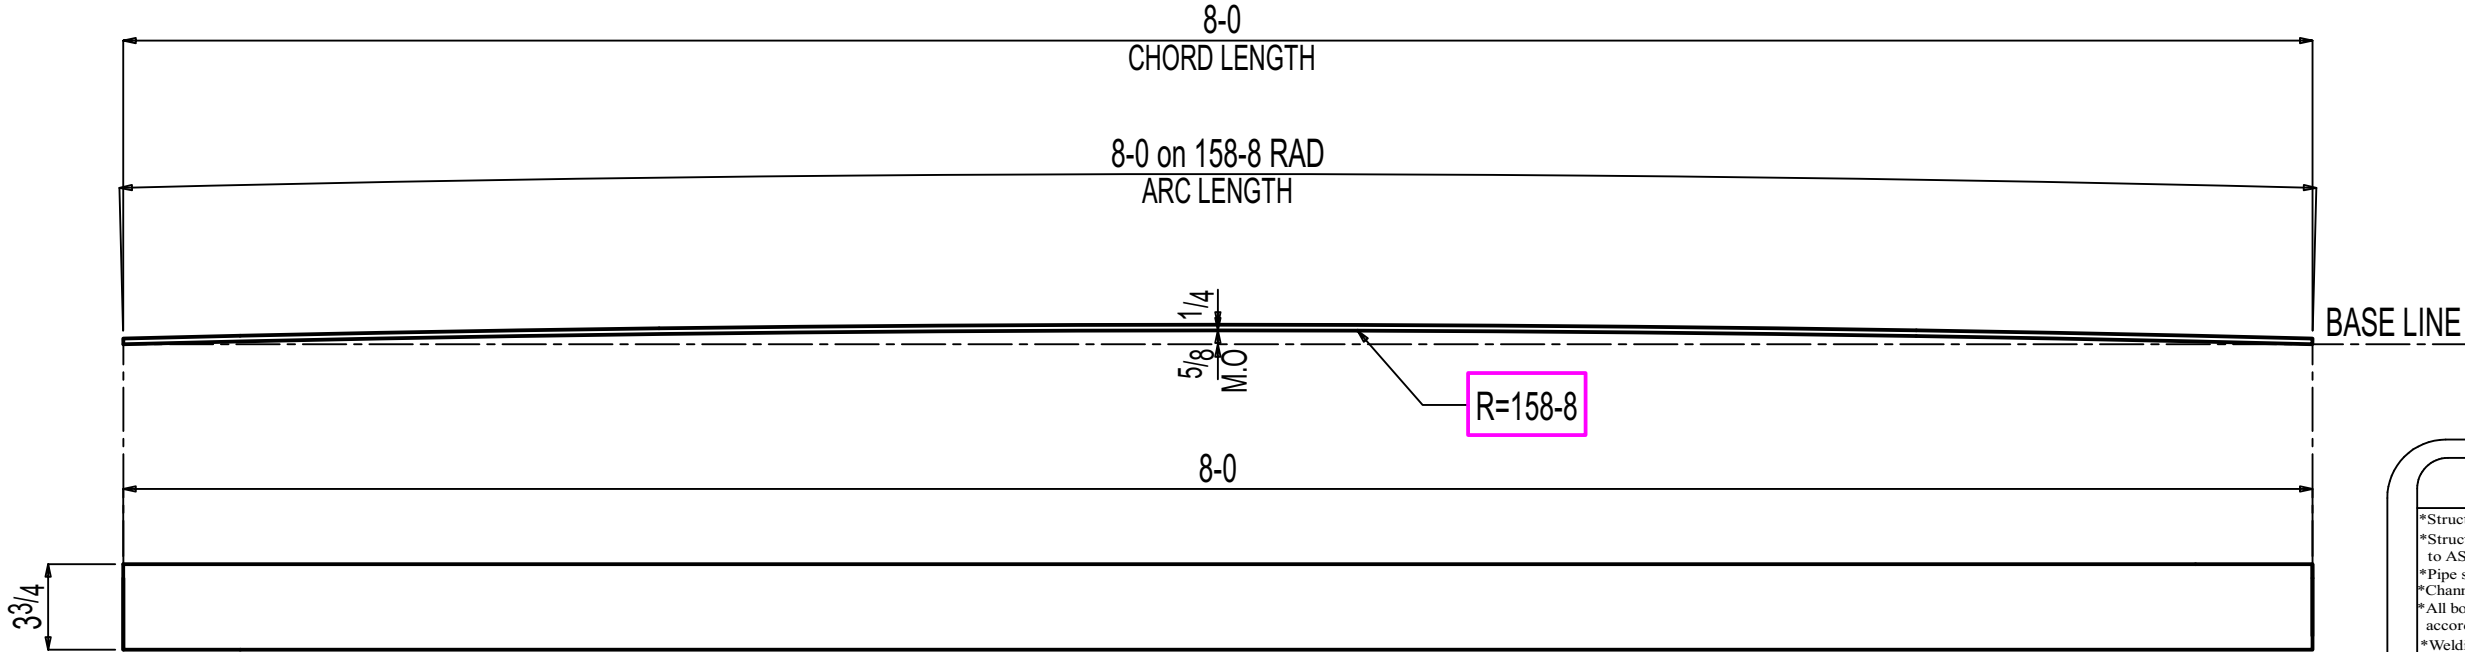

ONE FL 1/4x3 3/4x8-0 fb143

GRADE: A36

General Notes			
*Structural steel shall conform to ASTM-A992.			
*Structural SQR/RND.tubing conform to ASTM A500 Grade C			
*Pipe shall conform to ASTM A53, Grade B.			
*Channels, Angles and plates shall conform to A36.			
*All bolts shall be 3/4" High strength in accordance with ASTM A325 (UNO)			
*Welding Electrodes for Carbon steel :E70xx			
*Structural members are to be shop primer (U.N.O).			
*Surface Preparation-SSPC-SP3 UNO.			
*If welds exposed to view, should be ground smooth.			
1	0	FOR FABRICATION	11-14-2025
# of Copies	Revision/ Issue	Destination	Date

IRON FABRICATION SERVICES, LLC.

3029 M. Street, NW, Suite 202
Washington, DC 20007
Tel: 202-800-5599
Fax: 202-478-0303

Project Name and Address

MARYLAND AVENUE

Location: 1250 MARYLAND AVENUE SW
WASHINGTON, DC 20024

Contractor:

BALFOUR BEATTY

Approved for Fabrication by:	Signature

Contract #	224009	Drawing #	fb143
Contract Item: PLATE			
Ref: SOW -09:F-09.00-F-09.06			
Date 01/ 23/ 2025	Drawing Title: PLATE		
Scale VARIES			

HOLE:13/16 Ø (U.N.O)