

BILL OF MATERIAL							
LINE #	QTY TOTAL	PC MARK	DESCRIPTION	LENGTH	REMARKS	WEIGHT TOTAL	ADVANCE MILL #
	4	F-10.00FR1	FRAME			990	
		F-10.00FR1	HSS6x6x ³ / ₁₆	3 5 ³ / ₄	A500C	325	
	4	w2766	V8x31	1 4	A992	165	
	4	p341	PL ¹ / ₂ x16	4 6	A36	490	
	4	p692	PL ¹ / ₄ x6	0 6	A36	10	
	ONE	F-10.00FR2	FRAME			293	
	1	F-10.00FR2	HSS6x6x ³ / ₁₆	3 7 ³ / ₄	A500C	85	
	1	hss261	HSS6x6x ³ / ₁₆	1 9 ⁷ / ₈	A500C	43	
	1	hss260	HSS6x6x ³ / ₁₆	1 7 ³ / ₈	A500C	38	
	1	p341	PL ¹ / ₂ x16	4 6	A36	123	
	2	p692	PL ¹ / ₄ x6	0 6	A36	5	
	ONE	F-10.00FR3	FRAME			210	
	1	F-10.00FR3	HSS6x6x ³ / ₁₆	3 7 ³ / ₄	A500C	85	
	1	p341	PL ¹ / ₂ x16	4 6	A36	123	
	1	p692	PL ¹ / ₄ x6	0 6	A36	5	
	ONE	F-10.00FR4	FRAME			356	
	1	F-10.00FR4	HSS6x6x ³ / ₁₆	3 7 ¹ / ₈	A500C	84	
	1	hss3790	HSS6x6x ³ / ₁₆	3 6 ³ / ₄	A500C	83	
	1	hss2698	HSS6x6x ³ / ₁₆	2 6 ¹ / ₄	A500C	59	
	1	p341	PL ¹ / ₂ x16	4 6	A36	123	
	3	p692	PL ¹ / ₄ x6	0 6	A36	8	

Total weight : 1849



PAINT	:NO PAINT
PREPARATION	:SSPC-SP3

- *Structural steel shall conform to ASTM-A992.
- *Structural SQR/RND.tubing conform to ASTM A500 Grade C
- *Pipe shall conform to ASTM A53, Grade B.
- *Channels, Angles and plates shall conform to A36.
- *All bolts shall be 3/4" High strength in accordance with ASTM A325 (UNO)
- *Welding Electrodes for Carbon steel :E70xx

5	0	For Fabrication	11-14-2025
4	D	For Re-Approval	10-24-2025
3	C	For Re-Approval	09-19-2025
2	B	For Re-Approval	06-23-2025
1	A	For Approval	02-25-2025
# of Copies	Revision/ Issue	Destination	Date

IRON FABRICATION SERVICES, LLC.

3029 M. Street, NW, Suite 202
Washington, DC 20007
Tel: 202-800-5599
Fax: 202-478-0303

Project Name and Address
MARYLAND AVENUE

Location: **1250 MARYLAND AVENUE SW**
WASHINGTON, DC 20024

Contractor: **BALFOUR BEATTY**

Approved for Fabrication by:	Signature
------------------------------	-----------

Contract # 224009	Drawing # F-10.00
--------------------------	--------------------------

Contract Item: **FRAME**

Ref:


SOW - 10: E-10.00 - E-10.02

Date 01/ 23/ 2025	Drawing Title: FRAME DETAIL
----------------------	---------------------------------------


Scale	
VARIES	

BILL OF MATERIAL							
LINE #	QTY	PC	MARK	DESCRIPTION	LENGTH	REMARKS	ADVANCE MILL #
ONE	TOTAL	F-10.01FR1	FRAME				437
1		F-10.01FR1	HSS6x6x $\frac{9}{16}$		3 $\frac{73}{4}$	A500C	85
1		hss297	HSS6x6x $\frac{9}{16}$		4 $\frac{111}{8}$	A500C	115
1		hss398	HSS6x6x $\frac{9}{16}$		4 8	A500C	109
1		p341	PL $\frac{1}{2}$ x16		4 6	A36	123
1		p3235	PL $\frac{1}{2}$ x6		0 $\frac{71}{16}$	A36	3
1		p692	PL $\frac{1}{2}$ x6		0 6	A36	3
ONE		F-10.01FR2	FRAME				315
1		F-10.01FR2	HSS6x6x $\frac{9}{16}$		3 $\frac{73}{4}$	A500C	85
1		hss3795	HSS6x6x $\frac{9}{16}$		2 $\frac{11}{8}$	A500C	49
1		hss1586	HSS6x6x $\frac{9}{16}$		1 $\frac{113}{4}$	A500C	46
1		p3618	PL $\frac{1}{2}$ x16		4 9	A36	129
2		p692	PL $\frac{1}{2}$ x6		0 6	A36	5
ONE		F-10.01M1	PLATE				189
1		F-10.01M1	PL1x18		2 1	A36	128
1		p232	PL1x8		1 6	A36	41
3		p353	PL $\frac{1}{2}$ x7		0 7	A36	21
ONE		F-10.01M2	PLATE				37
1		F-10.01M2	PL $\frac{3}{4}$ x6		1 3	A36	19
2		p3243	PL $\frac{3}{4}$ x6		0 7	A36	18
ONE		F-10.01M3	HSS				29
1		F-10.01M3	HSS5 $\frac{1}{2}$ x5 $\frac{1}{2}$ x $\frac{5}{16}$		1 $\frac{15}{8}$	A500C	24
2		p3226	PL $\frac{1}{2}$ x5 $\frac{1}{2}$		0 6	A36	5
6		F-10.01M4	PLATE WASHER				8
6		F-10.01M4	PL $\frac{1}{2}$ x3		0 3	A36	8
6		F-10.01M5	THREADED ROD				16
6		F-10.01M5	1" Ø THREADED ROD		1 0	F1554 GR.55	16
			w/ HILTI HIT HY-200 V3			(8" EMBED)	
			ADHESIVE				
6			FIELD BOLTS				
1			1 NUT			HHNT A563	
72		F-10.01M6	THREADED ROD				136
72		F-10.01M6	1" Ø THREADED ROD		0 $\frac{81}{2}$	F1554 GR.55	136
			w/ HILTI HIT HY-200 V3			(6" EMBED)	
			ADHESIVE				
72			1 NUT			HHNT A563	
72			1 WASHER			HD F436	
ONE		F-10.01M7	HSS				166
1		F-10.01M7	HSS6x3x $\frac{9}{16}$		9 $\frac{71}{2}$	A500C	163
2		p486	PL $\frac{1}{2}$ x3		0 6	A36	3
ONE		F-10.01EP1	EMBED PLATE				230
1		F-10.01EP1	PL5 $\frac{1}{8}$ x22		4 11	A36	230
			FIELD BOLTS				
10			$\frac{3}{4}$ Dia HILTI HAS V-36		0 8	(5" EMBED)	
			w/ HILTI HIT HY-200 V3				
			ADHESIVE				
ONE		F-10.01LP1	LEVELING PLATE				9
1		F-10.01LP1	PL $\frac{1}{2}$ x7		1 6	A36	9
ONE		F-10.01LP2	LEVELING PLATE				8
1		F-10.01LP2	PL $\frac{1}{2}$ x6 $\frac{1}{2}$		1 6	A36	8


Total weight : 1580

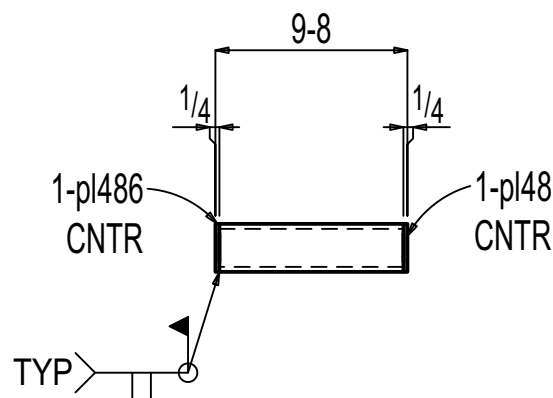


ONE HSS F-10.01M7

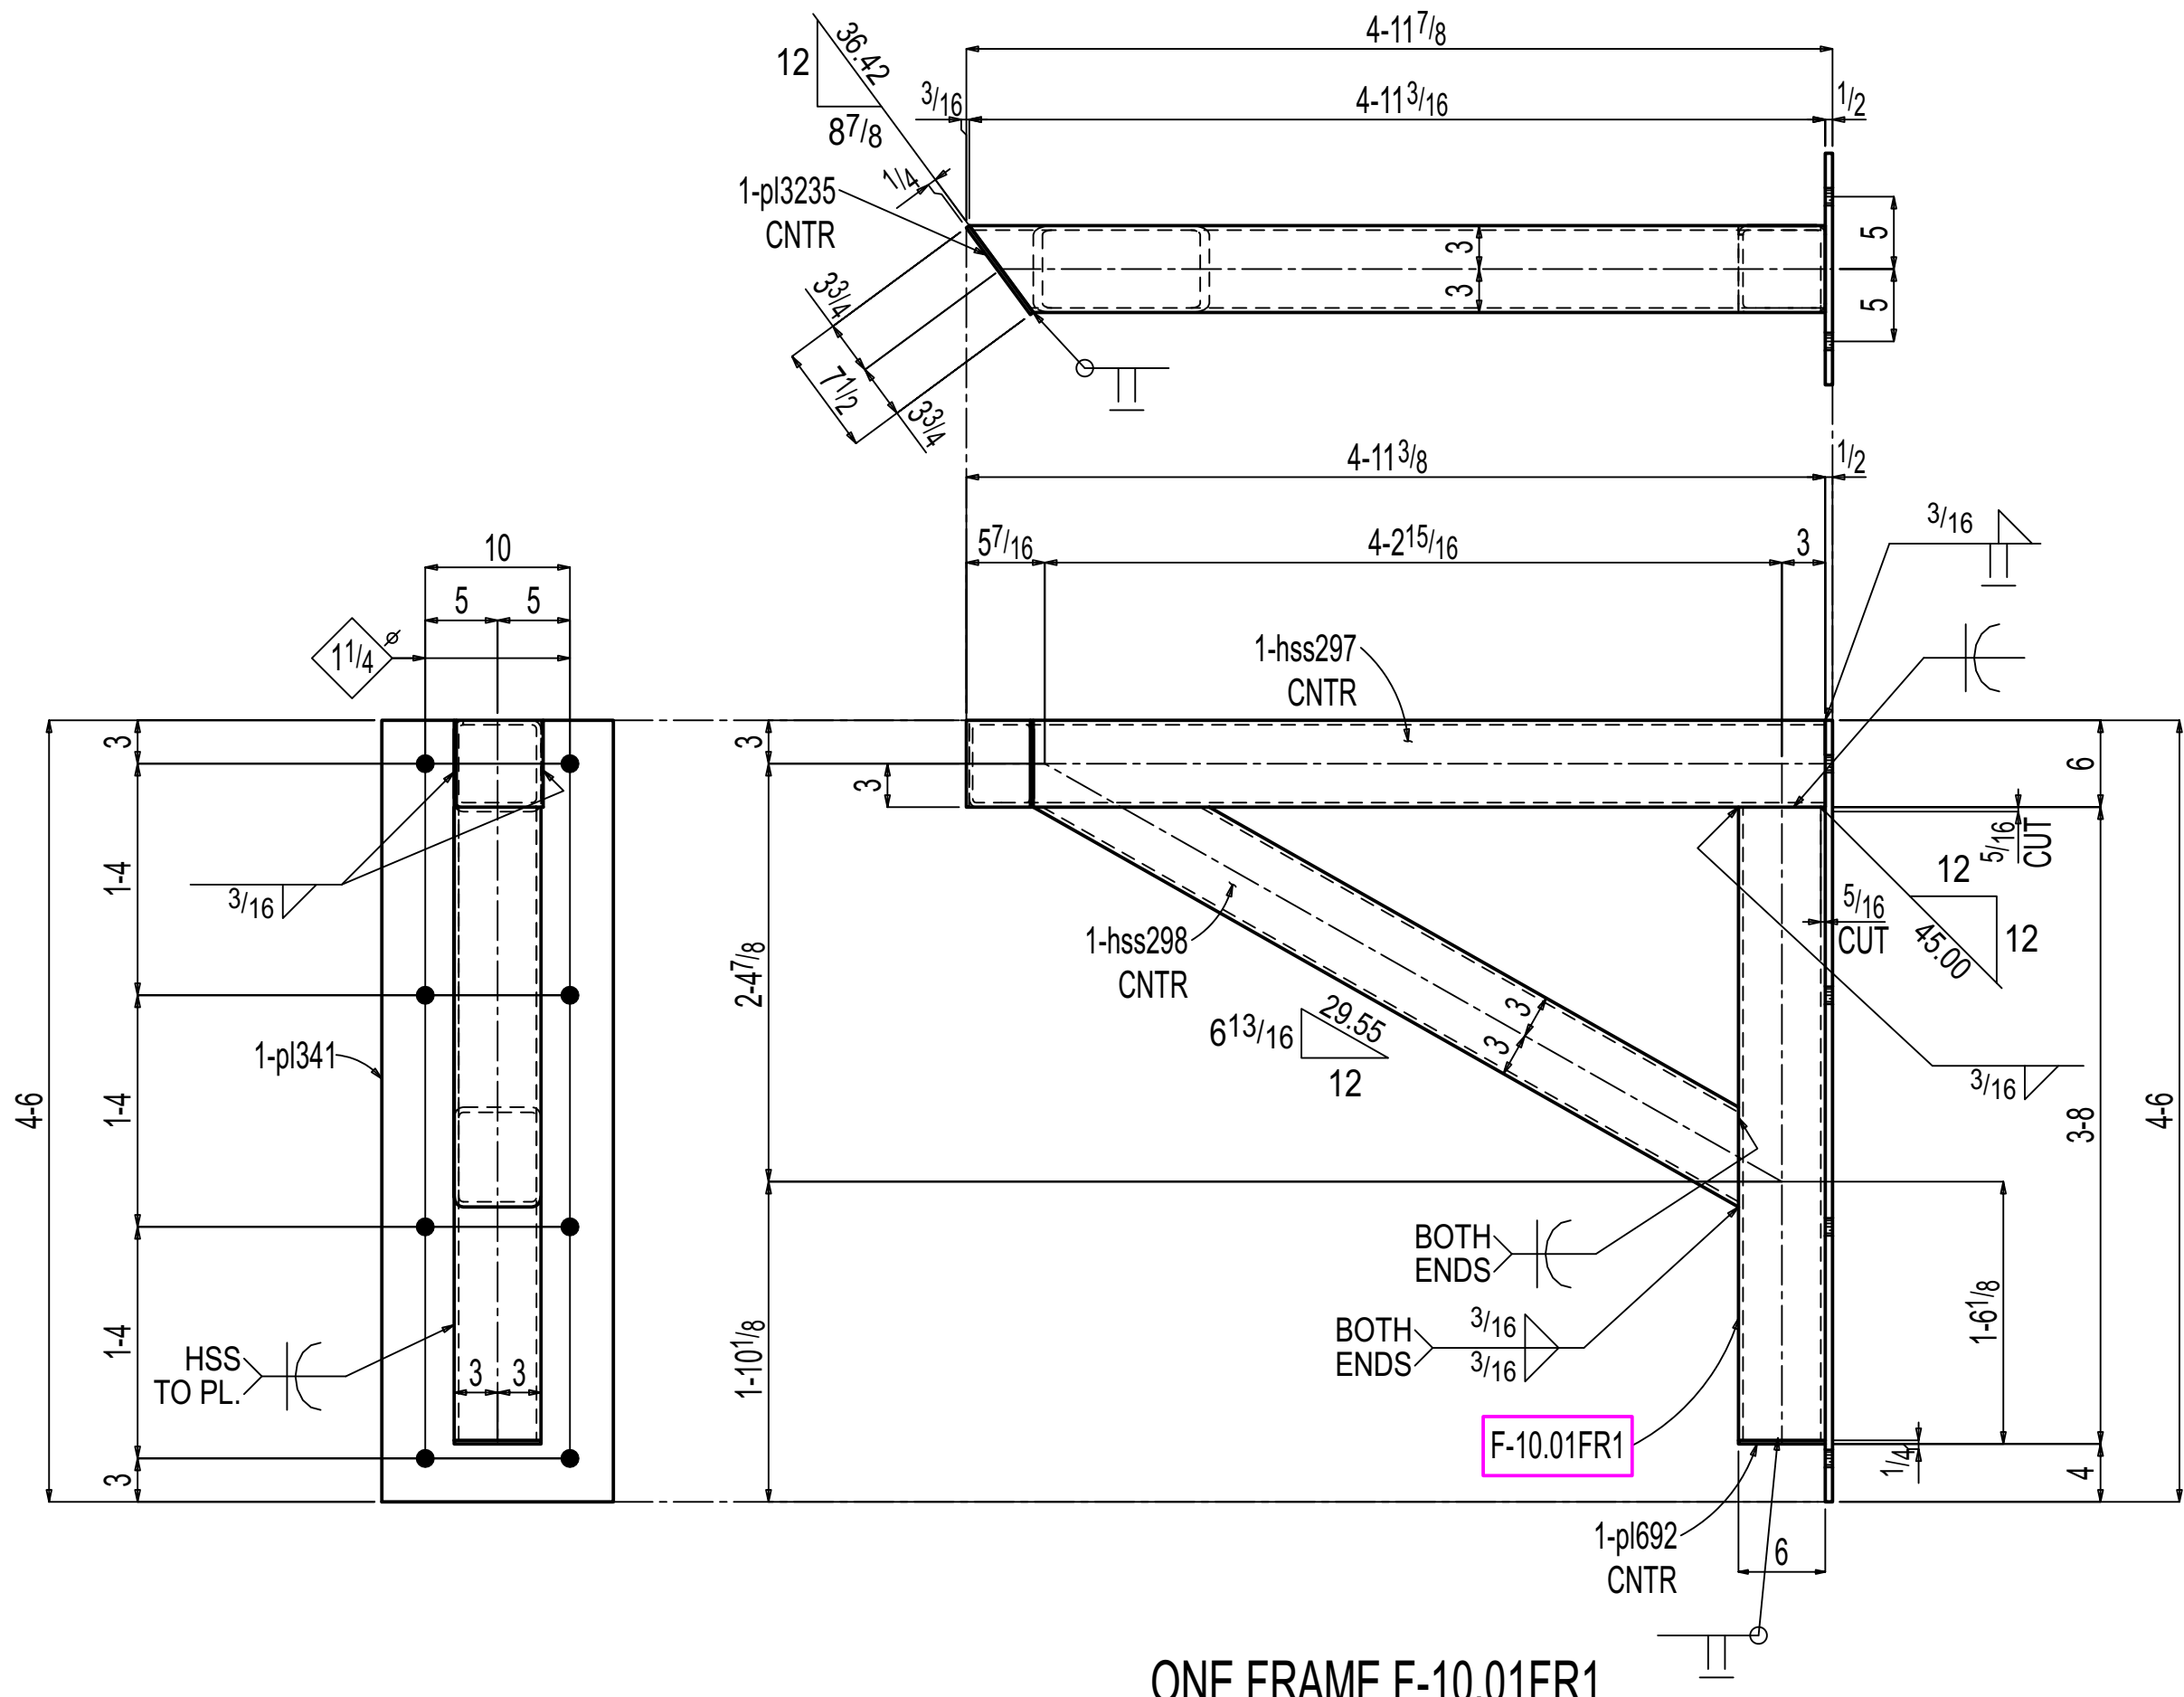


ONE FRAME F-10.01FR1

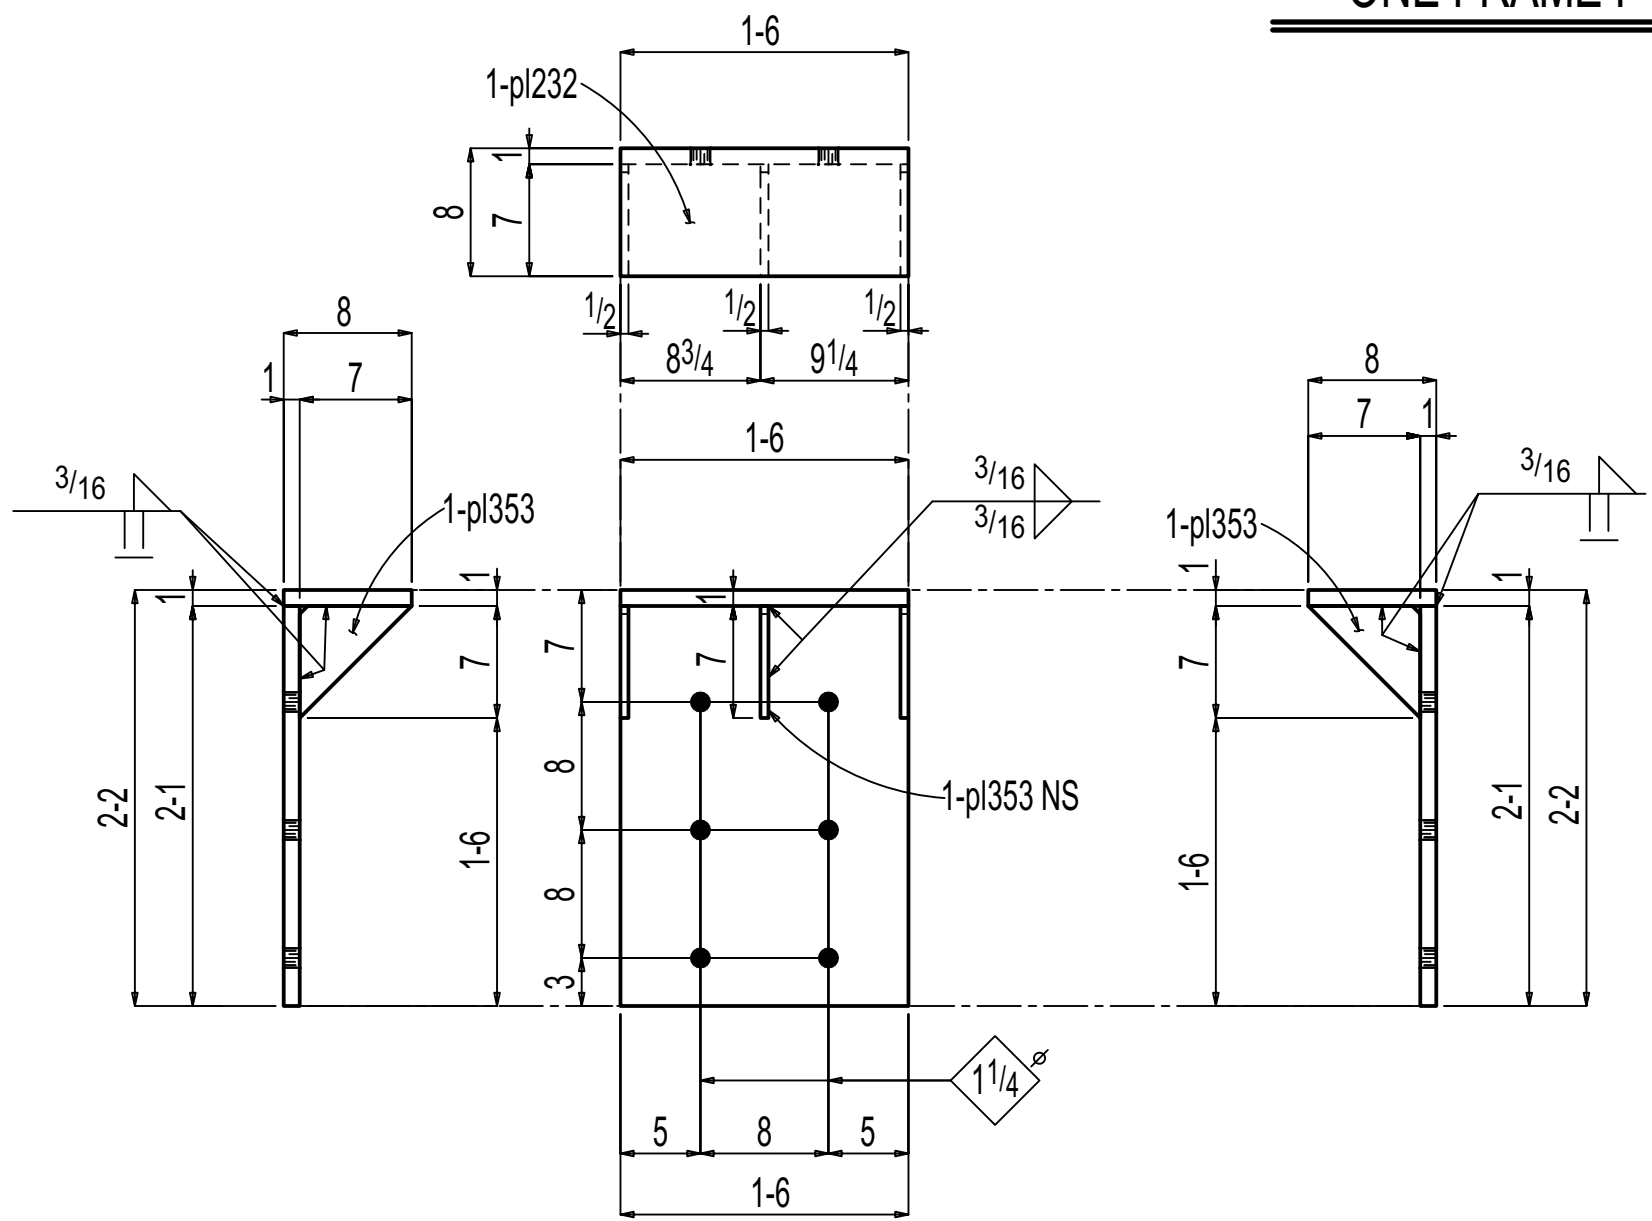


ONE PLATE F-10.01M1

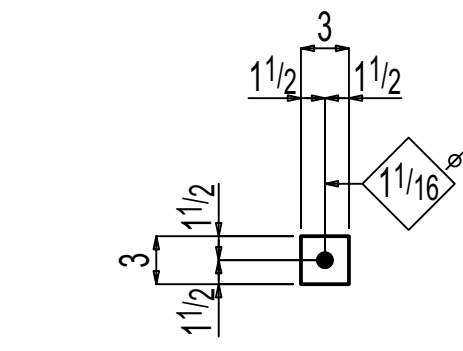


6 PLATE WASHERS F-10.01M4

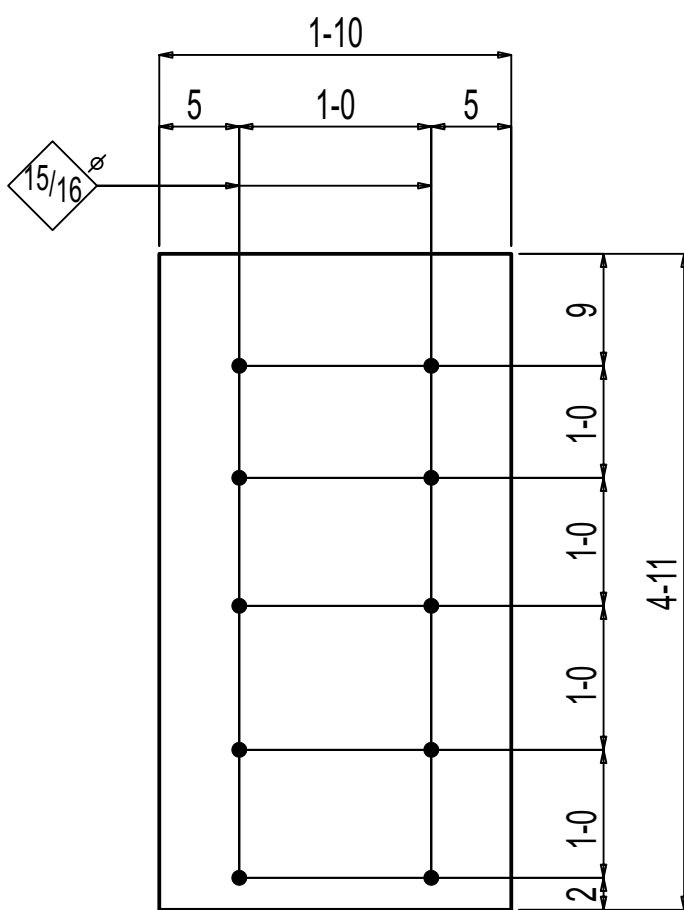


ONE EMBED PLATE F-10.01EP1

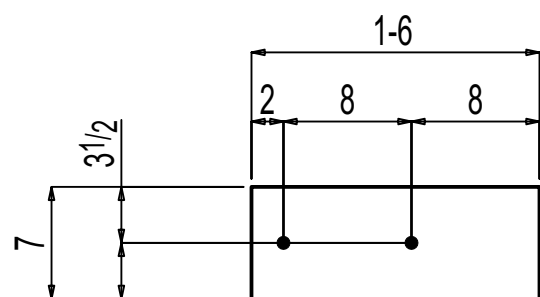


ONE LEVELING PLATE F-10.01LP1

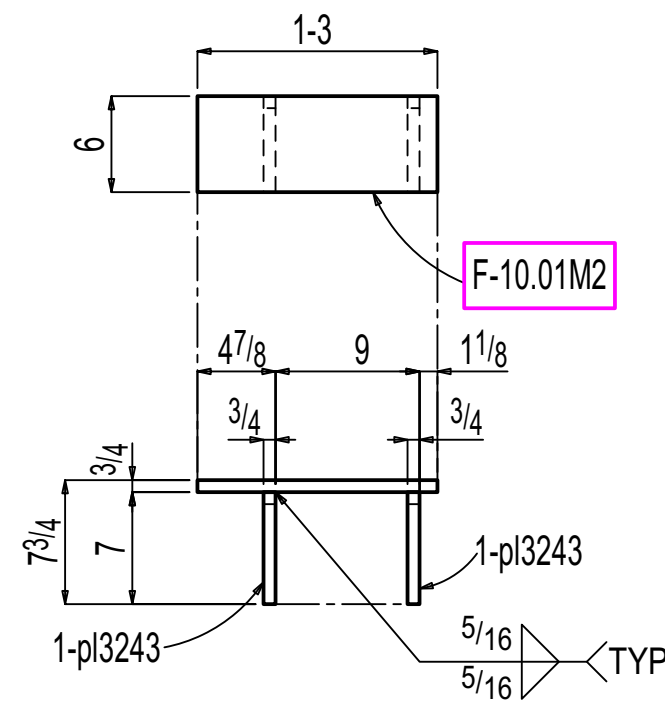


ONE PLATE F-10.01M2

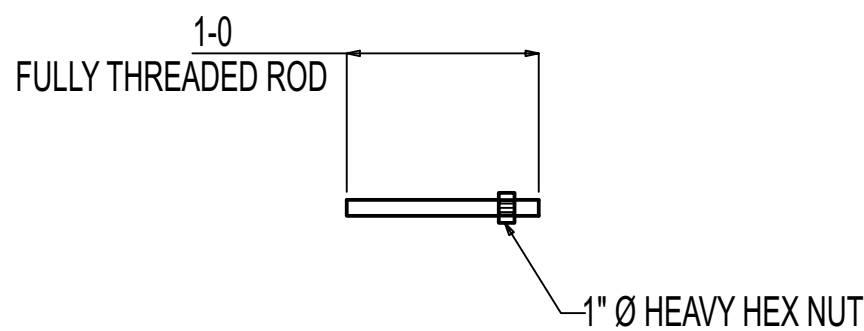


6 THREADED RODS F-10.01M5

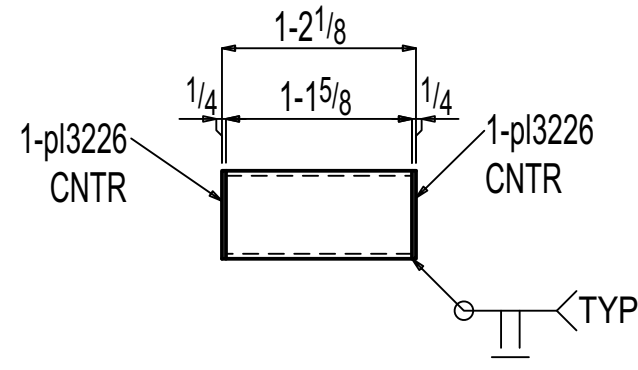

ONE HSS F-10.01M3

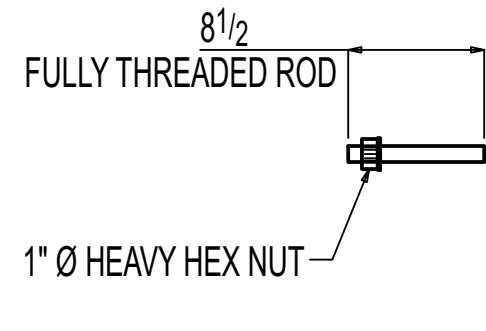

72 THREADED RODS F-10.01M6

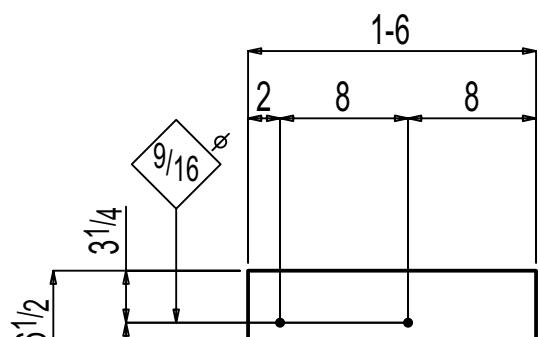

ONE LEVELING PLATE F-10.01LP2

PAINT PREPARATION :NO PAINT
PREPARATION :SSPC-SP3

General Notes

- *Structural steel shall conform to ASTM-A992.
- *Structural SQR/RND,tubing conform to ASTM A500 Grade C
- *Pipe shall conform to ASTM A53, Grade B.
- *Channels, Angles and plates shall conform to A36.
- *All bolts shall be $\frac{3}{4}$ " High strength in accordance with ASTM A325 (UNO)
- *Welding Electrodes for Carbon steel :E70xx

# of Copies	Revision/ Issue	Destination	Date
5	0	For Fabrication	11-14-2025
4	D	For Re-Approval	10-24-2025
3	C	For Re-Approval	09-19-2025
2	B	For Re-Approval	06-23-2025
1	A	For Approval	02-25-2025

IRON FABRICATION SERVICES, LLC.

3029 M. Street, NW, Suite 202
Washington, DC 20007
Tel: 202-800-5599
Fax: 202-478-0303

Project Name and Address

MARYLAND AVENUE

Location: 1250 MARYLAND AVENUE SW
WASHINGTON, DC 20024

Contractor:

BALFOUR BEATTY

Approved for Fabrication by:

Signature

Contract

224009

Drawing

F-10.01

Contract Item:

MISCELLANEOUS

Ref:

SOW - 10: E-10.00 - E-10.02

Date

01/ 23/ 2025

Drawing Title:


FRAME & MISCELLANEOUS
DETAIL

Scale

VARIES


BILL OF MATERIAL							
LINE #	QTY	PC	MARK		DESCRIPTION	LENGTH	WEIGHT
	TOTAL		MARK				ADVANCE
		ONE	F-10.02C1		COLUMN		329
	1	F-10.02C1	HSS6x6x3/8	10	4	S2E A500C	284
	1	pl1970	PL11/4x7	1	6	A36	45
					FIELD BOLTS		
	2		3/4 Dia HILTI HAS V-36	0	8	(31/4" EMBEDMENT)	
			w/ HILTI HIT HY-200 EPOXY				
	ONE	F-10.02C2			COLUMN		353
	1	F-10.02C2	HSS6x6x3/8	9	101/4	S2E A500C	271
	1	hss434	HSS4x4x3/16	1	61/4	A500C	23
	1	hss433	HSS4x4x3/16	1	07/8	A500C	16
	1	a171	L11/2x1x3/16	0	5	A36	1
	2	pl350	PL5/8x61/2	1	6	A36	41
	1	pl3522	PL11/4x4	0	4	A36	1
					FIELD BOLTS		
	2		1/2" Dia HILTI KWIK HUS-EZ	0	41/2	(23/4" EMBEDMENT)	
			SCREW ANCHOR				
	ONE	F-10.02B1			BEAM		1430
	1	F-10.02B1	W12x79	18	11/4	A992	1430
	ONE	F-10.02B2			BEAM		460
	1	F-10.02B2	HSS12x4x3/8	12	03/8	A500C	453
	2	pl3245	PL11/4x4	1	0	A36	7

Total weight : 2572

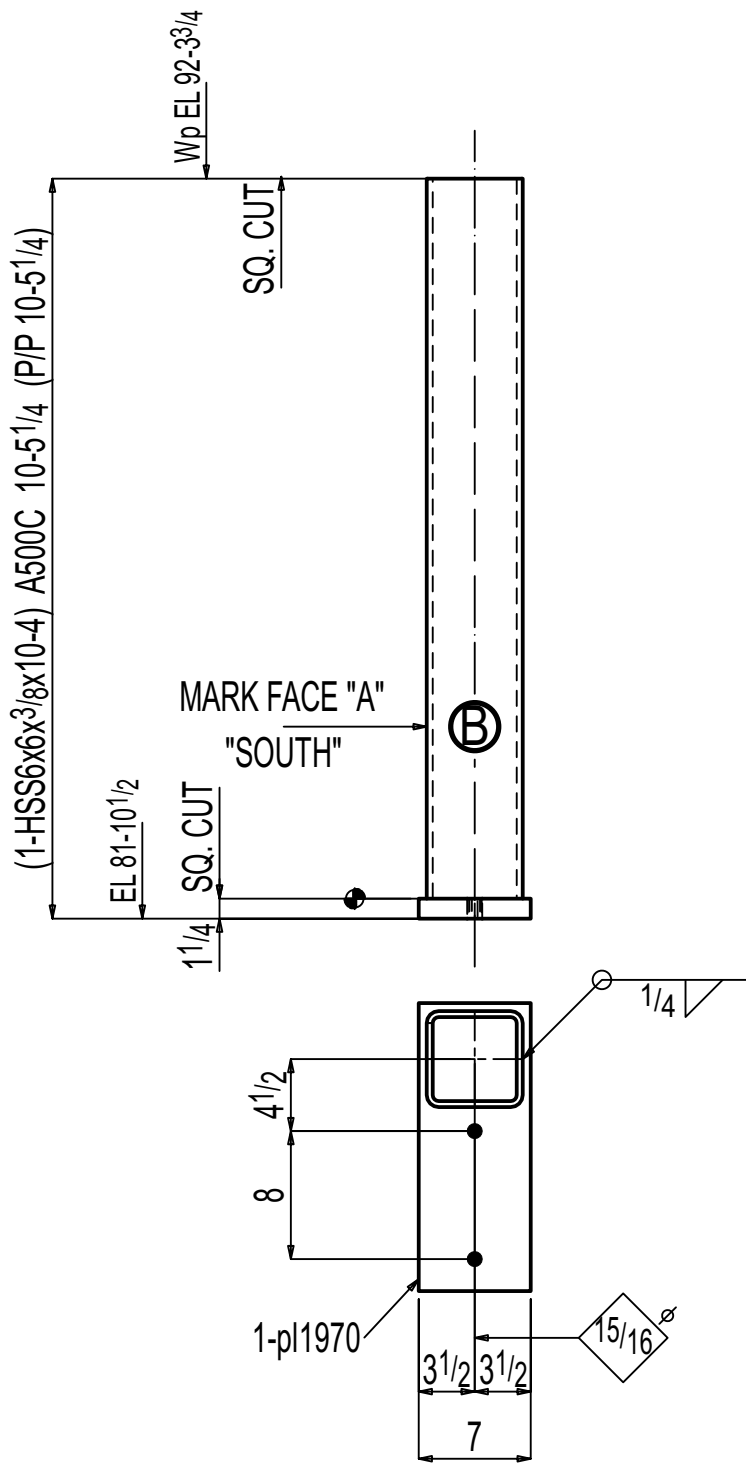


ONE COLUMN F-10.02C1

AT GRID:
EE & A

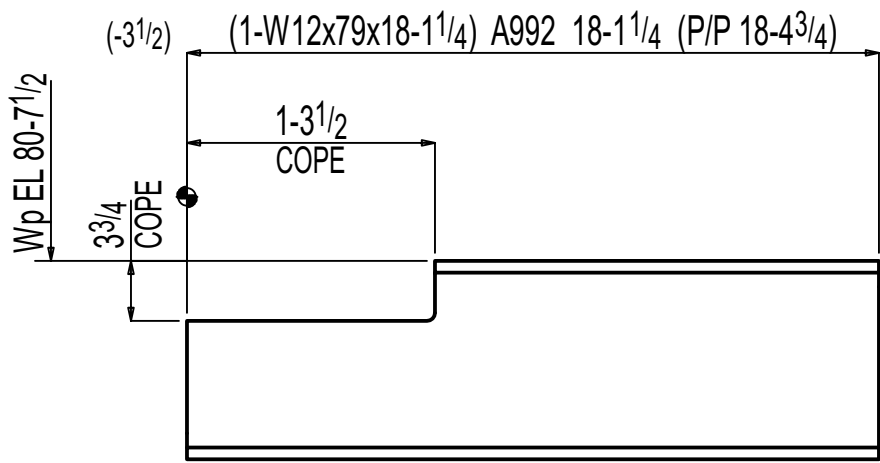


ONE BEAM F-10.02B1

W 123/8x11/2
F 121/8x3/4
K 15/8x11/8

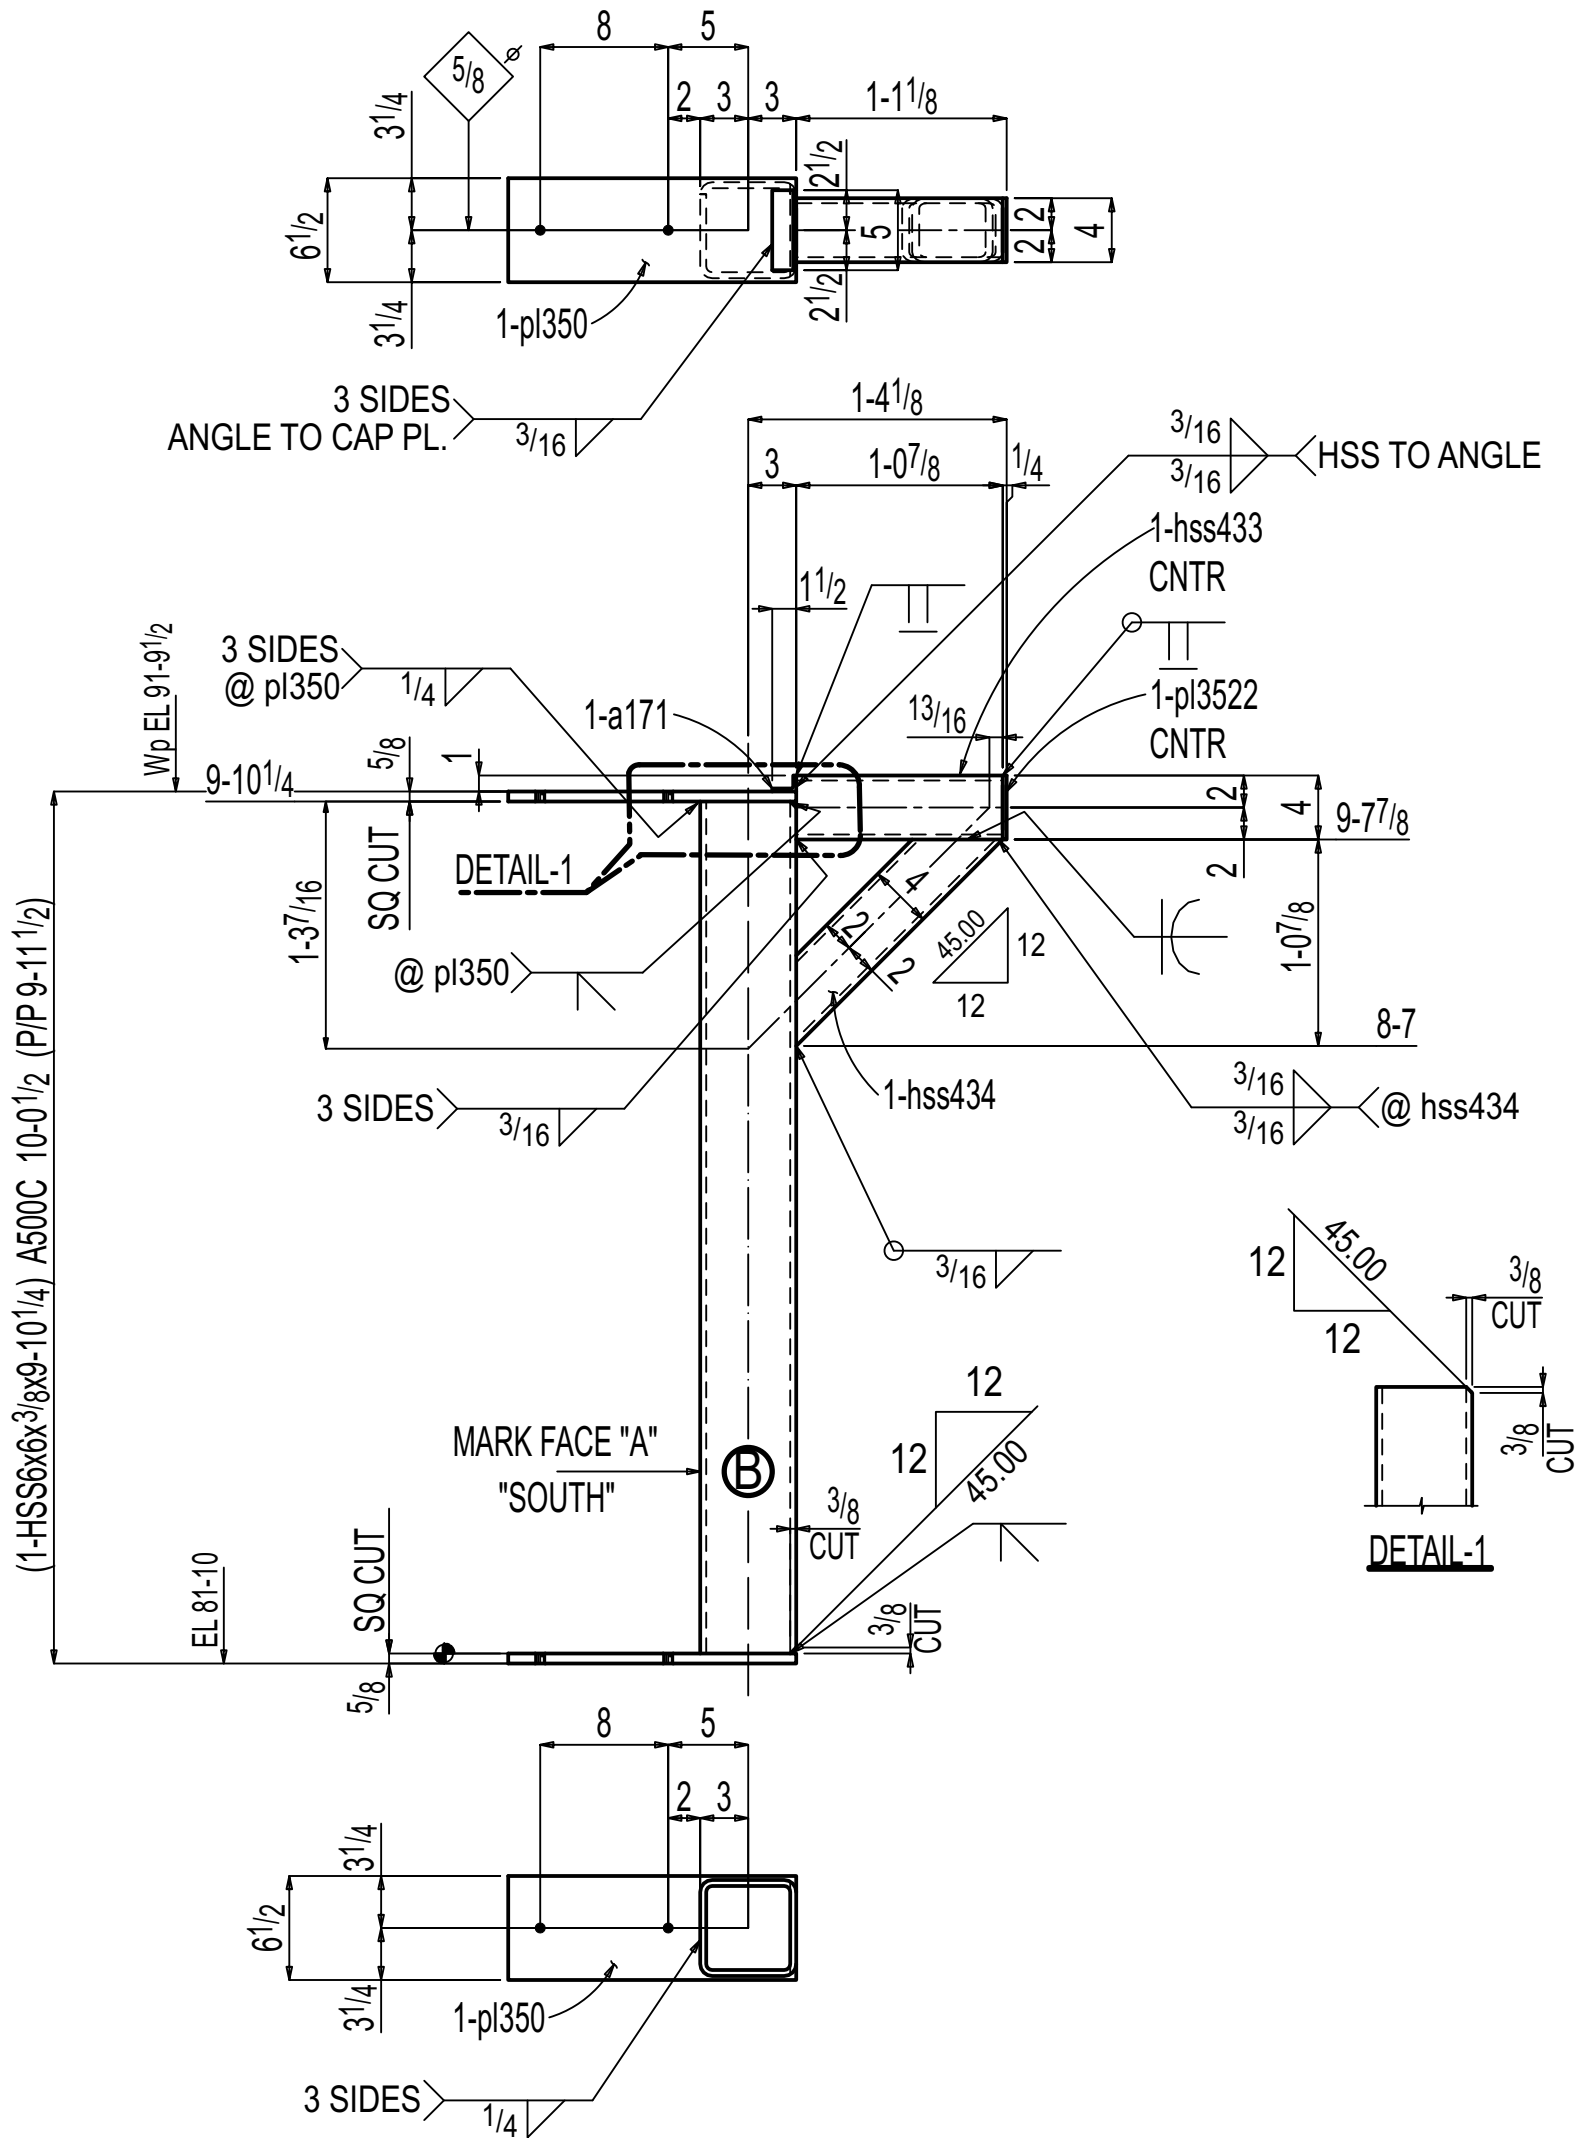

ONE COLUMN F-10.02C2

AT GRID:
AA & K

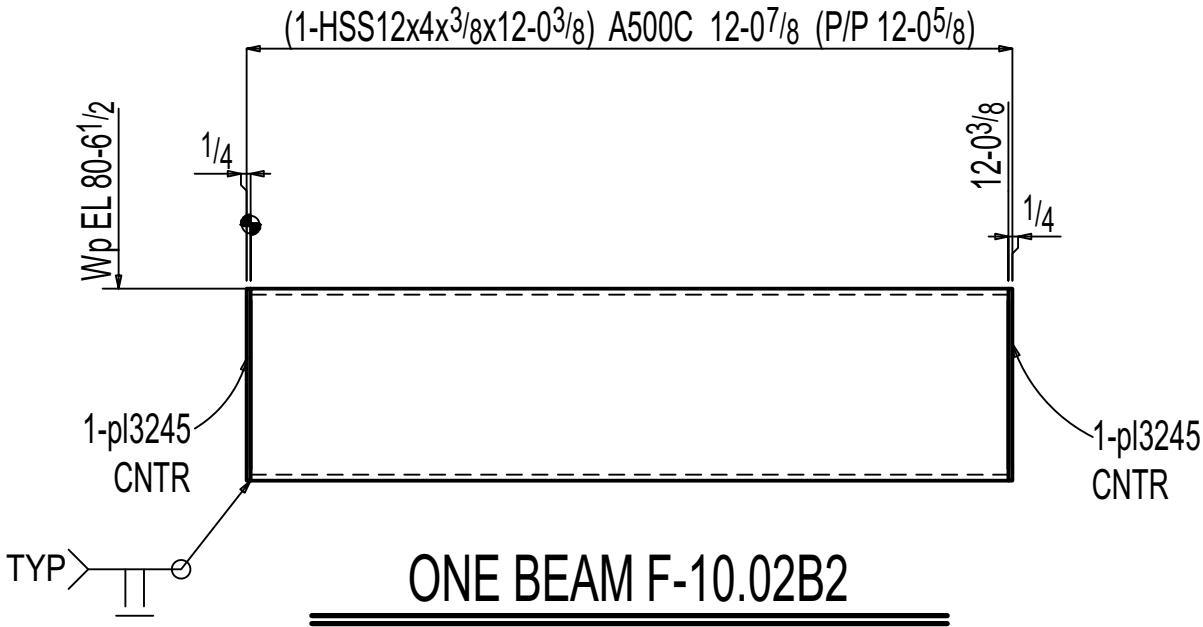

ONE BEAM F-10.02B2

PAINT PREPARATION :NO PAINT :SSPC-SP3

General Notes			
*Structural steel shall conform to ASTM-A992.			
*Structural SQR/RND,tubing conform to ASTM A500 Grade C			
*Pipe shall conform to ASTM A53, Grade B.			
*Channels, Angles and plates shall conform to A36.			
*All bolts shall be 3/4" High strength in accordance with ASTM A325 (UNO)			
*Welding Electrodes for Carbon steel :E70xx			
5	0	For Fabrication	11-14-2025
4	D	For Re-Approval	10-24-2025
3	C	For Re-Approval	09-19-2025
2	B	Deleted	06-23-2025
1	A	For Approval	02-25-2025
# of Copies	Revision/ Issue	Destination	Date

IRON FABRICATION SERVICES, LLC.

3029 M. Street, NW, Suite 202
Washington, DC 20007
Tel: 202-800-5599
Fax: 202-478-0303

Project Name and Address
MARYLAND AVENUE

Location: **1250 MARYLAND AVENUE SW
WASHINGTON, DC 20024**

Contractor:
BALFOUR BEATTY

Approved for Fabrication by: Signature

Contract # **224009** Drawing # **F-10.02**









Contract Item: **COLUMN & BEAM**

Ref:
SOW - 10: E-10.00 - E-10.02

Date **01/ 23/ 2025** Drawing Title: **COLUMN & BEAM DETAIL**
Scale **VARIES**

BILL OF MATERIAL							
LINE #	QTY	PC	MARK	DESCRIPTION	LENGTH	REMARKS	WEIGHT
	TOTAL						TOTAL
							MILL #
ONE	F-10.03B1	BEAM					101
1	F-10.03B1	HSS6x4x ³ / ₈		4	5 ⁷ / ₁₆	B1E A500C	100
1	p246	PL ¹ / ₄ x4		0	6	A36	2
ONE	F-10.03B2	BEAM					565
1	F-10.03B2	HSS6x4x ³ / ₈		25	0 ³ / ₁₆	A500C	560
1	fb321	FL ³ / ₈ x4		0	5 ⁵ / ₈	A36	2
1	p2523	PL ¹ / ₄ x4 ¹ / ₄		0	6	A36	2
1	p246	PL ¹ / ₄ x4		0	6	A36	2
ONE	F-10.03M1	HSS					52
1	F-10.03M1	HSS6x6x ³ / ₁₆		2	2 ¹³ / ₁₆	A500C	52
ONE	F-10.03M2	HSS					59
1	F-10.03M2	HSS6x6x ³ / ₁₆		2	4 ³ / ₄	A500C	56
1	p2253	PL ¹ / ₄ x6		0	6 ³ / ₈	A36	3
2	F-10.03M3	THREADED ROD					1
2	F-10.03M3	1/2"Ø THREADED ROD		0	6	F1554 GR. 55	1
		w/ HILTI HIT HY-200				(2 ³ / ₄ " EMBED)	
		ADHESIVE					
2		1/2 NUT				HHNT A563	
2		1/2 WASHER				HD F436	
ONE	F-10.03P1	PLATE					3
1	F-10.03P1	PL ³ / ₈ x4		0	6	A36	3
ONE	F-10.03P2	PLATE					55
1	F-10.03P2	PL ¹ / ₄ x7		1	10	A36	55
		FIELD BOLTS					
2		3/4"Ø HILTI KWIK HUS-EZ		0	7	(3 ¹ / ₄ " EMBED)	
		SCREW ANCHOR					
ONE	F-10.03A1	ANGLE					2
1	F-10.03A1	L4x4x ¹ / ₄		0	4	A36	2

Total weight : 837

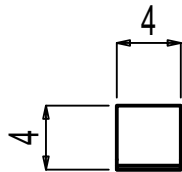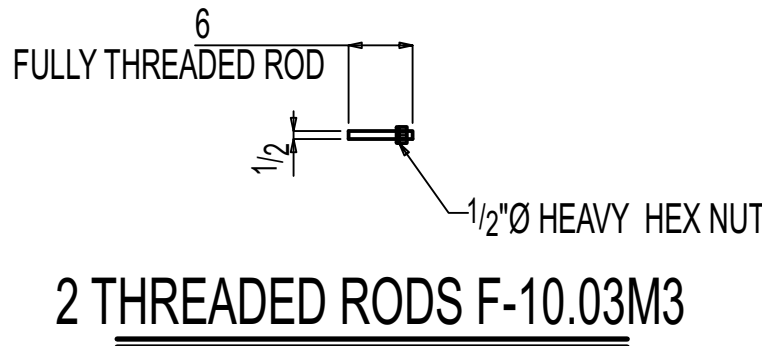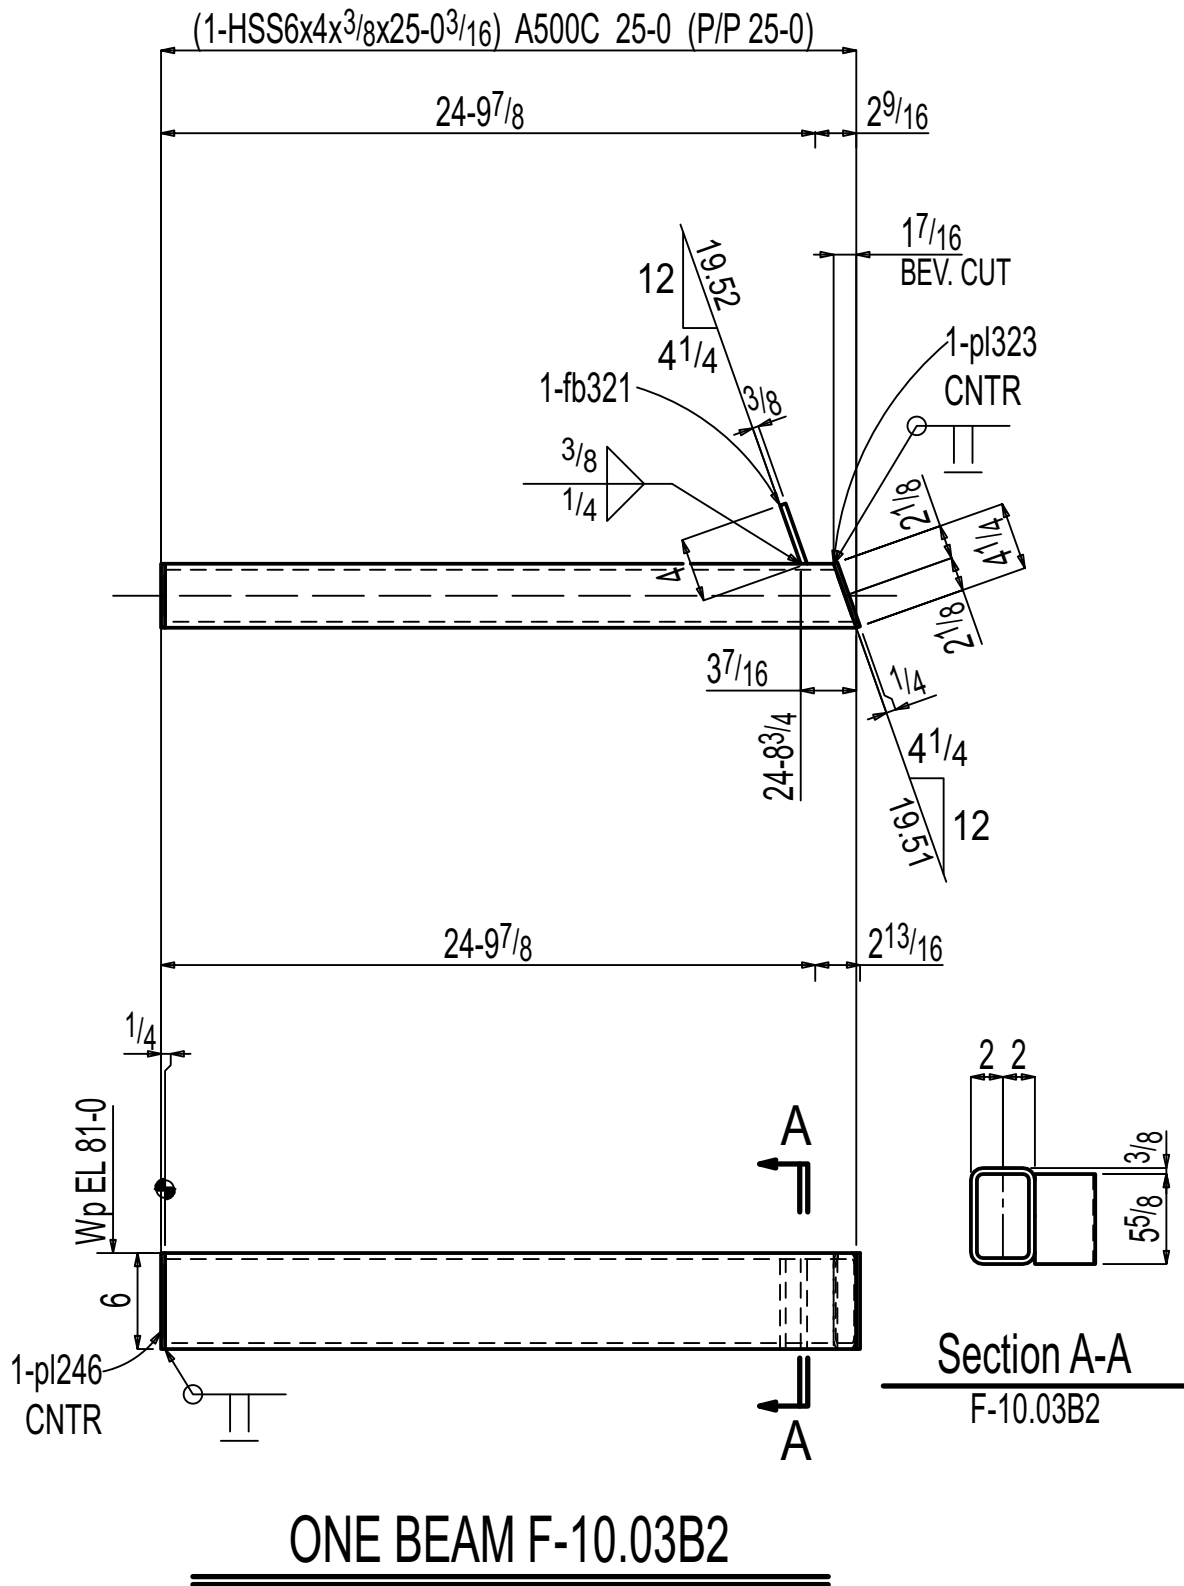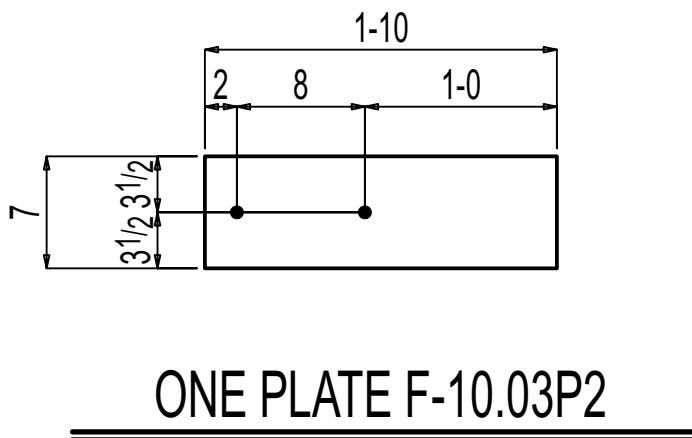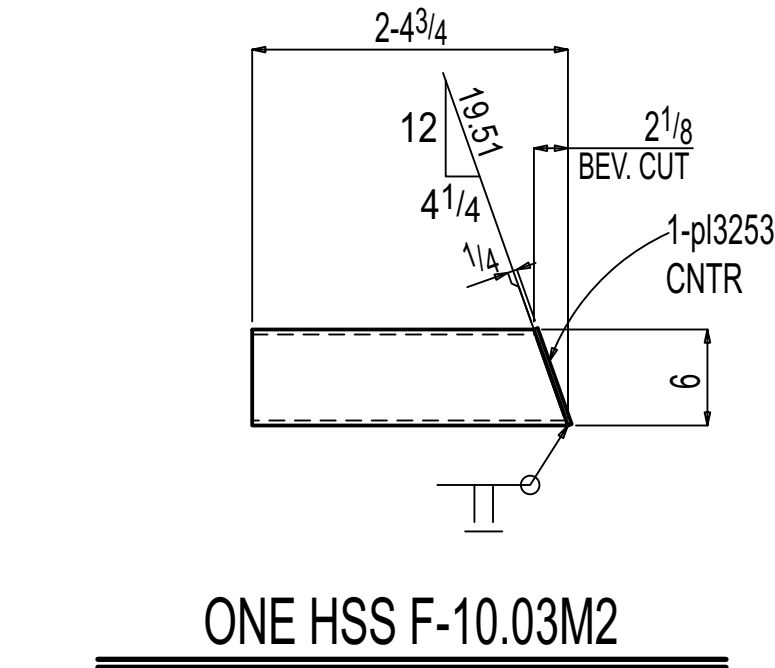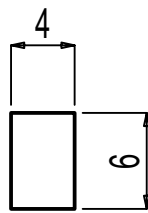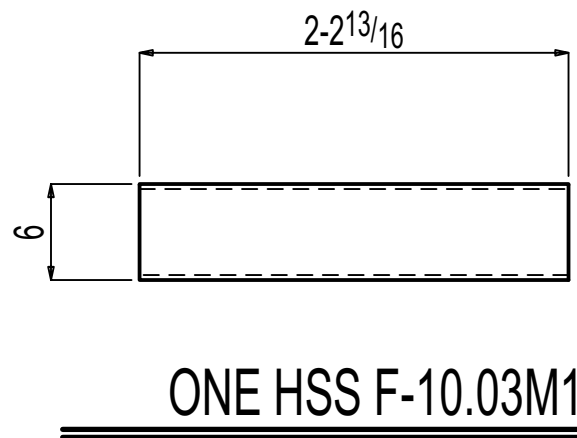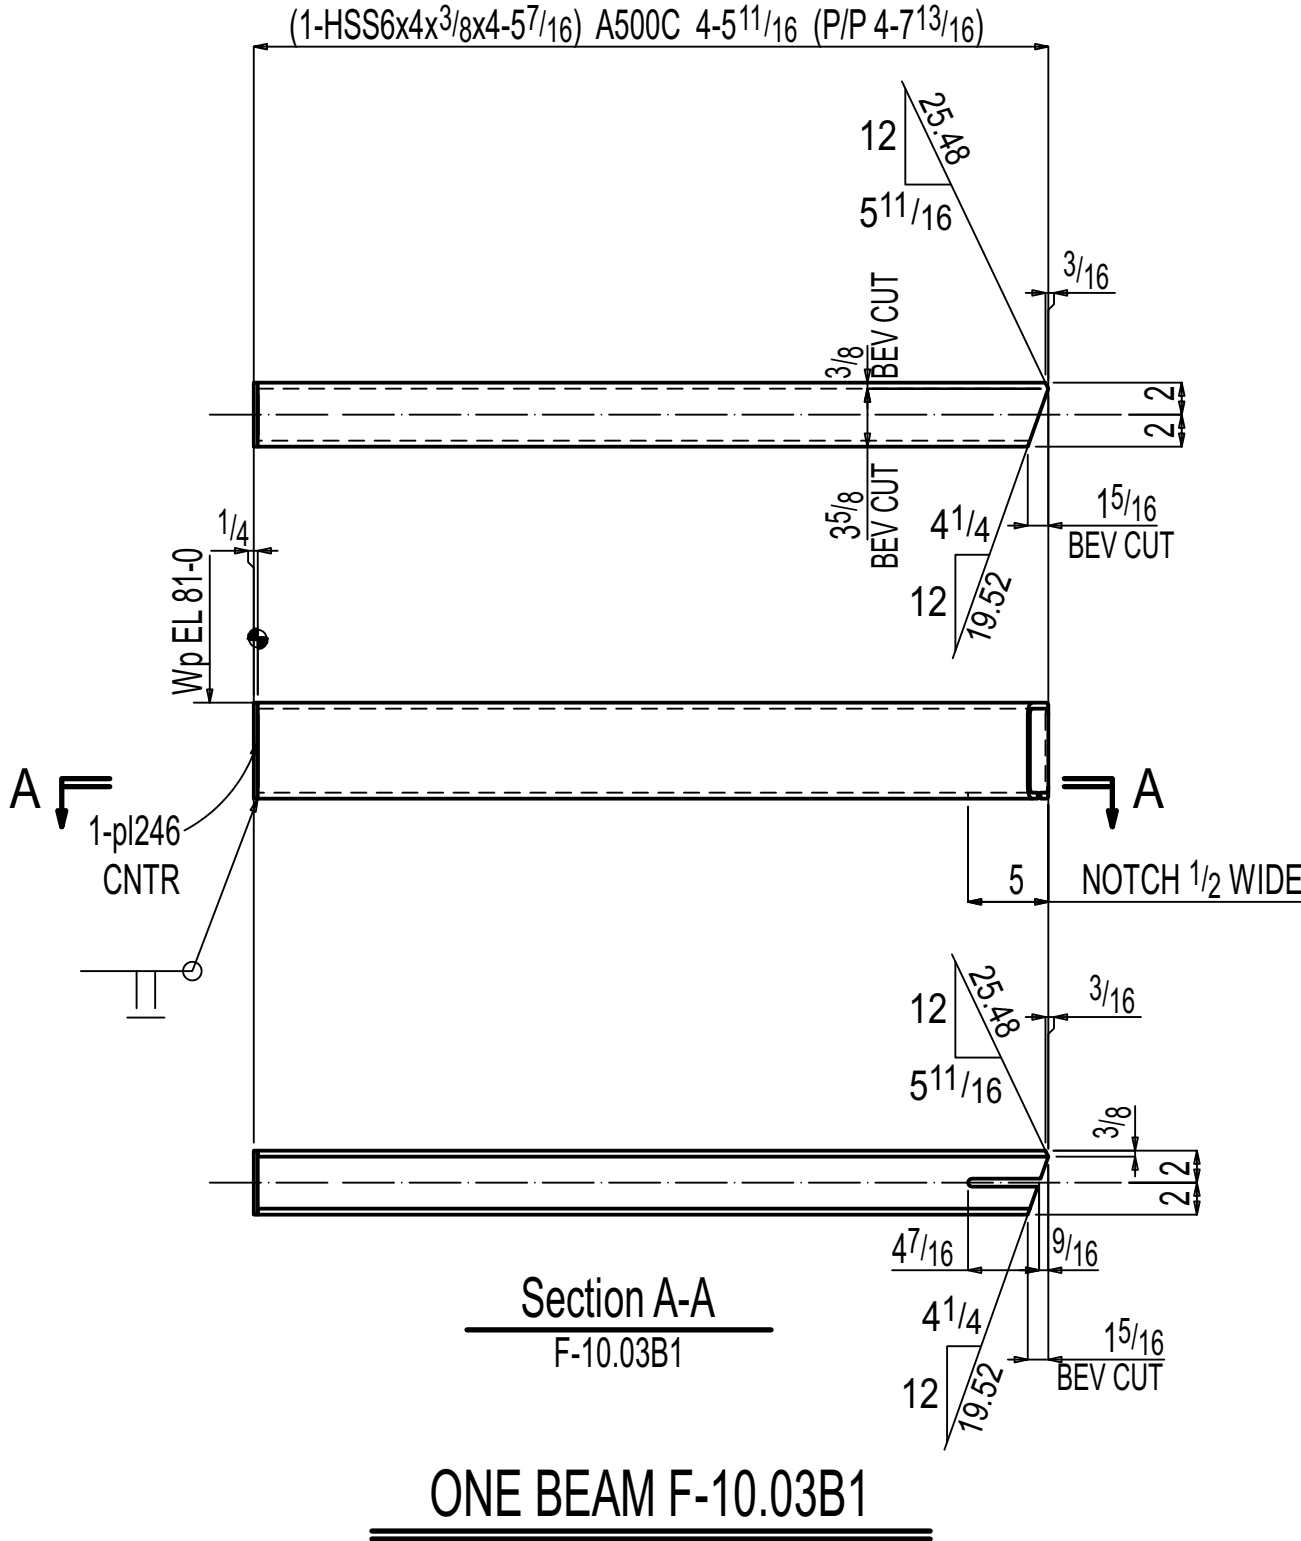

PAINT :NO PAINT
PREPARATION :SSPC-SP3

General Notes			
*Structural steel shall conform to ASTM-A992.			
*Structural SQR/RND,tubing conform to ASTM A500 Grade C			
*Pipe shall conform to ASTM A53, Grade B.			
*Channels, Angles and plates shall conform to A36.			
*All bolts shall be 3/4" High strength in accordance with ASTM A325 (UNO)			
*Welding Electrodes for Carbon steel :E70xx			
5	0	For Fabrication	11-14-2025
4	D	For Re-Approval	10-24-2025
3	C	For Re-Approval	09-19-2025
2	B	For Re-Approval	06-23-2025
1	A	For Approval	02-25-2025
# of Copies	Revision/ Issue	Destination	Date

IRON FABRICATION SERVICES, LLC.

3029 M. Street, NW, Suite 202
Washington, DC 20007
Tel: 202-800-5599
Fax: 202-478-0303

Project Name and Address

MARYLAND AVENUE

Location: **1250 MARYLAND AVENUE SW
WASHINGTON, DC 20024**

Contractor:

BALFOUR BEATTY

Approved for Fabrication by:

Signature

Contract # **224009**

Drawing # **F-10.03**

Contract Item: **BEAM , MISCELLANEOUS**

Ref:

SOW - 10: E-10.00 - E-10.02

Date

01/ 23/ 2025

Drawing Title:

**BEAM DETAIL
& MISCELLANEOUS**

Scale

VARIES