



BILL OF MATERIAL							
LINE #	QTY	PC MARK	DESCRIPTION	LENGTH		WEIGHT	ADVANCE
	TOTAL	MARK	DESCRIPTION		REMARKS	TOTAL	MILL #
ONE	F-11.04C1	COLUMN				329	
1	F-11.04C1	HSS6x6x3/8		10	4	S2E A500C	284
1	p1971	PL1"x7		1	6	A36	45
2		FIELD BOLTS					
		3/4 Dia HILTI HAS V-36		0	8	+1HD WASH	
		w/ HILTI HIT HY-200 V3				(3 1/4" EMBEDMENT)	
		ADHESIVE					
ONE	F-11.04C2	COLUMN				313	
1	F-11.04C2	HSS6x6x3/8		9	10 1/2	S2E A500C	271
1	p358	PL5/8x6 1/2		1	6	A36	21
1	p3371	PL5/8x6 1/2		1	6	A36	21
2		FIELD BOLTS					
		1/2 Dia HILTI KWIK HUS-EZ		0	4 1/2		
		SCREW ANCHOR				(2 3/4" EMBEDMENT)	
ONE	F-11.04B1	BEAM				2397	
1	F-11.04B1	HSS12x12x3/4		21	7 1/2	A500C	2377
2	p3644	PL1"x12		1	0	A36	20
2	F-11.04B2	BEAM				1090	
2	F-11.04B2	HSS8x8x1/4		20	9	A500C	1072
4	p567	PL1"x8		0	8	A36	18
2	F-11.04M1	THREADED ROD				1	
2	F-11.04M1	1/2" Ø THREADED ROD		0	6	F1554 GR. 55	1
2		1/2 NUT				HHNT A563	
2		1/2 WASHER				HD F436	
ONE	F-11.04M2	HSS				265	
1	F-11.04M2	HSS5x5x5/16		13	8 1/2	A500C	262
2	p567	PL1"x5		0	5	A36	4
ONE	F-11.04M3	HSS				145	
1	F-11.04M3	HSS5x5x5/16		9	7 1/2	A500C	143
2	p570	PL1"x3		0	5	A36	2
ONE	F-11.04A1	ANGLE				7	
1	F-11.04A1	L4x4x1/4		1	0	A36	7
ONE	F-11.04A2	ANGLE				2	
1	F-11.04A2	L4x4x1/4		0	4	A36	2
2	F-11.04P1	PLATE				18	
2	F-11.04P1	PL1"x8		0	8	A36	18
ONE	F-11.04P2	PLATE				55	
1	F-11.04P2	PL1"x7		1	10	A36	55
2		FIELD BOLTS					
		3/4 Dia HILTI KWIK HUS-EZ		0	7		
		SCREW ANCHOR					

Total weight : 4621

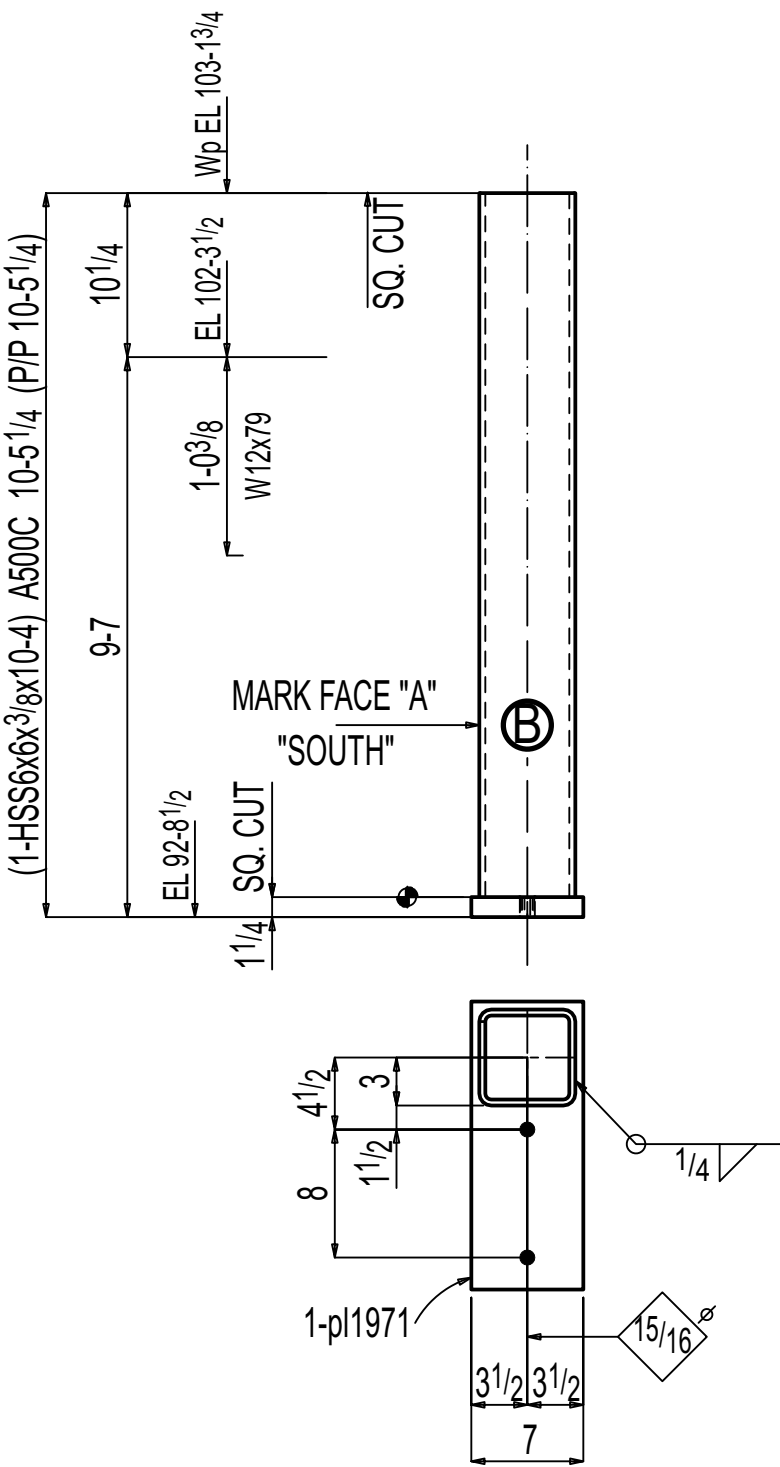


ONE COLUMN F-11.04C1


AT GRID:
EE & A

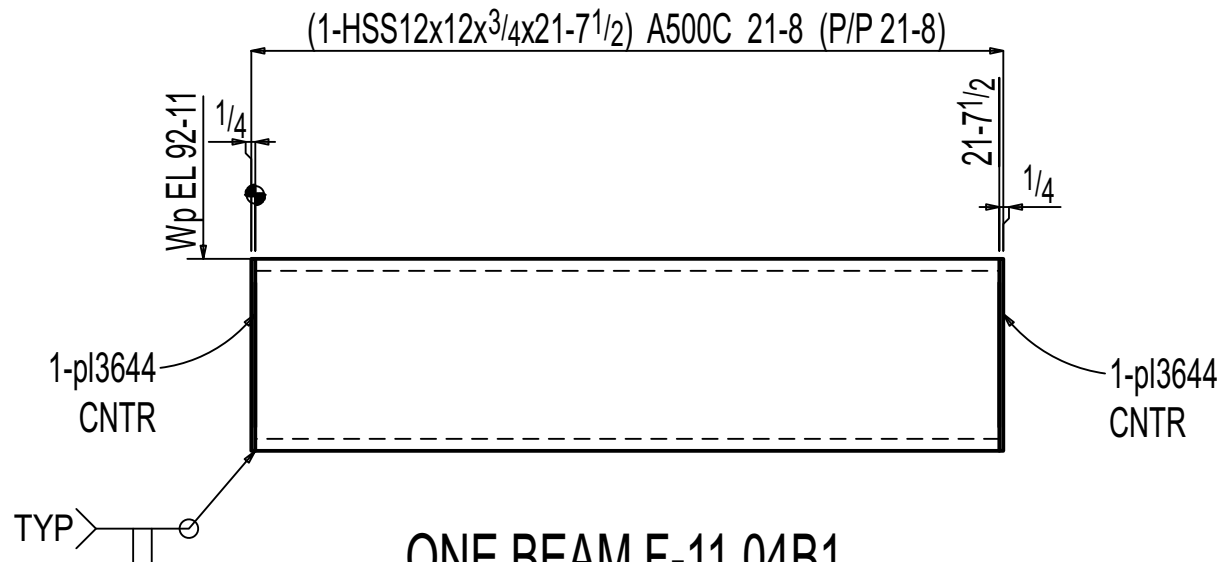


ONE BEAM F-11.04B1

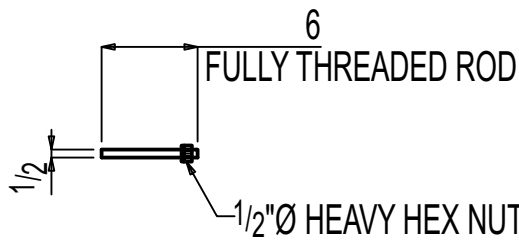

2 THREADED RODS F-11.04M1

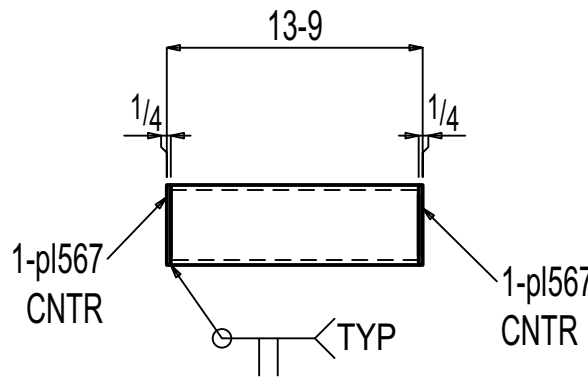


ONE HSS F-11.04M2

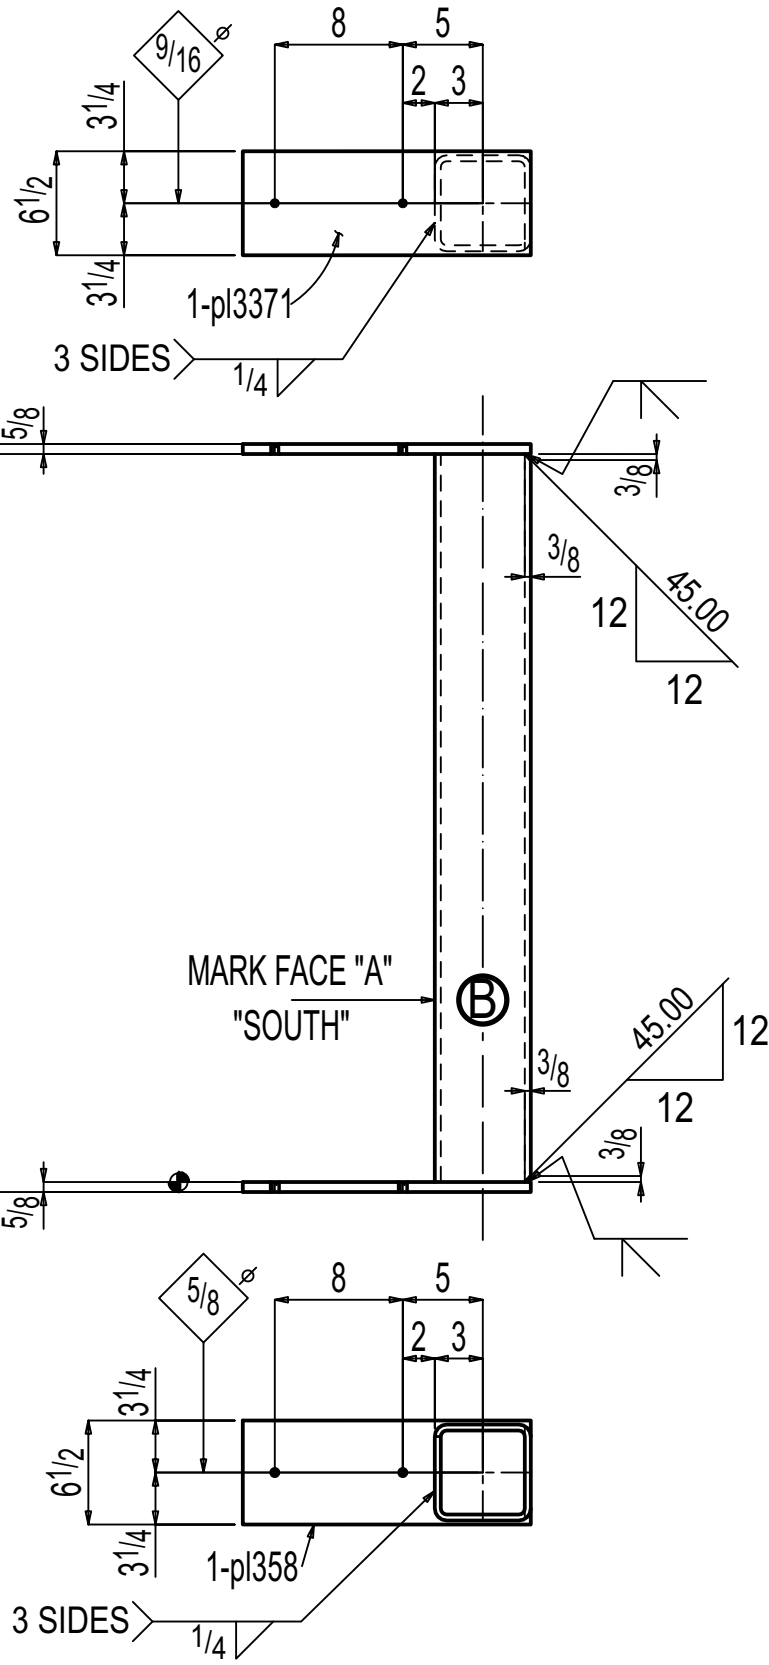


ONE COLUMN F-11.04C2


AT GRID:
AA & K

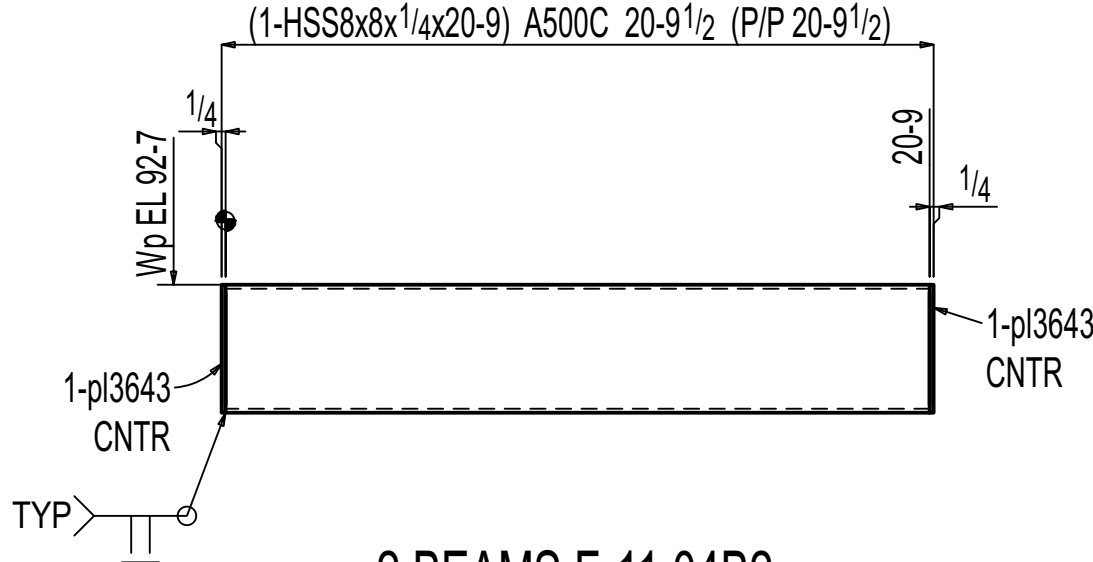


2 BEAMS F-11.04B2

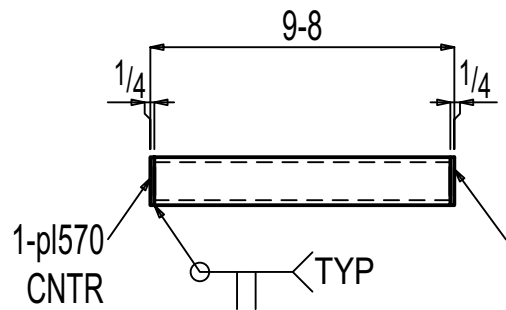


ONE HSS F-11.04M3

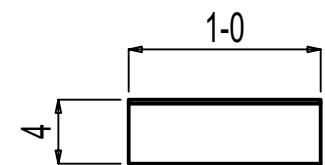


ONE ANGLE F-11.04A1

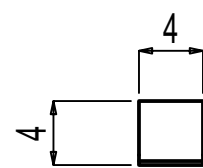

ONE ANGLE F-11.04A2

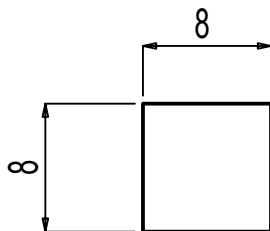

2 PLATES F-11.04P1

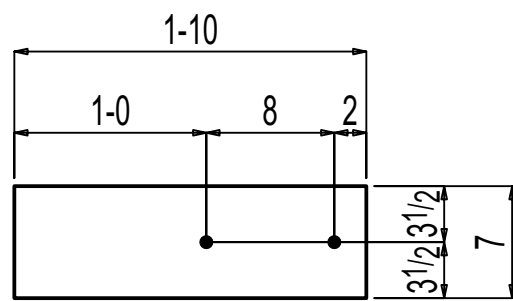

ONE PLATE F-11.04P2

PAINT PREPARATION :NO PAINT :SSPC-SP3

General Notes			
*Structural steel shall conform to ASTM-A992.			
*Structural SQR/RND,tubing conform to ASTM A500 Grade C			
*Pipe shall conform to ASTM A53, Grade B.			
*Channels, Angles and plates shall conform to A36.			
*All bolts shall be 3/4" High strength in accordance with ASTM A325 (UNO)			
*Welding Electrodes for Carbon steel :E70xx			
5	0	For Fabrication	11-14-2025
4	D	For Re-Approval	10-24-2025
3	C	For Re-Approval	09-19-2025
2	B	For Re-Approval	06-23-2025
1	A	For Approval	02-25-2025
# of Copies	Revision/ Issue	Destination	Date

IRON FABRICATION SERVICES, LLC.

3029 M. Street, NW, Suite 202
Washington, DC 20007
Tel: 202-800-5599
Fax: 202-478-0303

Project Name and Address
MARYLAND AVENUE

Location: **1250 MARYLAND AVENUE SW
WASHINGTON, DC 20024**

Contractor:
BALFOUR BEATTY

Approved for Fabrication by:	Signature
------------------------------	-----------

Contract #	224009	Drawing #	F-11.04
Contract Item:	FRAME		
Ref:	SOW - 11: E-11.00 - E-11.02		
Date 01/ 23/ 2025	Drawing Title: COLUMN & BEAM DETAIL		
Scale VARIES			