


BILL OF MATERIAL							
LINE #	QTY	PC MARK	DESCRIPTION	LENGTH	REMARKS	WEIGHT TOTAL	ADVANCE MILL #
	ONE	F-11.07B1	BEAM			516	
	1	F-11.07B1	HSS6x6x1/2	14	513/16	A500C	511
	2	p696	PL1/4x6	0	6	A36	5
	6	F-11.07M1	PLATE			68	
	6	F-11.07M1	PL1/2x8	0	10	A36	68
	6	F-11.07M2	PLATE			34	
	6	F-11.07M2	PL1/2x4	0	10	A36	34
	ONE	F-11.07A1	ANGLE			145	
	1	F-11.07A1	L4x4x5/16	17	85/16	A36	145
	27		FIELD BOLTS 1/2" Ø HILTI HAS V-36 w/ HILTI HIT HY-200 V3 ADHESIVE	0	41/2	(23/4" EMBEDMENT)	
	ONE	F-11.07A2	ANGLE			126	
	1	F-11.07A2	L4x4x5/16	15	49/16	A36	126
	24		FIELD BOLTS 1/2" Ø HILTI HAS V-36 w/ HILTI HIT HY-200 V3 ADHESIVE	0	41/2	(23/4" EMBEDMENT)	
	ONE	F-11.07A3	ANGLE			136	
	1	F-11.07A3	L4x4x5/16	16	71/16	A36	136
	25		FIELD BOLTS 1/2" Ø HILTI HAS V-36 w/ HILTI HIT HY-200 V3 ADHESIVE	0	41/2	(23/4" EMBEDMENT)	

Total weight : 1025

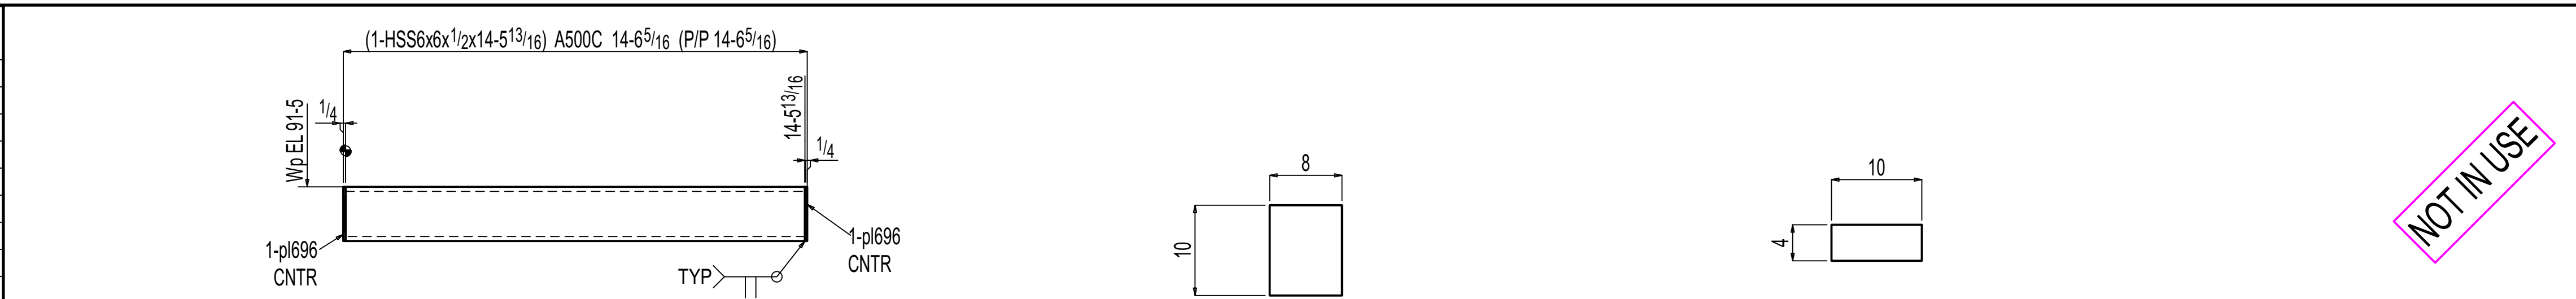


ONE BEAM F-11.07B1	6 PLATES F-11.07M1	6 PLATES F-11.07M2	ONE HSS F-11.07M3
--------------------	--------------------	--------------------	-------------------


[illegible]

17-8 1/2
CHORD LENGTH
17.85% or 161.81% RAD


7 on $161-8\frac{1}{2}$ RAD

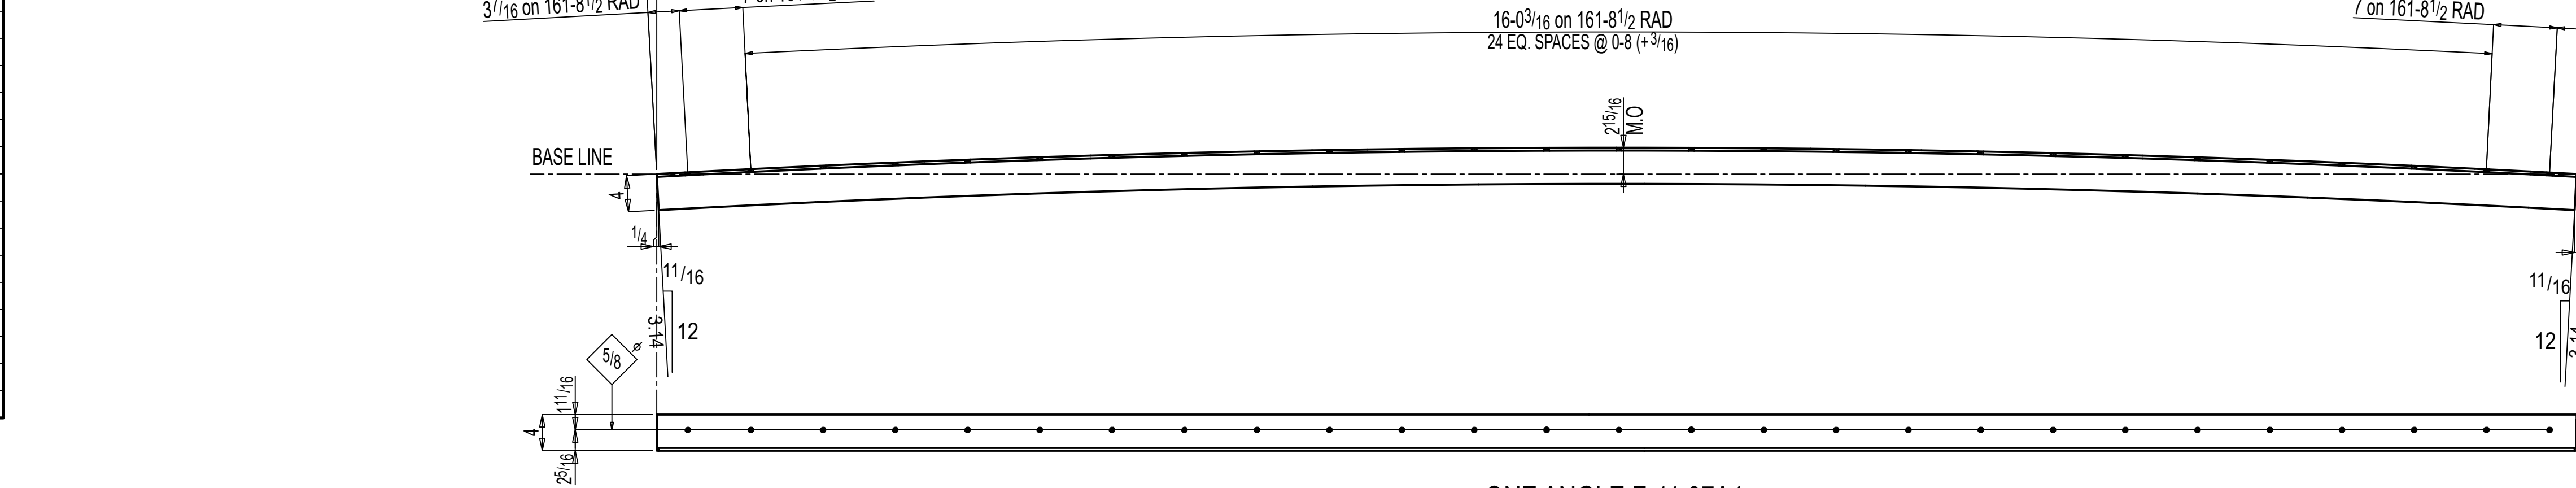

ONE ANGLE F-11.07A1

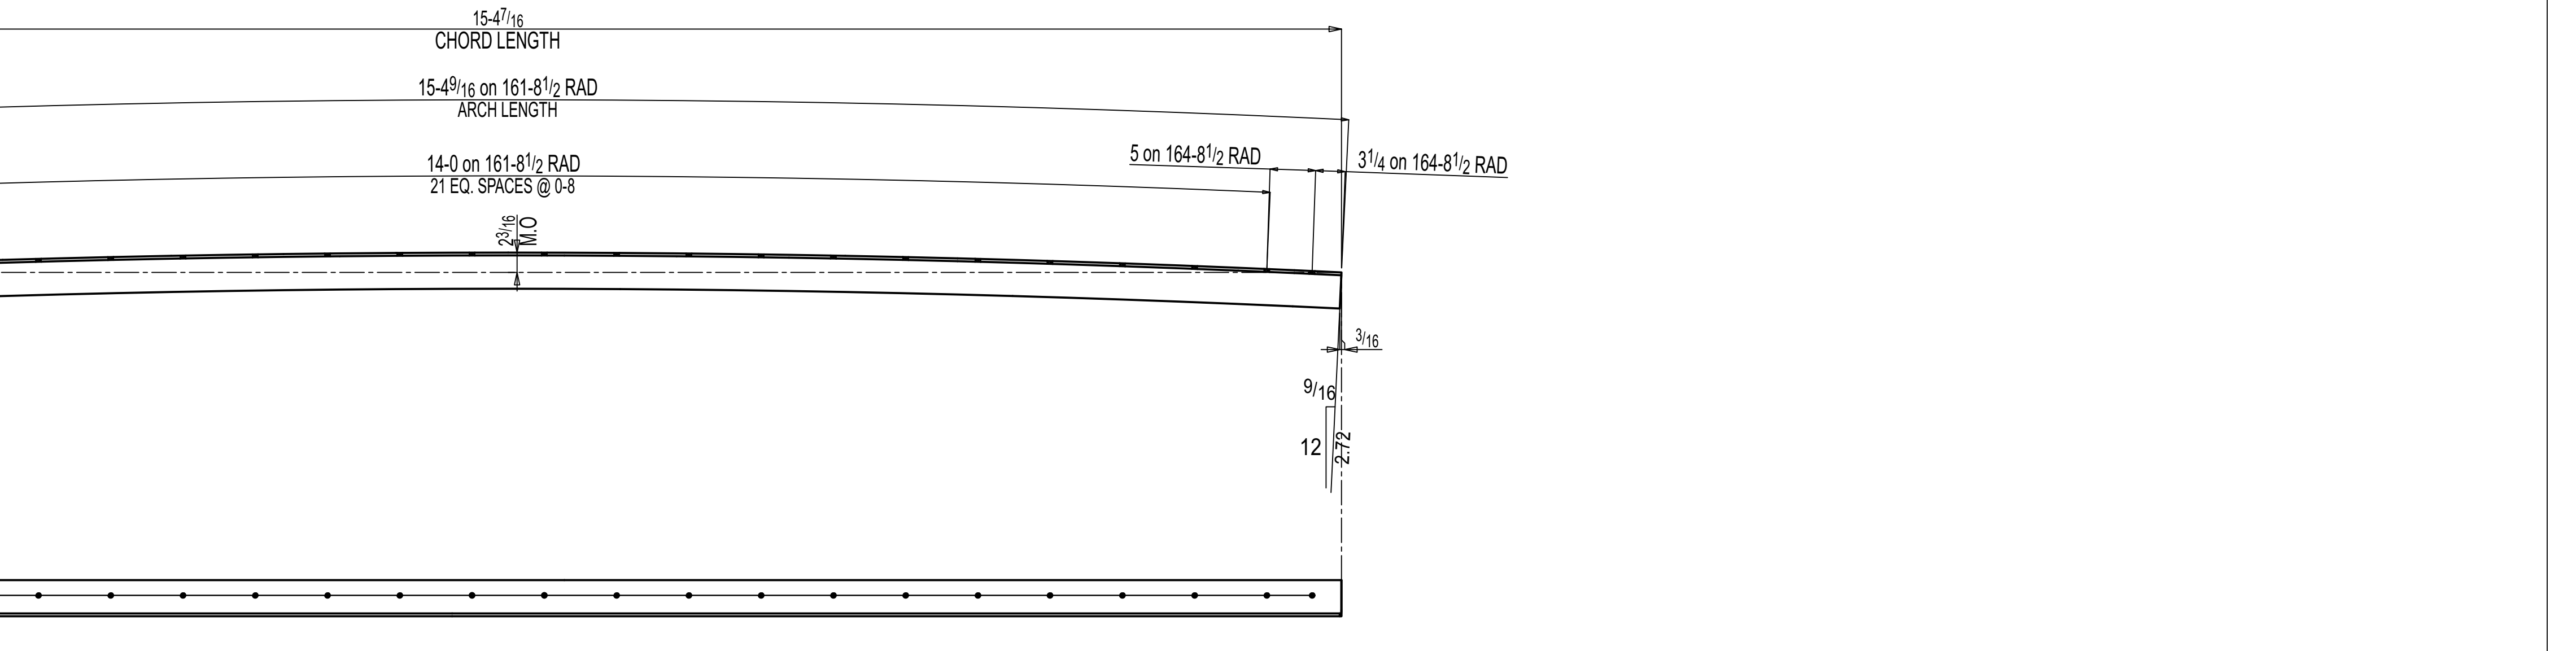

ONE ANGLE F-11.07A2

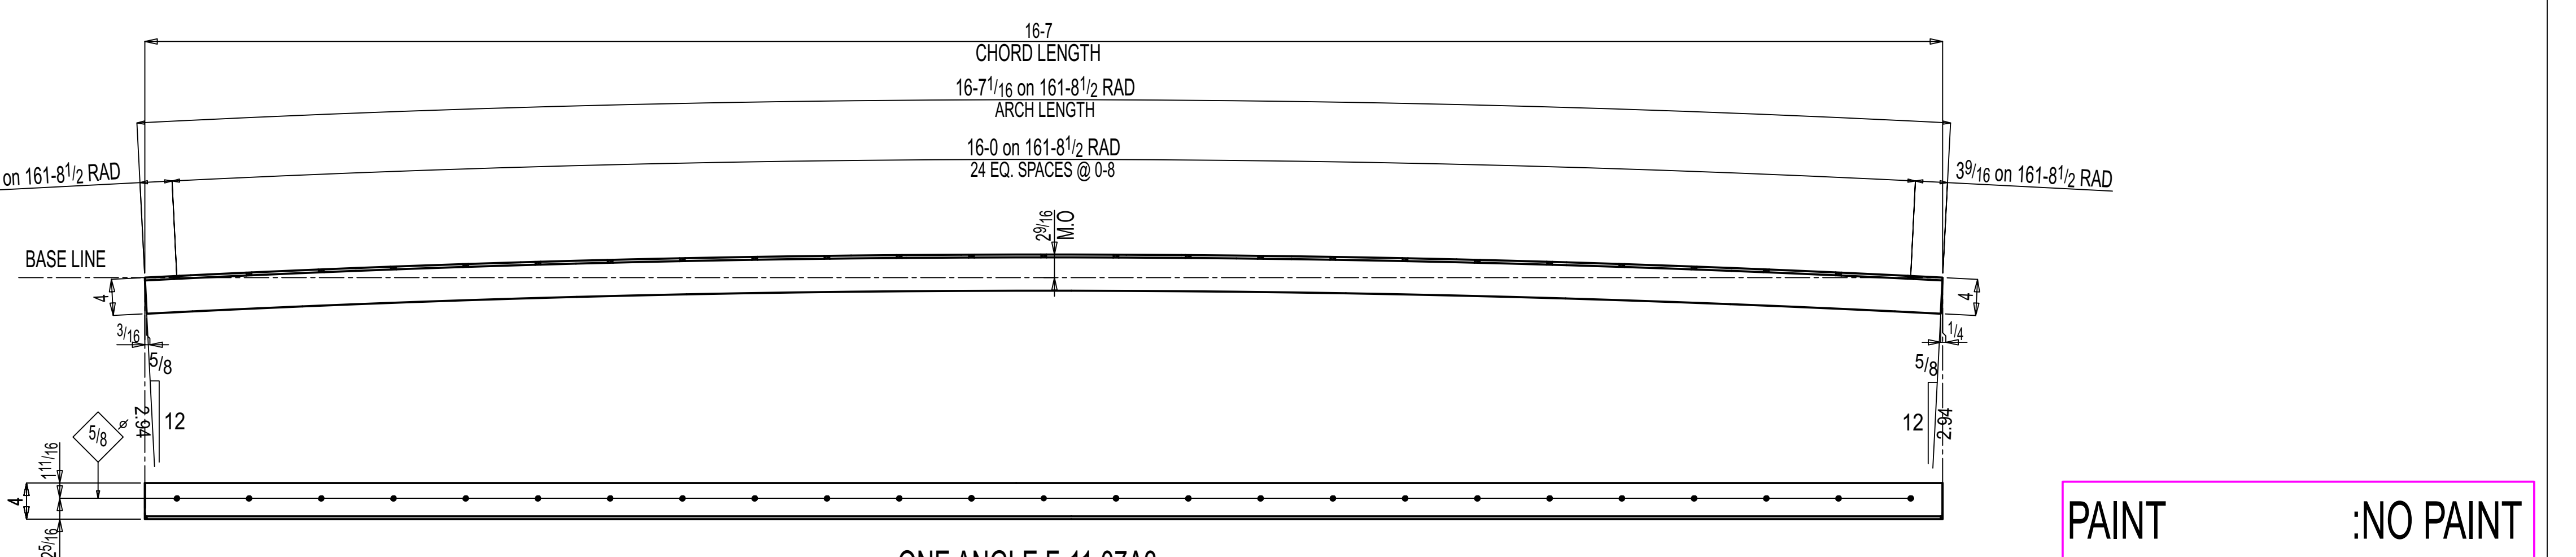

PREPARATION .SSPC-SP3

General Notes

*Structural steel shall conform to ASTM-A992. *Structural SQR/RND.tubing conform to ASTM A500 Grade C *Pipe shall conform to ASTM A53, Grade B. *Channels, Angles and plates shall conform to A36. *All bolts shall be 3/4" High strength in accordance with ASTM A325 (UNO) *Welding Electrodes for Carbon steel :E70xx

4	0	For Fabrication	11-14-2025
3	C	For Re-Approval	10-24-2025
2	B	For Re-Approval	09-19-2025
1	A	For Approval	06-23-2025
# of Copies	Revision/ Issue	Destination	Date

IRON FABRICATION SERVICES, LLC.

3029 M. Street, NW, Suite 202
Washington, DC 20007
Tel: 202-800-5599
Fax: 202-478-0303

Project Name and Address
MARYLAND AVENUE

Location: **1250 MARYLAND AVENUE SW**
WASHINGTON, DC 20024

Contractor: **DALE FOUR BEATTY**

BALFOUR BEATTY

Approved for Fabrication by:	Signature

Contract #	224009
Expiry date	5-11-07

Contract # 22-009	Drawing # F-11.07
Contract Item: FRAME	

Ref:	SOW - 11: E-11.00 - E-11.02
------	------------------------------------

Date 01/ 23/ 2025	Drawing Title: BEAM & MISCELLANEOUS
----------------------	---

Scale VARIES	DETAIL
-----------------	---------------

01/ 23/ 2025	BEAM & MISCELLANEOUS DETAIL
Scale VARIES	

Scale	
VARIES	

PAINT	:NO PAINT
PREPARATION	:SSPC-SP3