

BILL OF MATERIAL							
LINE #	QTY TOTAL	PC MARK	DESCRIPTION	LENGTH	REMARKS	WEIGHT TOTAL	ADVANCE MILL #
	ONE	F-12.00FR1	FRAME			296	
	1	F-12.00FR1	HSS56x69 ⁵ / ₁₆	3 8	A500C	86	
	1	hss3646	HSS56x69 ⁵ / ₁₆	1 10 ³ / ₄	A500C	44	
	1	hss3635	HSS56x69 ⁵ / ₁₆	1 7 ⁷ / ₈	A500C	39	
	1	p1795	PL ¹ / ₂ x216	4 6	A36	123	
	2	p1700	PL ¹ / ₄ x46	0 6	A36	5	
	3	F-12.00FR2	FRAME			743	
	3	F-12.00FR2	HSS56x69 ⁵ / ₁₆	3 5 ³ / ₄	A500C	244	
	3	w2797	W8x31	1 4	A992	124	
	3	p1795	PL ¹ / ₂ x216	4 6	A36	368	
	3	p1700	PL ¹ / ₄ x46	0 6	A36	8	
	ONE	F-12.00FR3	FRAME			296	
	1	F-12.00FR3	HSS56x69 ⁵ / ₁₆	3 7 ³ / ₄	A500C	85	
	1	hss304	HSS56x69 ⁵ / ₁₆	1 10 ⁹ / ₁₆	A500C	44	
	1	hss305	HSS56x69 ⁵ / ₁₆	1 8 ⁷ / ₁₆	A500C	40	
	1	p1795	PL ¹ / ₂ x216	4 6	A36	123	
	1	p13248	PL ¹ / ₂ x46	0 6 ³ / ₈	A36	3	
	1	p1700	PL ¹ / ₄ x46	0 6	A36	3	
	ONE	F-12.00FR4	FRAME			356	
	1	F-12.00FR4	HSS56x69 ⁵ / ₁₆	3 7 ¹ / ₈	A500C	84	
	1	hss3791	HSS56x69 ⁵ / ₁₆	3 6 ³ / ₄	A500C	83	
	1	hss2702	HSS56x69 ⁵ / ₁₆	2 6 ¹ / ₄	A500C	59	
	1	p1795	PL ¹ / ₂ x216	4 6	A36	123	
	3	p1700	PL ¹ / ₄ x46	0 6	A36	8	
	6	F-12.00M1	THREADED ROD			16	
	6	F-12.00M1	1" Ø THREADED ROD w/ HILTI HIT HY-200 V3 ADHESIVE	1 0	F1554 GR. 55 (8" EMBEDMENT)	16	
	6		1 NUT		HHNT A563		
	64	F-12.00M2	THREADED ROD			121	
	64	F-12.00M2	1" Ø THREADED ROD w/ HILTI HIT HY-200 V3 ADHESIVE	0 8 ¹ / ₂	F1554 GR. 55 (6" EMBEDMENT)	121	
	64		1 NUT		HHNT A563		
	64		1 WASHER		HD F436		
	ONE	F-12.00M3	HSS			145	
	1	F-12.00M3	HSS55x39 ⁵ / ₁₆	9 7 ¹ / ₂	A500C	143	
	2	p1582	PL ¹ / ₂ x43	0 5	A36	2	

Total weight : 1973



General Notes			
*Structural steel shall conform to ASTM-A992.			
*Structural SQR/RND.tubing conform to ASTM A500 Grade C			
*Pipe shall conform to ASTM A53, Grade B.			
*Channels, Angles and plates shall conform to A36.			
*All bolts shall be 3/4" High strength in accordance with ASTM A325 (UNO)			
*Welding Electrodes for Carbon steel :E70xx			
5	O	For Fabrication	11-14-2025
4	D	For Re-Approval	10-24-2025
3	C	For Re-Approval	09-19-2025
2	B	For Re-Approval	06-23-2025
1	A	For Approval	02-25-2025
# of	Revision/	Destination	Date

3029 M. Street, NW, Suite 202
Washington, DC 20007
Tel: 202-800-5599
Fax: 202-478-0303

Contractor: **BALFOUR BEATTY**

Contract # 224009	Drawing # F-12.00
--------------------------	--------------------------

Contract Item: **FRAME & THREADED ROD**


Ref:

SOW - 12: E-12.00 - E-12.02


Date 01/ 23/ 2025	Drawing Title: FRAME DETAIL
Scale VARIES	

BILL OF MATERIAL							
LINE #	QTY	PC	MARK	DESCRIPTION	LENGTH	WEIGHT	ADVANCE
	TOTAL					TOTAL	MILL #
ONE F-12.01FR1 FRAME							
1	F-12.01FR1	HSS6x6x3/16		3	73/4	A500C	85
1	hss303	HSS6x6x3/16		2	11/16	A500C	49
1	hss302	HSS6x6x3/16		2	01/4	A500C	47
1	p3504	PL1/2x16		4	9	A36	129
2	p700	PL1/4x6		0	6	A36	5
ONE F-12.01FR2 FRAME							
1	F-12.01FR2	HSS6x6x3/16		3	73/4	A500C	85
1	hss399	HSS6x6x3/16		4	115/16	A500C	115
1	hss300	HSS6x6x3/16		4	83/16	A500C	109
1	p795	PL1/2x16		4	6	A36	123
1	p3236	PL1/4x6		0	77/16	A36	3
1	p700	PL1/4x6		0	6	A36	3
ONE F-12.01M1 PLATE							
1	F-12.01M1	PL1x18		2	1	A36	128
1	p288	PL1x8		1	6	A36	41
3	p280	PL1/2x7		0	7	A36	21
ONE F-12.01M2 PLATE							
1	F-12.01M2	PL3/4x6		1	3	A36	19
2	p3620	PL3/4x6		0	7	A36	18
ONE F-12.01M3 HSS							
1	F-12.01M3	HSS51/2x51/2x3/16		1	75/8	A500C	24
2	p701	PL1/4x51/2		0	51/2	A36	4
6	F-12.01M4	PLATE WASHER					8
6	F-12.01M4	PL1/2x3		0	3	A36	8
ONE F-12.01EP1 EMBED PLATE							
1	F-12.01EP1	PL5/8x22		4	11	A36	230
FIELD BOLTS							
10		3/4 Dia HILTI HAS V-36		0	8	+1HD WASH	
		w/ HILTI HIT HY-200 V3				(5" EMBEDMENT)	
		ADHESIVE					
ONE F-12.01LP1 LEVELING PLATE							
1	F-12.01LP1	PL1/4x7		1	6	A36	9
ONE F-12.01LP2 LEVELING PLATE							
1	F-12.01LP2	PL1/4x61/2		1	6	A36	8


Total weight : 1263

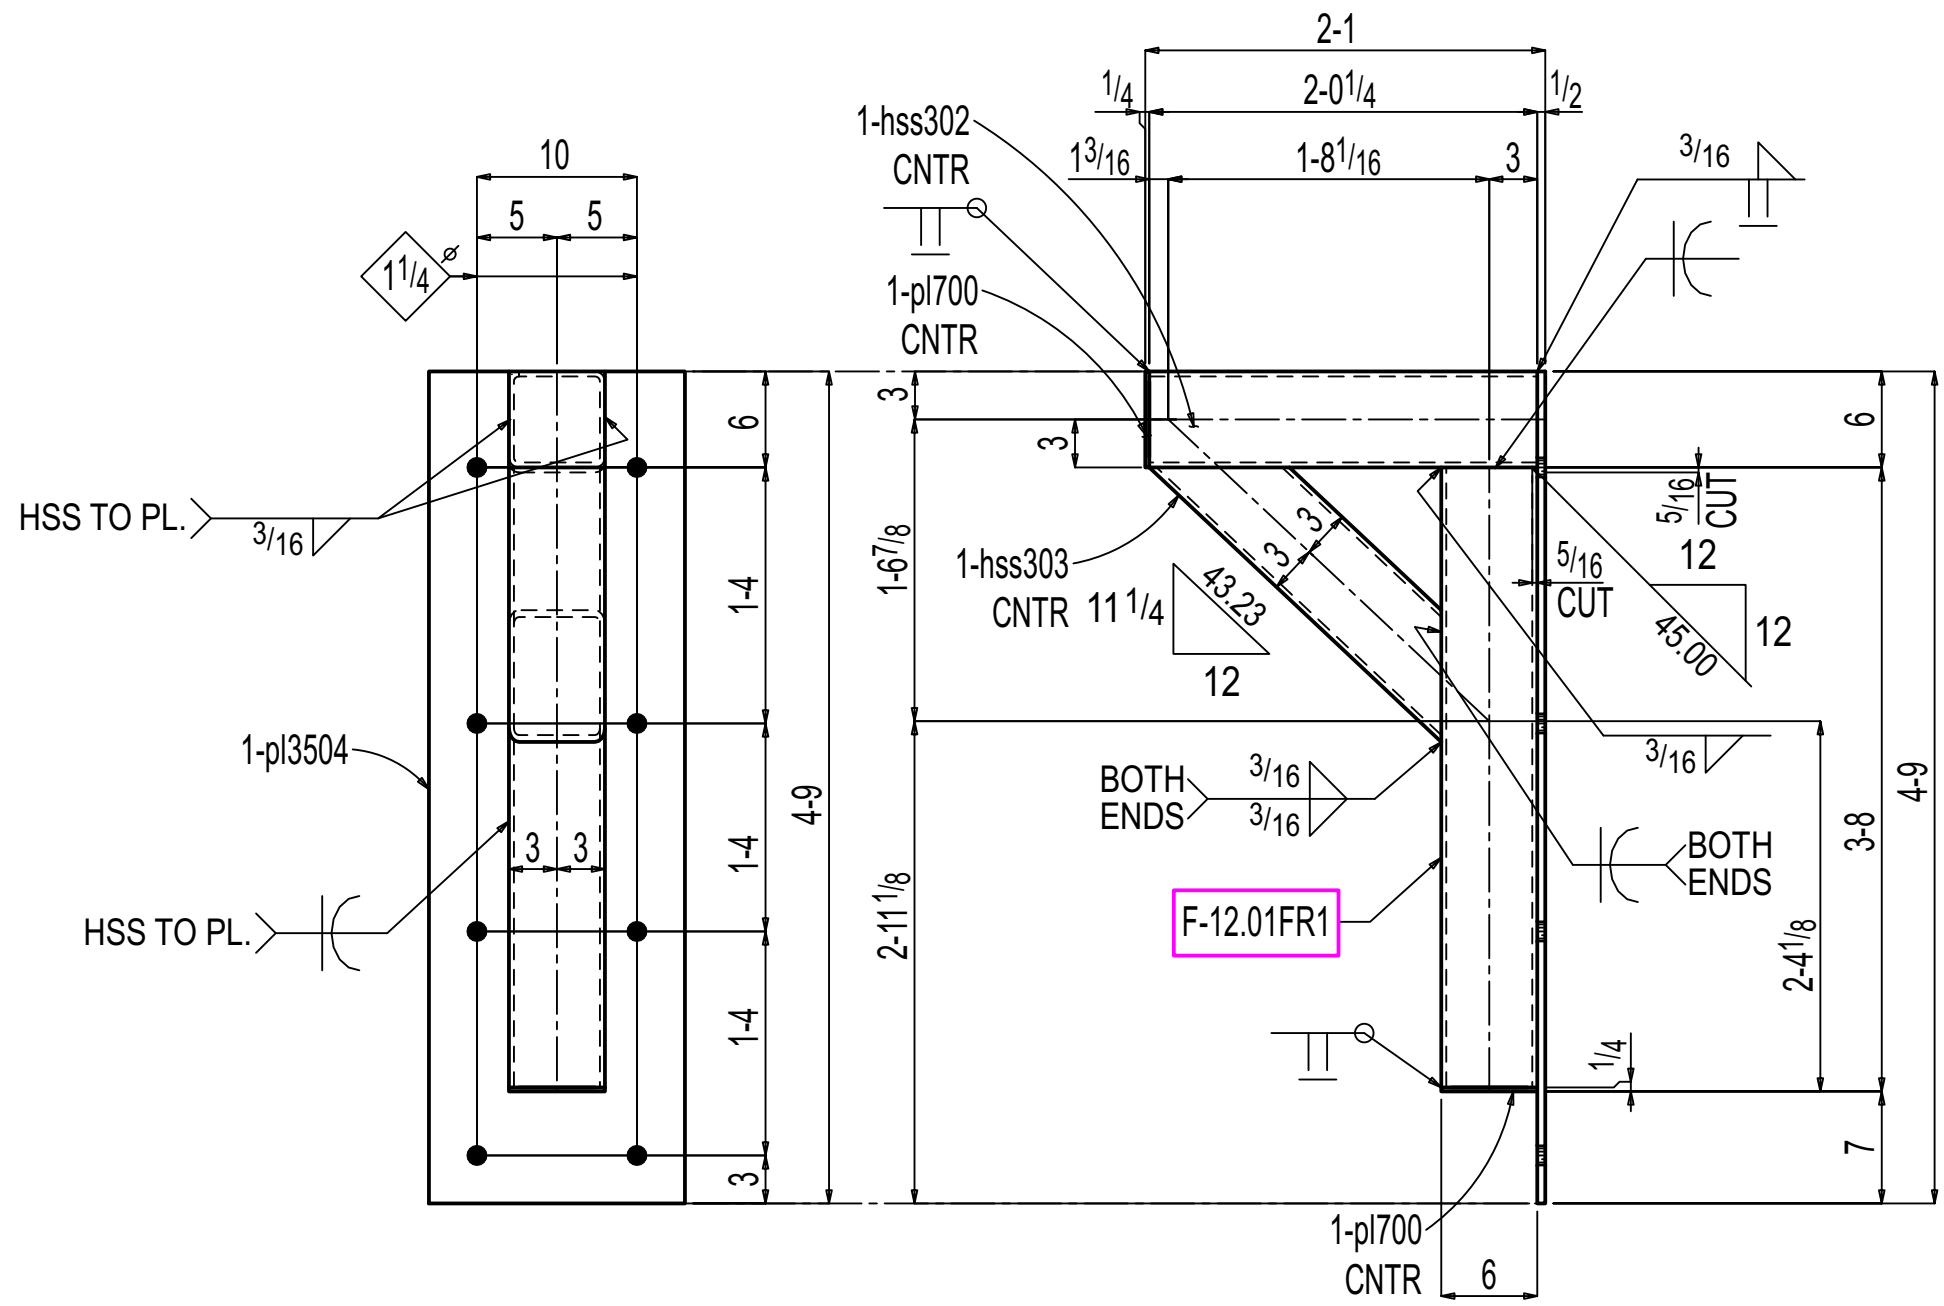


ONE FRAME F-12.01FR1

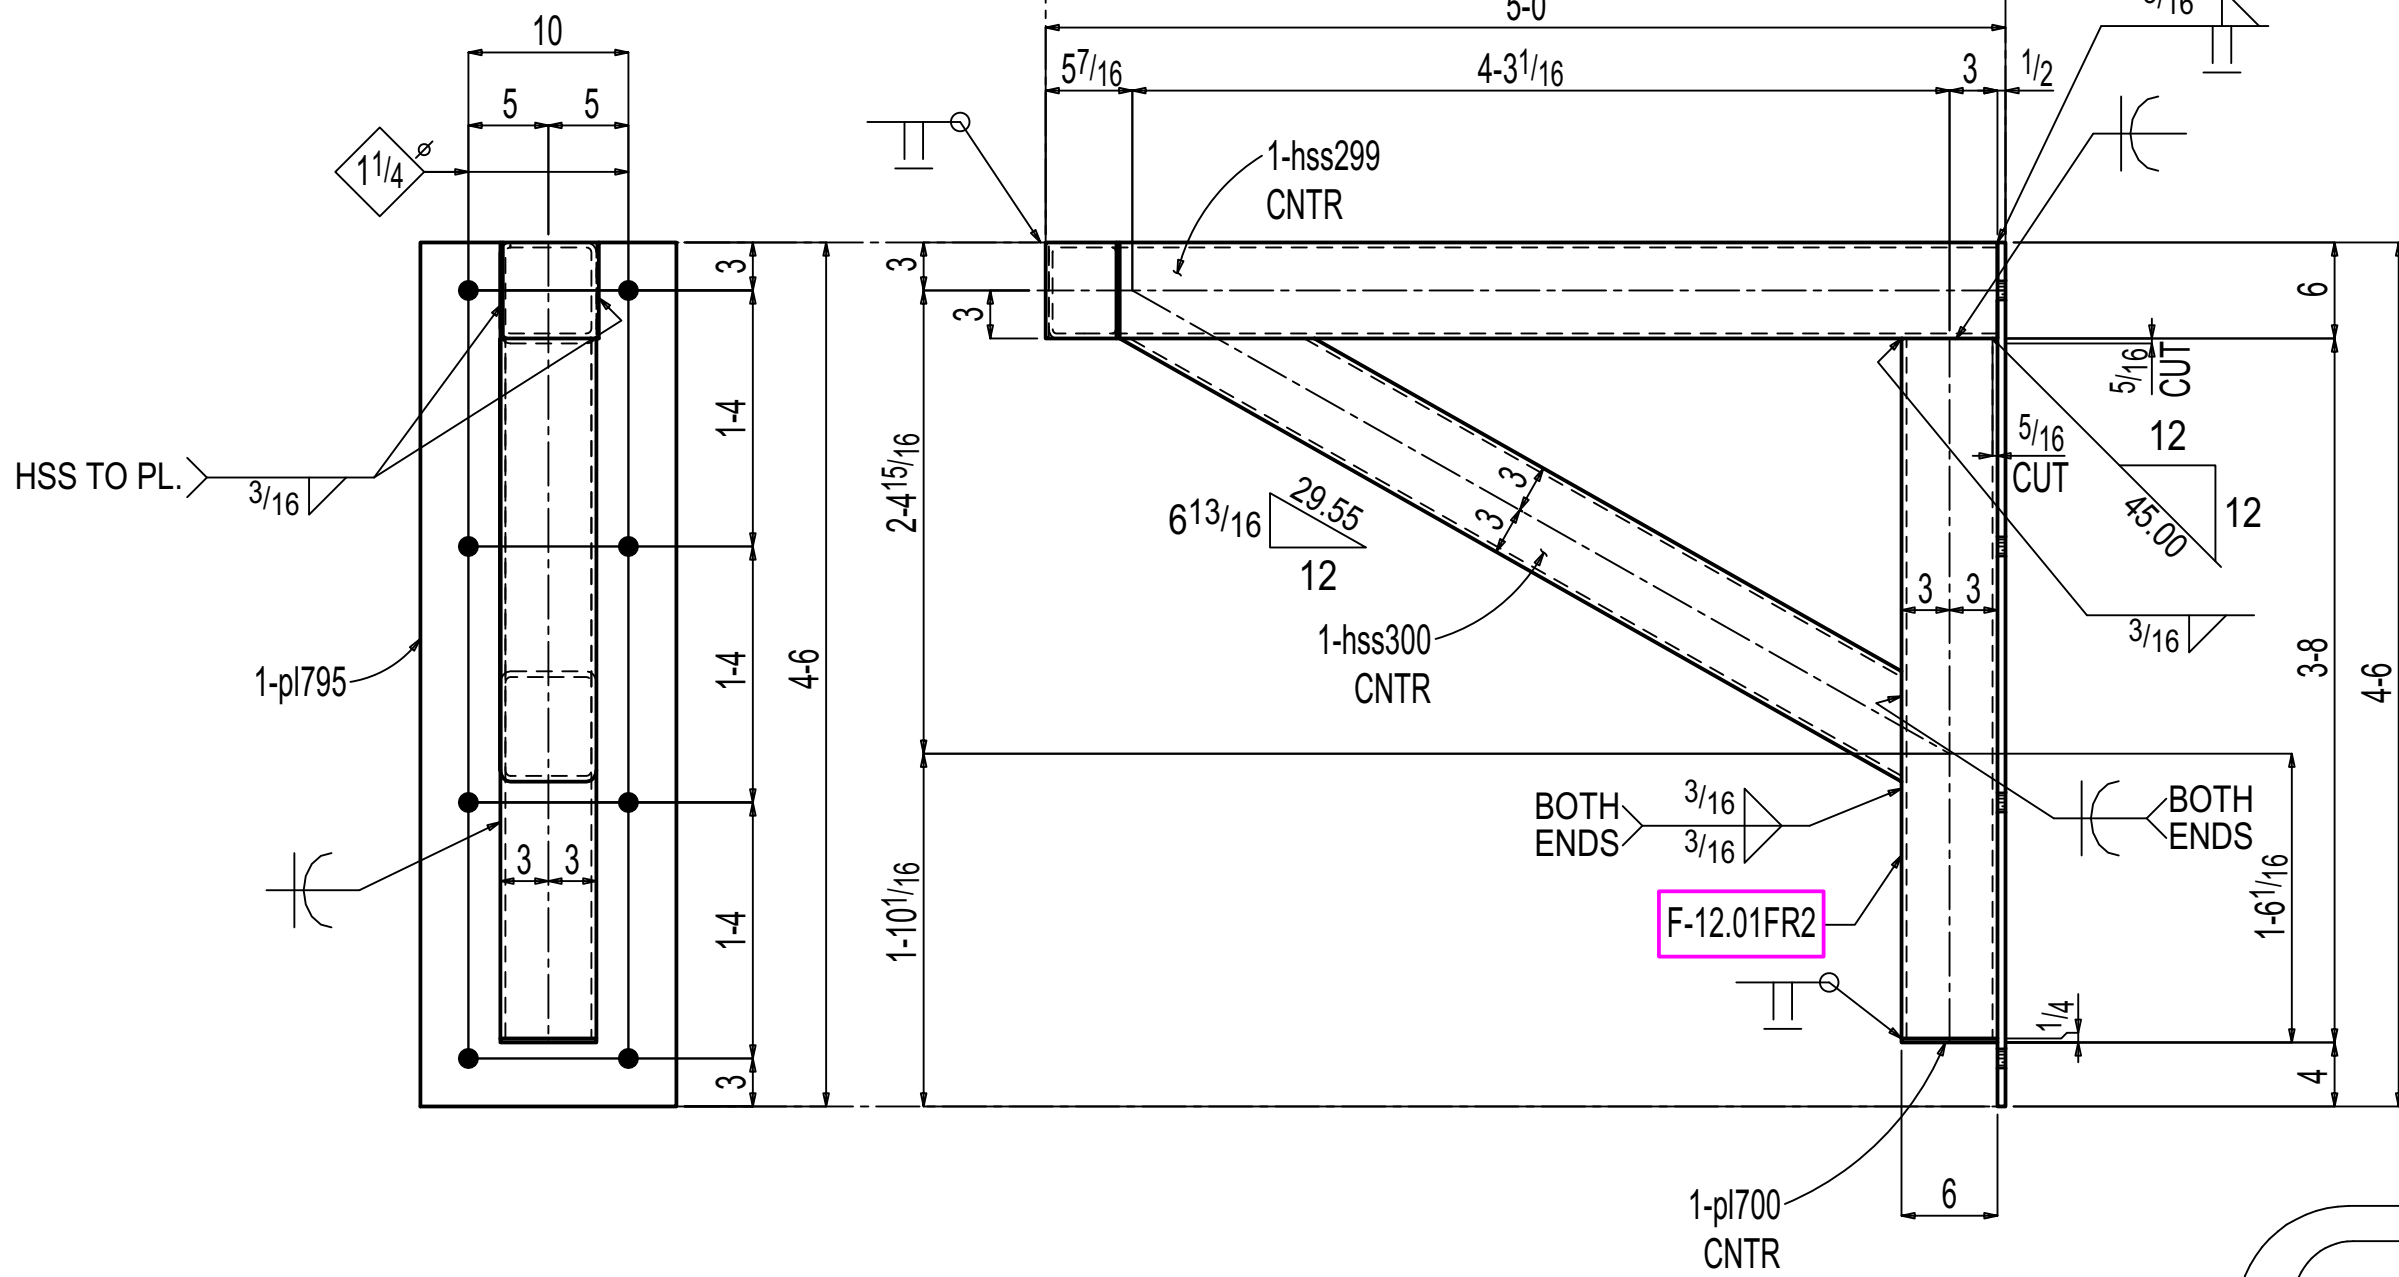


ONE FRAME F-12.01FR2

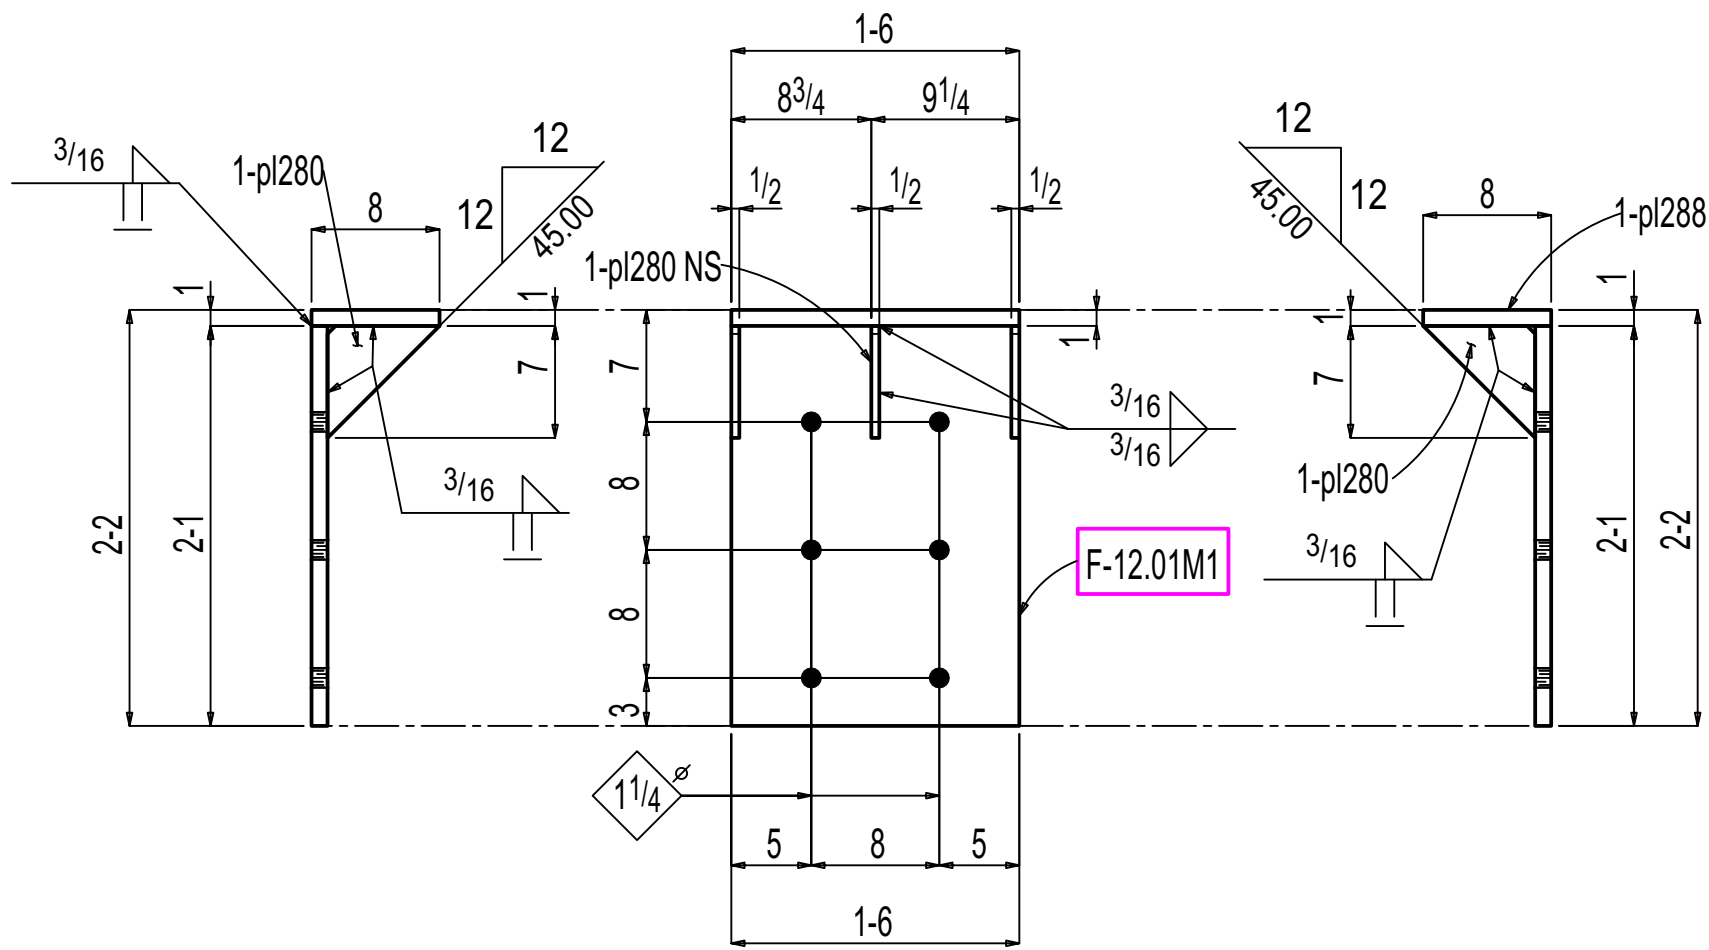


ONE PLATE F-12.01M1

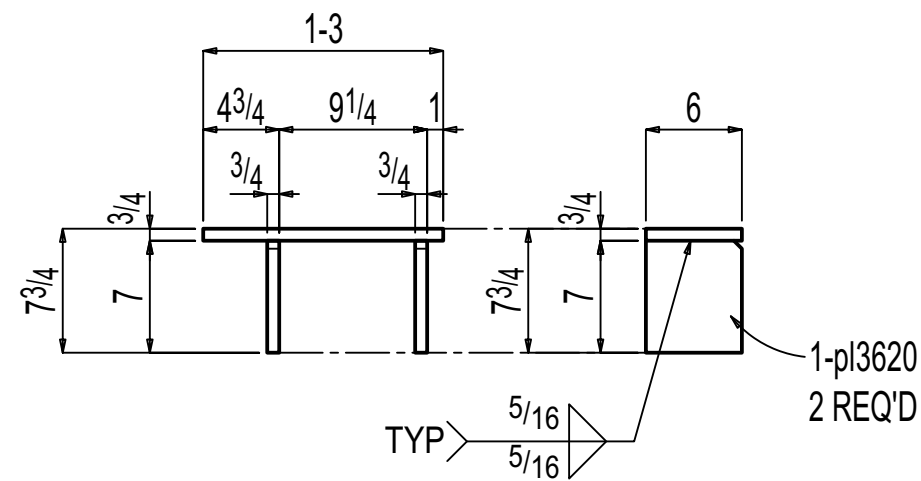

ONE PLATE F-12.01M2

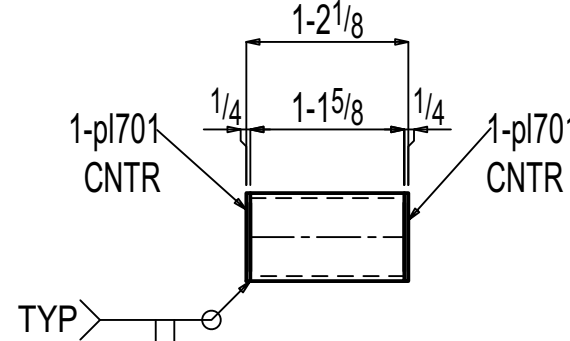


ONE HSS F-12.01M3

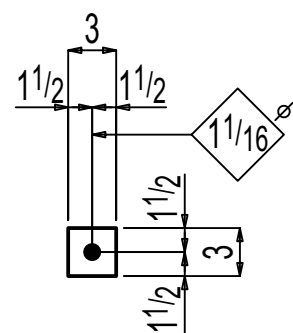


6 PLATE WASHERS F-12.01M4

NOT IN USE


F-12.01M5

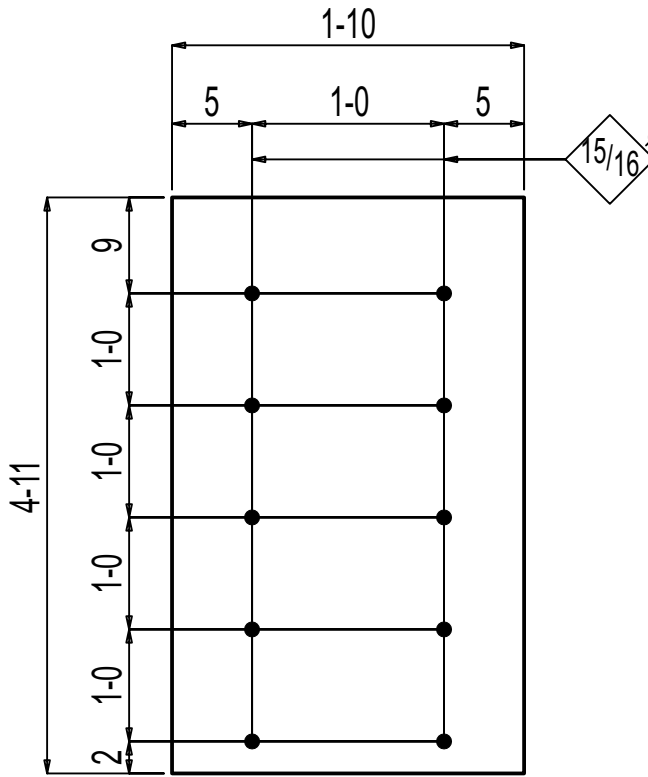

ONE EMBED PLATE F-12.01EP1

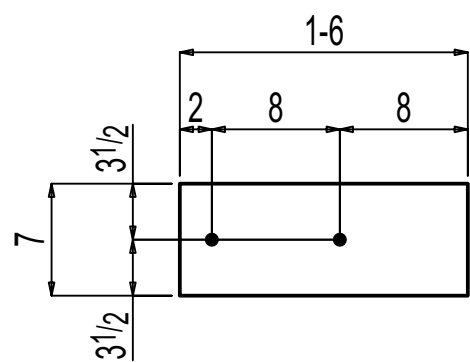

ONE LEVELING PLATE F-12.01LP1

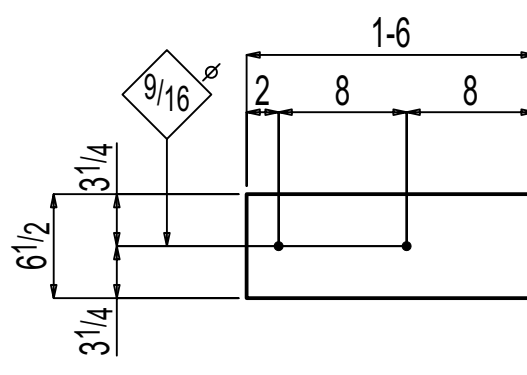

ONE LEVELING PLATE F-12.01LP2

PAINT PREPARATION :NO PAINT :SSPC-SP3

General Notes			
*Structural steel shall conform to ASTM-A992.			
*Structural SQR/RND,tubing conform to ASTM A500 Grade C			
*Pipe shall conform to ASTM A53, Grade B.			
*Channels, Angles and plates shall conform to A36.			
*All bolts shall be 3/4" High strength in accordance with ASTM A325 (UNO)			
*Welding Electrodes for Carbon steel :E70xx			
5	0	For Fabrication	11-14-2025
4	D	For Re-Approval	10-24-2025
3	C	For Re-Approval	09-19-2025
2	B	For Re-Approval	06-23-2025
1	A	For Approval	02-25-2025
# of Copies	Revision/ Issue	Destination	Date

IRON FABRICATION SERVICES, LLC.

3029 M. Street, NW, Suite 202
Washington, DC 20007
Tel: 202-800-5599
Fax: 202-478-0303

Project Name and Address
MARYLAND AVENUE
Location: **1250 MARYLAND AVENUE SW
WASHINGTON, DC 20024**


Contractor:
BALFOUR BEATTY

Approved for Fabrication by: Signature

Contract #	224009	Drawing #	F-12.01
Contract Item:	FRAME,HSS & THREADED ROD		
Ref:	SOW - 12: E-12.00 - E-12.02		
Date	01/ 23/ 2025	Drawing Title:	FRAME & MISCELLANEOUS DETAIL
Scale	VARIES		


BILL OF MATERIAL							
LINE #	QTY	PC	MARK	DESCRIPTION	LENGTH	REMARKS	WEIGHT
	TOTAL						TOTAL
							MILL #
ONE	F-12.02C1	COLUMN					329
1	F-12.02C1	HSS6x6x3/8		10 4	A500C		284
1	p1974	PL1/4x7		1 6	A36		45
		FIELD BOLTS					
2		3/4 Dia HILTI HAS V-36		0 8	+1HD WASH		
		w/ HILTI HIT HY-200 EPOXY			(3/4" EMBEDMENT)		
ONE	F-12.02C2	COLUMN					335
1	F-12.02C2	HSS6x6x3/8		9 10 3/8	A500C		272
1	hss124	HSS4x4x3/16		1 6 1/4	A500C		23
1	hss123	HSS4x4x3/16		1 0 7/8	A500C		16
1	a115	L1 1/2x1x3/16		0 5	A36		1
1	p356	PL3/8x6 1/2		1 6	A36		21
1	p3633	PL1/4x5 5/8		0 5 5/8	A36		2
1	p3634	PL1/4x4		0 4	A36		1
ONE	F-12.02B1	BEAM					1430
1	F-12.02B1	W12x79		18 1 1/4	A992		1430
ONE	F-12.02B2	BEAM					463
1	F-12.02B2	HSS12x4x3/8		12 13/8	A500C		457
2	p3645	PL1/4x4		1 0	A36		7
ONE	F-12.02B3	BEAM					101
1	F-12.02B3	HSS6x4x3/8		4 5 7/16	B1E A500C		100
1	p274	PL1/4x4		0 6	A36		2
ONE	F-12.02B4	BEAM					565
1	F-12.02B4	HSS6x4x3/8		25 0 3/16	A500C		560
1	fb324	FL3/8x4		0 5 5/8	A36		2
1	p275	PL1/4x4 1/4		0 6	A36		2
1	p274	PL1/4x4		0 6	A36		2

Total weight : 3224

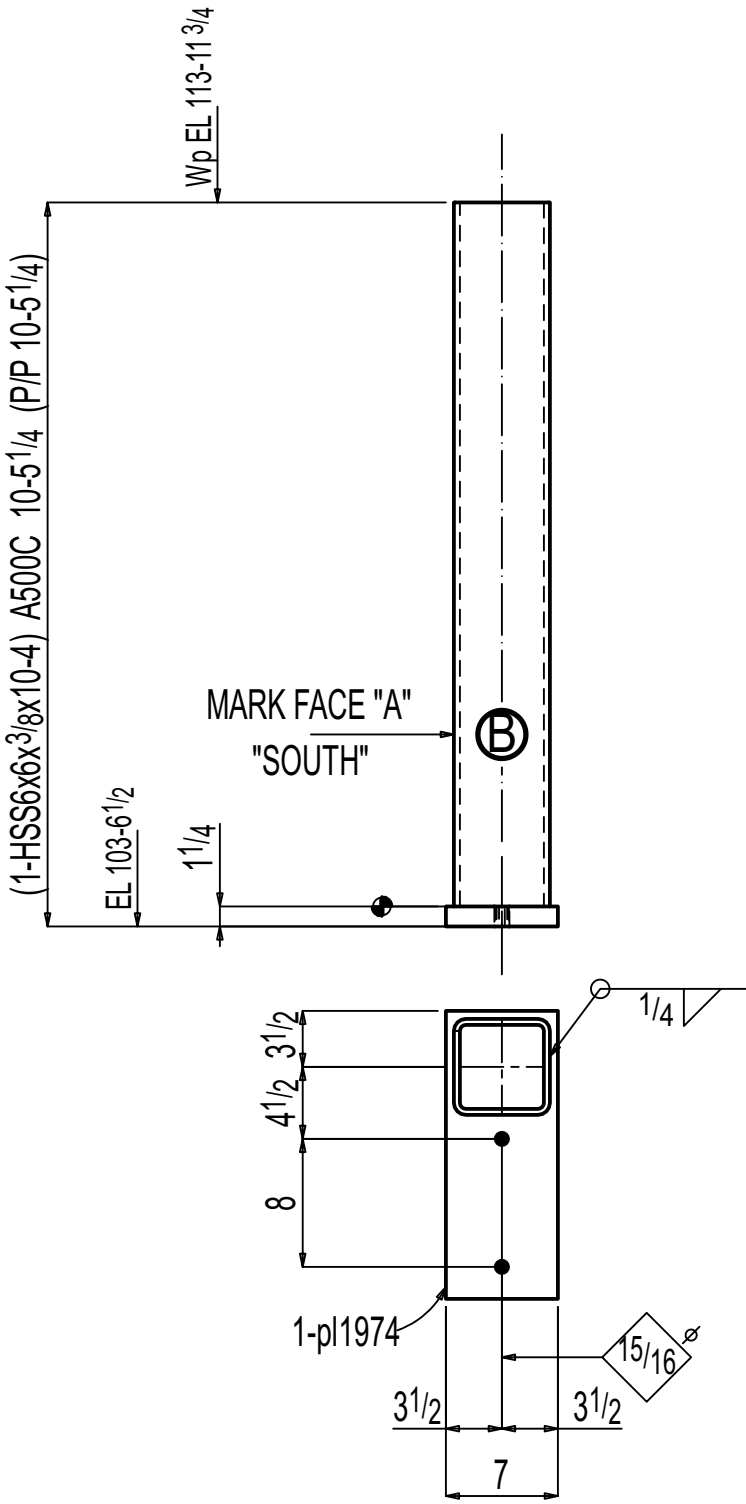


ONE COLUMN F-12.02C1

AT GRID:
EE & A

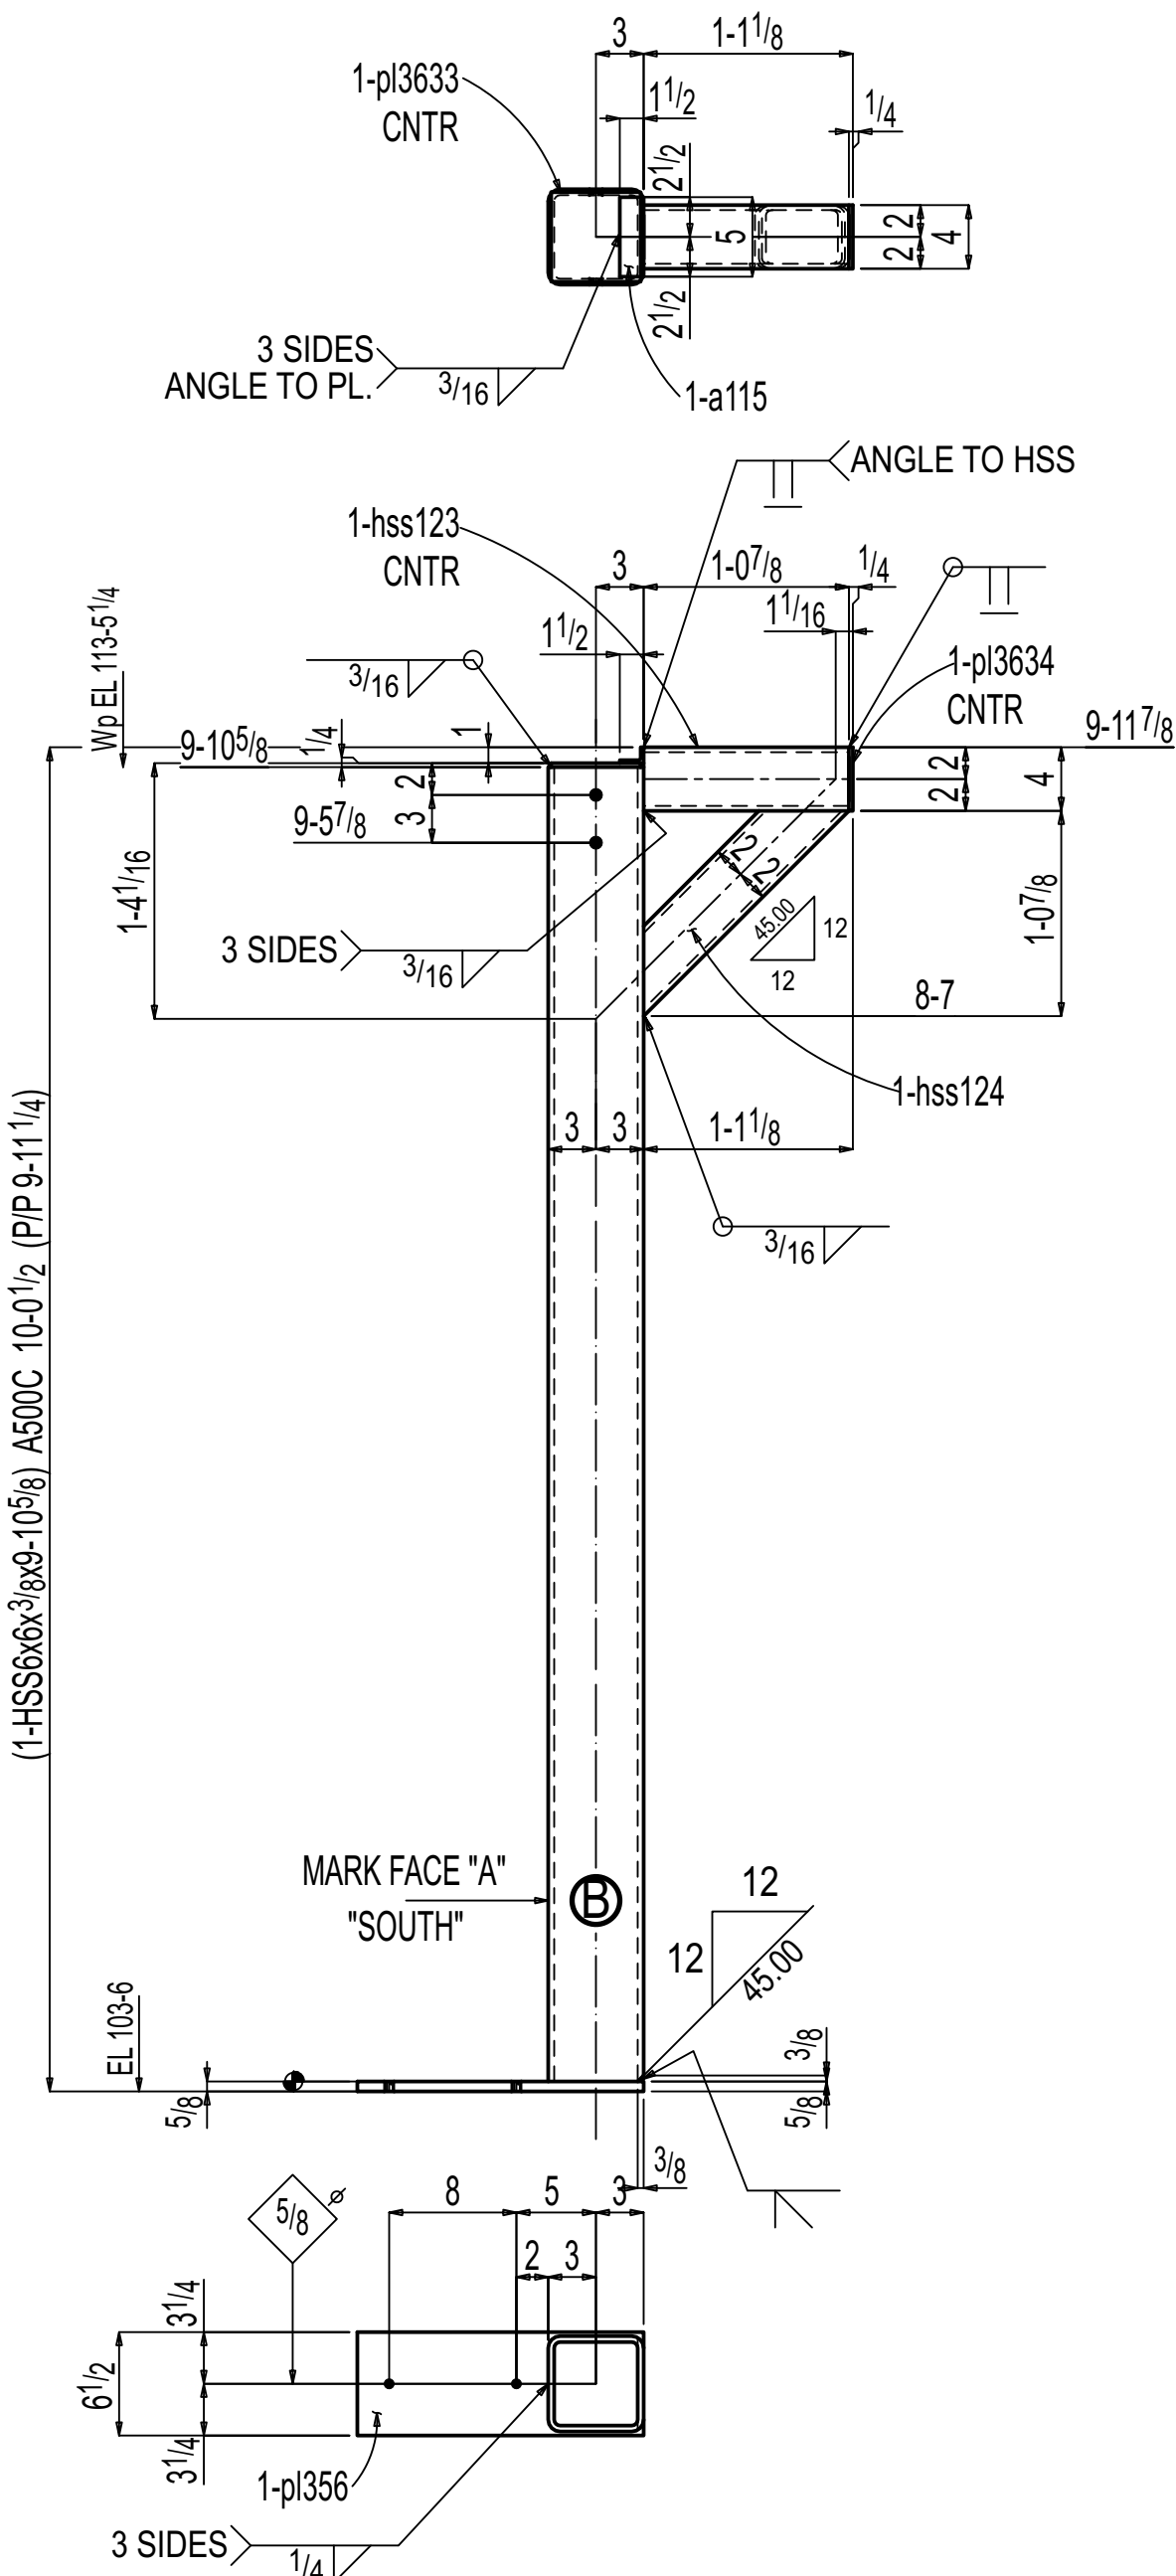


ONE COLUMN F-12.02C2

AT GRID:
AA & K

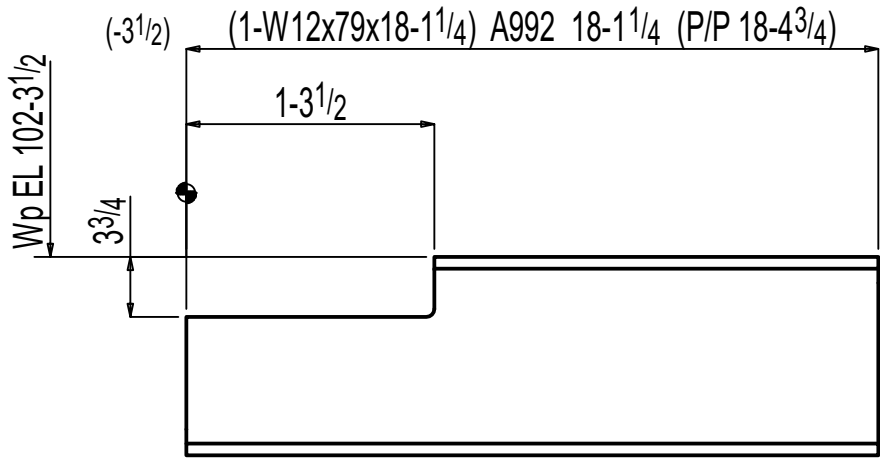


ONE BEAM F-12.02B1

W 12 3/8x1 1/2
F 12 1/8x3/4
K 15/8x1 1/8

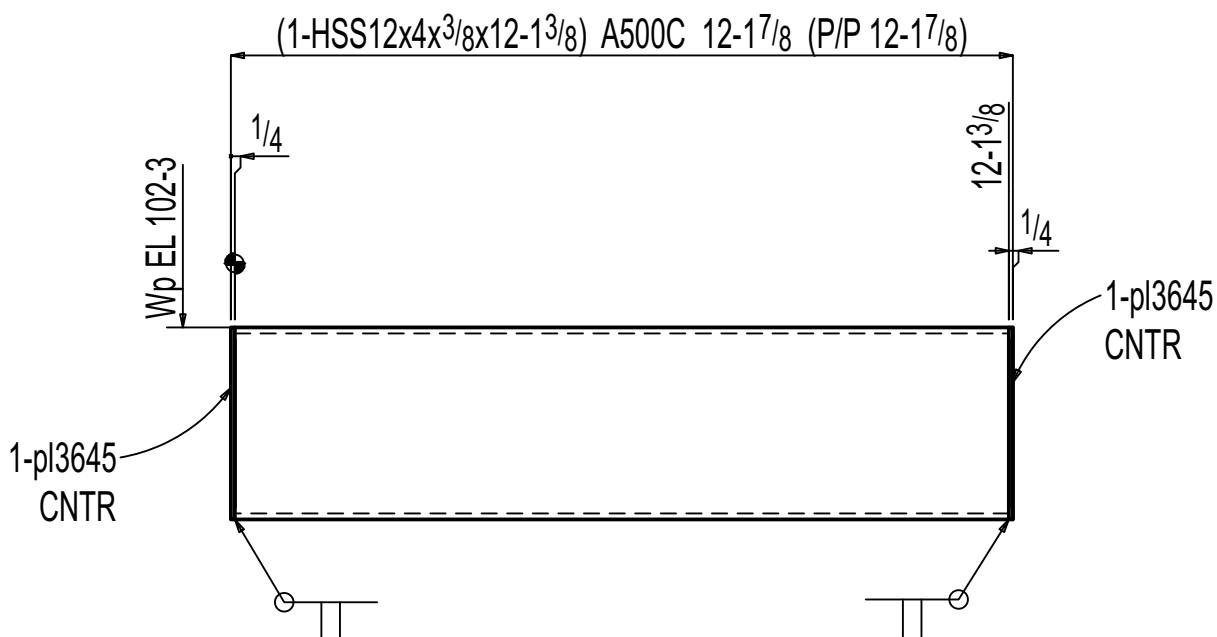


ONE BEAM F-12.02B2

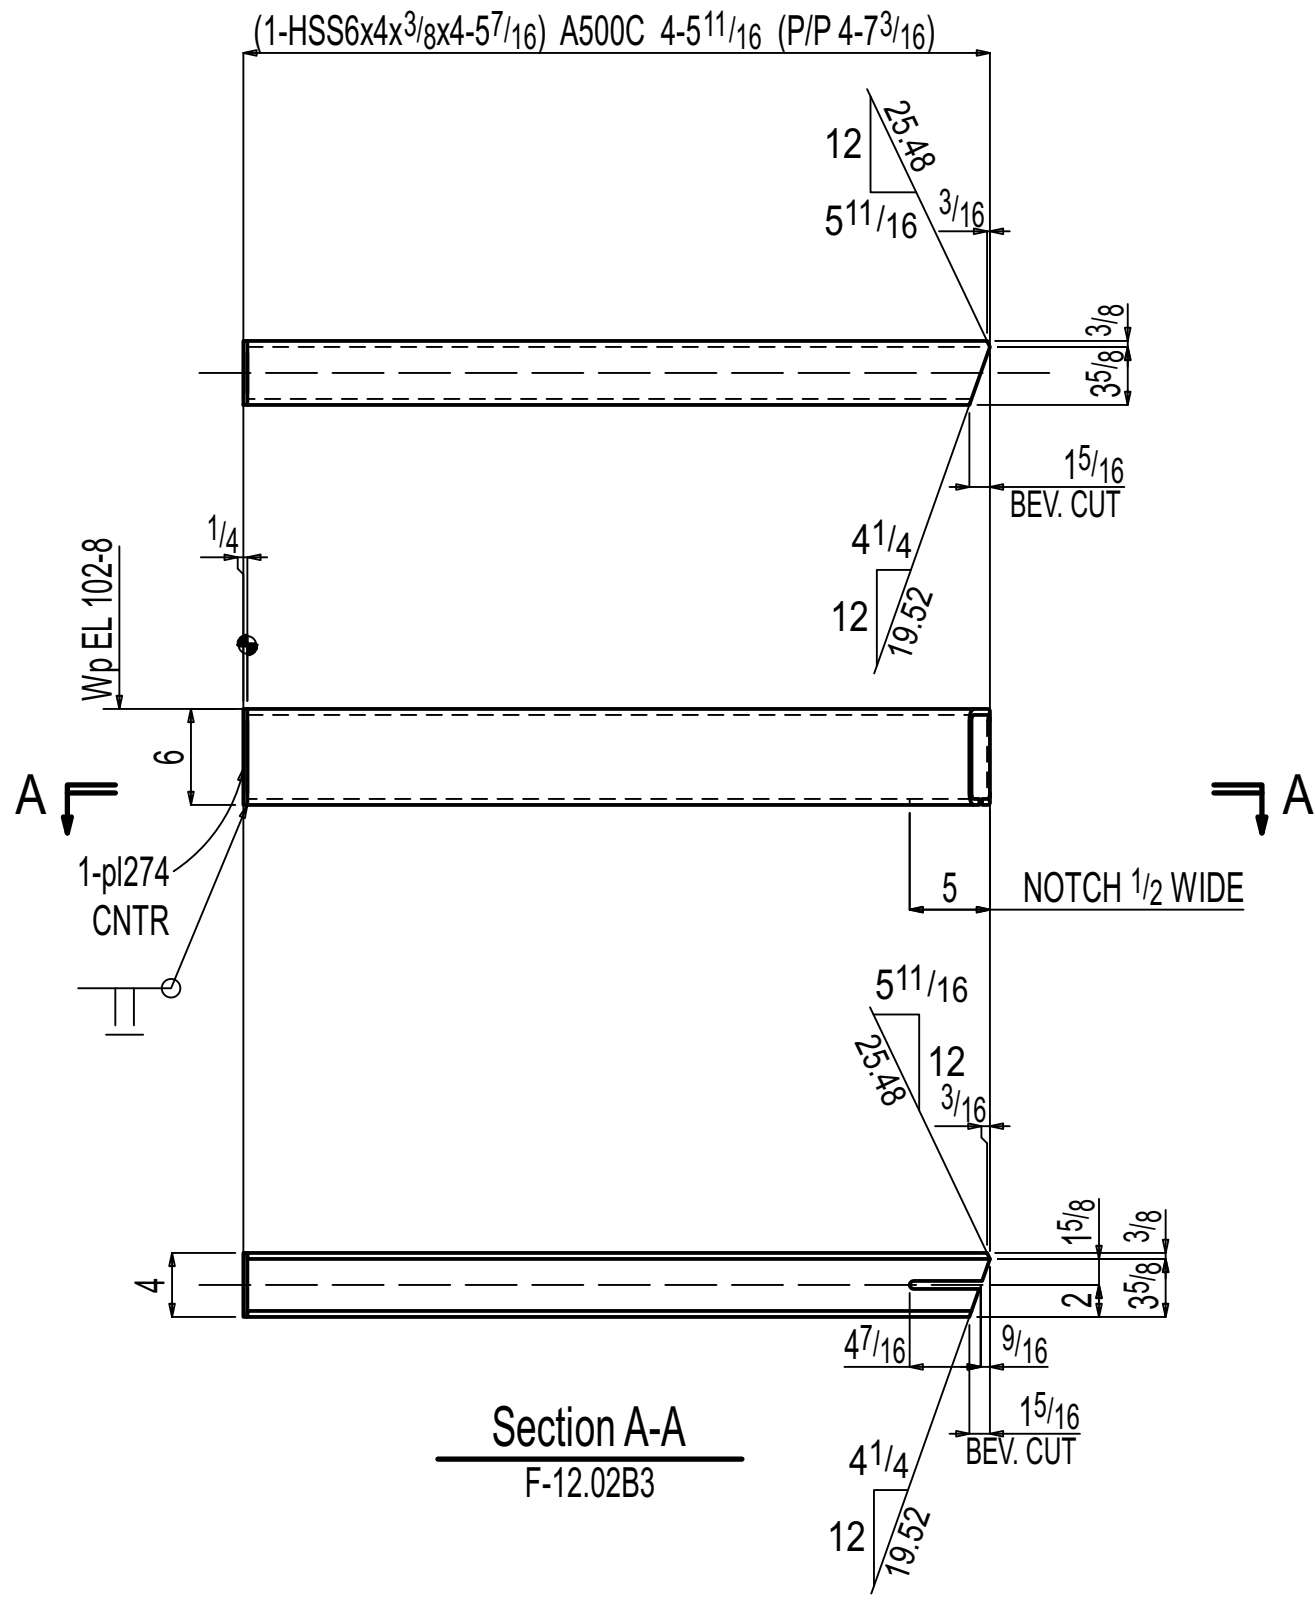

ONE BEAM F-12.02B3

Section A-A
F-12.02B3

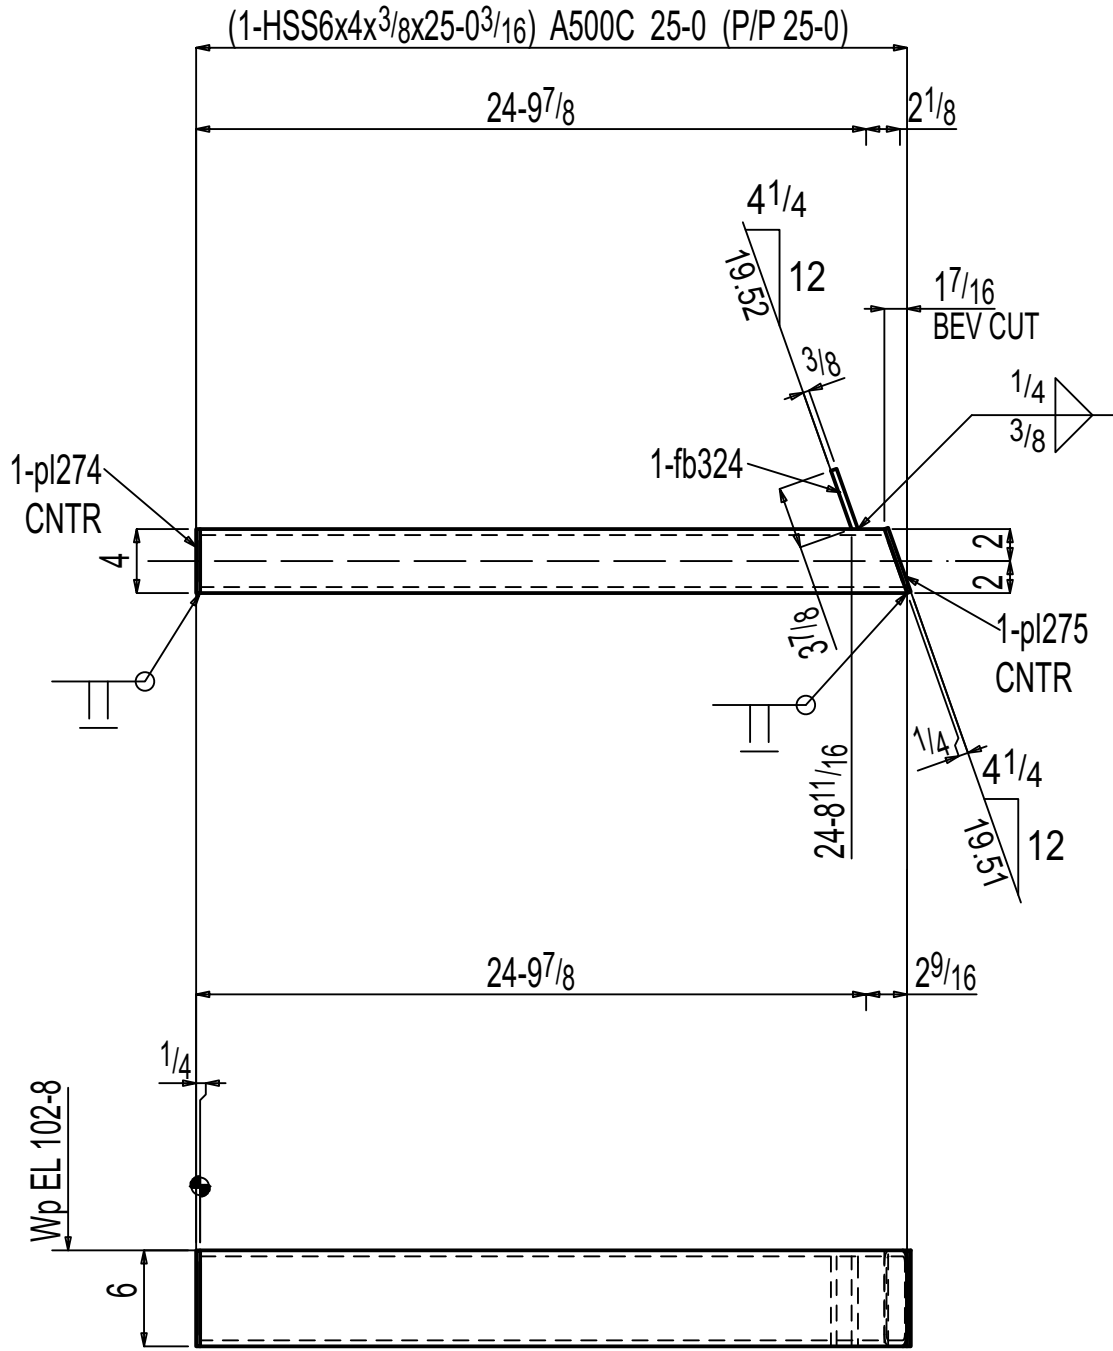

ONE BEAM F-12.02B4

PAINT :NO PAINT
PREPARATION :SSPC-SP3

General Notes			
*Structural steel shall conform to ASTM-A992.			
*Structural SQR/RND,tubing conform to ASTM A500 Grade C			
*Pipe shall conform to ASTM A53, Grade B.			
*Channels, Angles and plates shall conform to A36.			
*All bolts shall be 3/4" High strength in accordance with ASTM A325 (UNO)			
*Welding Electrodes for Carbon steel :E70xx			
5	0	For Fabrication	11-14-2025
4	D	For Re-Approval	10-24-2025
3	C	For Re-Approval	09-19-2025
2	B	Deleted	06-23-2025
1	A	For Approval	02-25-2025
# of Copies	Revision/ Issue	Destination	Date

IRON FABRICATION SERVICES, LLC.

3029 M. Street, NW, Suite 202
Washington, DC 20007
Tel: 202-800-5599
Fax: 202-478-0303

Project Name and Address
MARYLAND AVENUE
Location: **1250 MARYLAND AVENUE SW
WASHINGTON, DC 20024**

Contractor:
BALFOUR BEATTY

Approved for Fabrication by: Signature


Contract #	224009	Drawing #	F-12.02
Contract Item:	COLUMN & BEAM		
Ref:	SOW - 12: E-12.00 - E-12.02		
Date	01/ 23/ 2025	Drawing Title:	COLUMN & BEAM DETAIL
Scale	VARIABLES		

BILL OF MATERIAL							
LINE #	QTY	PC MARK	DESCRIPTION	LENGTH	REMARKS	WEIGHT TOTAL	ADVANCE MILL #
	ONE	F-12.03P2	PLATE			3	
	1	F-12.03P2	PL3/8x4	0 6	A36	3	
	ONE	F-12.03P3	PLATE			55	
	1	F-12.03P3	PL1 1/4x7	1 10	A36	55	
			FIELD BOLTS				
	2		3/4 Dia HILTI KWIK HUS-EZ	0 7	(3 1/4" EMBEDMENT)		
			SCREW ANCHOR				
	2	F-12.03M1	THREADED ROD			1	
	2	F-12.03M1	1/2"Ø THREADED ROD	0 6	F1554 GR. 55	1	
	2		1/2 NUT		HHINT A563		
	2		1/2 WASHER		HD F436		
	ONE	F-12.03A1	ANGLE			2	
	1	F-12.03A1	L4x4x1/4	0 4	A36	2	


Total weight : 60

NOT IN USE


F-12.03P1

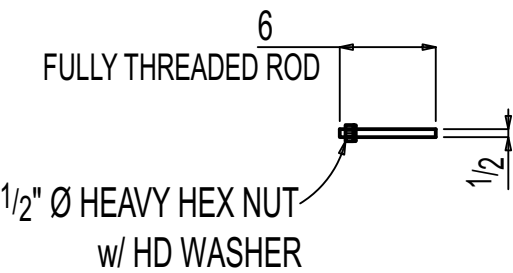


2 THREADED RODS F-12.03M1

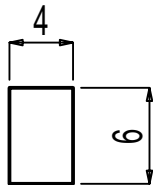

ONE PLATE F-12.03P2

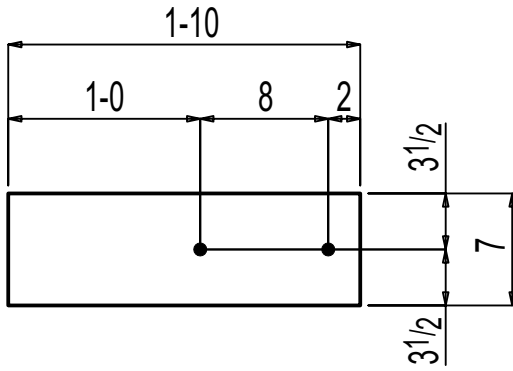

ONE PLATE F-12.03P3

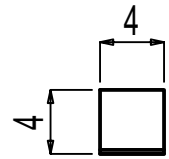

ONE ANGLE F-12.03A1

General Notes			
*Structural steel shall conform to ASTM-A992.			
*Structural SQR/RND,tubing conform to ASTM A500 Grade C			
*Pipe shall conform to ASTM A53, Grade B.			
*Channels, Angles and plates shall conform to A36.			
*All bolts shall be 3/4" High strength in accordance with ASTM A325 (UNO)			
*Welding Electrodes for Carbon steel :E70xx			
4	0	For Fabrication	11-14-2025
3	C	Deleted	09-19-2025
2	B	For Re-Approval	06-23-2025
1	A	For Approval	02-25-2025
# of Copies	Revision/ Issue	Destination	Date

IRON FABRICATION SERVICES, LLC.

3029 M. Street, NW, Suite 202
Washington, DC 20007
Tel: 202-800-5599
Fax: 202-478-0303

Project Name and Address
MARYLAND AVENUE

Location: 1250 MARYLAND AVENUE SW
WASHINGTON, DC 20024

Contractor:
BALFOUR BEATTY

Approved for Fabrication by:	Signature

Contract # 224009	Drawing # F-12.03
Contract Item: FRAME,HSS & THREADED ROD	
Ref: SOW - 12: E-12.00 - E-12.02	
Date 01/ 23/ 2025	Drawing Title: MISC DETAIL
Scale VARIES	

PAINT :NO PAINT
PREPARATION :SSPC-SP3