
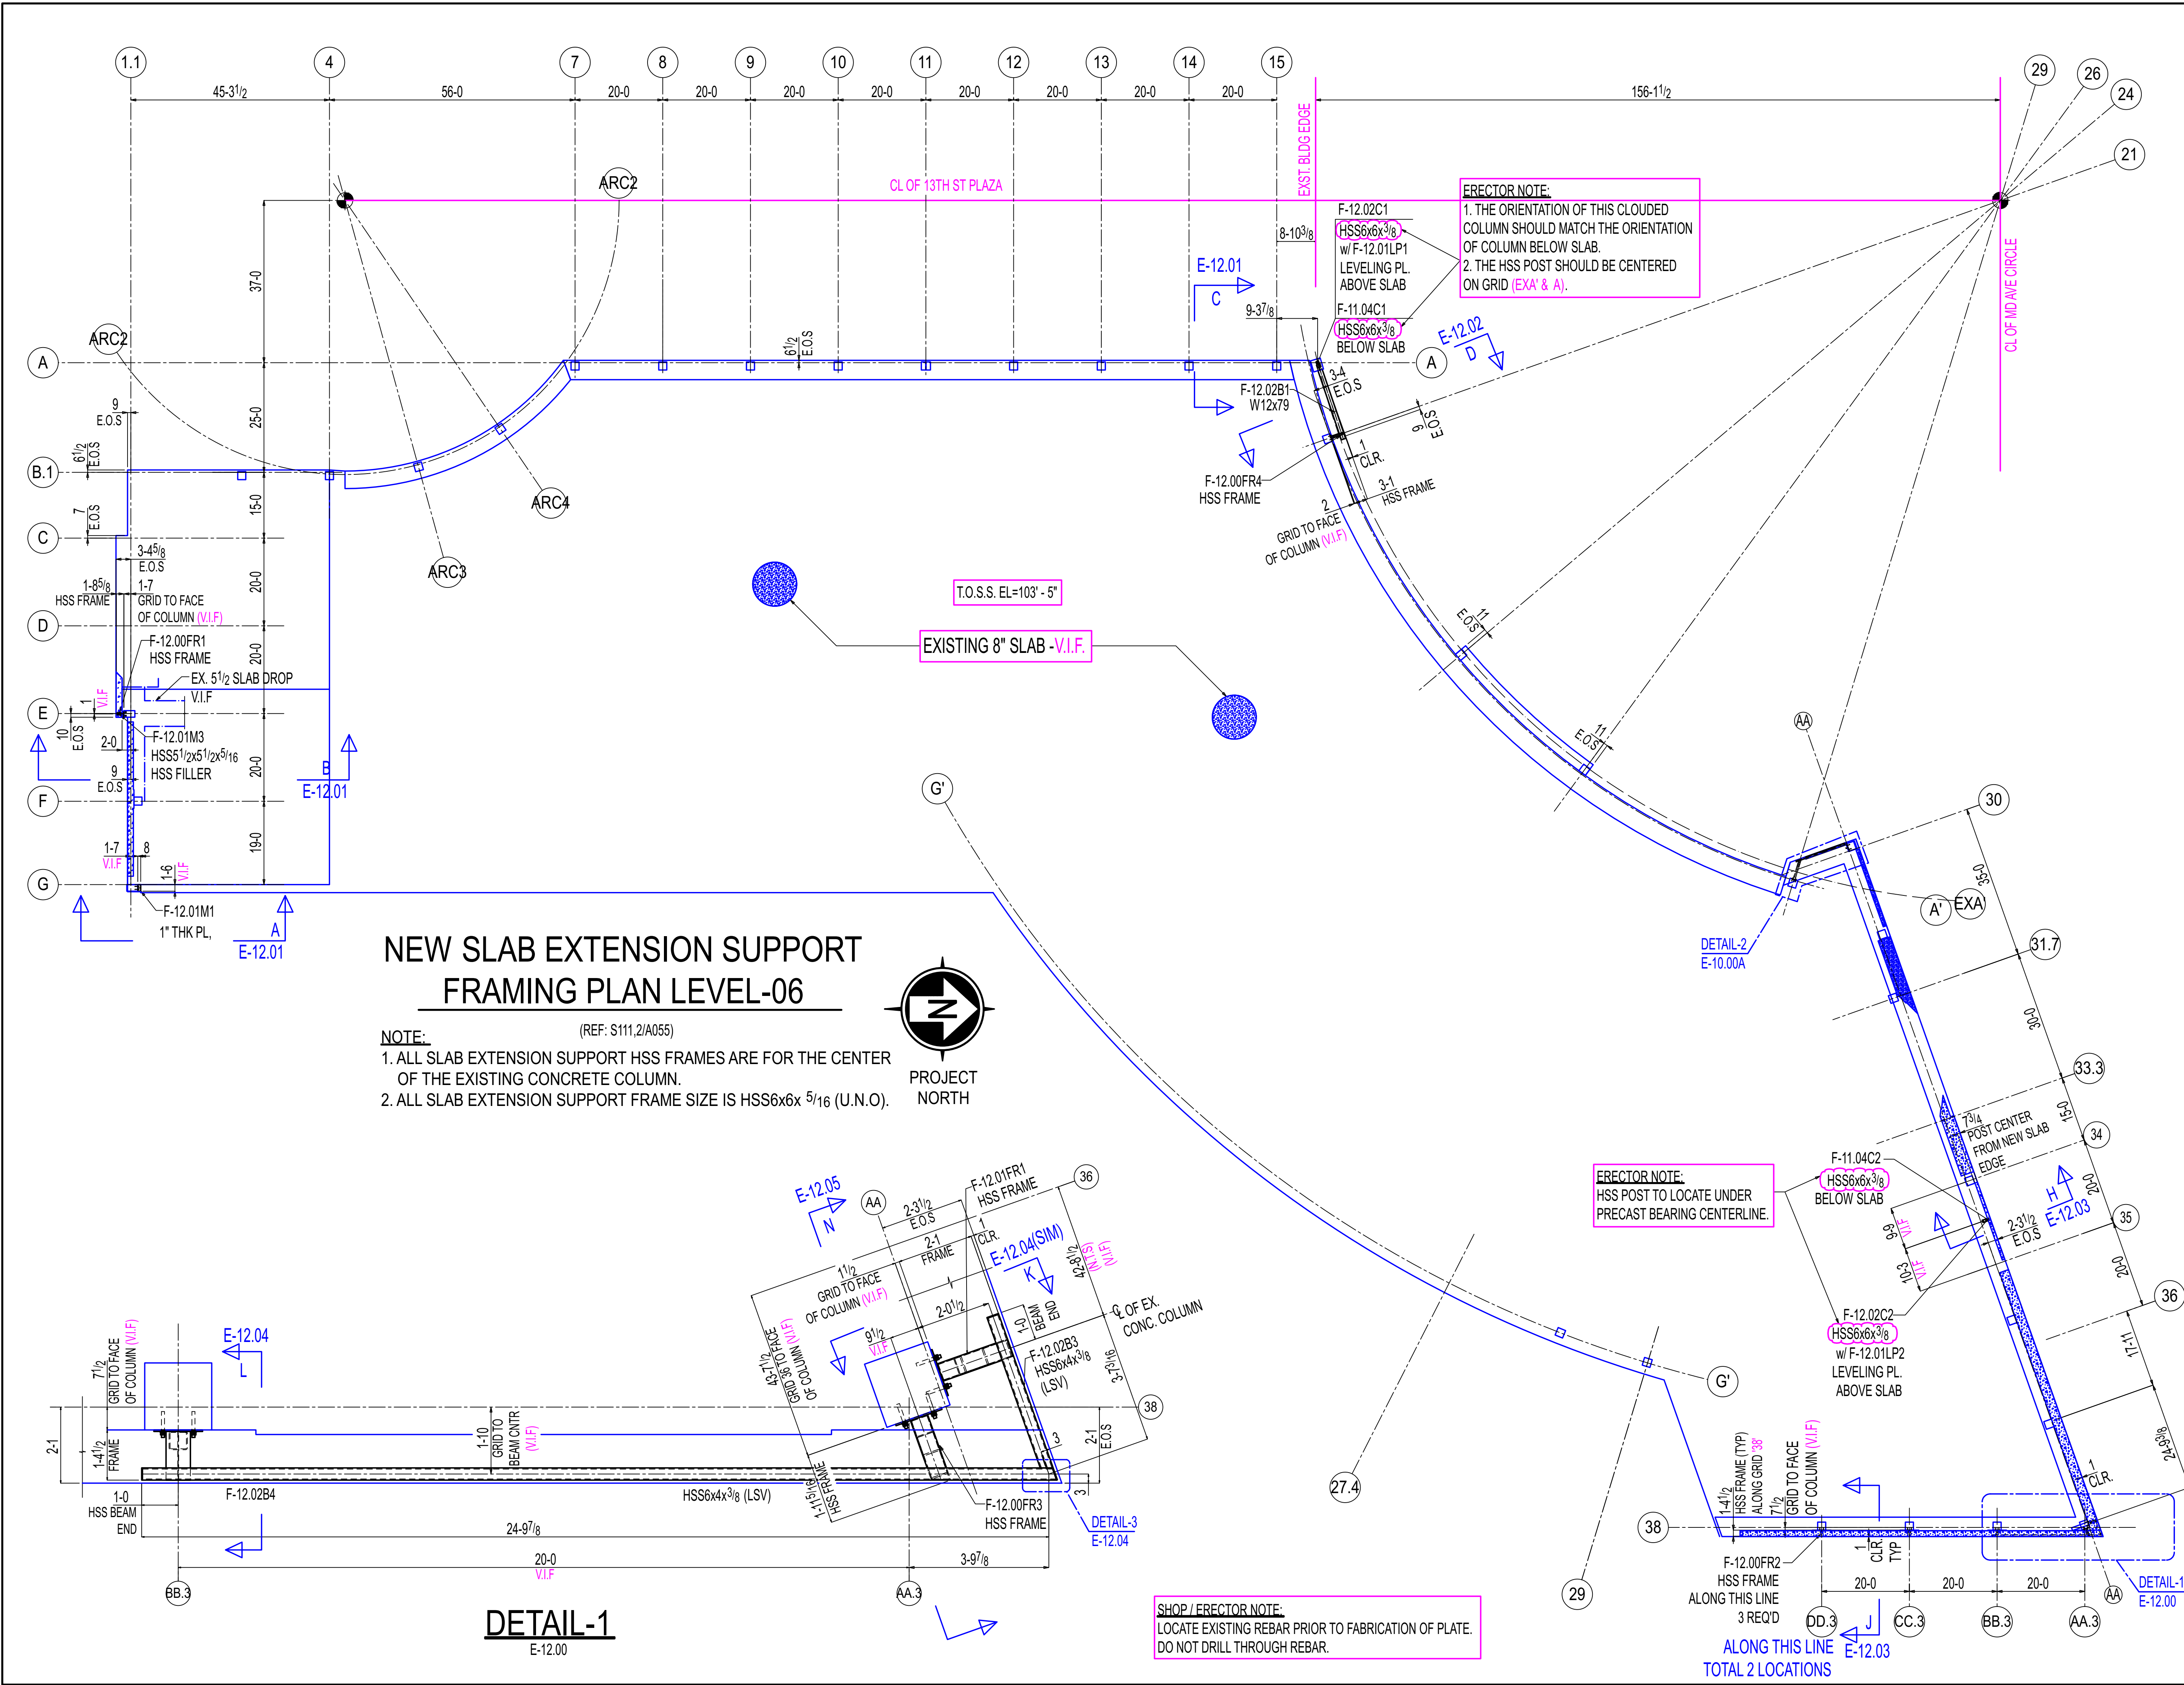


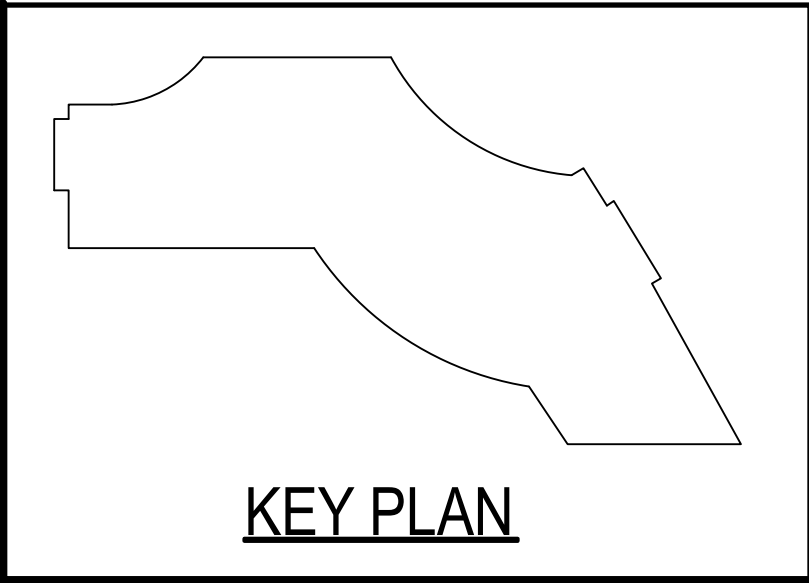

General Notes

- *Structural steel shall conform to ASTM-A992.
- *Structural SQR/RND tubing conform to ASTM A500 Grade C.
- *Pipe shall conform to ASTM A53, Grade B.
- *Channels, Angles and plates shall conform to A36.
- *All bolts shall be 3/4" High strength in accordance with ASTM A325 (UNO).
- *Welding Electrodes for Carbon steel :E70xx

# of Copies	Revision/ Issue	Destination	Date
5	0	For Construction	11-14-2025
4	D	For Re-Approval	10-24-2025
3	C	For Re-Approval	09-19-2025
2	B	For Re-Approval	06-23-2025
1	A	For Approval	02-25-2025

IRON FABRICATION SERVICES, LLC.

3029 M. Street, NW, Suite 202
Washington, DC 20007
Tel: 202-800-5599
Fax: 202-478-0303

Project Name and Address

MARYLAND AVENUE

Location: **1250 MARYLAND AVENUE SW
WASHINGTON, DC 20024**

Contractor:

BALFOUR BEATTY

Approved for Fabrication by: _____

Signature _____

Contract # **224009**

Contract Item: **LEVEL-06
SLAB EXTENSION**

Ref: **SOW-12: (S111,2/A055)**

Date: **01/20/2025**

Scale: **VARIES**

Drawing Title: **SOW #12 LEVEL-06 NEW
SLAB EXTENSION SUPPORT
FRAMING PLAN**

Drawing # **E-12.00**



E-12.00

OTHERS NOT SHOWN FOR CLARITY

- *Structural steel shall conform to ASTM-A992.
- *Structural SQR/RND tubing conform to ASTM A500 Grade C
- *Pipe shall conform to ASTM A53, Grade B.
- *Channels, Angles and plates shall conform to A36.
- *All bolts shall be $\frac{3}{4}$ " High strength in accordance with ASTM A325 (UNO)
- *Welding Electrodes for Carbon steel :E70xx

1	0	For Construction	11-14-2025
# of Copies	Revision/ Issue	Destination	Date

3029 M. Street, NW, Suite 202
Washington, DC 20007
Tel: 202-800-5599
Fax: 202-478-0303

Location: **1250 MARYLAND AVENUE SW**
WASHINGTON, DC 20024

BALFOUR BEATTY

Signature


Drawing # **E-12.00A**

Ref: **SOW-12: (S111,2/A055)**


Drawing Title:

**SOW #12 LEVEL-06 NEW
SLAB EXTENSION SUPPORT
FRAMING PLAN**

Scale
VARIES

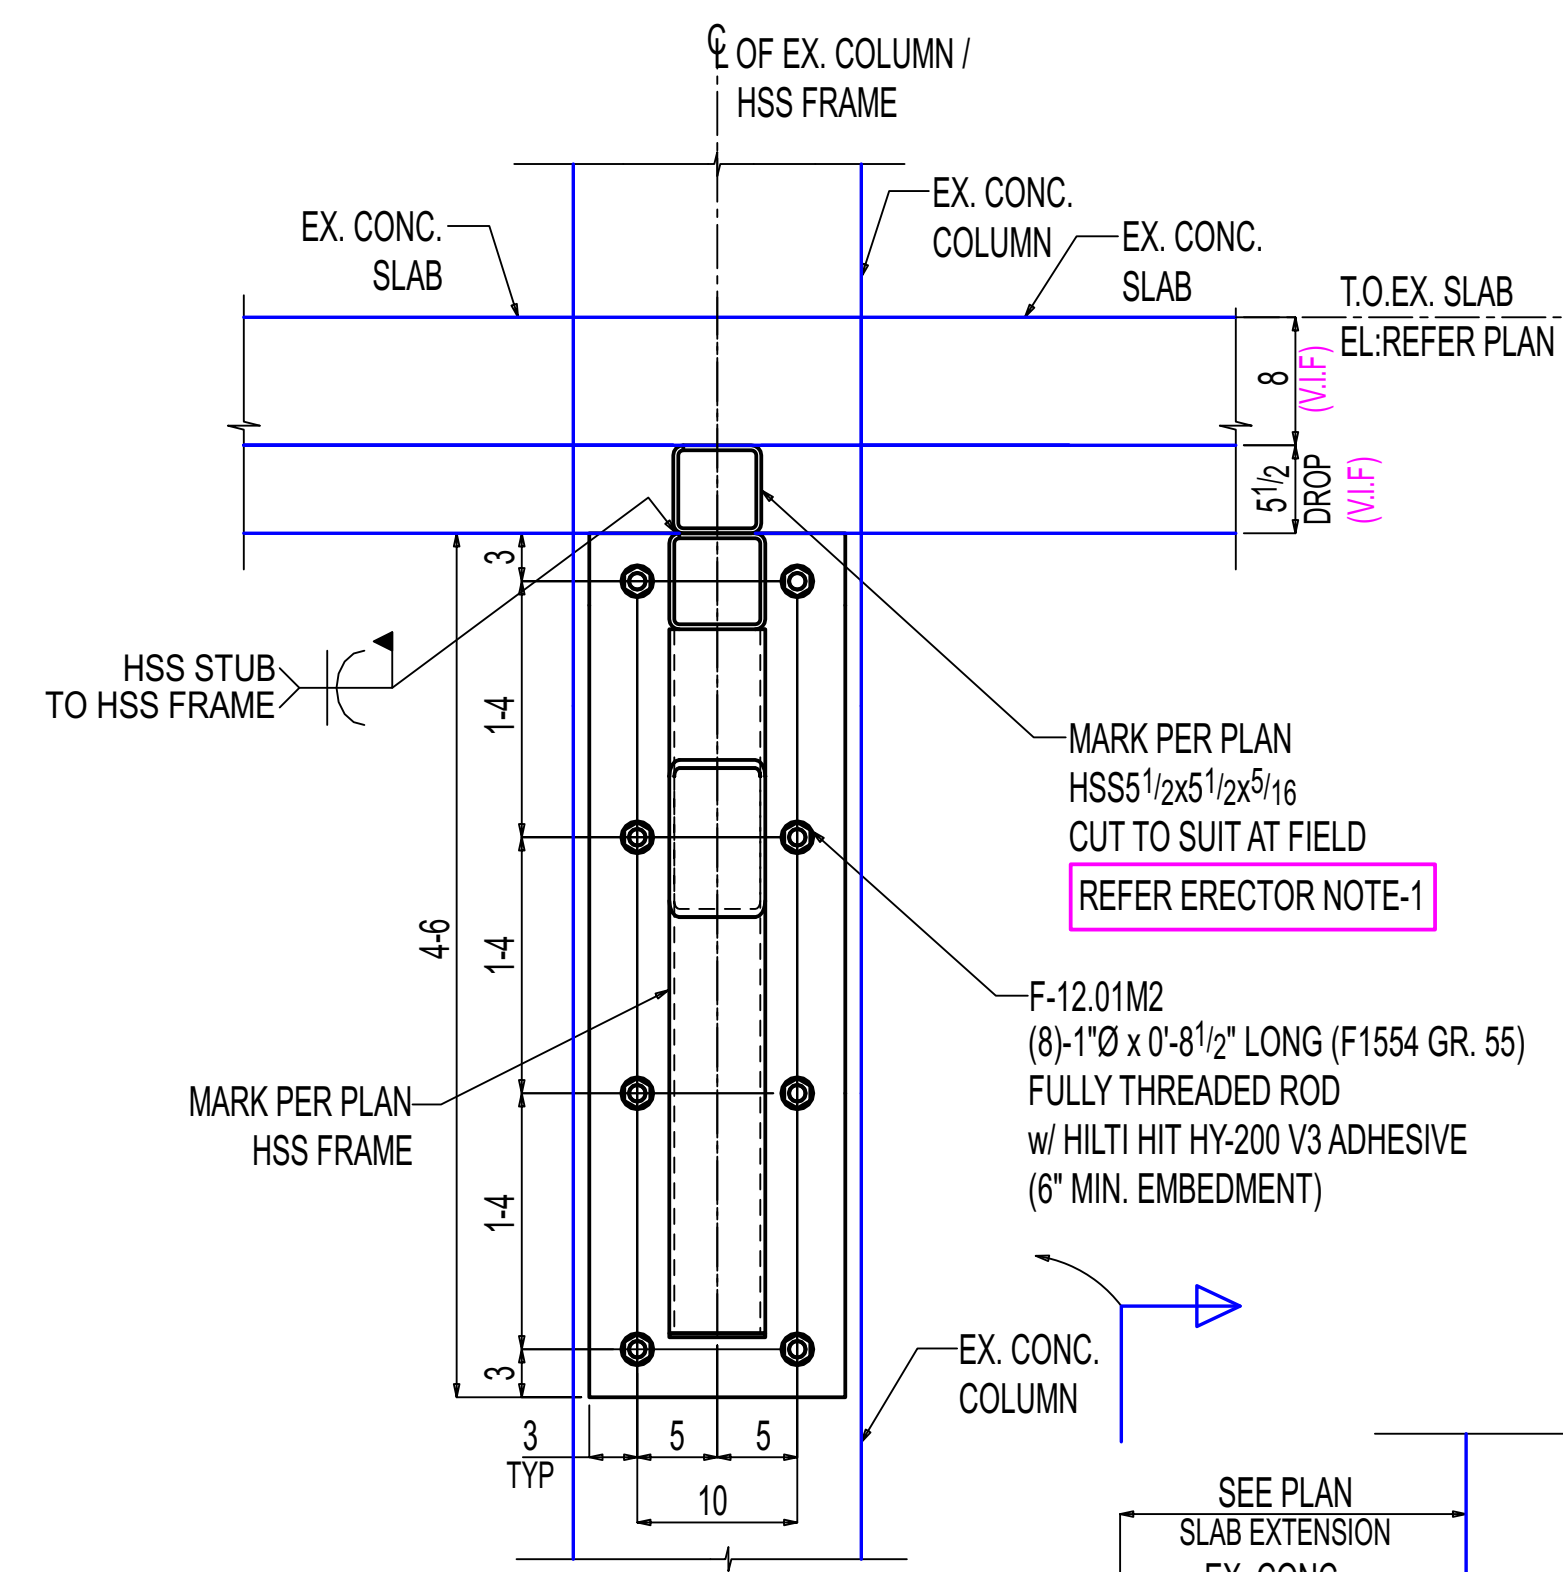

MARK PER PL
HSS51/2x51/2x5/
CUT TO SUIT AT FIELD
REFER ERECTOR NOTE-

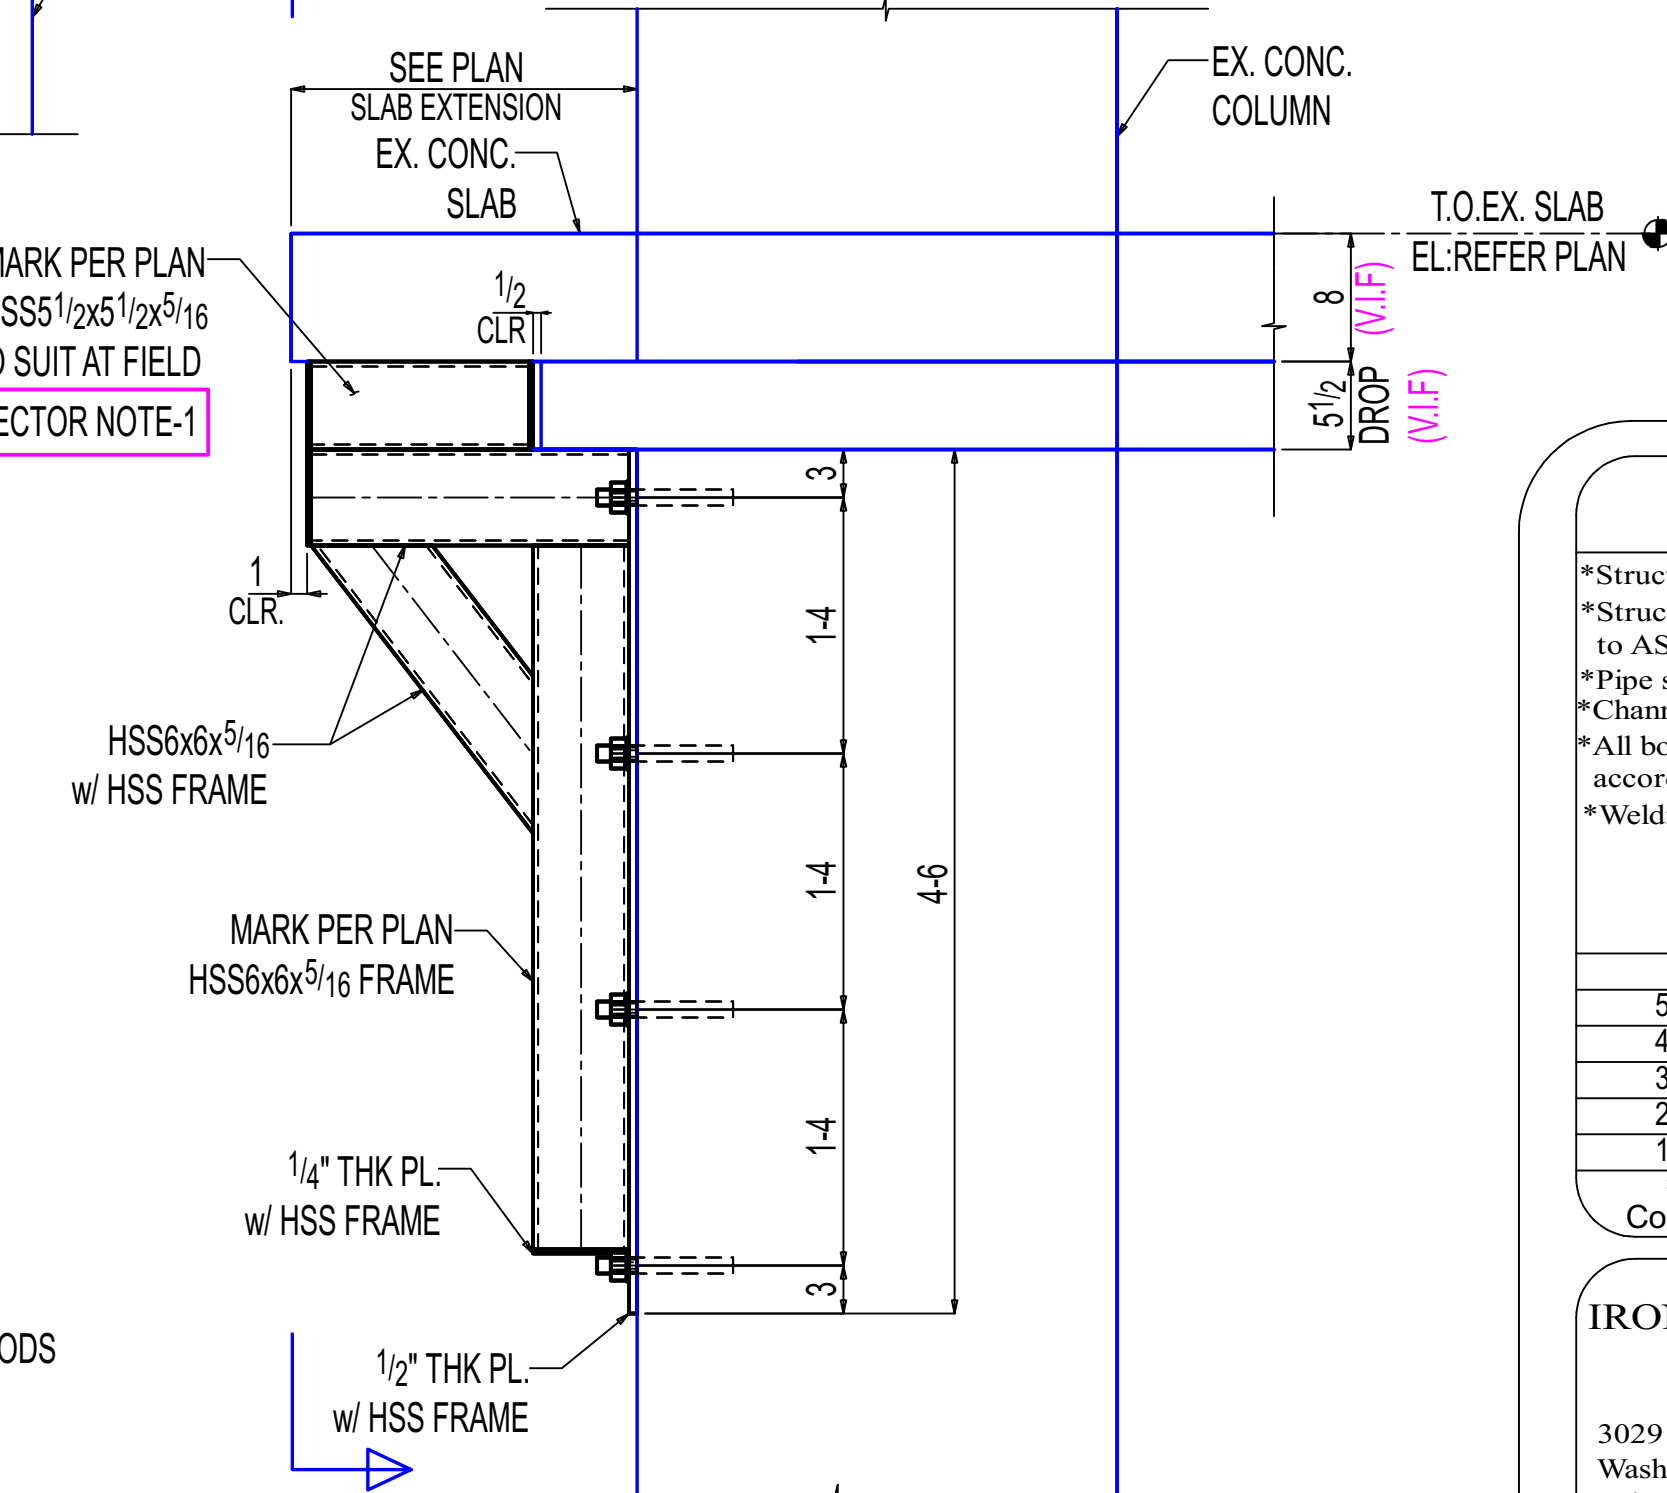[illegible]

OTHERS NOT SHOWN FOR CLARITY

* -FRETOR NOTE:
PROVIDE 1" NON -SHRINK GROUT x 12" LONG
CENTERED BENEATH AT PRECAST
ATTACHMENT POINTS.



SHOP / ERECTOR NOTE:
LOCATE EXISTING REBAR PRIOR TO FABRICATION OF PLATE.
DO NOT DRILL THROUGH REBAR.

Project Name and Address
MARYLAND AVENUE

Location: **1250 MARYLAND AVENUE SW**
WASHINGTON, DC 20024

Approved for Fabrication by:	Signature



Contract # 224009		Drawing # E-12.01
Contract Item: LEVEL-06 SLAB EXTENSION		
Ref: SOW-12: 3,4,5&6 / S307		
Date 01/20/2025	Drawing Title: SOW #12 LEVEL-06 NEW SLAB EXTENSION SUPPORT SECTIONS	
Scale VARIES		

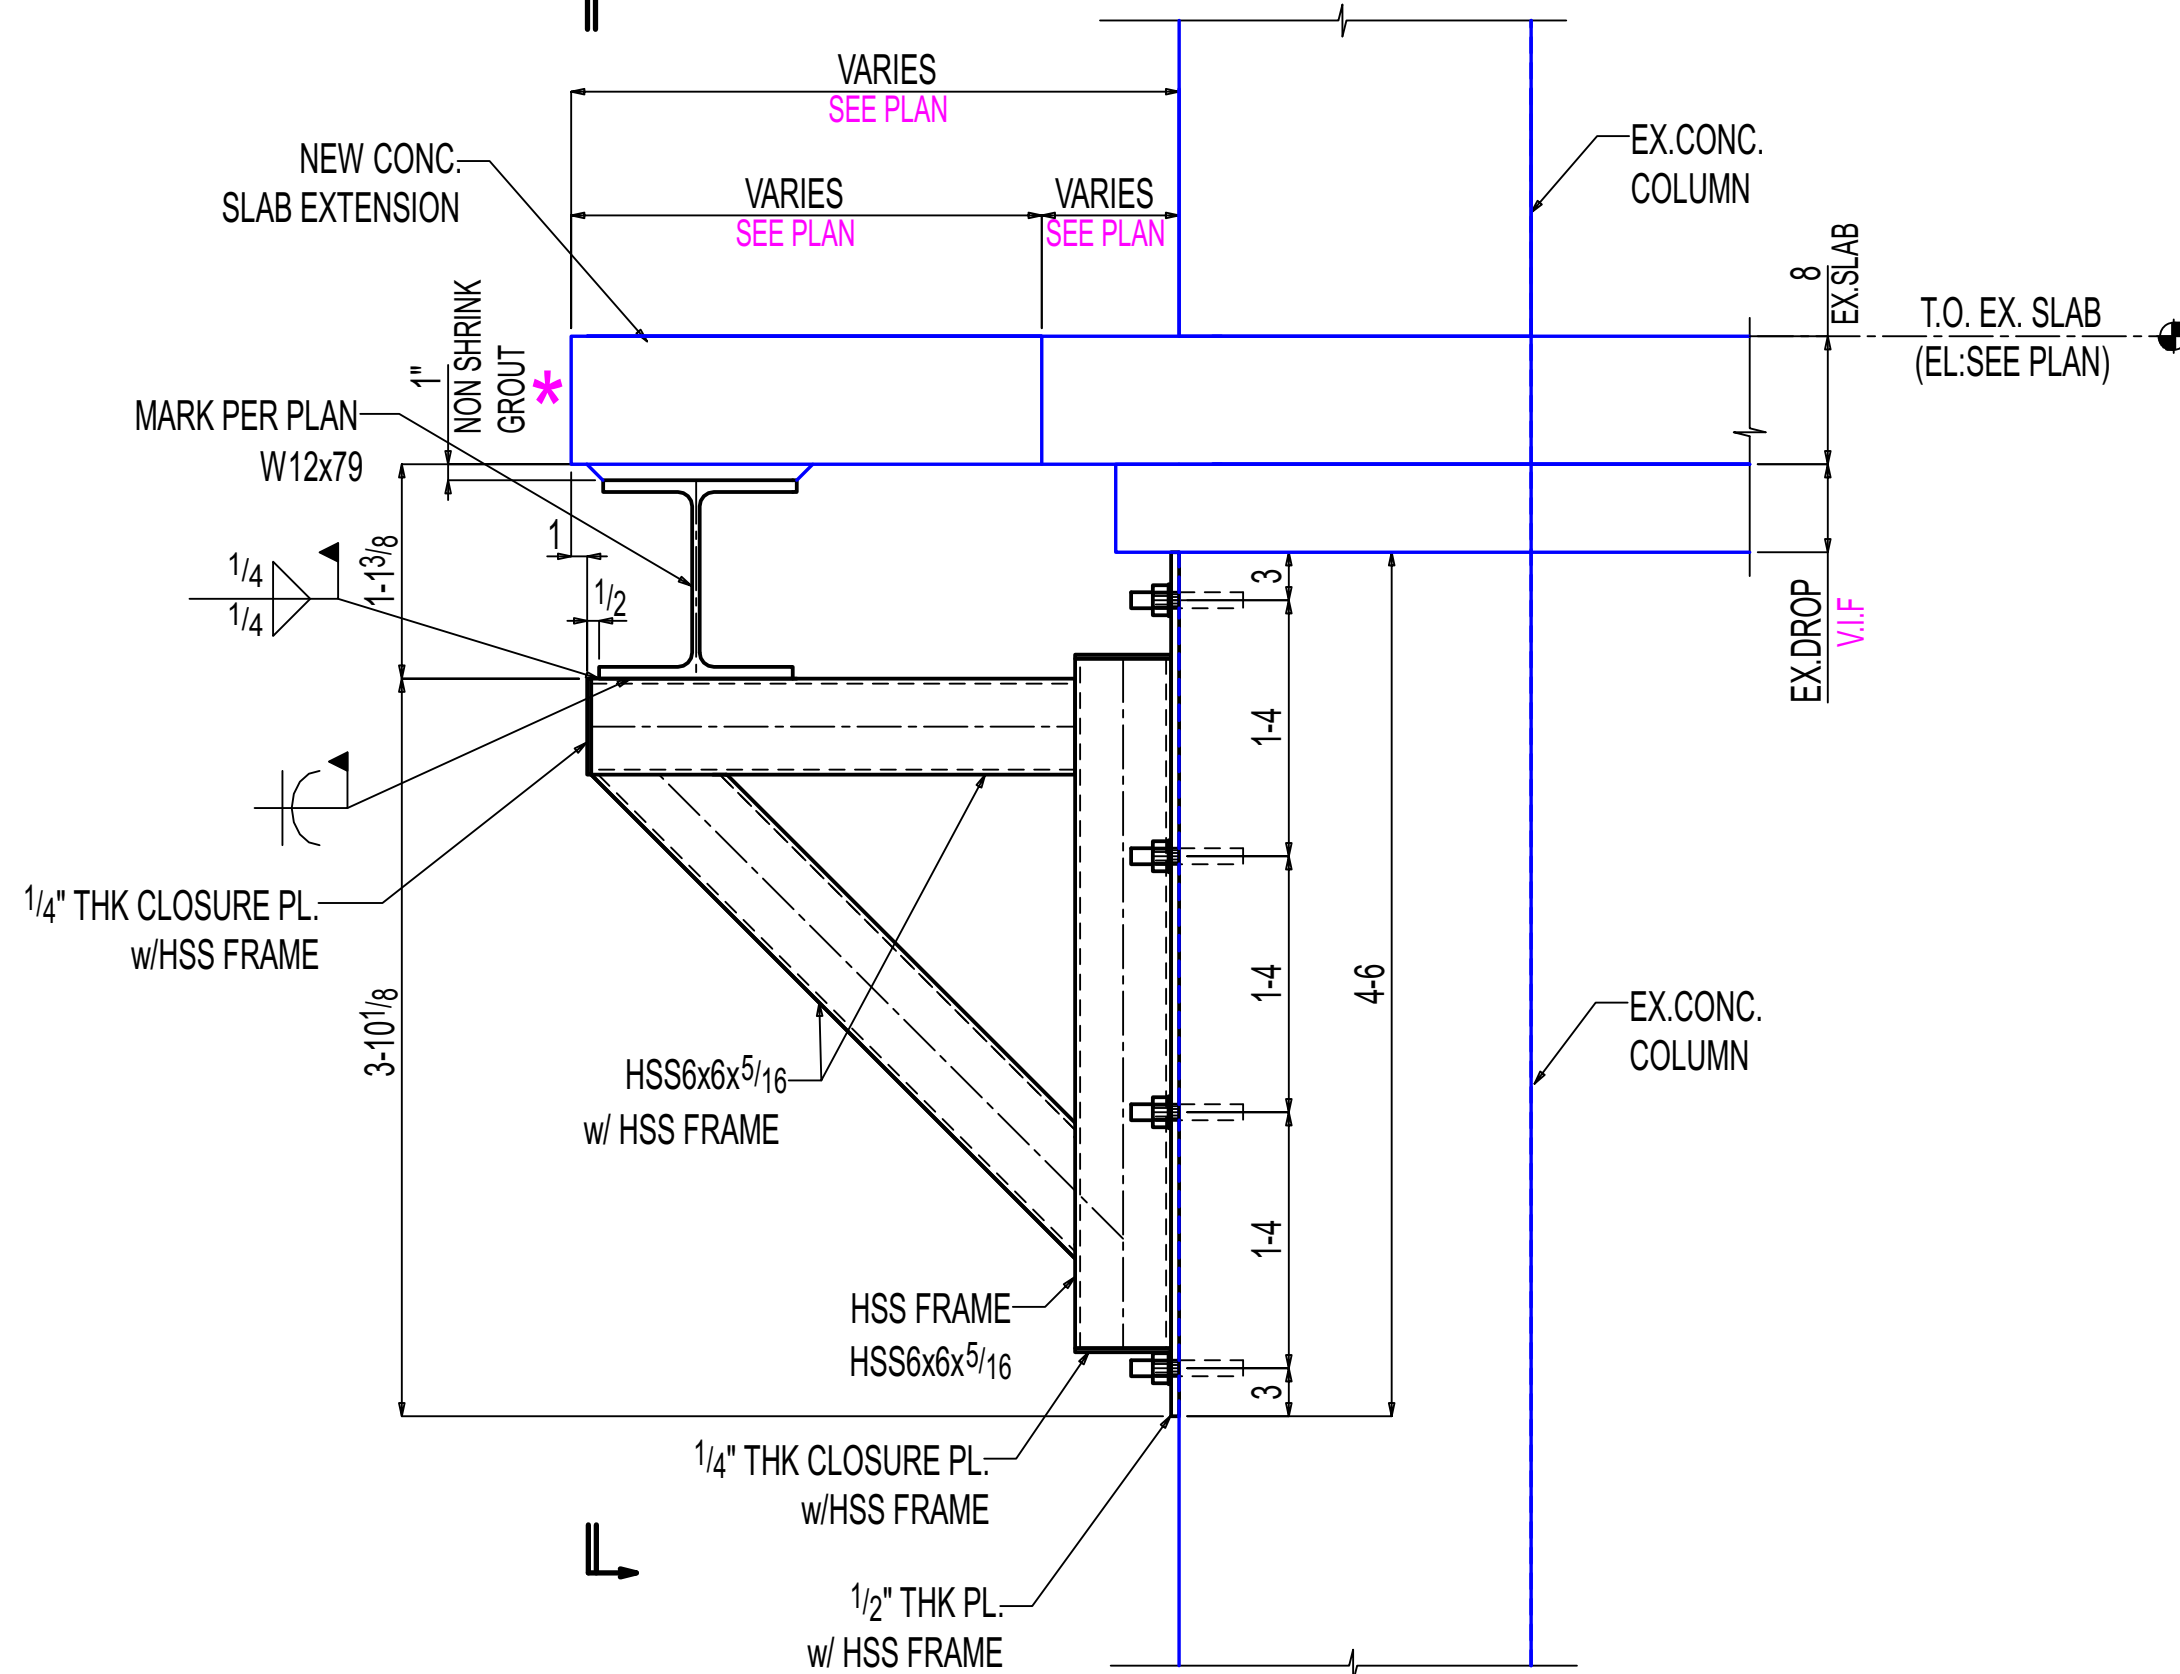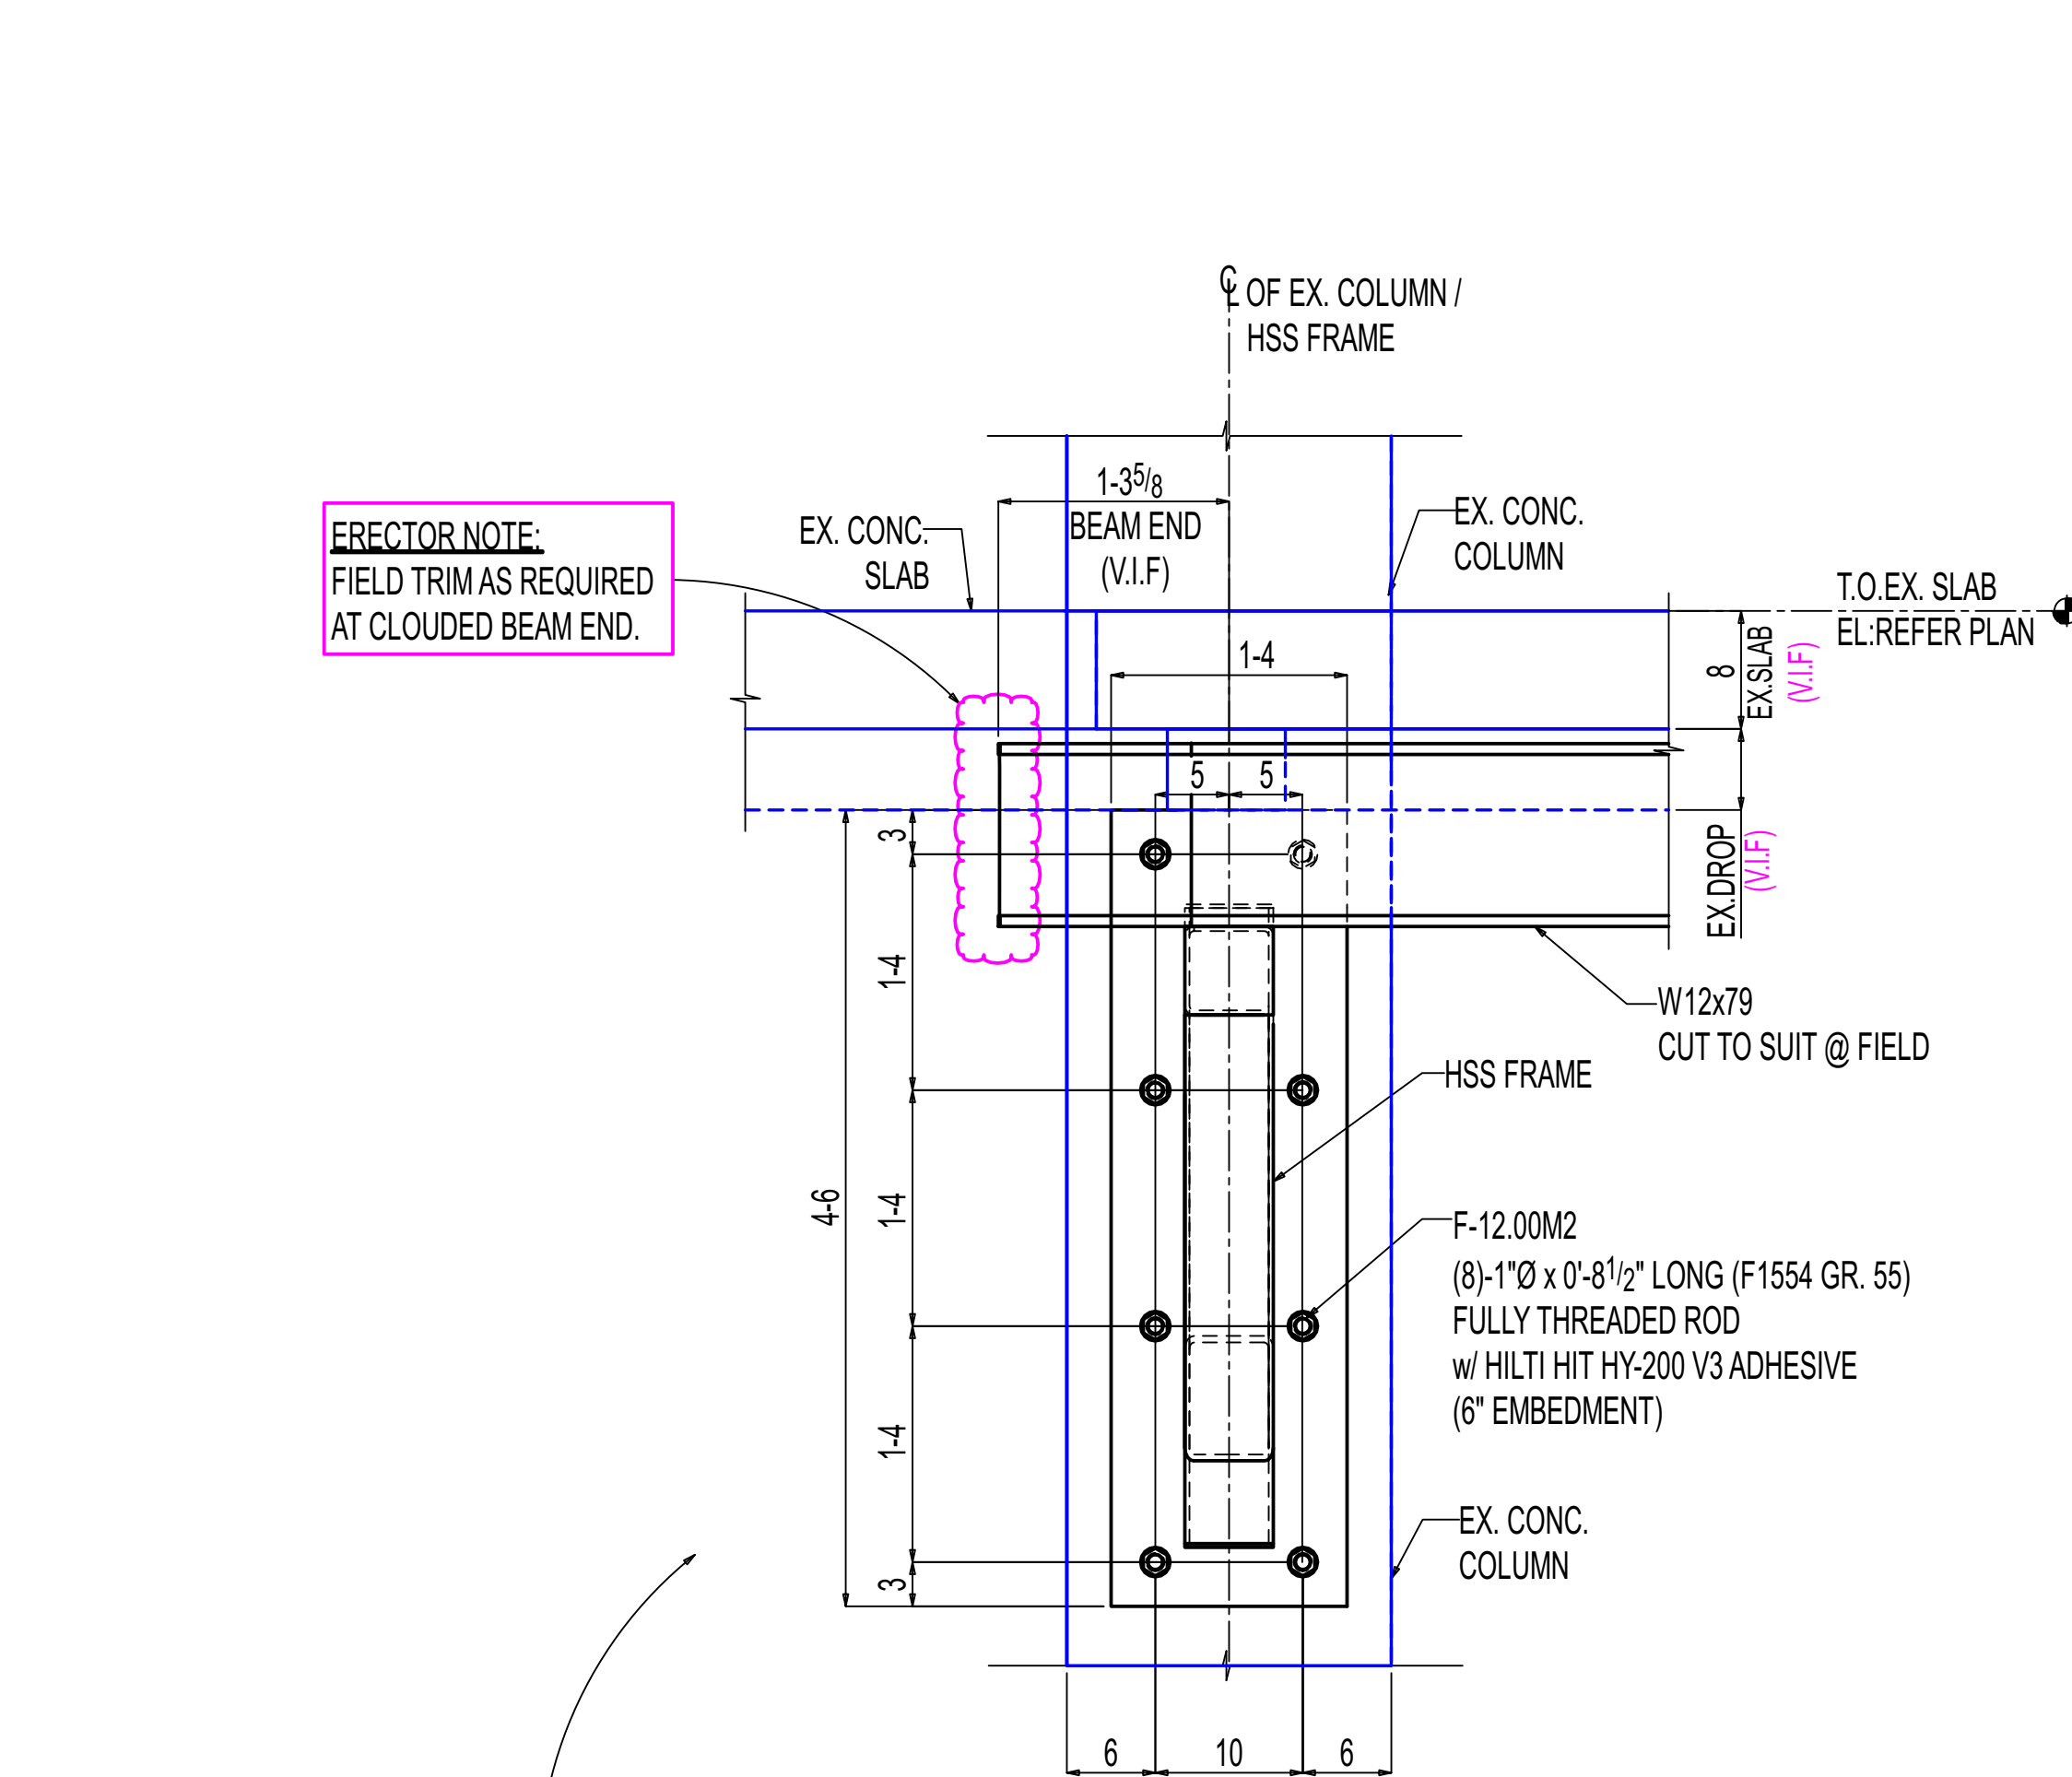

D-D

E-12.00
(REF:13/S312)

OTHERS NOT SHOWN FOR CLARITY

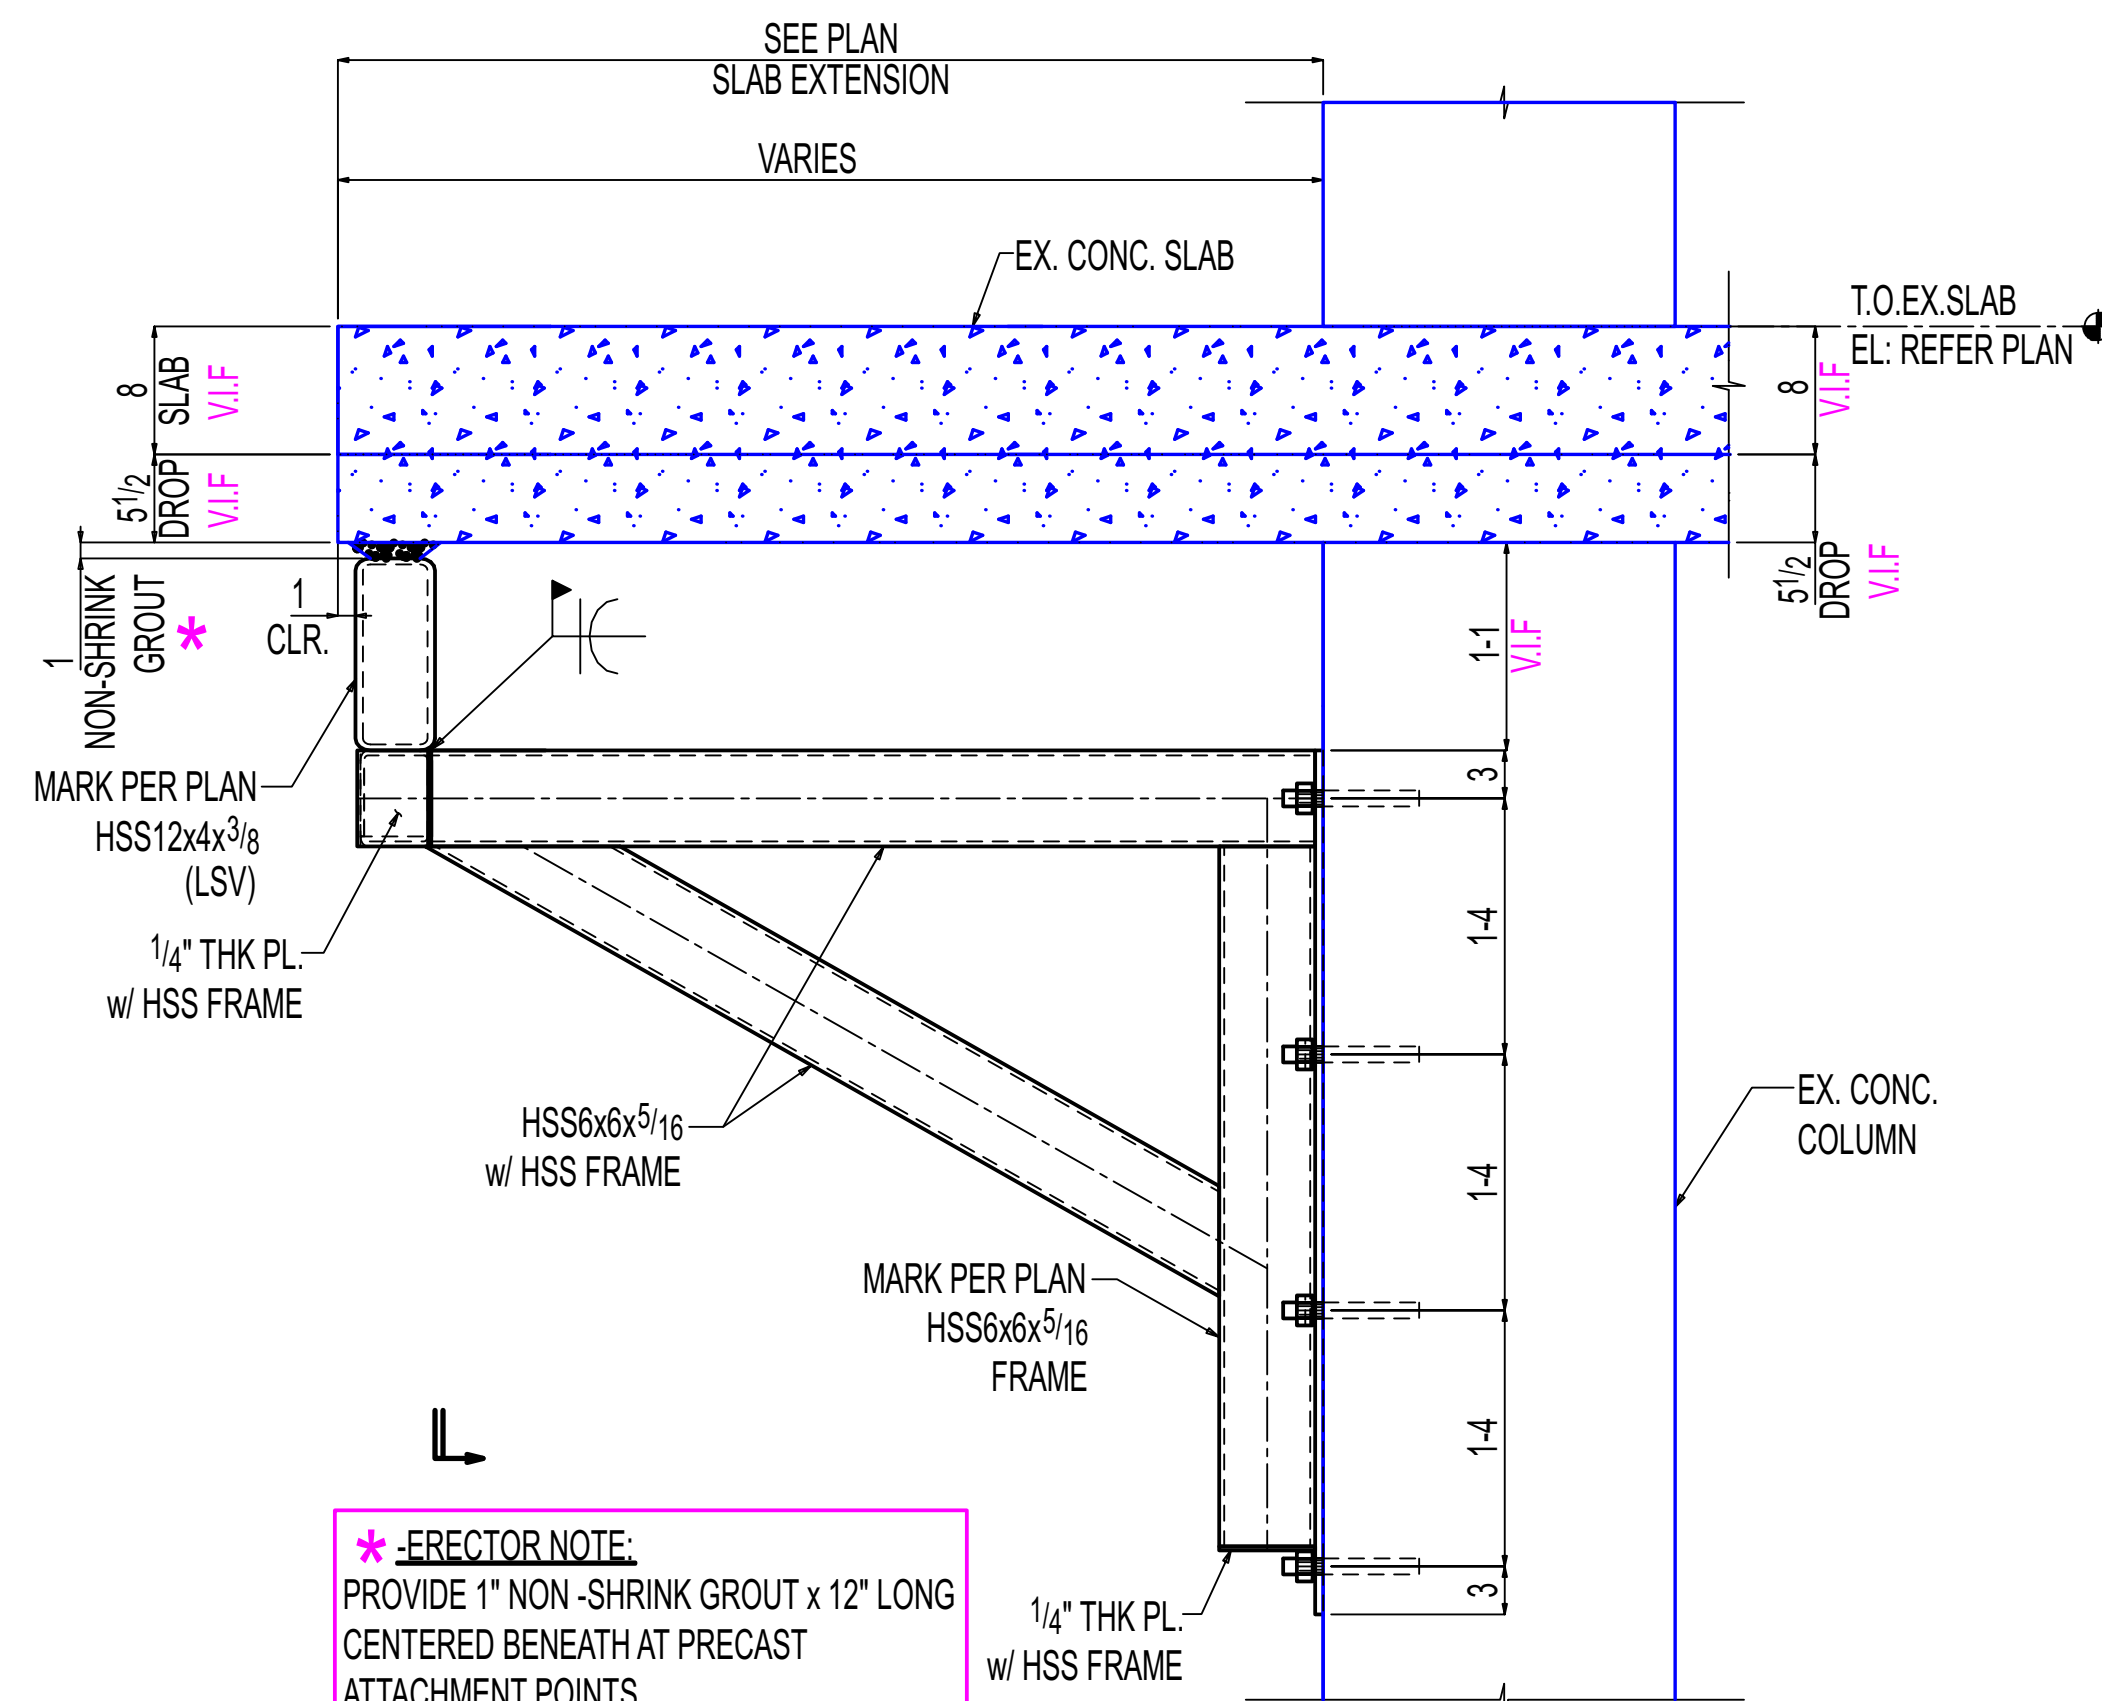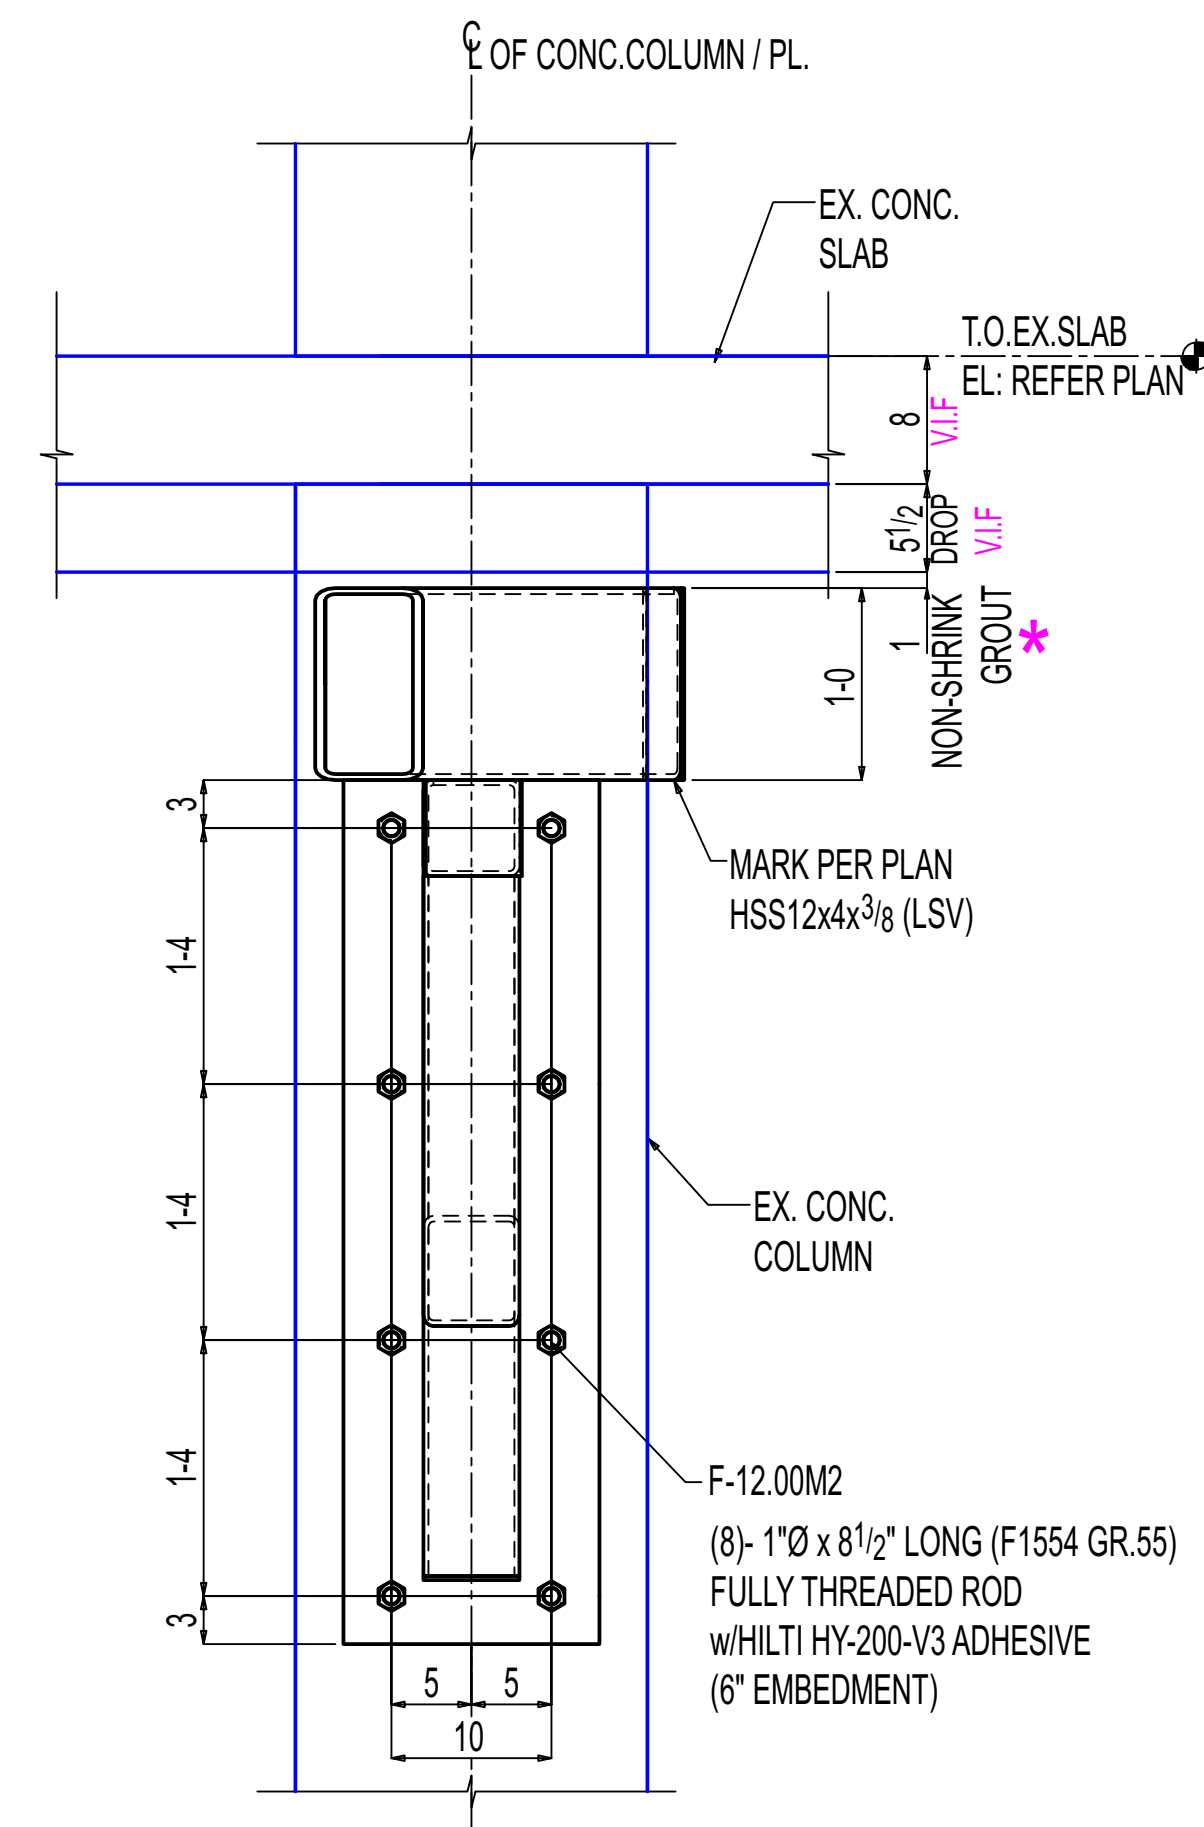

*-ERECTOR NOTE:
PROVIDE 1" NON-SHRINK GROUT x 12" LONG
CENTERED BENEATH AT PRECAST
ATTACHMENT POINTS.

F-F

E-12.00A
(REF:6/S316)

OTHERS NOT SHOWN FOR CLARITY

SHOP / ERECTOR NOTE:
LOCATE EXISTING REBAR PRIOR TO FABRICATION OF PLATE.
DO NOT DRILL THROUGH REBAR.

General Notes

- *Structural steel shall conform to ASTM-A992.
- *Structural SQR/RND.tubing conform to ASTM A500 Grade C
- *Pipe shall conform to ASTM A53, Grade B.
- *Channels, Angles and plates shall conform to A36.
- *All bolts shall be 3/4" High strength in accordance with ASTM A325 (UNO)
- *Welding Electrodes for Carbon steel :E70xx

# of Copies	Revision/ Issue	Destination	Date
5	0	For Construction	11-14-2025
4	D	For Re-Approval	10-24-2025
3	C	For Re-Approval	09-19-2025
2	B	For Re-Approval	06-23-2025
1	A	For Approval	02-25-2025

IRON FABRICATION SERVICES, LLC.

3029 M. Street, NW, Suite 202
Washington, DC 20007
Tel: 202-800-5599
Fax: 202-478-0303

Project Name and Address

MARYLAND AVENUE

Location: **1250 MARYLAND AVENUE SW
WASHINGTON, DC 20024**

Contractor:

BALFOUR BEATTY

Approved for Fabrication by:

Signature

Contract # **224009**

Drawing # **E-12.02**

Contract Item: **LEVEL-06
SLAB EXTENSION**

Ref: **SOW-12: 3,4,5&6 / S307**


Date
01/20/2025

Drawing Title:


**SOW #12 LEVEL-06 NEW
SLAB EXTENSION SUPPORT
SECTIONS**

Scale
VARIES

ERECTOR NOTE:
1"NS&6" WIDTH GROUT @ PRECAST BEARING POINT ONLY
CO-ORDINATE BEARING POINT LOCATION WITH
PRECAST MANUFACTURER.

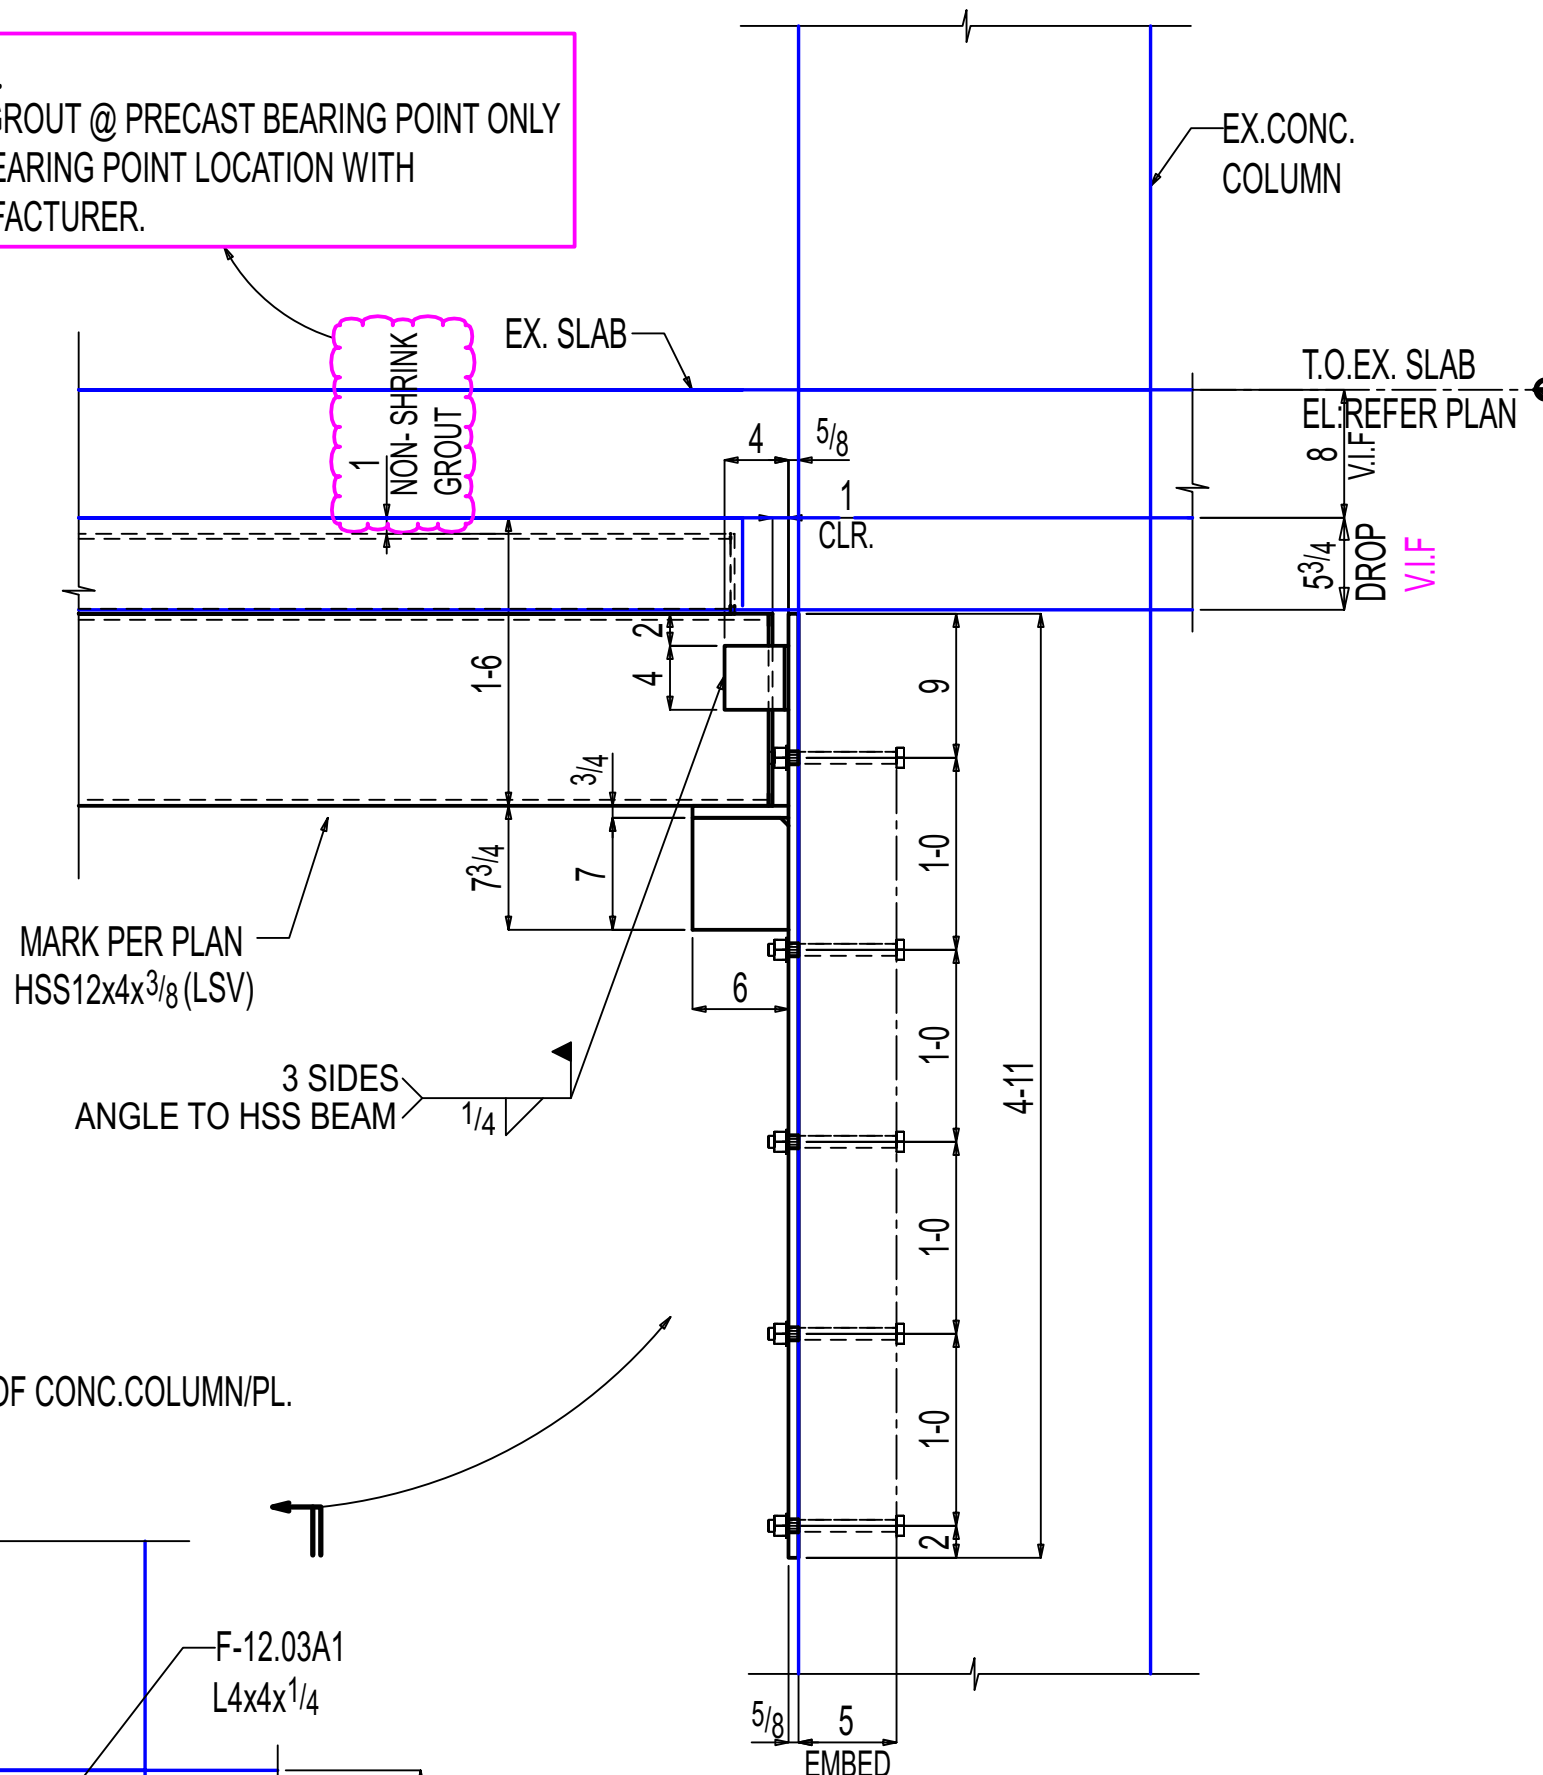


NOTE:
FILLER SIZE AND REQUIREMENT WILL BE
FINALIZED AFTER FIELD MEASUREMENT.

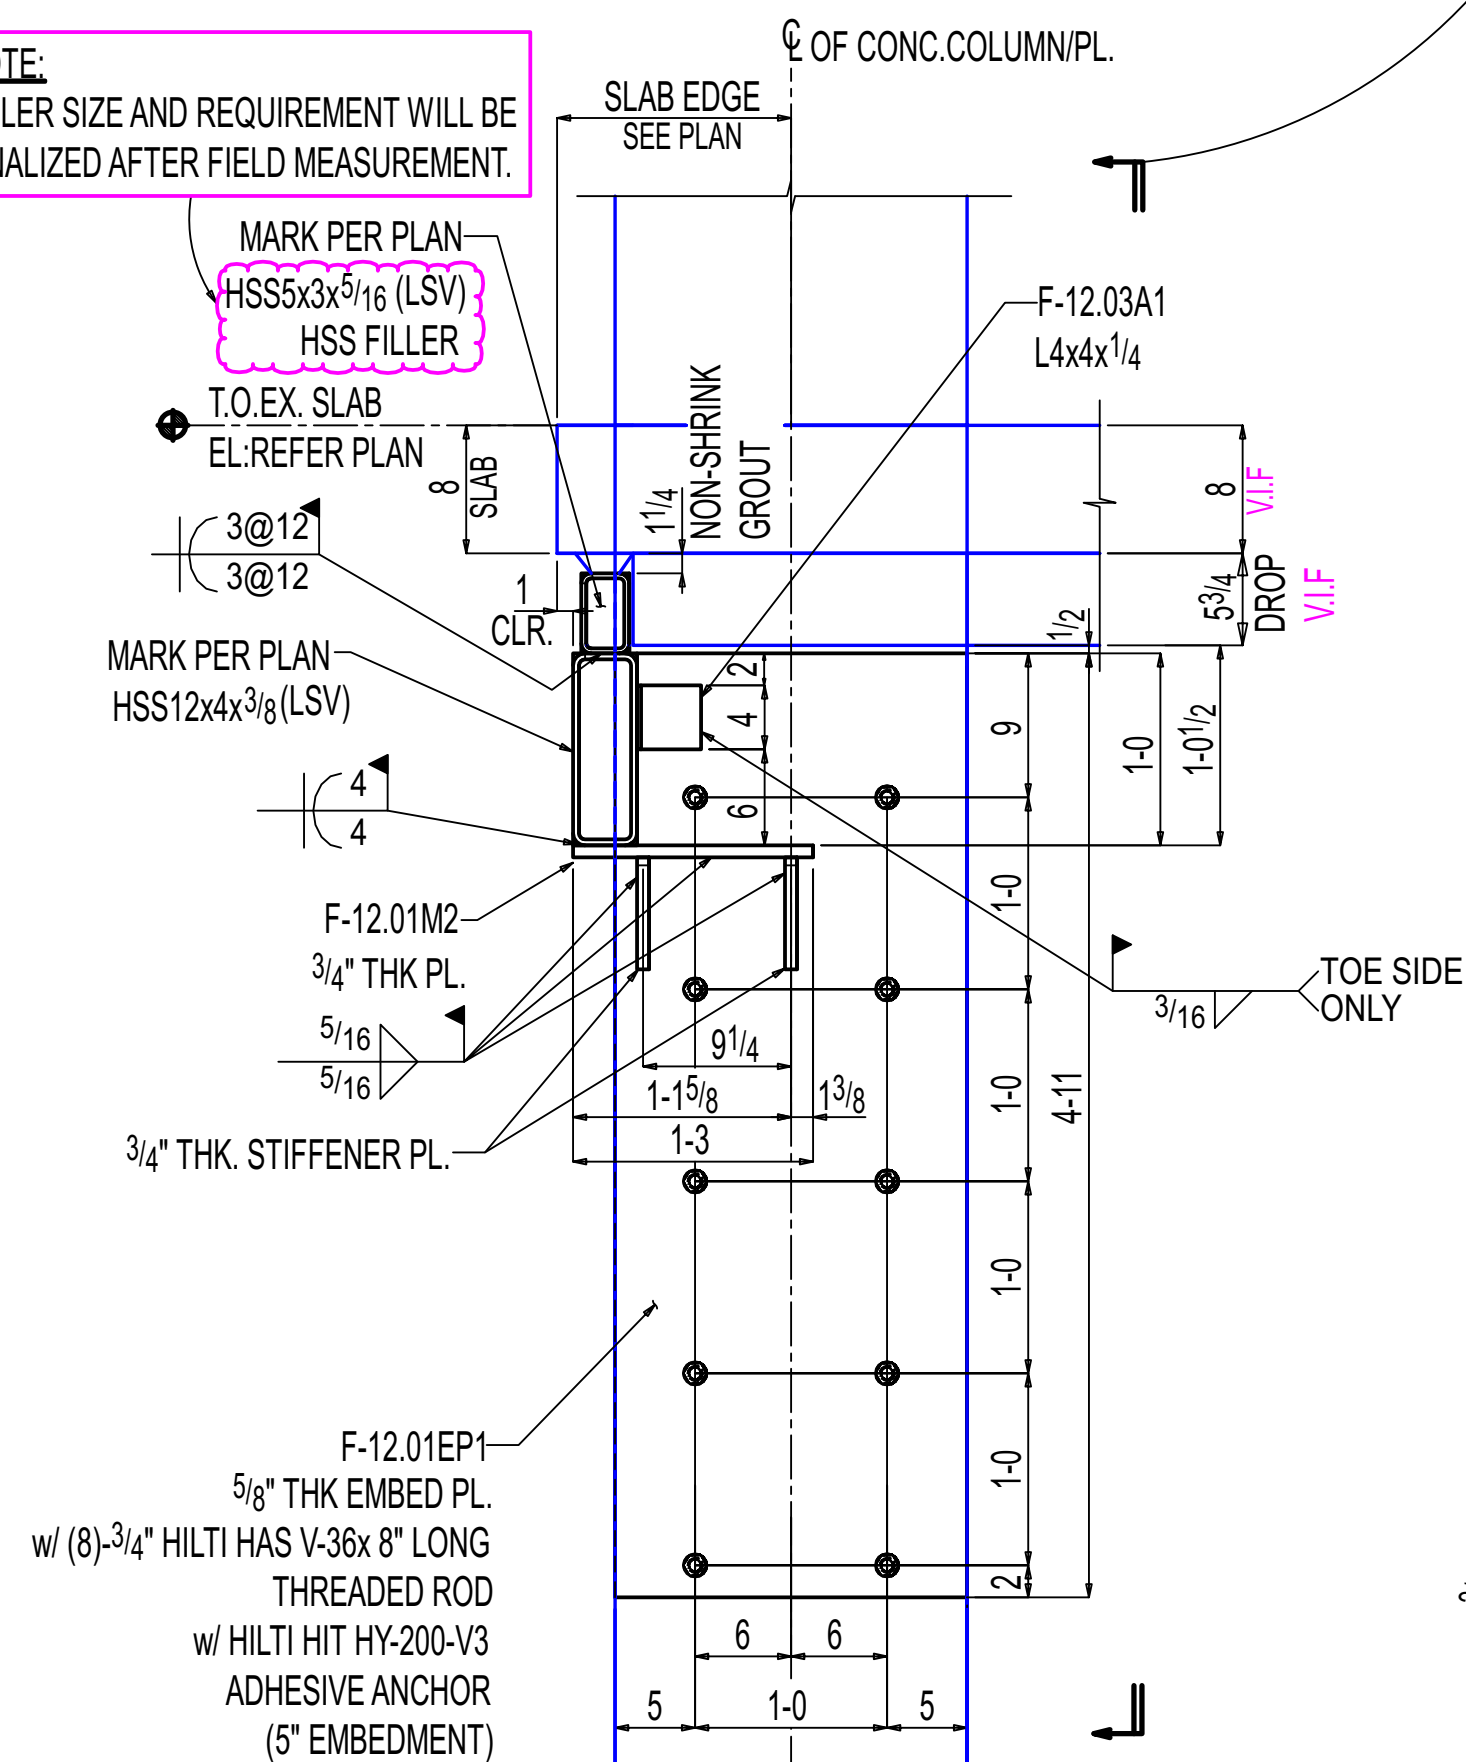

G-G

E-12.00
(REF:1/S316)


OTHERS NOT SHOWN FOR CLARITY

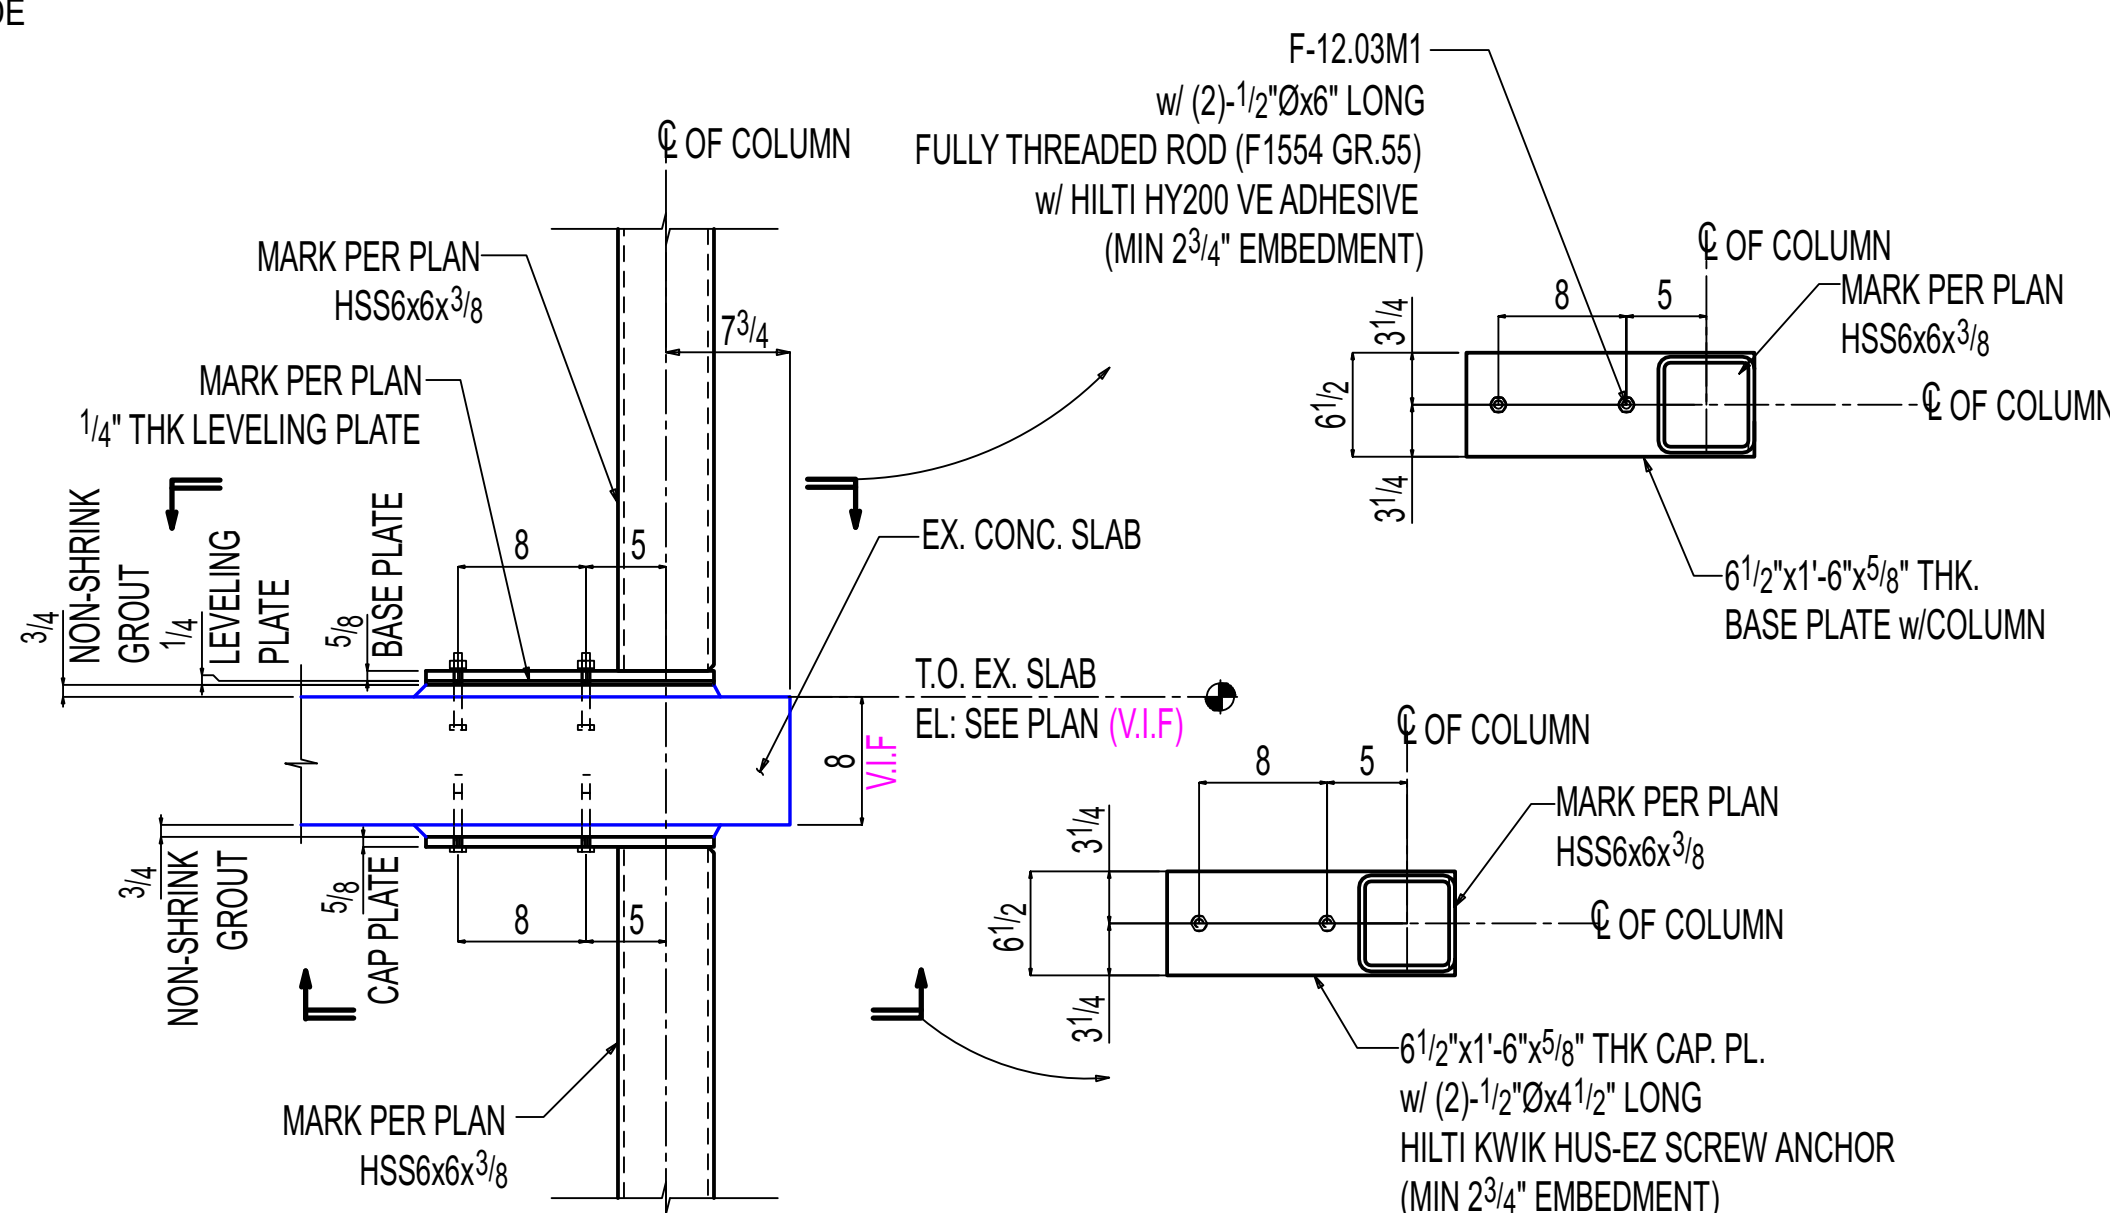

H-H

E-12.00
(REF:1/S317)

OTHERS NOT SHOWN FOR CLARITY

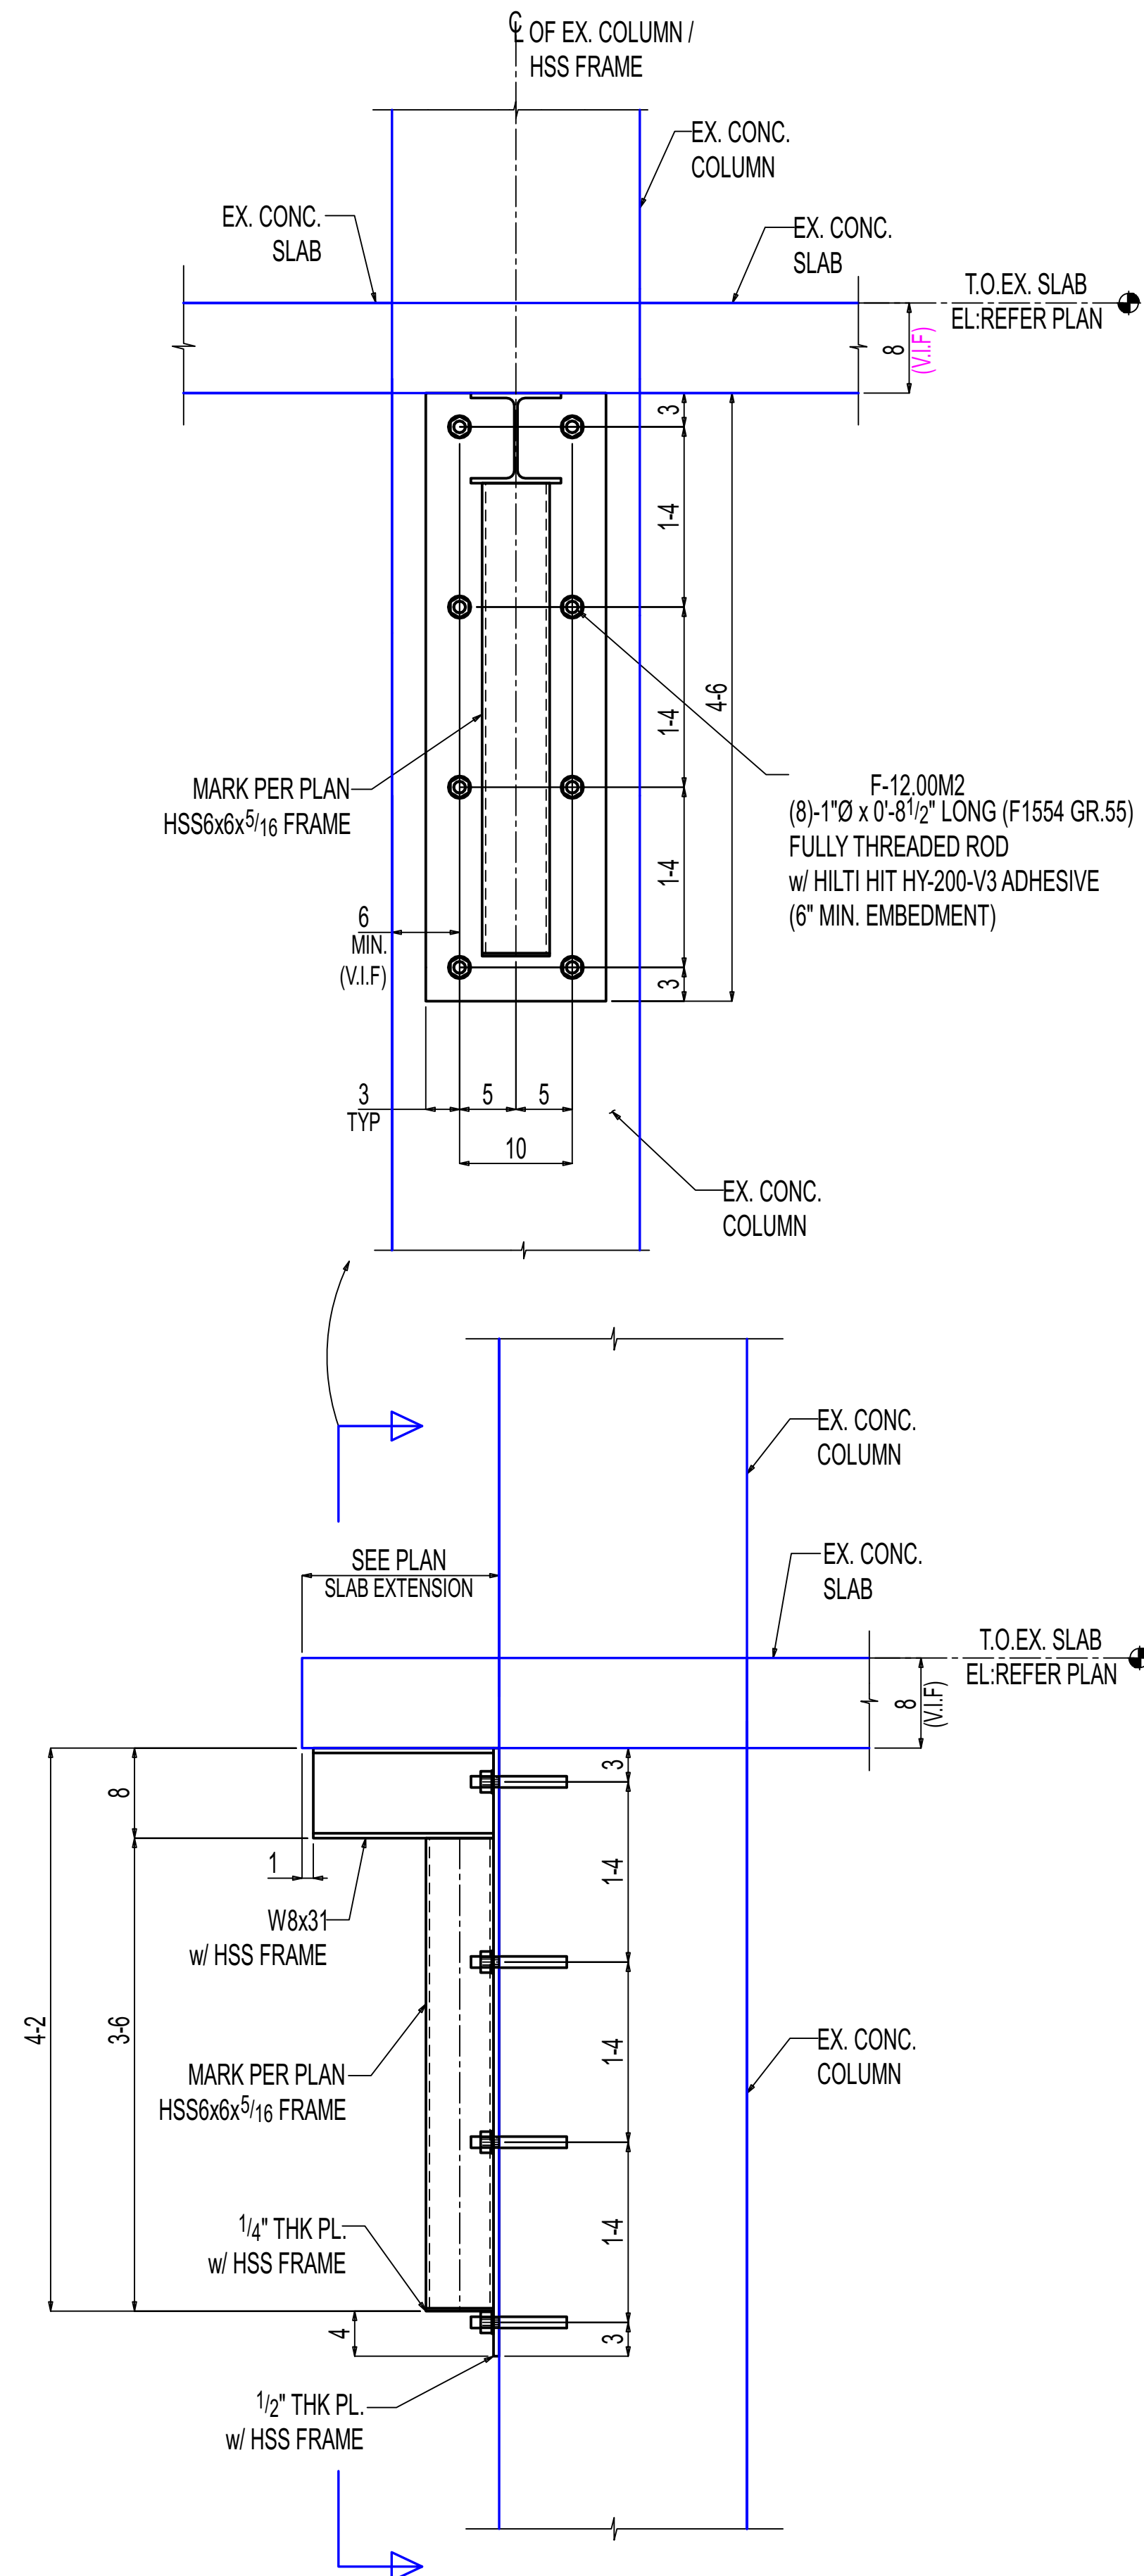

J-J

(NEW SLAB EXTENSION SUPPORT 1'-6" TO 3'-1")

E-12.00
(REF:10/S314)

OTHERS NOT SHOWN FOR CLARITY

General Notes

- *Structural steel shall conform to ASTM-A992.
- *Structural SQR/RND tubing conform to ASTM A500 Grade C
- *Pipe shall conform to ASTM A53, Grade B.
- *Channels, Angles and plates shall conform to A36.
- *All bolts shall be 3/4" High strength in accordance with ASTM A325 (UNO)
- *Welding Electrodes for Carbon steel :E70xx

# of Copies	Revision/ Issue	Destination	Date
3	0	For Construction	11-14-2025
2	B	For Re-Approval	10-24-2025
1	A	For Approval	09-19-2025

IRON FABRICATION SERVICES, LLC.

3029 M. Street, NW, Suite 202
Washington, DC 20007
Tel: 202-800-5599
Fax: 202-478-0303

Project Name and Address

MARYLAND AVENUE

Location: **1250 MARYLAND AVENUE SW
WASHINGTON, DC 20024**

Contractor:

BALFOUR BEATTY

Approved for Fabrication by:

Signature

Contract # **224009**

Drawing # **E-12.03**

Contract Item: **LEVEL-06
SLAB EXTENSION**

Ref: **SOW-12: 3,4,5&6 / S307**

Date

01/20/2025


Drawing Title:

**SOW #12 LEVEL-06 NEW
SLAB EXTENSION SUPPORT
SECTIONS**

Scale


VARIES

SHOP / ERECTOR NOTE:
LOCATE EXISTING REBAR PRIOR TO FABRICATION OF PLATE.
DO NOT DRILL THROUGH REBAR.

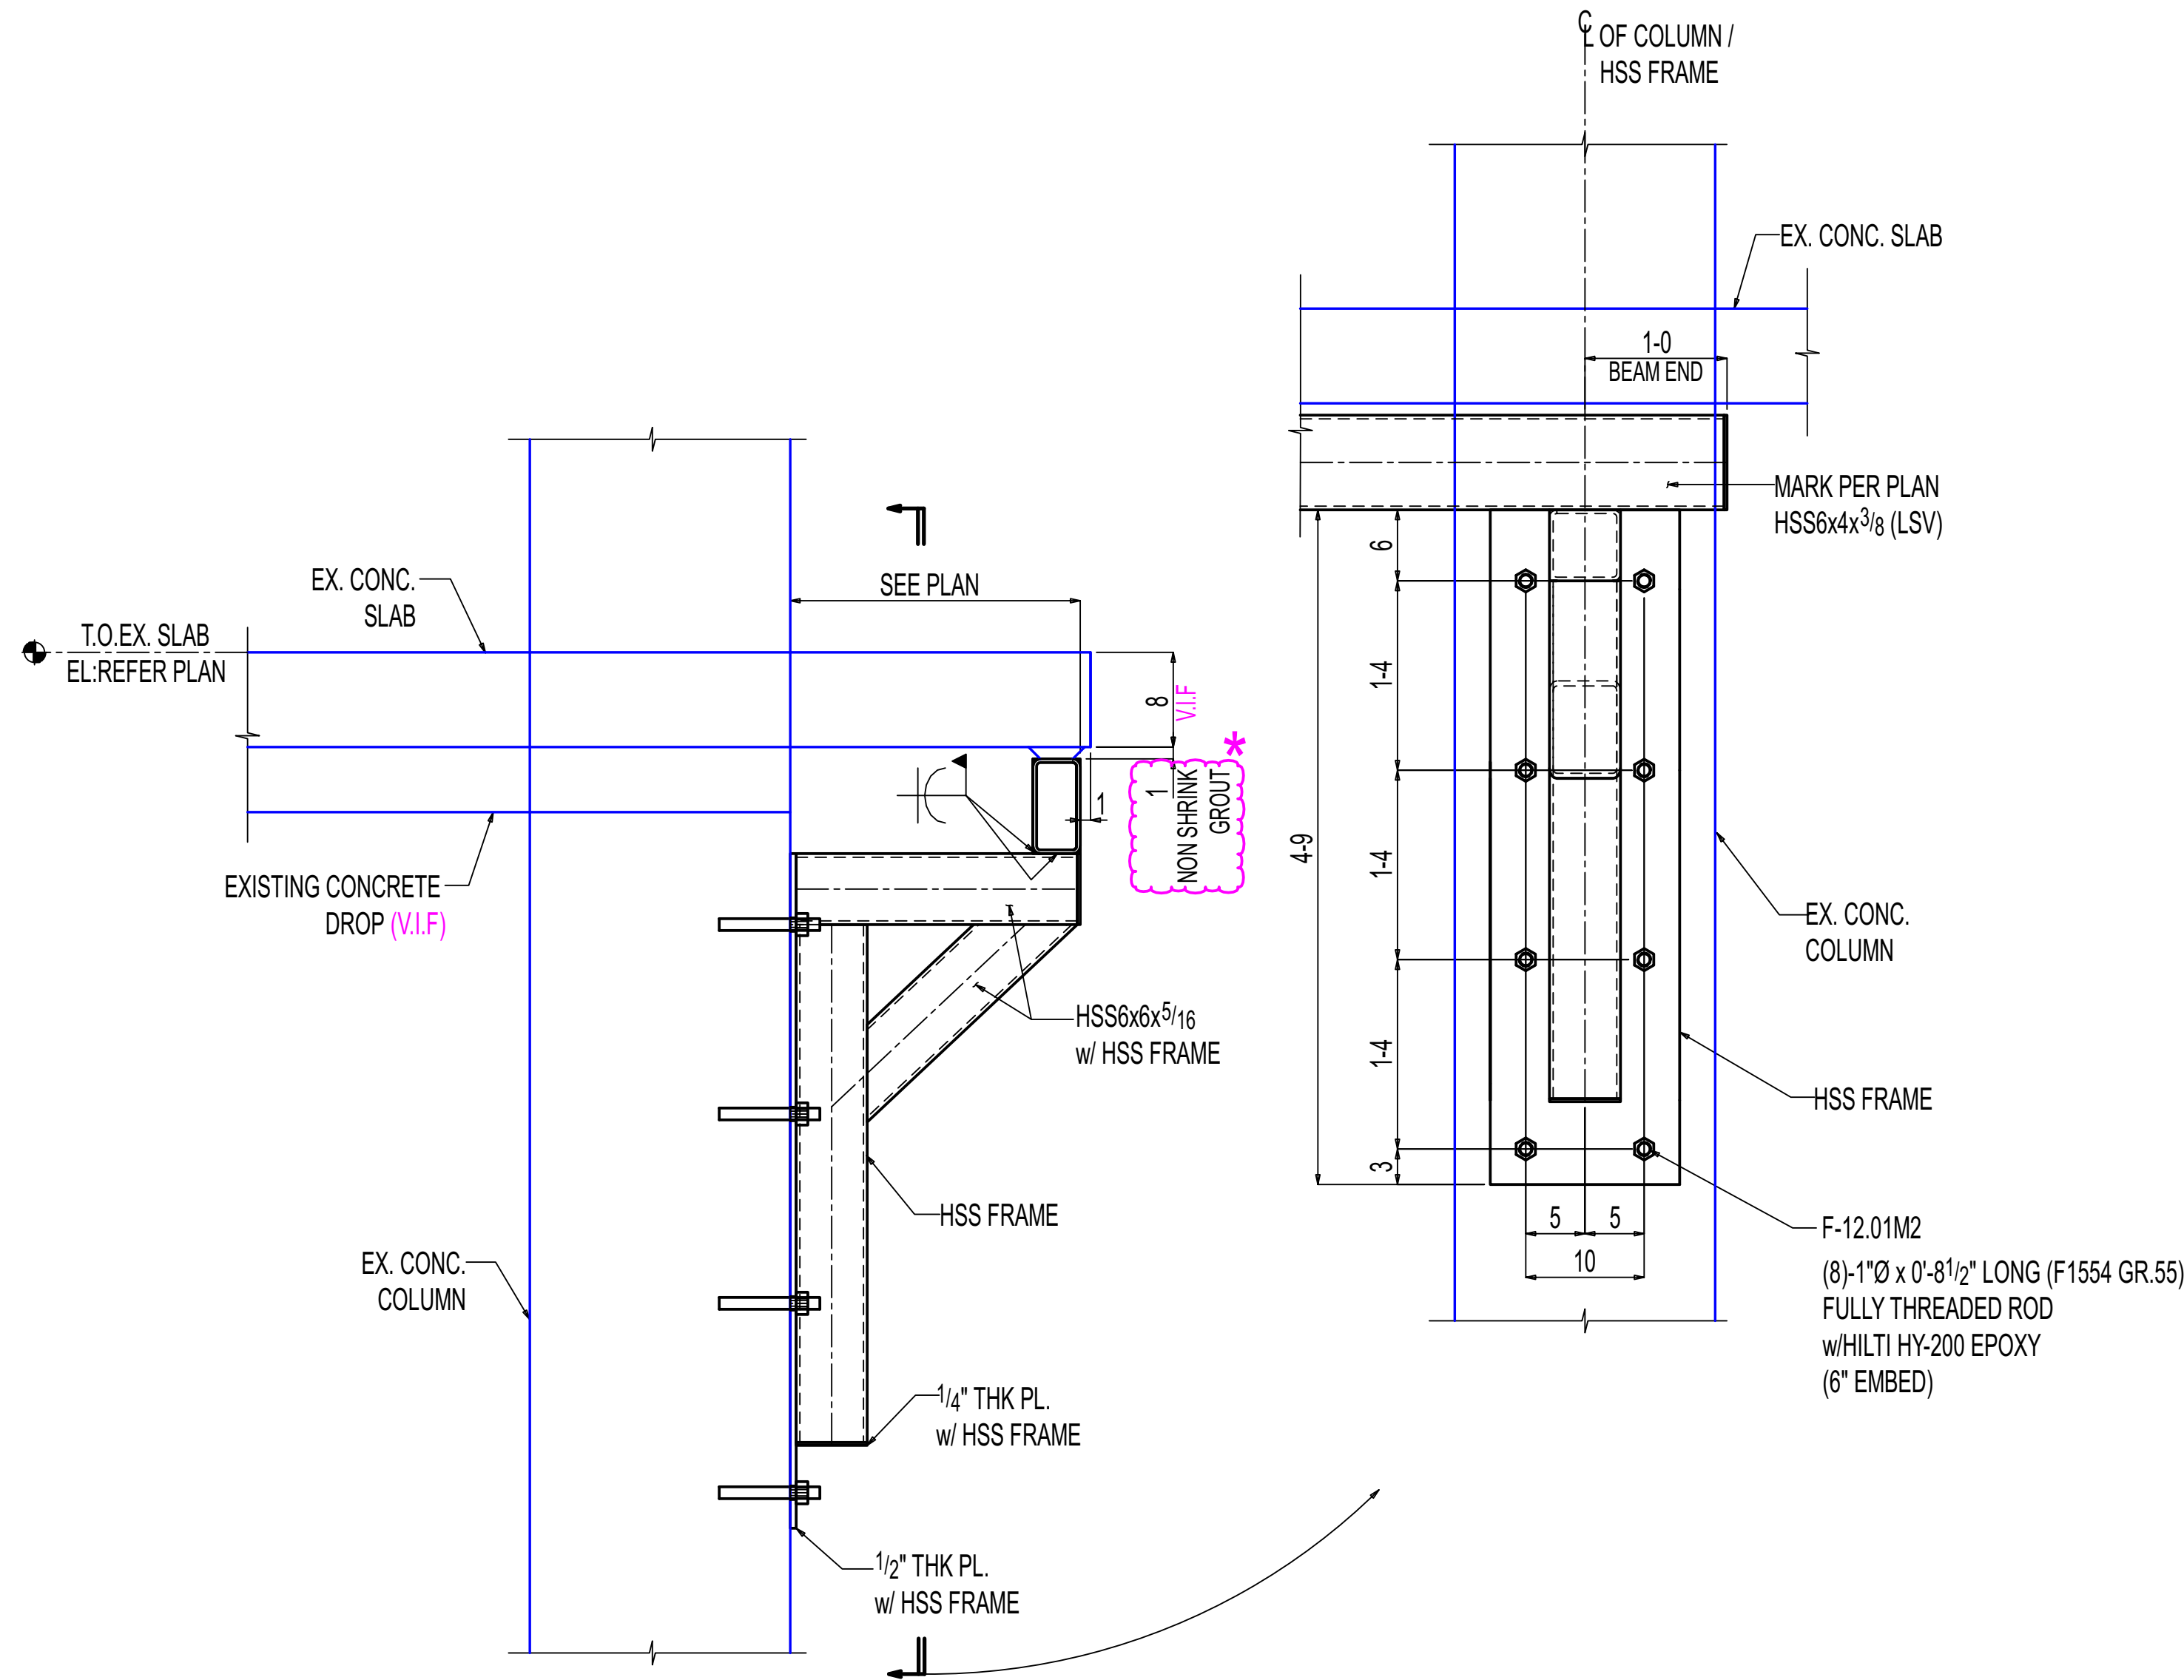


K-K
E-12.00
(REF: 9/S315) (SIM)
OTHERS NOT SHOWN FOR CLARITY


*** ERECTOR NOTE:**
PROVIDE 1\"/>

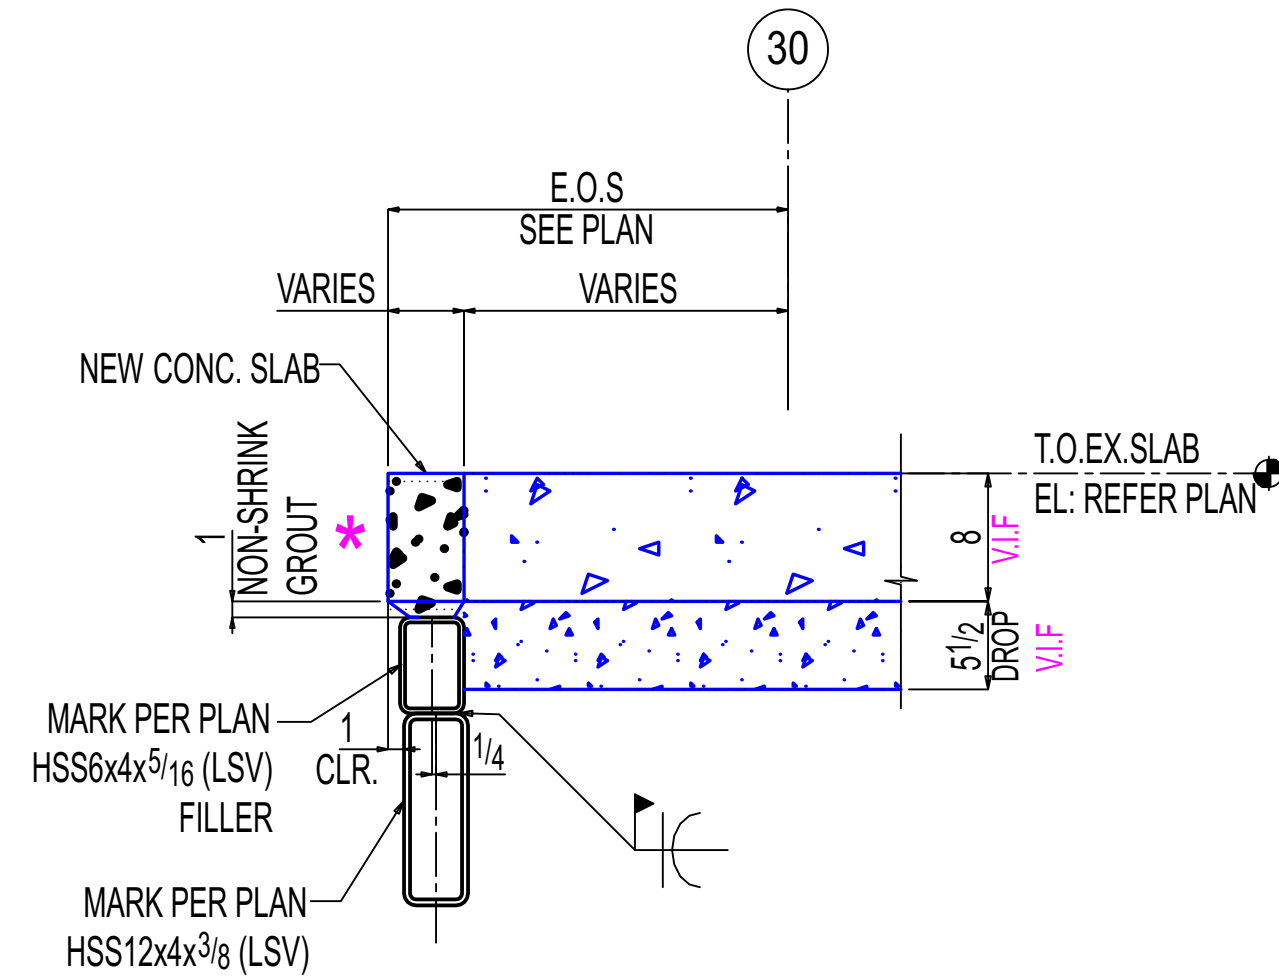


M-M
E-12.00A
(REF: 4/S315)
OTHERS NOT SHOWN FOR CLARITY

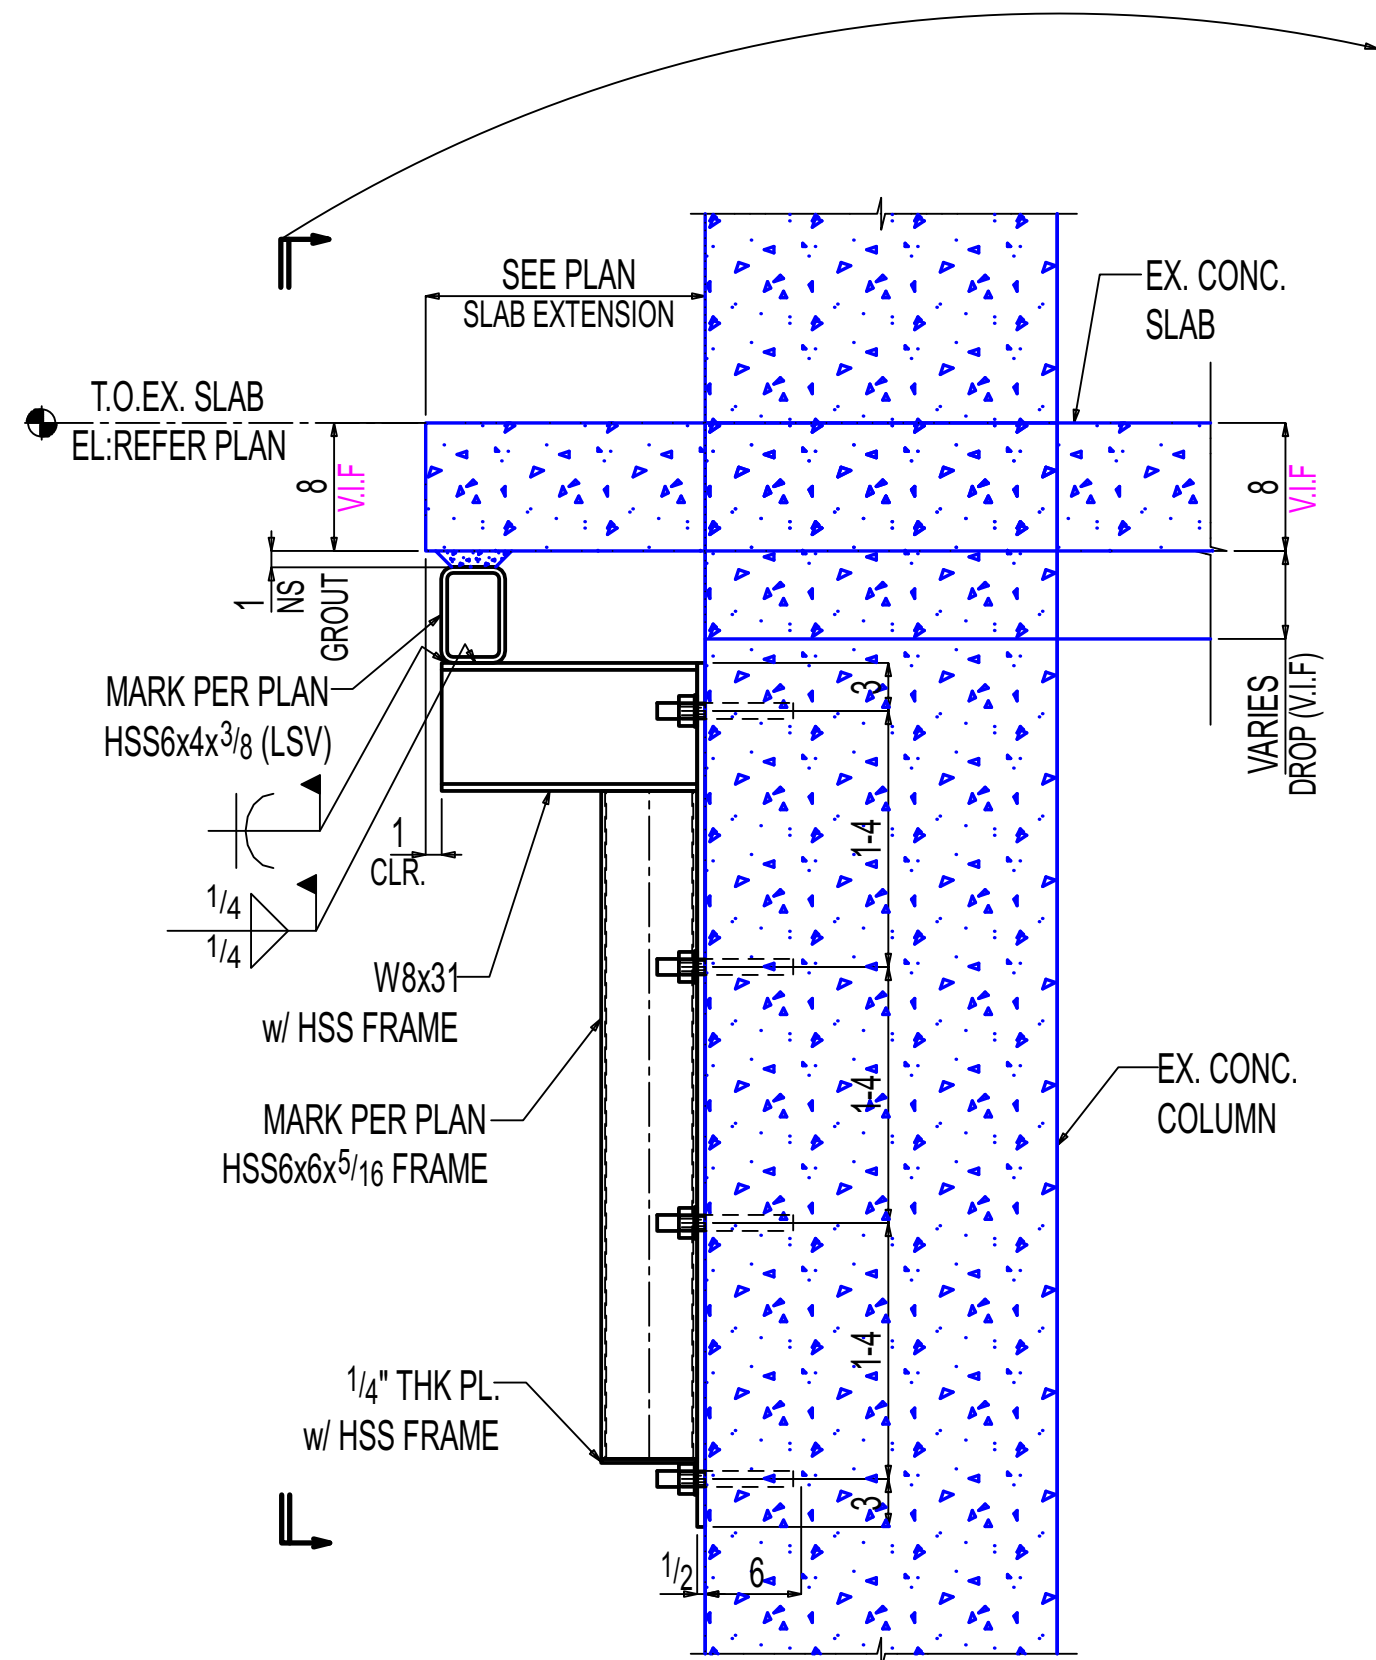

L-L
E-12.00
(REF: 10/S315)
OTHERS NOT SHOWN FOR CLARITY

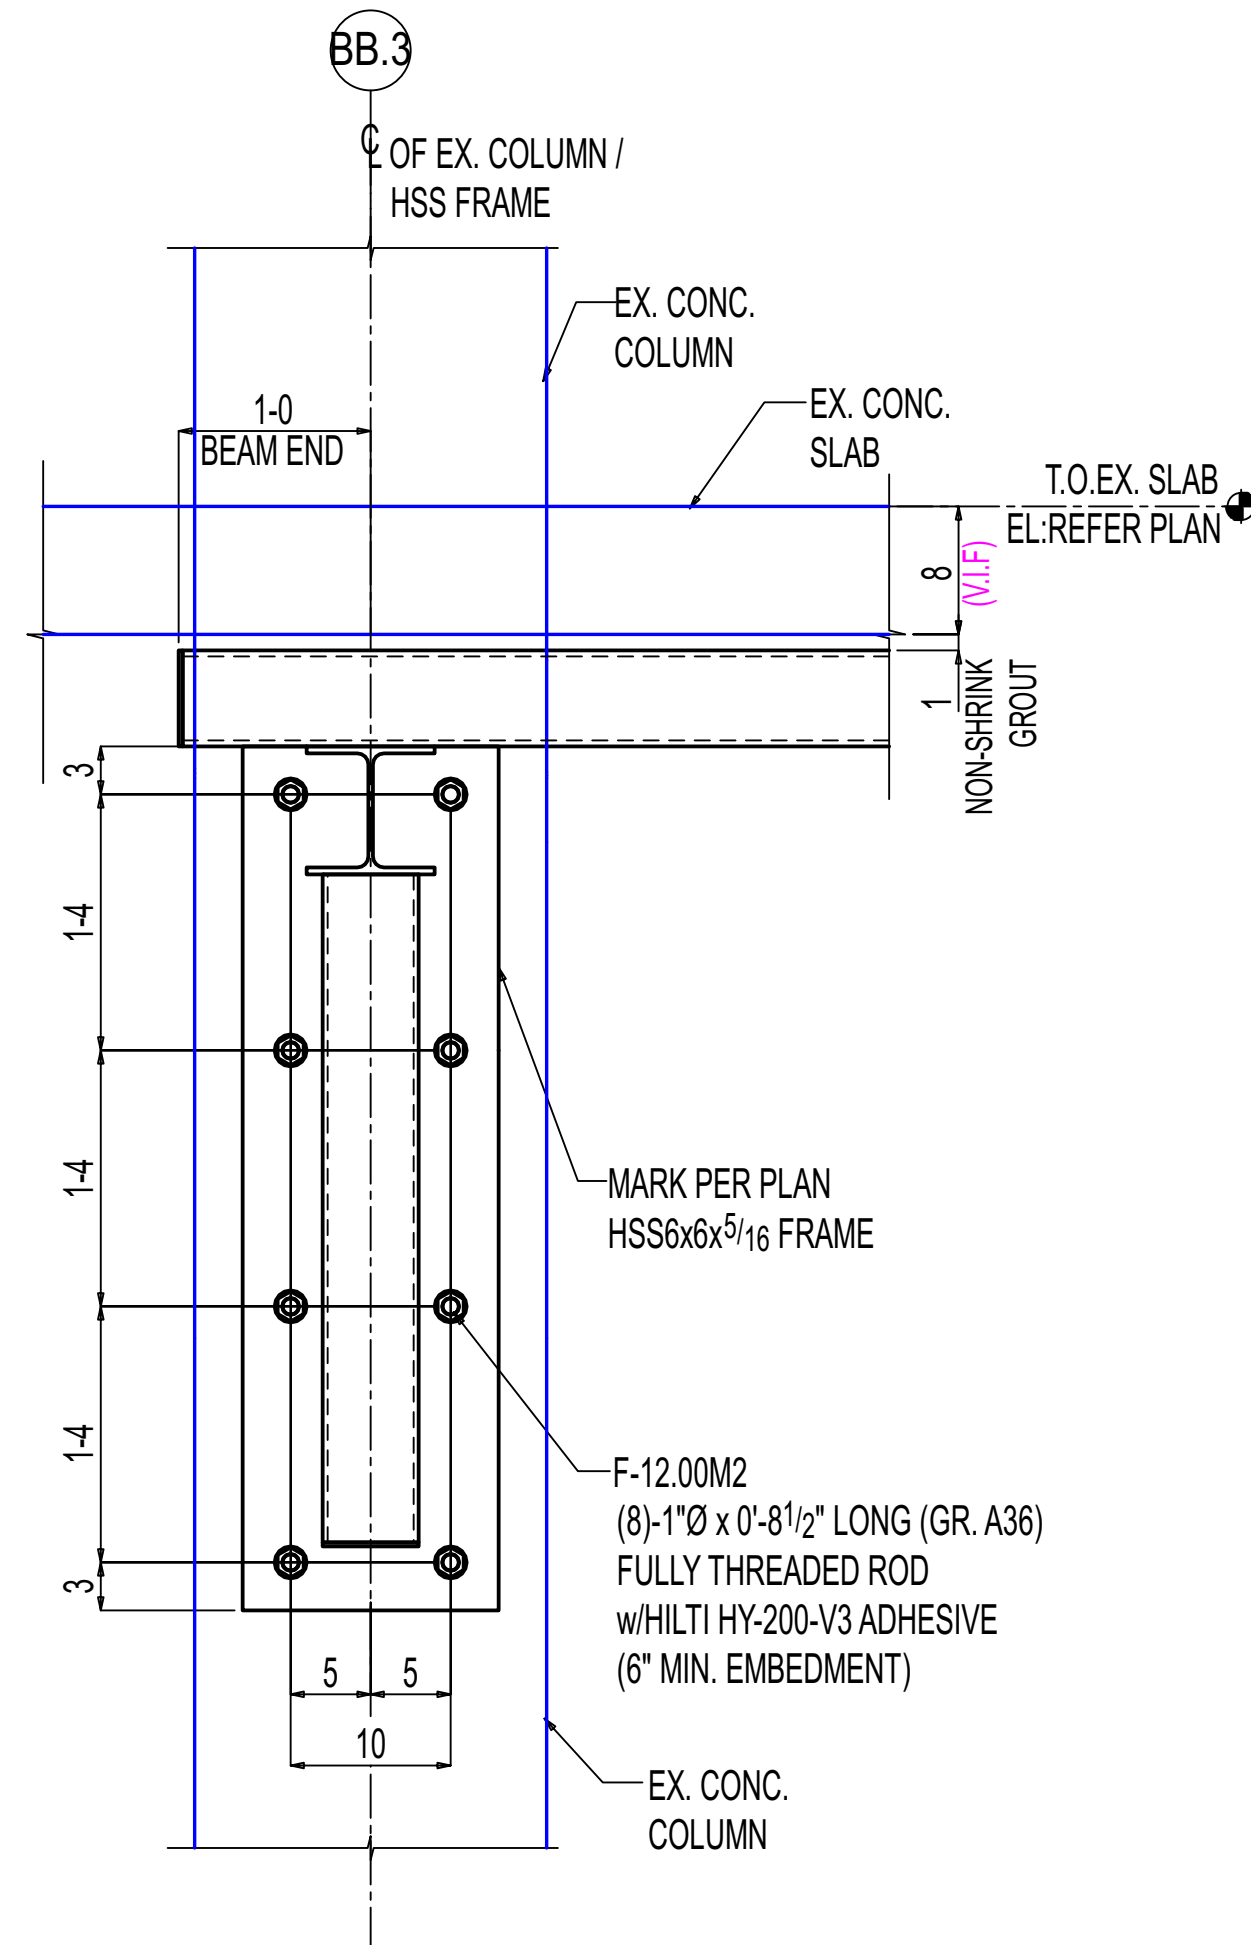

SHOP / ERECTOR NOTE:
LOCATE EXISTING REBAR PRIOR TO FABRICATION OF PLATE.
DO NOT DRILL THROUGH REBAR.

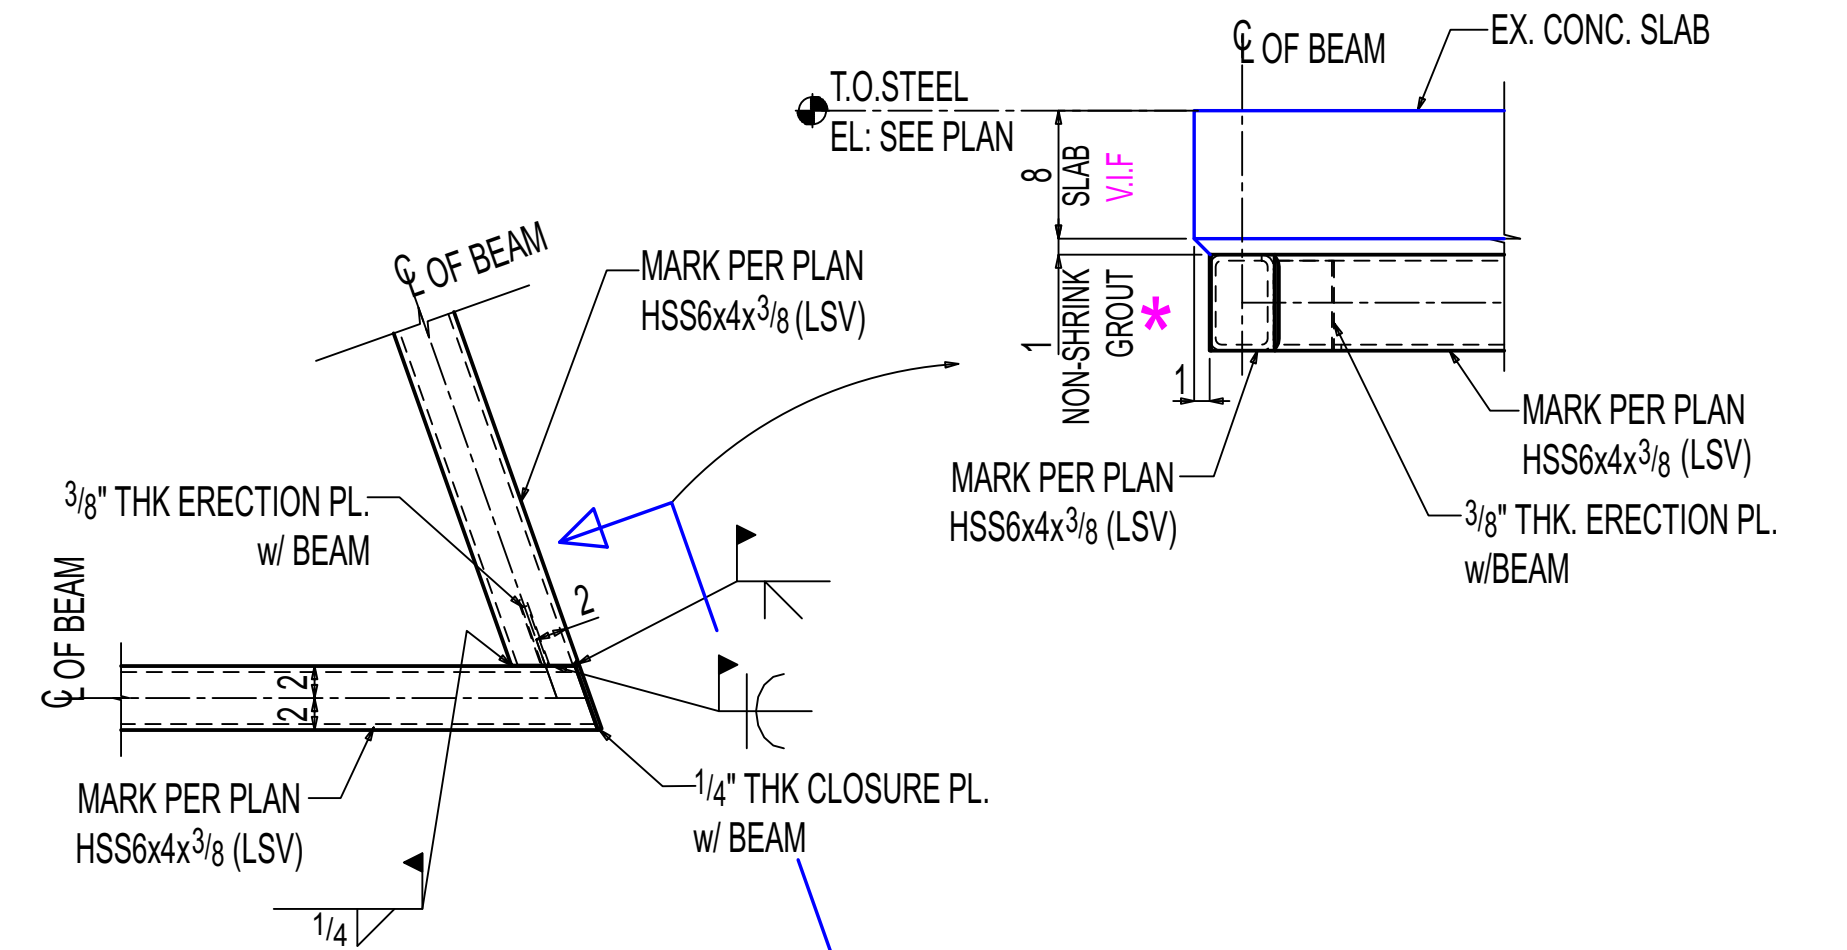

DETAIL-3
E-10.00
OTHERS NOT SHOWN FOR CLARITY

General Notes

- *Structural steel shall conform to ASTM-A992.
- *Structural SQR/RND.tubing conform to ASTM A500 Grade C
- *Pipe shall conform to ASTM A53, Grade B.
- *Channels, Angles and plates shall conform to A36.
- *All bolts shall be 3/4" High strength in accordance with ASTM A325 (UNO)
- *Welding Electrodes for Carbon steel :E70xx

# of Copies	Revision/ Issue	Destination	Date
1	0	For Construction	11-14-2025
2	B	For Re-Approval	10-24-2025
1	A	For Approval	09-19-2025

IRON FABRICATION SERVICES, LLC.

3029 M. Street, NW, Suite 202
Washington, DC 20007
Tel: 202-800-5599
Fax: 202-478-0303

Project Name and Address
MARYLAND AVENUE

Location: **1250 MARYLAND AVENUE SW
WASHINGTON, DC 20024**


Contractor:
BALFOUR BEATTY

Approved for Fabrication by: _____

Signature _____

Contract # 224009	Drawing # E-12.04
Contract Item: LEVEL-06 SLAB EXTENSION	
Ref: SOW-12: 3,4,5&6 / S307	

Date 01/20/2025	Drawing Title: SOW #12 LEVEL-06 NEW SLAB EXTENSION SUPPORT SECTIONS
Scale VARIES	

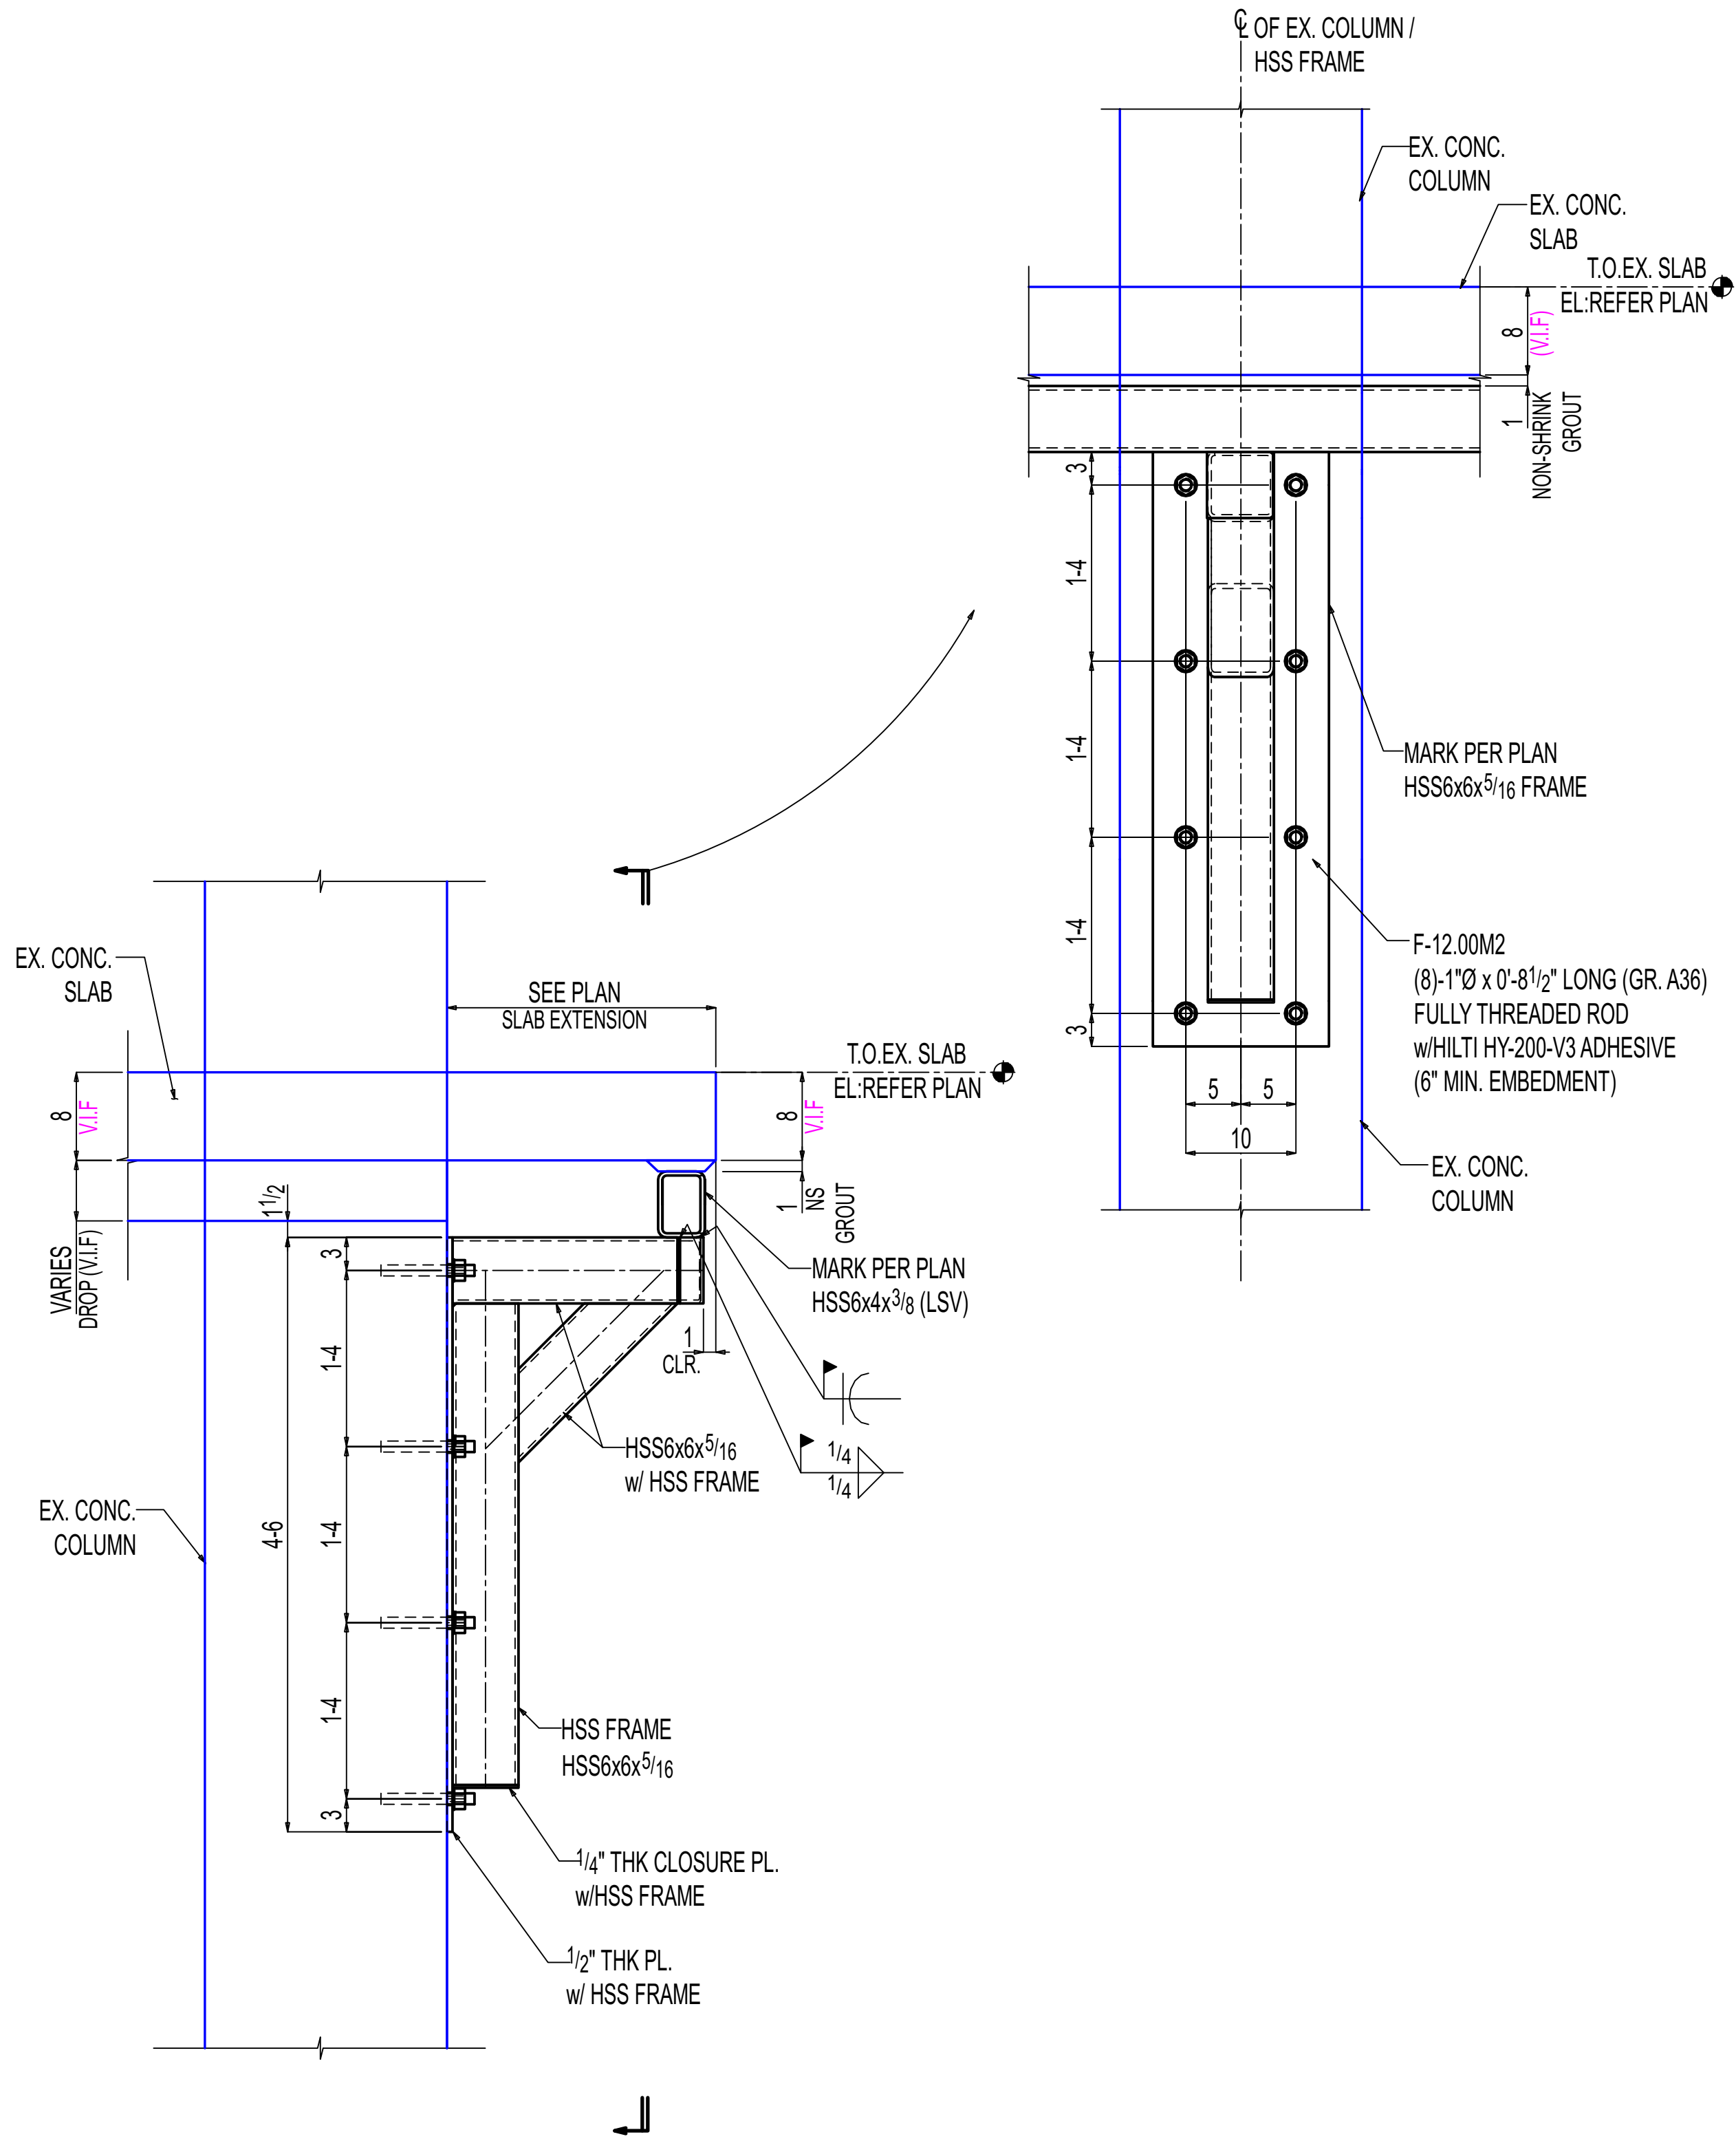

N-N
E-12.00
(REF:10/S315)
OTHERS NOT SHOWN FOR CLARITY

SHOP / ERECTOR NOTE:
LOCATE EXISTING REBAR PRIOR TO FABRICATION OF PLATE.
DO NOT DRILL THROUGH REBAR.

- General Notes
- *Structural steel shall conform to ASTM-A992.
 - *Structural SQR/RND.tubing conform to ASTM A500 Grade C
 - *Pipe shall conform to ASTM A53, Grade B.
 - *Channels, Angles and plates shall conform to A36.
 - *All bolts shall be 3/4" High strength in accordance with ASTM A325 (UNO)
 - *Welding Electrodes for Carbon steel :E70xx

1	0	For Construction	11-14-2025
# of Copies	Revision/ Issue	Destination	Date

IRON FABRICATION SERVICES, LLC.

3029 M. Street, NW, Suite 202
Washington, DC 20007
Tel: 202-800-5599
Fax: 202-478-0303

Project Name and Address

MARYLAND AVENUE
Location: **1250 MARYLAND AVENUE SW**
WASHINGTON, DC 20024

Contractor:

BALFOUR BEATTY

Approved for Fabrication by:	Signature

Contract #	224009	Drawing #	E-12.05
Contract Item:	LEVEL-06 SLAB EXTENSION		
Ref:	SOW-12: 3,4,5&6 / S307		
Date	01/ 20/ 2025	Drawing Title:	SOW #12 LEVEL-06 NEW SLAB EXTENSION SUPPORT SECTIONS
Scale	VARIES		