



BILL OF MATERIAL							
LINE #	QTY	PC	MARK	DESCRIPTION	LENGTH	REMARKS	WEIGHT
	TOTAL						TOTAL
							MILL #
ONE	F-12.02C1	COLUMN					329
1	F-12.02C1	HSS6x6x3/8		10 4	A500C		284
1	p1974	PL1/4x7		1 6	A36		45
		FIELD BOLTS					
2		3/4 Dia HILTI HAS V-36		0 8	+1HD WASH		
		w/ HILTI HIT HY-200 EPOXY			(3/4" EMBEDMENT)		
ONE	F-12.02C2	COLUMN					335
1	F-12.02C2	HSS6x6x3/8		9 10 3/8	A500C		272
1	hss124	HSS4x4x3/16		1 6 1/4	A500C		23
1	hss123	HSS4x4x3/16		1 0 7/8	A500C		16
1	a115	L1 1/2x1x3/16		0 5	A36		1
1	p356	PL3/8x6 1/2		1 6	A36		21
1	p3633	PL1/4x5 5/8		0 5 5/8	A36		2
1	p3634	PL1/4x4		0 4	A36		1
ONE	F-12.02B1	BEAM					1430
1	F-12.02B1	W12x79		18 1 1/4	A992		1430
ONE	F-12.02B2	BEAM					463
1	F-12.02B2	HSS12x4x3/8		12 13/8	A500C		457
2	p3645	PL1/4x4		1 0	A36		7
ONE	F-12.02B3	BEAM					101
1	F-12.02B3	HSS6x4x3/8		4 5 7/16	B1E A500C		100
1	p274	PL1/4x4		0 6	A36		2
ONE	F-12.02B4	BEAM					565
1	F-12.02B4	HSS6x4x3/8		25 0 3/16	A500C		560
1	fb324	FL3/8x4		0 5 5/8	A36		2
1	p275	PL1/4x4 1/4		0 6	A36		2
1	p274	PL1/4x4		0 6	A36		2

Total weight : 3224

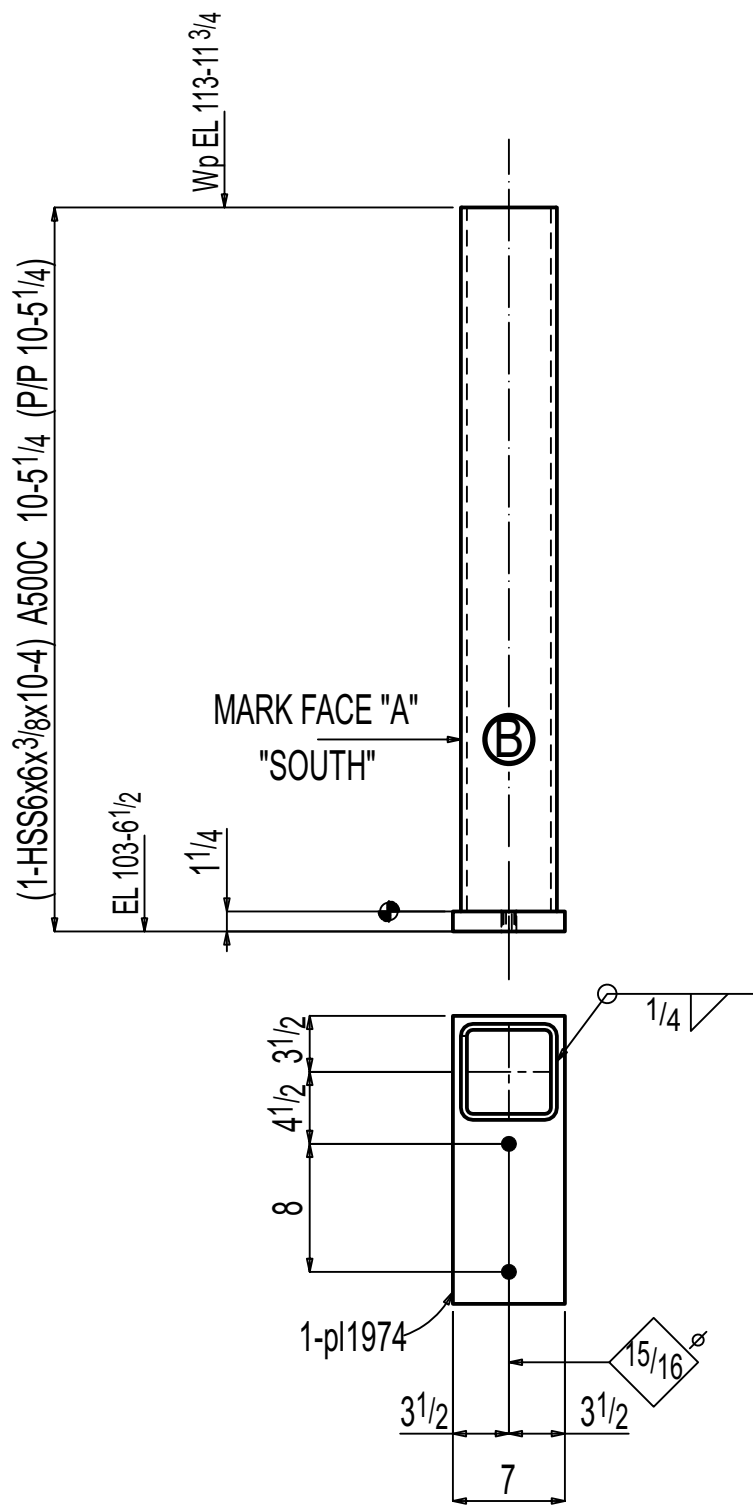


ONE COLUMN F-12.02C1

AT GRID:
EE & A

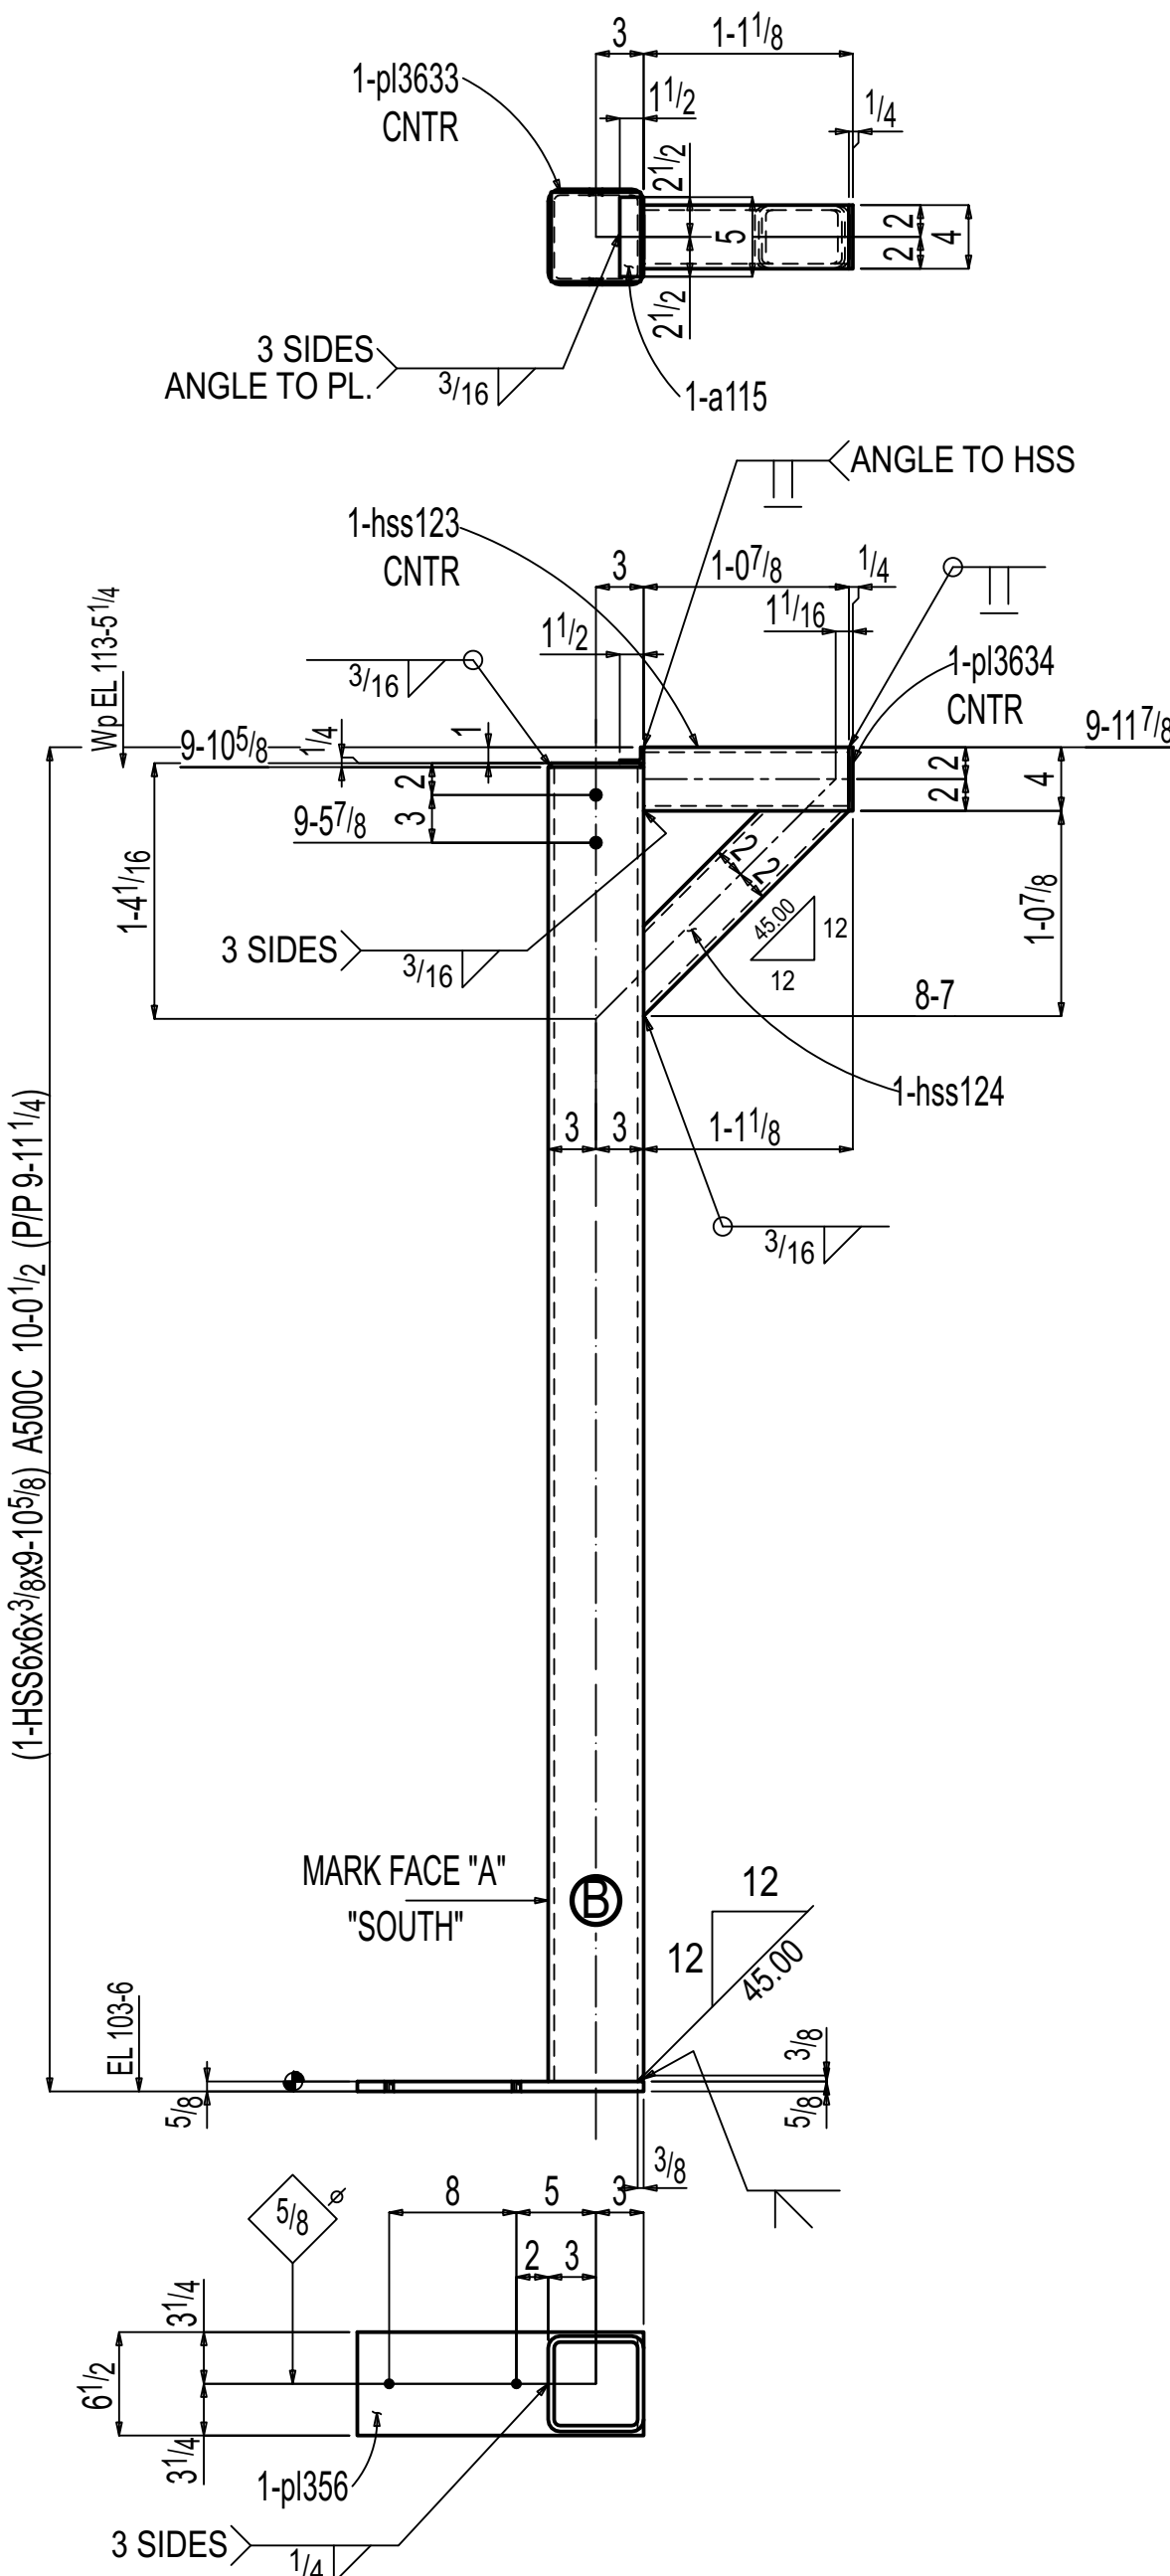


ONE COLUMN F-12.02C2

AT GRID:
AA & K

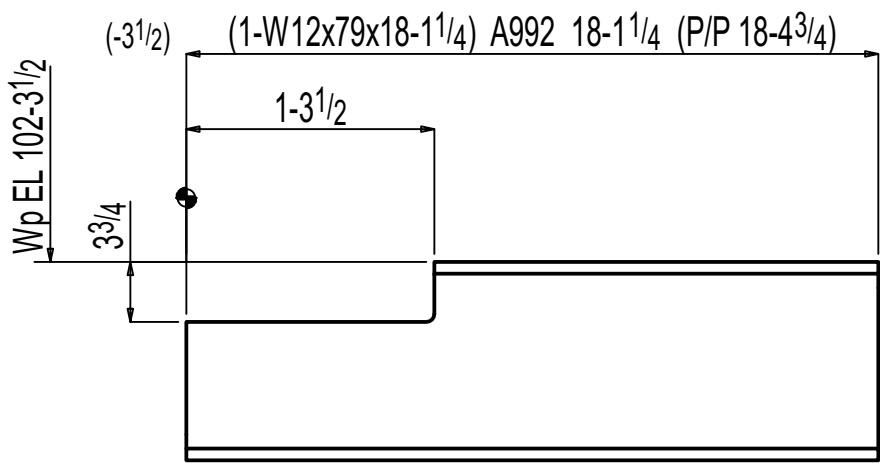


ONE BEAM F-12.02B1

W 12 3/8x1 1/2
F 12 1/8x3/4
K 15/8x1 1/8

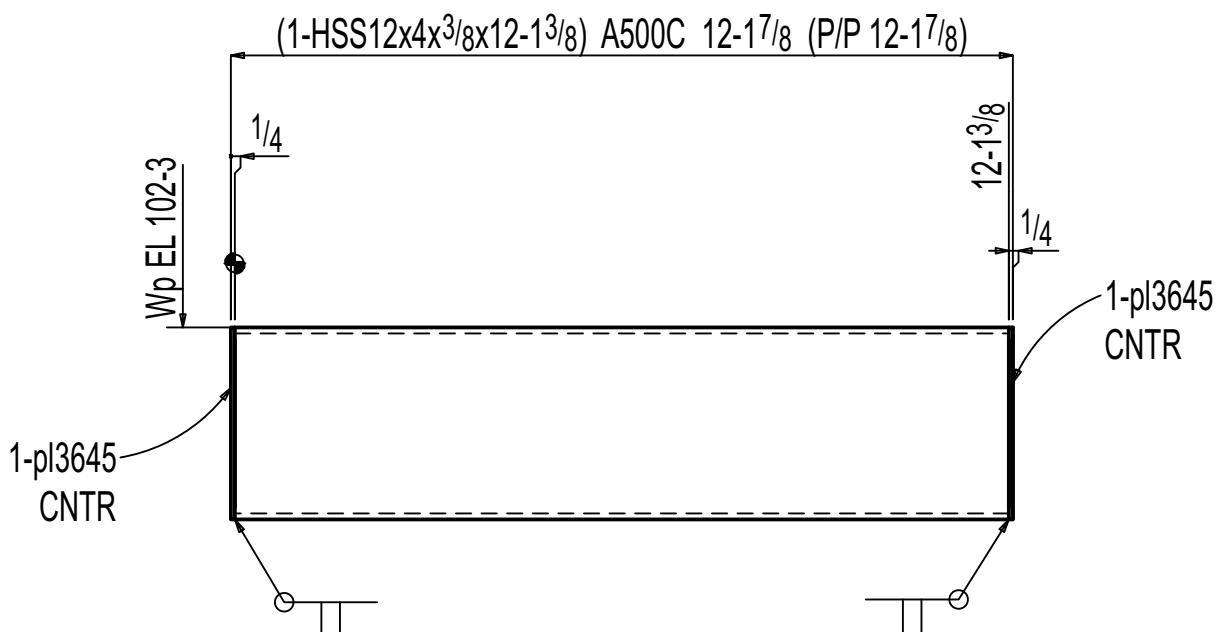


ONE BEAM F-12.02B2

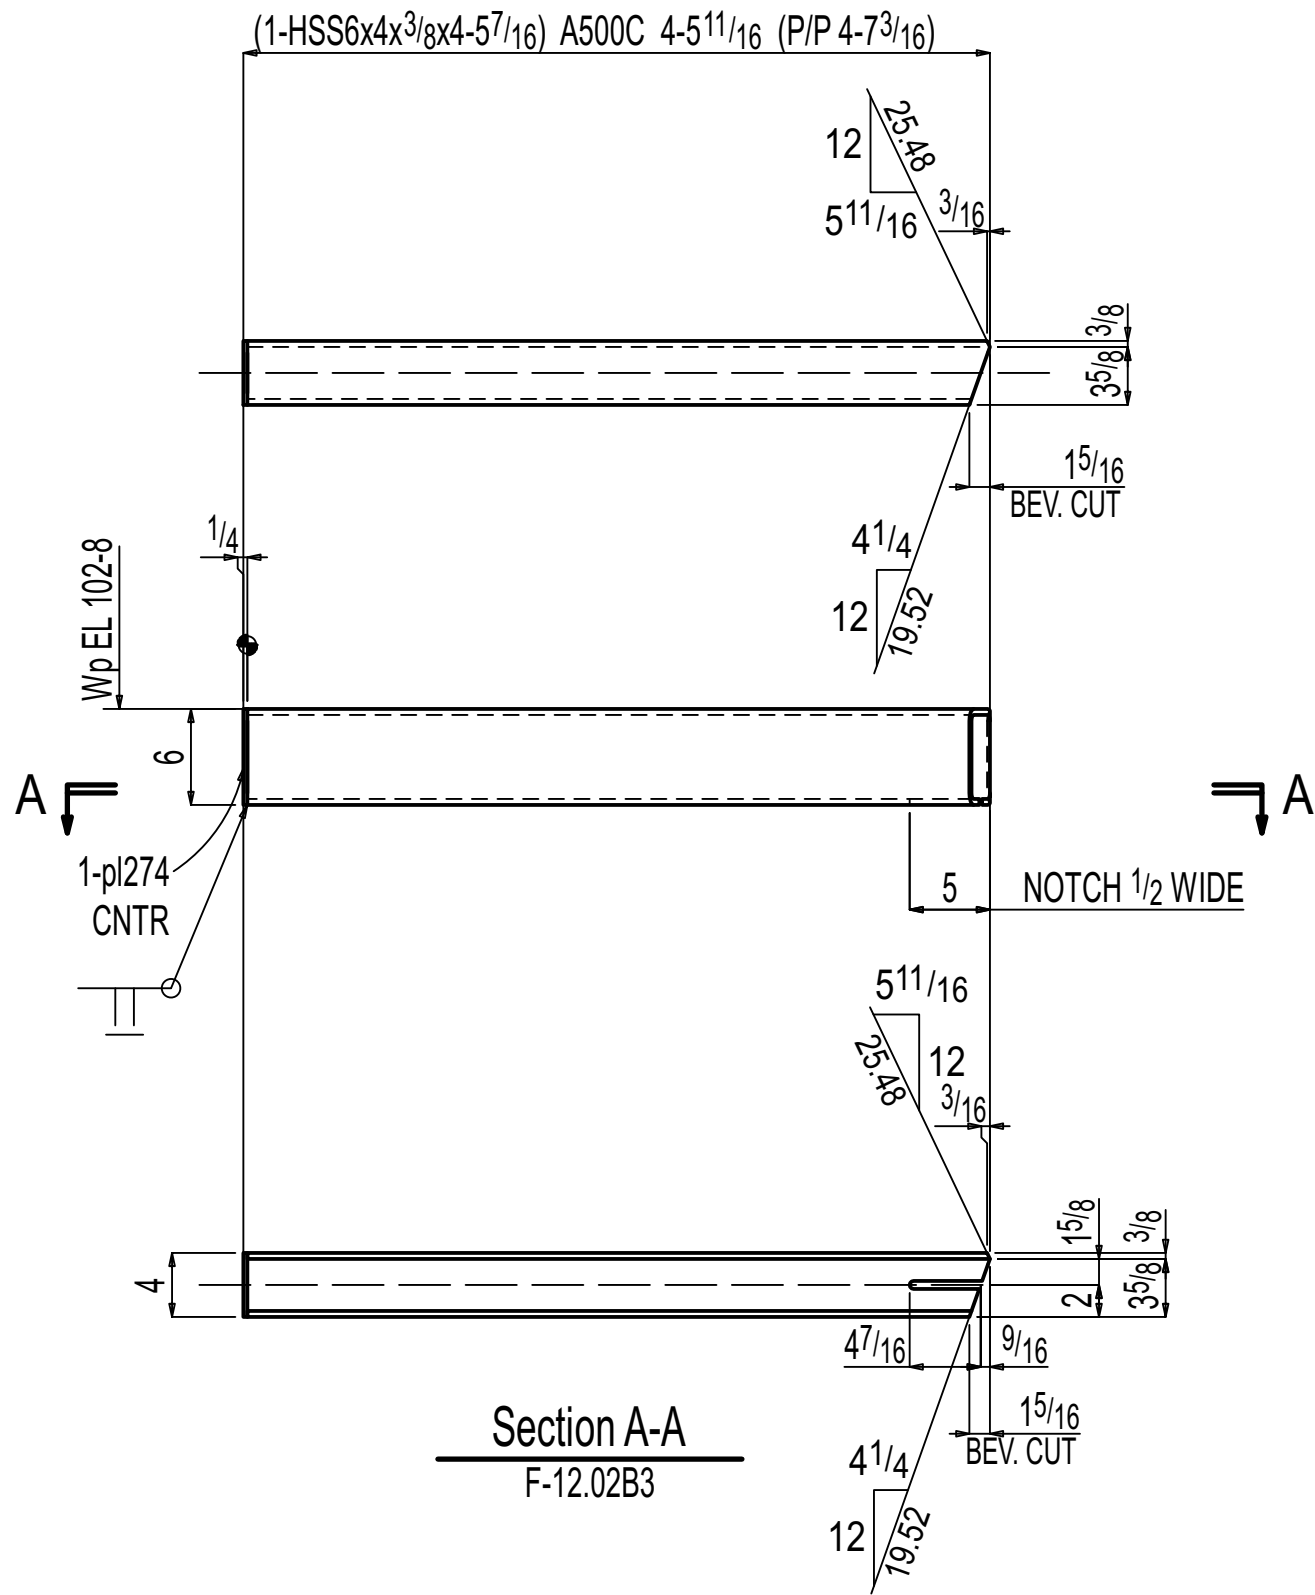

ONE BEAM F-12.02B3

Section A-A
F-12.02B3

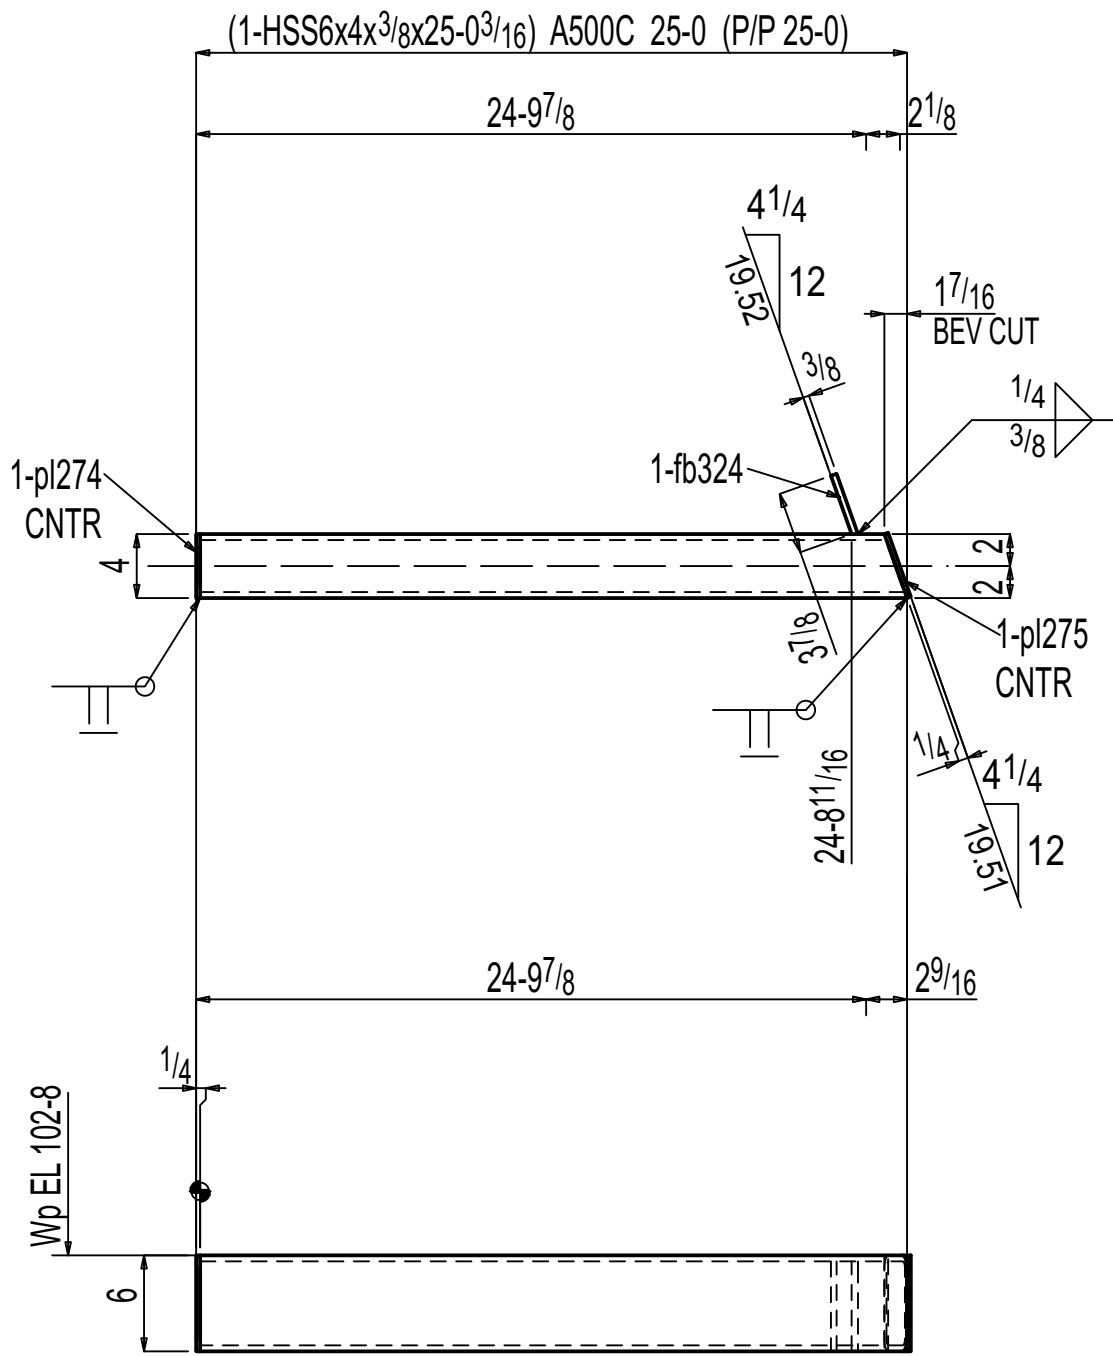

ONE BEAM F-12.02B4

PAINT :NO PAINT
PREPARATION :SSPC-SP3

General Notes			
*Structural steel shall conform to ASTM-A992.			
*Structural SQR/RND,tubing conform to ASTM A500 Grade C			
*Pipe shall conform to ASTM A53, Grade B.			
*Channels, Angles and plates shall conform to A36.			
*All bolts shall be 3/4" High strength in accordance with ASTM A325 (UNO)			
*Welding Electrodes for Carbon steel :E70xx			
5	0	For Fabrication	11-14-2025
4	D	For Re-Approval	10-24-2025
3	C	For Re-Approval	09-19-2025
2	B	Deleted	06-23-2025
1	A	For Approval	02-25-2025
# of Copies	Revision/ Issue	Destination	Date

IRON FABRICATION SERVICES, LLC.

3029 M. Street, NW, Suite 202
Washington, DC 20007
Tel: 202-800-5599
Fax: 202-478-0303

Project Name and Address
MARYLAND AVENUE
Location: **1250 MARYLAND AVENUE SW
WASHINGTON, DC 20024**

Contractor:
BALFOUR BEATTY

Approved for Fabrication by: Signature

Contract # **224009** Drawing # **F-12.02**

Contract Item: **COLUMN & BEAM**

Ref:
SOW - 12: E-12.00 - E-12.02

Date
01/ 23/ 2025
Scale
VARIES
Drawing Title:
COLUMN & BEAM DETAIL