



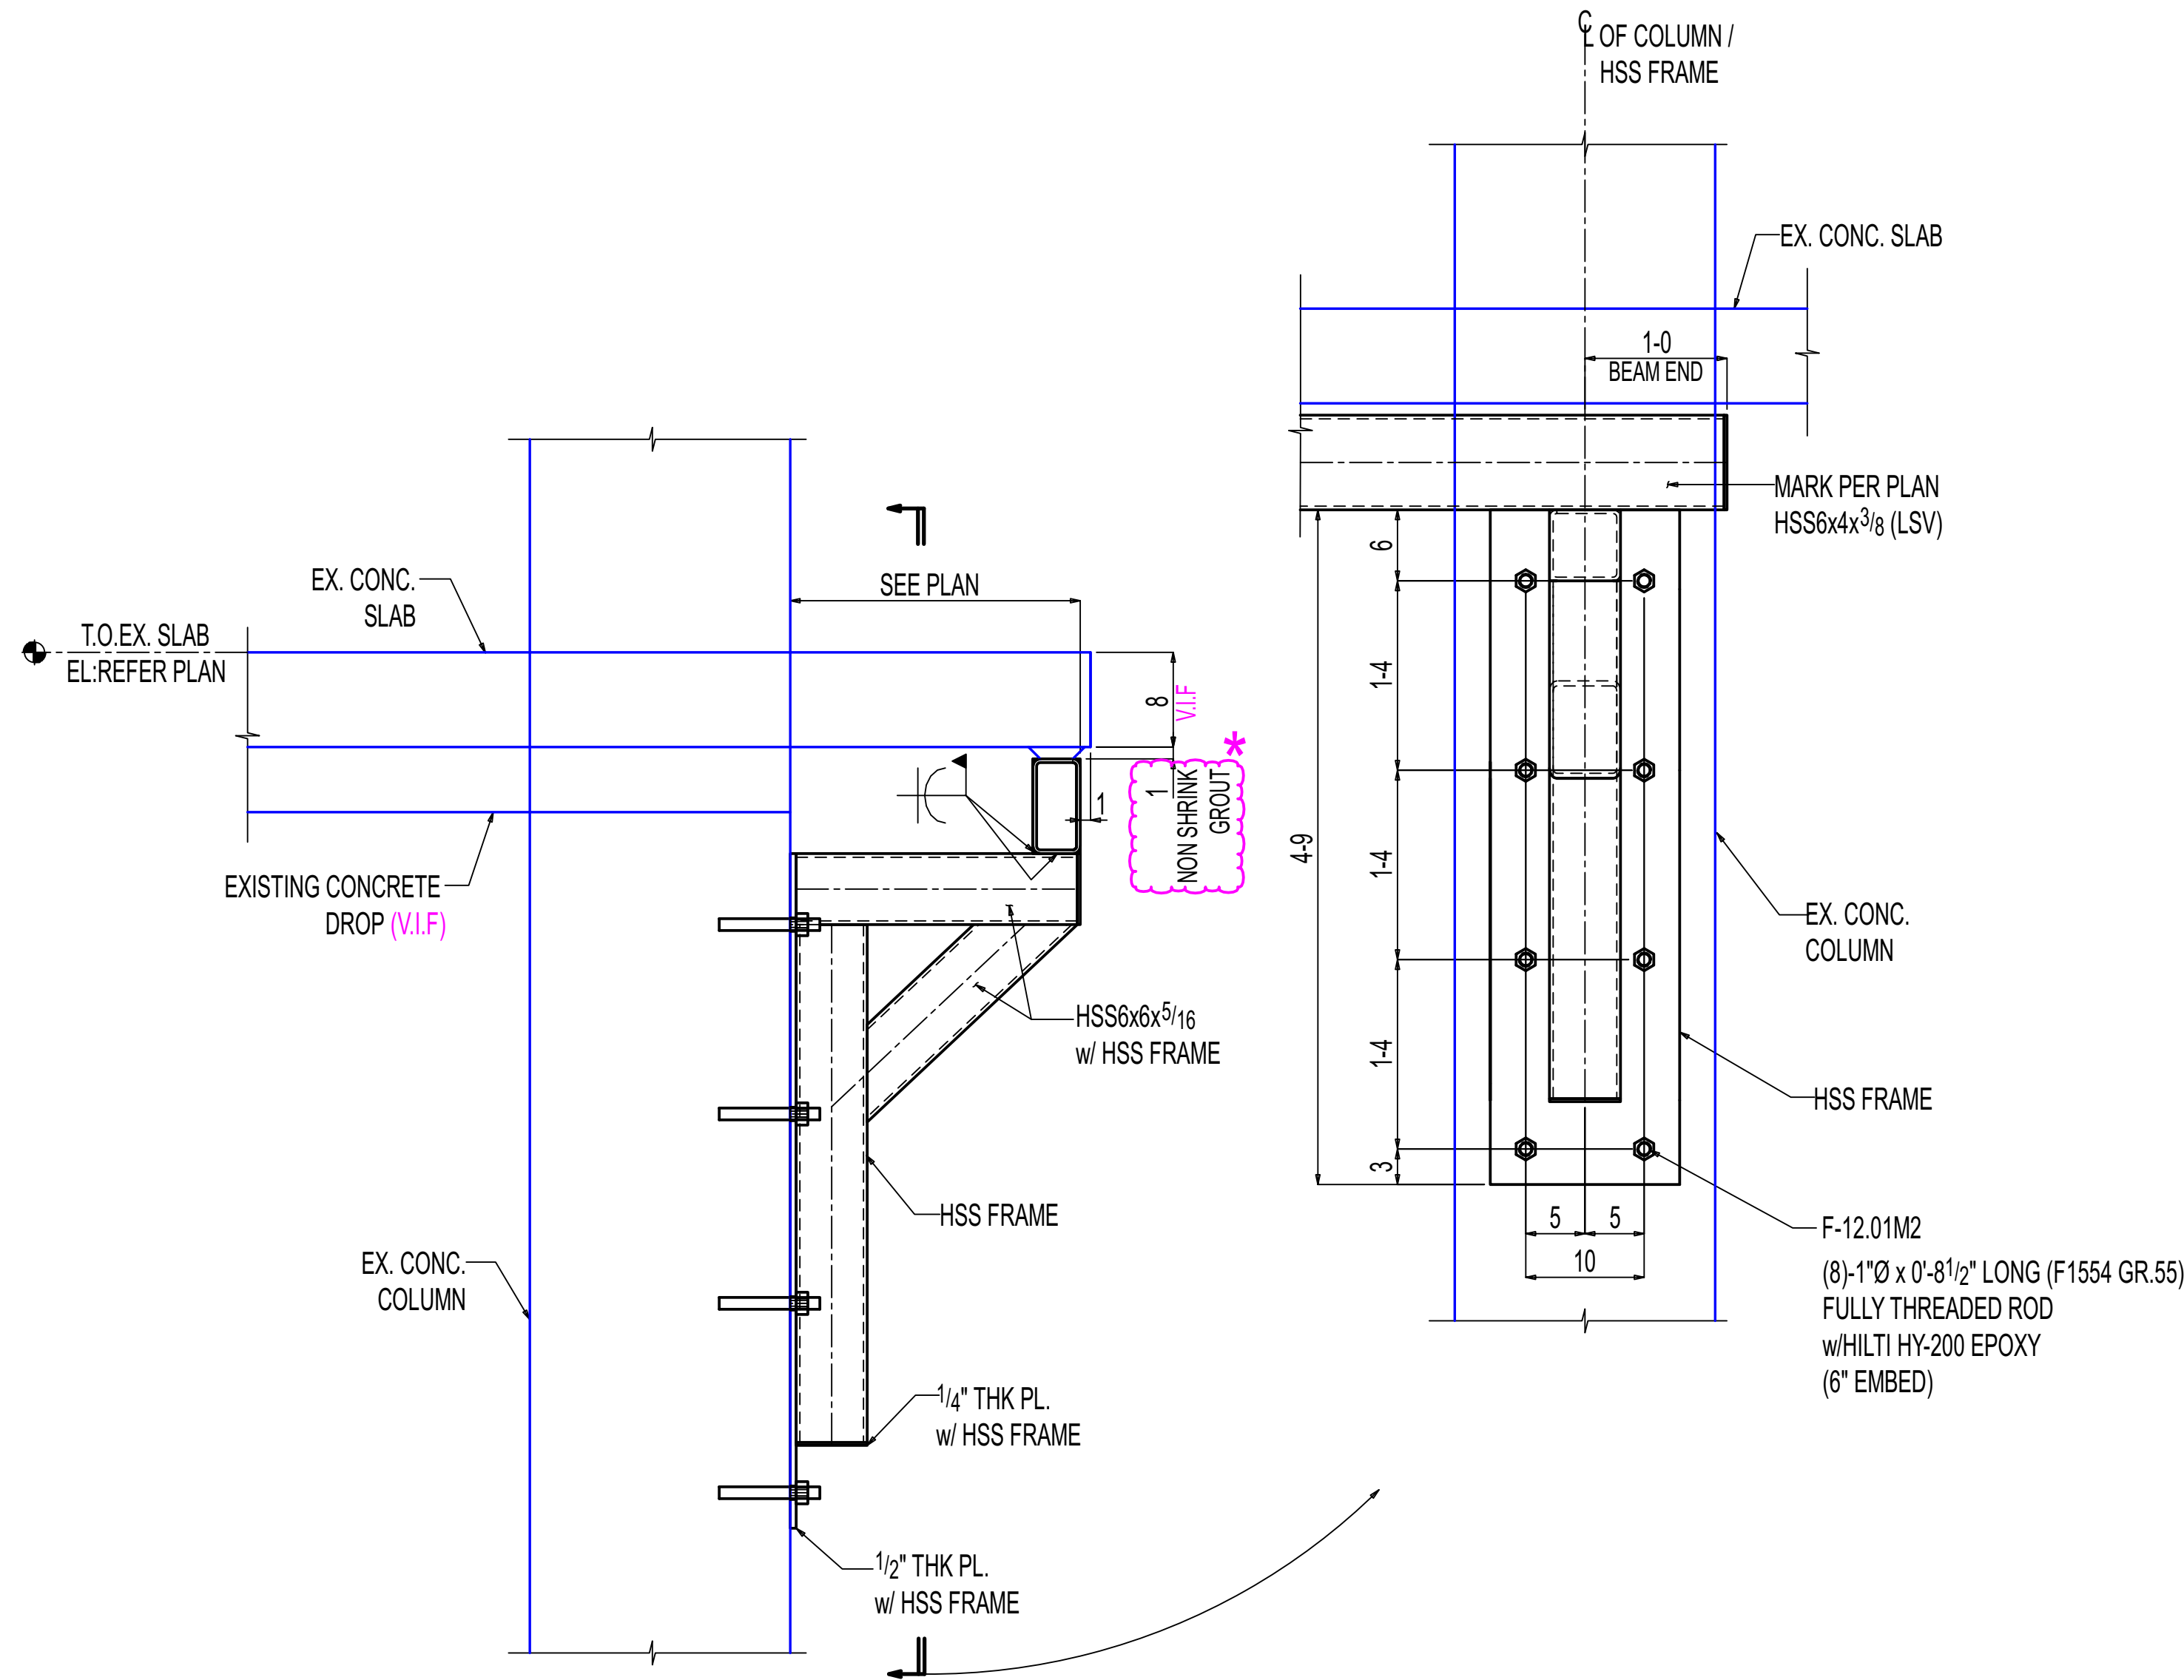


K-K
E-12.00
(REF: 9/S315) (SIM)
OTHERS NOT SHOWN FOR CLARITY

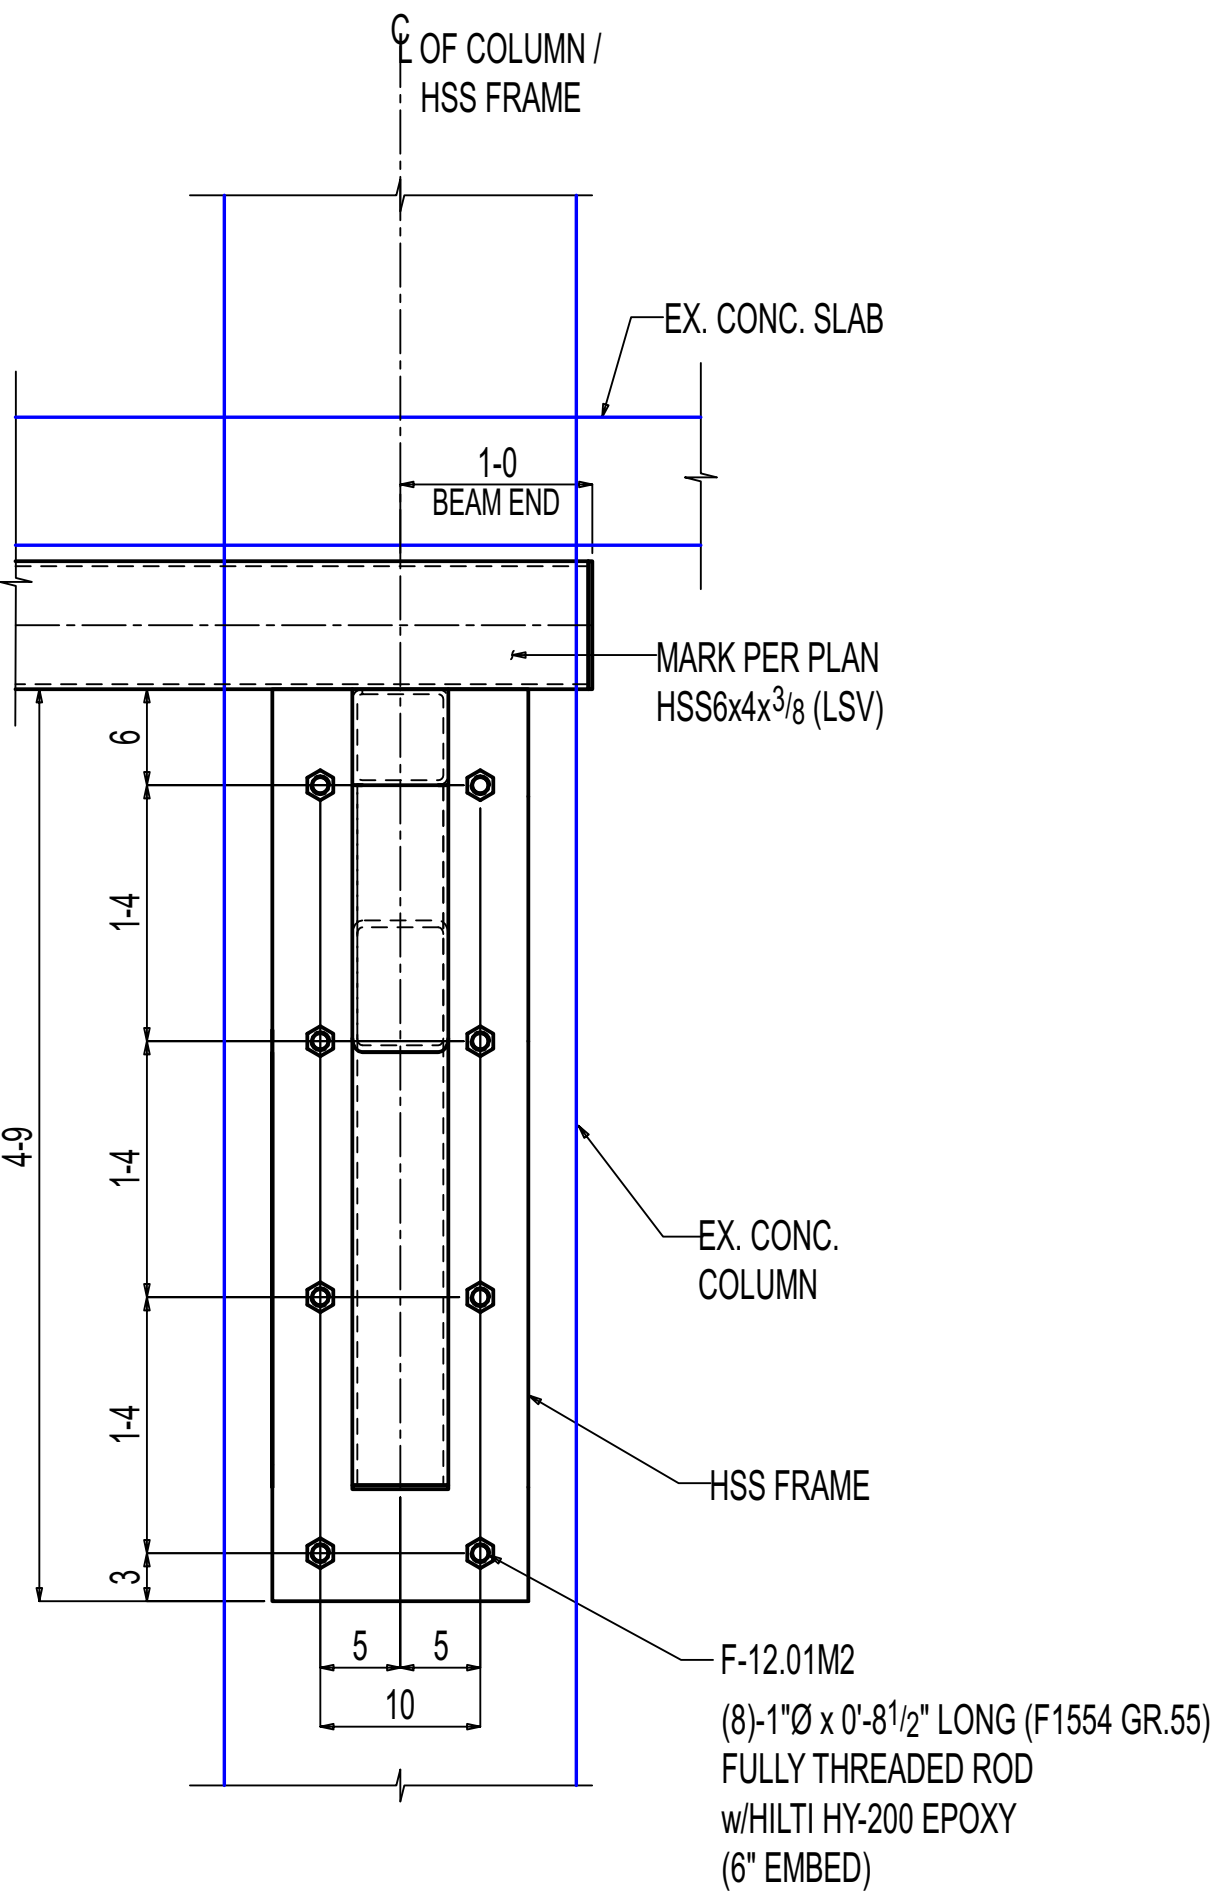


L-L
E-12.00
(REF: 10/S315)
OTHERS NOT SHOWN FOR CLARITY



*** ERECTOR NOTE:**
PROVIDE 1" NON-SHRINK GROUT, 6" LONG, CENTERED BENEATH PRECAST BEARING POINTS. COORDINATE WITH PRECAST MANUFACTURER TO CONFIRM BEARING LOCATIONS PRIOR TO INSTALLATION.

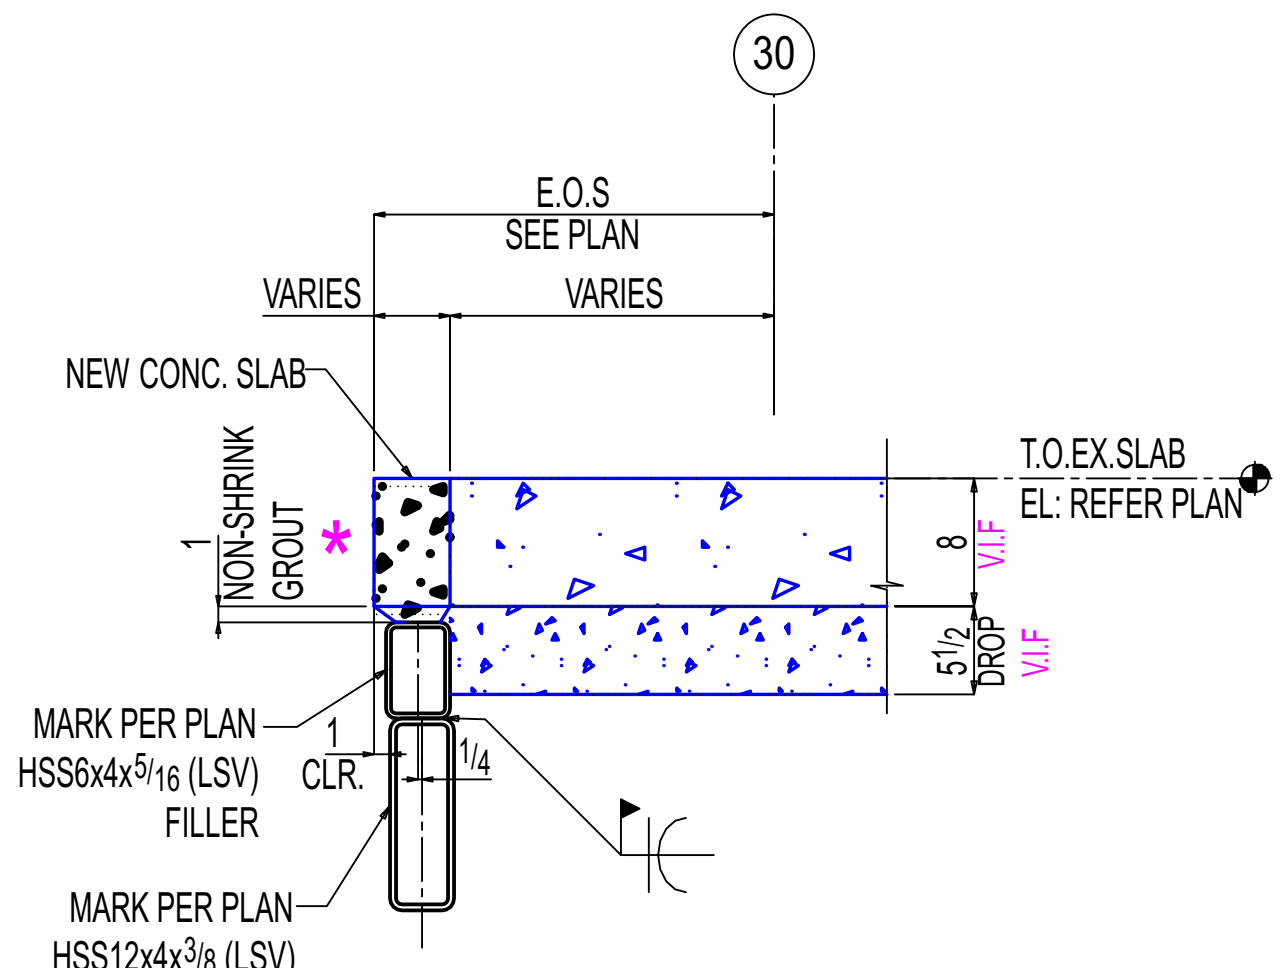

M-M
E-12.00A
(REF: 4/S315)
OTHERS NOT SHOWN FOR CLARITY

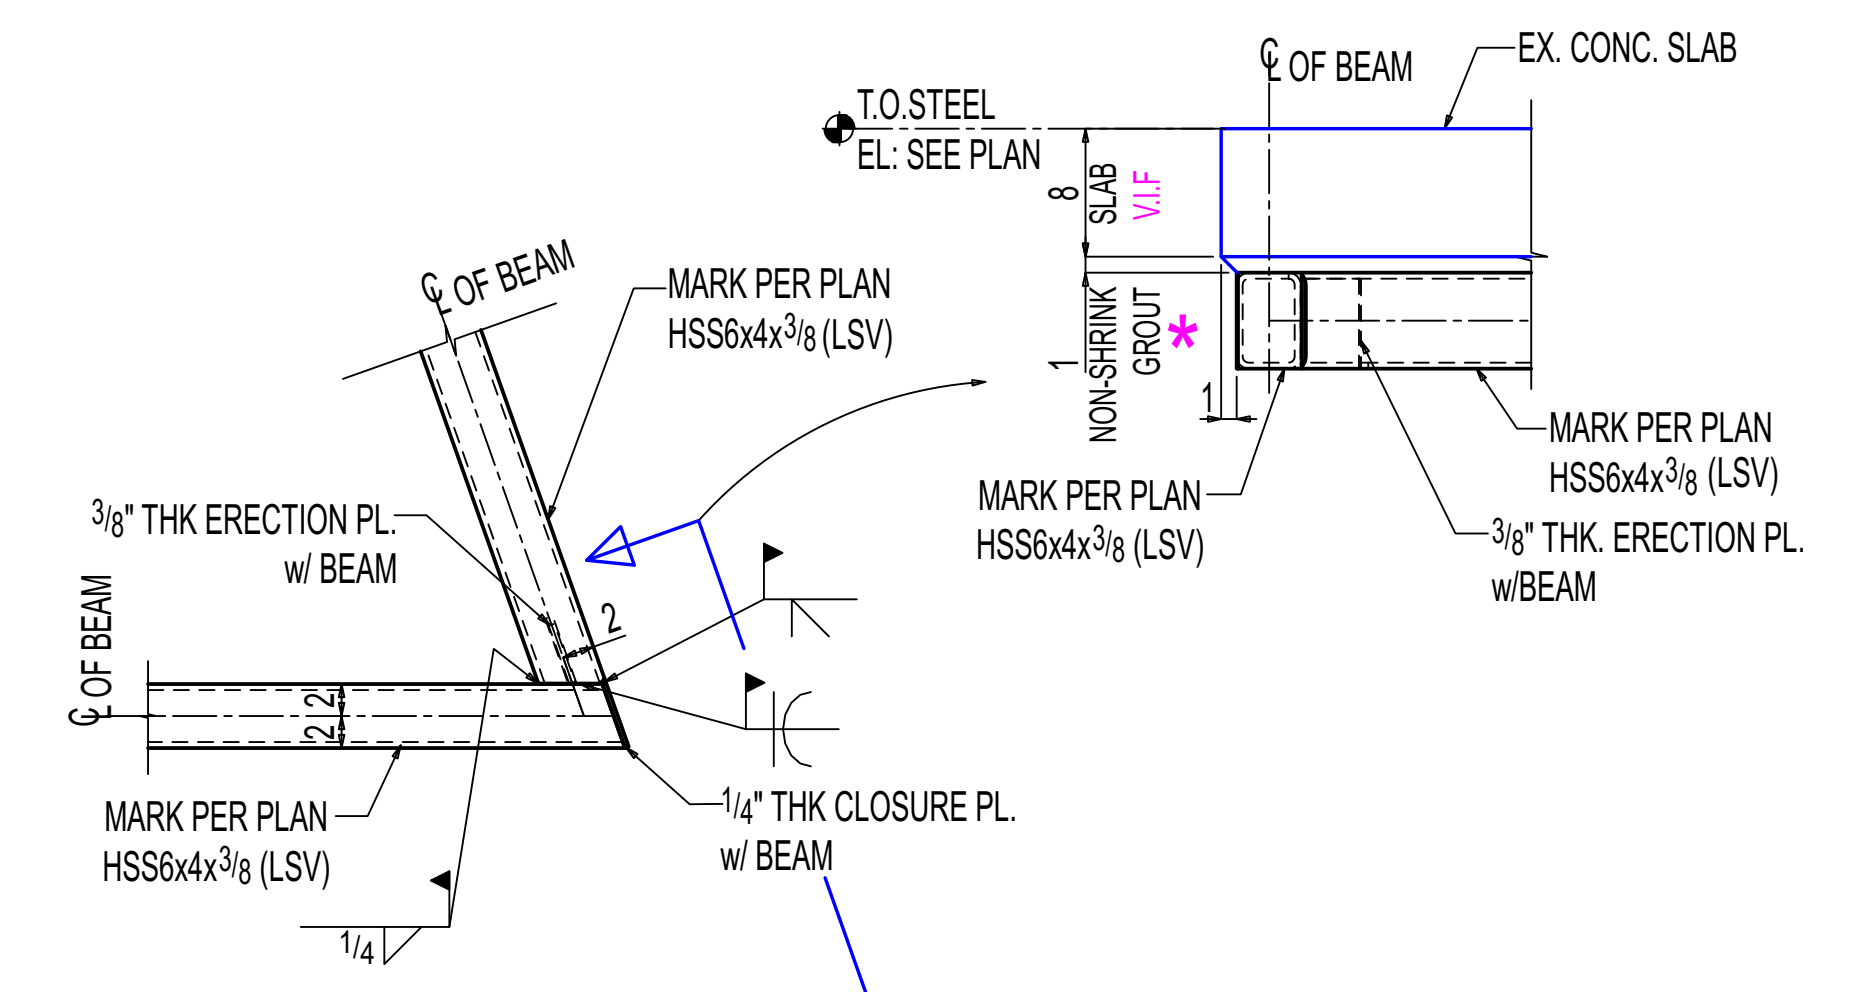

DETAIL-3
E-10.00
OTHERS NOT SHOWN FOR CLARITY

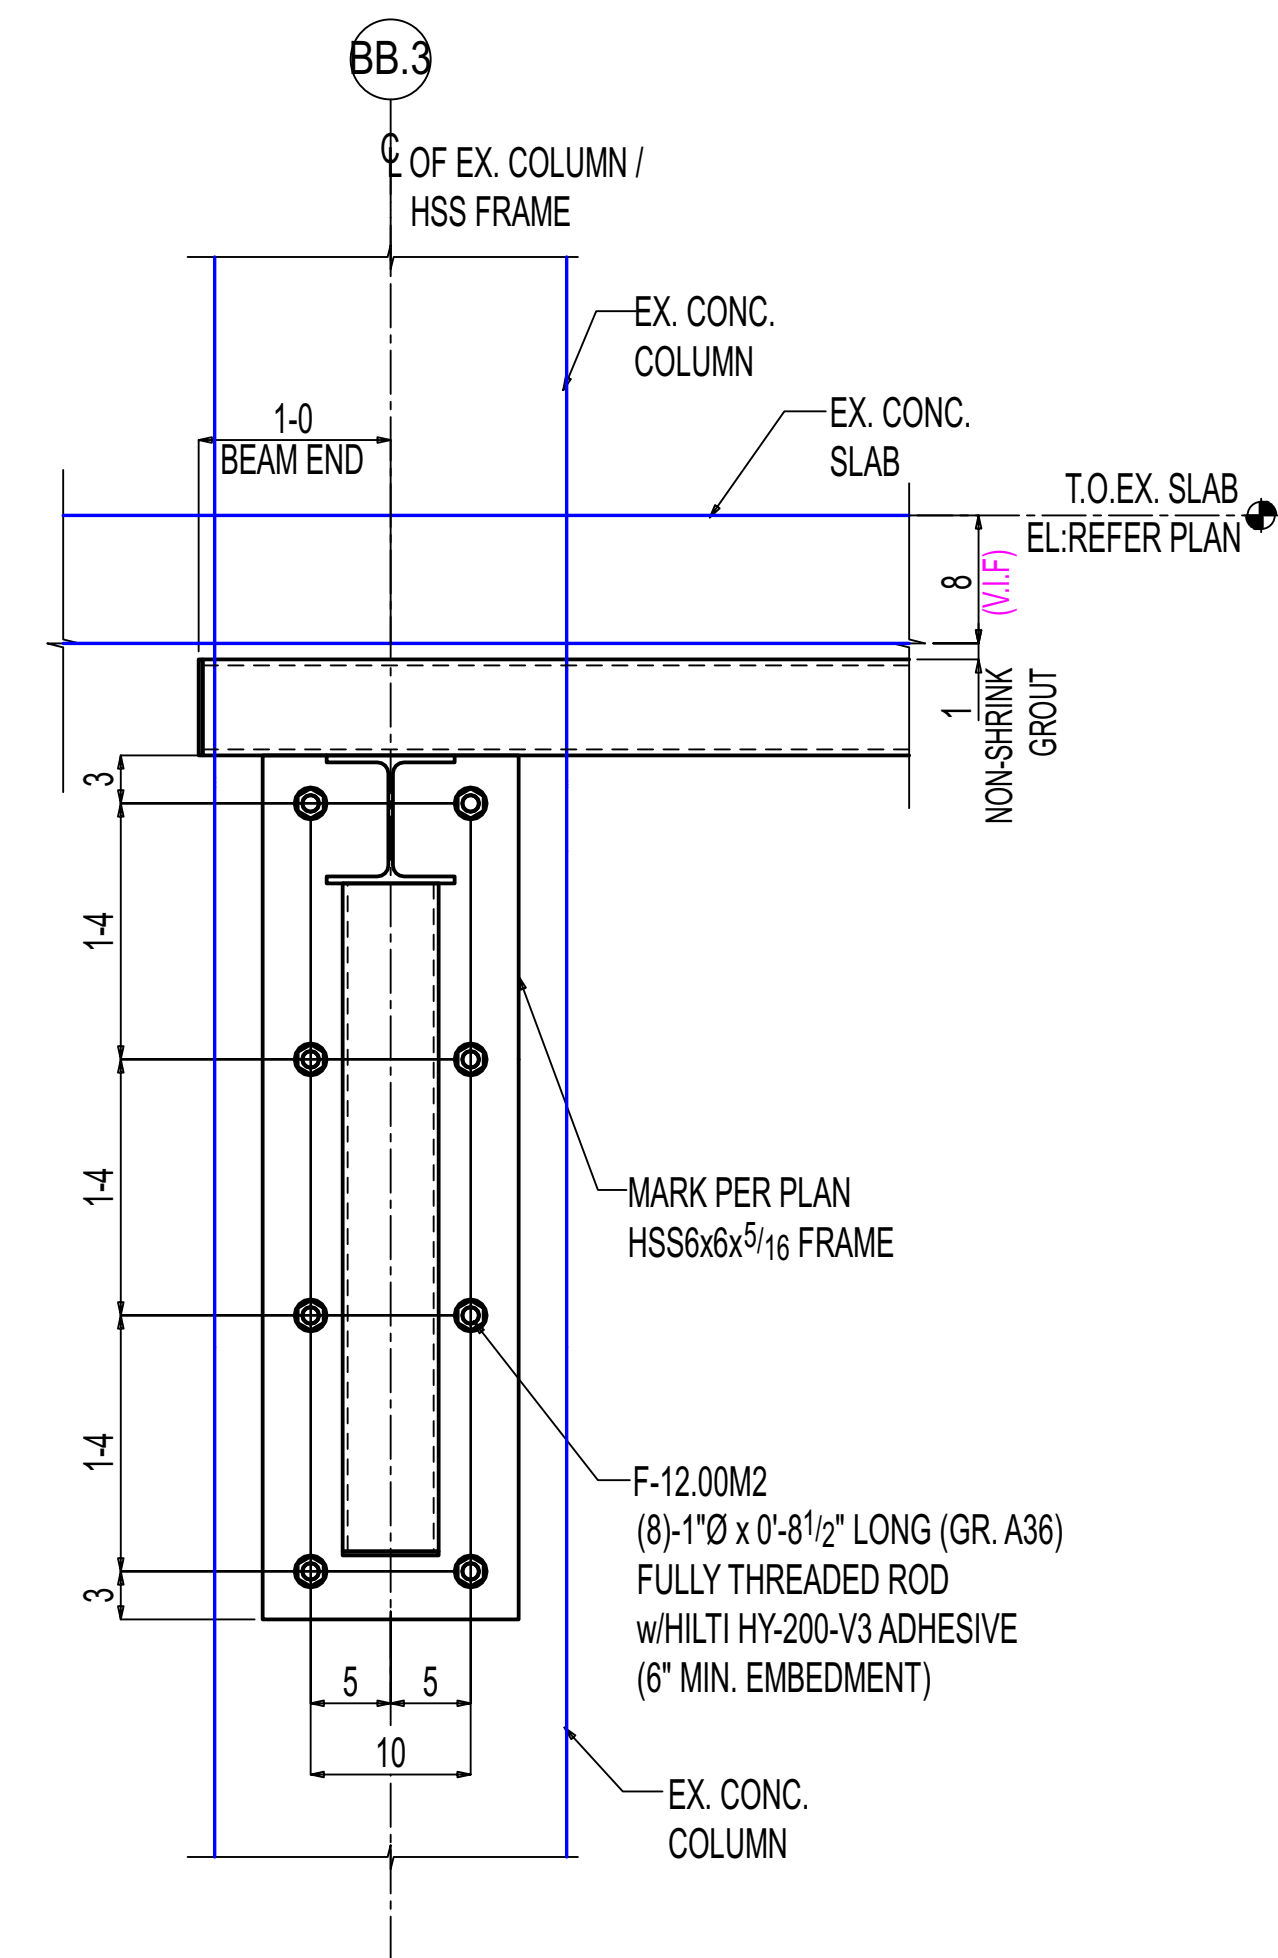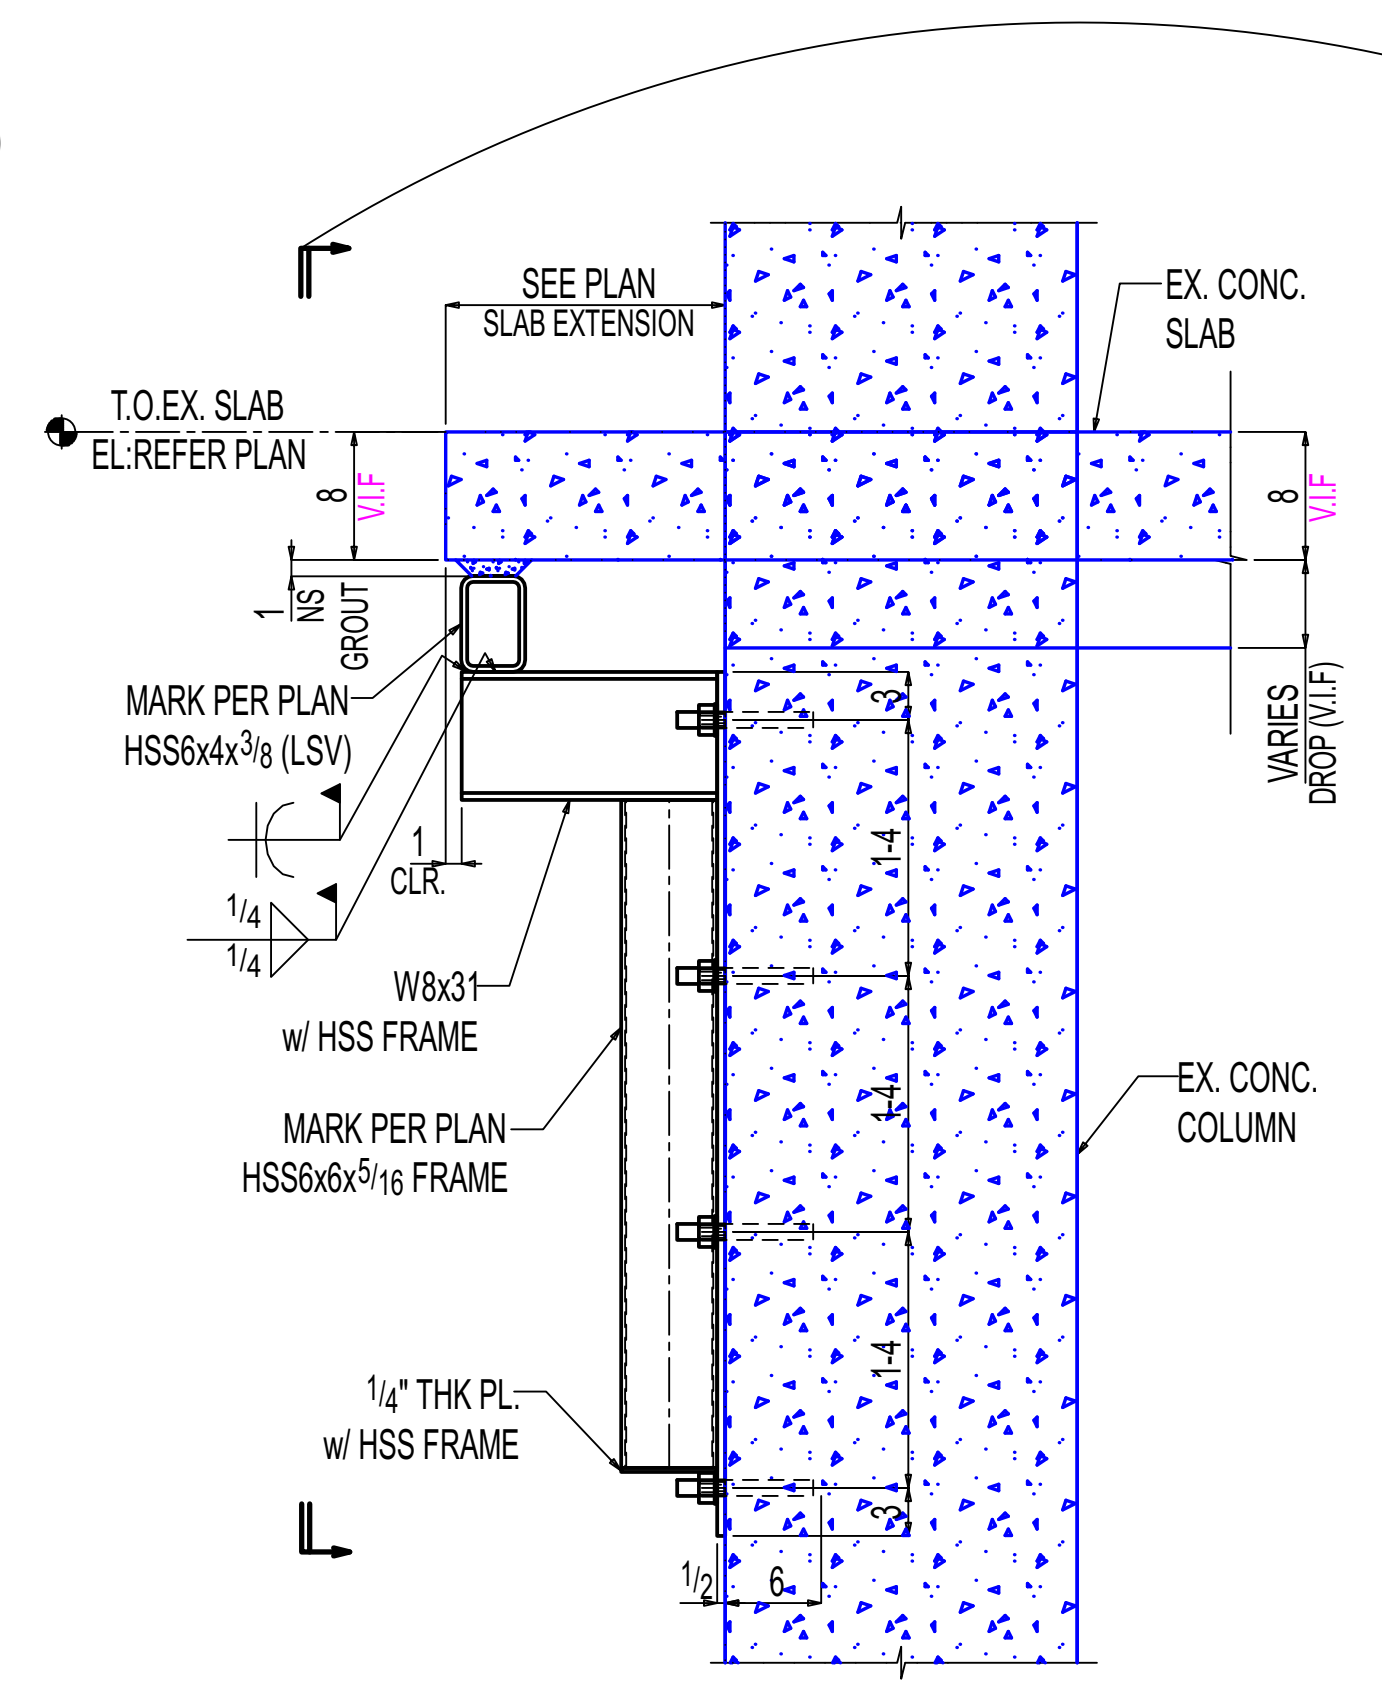

SHOP / ERECTOR NOTE:
LOCATE EXISTING REBAR PRIOR TO FABRICATION OF PLATE. DO NOT DRILL THROUGH REBAR.

General Notes

- *Structural steel shall conform to ASTM-A992.
- *Structural SQR/RND tubing conform to ASTM A500 Grade C.
- *Pipe shall conform to ASTM A53, Grade B.
- *Channels, Angles and plates shall conform to A36.
- *All bolts shall be 3/4" High strength in accordance with ASTM A325 (UNO)
- *Welding Electrodes for Carbon steel :E70xx

# of Copies	Revision/ Issue	Destination	Date
1	0	For Construction	11-14-2025
2	B	For Re-Approval	10-24-2025
1	A	For Approval	09-19-2025

IRON FABRICATION SERVICES, LLC.

3029 M. Street, NW, Suite 202
Washington, DC 20007
Tel: 202-800-5599
Fax: 202-478-0303

Project Name and Address
MARYLAND AVENUE

Location: **1250 MARYLAND AVENUE SW WASHINGTON, DC 20024**

Contractor:
BALFOUR BEATTY

Approved for Fabrication by: _____

Signature _____

Contract # **224009** Drawing # **E-12.04**

Contract Item: **LEVEL-06 SLAB EXTENSION**

Ref: **SOW-12: 3,4,5&6 / S307**

Date **01/20/2025** Drawing Title: **SOW #12 LEVEL-06 NEW SLAB EXTENSION SUPPORT SECTIONS**

Scale **VARIES**