


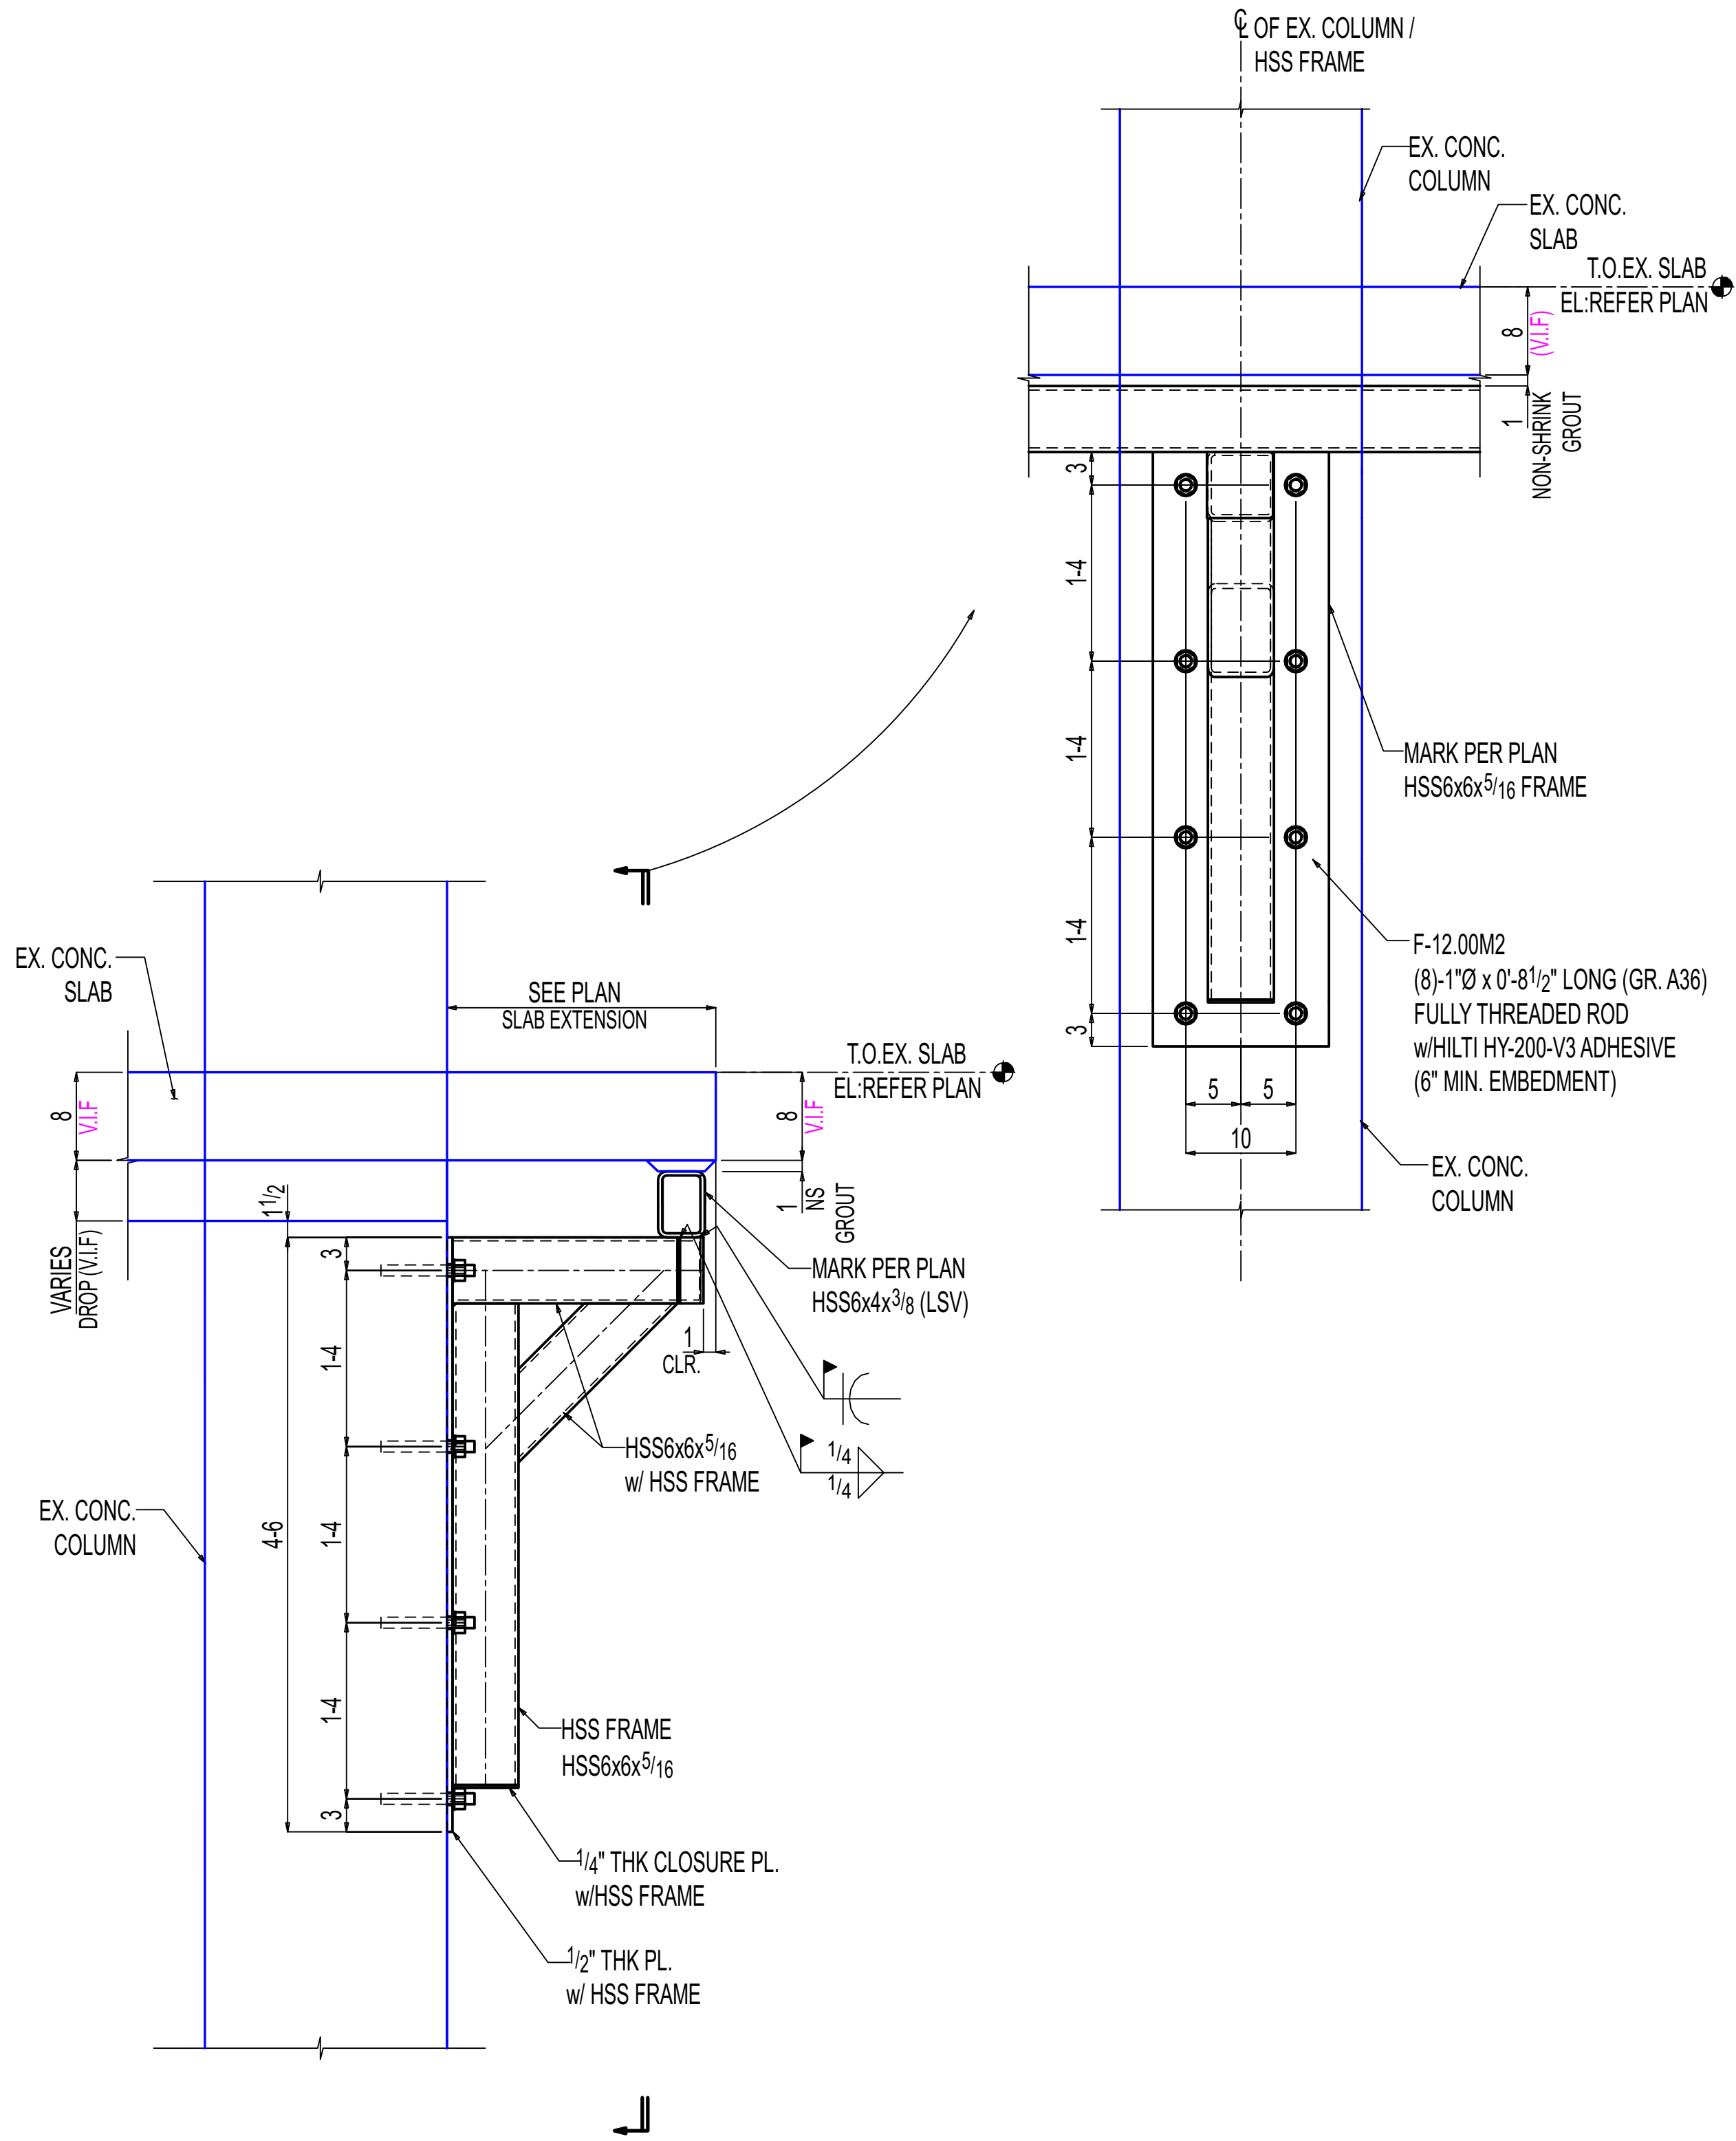

N-N
E-12.00
(REF:10/S315)
OTHERS NOT SHOWN FOR CLARITY

SHOP/ERECTOR NOTE:
LOCATE EXISTING REBAR PRIOR TO FABRICATION OF PLATE.
DO NOT DRILL THROUGH REBAR.

- General Notes
- *Structural steel shall conform to ASTM-A992.
 - *Structural SQR/RND.tubing conform to ASTM A500 Grade C
 - *Pipe shall conform to ASTM A53, Grade B.
 - *Channels, Angles and plates shall conform to A36.
 - *All bolts shall be 3/4" High strength in accordance with ASTM A325 (UNO)
 - *Welding Electrodes for Carbon steel :E70xx

1	0	For Construction	11-14-2025
# of Copies	Revision/ Issue	Destination	Date

IRON FABRICATION SERVICES, LLC.

3029 M. Street, NW, Suite 202
Washington, DC 20007
Tel: 202-800-5599
Fax: 202-478-0303

Project Name and Address

MARYLAND AVENUE
Location: **1250 MARYLAND AVENUE SW**
WASHINGTON, DC 20024

Contractor:

BALFOUR BEATTY

Approved for Fabrication by:	Signature

Contract #	224009	Drawing #	E-12.05
Contract Item:	LEVEL-06 SLAB EXTENSION		
Ref:	SOW-12: 3,4,5&6 / S307		
Date	Drawing Title:		
01/20/2025	SOW #12 LEVEL-06 NEW SLAB EXTENSION SUPPORT SECTIONS		
Scale			
VARIES			