
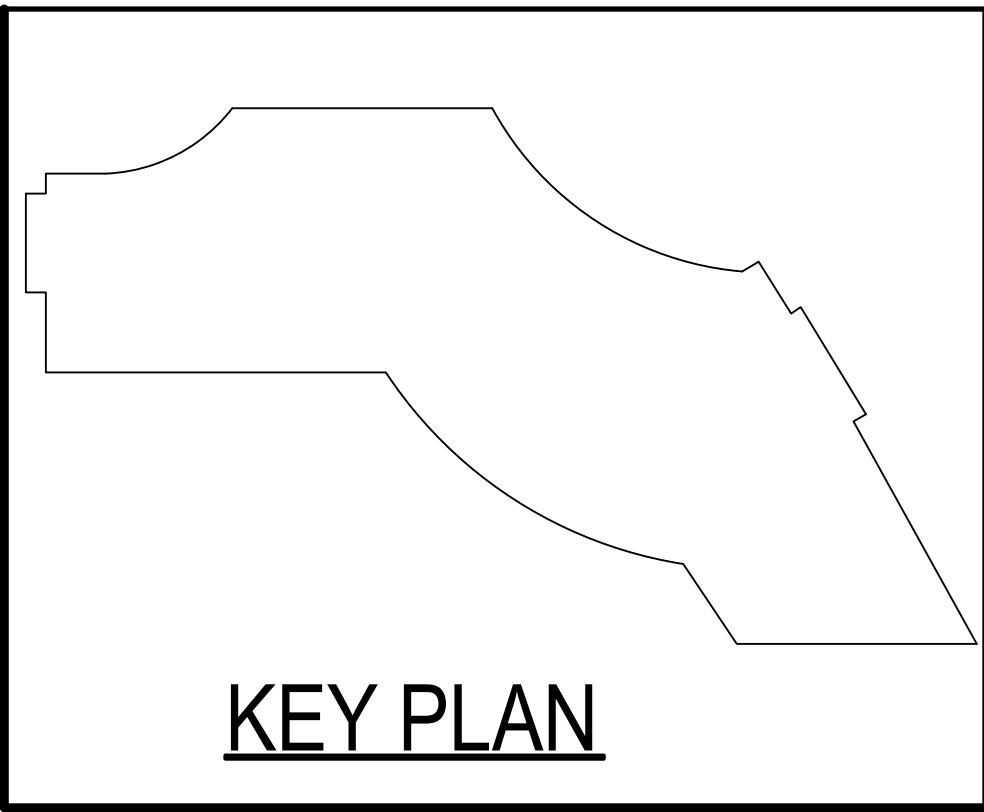


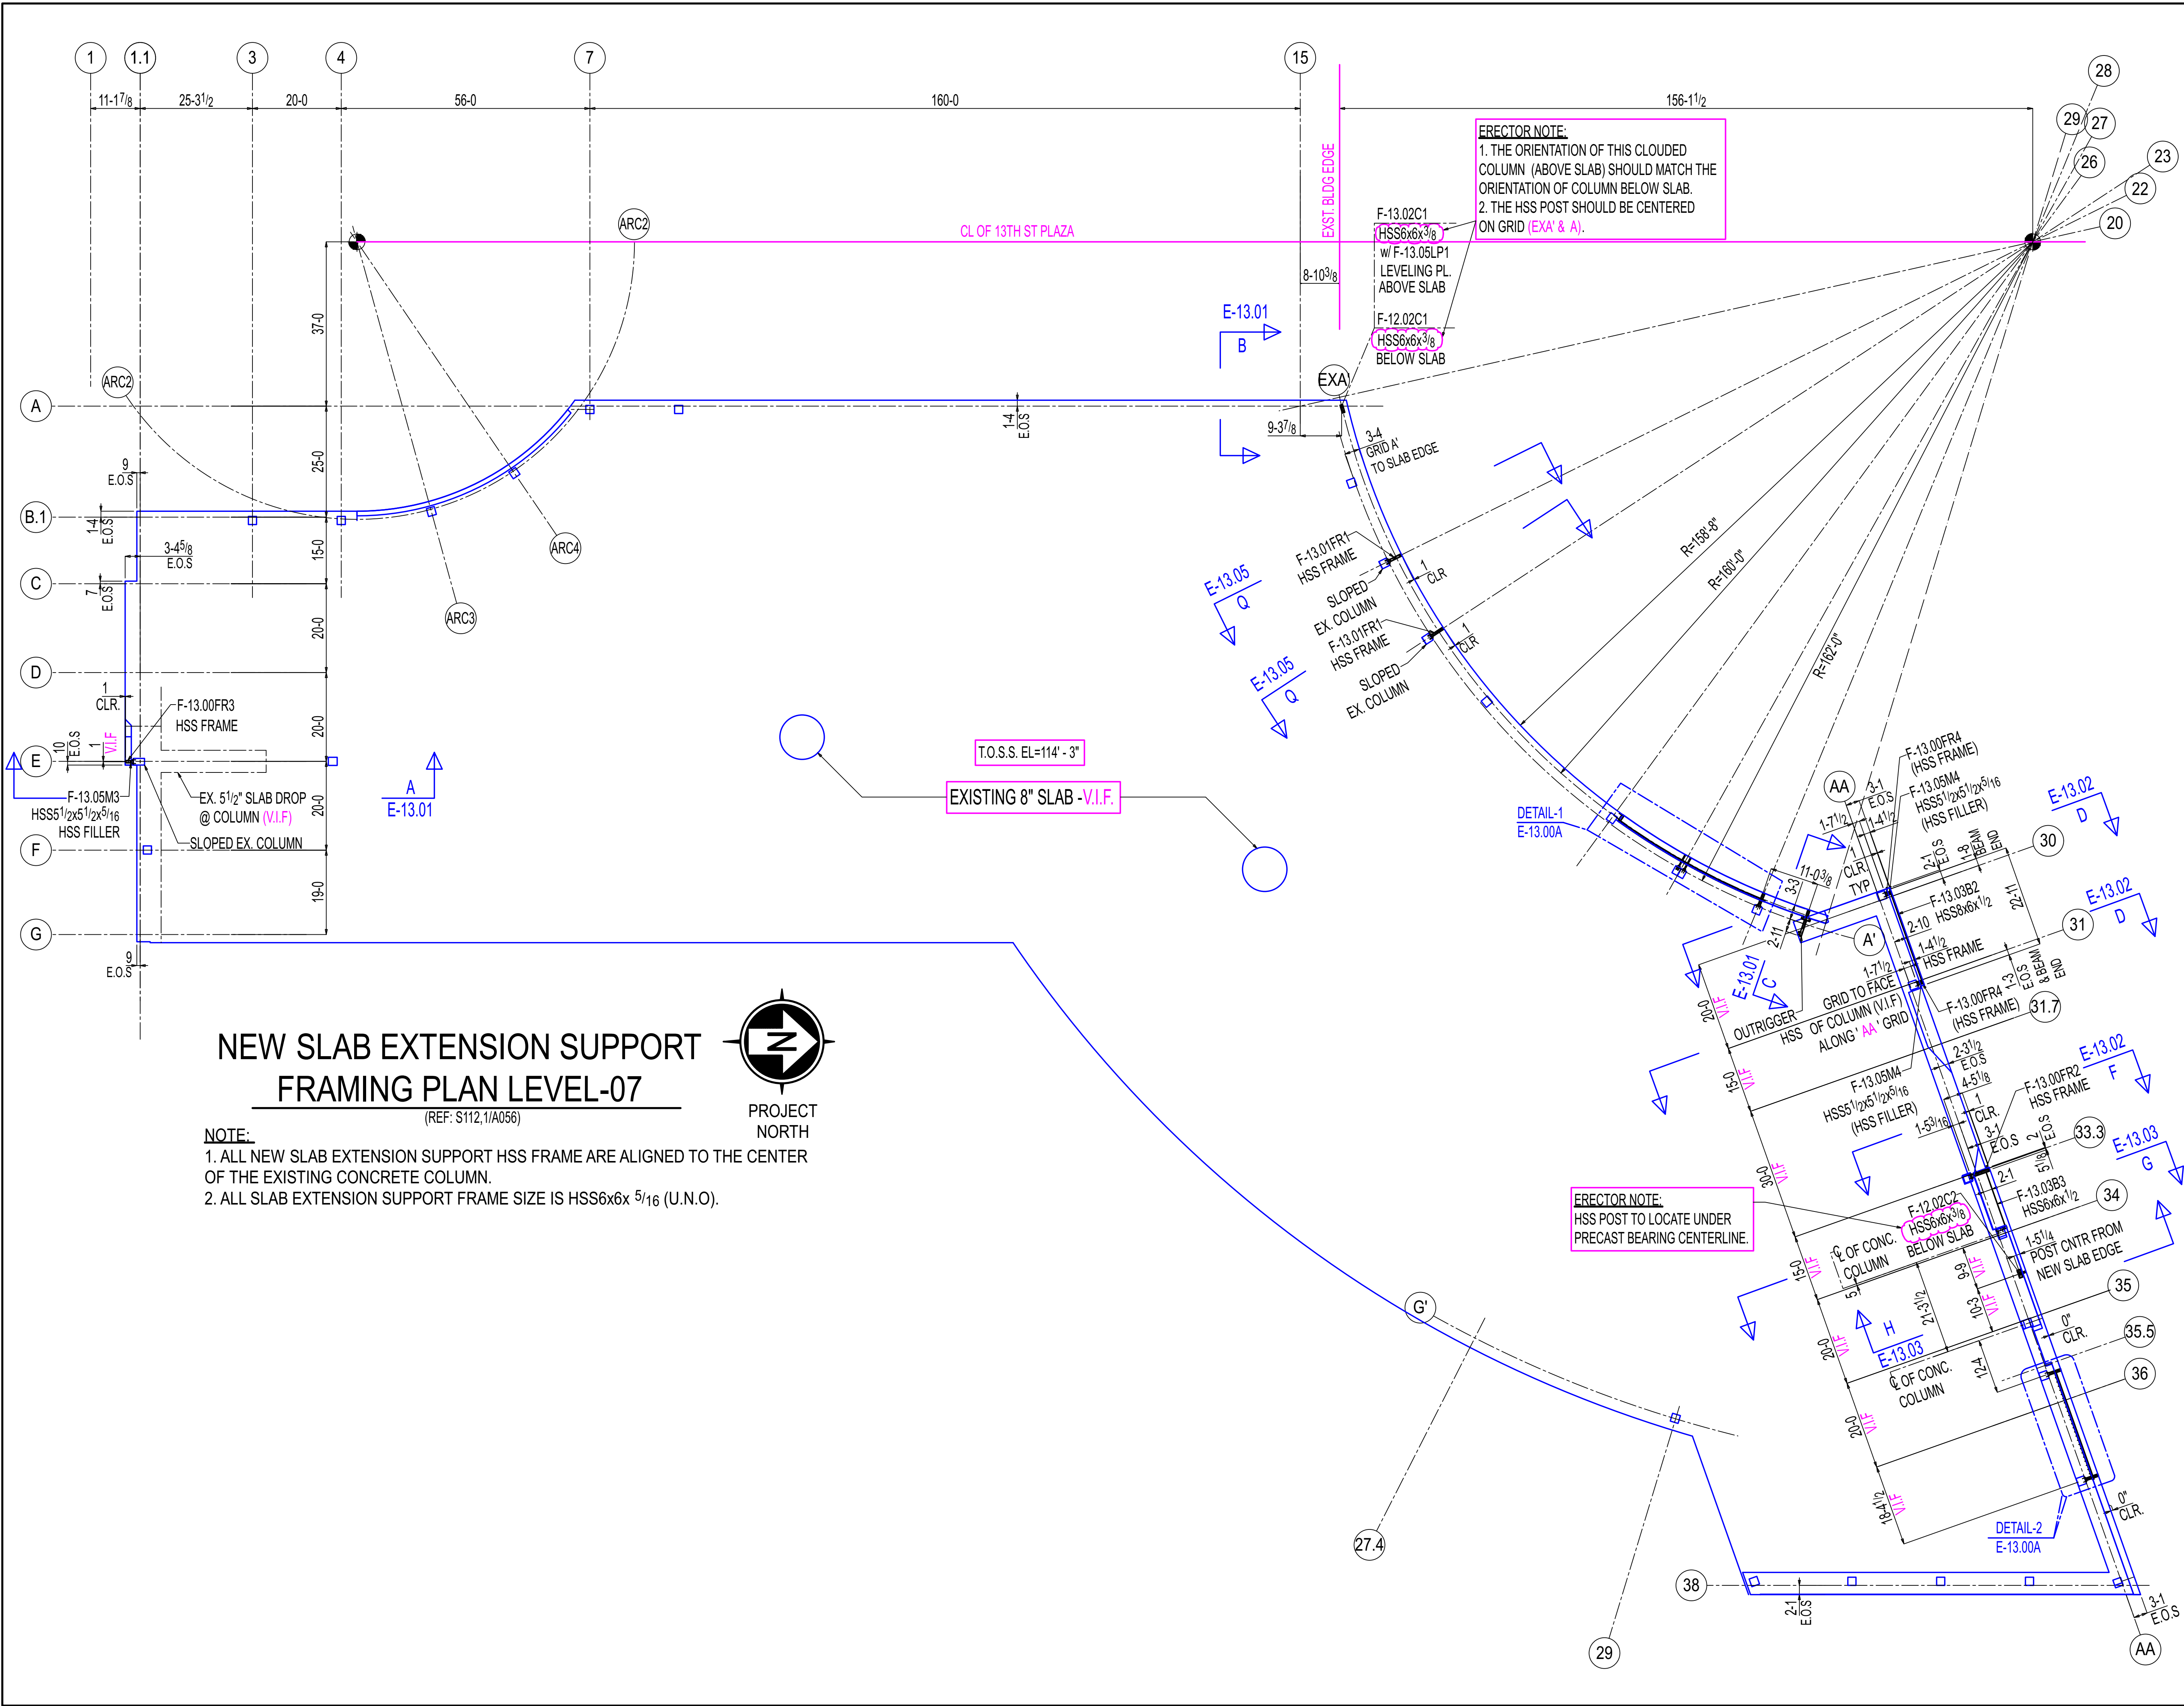

General Notes

- *Structural steel shall conform to ASTM-A992.
- *Structural SQR/RND.tubing conform to ASTM A500 Grade C
- *Pipe shall conform to ASTM A53, Grade B.
- *Channels, Angles and plates shall conform to A36.
- *All bolts shall be 3/4" High strength in accordance with ASTM A325 (UNO)
- *Welding Electrodes for Carbon steel :E70xx

# of Copies	Revision/ Issue	Destination	Date
5	0	For Construction	11-17-2025
4	D	For Re-Approval	10-24-2025
3	C	For Re-Approval	09-19-2025
2	B	For Re-Approval	06-23-2025
1	A	For Approval	02-25-2025

IRON FABRICATION SERVICES, LLC.

3029 M. Street, NW, Suite 202
Washington, DC 20007
Tel: 202-800-5599
Fax: 202-478-0303

Project Name and Address
MARYLAND AVENUE
Location: **1250 MARYLAND AVENUE SW
WASHINGTON, DC 20024**

Contractor:
BALFOUR BEATTY



Approved for Fabrication by: Signature

Contract # **224009** Drawing # **E-13.00**

Contract Item: **LEVEL-07
SLAB EXTENSION**

Ref: **SOW-13: (S112,1/A056)**

Date **01/20/2025** Drawing Title: **SOW #13 LEVEL-07 NEW
SLAB EXTENSION SUPPORT
FRAMING PLAN**
Scale **VARIES**

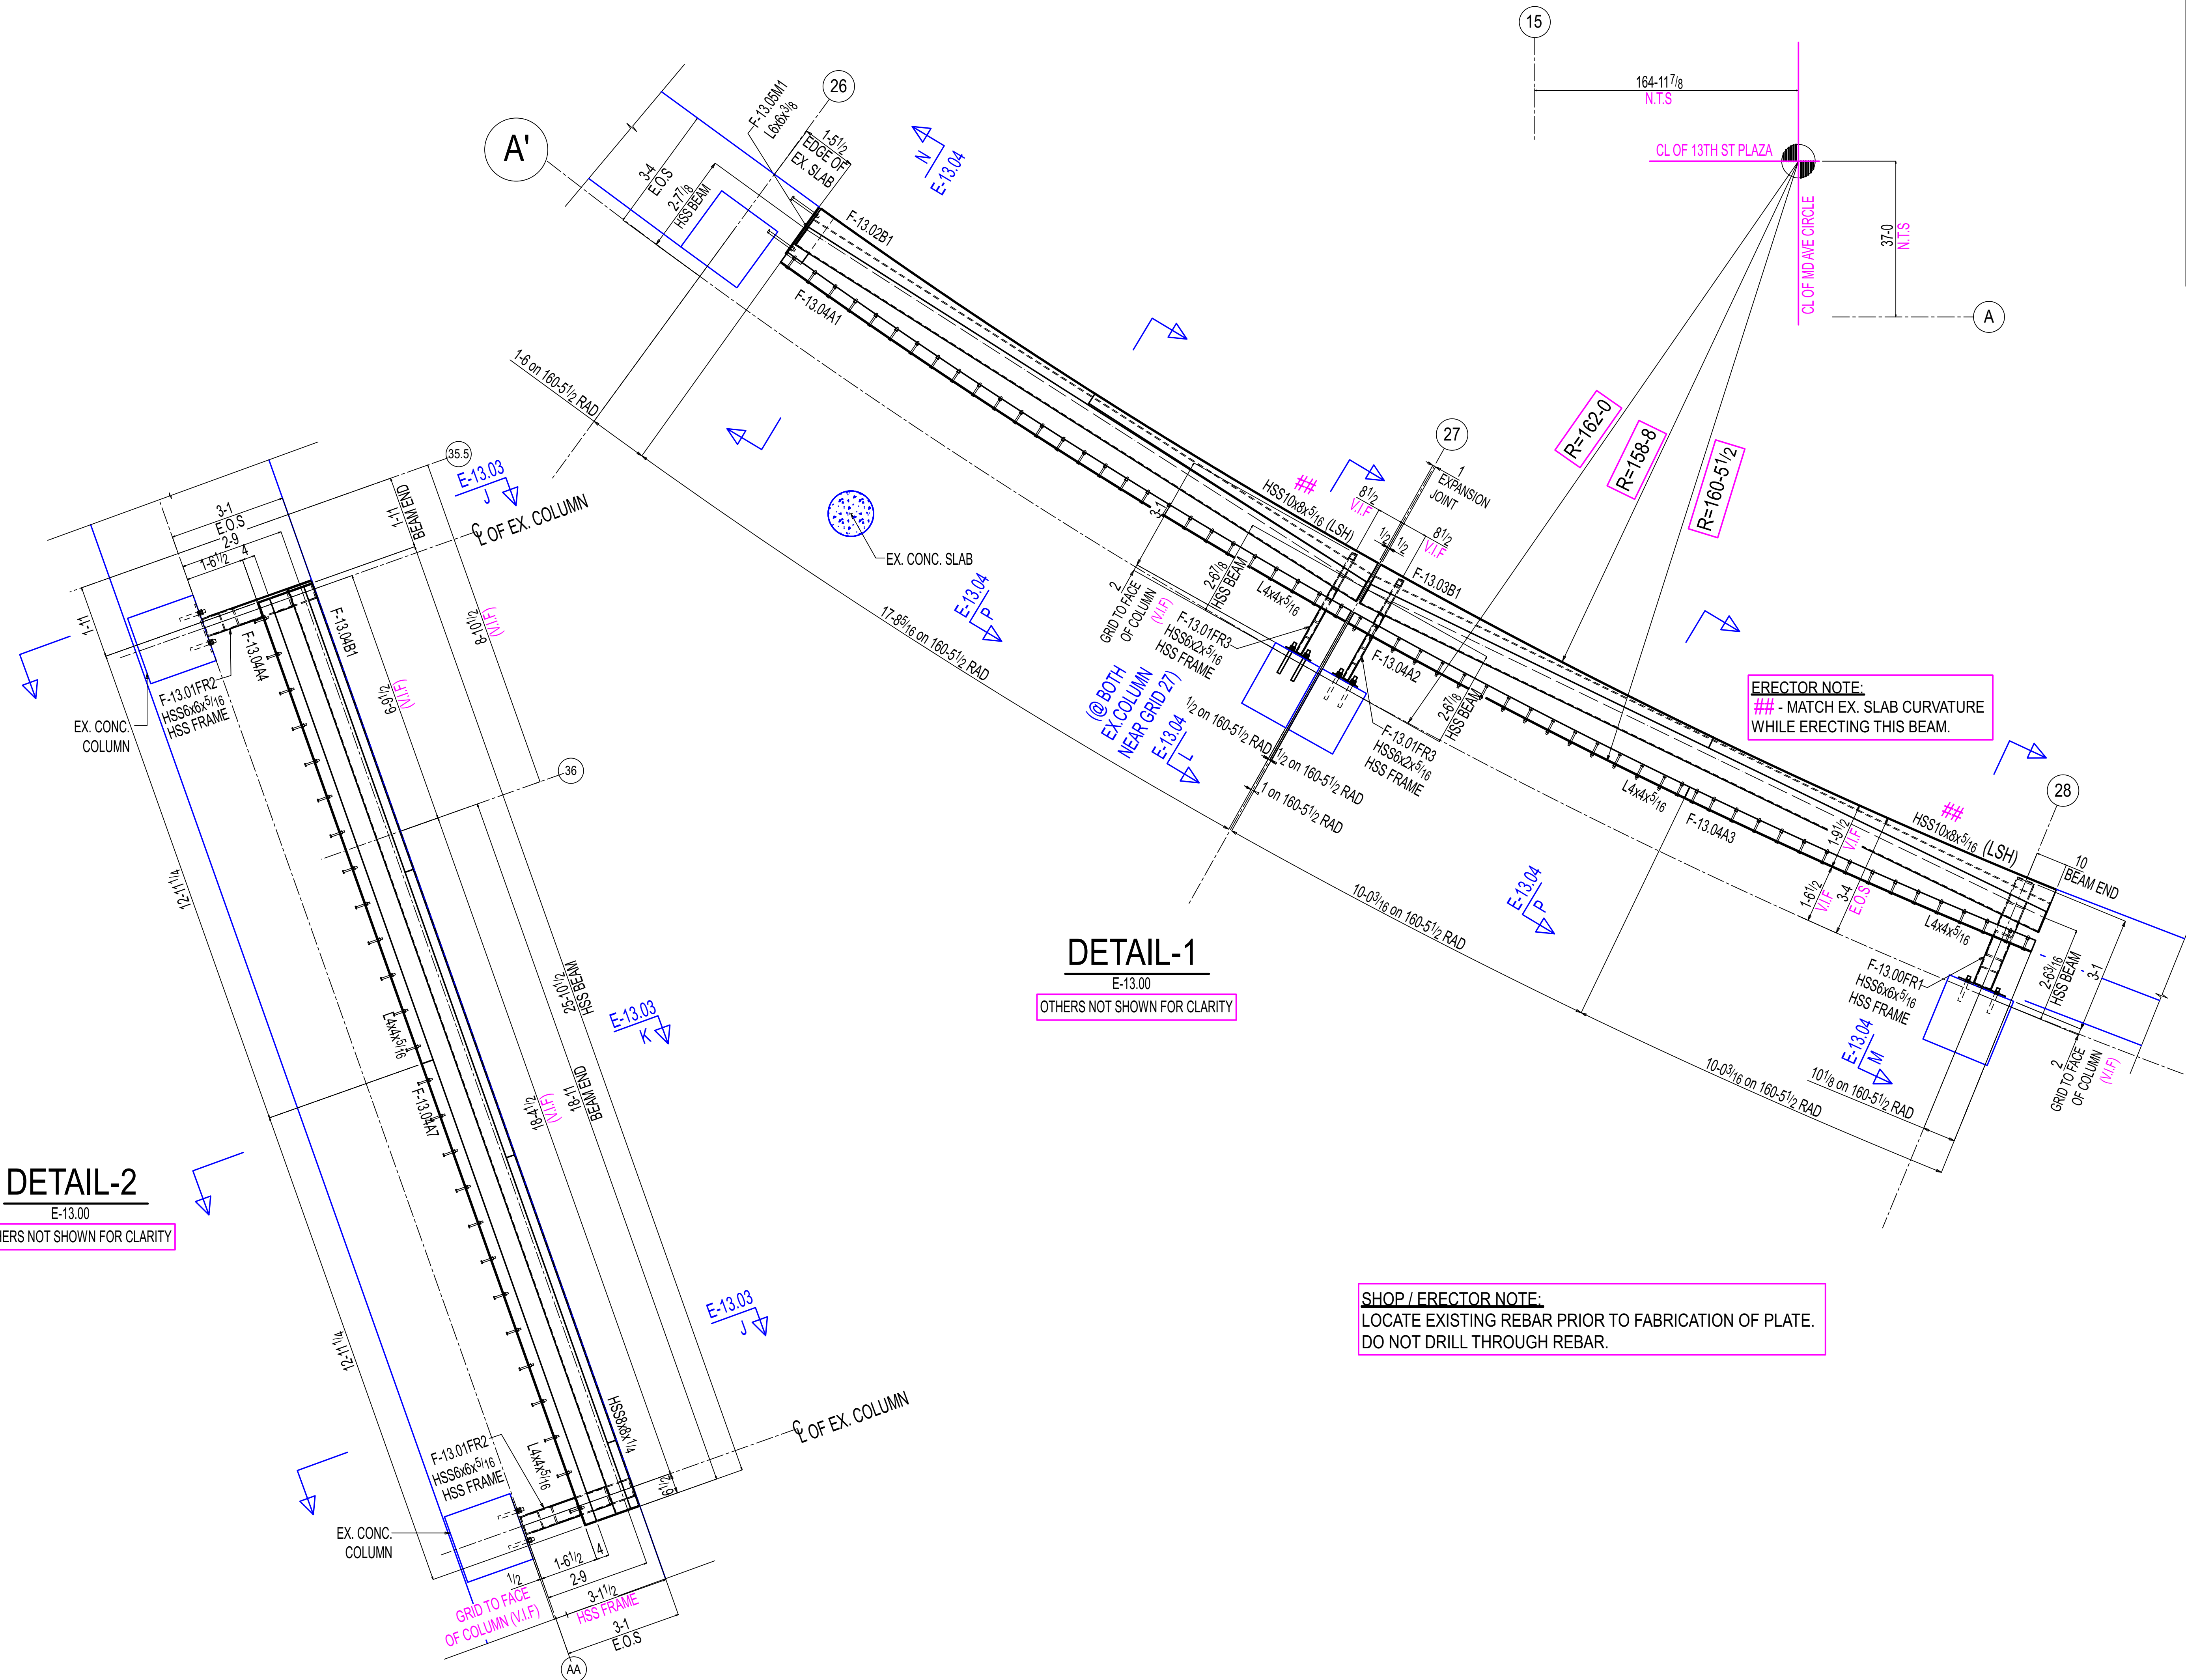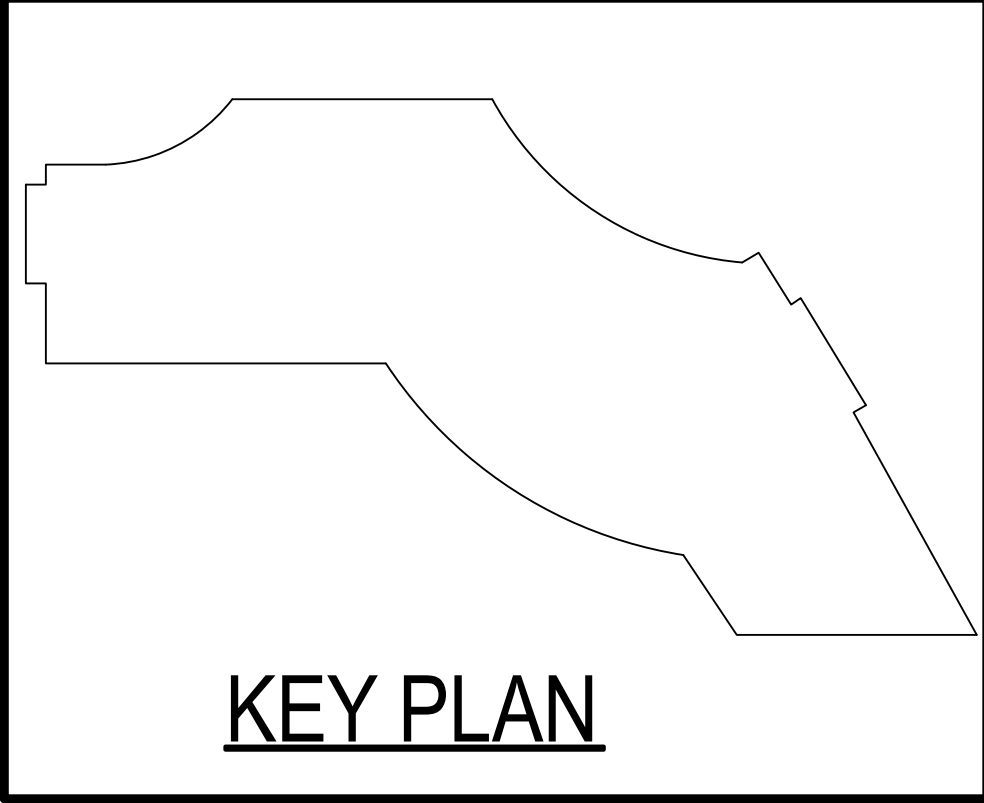

DETAIL-2
E-13.00
OTHERS NOT SHOWN FOR CLARITY

DETAIL-1
E-13.00
OTHERS NOT SHOWN FOR CLARITY

SHOP / ERECTOR NOTE:
LOCATE EXISTING REBAR PRIOR TO FABRICATION OF PLATE.
DO NOT DRILL THROUGH REBAR.

General Notes			
*Structural steel shall conform to ASTM-A992.			
*Structural SQR/RND.tubing conform to ASTM A500 Grade C			
*Pipe shall conform to ASTM A53, Grade B.			
*Channels, Angles and plates shall conform to A36.			
*All bolts shall be 3/4" High strength in accordance with ASTM A325 (UNO)			
*Welding Electrodes for Carbon steel :E70xx			
# of Copies	Revision/ Issue	Destination	Date
3	0	For Construction	11-17-2025
2	B	For Re-Approval	10-24-2025
1	A	For Approval	09-19-2025

IRON FABRICATION SERVICES, LLC.

3029 M. Street, NW, Suite 202
Washington, DC 20007
Tel: 202-800-5599
Fax: 202-478-0303



Project Name and Address
MARYLAND AVENUE

Location: **1250 MARYLAND AVENUE SW
WASHINGTON, DC 20024**

Contractor:
BALFOUR BEATTY

Approved for Fabrication by: _____
Signature

Contract #	224009	Drawing #	E-13.00A
Contract Item:	LEVEL-07 SLAB EXTENSION		
Ref:	SOW-13: (S112,1/A056)		
Date	01/20/2025	Drawing Title:	SOW #13 LEVEL-07 NEW SLAB EXTENSION SUPPORT FRAMING PLAN
Scale	VARIES		

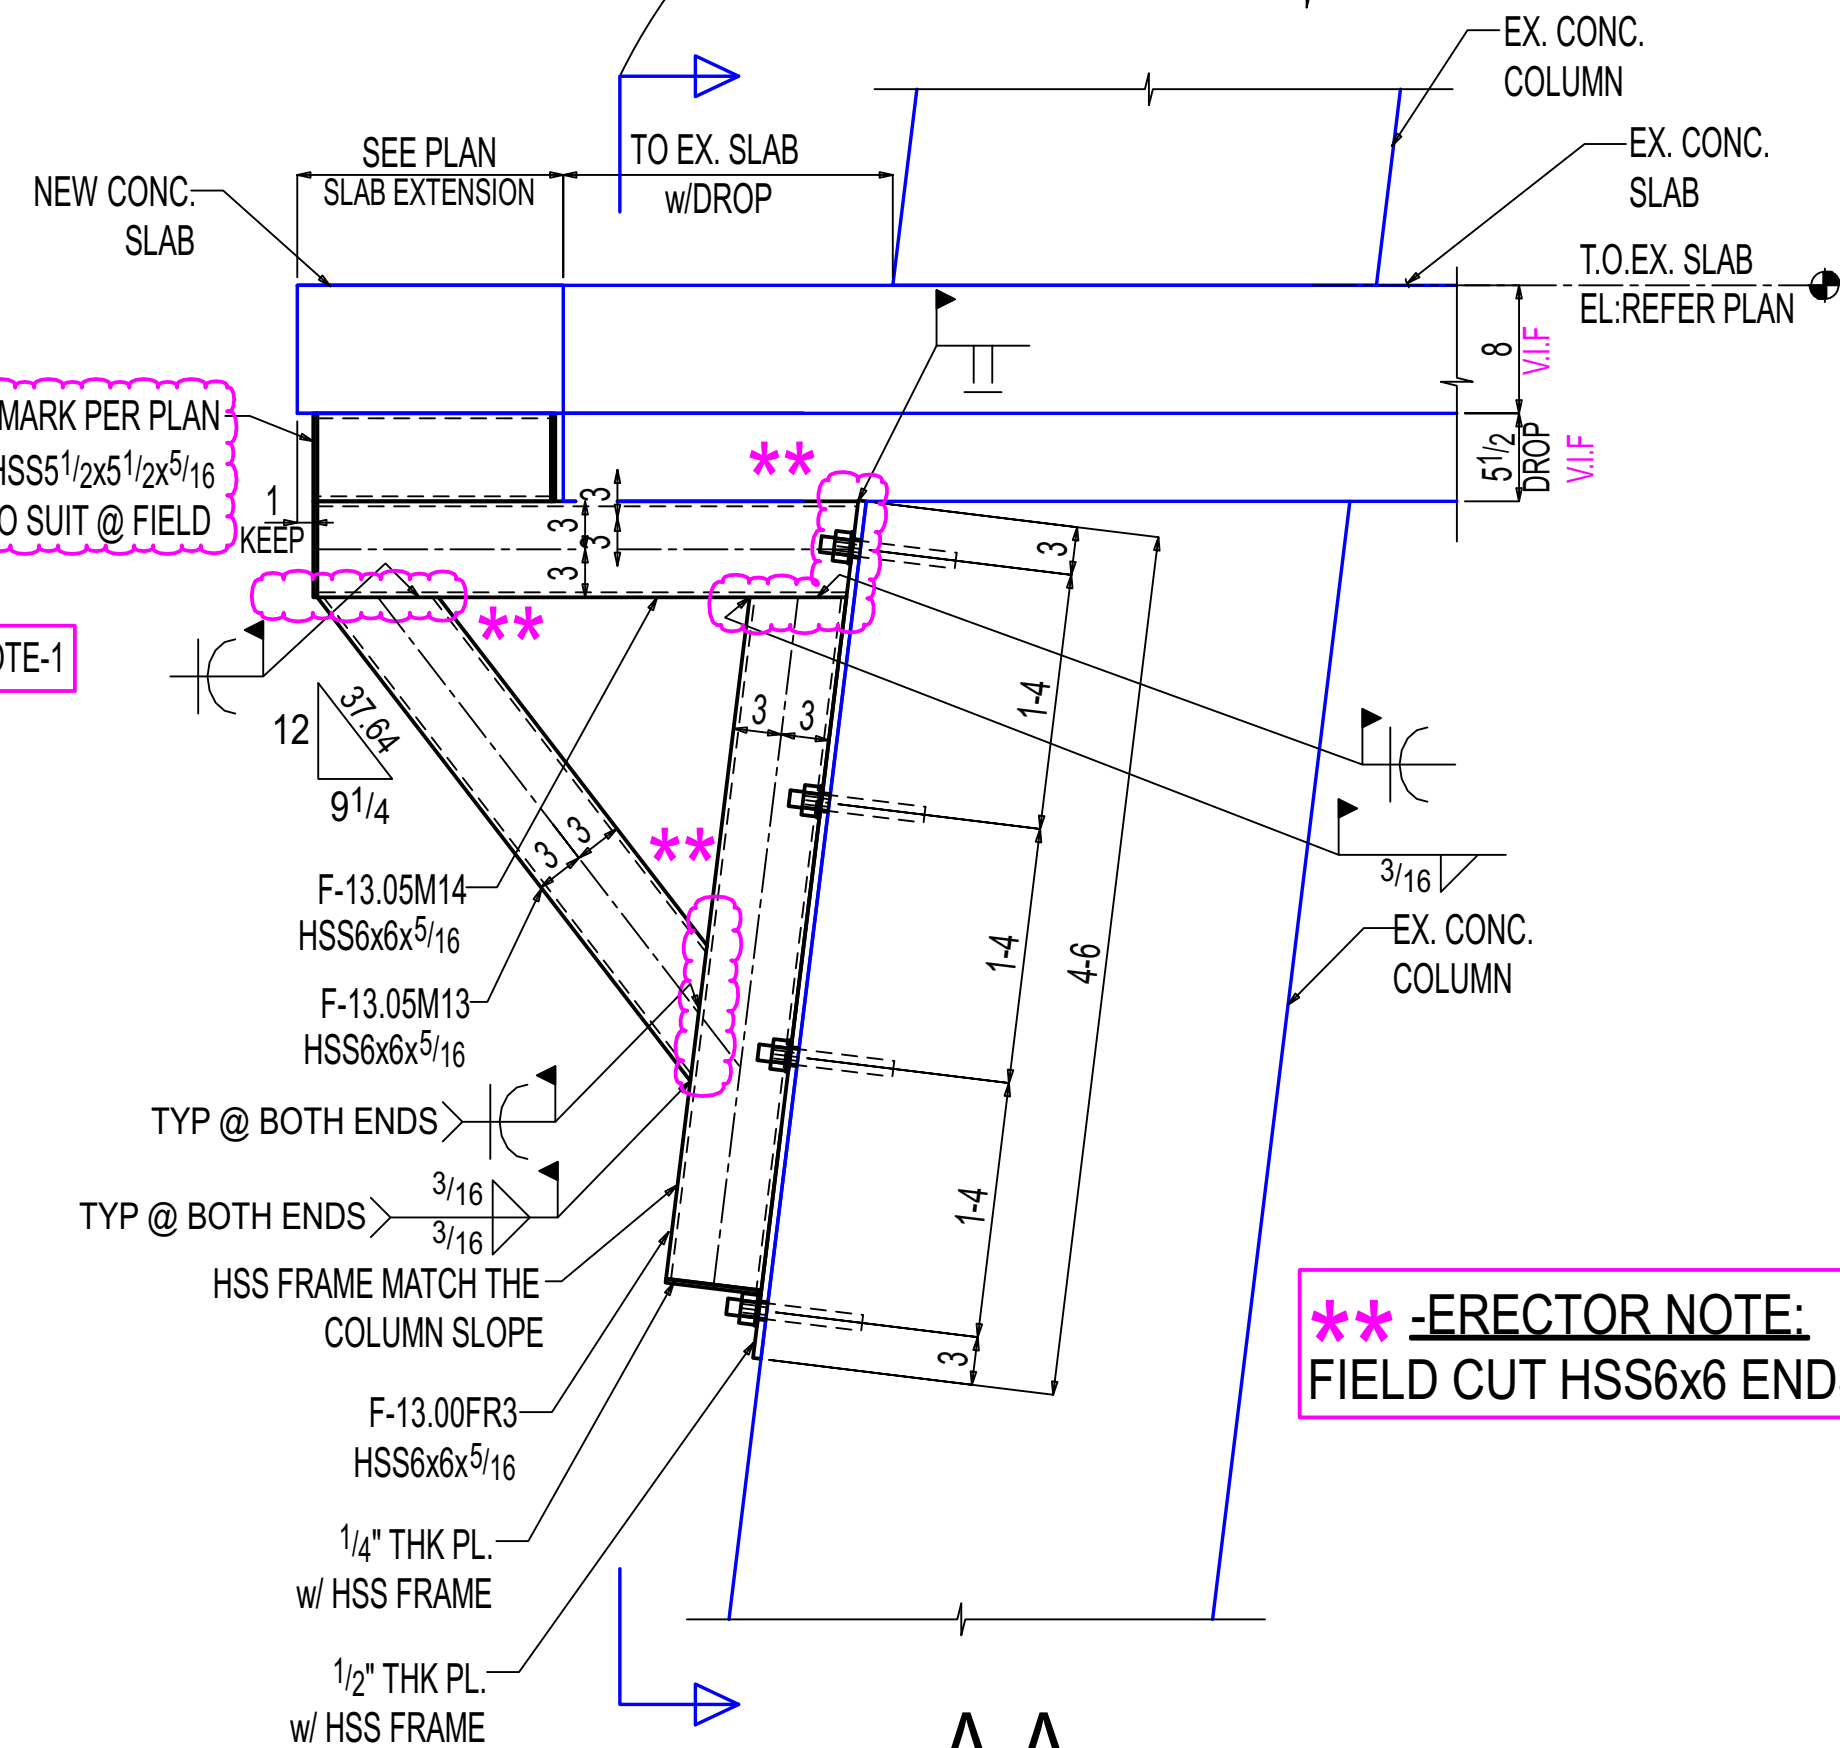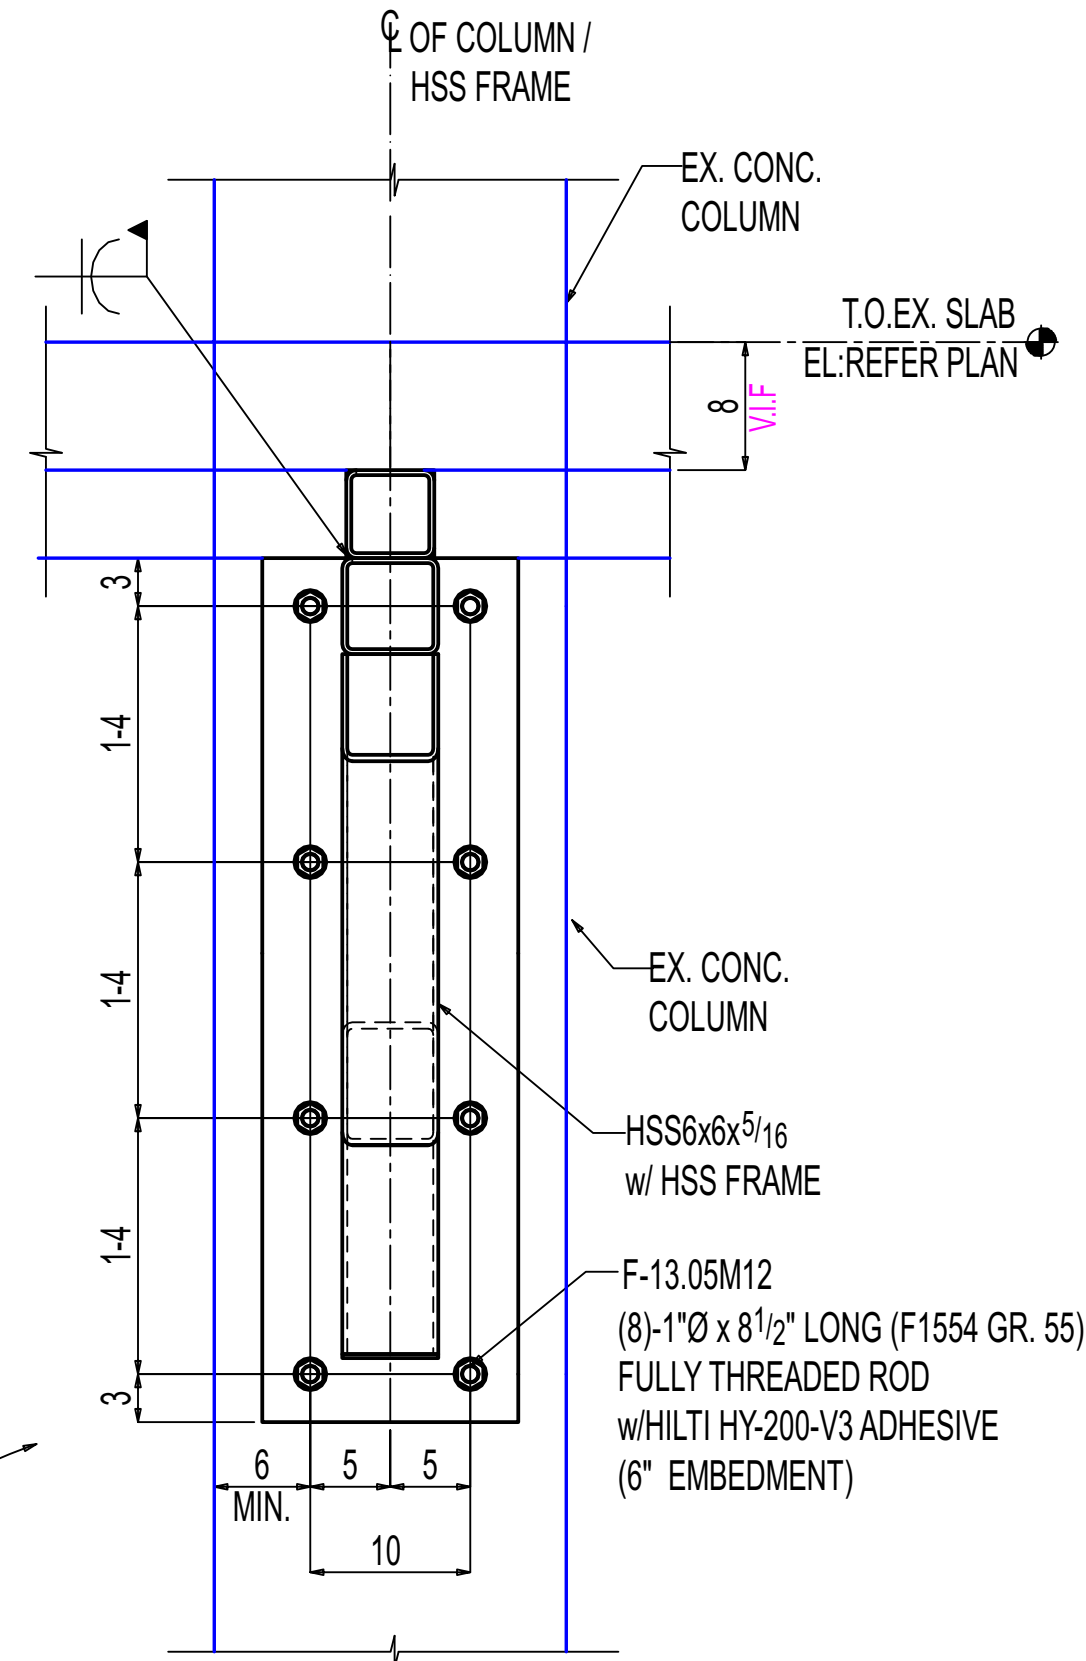

A-A


E-13.00
(REF: 9/S315)

OTHERS NOT SHOWN FOR CLARITY

**** -ERECTOR NOTE:**
FIELD CUT HSS6x6 ENDS TO SUIT AT EXISTING COLUMN SLOPE.

SHOP / ERECTOR NOTE:
LOCATE EXISTING REBAR PRIOR TO FABRICATION OF PLATE.
DO NOT DRILL THROUGH REBAR.


ERECTOR NOTE-1:
ADJUST HSS FILLER DEPTH IN FIELD BY CUT THE HSS FILLER TO MATCH
EXISTING SLAB DROP THICKNESS, AND WELD TO THE
TOP OF HSS FRAME AT SITE PRIOR TO ERECTING THE HSS FRAME.

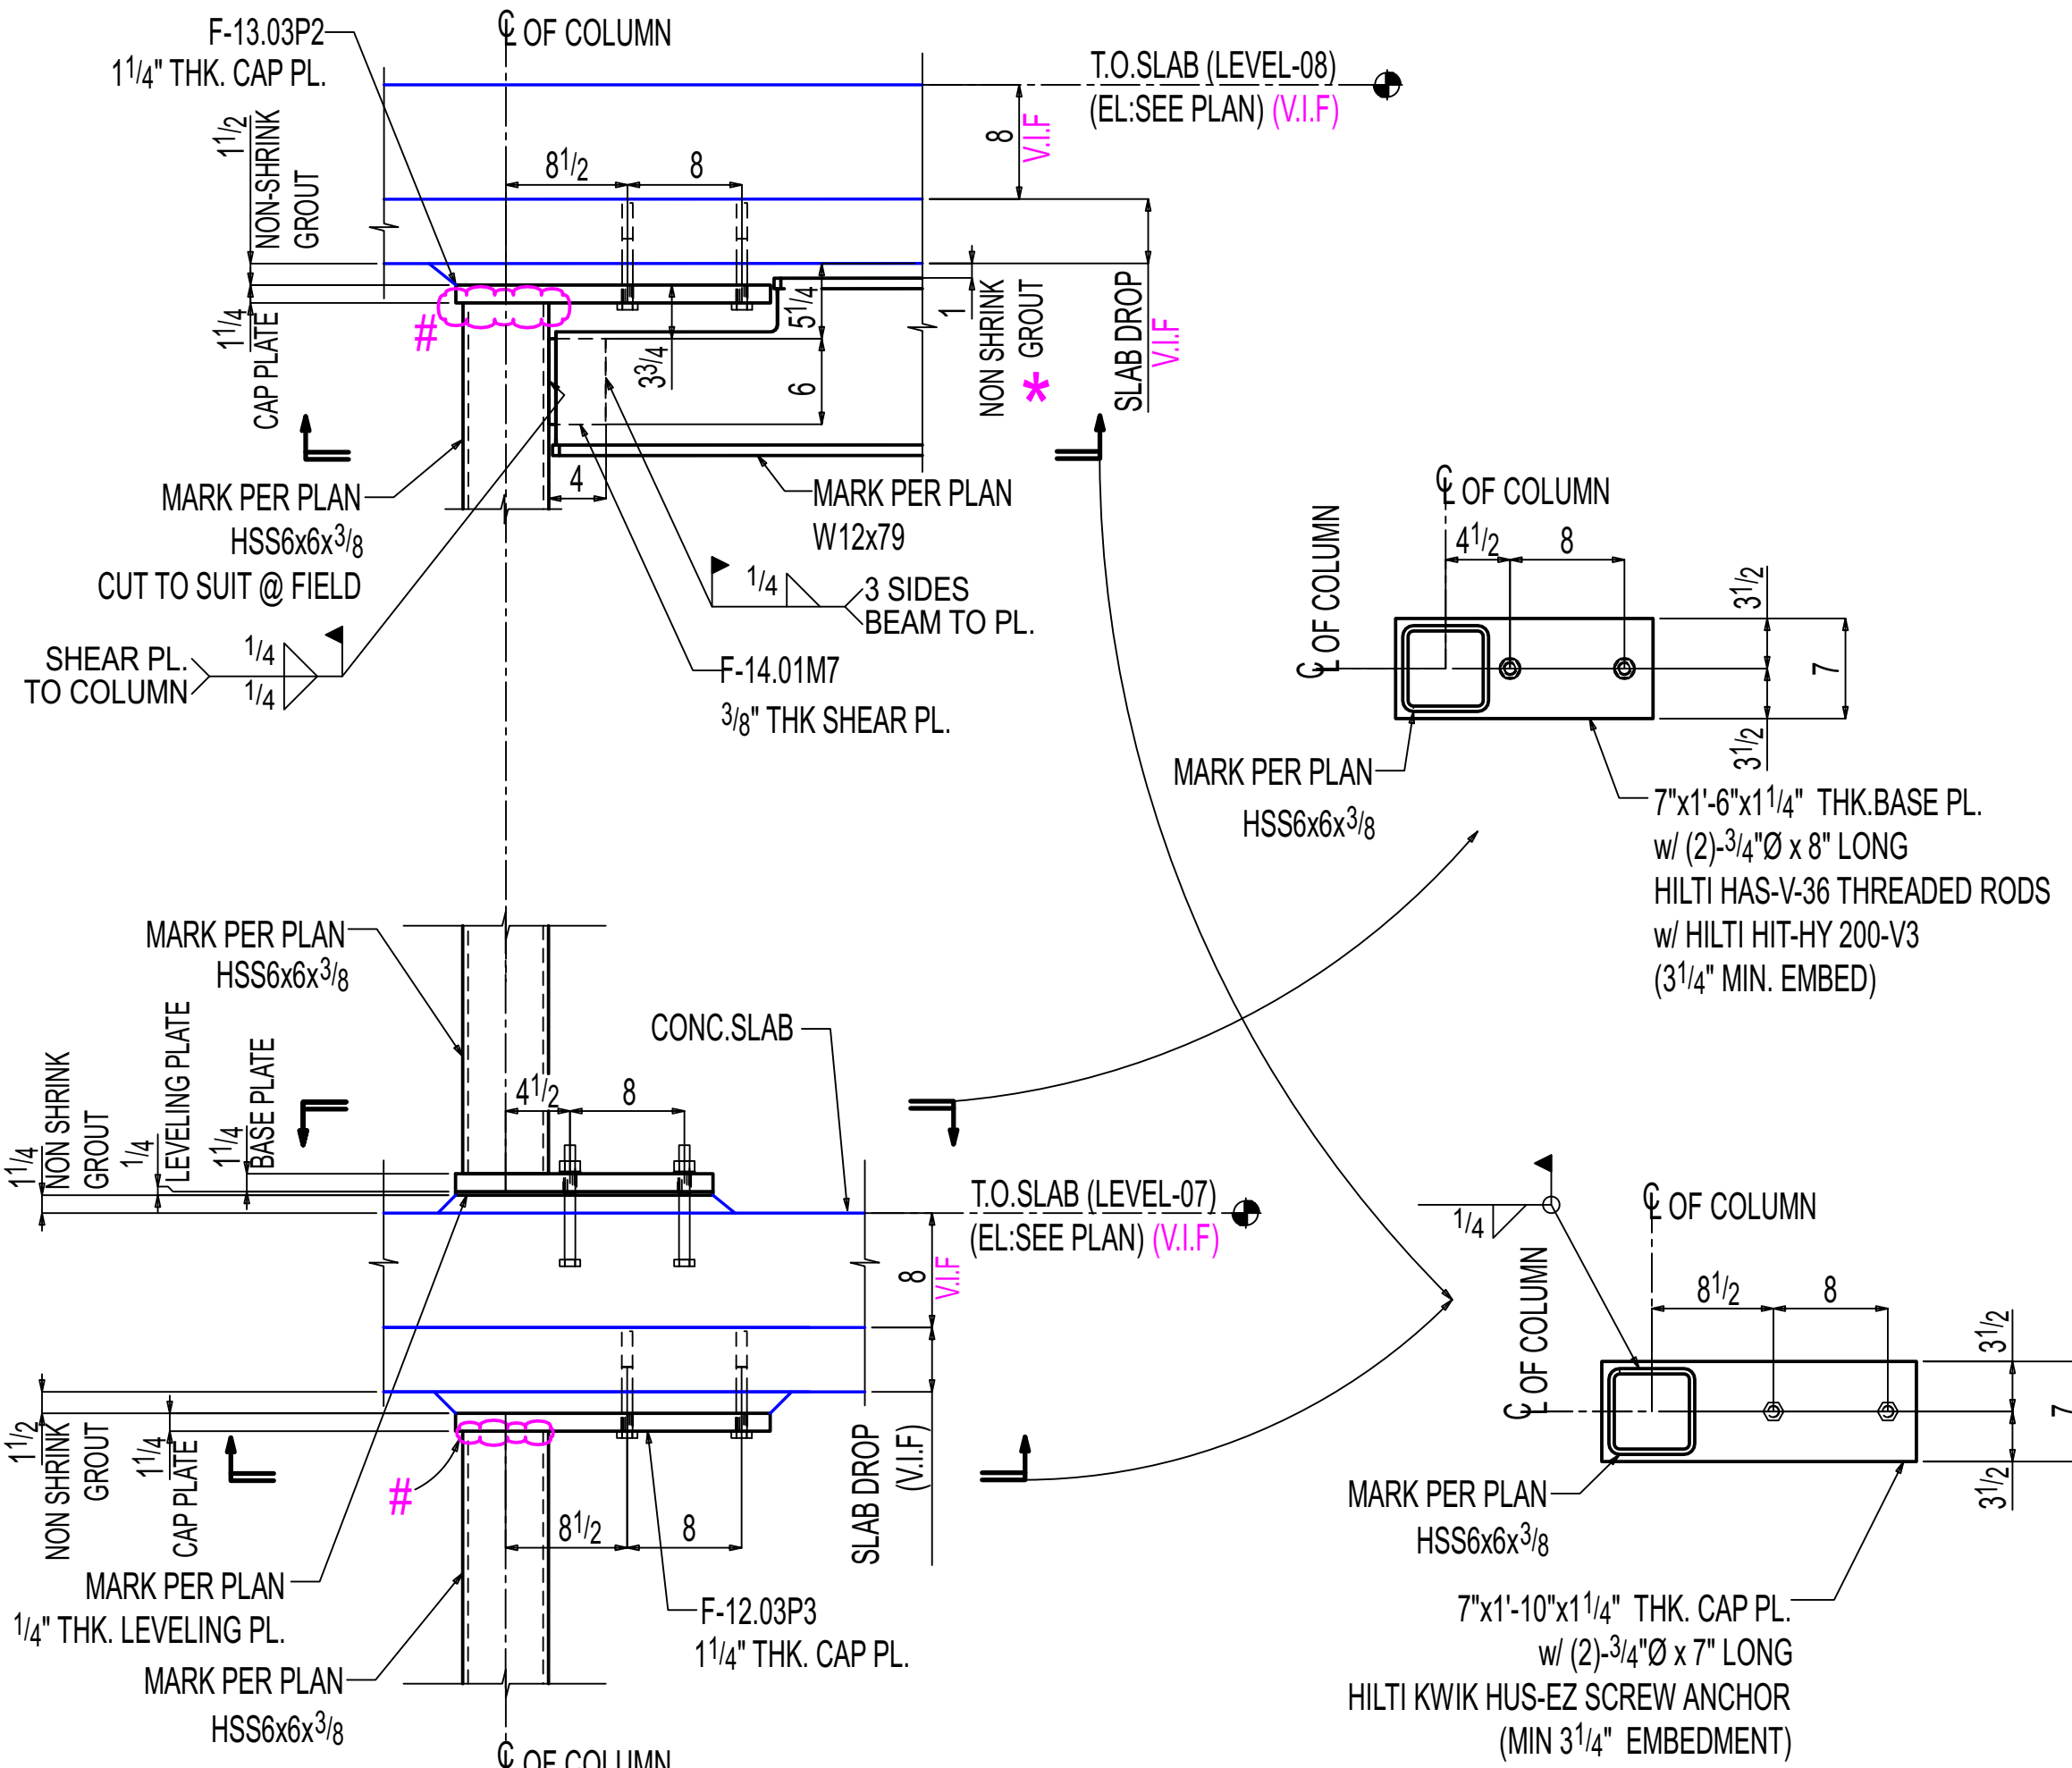

B-B

E-13.00
(REF: 5,6/S314)

OTHERS NOT SHOWN FOR CLARITY

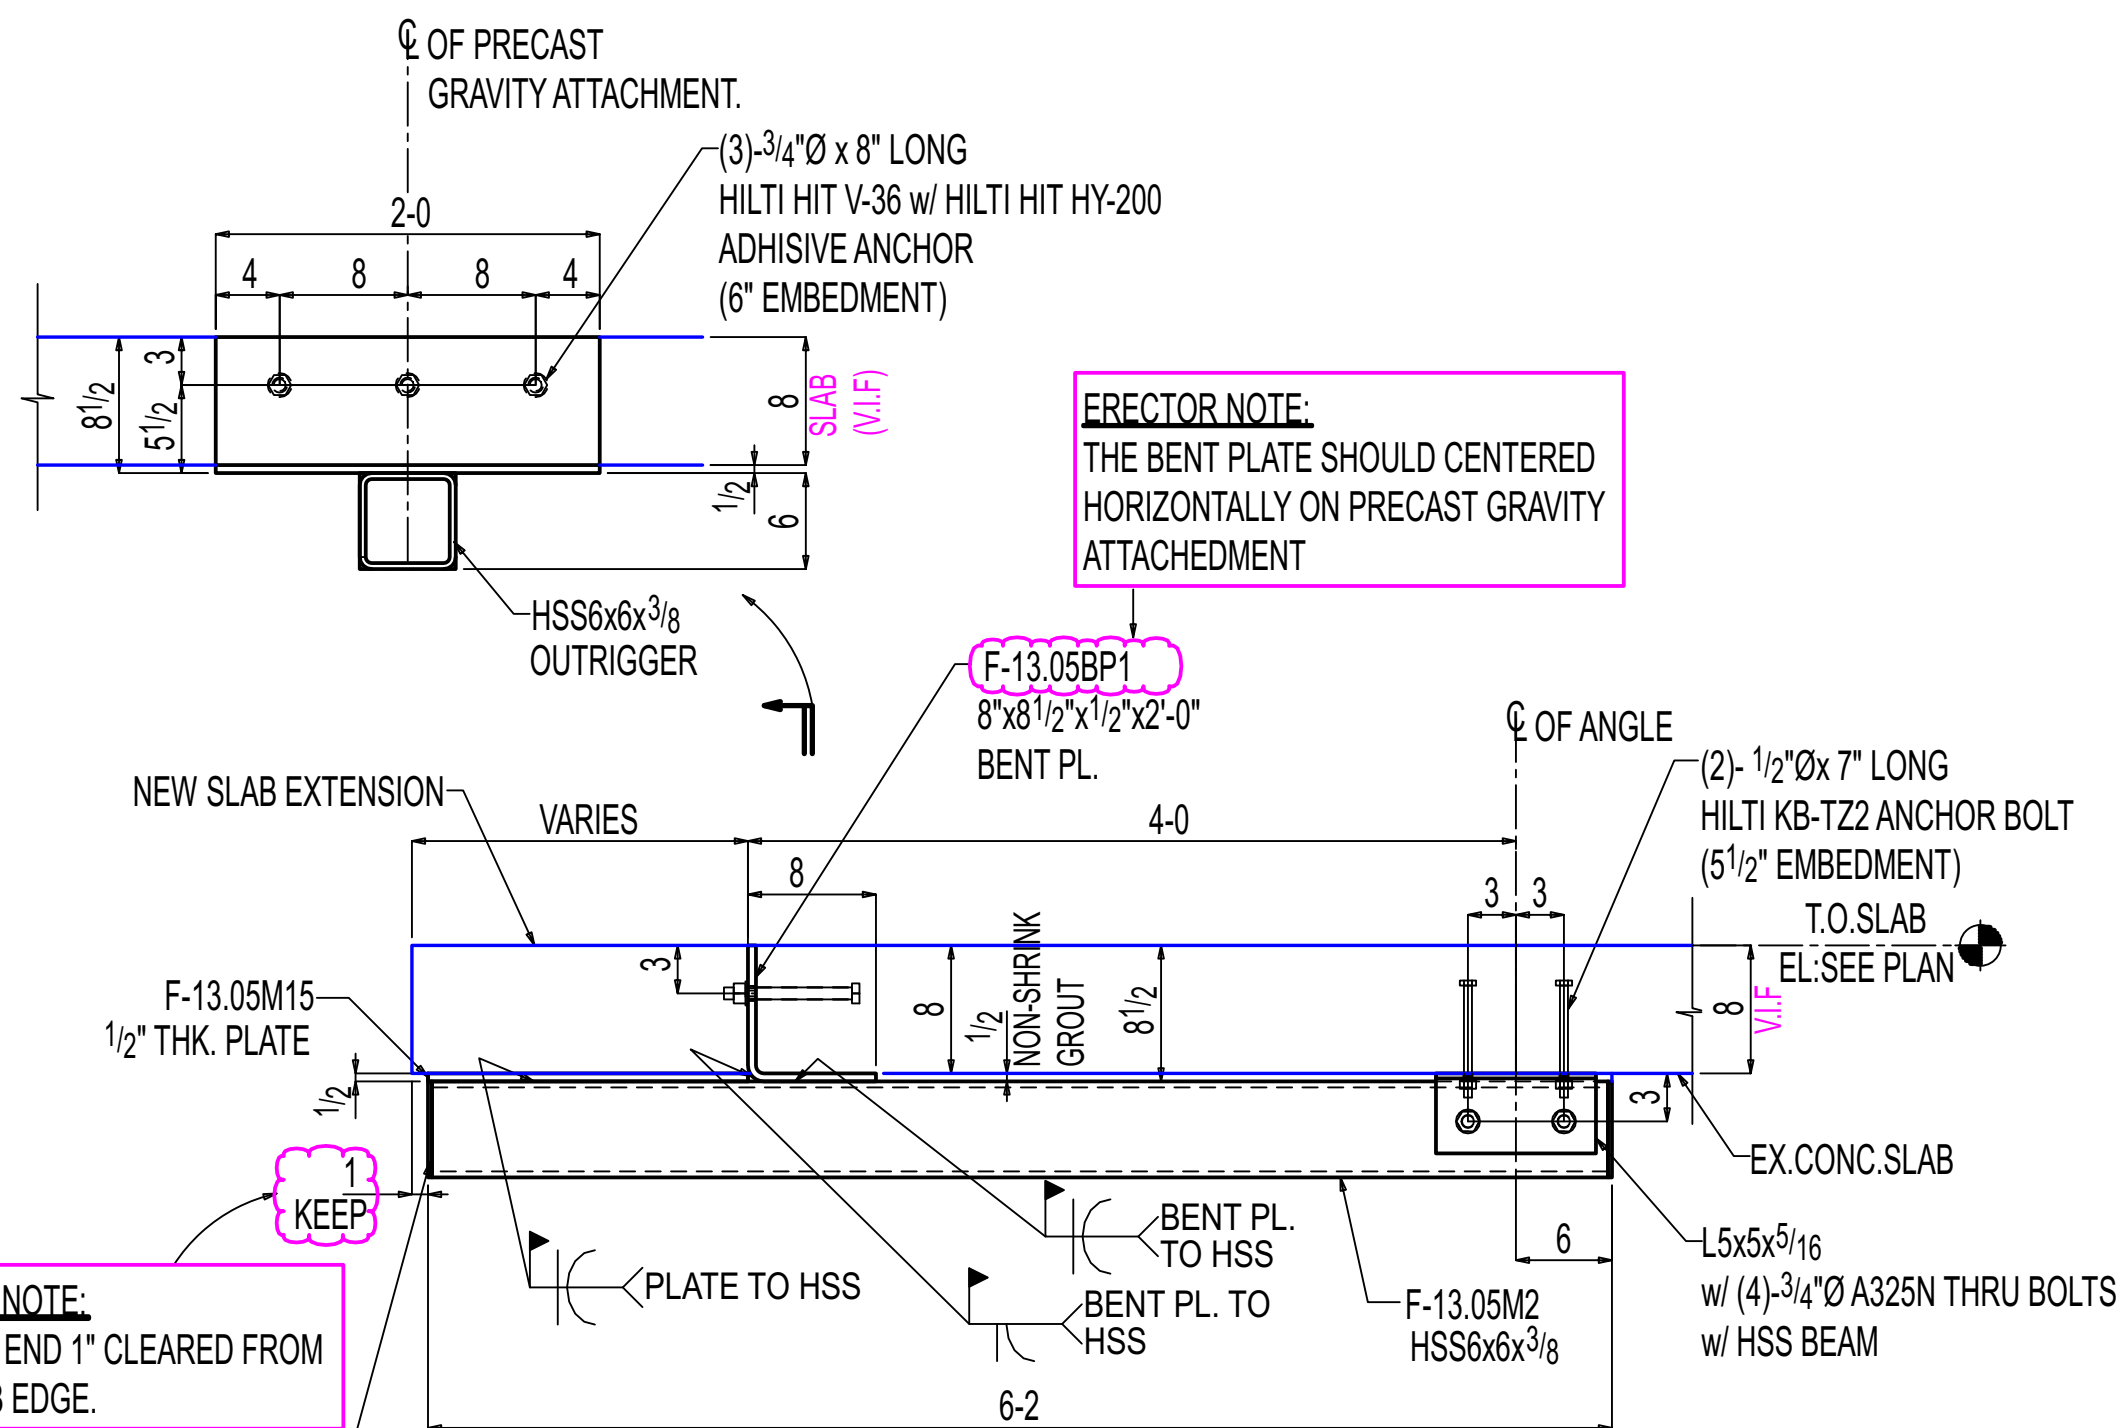

C-C

E-13.00
(REF: 3/S316)

OTHERS NOT SHOWN FOR CLARITY

*** -ERECTOR NOTE:**
PROVIDE 1" NON -SHRINK GROUT x 12" LONG
CENTERED BENEATH AT PRECAST
ATTACHMENT POINTS.

ERECTOR NOTE:
ALL # INDICATED COLUMN ENDS TO BE
CUT TO SUIT @ FIELD BASED ON FLOOR
TO FLOOR CLEARANCE AND WELD IT TO
THE CAP PLATE.

General Notes

- *Structural steel shall conform to ASTM-A992.
- *Structural SQR/RND tubing conform to ASTM A500 Grade C
- *Pipe shall conform to ASTM A53, Grade B.
- *Channels, Angles and plates shall conform to A36.
- *All bolts shall be 3/4" High strength in accordance with ASTM A325 (UNO)
- *Welding Electrodes for Carbon steel :E70xx

# of Copies	Revision/ Issue	Destination	Date
5	0	For Construction	11-17-2025
4	D	For Re-Approval	10-24-2025
3	C	For Re-Approval	09-19-2025
2	B	For Re-Approval	06-23-2025
1	A	For Approval	02-25-2025

IRON FABRICATION SERVICES, LLC.

3029 M. Street, NW, Suite 202
Washington, DC 20007
Tel: 202-800-5599
Fax: 202-478-0303

Project Name and Address
MARYLAND AVENUE

Location: **1250 MARYLAND AVENUE SW
WASHINGTON, DC 20024**

Contractor:
BALFOUR BEATTY



Approved for Fabrication by: Signature

Contract # **224009** Drawing # **E-13.01**


Contract Item: **LEVEL-07
SLAB EXTENSION**

Ref: **SOW-13: 3,4,5&6 / S307**

Date
01/20/2025
Drawing Title:
**SOW #13 LEVEL-07 NEW
SLAB EXTENSION SUPPORT
SECTIONS**

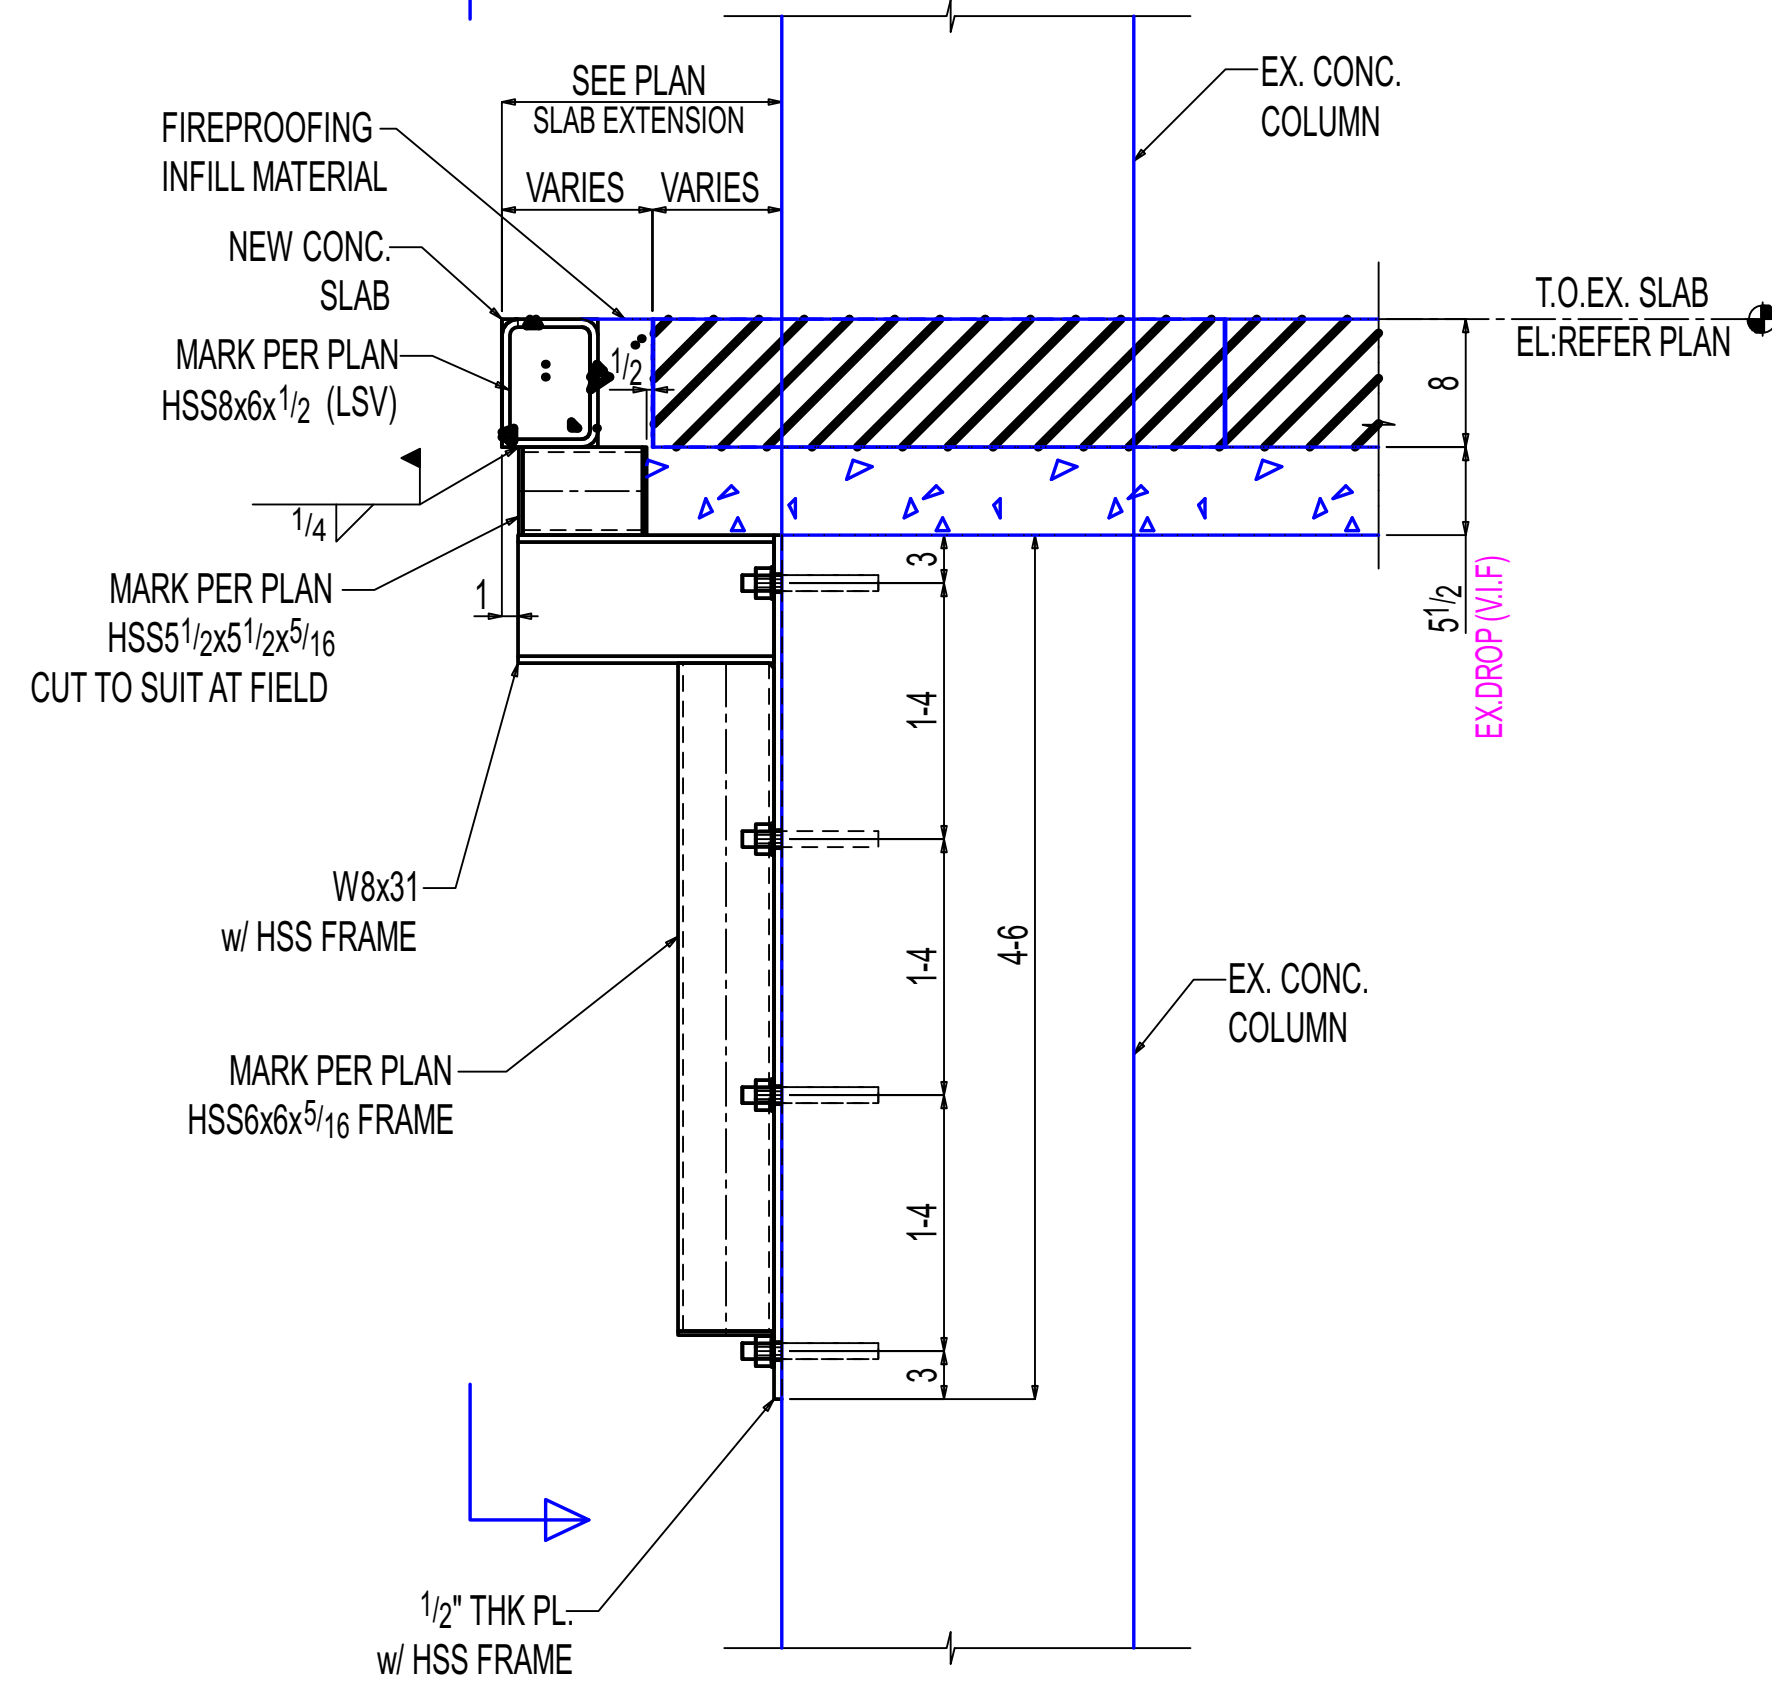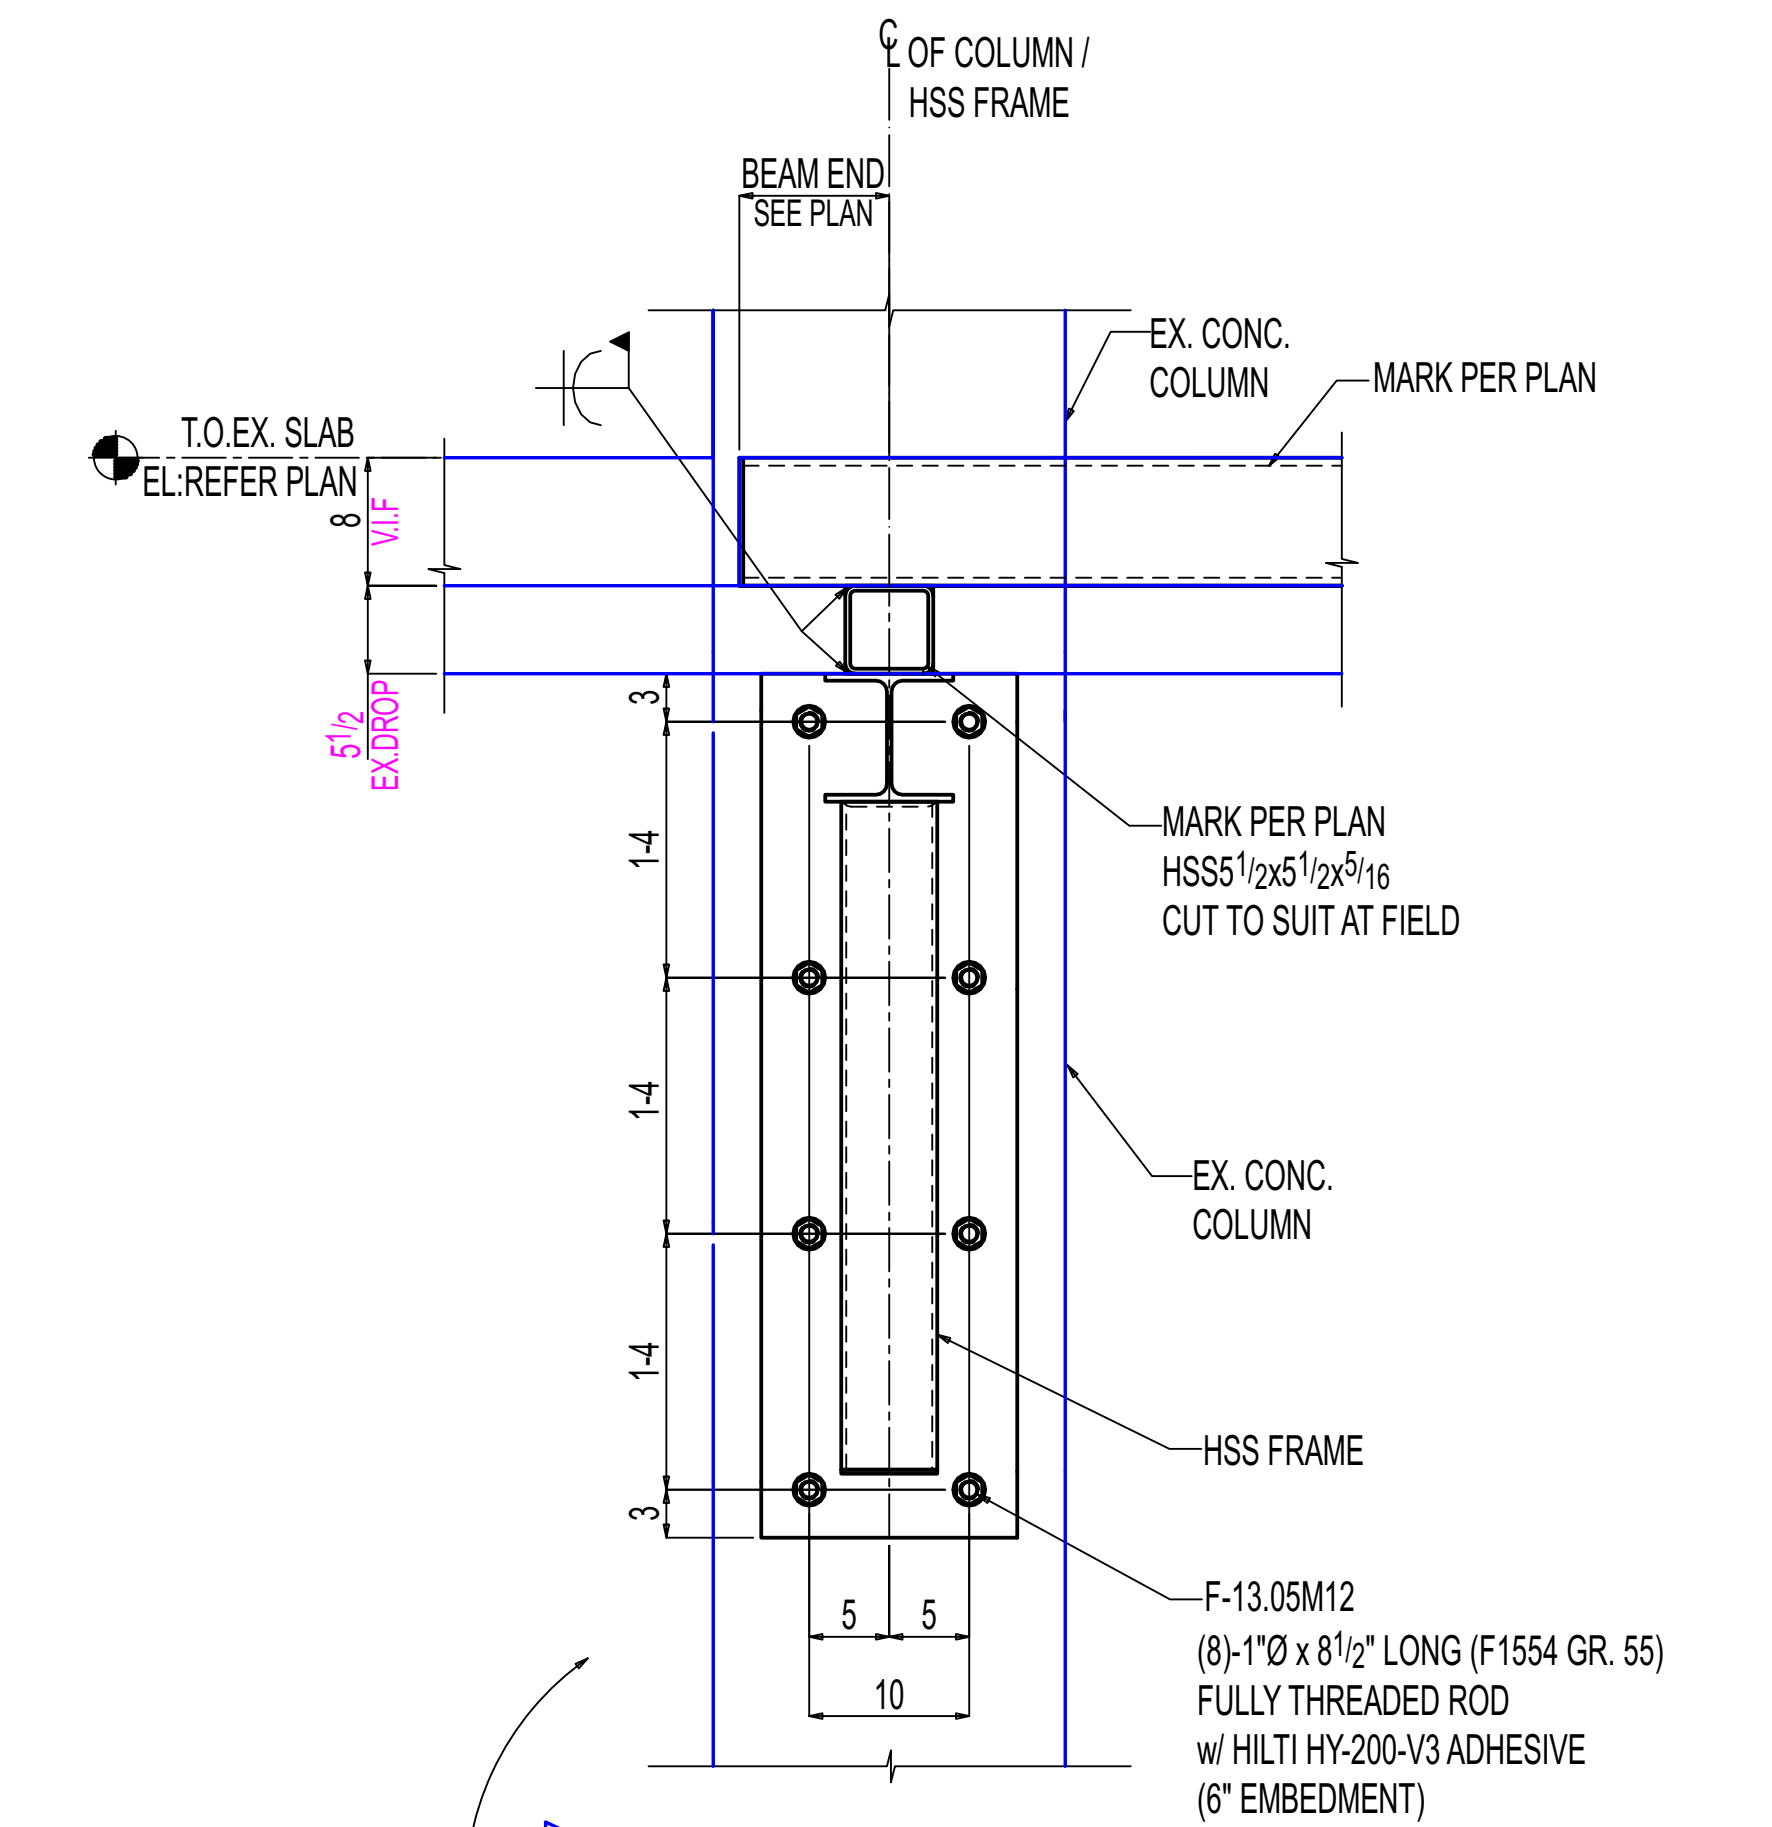


D-D
(NEW SLAB EXTENSION SUPPORT
@ SLAB DROP LOCATION NEW SLAB EXTENSION BETWEEN 1'-0" TO 1'-6")
E-13.00
(REF: 10 & 11/S314)
OTHERS NOT SHOWN FOR CLARITY

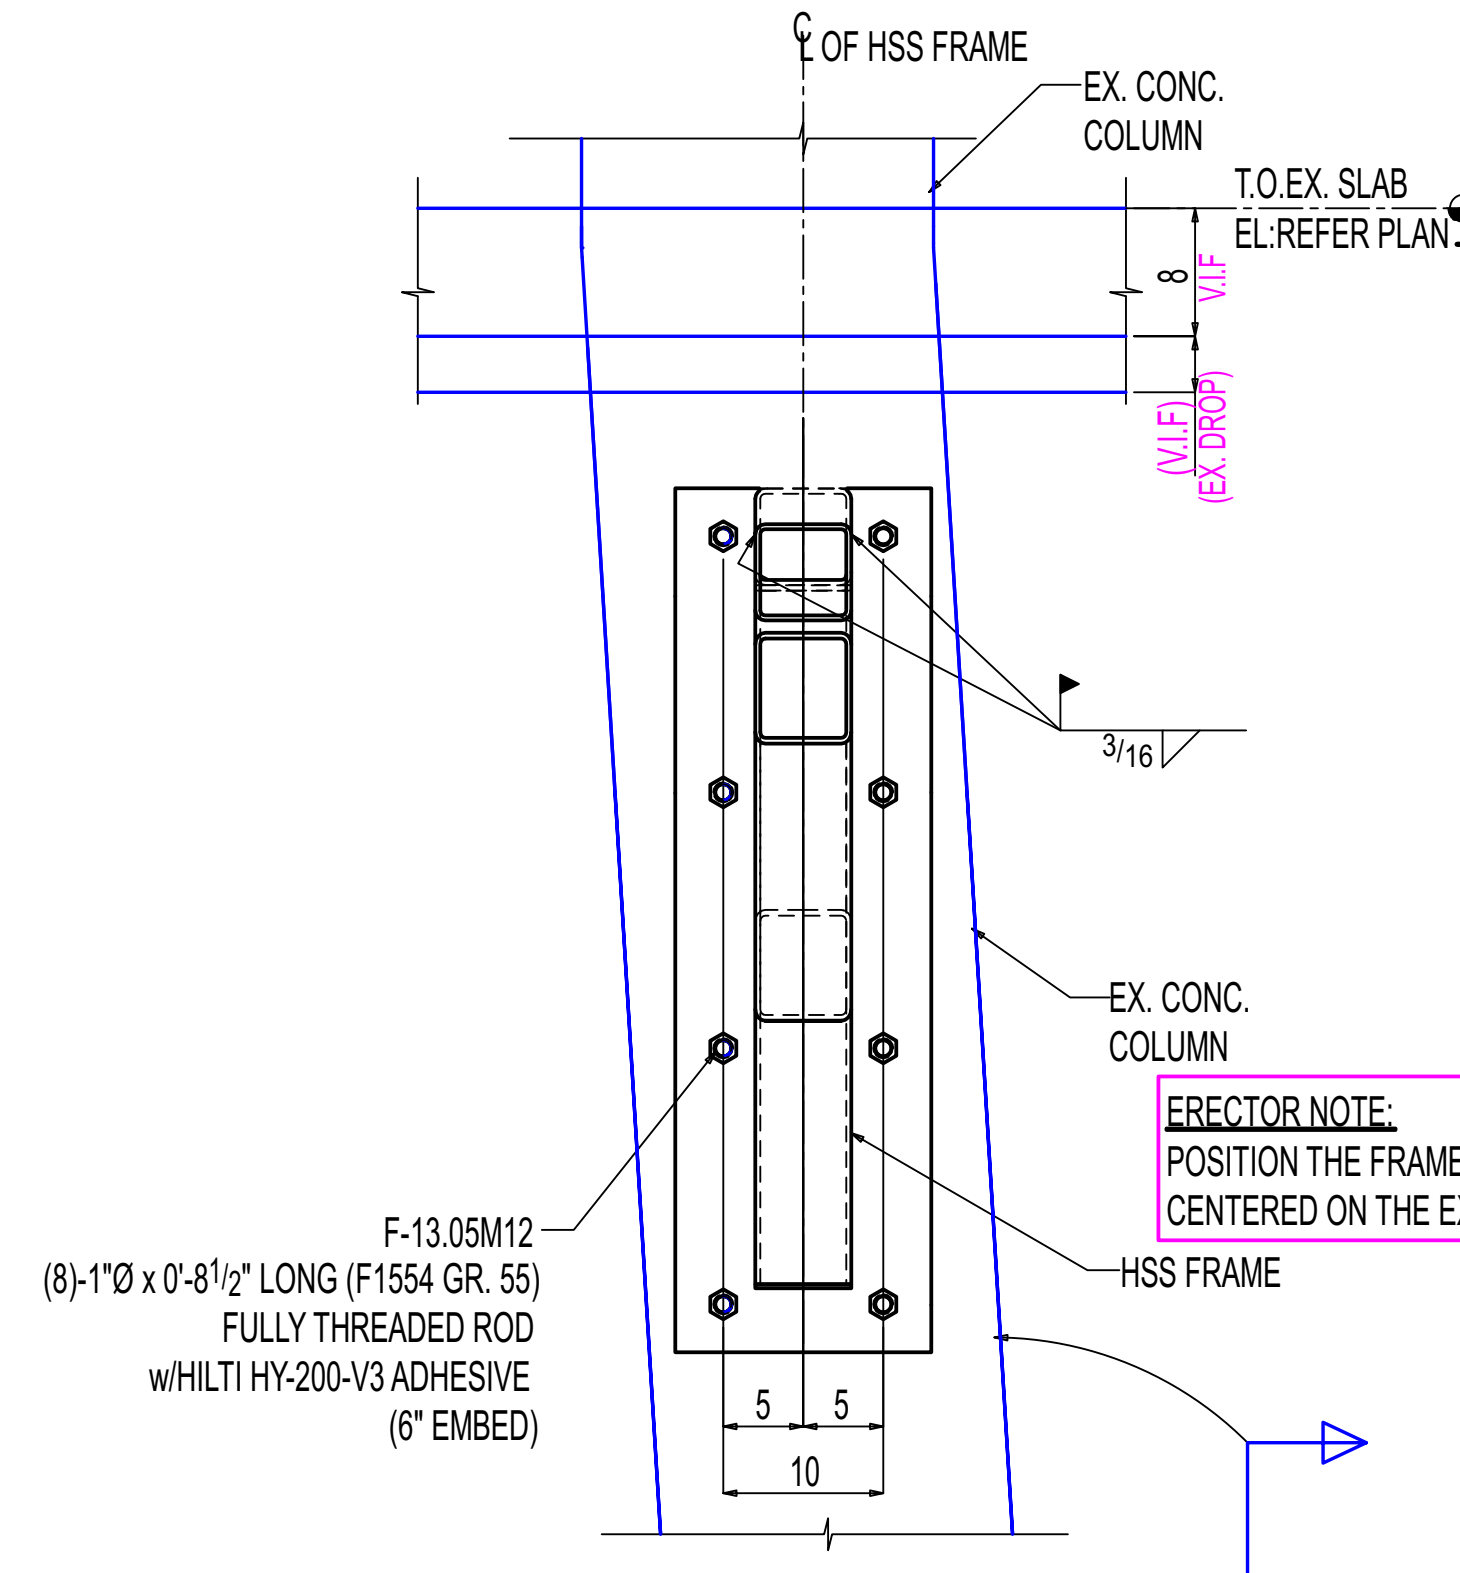

*** -ERECTOR NOTE:**
FIELD CUT HSS6x6 ENDS TO SUIT AT EXISTING COLUMN SLOPE.

ERECTOR NOTE:
POSITION THE FRAME TO BE
CENTERED ON THE EXISTING COLUMN.

ERECTOR NOTE:
1"NSx6" WIDTH GROUT @ PRECAST BEARING POINT ONLY
CO-ORDINATE BEARING POINT LOCATION WITH
PRECAST MANUFACTURER.

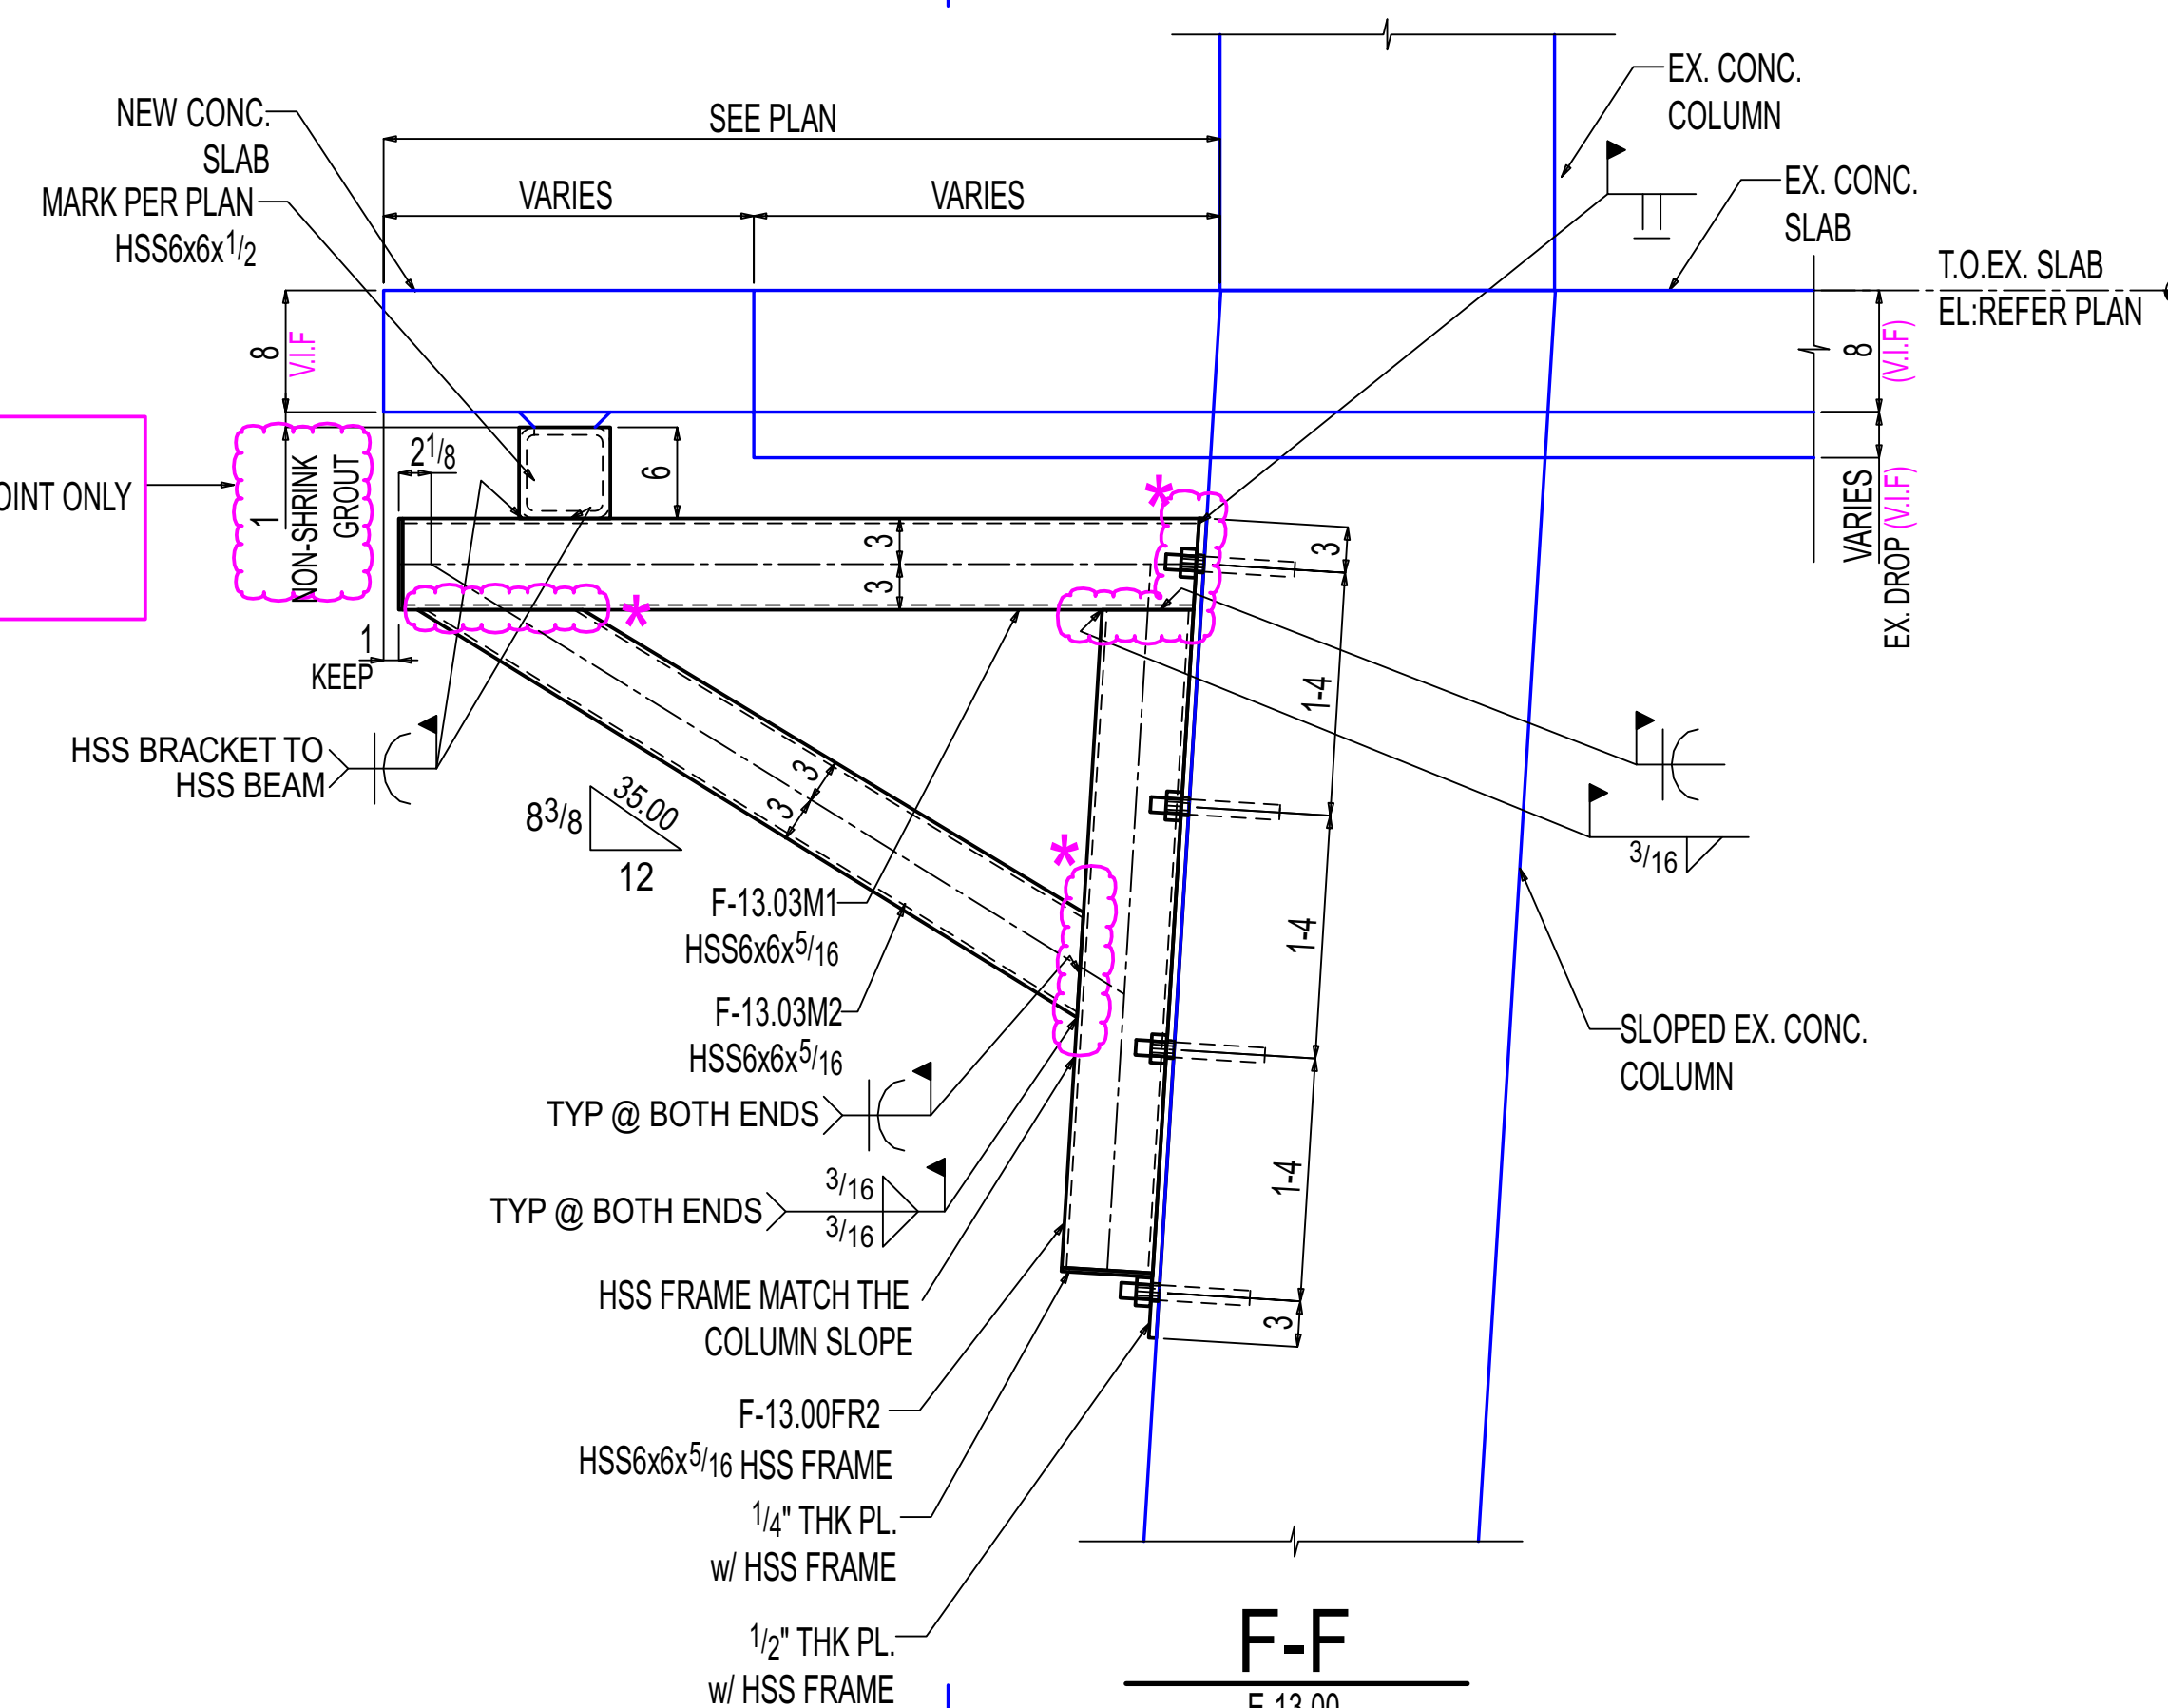

F-F
E-13.00
(REF: 9/S315)
OTHERS NOT SHOWN FOR CLARITY

SHOP / ERECTOR NOTE:
LOCATE EXISTING REBAR PRIOR TO FABRICATION OF PLATE.
DO NOT DRILL THROUGH REBAR.

General Notes

- *Structural steel shall conform to ASTM-A992.
- *Structural SQR/RND tubing conform to ASTM A500 Grade C
- *Pipe shall conform to ASTM A53, Grade B.
- *Channels, Angles and plates shall conform to A36.
- *All bolts shall be 3/4" High strength in accordance with ASTM A325 (UNO)
- *Welding Electrodes for Carbon steel :E70xx

# of Copies	Revision/ Issue	Destination	Date
5	0	For Construction	11-17-2025
4	D	For Re-Approval	10-24-2025
3	C	For Re-Approval	09-19-2025
2	B	For Re-Approval	06-23-2025
1	A	For Approval	02-25-2025

IRON FABRICATION SERVICES, LLC.

3029 M. Street, NW, Suite 202
Washington, DC 20007
Tel: 202-800-5599
Fax: 202-478-0303

Project Name and Address
MARYLAND AVENUE

Location: **1250 MARYLAND AVENUE SW
WASHINGTON, DC 20024**

Contractor:
BALFOUR BEATTY


Approved for Fabrication by: Signature

Contract # **224009** Drawing # **E-13.02**

Contract Item: **LEVEL-07
SLAB EXTENSION**

Ref: **SOW-13: 3,4,5&6 / S307**

Date
01/20/2025
Scale
VARIES
Drawing Title:
**SOW #13 LEVEL-07 NEW
SLAB EXTENSION SUPPORT
SECTIONS**

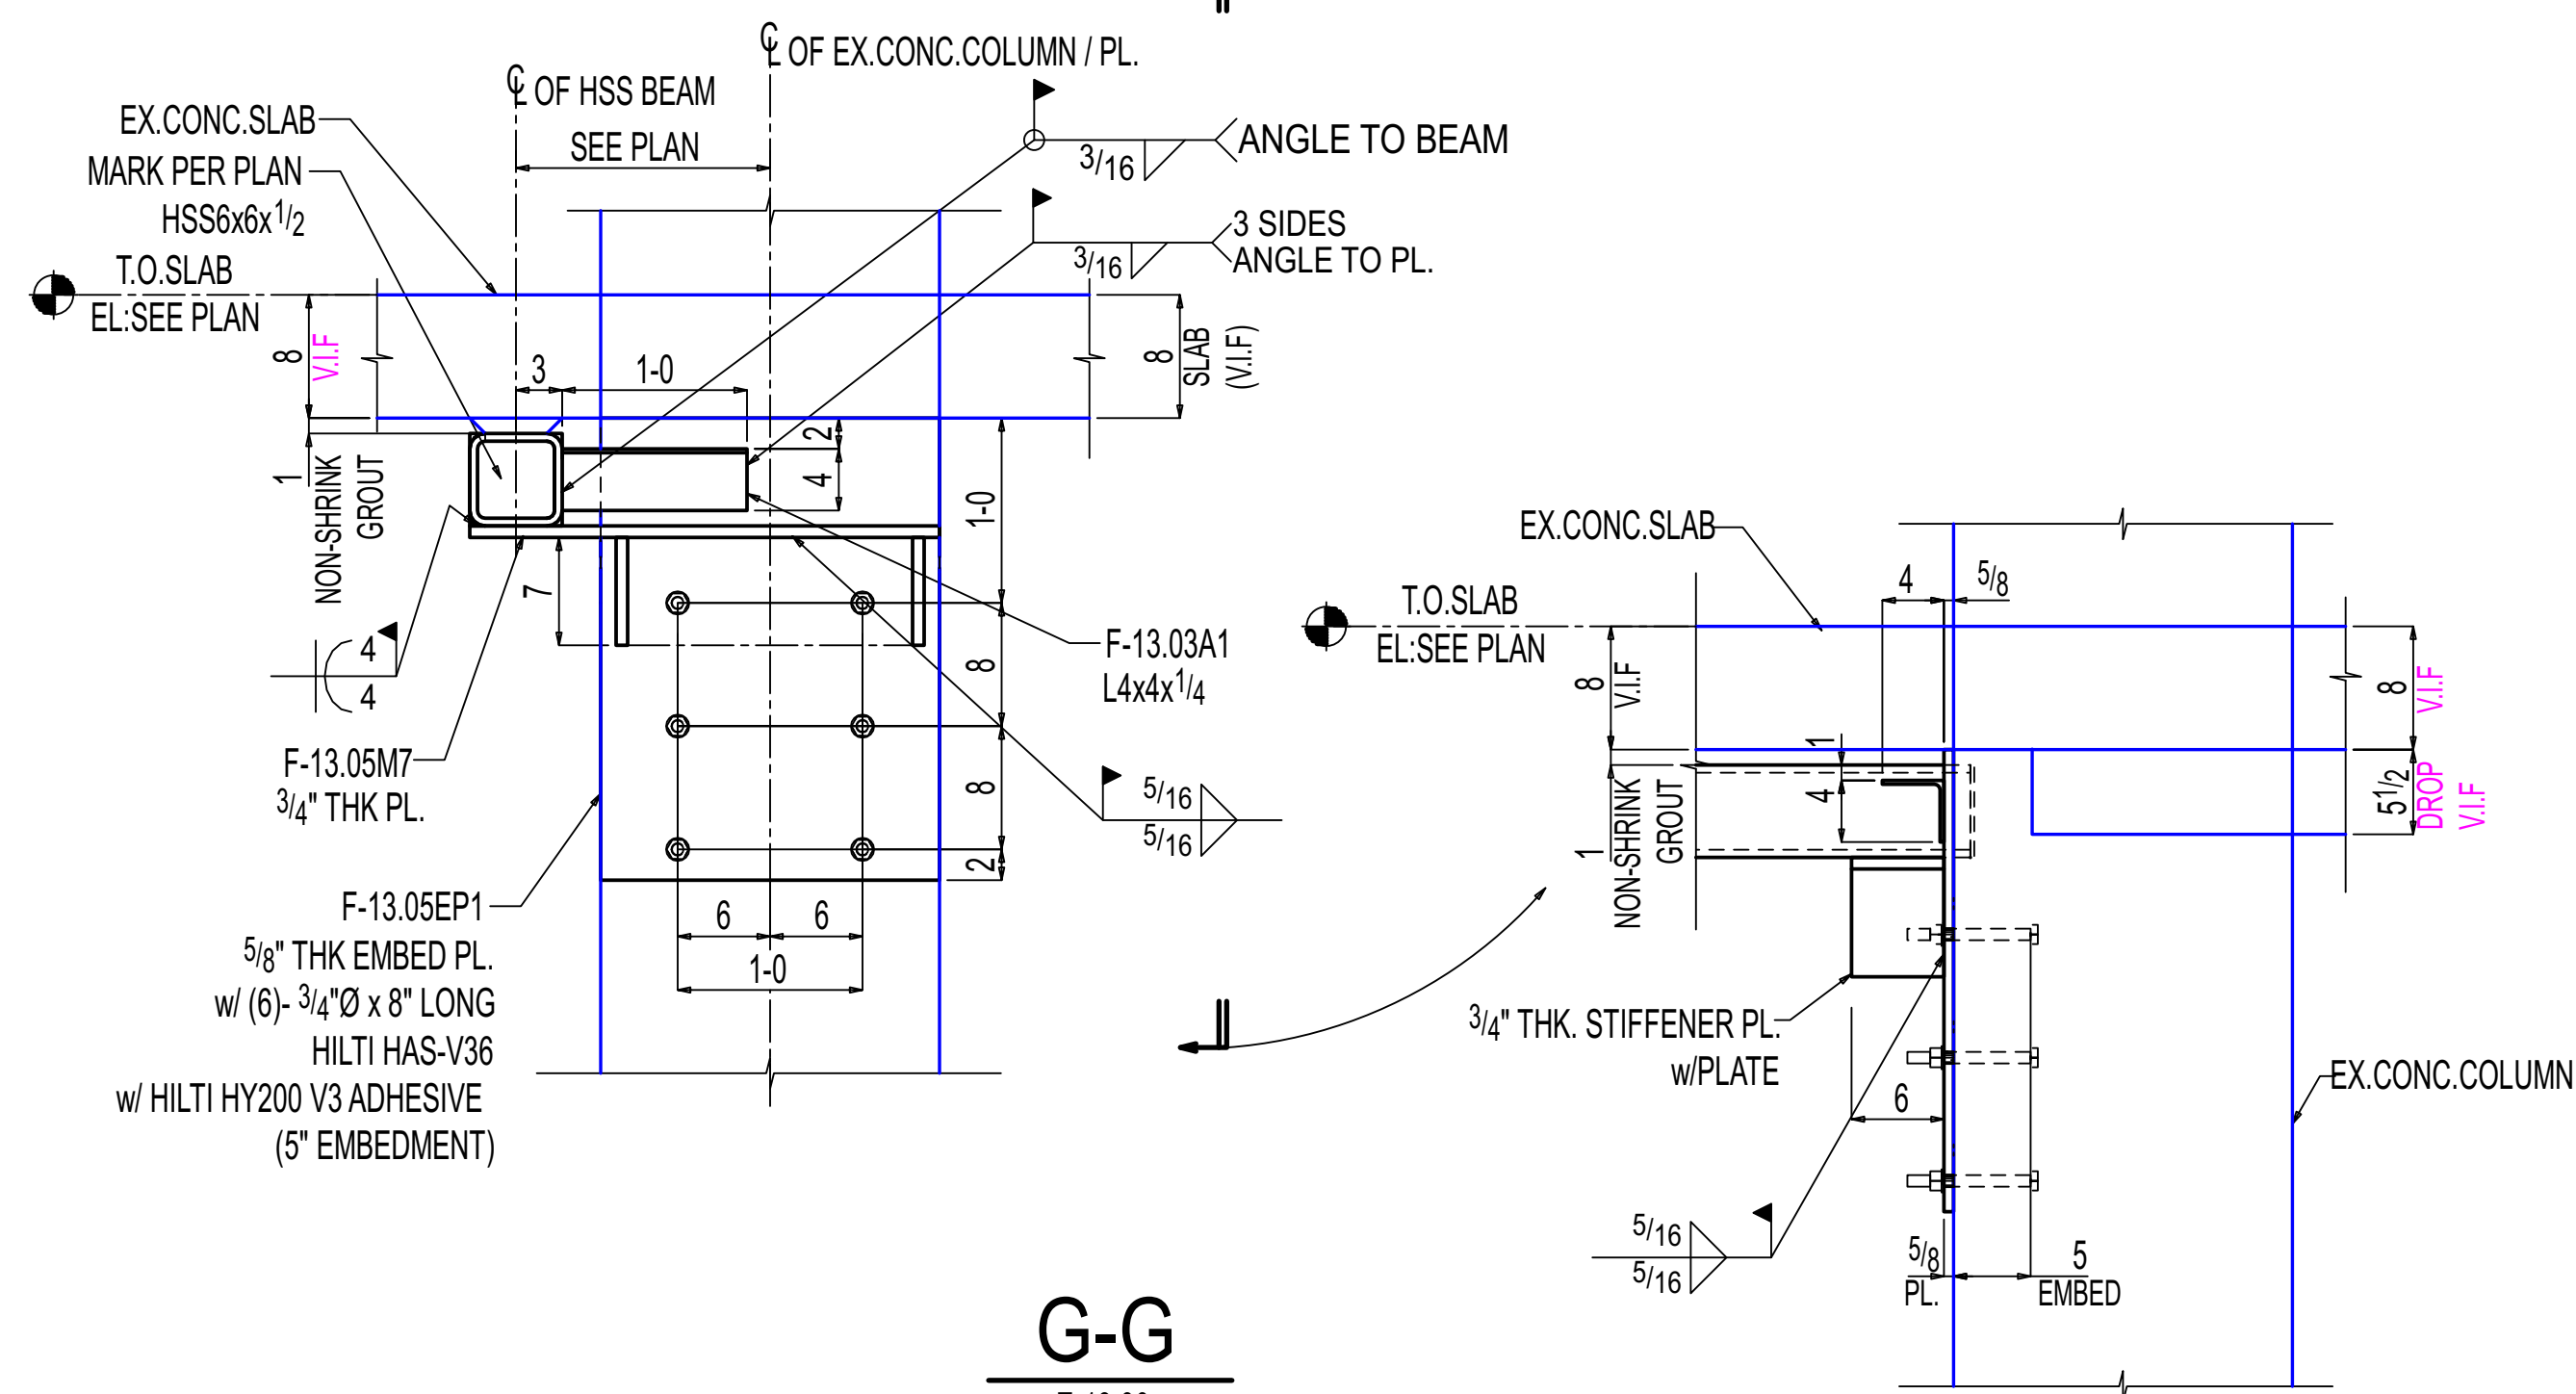


G-G

E-13.00

(REF: 7/S316)

OTHERS NOT SHOWN FOR CLARITY

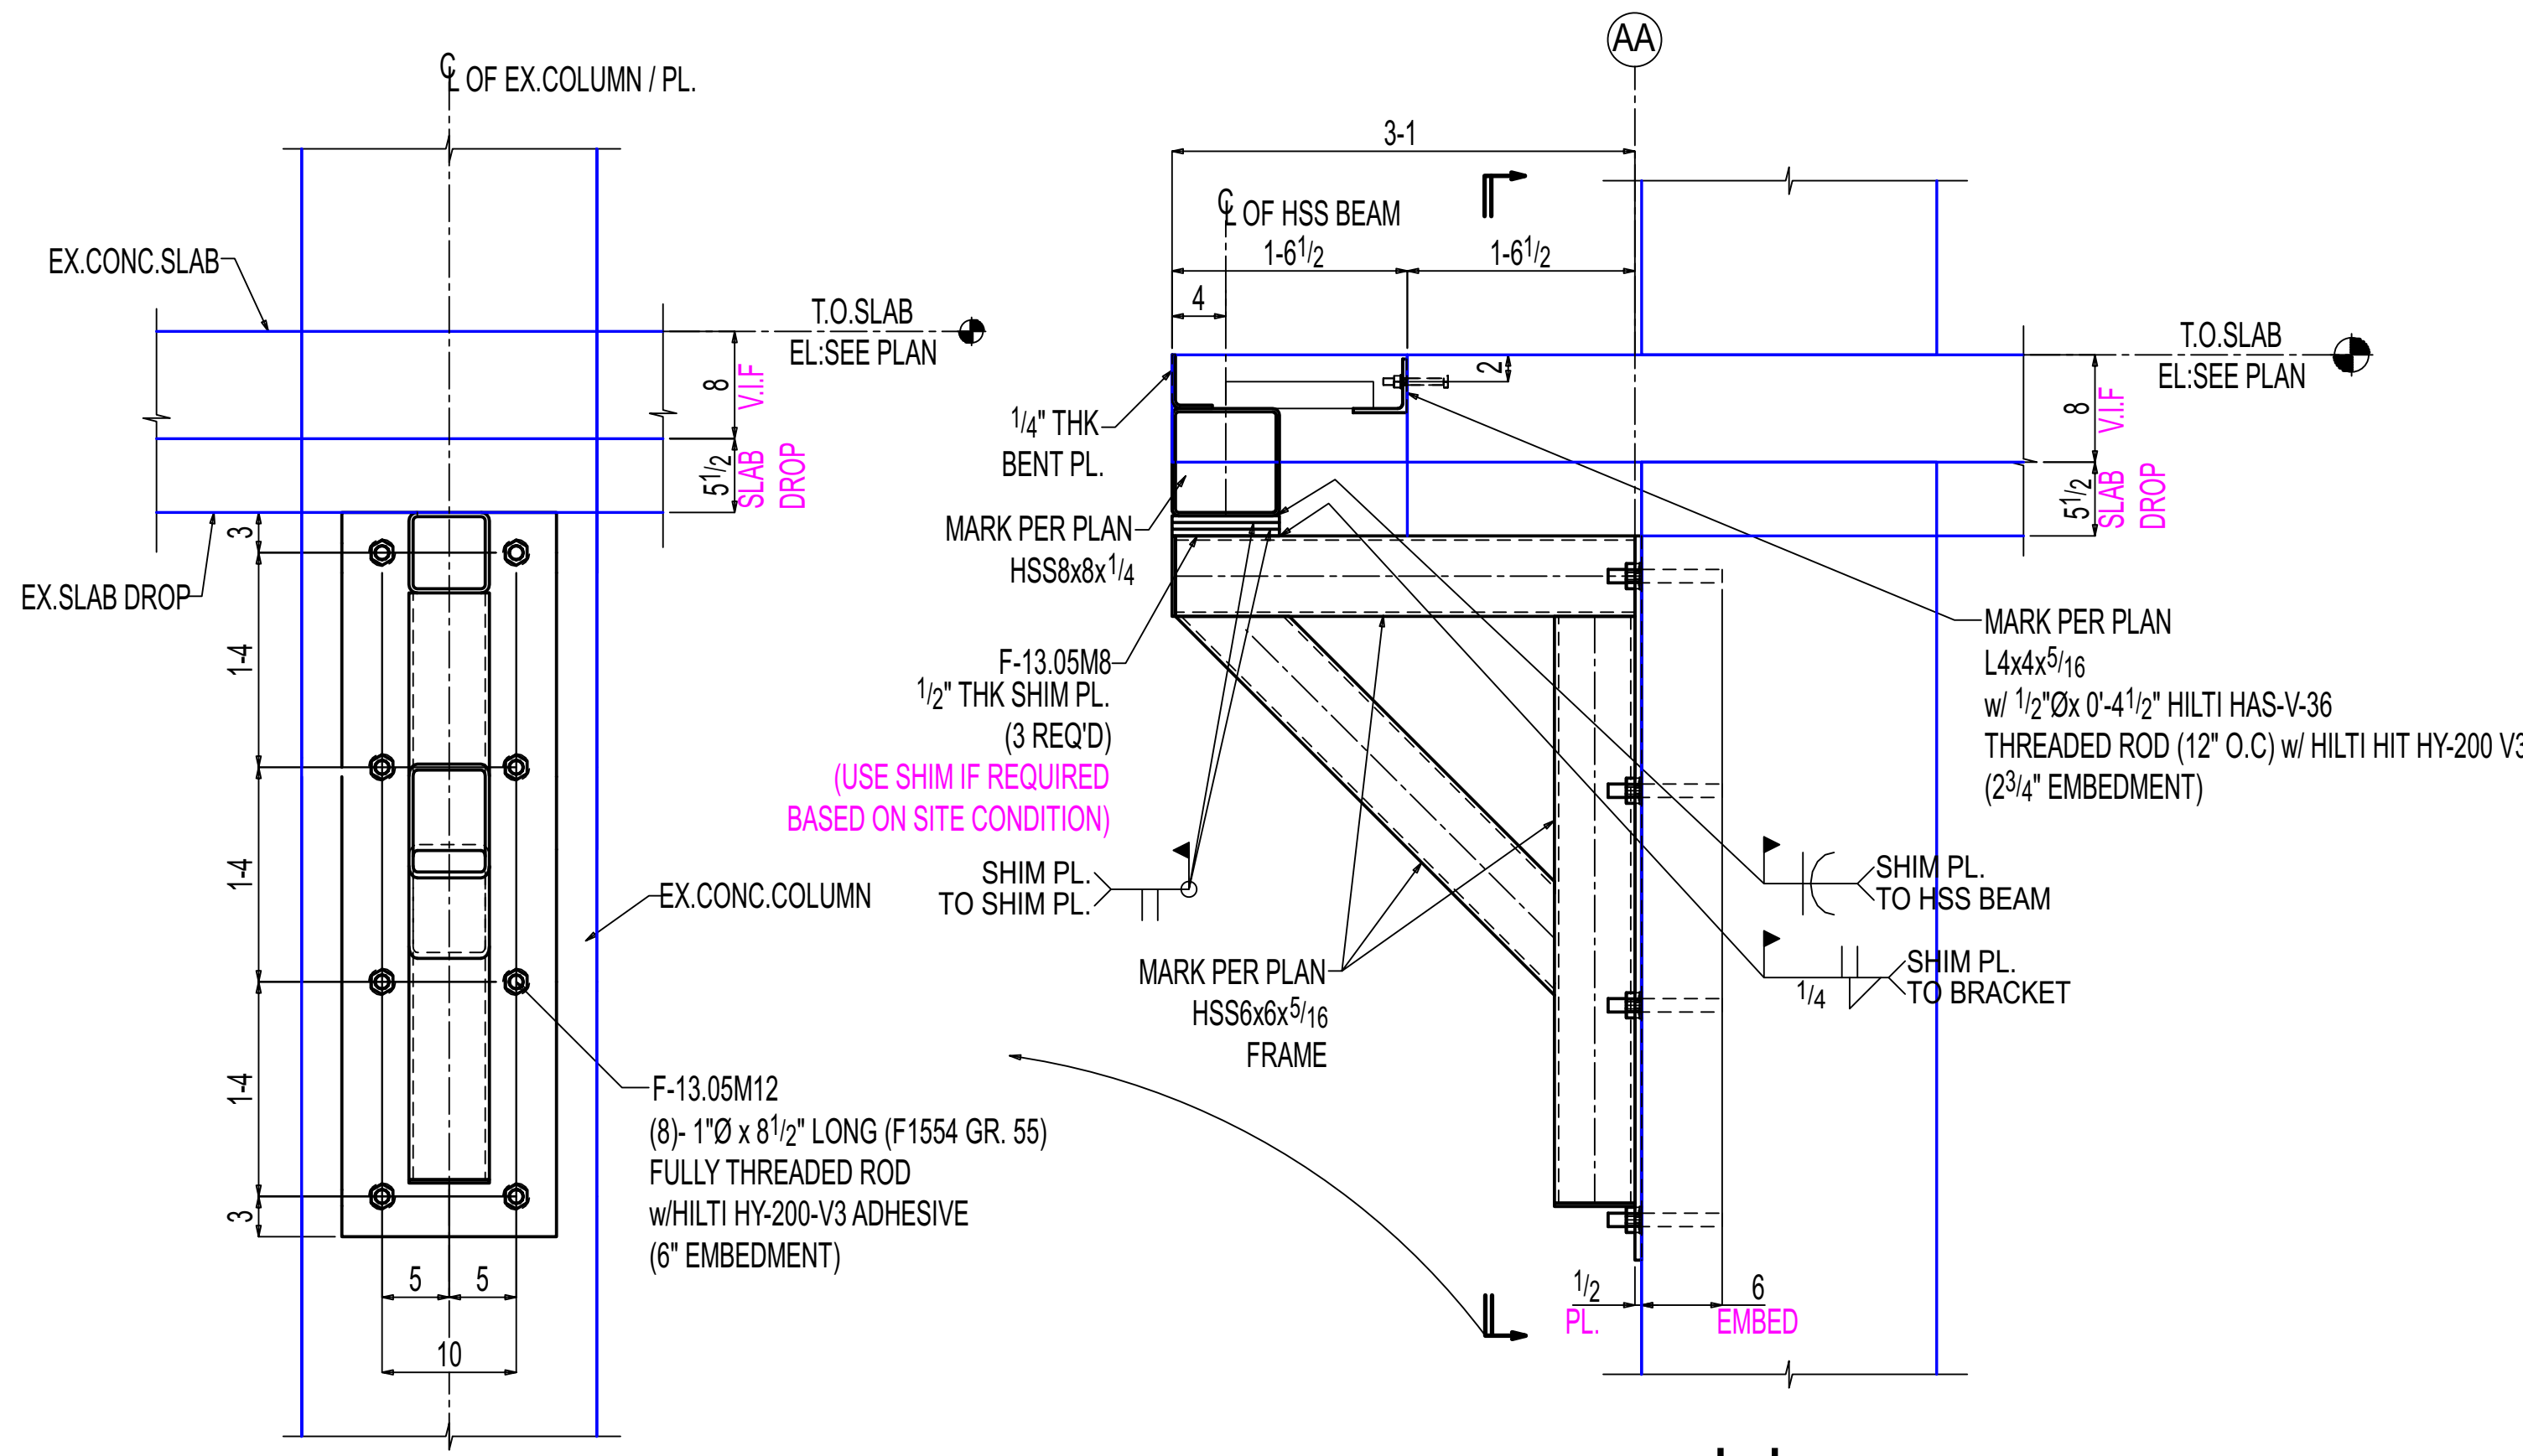


J-J

E-13.00

(REF: 5/S316)

OTHERS NOT SHOWN FOR CLARITY

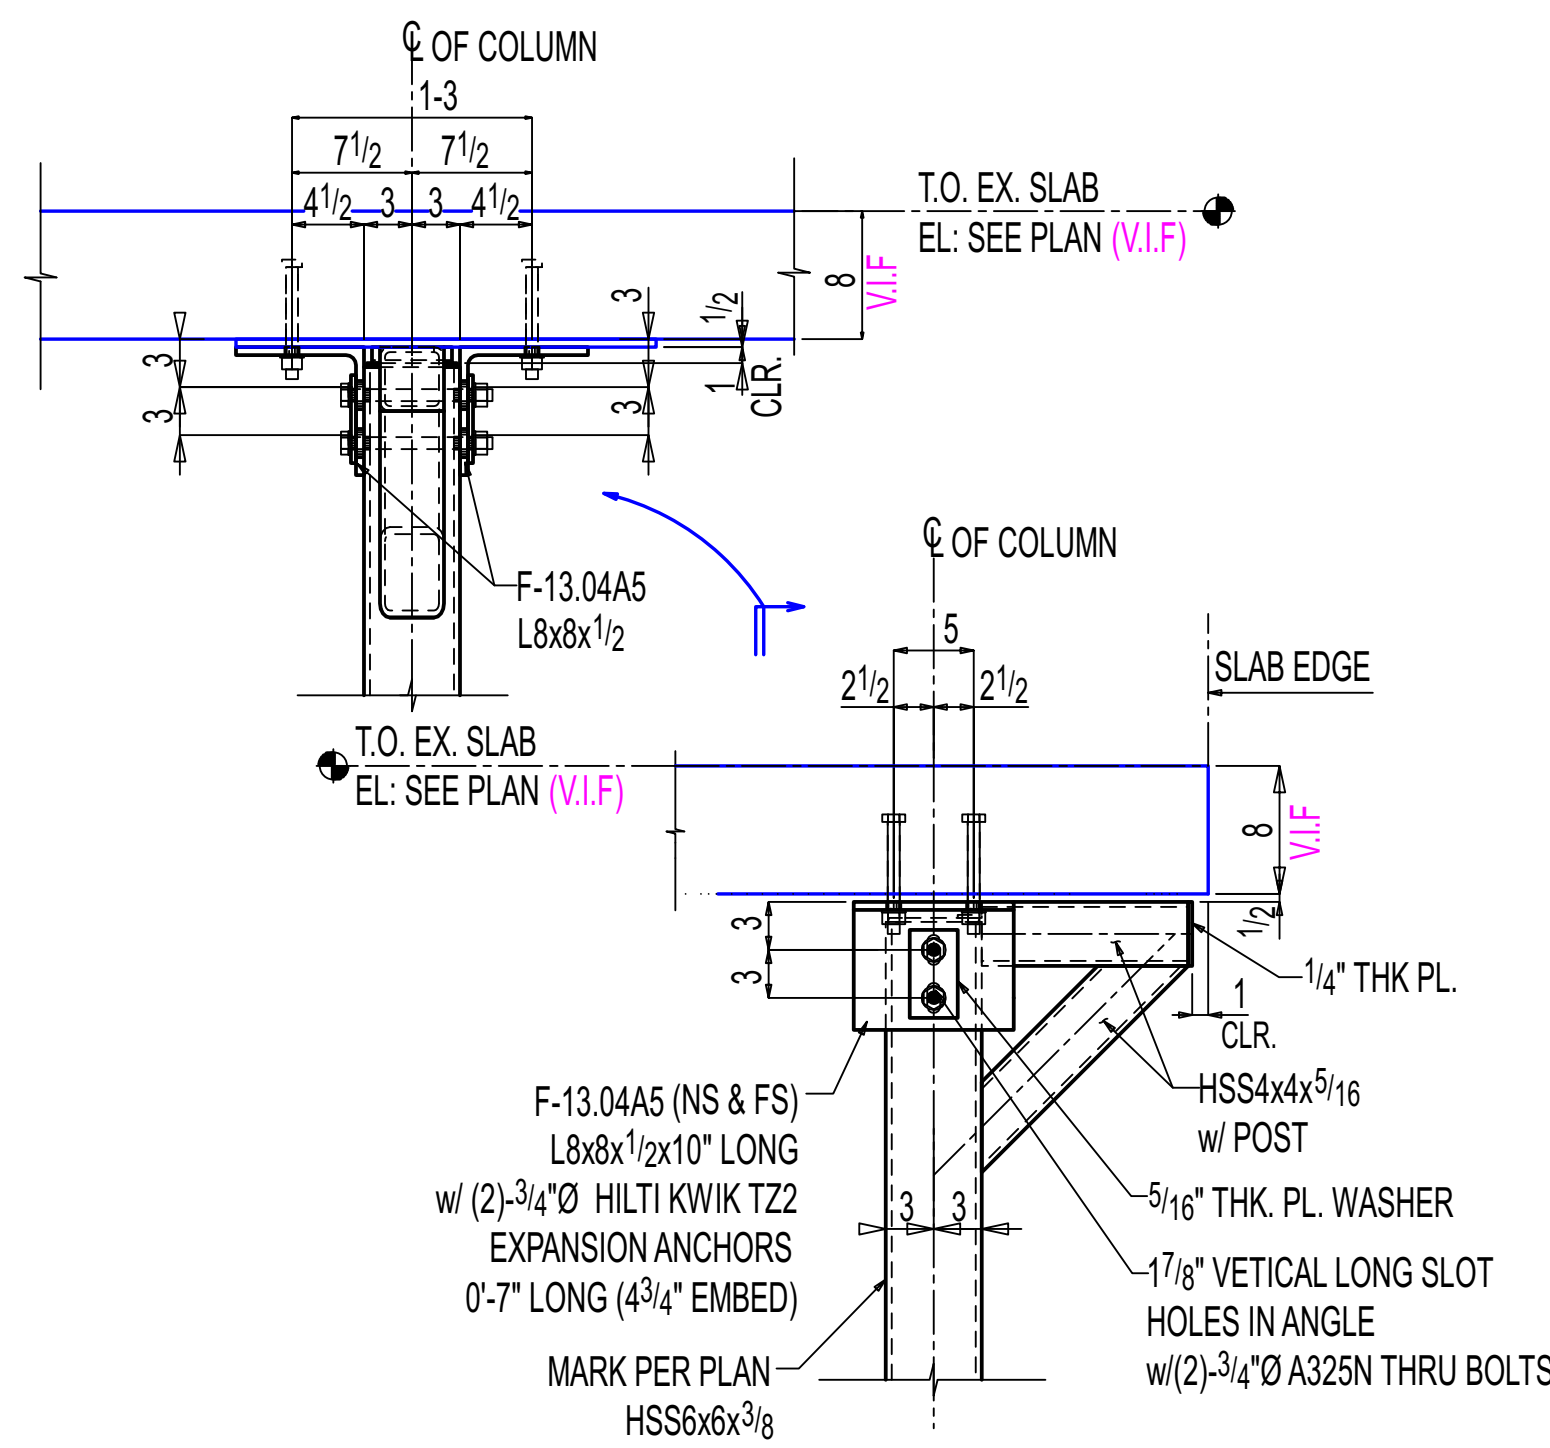


H-H

E-13.00

(REF: 1 & 2/S317)

OTHERS NOT SHOWN FOR CLARITY

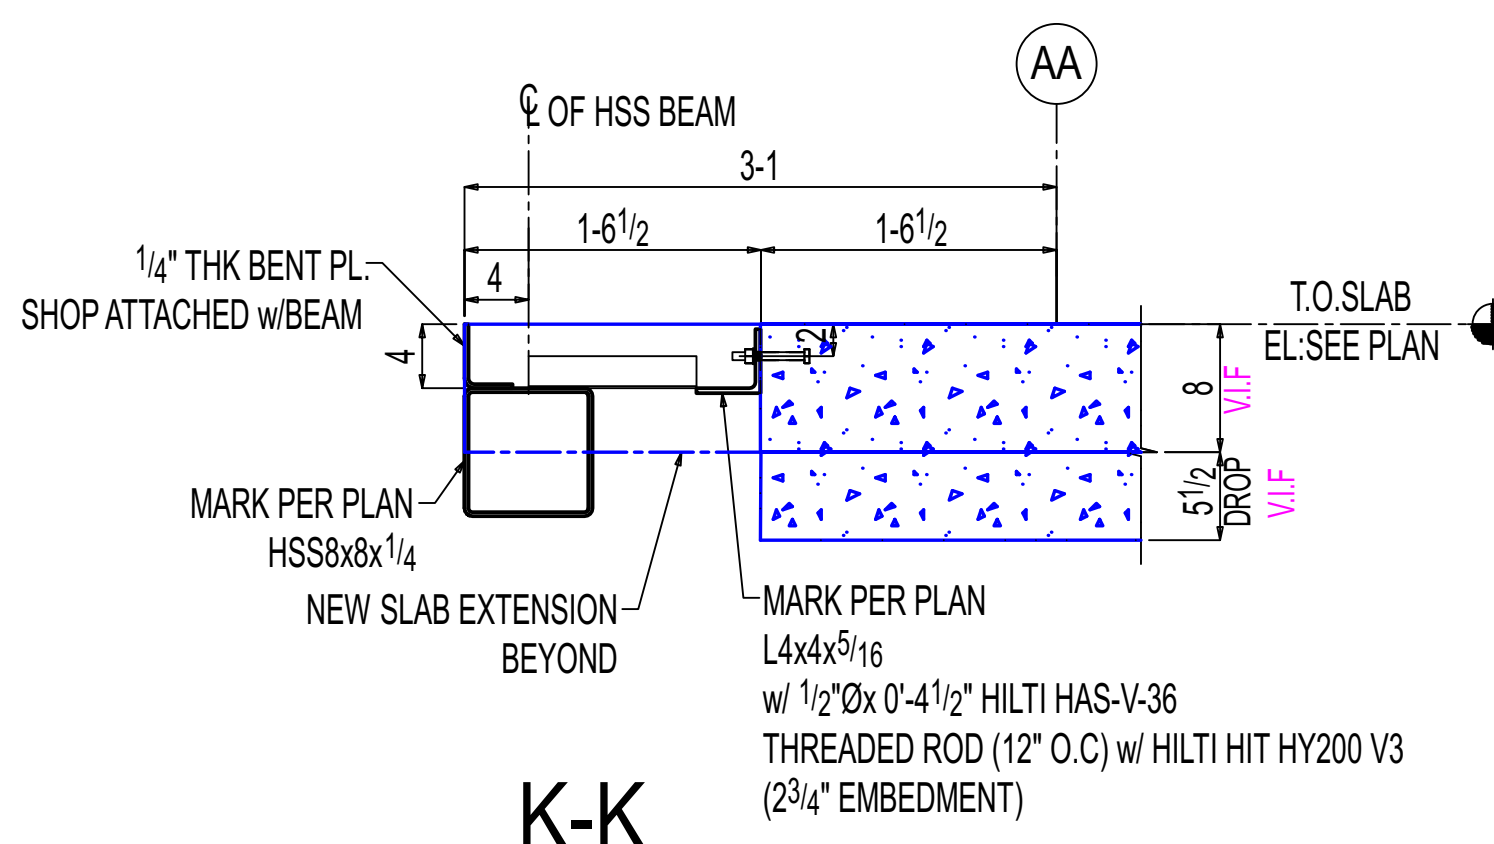

K-K

E-13.00A

(REF: 8/S315)

OTHERS NOT SHOWN FOR CLARITY

General Notes

- *Structural steel shall conform to ASTM-A992.
- *Structural SQR/RND.tubing conform to ASTM A500 Grade C
- *Pipe shall conform to ASTM A53, Grade B.
- *Channels, Angles and plates shall conform to A36.
- *All bolts shall be 3/4" High strength in accordance with ASTM A325 (UNO)
- *Welding Electrodes for Carbon steel :E70xx

# of Copies	Revision/ Issue	Destination	Date
4	0	For Construction	11-17-2025
3	C	For Re-Approval	10-24-2025
2	B	For Re-Approval	09-19-2025
1	A	For Approval	06-23-2025

IRON FABRICATION SERVICES, LLC.

3029 M. Street, NW, Suite 202
Washington, DC 20007
Tel: 202-800-5599
Fax: 202-478-0303

Project Name and Address

MARYLAND AVENUE

Location: **1250 MARYLAND AVENUE SW
WASHINGTON, DC 20024**

Contractor:

BALFOUR BEATTY

Approved for Fabrication by:

Signature

Contract

224009

Drawing

E-13.03

Contract Item:

**LEVEL-07
SLAB EXTENSION**

Ref:

SOW-13: 3,4,5&6 / S307

Date



01/ 20/ 2025

Scale

VARIES

Drawing Title:

**SOW #13 LEVEL-07 NEW
SLAB EXTENSION SUPPORT
SECTIONS**

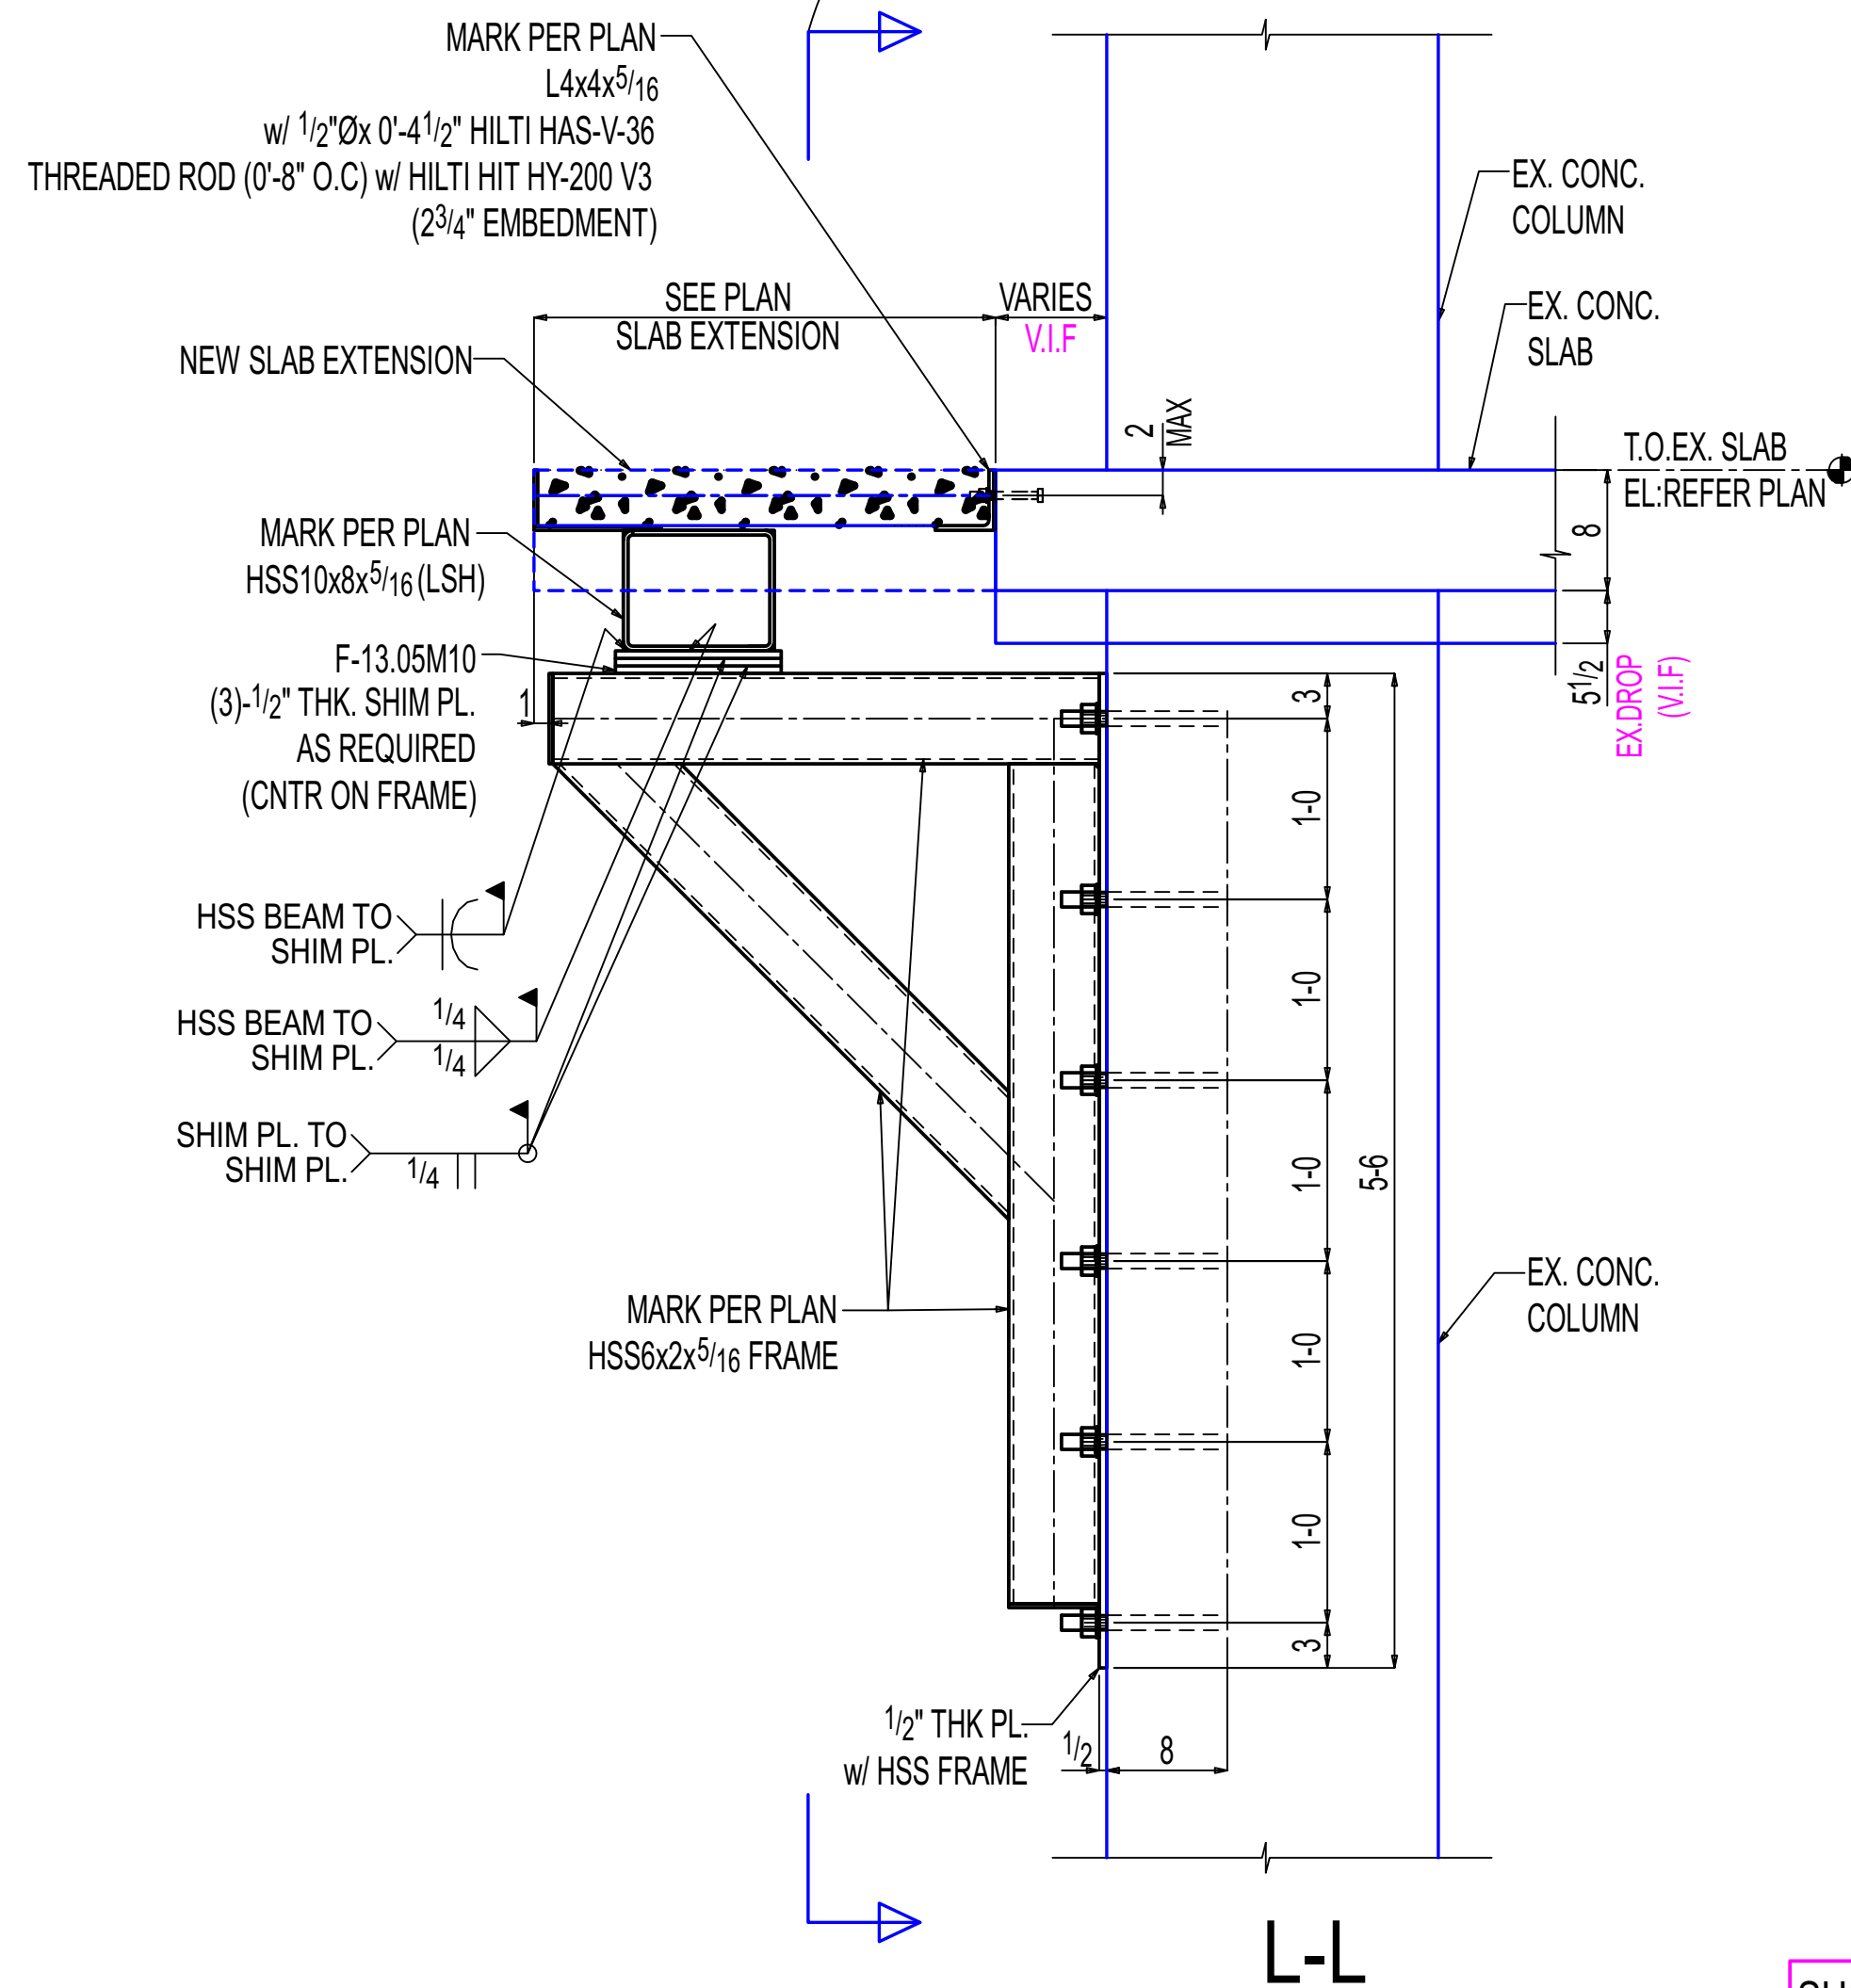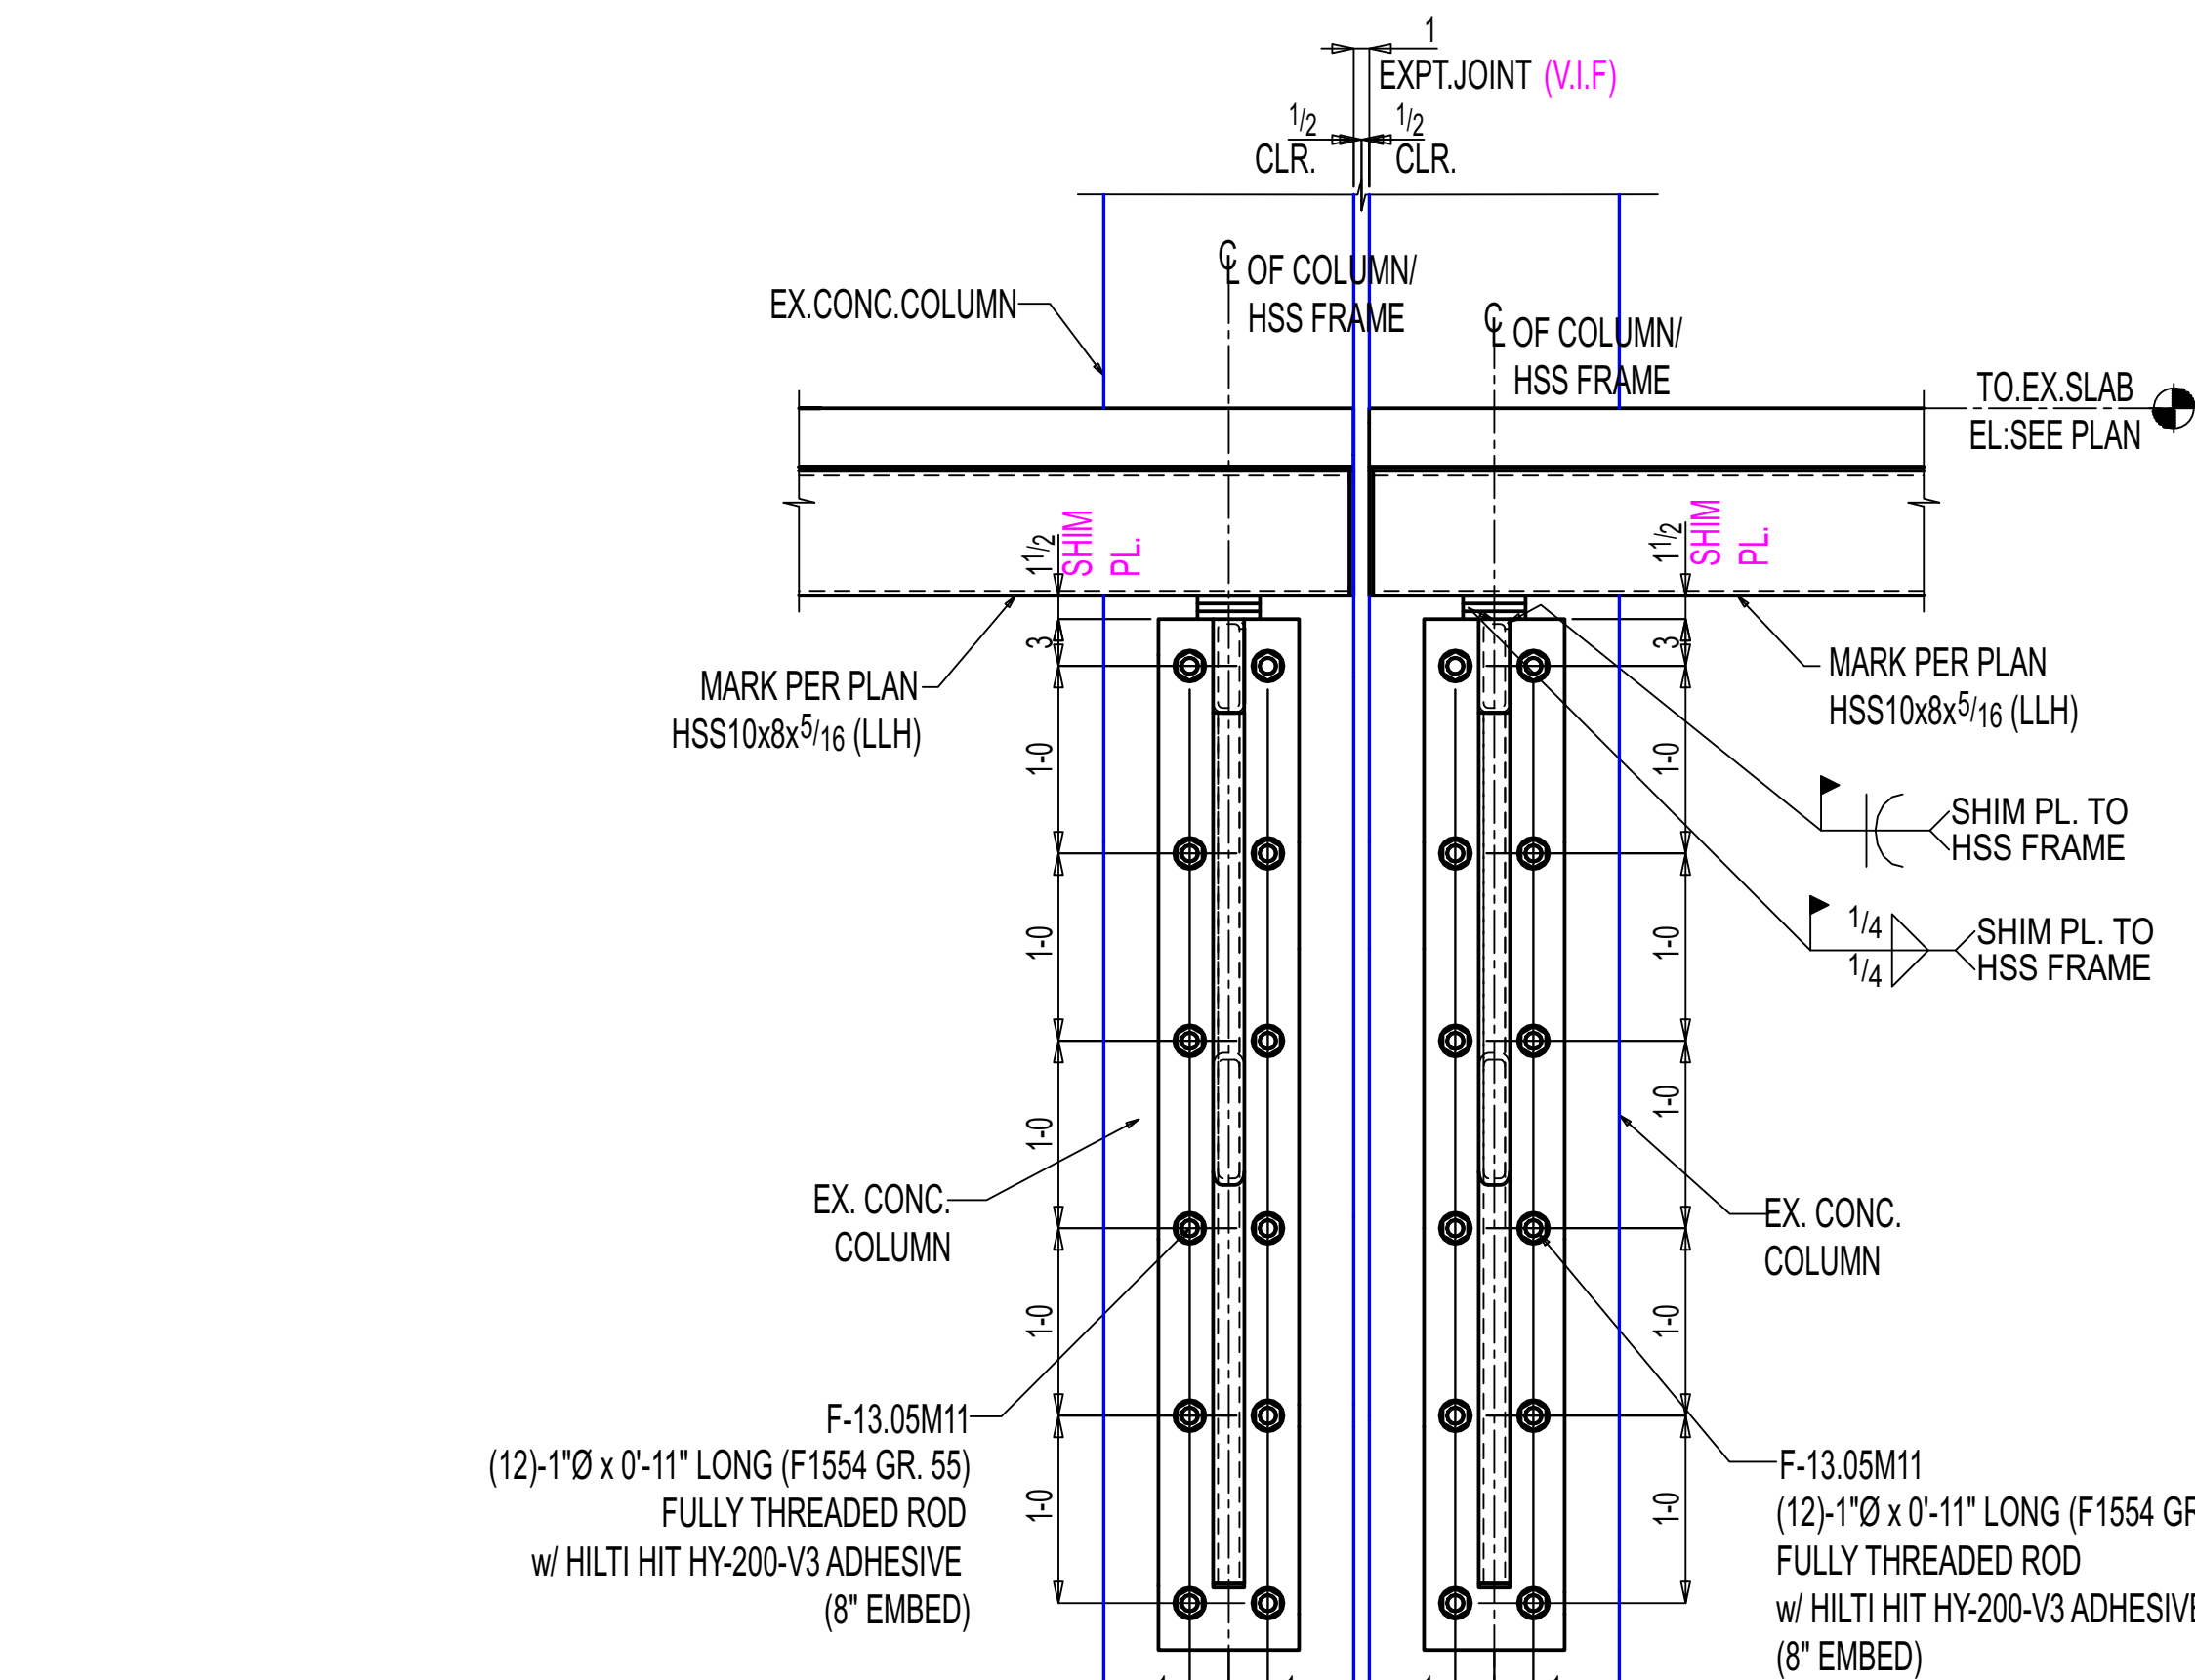


L-L

E-13.00A
(REF: 18/S205)

OTHERS NOT SHOWN FOR CLARITY


SHOP / ERECTOR NOTE:
LOCATE EXISTING REBAR PRIOR TO FABRICATION OF PLATE.
DO NOT DRILL THROUGH REBAR.

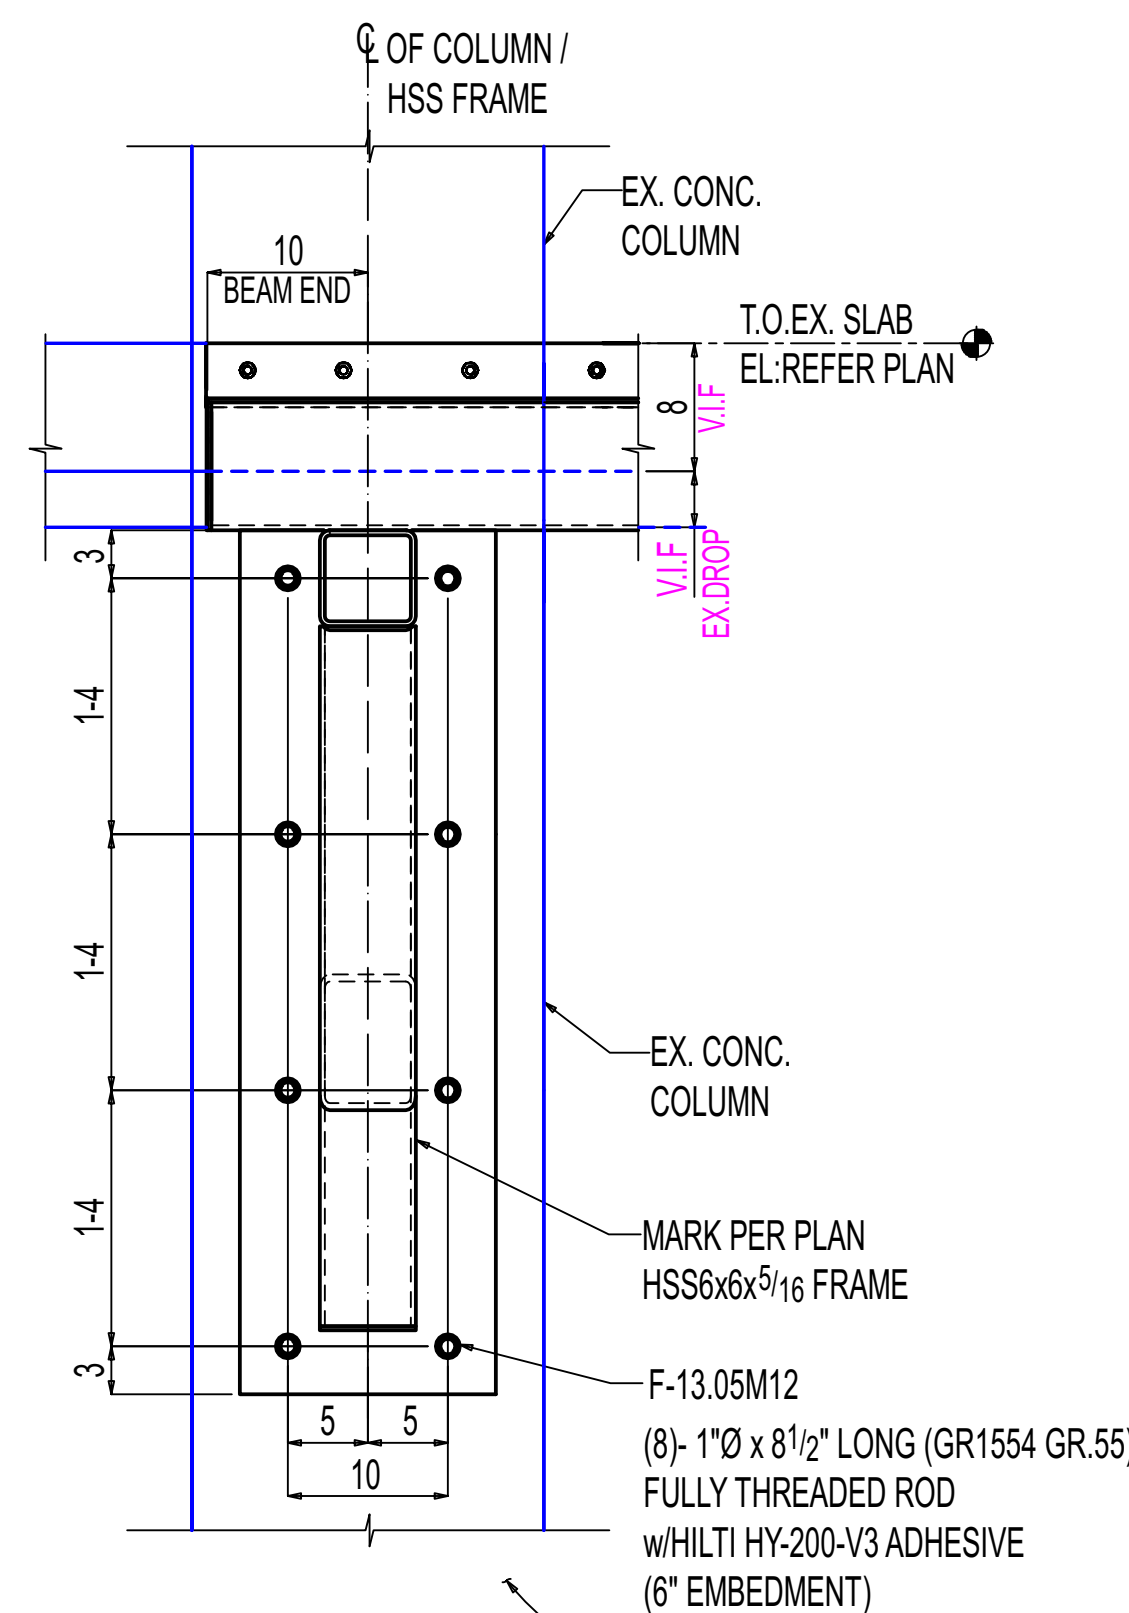

M-M

E-13.00A
(REF: 4/S316)


OTHERS NOT SHOWN FOR CLARITY

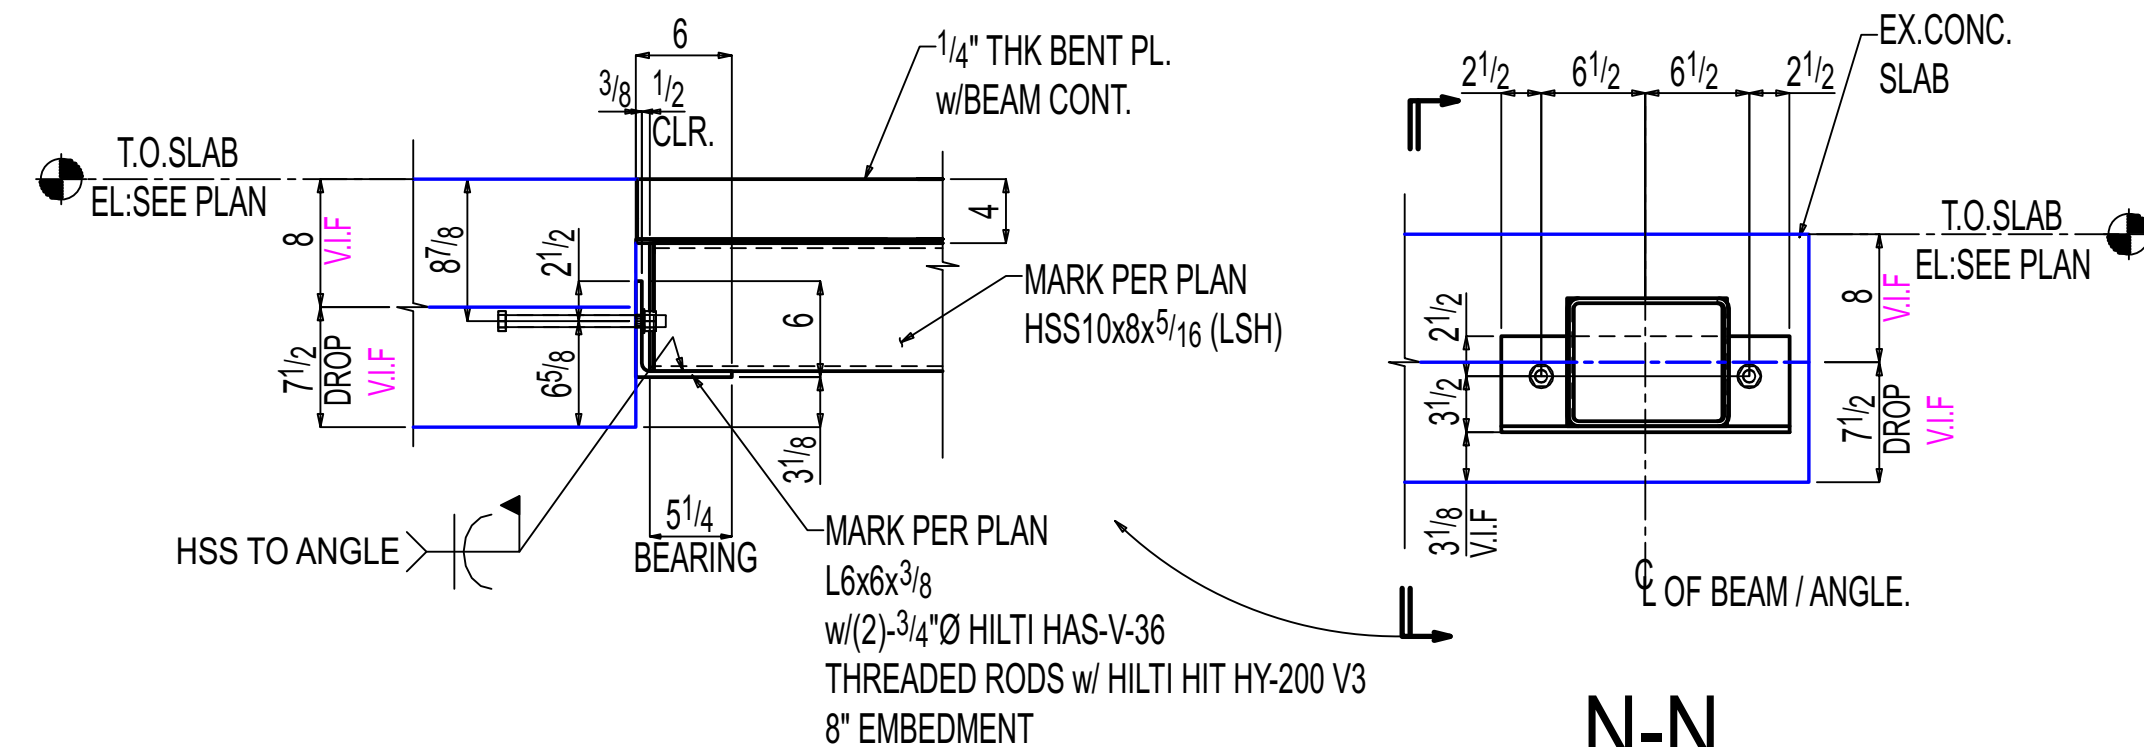

N-N

E-13.00A
(REF: 2 & 2A/S316)

OTHERS NOT SHOWN FOR CLARITY

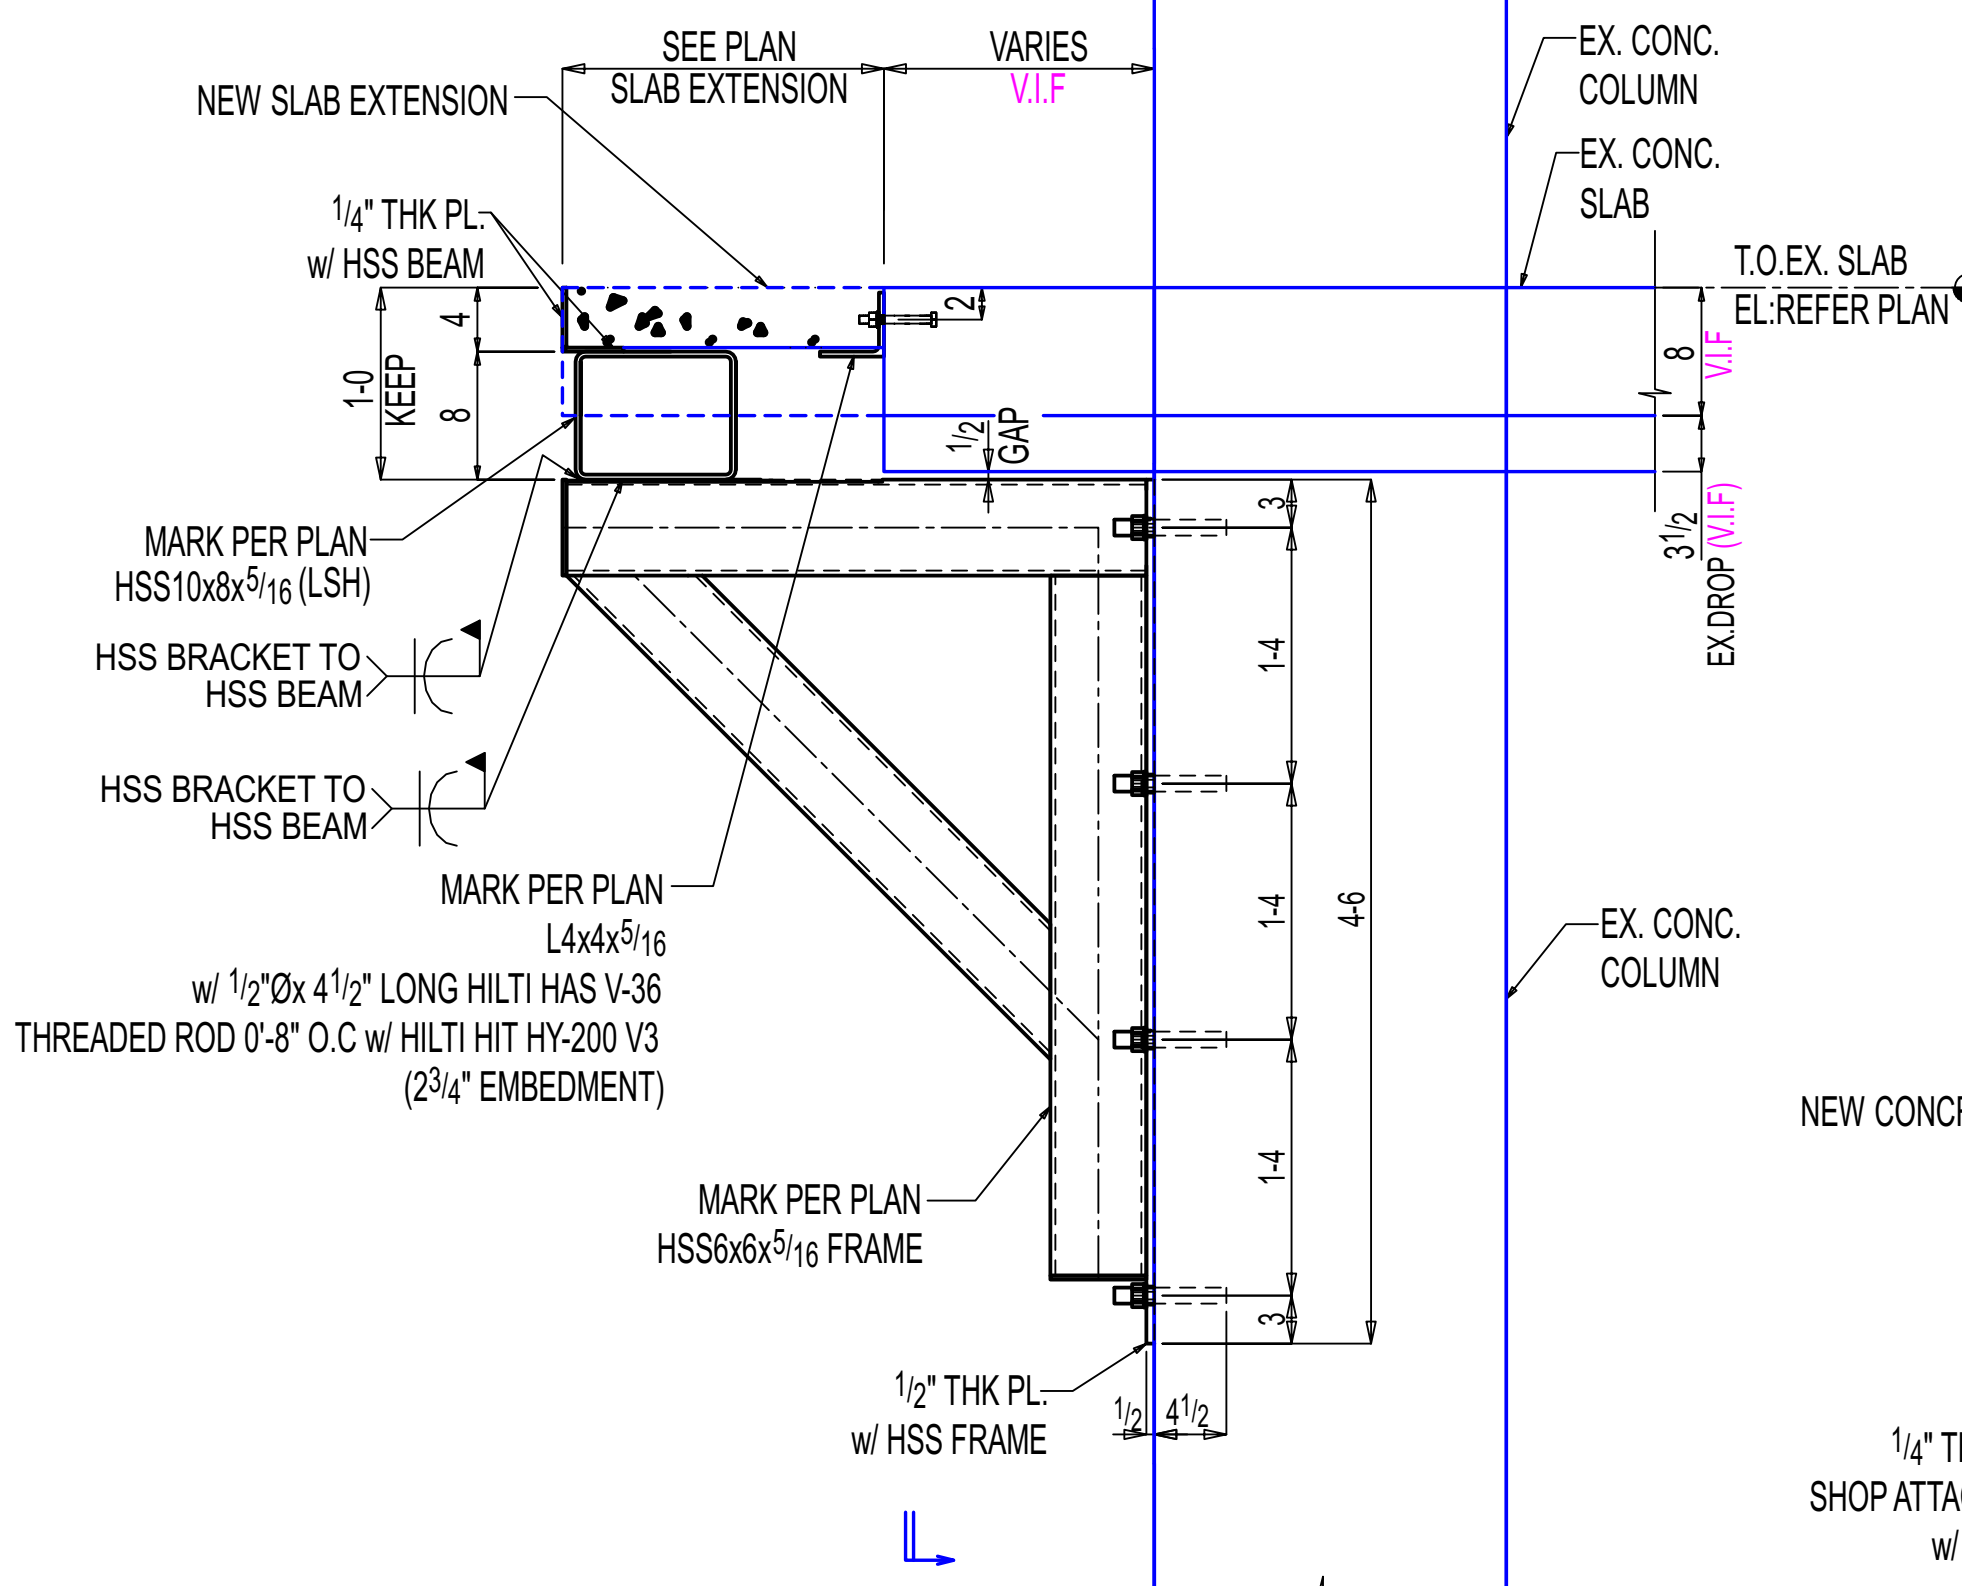

P-P

E-13.00A
(REF: 8/S315)

OTHERS NOT SHOWN FOR CLARITY

General Notes

- *Structural steel shall conform to ASTM-A992.
- *Structural SQR/RND.tubing conform to ASTM A500 Grade C
- *Pipe shall conform to ASTM A53, Grade B.
- *Channels, Angles and plates shall conform to A36.
- *All bolts shall be 3/4" High strength in accordance with ASTM A325 (UNO)
- *Welding Electrodes for Carbon steel :E70xx

# of Copies	Revision/ Issue	Destination	Date
3	0	For Construction	11-17-2025
2	B	For Re-Approval	10-24-2025
1	A	For Approval	09-19-2025

IRON FABRICATION SERVICES, LLC.

3029 M. Street, NW, Suite 202
Washington, DC 20007
Tel: 202-800-5599
Fax: 202-478-0303

Project Name and Address

MARYLAND AVENUE
Location: **1250 MARYLAND AVENUE SW**
WASHINGTON, DC 20024

Contractor:

BALFOUR BEATTY

Approved for Fabrication by:

Signature

Contract

224009

Drawing

E-13.04

Contract Item:

LEVEL-07
SLAB EXTENSION

Ref:

SOW-13: 3,4,5&6 / S307

Date


01/20/2025

Scale

VARIES

Drawing Title:

SOW #13 LEVEL-07 NEW
SLAB EXTENSION SUPPORT
SECTIONS

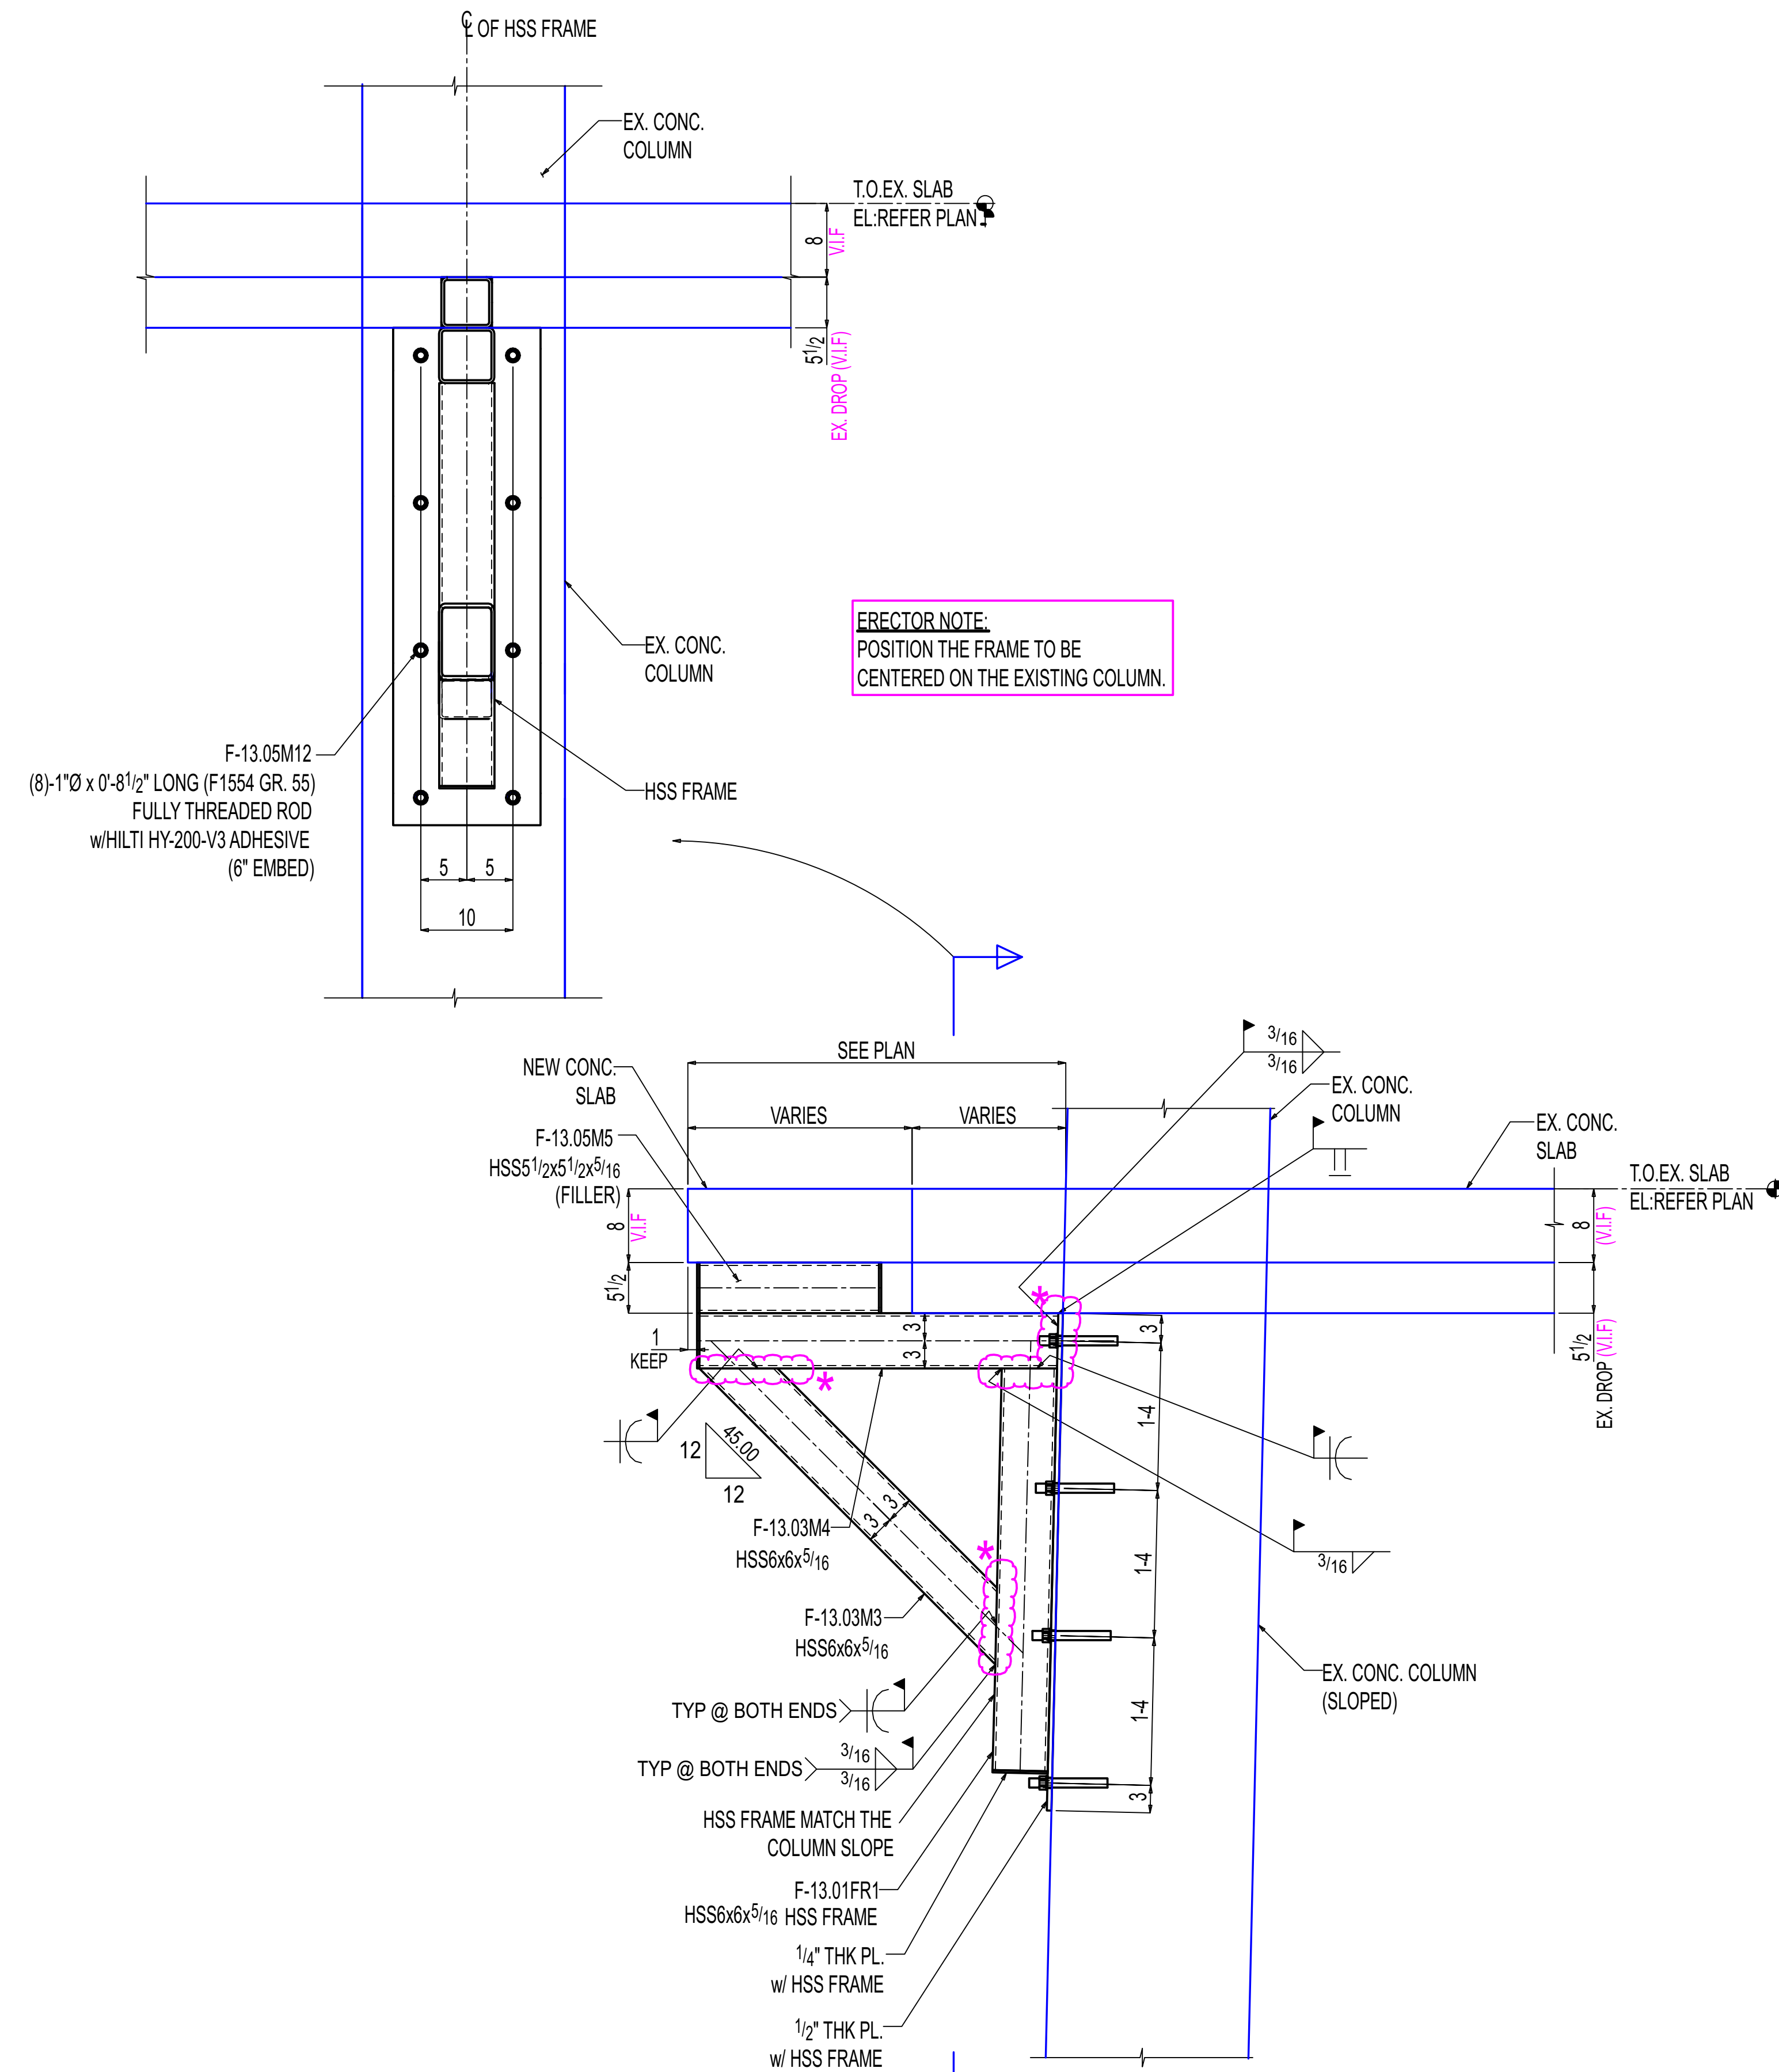

*-ERECTOR NOTE:
FIELD CUT HSS6x6x ENDS TO SUIT AT EXISTING COLUMN SLOPE.

OTHERS NOT SHOWN FOR CLARITY

SHOP / ERECTOR NOTE:
LOCATE EXISTING REBAR PRIOR TO FABRICATION OF PLATE.
DO NOT DRILL THROUGH REBAR.

General Notes

- *Structural steel shall conform to ASTM-A992.
- *Structural SQR/RND.tubing conform to ASTM A500 Grade C
- *Pipe shall conform to ASTM A53, Grade B.
- *Channels, Angles and plates shall conform to A36.
- *All bolts shall be 3/4" High strength in accordance with ASTM A325 (UNO)
- *Welding Electrodes for Carbon steel :E70xx

# of Copies	Revision/ Issue	For Construction Destination	11-17-2025 Date
1	0		

IRON FABRICATION SERVICES, LLC.

3029 M. Street, NW, Suite 202
Washington, DC 20007
Tel: 202-800-5599
Fax: 202-478-0303

Project Name and Address

MARYLAND AVENUE

Location: **1250 MARYLAND AVENUE SW
WASHINGTON, DC 20024**

Contractor:

BALFOUR BEATTY

Approved for Fabrication by:

Signature

Contract # **224009**

Drawing # **E-13.05**

Contract Item: **LEVEL-07
SLAB EXTENSION**

Ref: **SOW-13: 3,4,5&6 / S307**

Date

01/ 20/ 2025

Scale

VARIES

Drawing Title:

**SOW #13 LEVEL-07 NEW
SLAB EXTENSION SUPPORT
SECTIONS**