

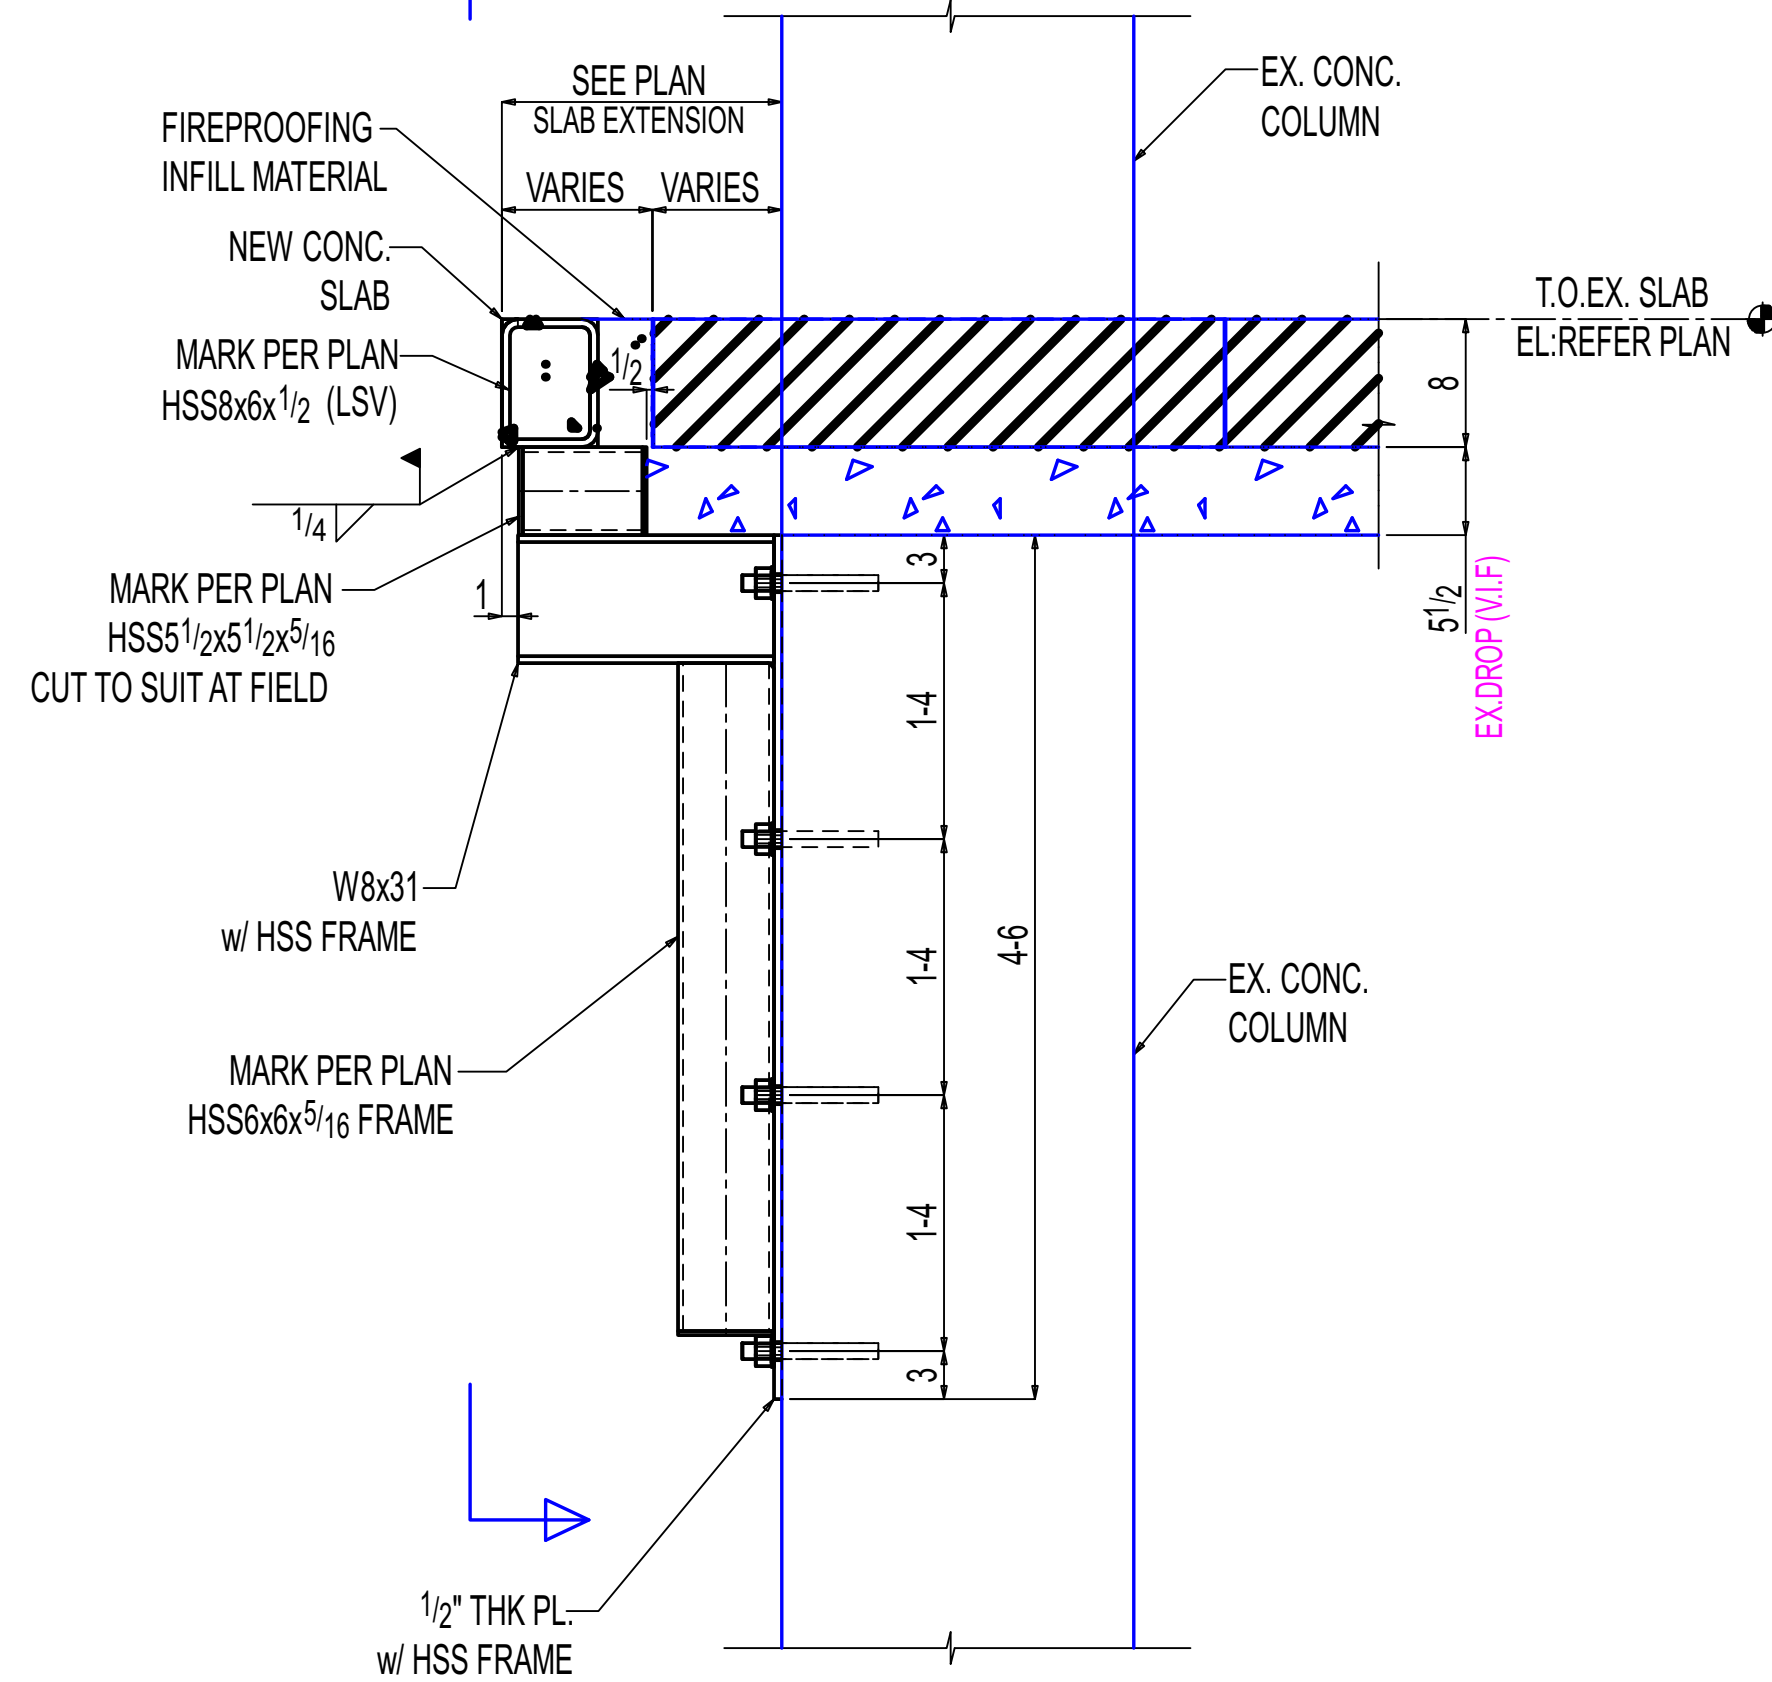


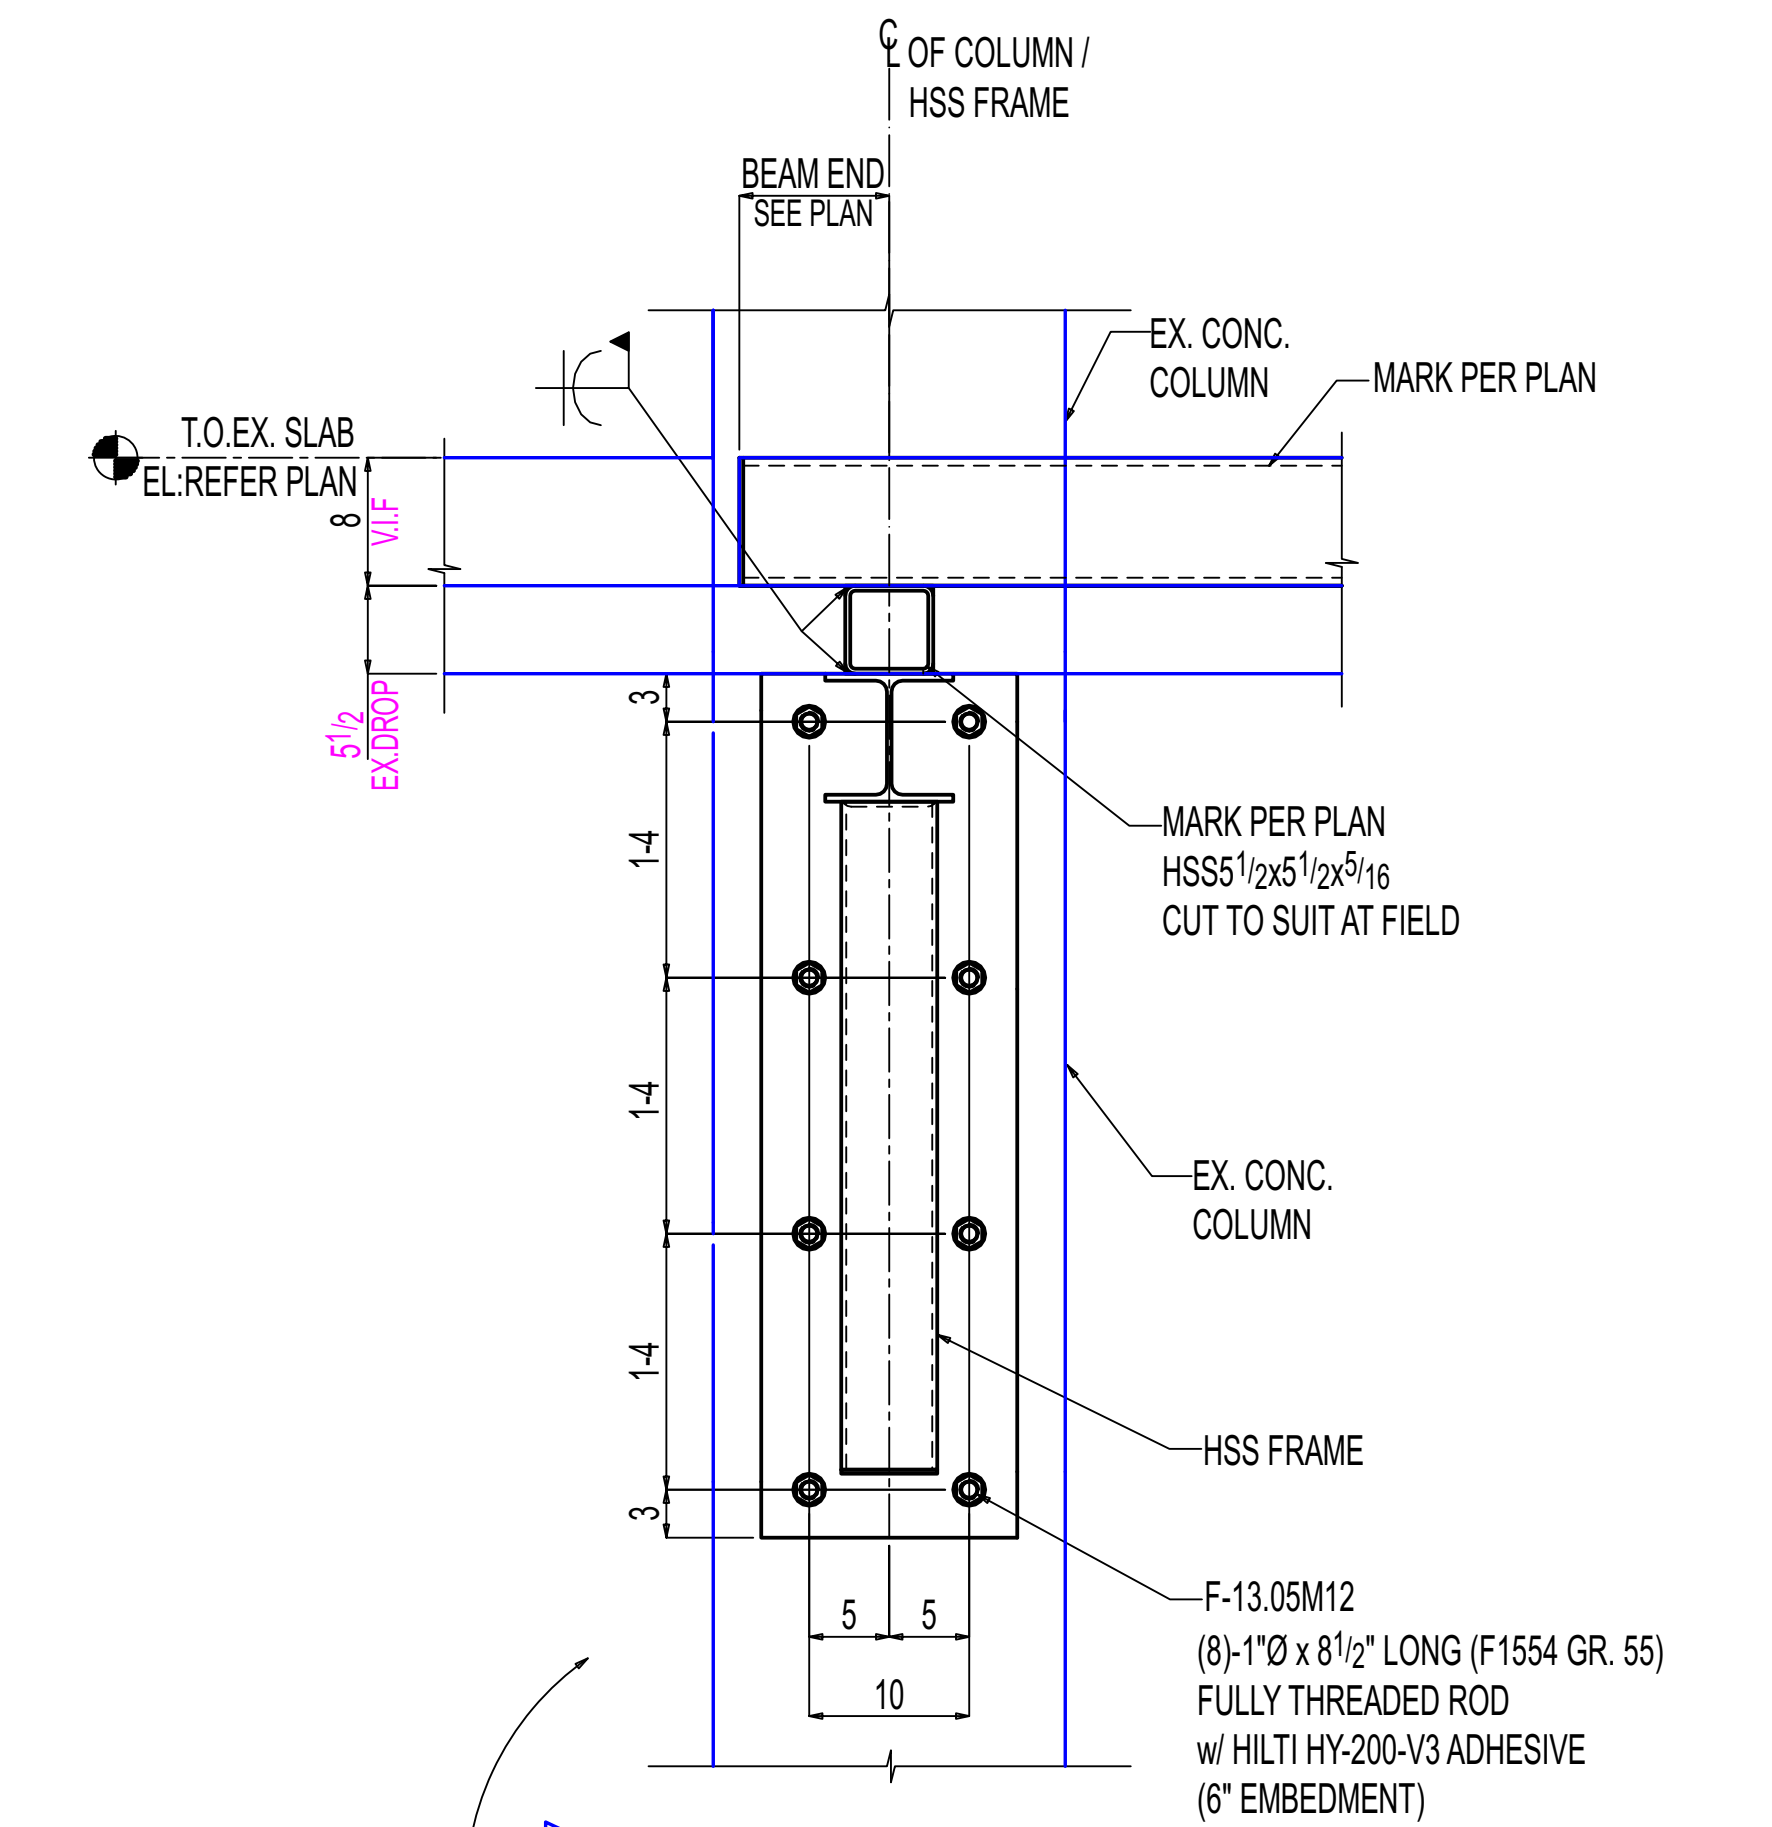


**D-D**  
( NEW SLAB EXTENSION SUPPORT  
@ SLAB DROP LOCATION NEW SLAB EXTENSION BETWEEN 1'-0" TO 1'-6" )  
E-13.00  
(REF:10 & 11/S314)  
OTHERS NOT SHOWN FOR CLARITY

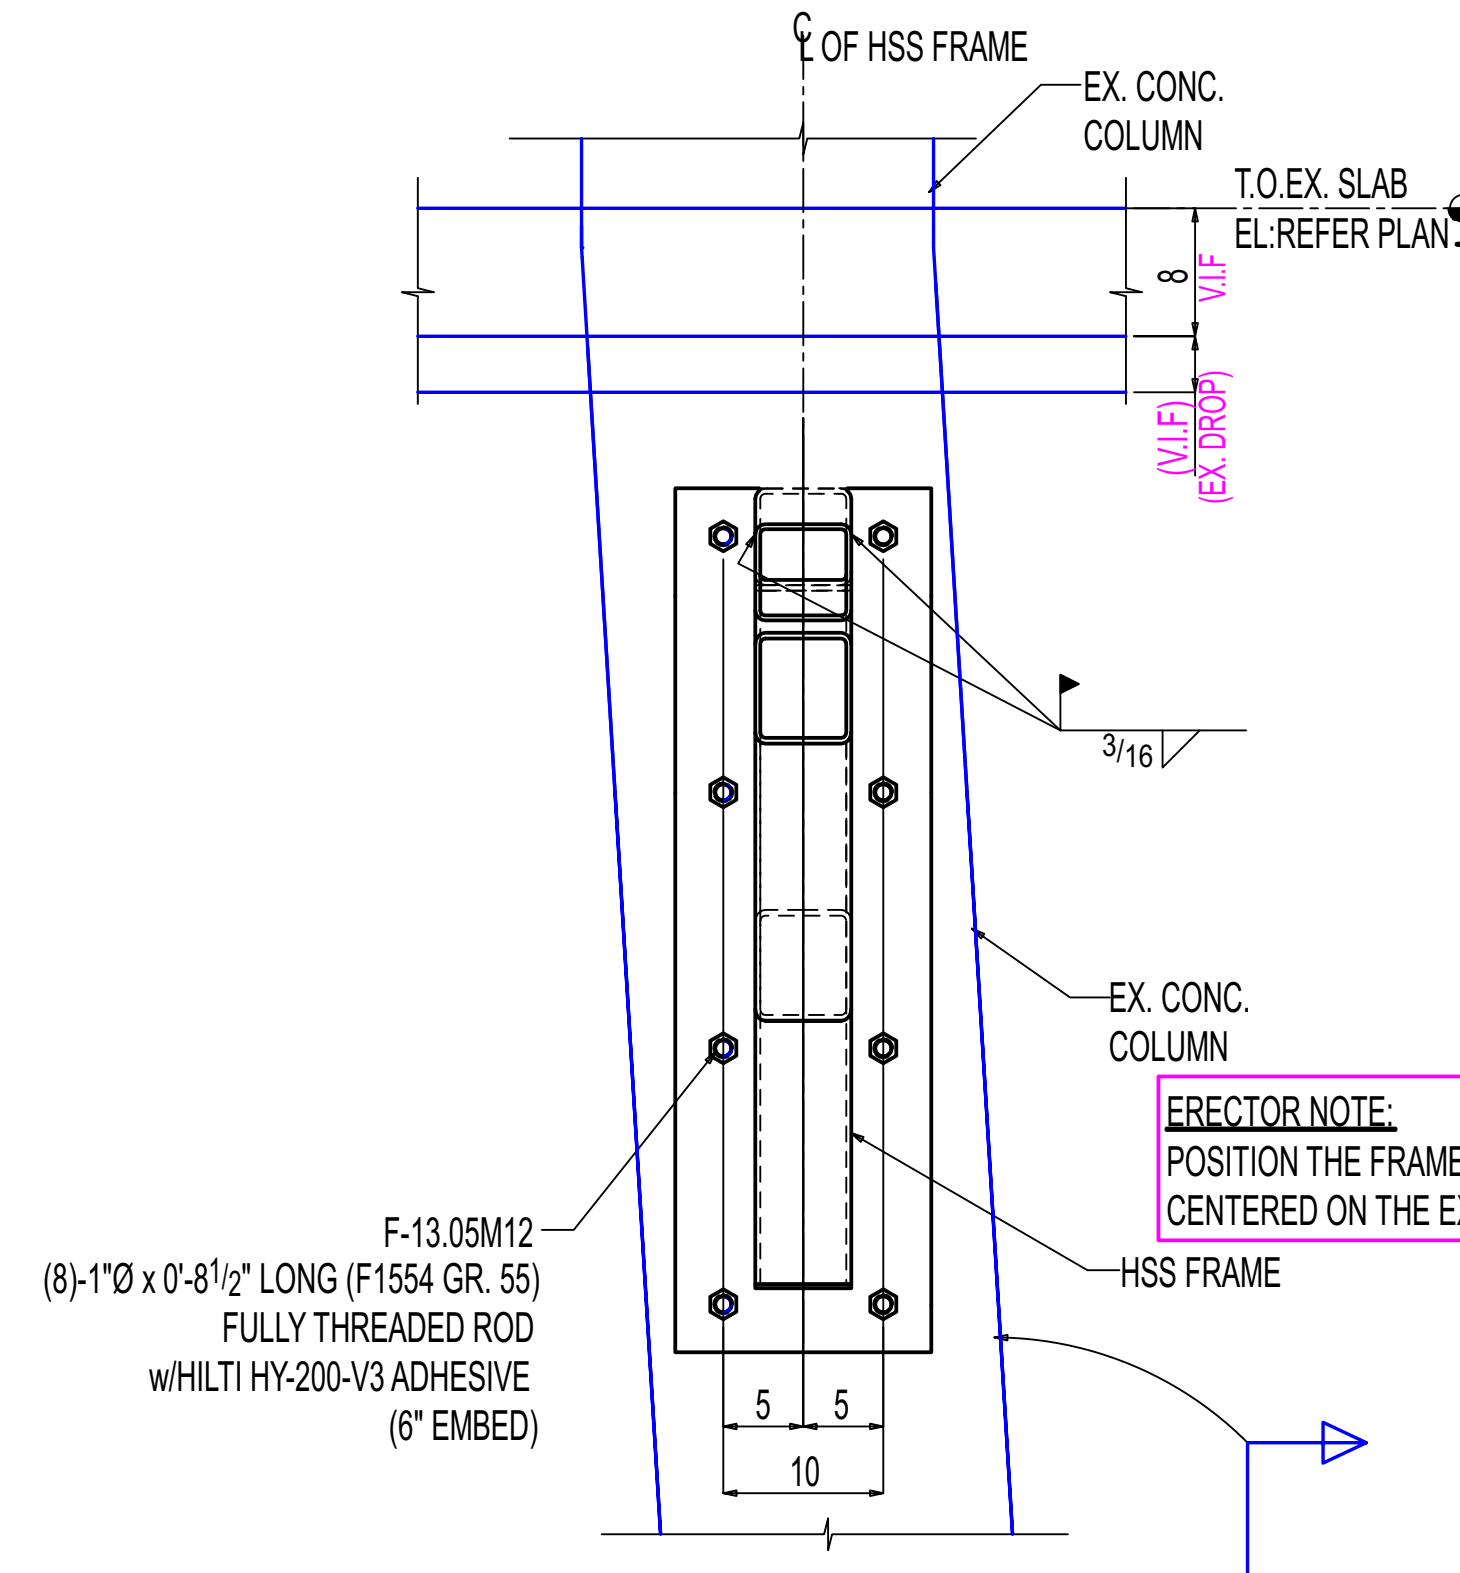

**\* -ERECTOR NOTE:**  
FIELD CUT HSS6x6 ENDS TO SUIT AT EXISTING COLUMN SLOPE.

**ERECTOR NOTE:**  
POSITION THE FRAME TO BE  
CENTERED ON THE EXISTING COLUMN.

**ERECTOR NOTE:**  
1"NSx6" WIDTH GROUT @ PRECAST BEARING POINT ONLY  
CO-ORDINATE BEARING POINT LOCATION WITH  
PRECAST MANUFACTURER.

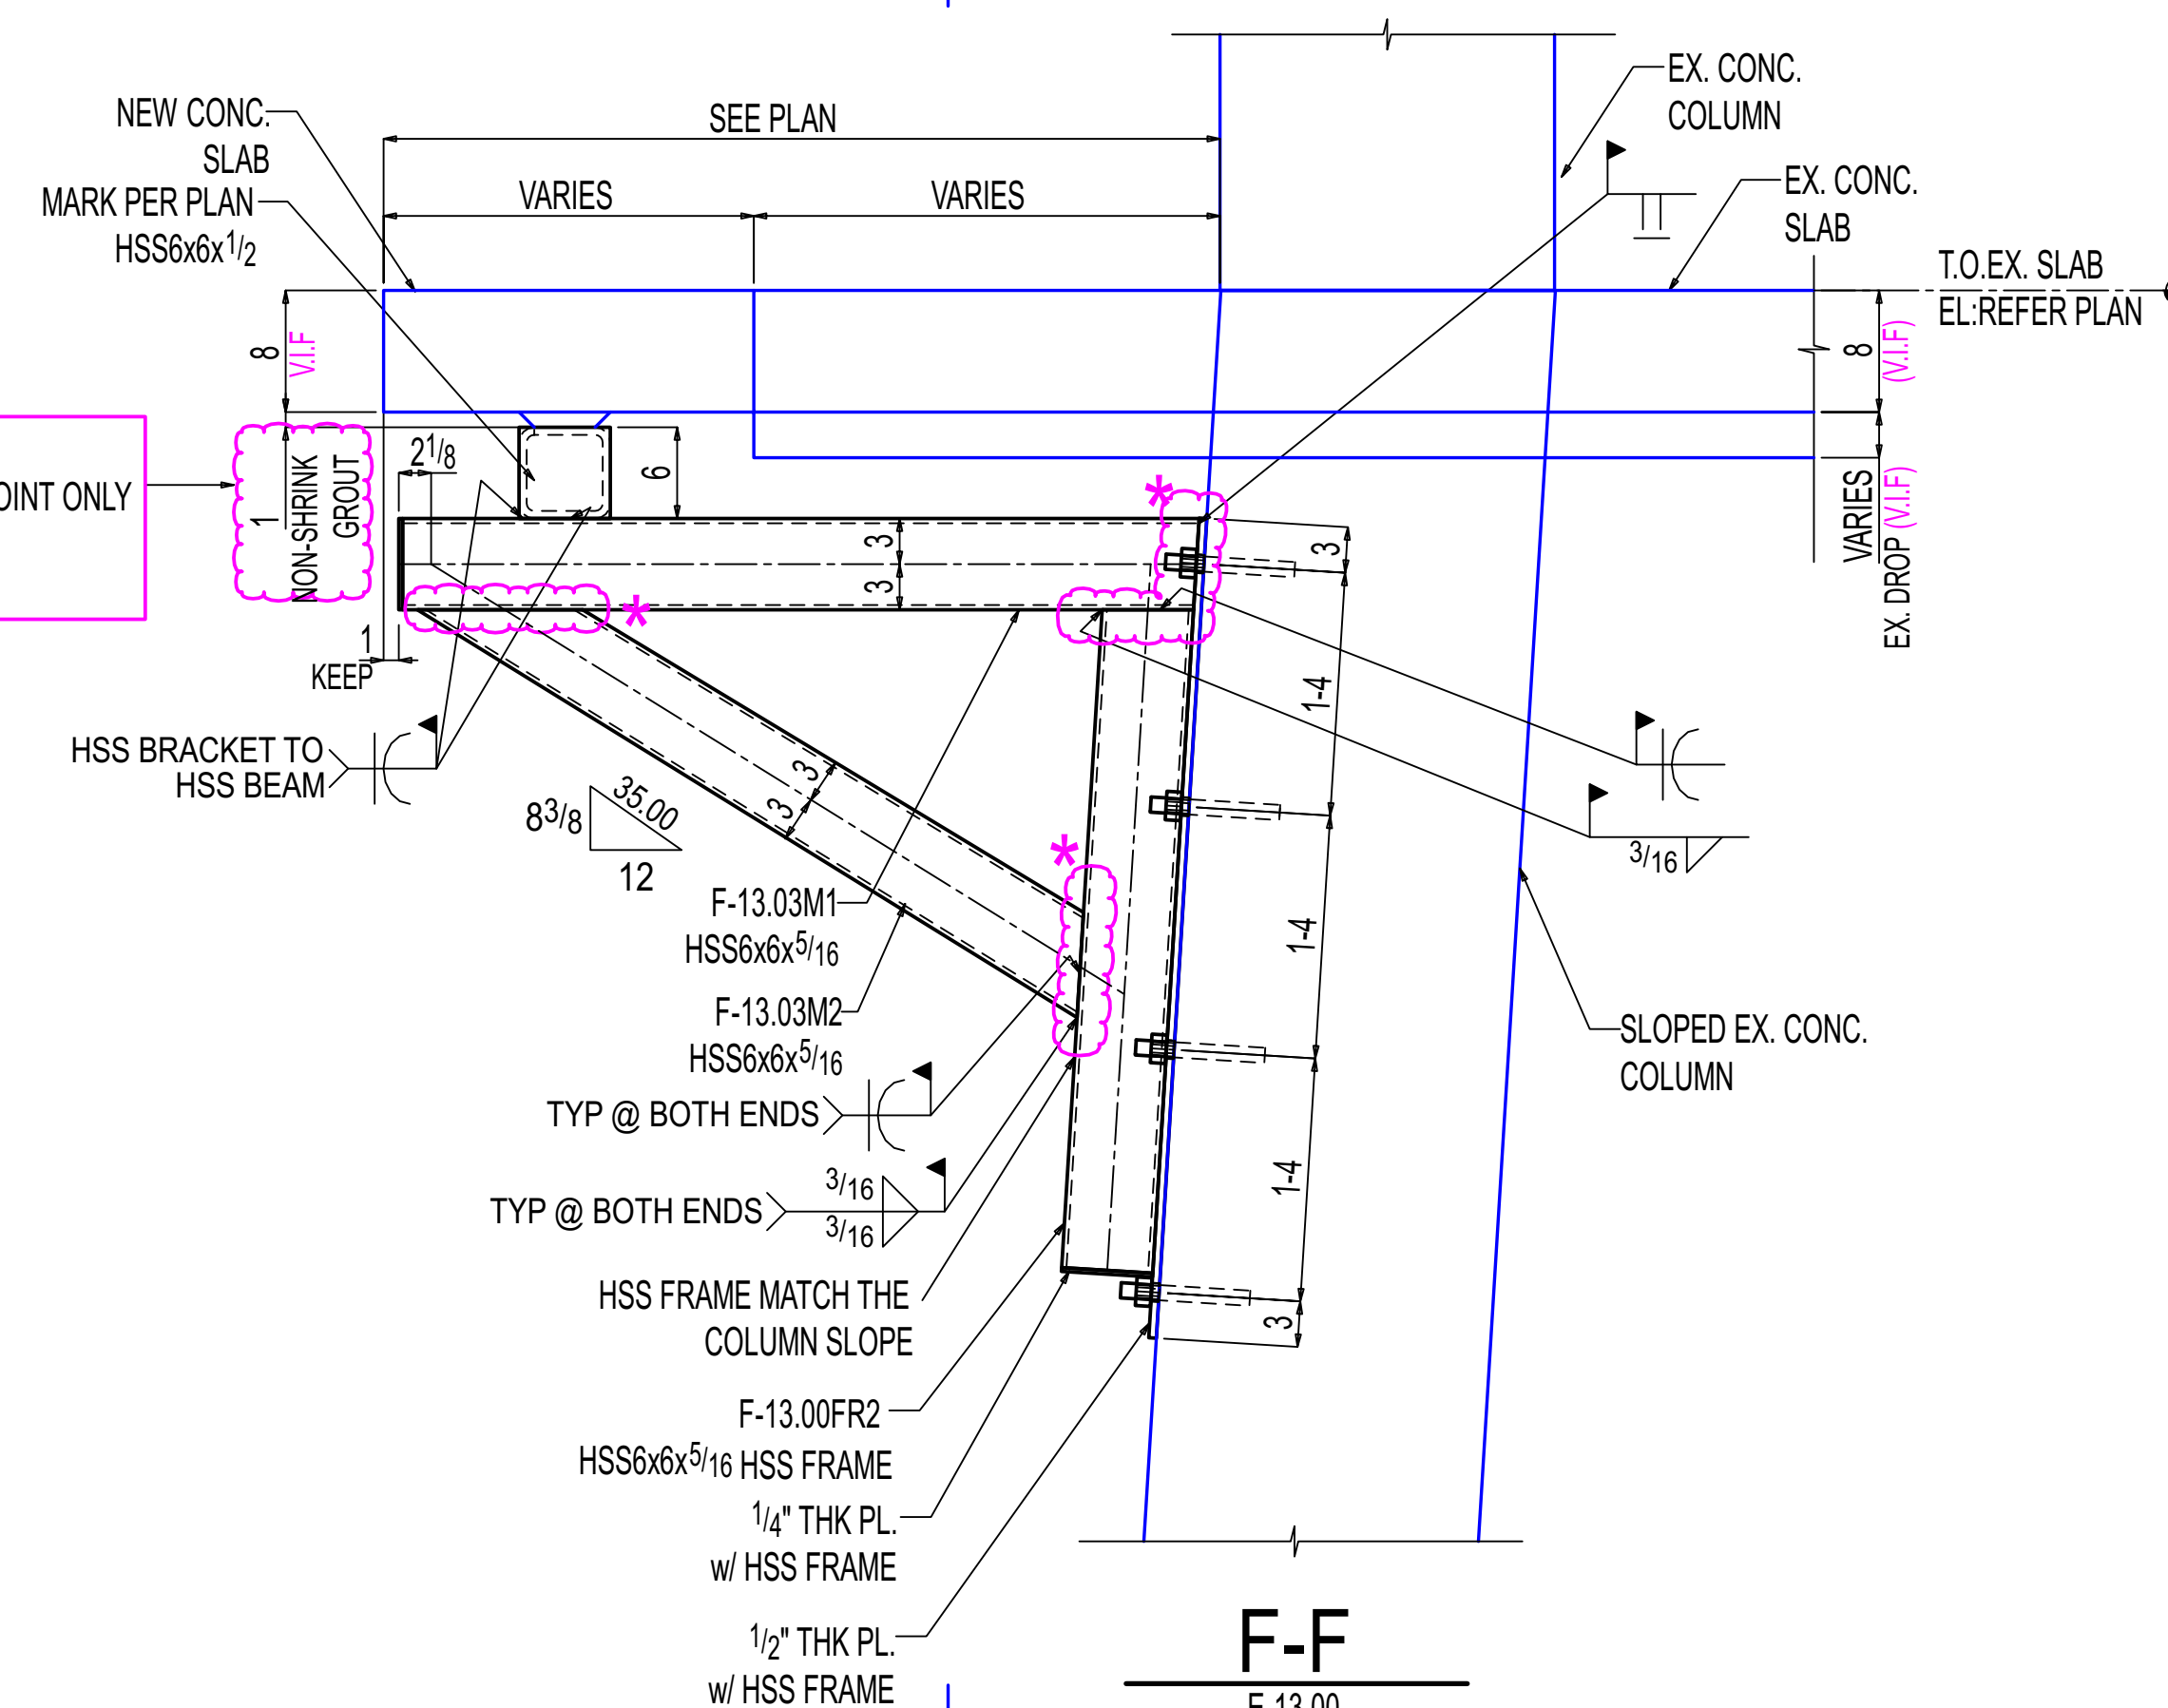

**F-F**  
E-13.00  
(REF: 9/S315)  
OTHERS NOT SHOWN FOR CLARITY

**SHOP / ERECTOR NOTE:**  
LOCATE EXISTING REBAR PRIOR TO FABRICATION OF PLATE.  
DO NOT DRILL THROUGH REBAR.

#### General Notes

- \*Structural steel shall conform to ASTM-A992.
- \*Structural SQR/RND.tubing conform to ASTM A500 Grade C
- \*Pipe shall conform to ASTM A53, Grade B.
- \*Channels, Angles and plates shall conform to A36.
- \*All bolts shall be 3/4" High strength in accordance with ASTM A325 (UNO)
- \*Welding Electrodes for Carbon steel :E70xx

| # of Copies | Revision/ Issue | Destination      | Date       |
|-------------|-----------------|------------------|------------|
| 5           | 0               | For Construction | 11-17-2025 |
| 4           | D               | For Re-Approval  | 10-24-2025 |
| 3           | C               | For Re-Approval  | 09-19-2025 |
| 2           | B               | For Re-Approval  | 06-23-2025 |
| 1           | A               | For Approval     | 02-25-2025 |

#### IRON FABRICATION SERVICES, LLC.

3029 M. Street, NW, Suite 202  
Washington, DC 20007  
Tel: 202-800-5599  
Fax: 202-478-0303

Project Name and Address  
**MARYLAND AVENUE**

Location: **1250 MARYLAND AVENUE SW  
WASHINGTON, DC 20024**

Contractor:  
**BALFOUR BEATTY**

Approved for Fabrication by: Signature

Contract # **224009** Drawing # **E-13.02**

Contract Item: **LEVEL-07  
SLAB EXTENSION**

Ref: **SOW-13: 3,4,5&6 / S307**

Date  
**01/20/2025**  
Scale  
**VARIES**  
Drawing Title:  
**SOW #13 LEVEL-07 NEW  
SLAB EXTENSION SUPPORT  
SECTIONS**