


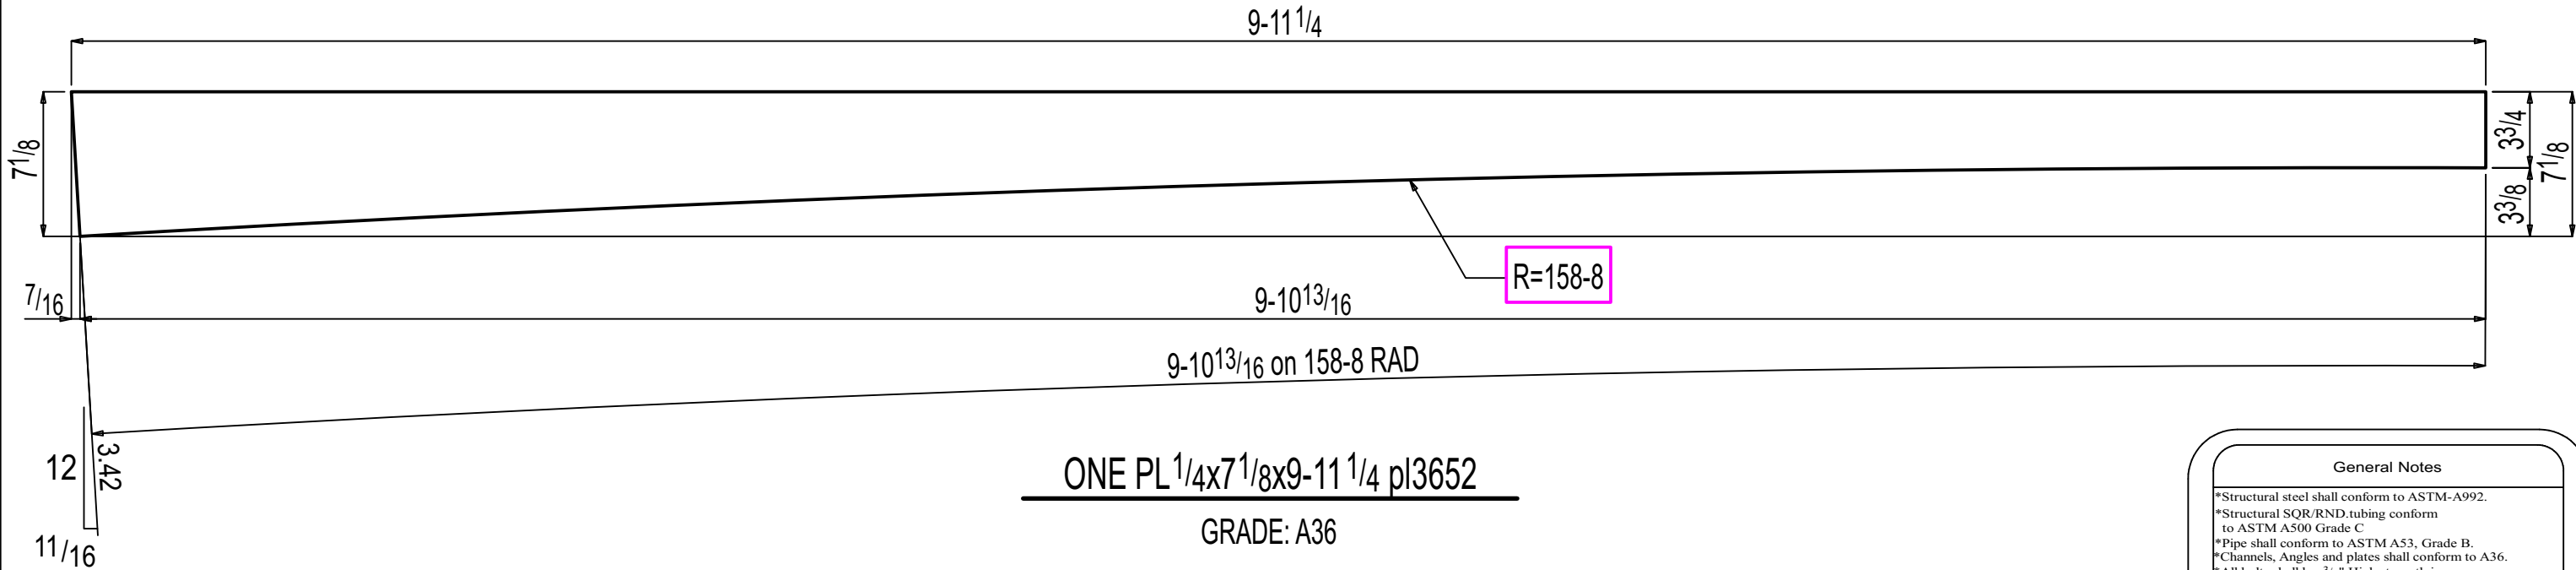

General Notes

- *Structural steel shall conform to ASTM-A992.
- *Structural SQR/RND.tubing conform to ASTM A500 Grade C
- *Pipe shall conform to ASTM A53, Grade B.
- *Channels, Angles and plates shall conform to A36.
- *All bolts shall be 3/4" High strength in accordance with ASTM A325 (UNO)
- *Welding Electrodes for Carbon steel :E70xx
- *Structural members are to be shop primer (U.N.O).
- *Surface Preparation-SSPC-SP3 UNO.
- *If welds exposed to view, should be ground smooth.

1	0	FOR FABRICATION	11-17-2025
# of Copies	Revision/ Issue	Destination	Date

IRON FABRICATION SERVICES, LLC.

3029 M. Street, NW, Suite 202
Washington, DC 20007
Tel: 202-800-5599
Fax: 202-478-0303

Project Name and Address

MARYLAND AVENUE

Location: 1250 MARYLAND AVENUE SW
WASHINGTON, DC 20024

Contractor:

BALFOUR BEATTY

Approved for Fabrication by: Signature

Contract # 224009 Drawing # pl3652

Contract Item: PLATE

Ref:
SOW -13:F-13.00-F-13.05

Date
01/ 23/ 2025 Drawing Title:
PLATE

Scale
VARIES

HOLE:13/16 Ø (U.N.O)