
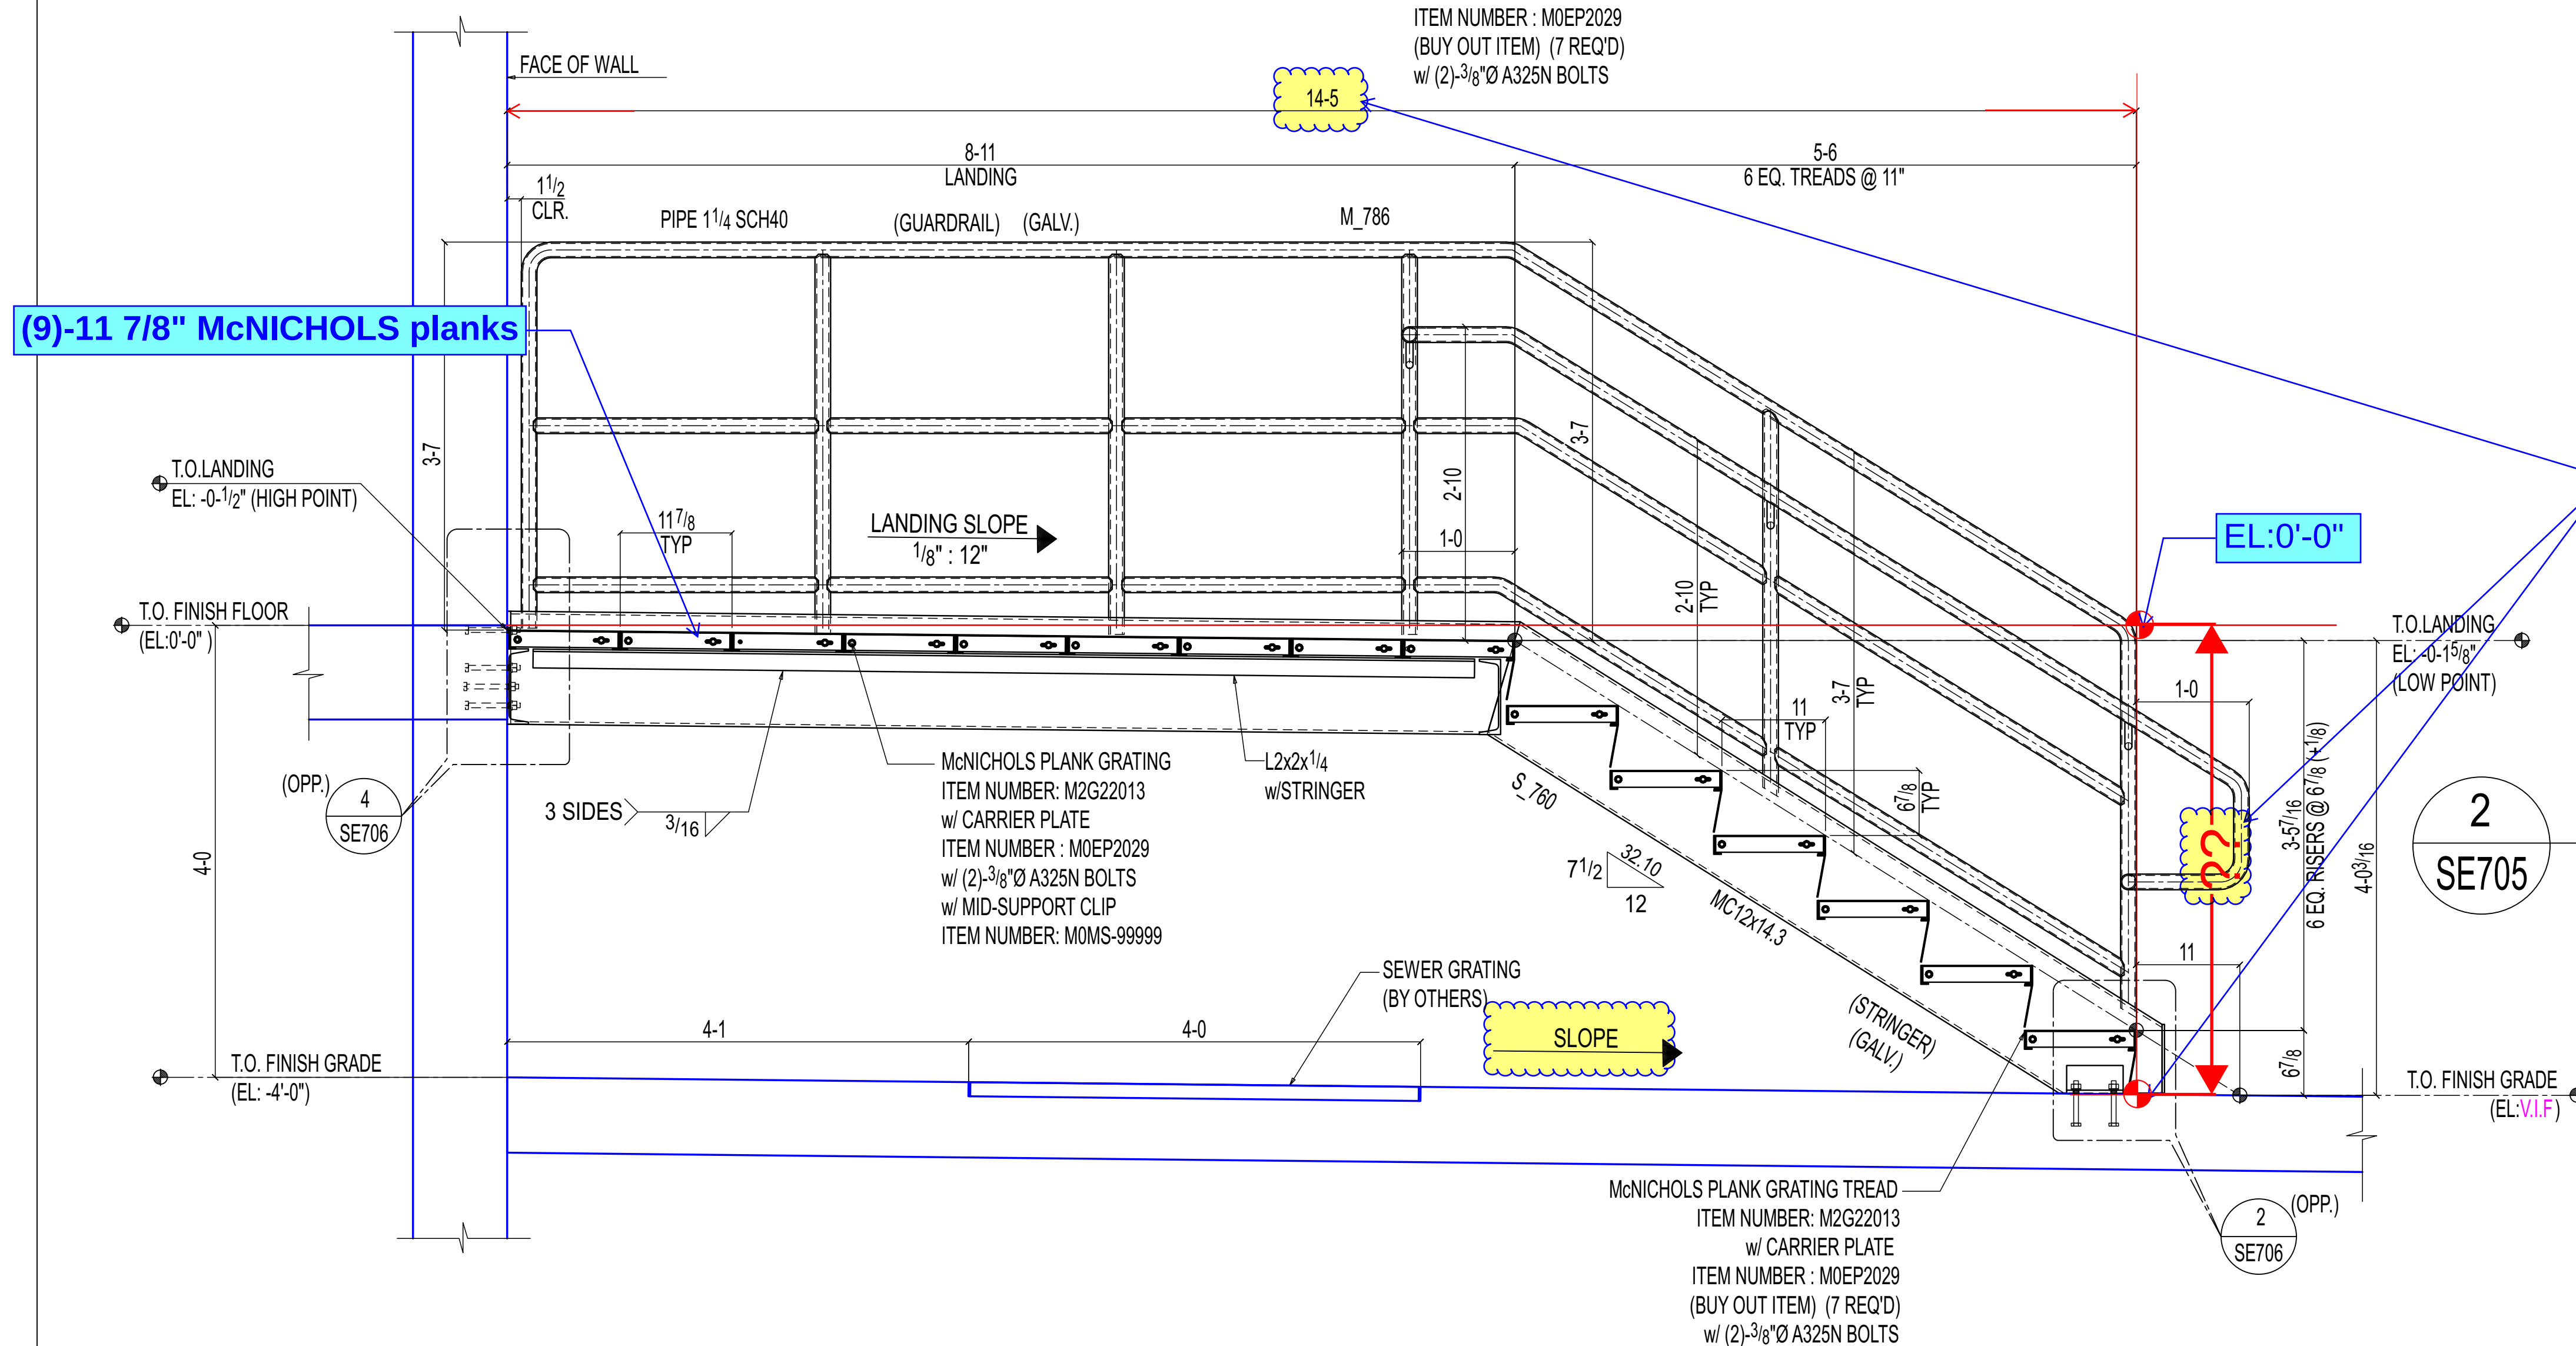


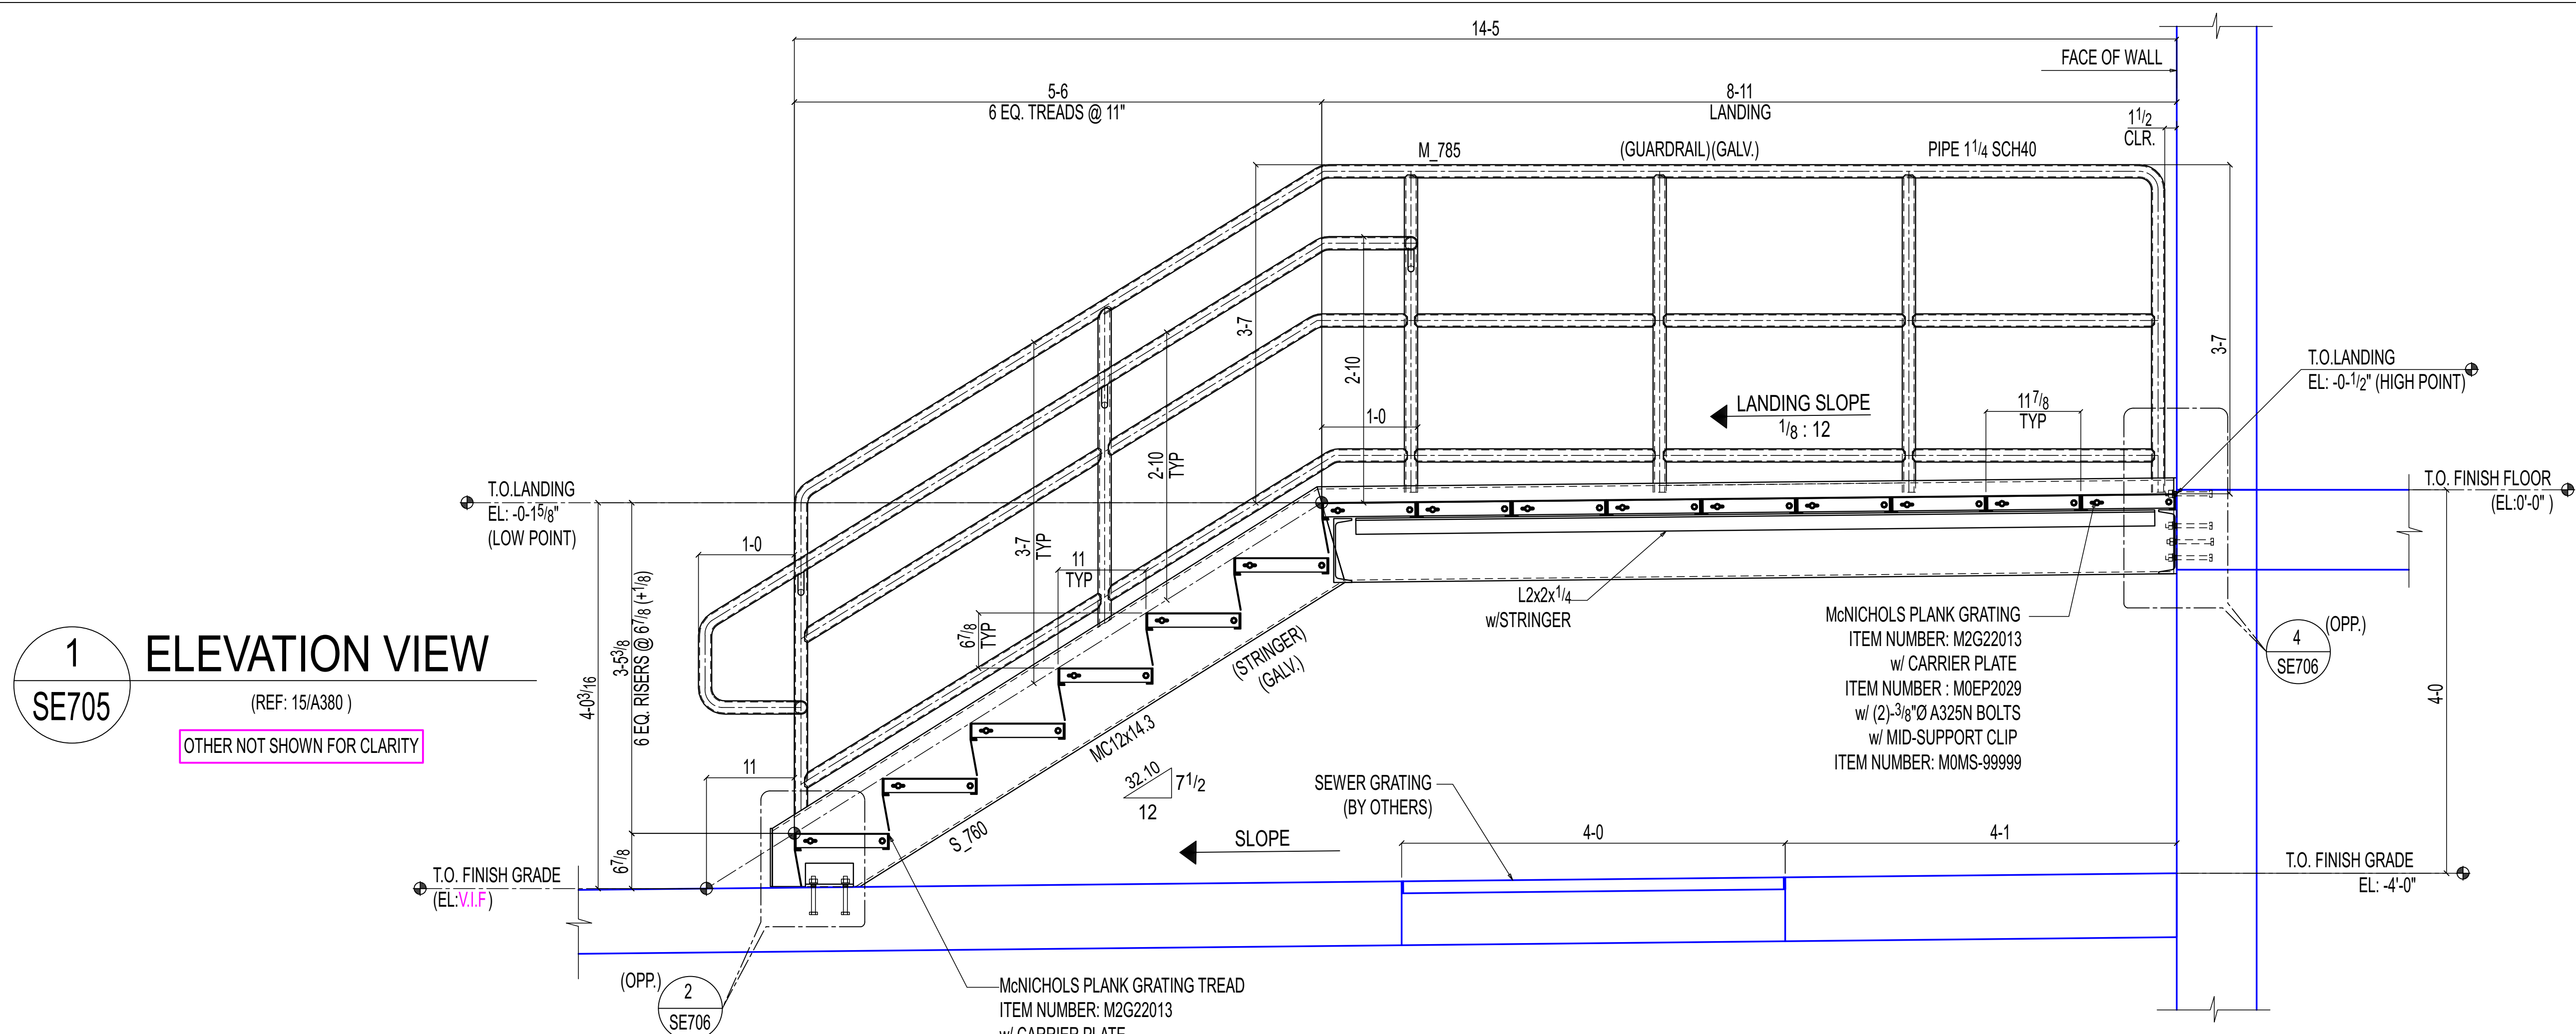


ERECTOR NOTE:

1. WIRE BRUSH GALVANIZED SURFACE AS REQUIRED FOR WELDING.
2. TOUCHUP ALL FIELD WELDS WITH ZINC RICH PAINT (U.N.O)

Q1


we have followed (9) qty of 11 7/8" wide planks and increased the landing length (8'-11").
Also, We need the top of slab elevation at the yellow clouded location which is 14'-5" far from the face of wall as marked, then only Connection team can able to re-design.

Please get the elevation ASAP.

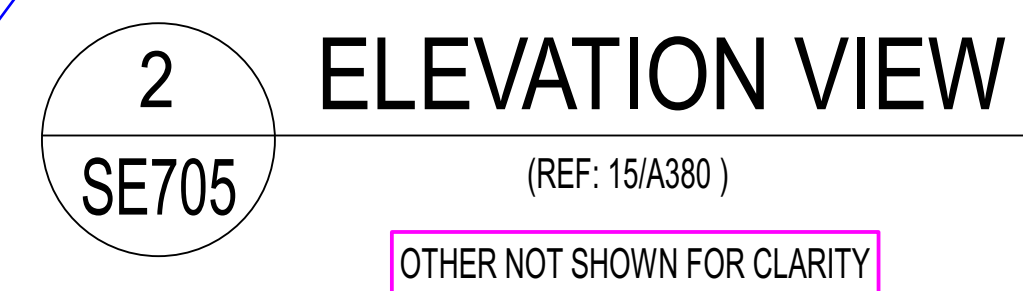

SK#28
02-06-2026

PROPERTY OF STEEL FAB ENTERPRISES, INC. AND SHALL
NOTED BE USED WITHOUT WRITTEN CONSENT.

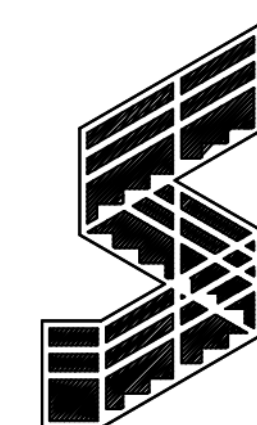

STEEL FAB
ENTERPRISES, LLC

MISCELLANEOUS METALS FABRICATOR AND ERECTORS
623 BAUMGARDNER ROAD, LANCASTER, PA 17603
TEL. (717)464-0330 FAX (717)464-9464
WWW.STEELEFABENTERPRISES.COM



PROJECT OWNER : CK CAPITAL, LLC

PROJECT DESCRIPTION : CLEVELAND BROTHERS-MILESBURG
--

PROJECT ADDRESS : 4025N. EAGLE VALLEY ROAD, HOWARD, PA 16841

CONTRACTOR: KINSLEY CONSTRUCTION, INC.

DRAWN BY : BAS

DATE : 5-20-25

PROJ.	05010
-------	-------

REV #

CHECKED BY: SRP

DATE : 5-20-25

NO. :	
DWG	05305

A

DWG DESCRIPTION : STAIR ELEVATION VIEW