
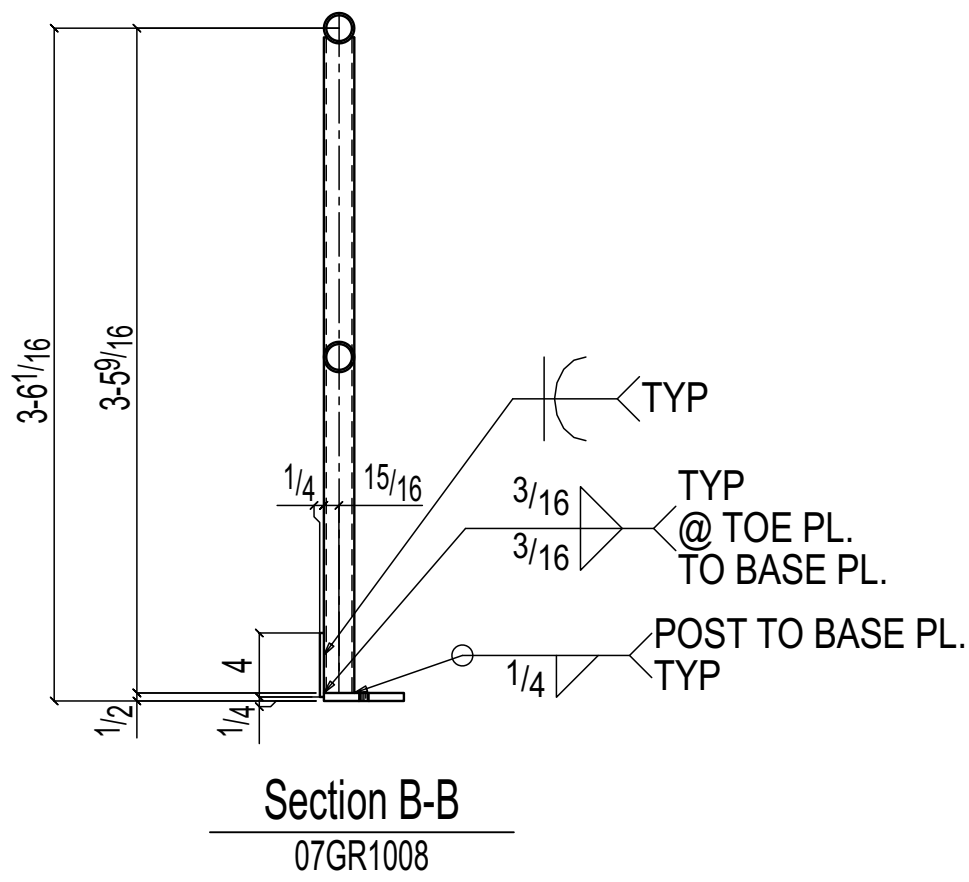


BILL OF MATERIAL									
ASSEMBLY	TOTAL	SUB-PIECE	UNIT	MATERIAL	LENGTH		REMARKS	UNIT	TOTAL
MARK	QTY	MARK	QTY	DESCRIPTION	FT	IN		WEIGHT	WEIGHT
07GR1008	ONE			GUARDRAIL			PNT	234	234
	1	07GR1008	1	PIPE 1½ SCH40	21	33⁄8	A53 GR B (TYPE-S)	58	58
	4	p4045	4	PIPE 1½ SCH40	3	83⁄16	A53 GR B (TYPE-S)	10	40
	4	p4063	4	PIPE 1½ SCH40	3	5	A53 GR B (TYPE-S)	9	37
	1	p4087	1	PIPE 1½ SCH40	2	83⁄4	A53 GR B (TYPE-S)	7	7
	1	p728	1	PL 1⁄2x5	0	10	A36	7	7
	4	p658	4	PL 1⁄2x5	0	8	A36	6	23
	1	p616	1	PL 1⁄4x4	10	0	A36	34	34
	1	p727	1	PL 1⁄4x4	7	11⁄8	A36	27	27
				FIELD BOLTS					
	10	m206		½ Dia HILTI KB-T22	0	33⁄4	+1HD WASH		
				EXPANSION ANCHOR					

Total weight : 234

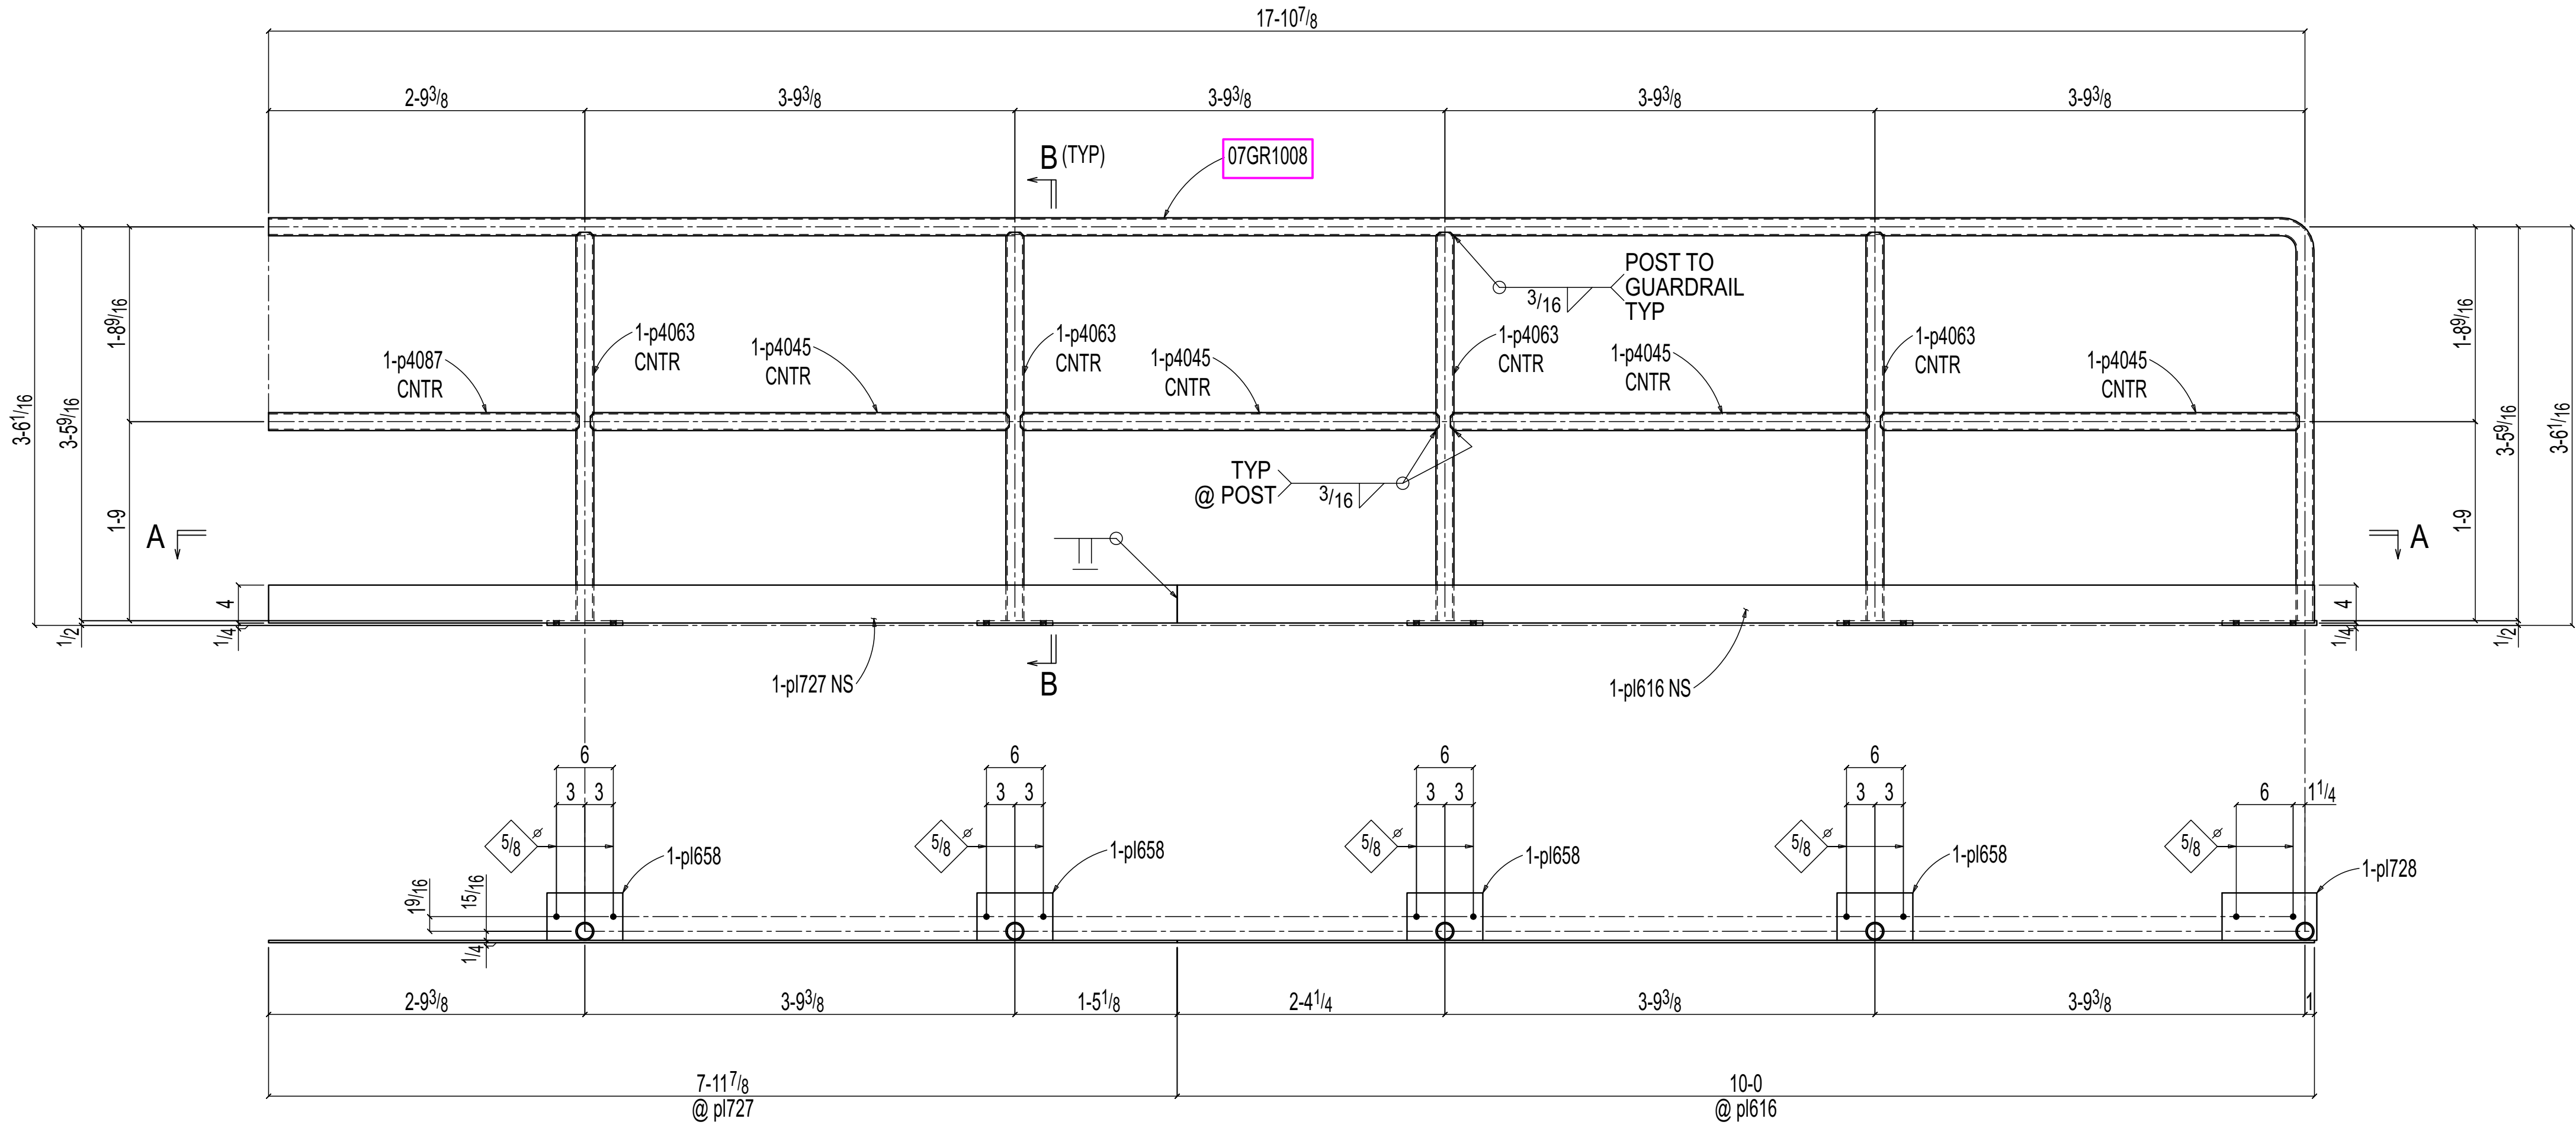

Section A-A
07GR1008


ONE GUARDRAIL 07GR1008

ALL RE-ENTRANT CUT
TO BE 1/2" RADIUS (U.N.O)
WELDS : E70XX
HOLES : 13/16" DIA (U.N.O)
MAT'L : A36 (U.N.O)
CLEAN : SSPC-SP3
PAINT : SHOP PRIMER

REVISIONS

REV	DWN BY	DATE	DESCRIPTION
A	GSV	Jun 16 2025	ISSUED FOR APPROVAL
0	GSV	Jan 27 2026	ISSUED FOR FABRICATION
1	GSV	Feb 5 2026	ISSUED FOR FABRICARION

THE INFORMATION NOTED HEREON THIS DRAWING IS THE
PROPERTY OF STEEL FAB ENTERPRISES, INC. AND SHALL
NOTED BE USED WITHOUT WRITTEN CONSENT.

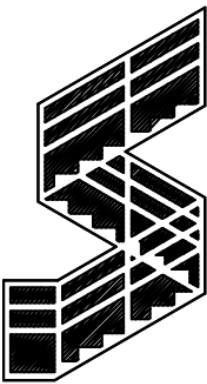

STEEL FAB
ENTERPRISES, LLC

MISCELLANEOUS METALS FABRICATOR AND ERECTORS
623 BAUMGARDNER ROAD, LANCASTER, PA 17603
TEL. (717)464-0330 FAX (717)464-9464
WWW.STEELFABENTERPRISES.COM



PROJECT OWNER : CK CAPITAL, LLC
PROJECT DESCRIPTION : CLEVELAND BROTHERS-MILESBURG
PROJECT ADDRESS : 1025N. EAGLE VALLY ROAD, HOWARD, PA 16841

CONTRACTOR : KINSLEY CONSTRUCTION, INC.

DRAWN BY : BAS	DATE : 06-07-2025	PROJ. NO. : 25012	REV #
CHECKED BY : GSV	DATE : 06-09-2025	DWG NO. : 07GR1008	⚠

DWG DESCRIPTION : GUARDRAIL DETAIL