

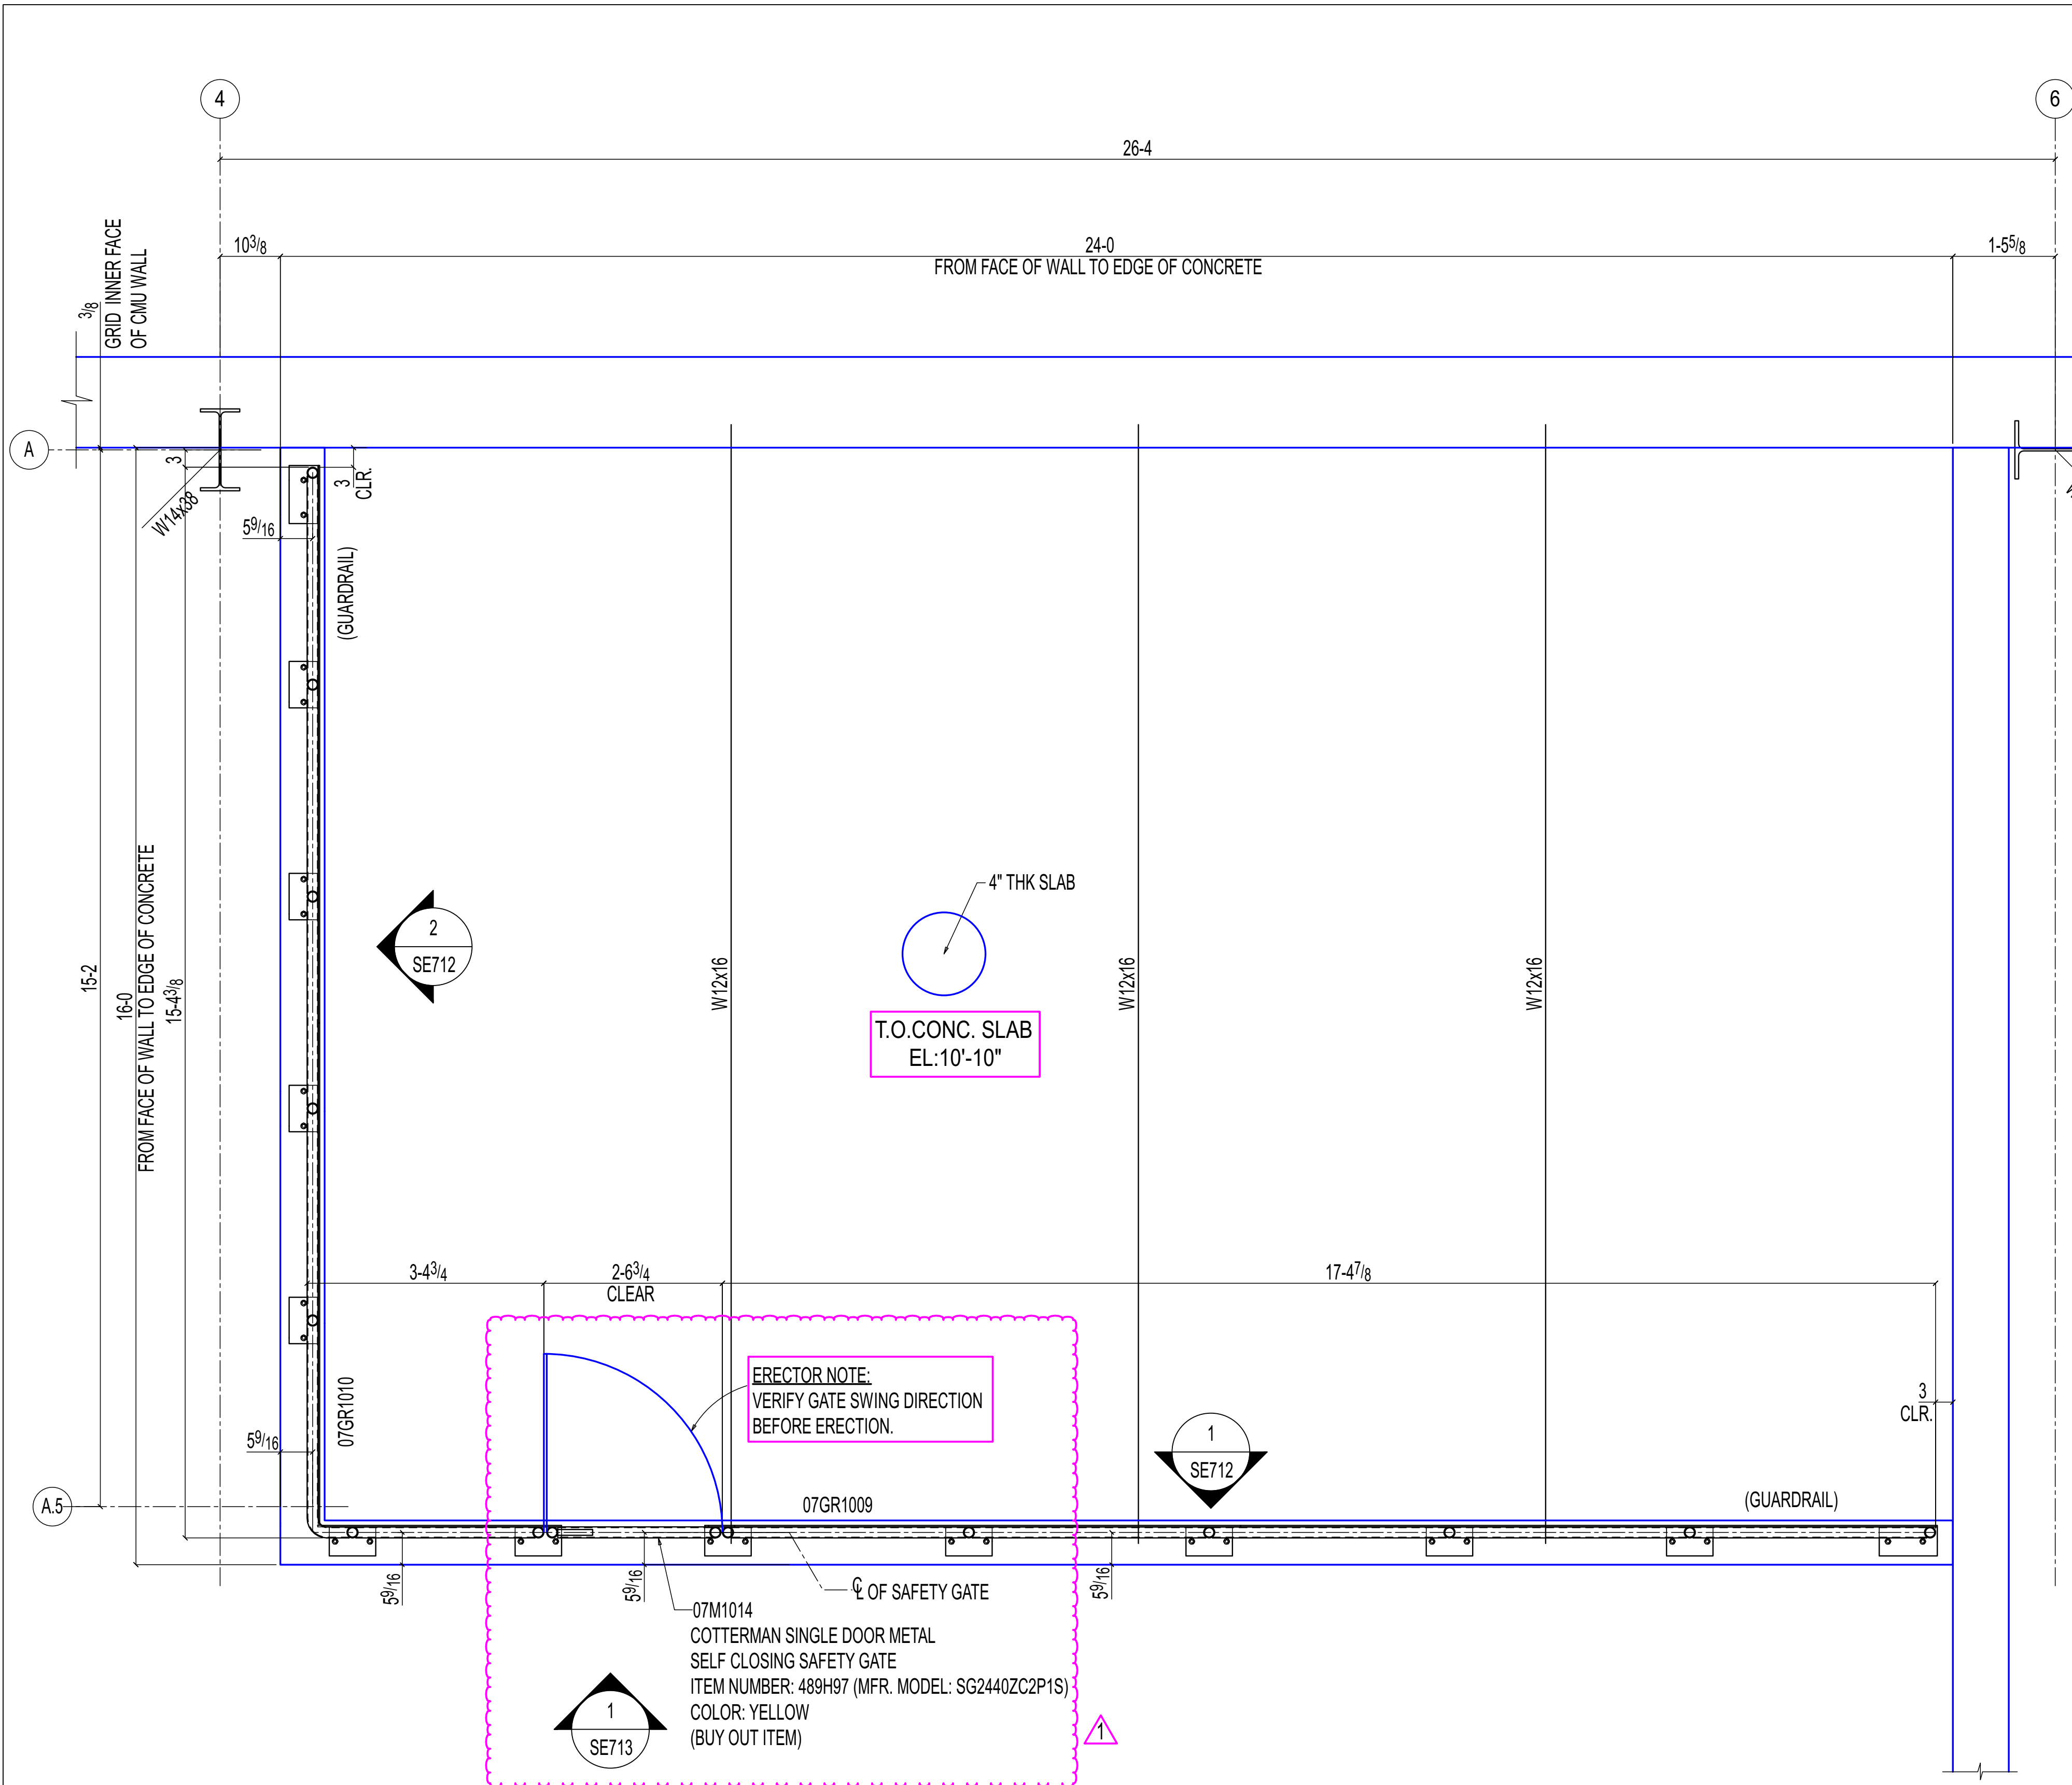


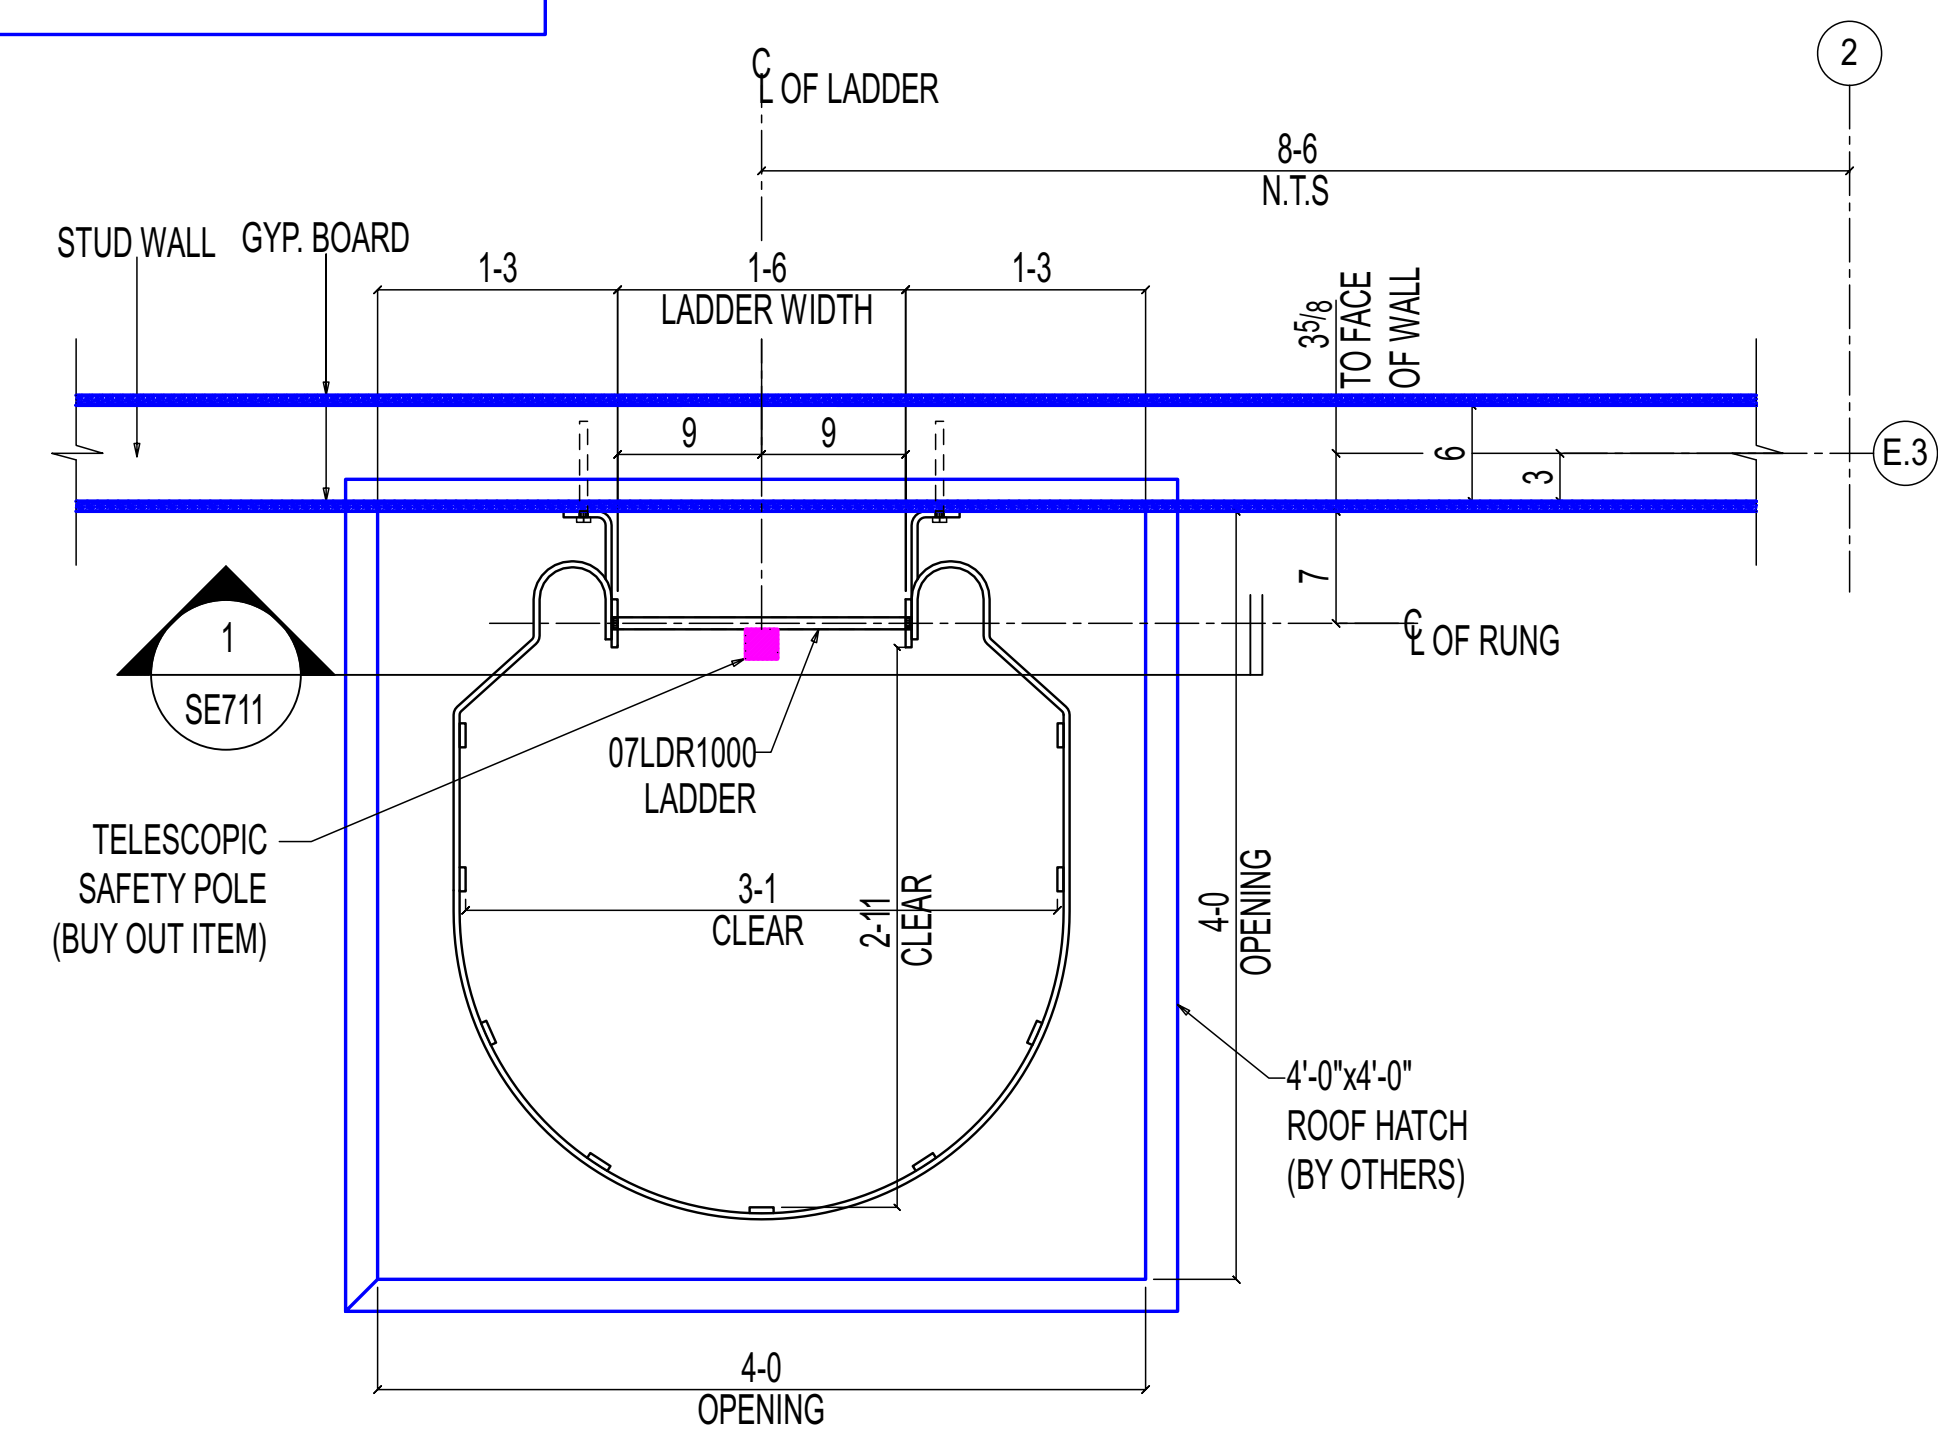

1
E704

HOSE ASSEMBLY DUSTCAAP (LADDER & GUARDRAIL PLAN)


NOTE:
1. ALL ELEVATION ARE REFERENCED FROM THE FINISHED FLOOR EL: [0'-0"] = DATUM EL:100'-0" (U.N.O).
2. ALL GUARDRAILS ARE PIPE 1 1/2 SCH40 (U.N.O).

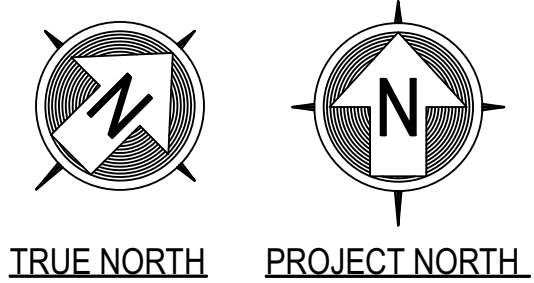

2
E704

MEZZANINE ROOF ACCESS LADDER


(REF:1/A102 & 3/S411)

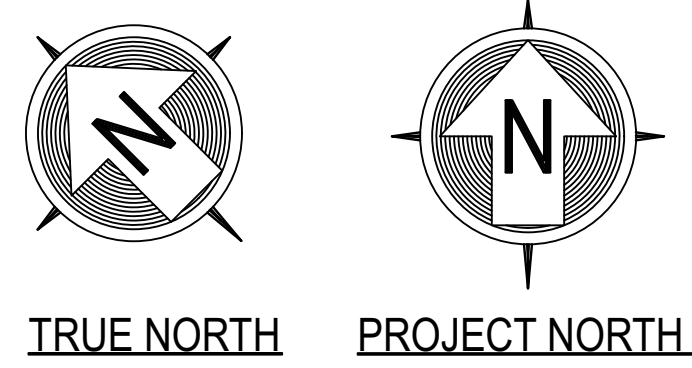

REVISIONS

REV#	DWN BY	DESCRIPTION	DATE
A	SRP	ISSUED FOR APPROVAL	Jun 16 2025
0	GSV	ISSUED FOR CONSTRUCTION	Jan 27 2026
1	GSV	REVISED AS NOTED	Mar 6 2026

THE INFORMATION NOTED HEREON THIS DRAWING IS THE PROPERTY OF STEEL FAB ENTERPRISES, INC. AND SHALL NOTED BE USED WITHOUT WRITTEN CONSENT.

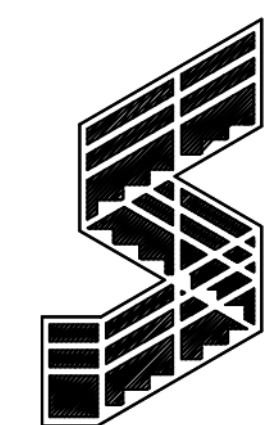

**STEEL FAB
ENTERPRISES, LLC**

MISCELLANEOUS METALS FABRICATOR AND ERECTORS
623 BAUMGARDNER ROAD, LANCASTER, PA 17603
TEL. (717)464-0330 FAX (717)464-9464
WWW.STEELFABENTERPRISES.COM



PROJECT OWNER : CK CAPITAL, LLC			
PROJECT DESCRIPTION : CLEVELAND BROTHERS-MILESBURG			
PROJECT ADDRESS : 4025N. EAGLE VALLEY ROAD, HOWARD, PA 16841			
CONTRACTOR : KINSLEY CONSTRUCTION, INC.			
DRAWN BY : BAS	DATE : 5-20-25	PROJ. NO. : 25012	REV # 
CHECKED BY : SRP	DATE : 5-20-25	DWG NO. : E704	
DWG DESCRIPTION : HOSE ASSEMBLY DUSTCAAP (LADDER & HUARDRAIL PLAN)			