



BILL OF MATERIAL									
ASSEMBLY	TOTAL	SUB-PIECE	UNIT	MATERIAL	LENGTH		REMARKS	UNIT	TOTAL
MARK	QTY	MARK	QTY	DESCRIPTION	FT	IN		WEIGHT	WEIGHT
07GR1009	ONE			GUARDRAIL			PNT	244	244
	1	07GR1009	1	PIPE 1½ SCH40	24	0	A53 GR B (TYPE-S)	65	65
	4	p4063	4	PIPE 1½ SCH40	3	5	A53 GR B (TYPE-S)	9	37
	1	p40245	1	PIPE 1½ SCH40	3	48½	A53 GR B (TYPE-S)	9	9
	4	p40244	4	PIPE 1½ SCH40	3	41¼	A53 GR B (TYPE-S)	9	36
	1	p1728	1	PL ½x5	0	10	A36	7	7
	5	p1658	5	PL ½x5	0	8	A36	6	28
	1	p1616	1	PL ½x4	10	0	A36	34	34
	1	p1730	1	PL ½x4	7	8¼	A36	26	26
				FIELD BOLTS					
	12	m206		½ Dia HILTI KB-T22	0	3¾	+1HD WASH		
				EXPANSION ANCHOR					

Total weight : 244

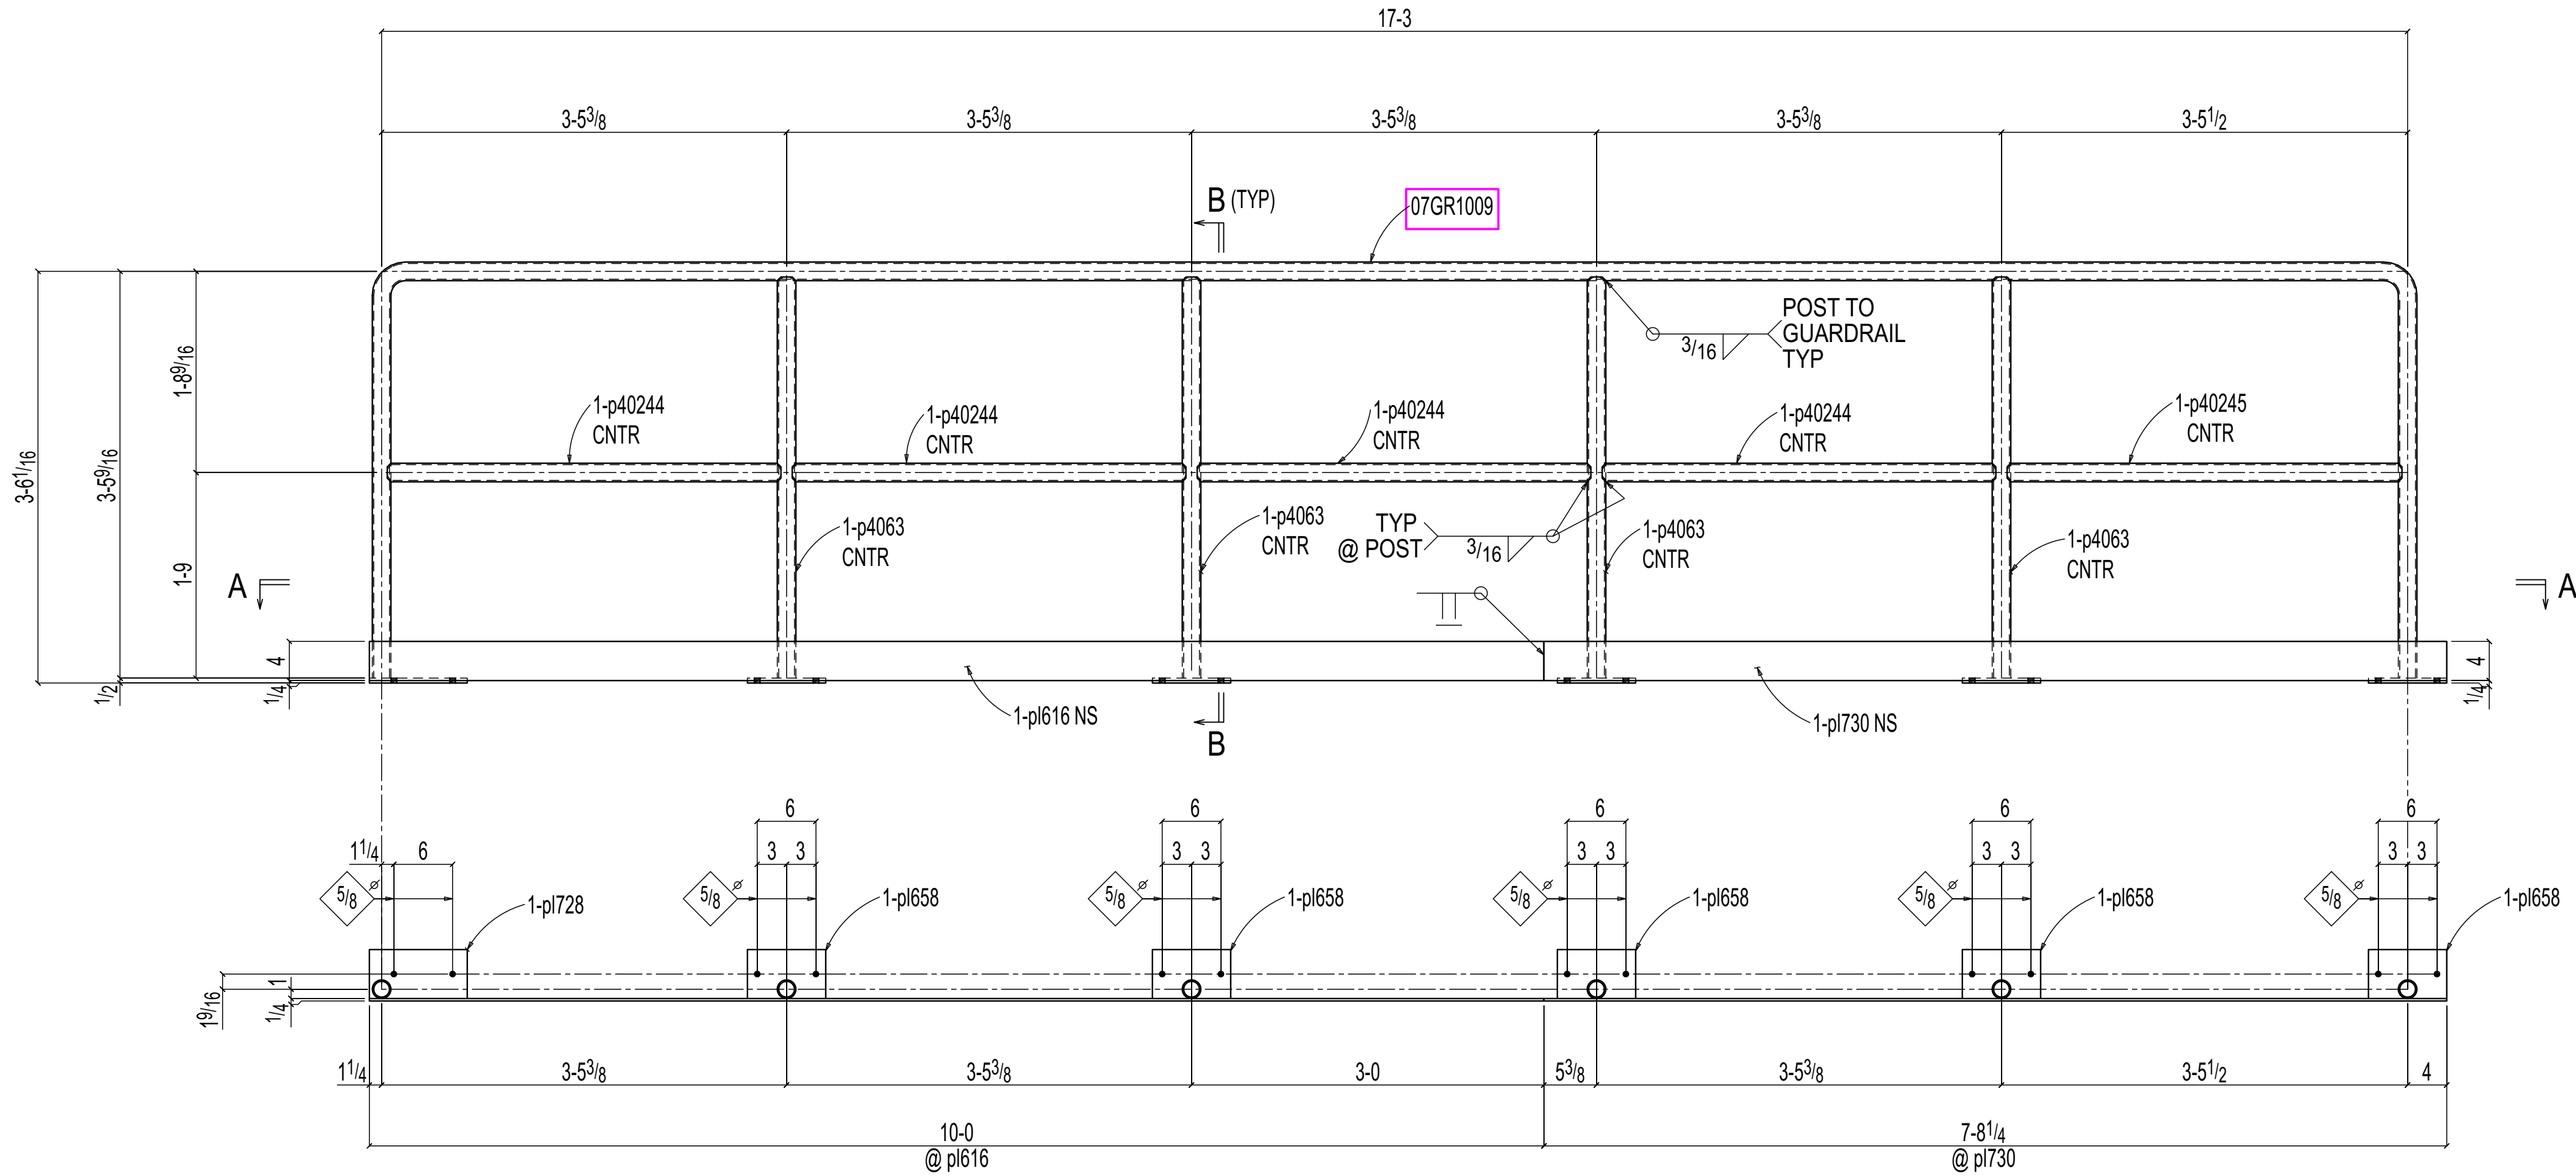

Section A-A
07GR1009

ONE GUARDRAIL 07GR1009

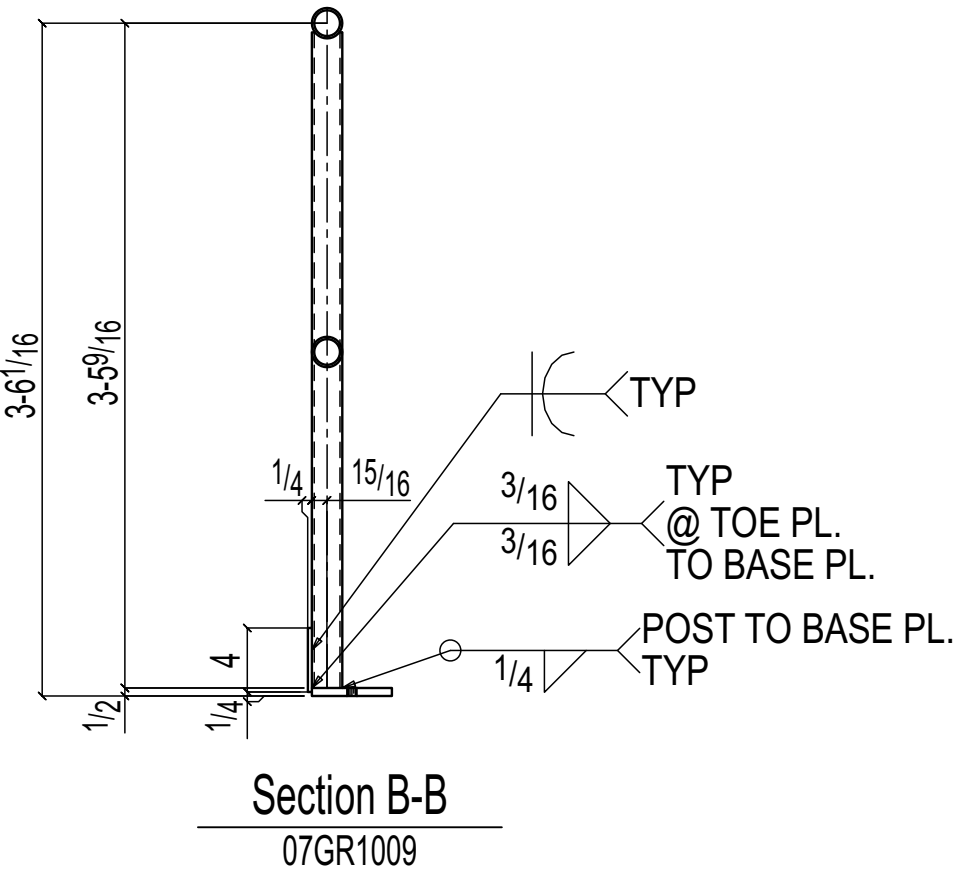

Section B-B
07GR1009

THE INFORMATION NOTED HEREON THIS DRAWING IS THE PROPERTY OF STEEL FAB ENTERPRISES, INC. AND SHALL NOTED BE USED WITHOUT WRITTEN CONSENT.



STEEL FAB
ENTERPRISES, LLC

MISCELLANEOUS METALS FABRICATOR AND ERECTORS
623 BAUMGARDNER ROAD, LANCASTER, PA 17603
TEL. (717)464-0330 FAX (717)464-9464
WWW.STEELFABENTERPRISES.COM



PROJECT OWNER : CK CAPITAL, LLC			
PROJECT DESCRIPTION : CLEVELAND BROTHERS-MILESBURG			
PROJECT ADDRESS : 1025N. EAGLE VALLY ROAD, HOWARD, PA 16841			
CONTRACTOR : KINSLEY CONSTRUCTION, INC.			
DRAWN BY : BAS	DATE : 06-07-2025	PROJ. NO. : 25012	REV # 
CHECKED BY : GSV	DATE : 06-09-2025	DWG NO. : 07GR1009	
DWG DESCRIPTION : GUARDRAIL DETAIL			

ALL RE-ENTRANT CUT
TO BE ½" RADIUS (U.N.O)
WELDS : E70XX
HOLES : 13/16" DIA (U.N.O)
MAT'L : A36 (U.N.O)
CLEAN : SSPC-SP3
PAINT : SHOP PRIMER

REVISIONS

REV	DWN BY	DATE	DESCRIPTION
A	GSV	Jun 16 2025	ISSUED FOR APPROVAL
0	GSV	Jan 27 2026	ISSUED FOR FABRICATION
1	GSV	Feb 5 2026	ISSUED FOR FABRICARION