


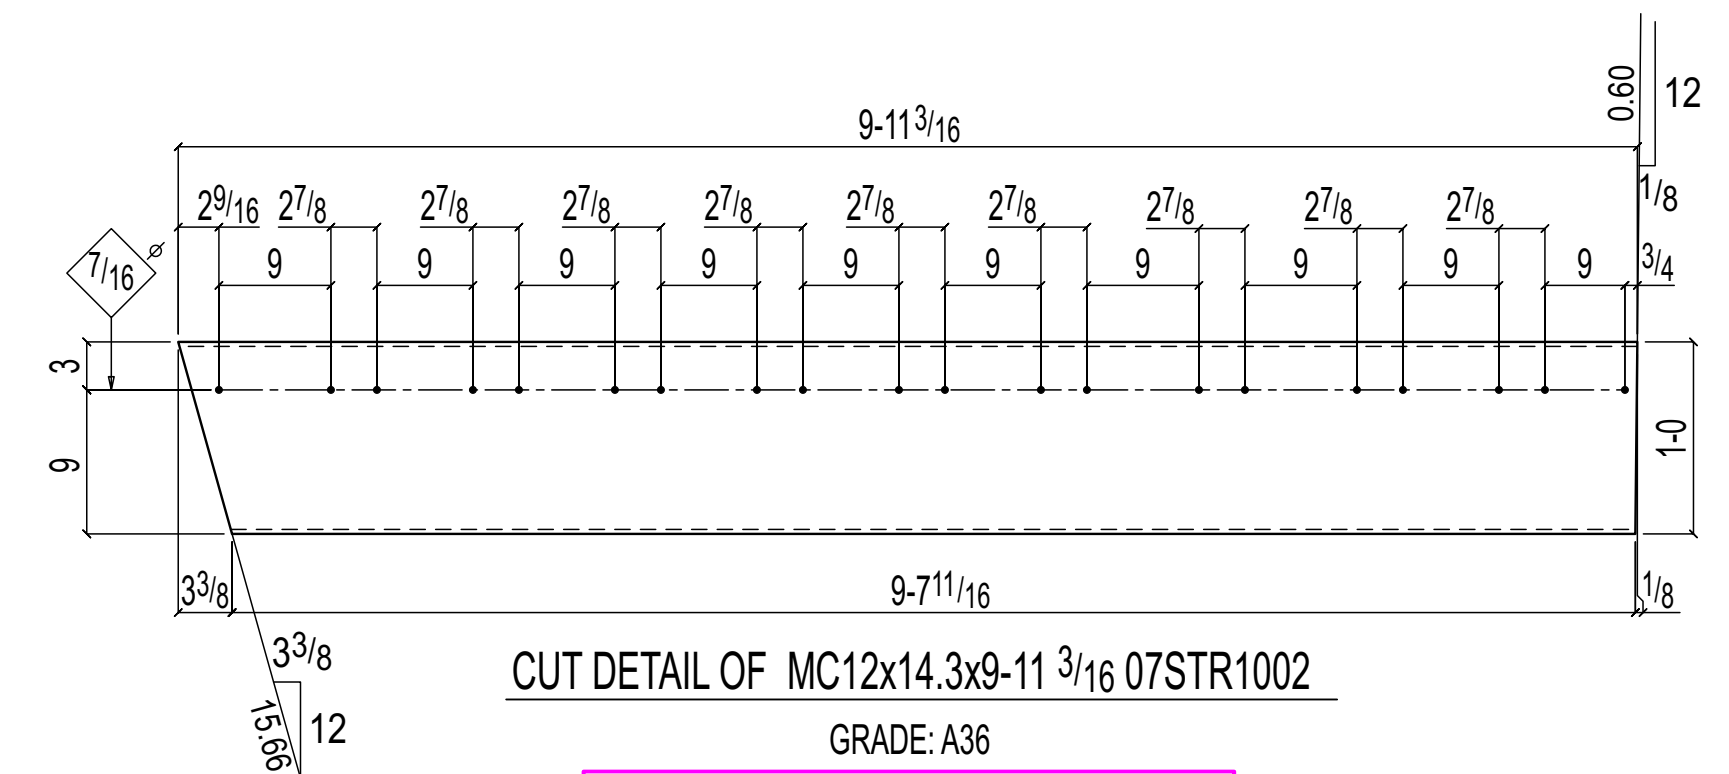

GRADE: A36

DETAIL FOR 07STR1002
(OTHERS NOT SHOWN FOR CLARITY)


SHOP NOTE:
TOE DIRECTION FAR SIDE

1-m38
10 REQ'D
McNICHOLS PLANK GRATING
ITEM NUMBER: M2G22013
WITH MID-SUPPORT CLIP
ITEM NUMBER : M0MS-99999
(BUY OUT ITEM)

1-m35
10 REQ'D
McNICHOLS CARRIER PLATE
ITEM NUMBER : M0EP2029
(BUY OUT ITEM)

Section A-A
07STR1002

APPROVER,
PLEASE CONFIRM ALL CLOUDED WELDS.

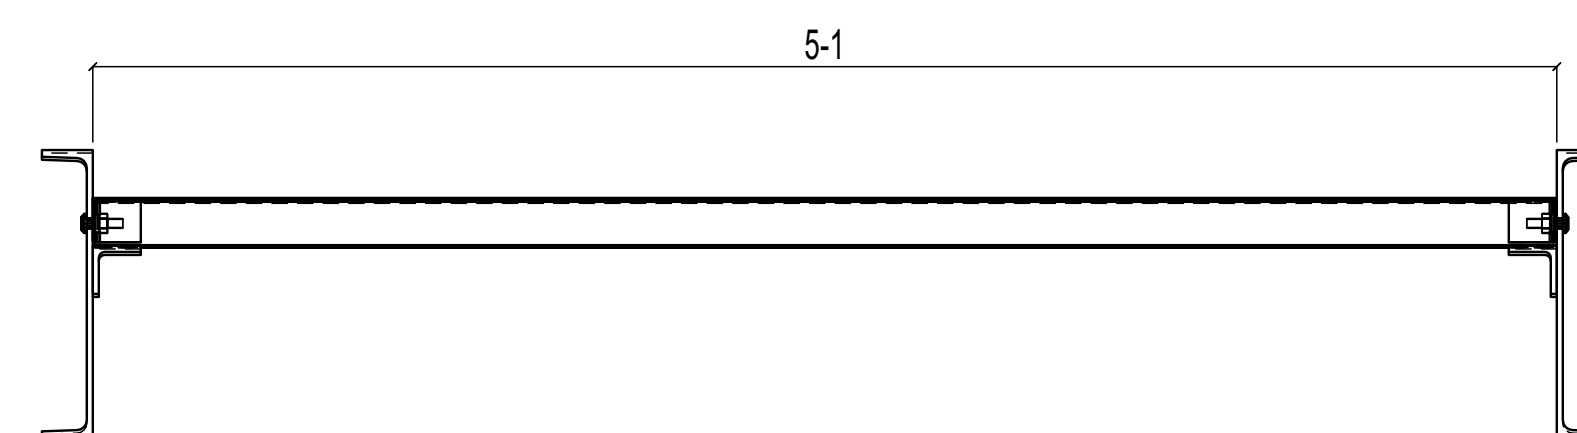

Section C-C
07STR1002

Section D-D
07STR1002

REVISIONS

REV	DWN BY	DATE	DESCRIPTION
A	GSV	Jun 16 2025	ISSUED FOR APPROVAL
B	GSV	Feb 18 2026	ISSUED FOR RE-APPROVAL

THE INFORMATION NOTED HEREON THIS DRAWING IS THE
PROPERTY OF STEEL FAB ENTERPRISES, INC. AND SHALL
NOTED BE USED WITHOUT WRITTEN CONSENT.



STEEL FAB
ENTERPRISES, LLC



MISCELLANEOUS METALS FABRICATOR AND ERECTORS
623 BAUMGARDNER ROAD, LANCASTER, PA 17603
TEL. (717)464-0330 FAX (717)464-9464
WWW.STEELFABENTERPRISES.COM

PROJECT OWNER : CK CAPITAL, LLC

PROJECT DESCRIPTION : CLEVELAND BROTHERS-MILESBURG
--

PROJECT ADDRESS : 1025N. EAGLE VALLEY ROAD, HOWARD, PA 16841
--

CONTRACTOR : KINSLEY CONSTRUCTION, INC.

DRAWN BY: BAS

DATE : 06-07-2025

5	PROJ. NO.:	25012
---	---------------	-------

REV #

	BRAUNST. DAS

DATE : 00-07-2023

3	PROG. NO.: 25012
---	------------------

CHECKED BY : GSV	DATE :
------------------	--------

READ THIS DRAWING IN CONJUNCTION WITH
SHEET 07STR1002 & 07STR1002B