


READ THIS DRAWING IN CONJUNCTION WITH SHEET 07STR1002A & 07STR1002B

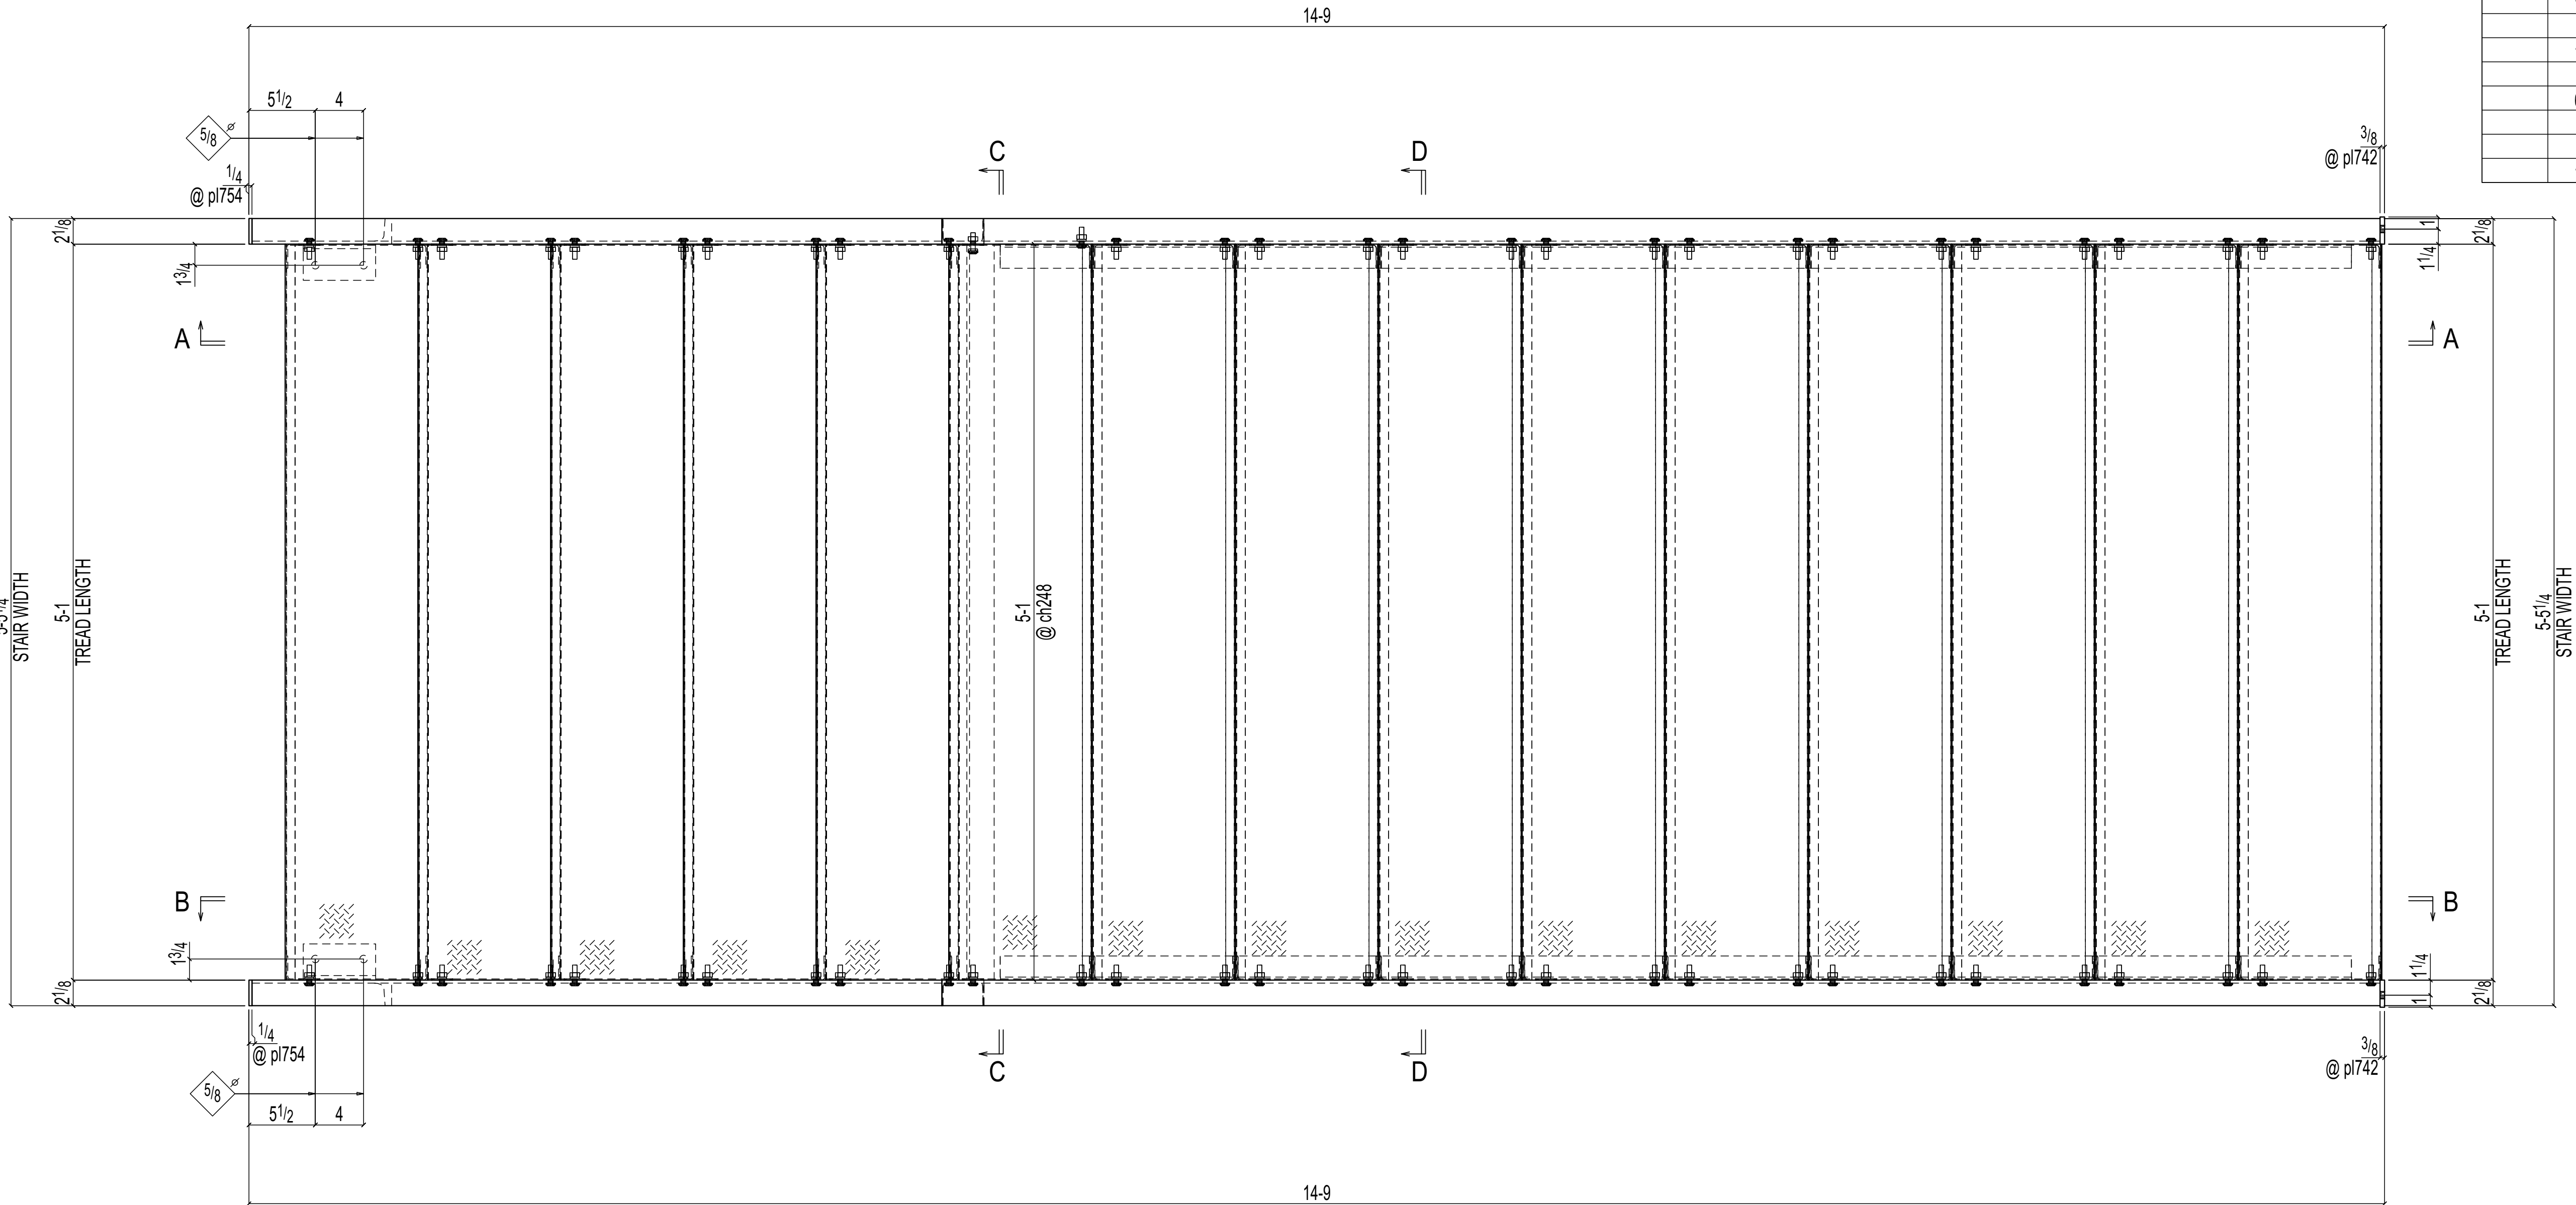

ONE STAIR 07STR1002

SHOP BOLTS (Unless Noted):
30-3/8Diax1 1/2 A325N GALV

GALVANIZED

ALL RE-ENTRANT CUT
TO BE 1/2" RADIUSED (U.N.O)
WELDS : E70XX
HOLES : 13/16" DIA (U.N.O)
MAT'L : A36 (U.N.O)
CLEAN : -
PAINT : GALVANIZED

REVISIONS


REV	DWN BY	DATE	DESCRIPTION
A	GSV	Jun 16 2025	ISSUED FOR APPROVAL
B	GSV	Feb 18 2026	ISSUED FOR RE-APPROVAL

BILL OF MATERIAL

ASSEMBLY MARK	TOTAL QTY	SUB-PIECE MARK	UNIT QTY	MATERIAL DESCRIPTION	LENGTH FT	IN	REMARKS	UNIT WEIGHT	TOTAL WEIGHT
07STR1002	ONE			STAIR			Galv	1173	1173
	1	07STR1002	1	MC12x14.3	9	11 3/16	A36	142	142
	1	ch308	1	MC12x14.3	9	11 3/16	A36	142	142
	1	ch307	1	MC12x14.3	5	10 3/8	A36	84	84
	1	ch309	1	MC12x14.3	5	10 3/8	A36	84	84
	2	a1073	2	L3x3x3/8	0	6	A36	4	7
	2	a527	2	L2x2x1/4	9	4	A36	30	60
	1	ch248	1	C8x11.5	5	1	A36	58	58
	2	pl742	2	PL 3/8x2 1/4	1	0	A36	3	6
	2	pl754	2	PL 1/4x2 1/8	0	7 1/8	A36	1	2
	6	bp1201	6	PL12GAx61	0	4 13/16	BENT A36	9	52
	5	m37	5	McNICHOLS PLANK GRATING	5	1	(BUY OUT ITEM)	35	177
				ITEM NUMBER: M2G22013					
	10	m38	10	McNICHOLS PLANK GRATING	5	1	(BUY OUT ITEM)	35	353
				ITEM NUMBER: M2G22013					
				WITH MID-SUPPORT CLIP					
				ITEM NUMBER: MOMS-99999					
	10	m33	10	McNICHOLS CARRIER PLATE			(BUY OUT ITEM)		
				ITEM NUMBER: MOEP2029					
	10	m35	10	McNICHOLS CARRIER PLATE			(BUY OUT ITEM)		
				ITEM NUMBER: MOEP2029					
	10	m36	10	McNICHOLS CARRIER PLATE			(BUY OUT ITEM)		
				ITEM NUMBER: MOEP2029					
	60		60	3/8 Dia A325N	0	1 1/2	GALV	0	6
				FIELD BOLTS					
	10	m200		1/2"x2 HILTI KB3	0	5 1/2	+1HD WASH		

Total weight : 1173

THE INFORMATION NOTED HEREON THIS DRAWING IS THE PROPERTY OF STEEL FAB ENTERPRISES, INC. AND SHALL NOTED BE USED WITHOUT WRITTEN CONSENT.

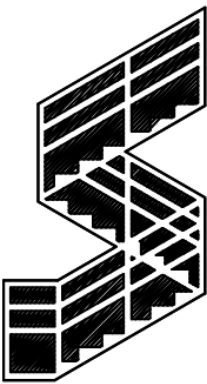

STEEL FAB
ENTERPRISES, LLC



MISCELLANEOUS METALS FABRICATOR AND ERECTORS
623 BAUMGARDNER ROAD, LANCASTER, PA 17603
TEL. (717)464-0330 FAX (717)464-9464
WWW.STEELFABENTERPRISES.COM

PROJECT OWNER : CK CAPITAL, LLC			
PROJECT DESCRIPTION : CLEVELAND BROTHERS-MILESBURG			
PROJECT ADDRESS : 1025N. EAGLE VALLY ROAD, HOWARD, PA 16841			
CONTRACTOR : KINSLEY CONSTRUCTION, INC.			
DRAWN BY : BAS	DATE : 06-07-2025	PROJ. NO. : 25012	REV #
CHECKED BY : GSV	DATE : 06-09-2025	DWG NO. : 07STR1002	
DWG DESCRIPTION : STAIR DETAIL			