


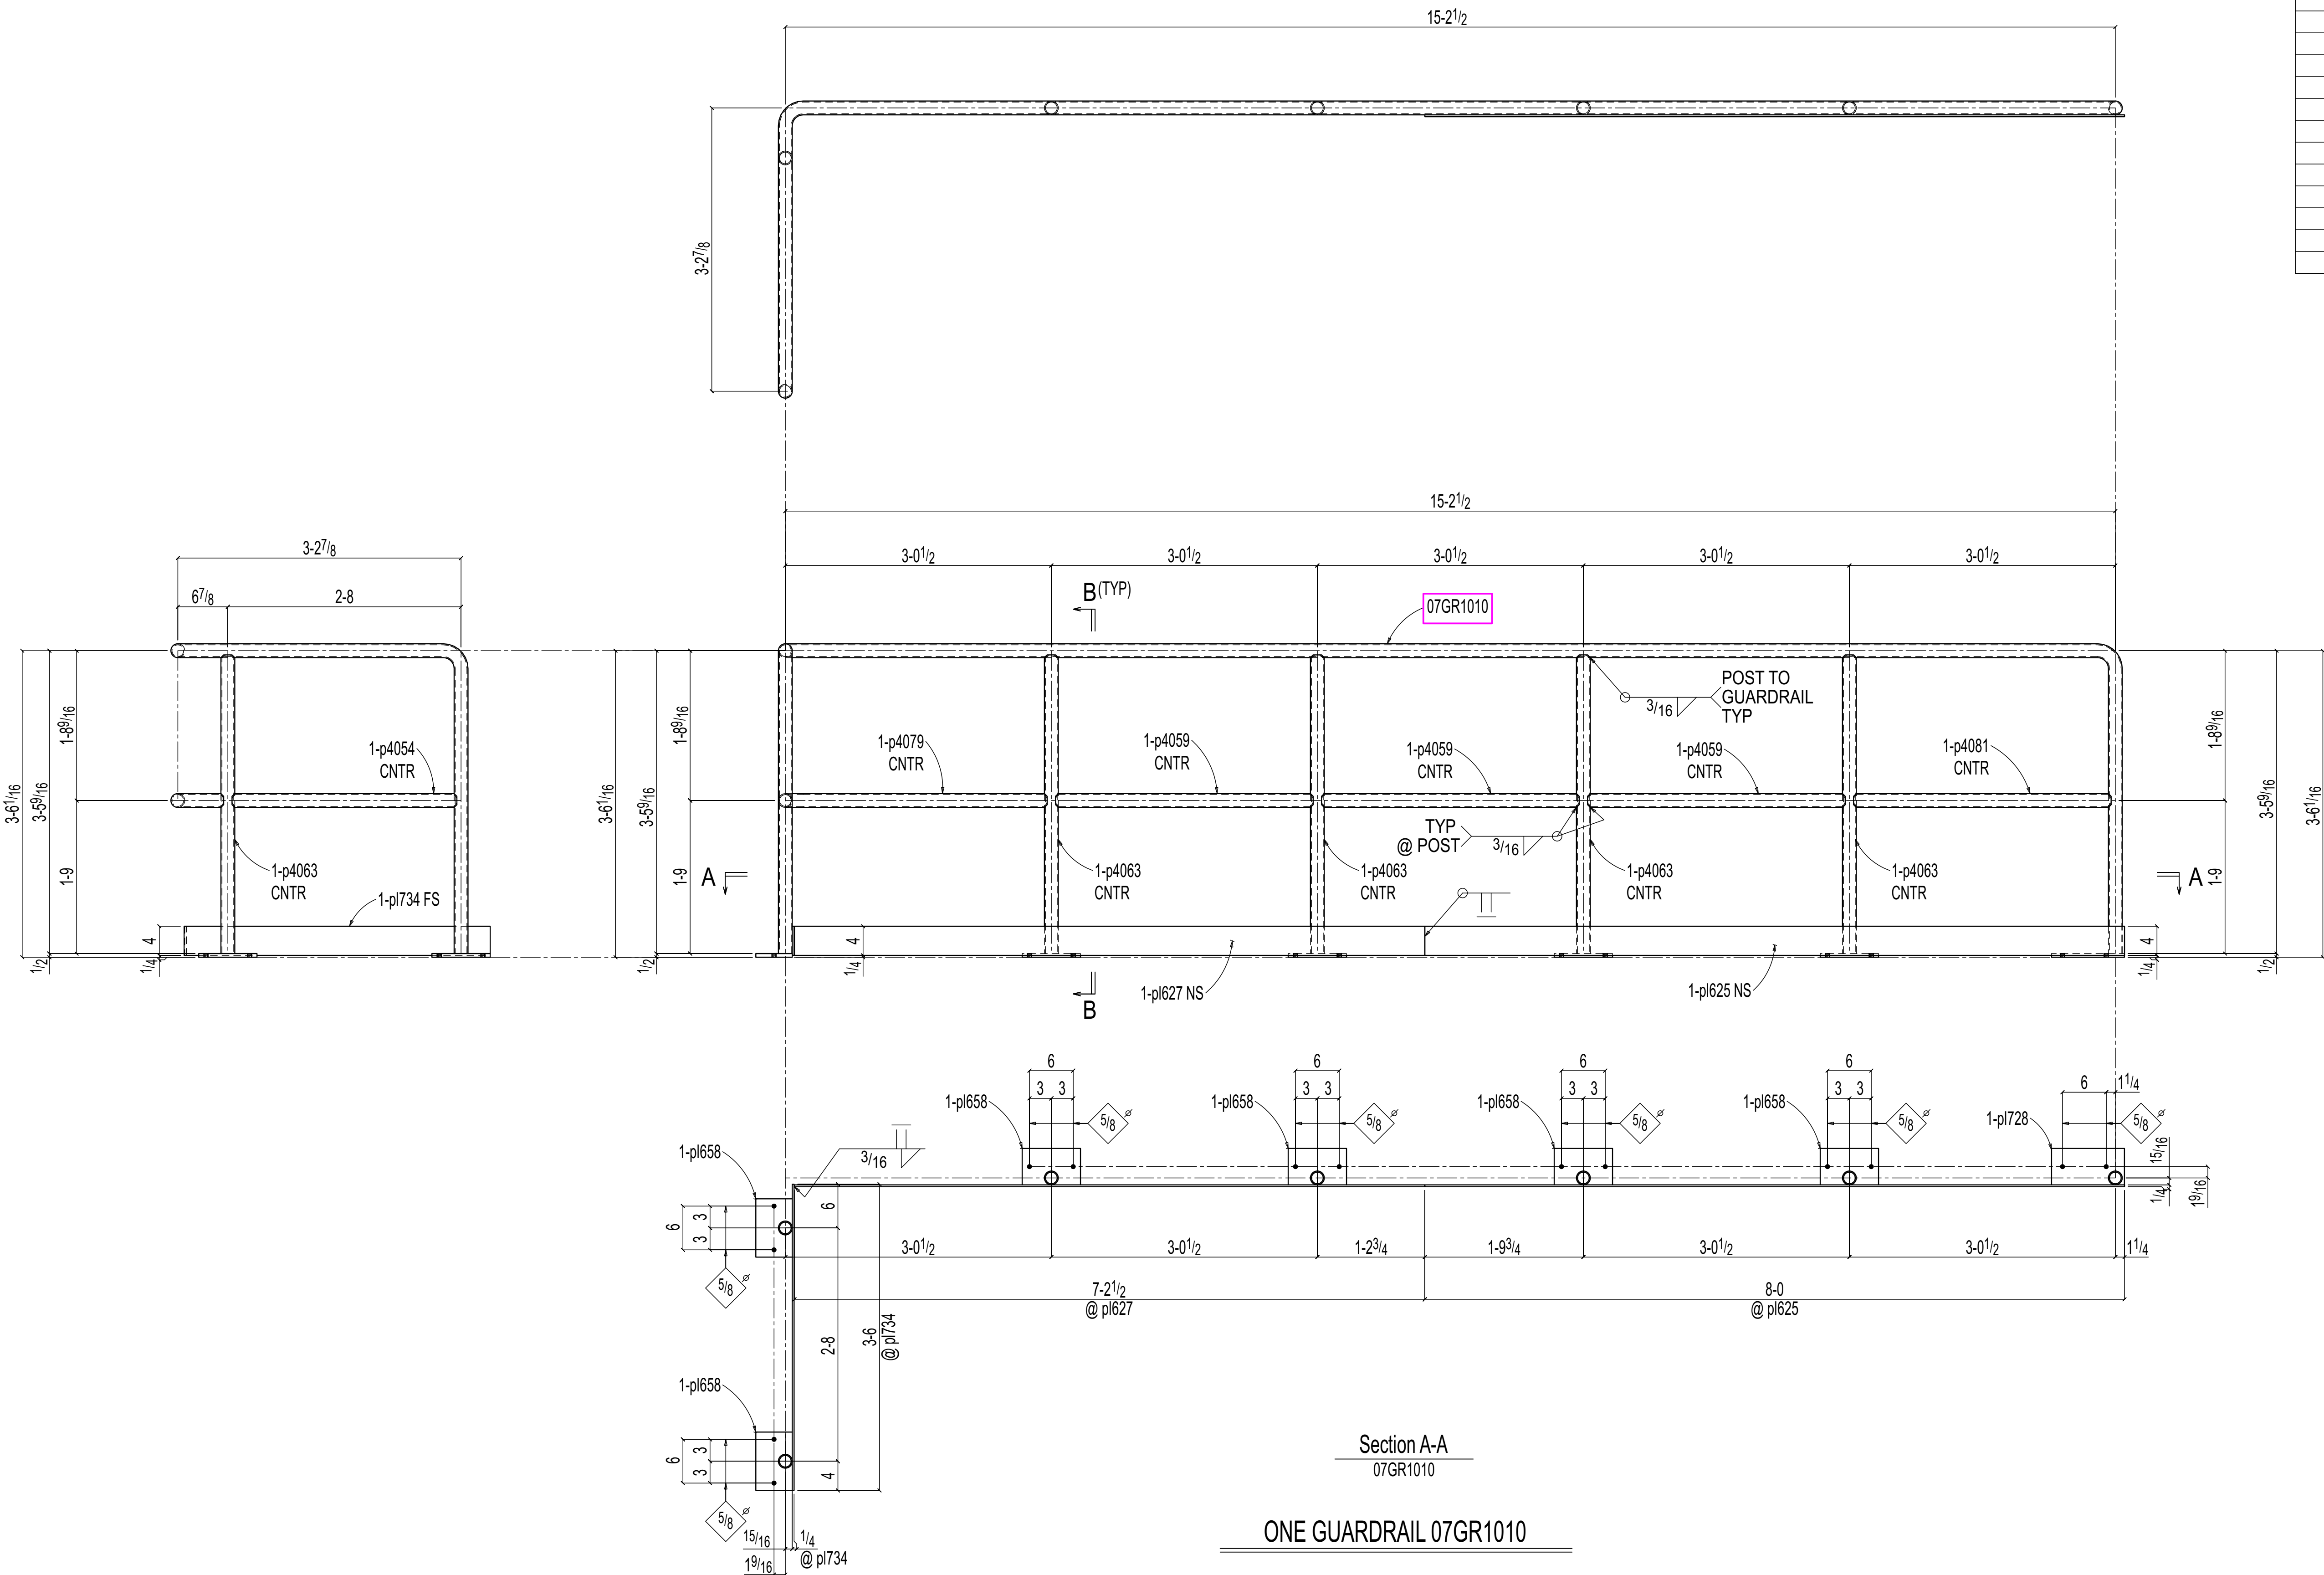


Section A-A
07GR1010
ONE GUARDRAIL 07GR1010

BILL OF MATERIAL

ASSEMBLY MARK	TOTAL QTY	SUB-PIECE MARK	UNIT QTY	MATERIAL DESCRIPTION	LENGTH FT	IN	REMARKS	UNIT WEIGHT	TOTAL WEIGHT
07GR1010	ONE			GUARDRAIL			PNT	268	268
	1	07GR1010	1	PIPE 1 1/2 SCH40	24	11 7/8	A53 GR B (TYPE-S)	68	68
	1	p4079	1	PIPE 1 1/2 SCH40	3	5 1/8	A53 GR B (TYPE-S)	9	9
	5	p4063	5	PIPE 1 1/2 SCH40	3	5	A53 GR B (TYPE-S)	9	46
	3	p4059	3	PIPE 1 1/2 SCH40	2	11 3/8	A53 GR B (TYPE-S)	8	24
	1	p4081	1	PIPE 1 1/2 SCH40	2	11 5/16	A53 GR B (TYPE-S)	8	8
	1	p4054	1	PIPE 1 1/2 SCH40	2	6 7/8	A53 GR B (TYPE-S)	7	7
	1	p1728	1	PL 1/2x5	0	10	A36	7	7
	6	p1658	6	PL 1/2x5	0	8	A36	6	34
	1	p1625	1	PL 1/4x4	8	0	A36	27	27
	1	p1627	1	PL 1/4x4	7	2 1/2	A36	25	25
	1	p1734	1	PL 1/4x4	3	6	A36	12	12
				FIELD BOLTS					
	14	m206		1/2 Dia HILTI KB-T22	0	3 3/4	+1HD WASH		
				EXPANSION ANCHOR					

Total weight : 268

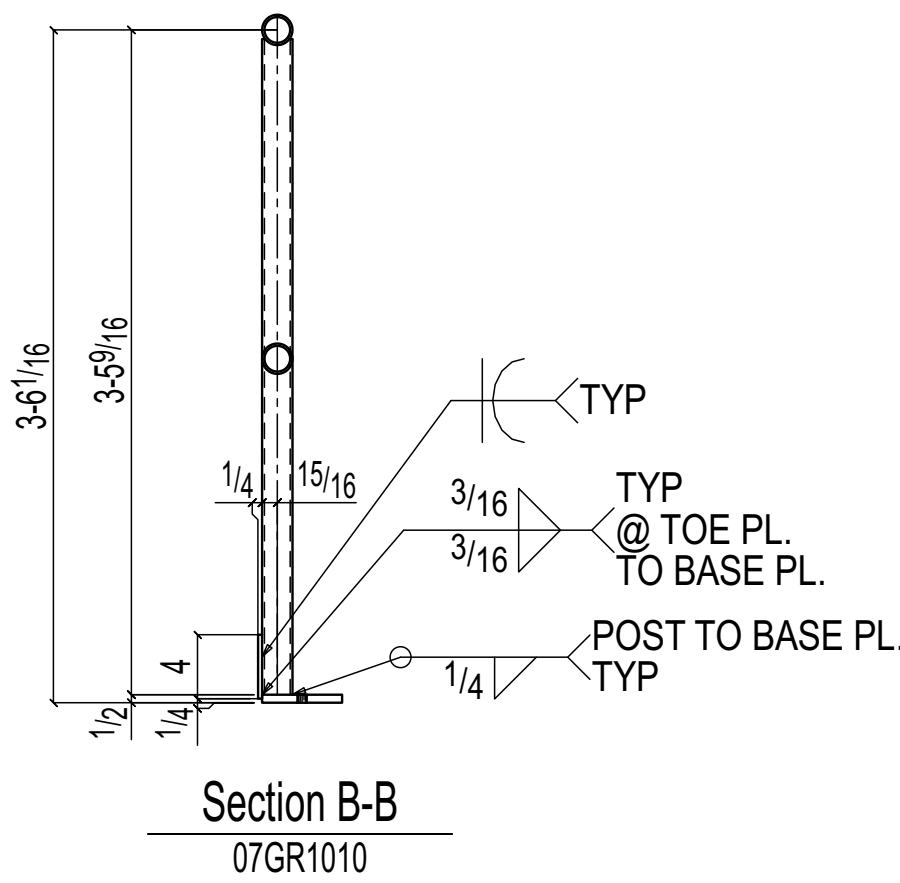

Section B-B
07GR1010

THE INFORMATION NOTED HEREON THIS DRAWING IS THE PROPERTY OF STEEL FAB ENTERPRISES, INC. AND SHALL NOTED BE USED WITHOUT WRITTEN CONSENT.



STEEL FAB
ENTERPRISES, LLC

MISCELLANEOUS METALS FABRICATOR AND ERECTORS
623 BAUMGARDNER ROAD, LANCASTER, PA 17603
TEL. (717)464-0330 FAX (717)464-9464
WWW.STEELFABENTERPRISES.COM



CERTIFIED
FABRICATOR
AND ERECTOR

PROJECT OWNER : CK CAPITAL, LLC			
PROJECT DESCRIPTION : CLEVELAND BROTHERS-MILESBURG			
PROJECT ADDRESS : 1025N. EAGLE VALLY ROAD, HOWARD, PA 16841			
CONTRACTOR : KINSLEY CONSTRUCTION, INC.			
DRAWN BY : BAS	DATE : 06-07-2025	PROJ. NO. : 25012	REV #
CHECKED BY : GSV	DATE : 06-09-2025	DWG NO. : 07GR1010	⚠
DWG DESCRIPTION : GUARDRAIL DETAIL			

ALL RE-ENTRANT CUT
TO BE 1/2" RADIUSED (U.N.O)
WELDS : E70XX
HOLES : 13/16" DIA (U.N.O)
MAT'L : A36 (U.N.O)
CLEAN : SSPC-SP3
PAINT : SHOP PRIMER

REVISIONS

REV	DWN BY	DATE	DESCRIPTION
A	GSV	Jun 16 2025	ISSUED FOR APPROVAL
0	GSV	Jan 27 2026	ISSUED FOR FABRICATION
1	GSV	Feb 5 2026	ISSUED FOR FABRICARION