



BILL OF MATERIAL							
LINE #	QTY	PC	MARK	DESCRIPTION	LENGTH	WEIGHT	ADVANCE
	TOTAL					TOTAL	MILL #
ONE F-08.00C1 COLUMN							
1	F-08.00C1	HSS6x6x3/8		11	9	SIZE A500C	323
1	bp1002	PL11/4x8		1	2	A36	40
1	p3065	PL11/4x7		1	10	A36	55
FIELD BOLTS							
2		3/4 Dia HILTI KWIK HUS-EZ		0	7	(3 1/4" EMBED)	
SCREW ANCHOR							
ONE F-08.00C2 COLUMN							
1	F-08.00C2	HSS6x6x3/8		9	4	SIZE A500C	256
1	p3065	PL11/4x7		1	10	A36	55
1	p1964	PL11/4x7		1	6	A36	45
FIELD BOLTS							
2		3/4 Dia HILTI HAS V-36		0	8	(3 1/4" EMBED)	
w/HILTI HY-200 EPOXY							
2		3/4 Dia HILTI KWIK HUS-EZ		0	7	(3 1/4" EMBED)	
SCREW ANCHOR							
B ONE F-08.00C3 COLUMN							
1	F-08.00C3	HSS6x6x3/8		13	0 3/4	SIZE A500C	359
1	p3367	PL3/8x6 1/2		1	6	A36	21
1	p230	PL3/8x6 1/2		1	2	A36	16
FIELD BOLTS							
2		3/4 Dia HILTI HAS V-36		0	8	(4" EMBED)	
THREADED ROD							
2		1/2 Dia HILTI KWIK HUS-EZ		0	4 1/2	(3 1/4" EMBED)	
SCREW ANCHOR							
ONE F-08.00C4 COLUMN							
1	F-08.00C4	HSS6x6x3/8		9	10 1/2	A500C	271
1	hss70	HSS4x4x3/16		1	6 3/4	A500C	23
1	hss69	HSS4x4x3/16		1	1	A500C	16
1	a155	L11/2x1x3/16		0	5	A36	1
1	p404	PL3/8x6 1/2		1	6	A36	21
1	p3367	PL3/8x6 1/2		1	6	A36	21
1	p3632	PL1/4x4		0	4	A36	1
FIELD BOLTS							
2		3/4 Dia HILTI KWIK HUS-EZ		0	4 1/2	(3 1/4" EMBED)	
SCREW ANCHOR							
ONE F-08.00B1 BEAM							
1	F-08.00B1	HSS10x8x1/2		12	17 7/8	A500C	677
2	p3657	PL1/4x8		0	10	A36	11

Total weight : 2211

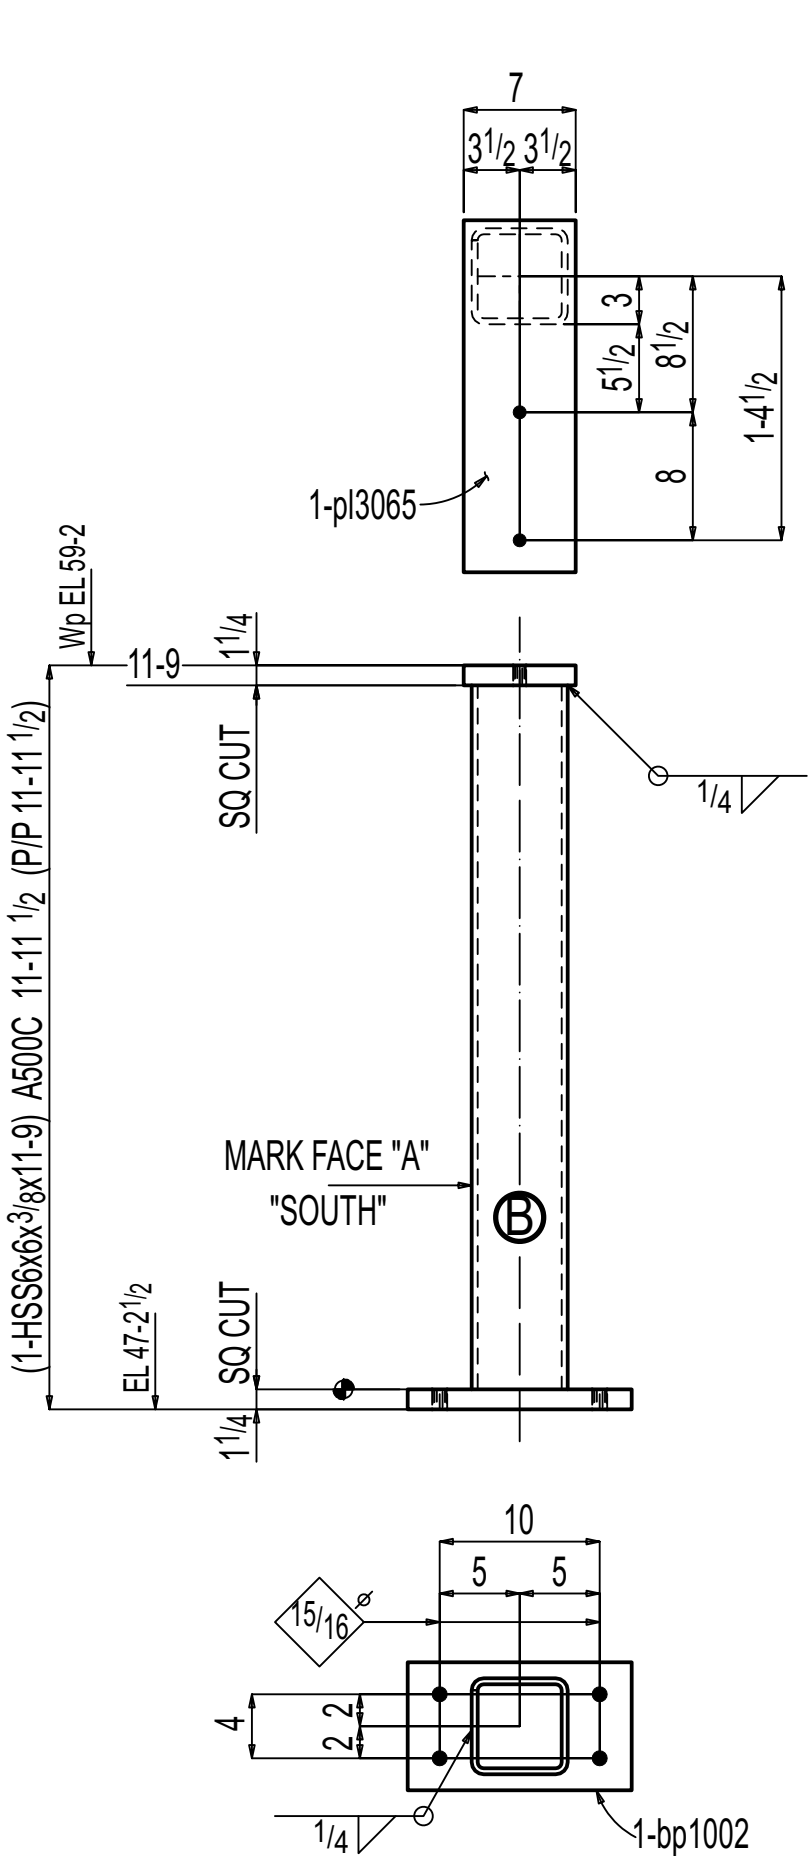


AT GRID:
EE & A

ONE COLUMN F-08.00C1

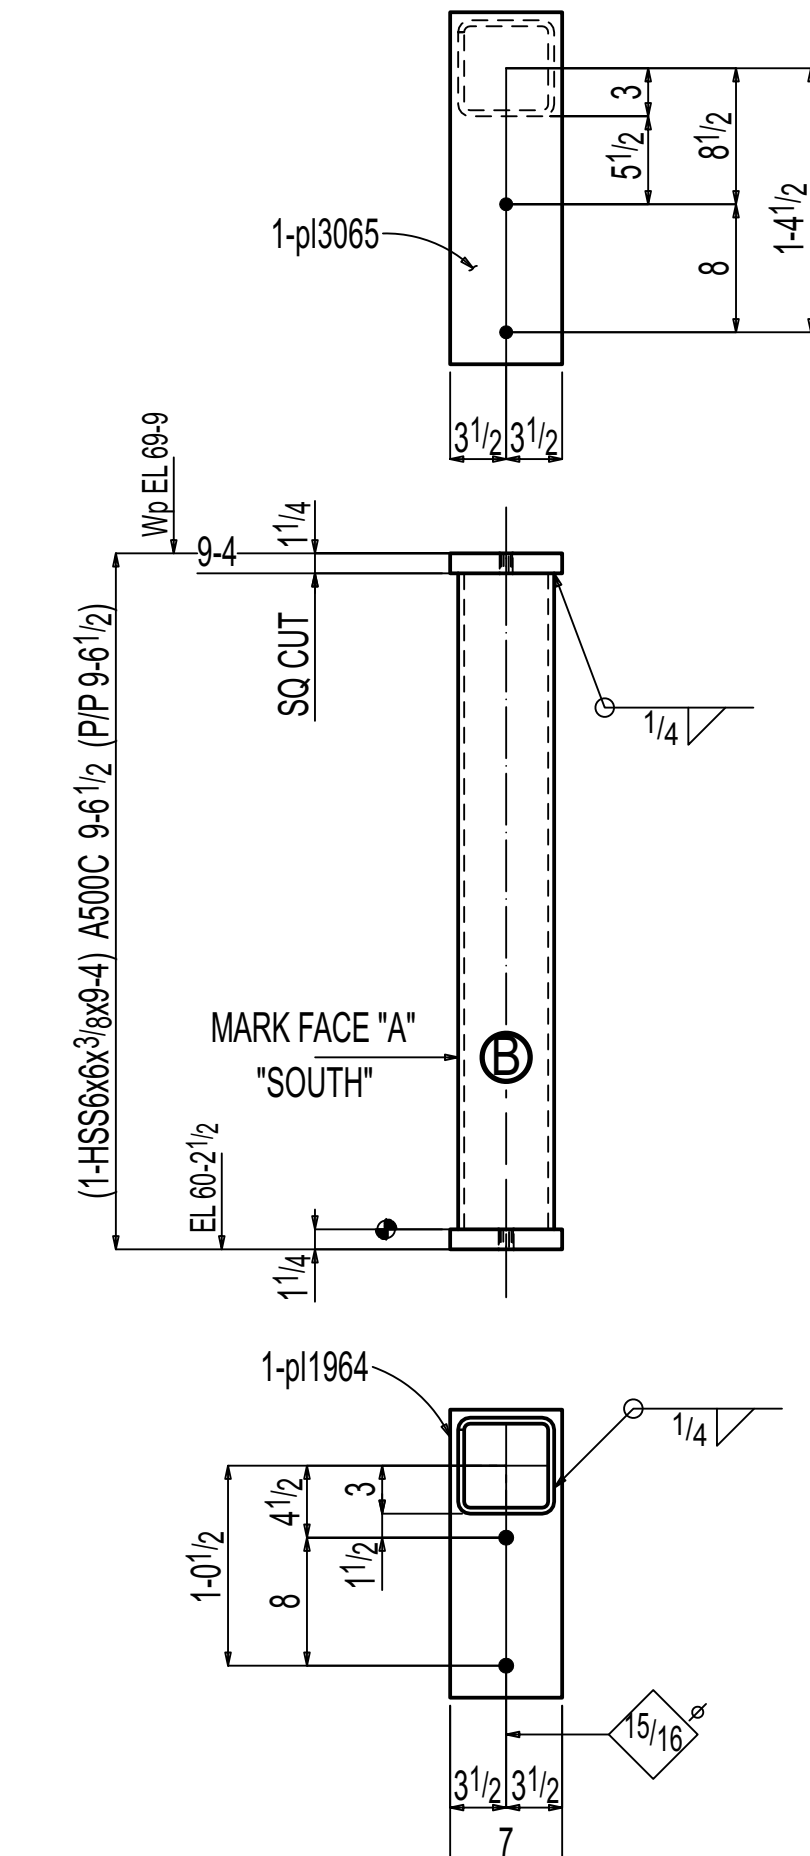


AT GRID:
EE & A

ONE COLUMN F-08.00C2

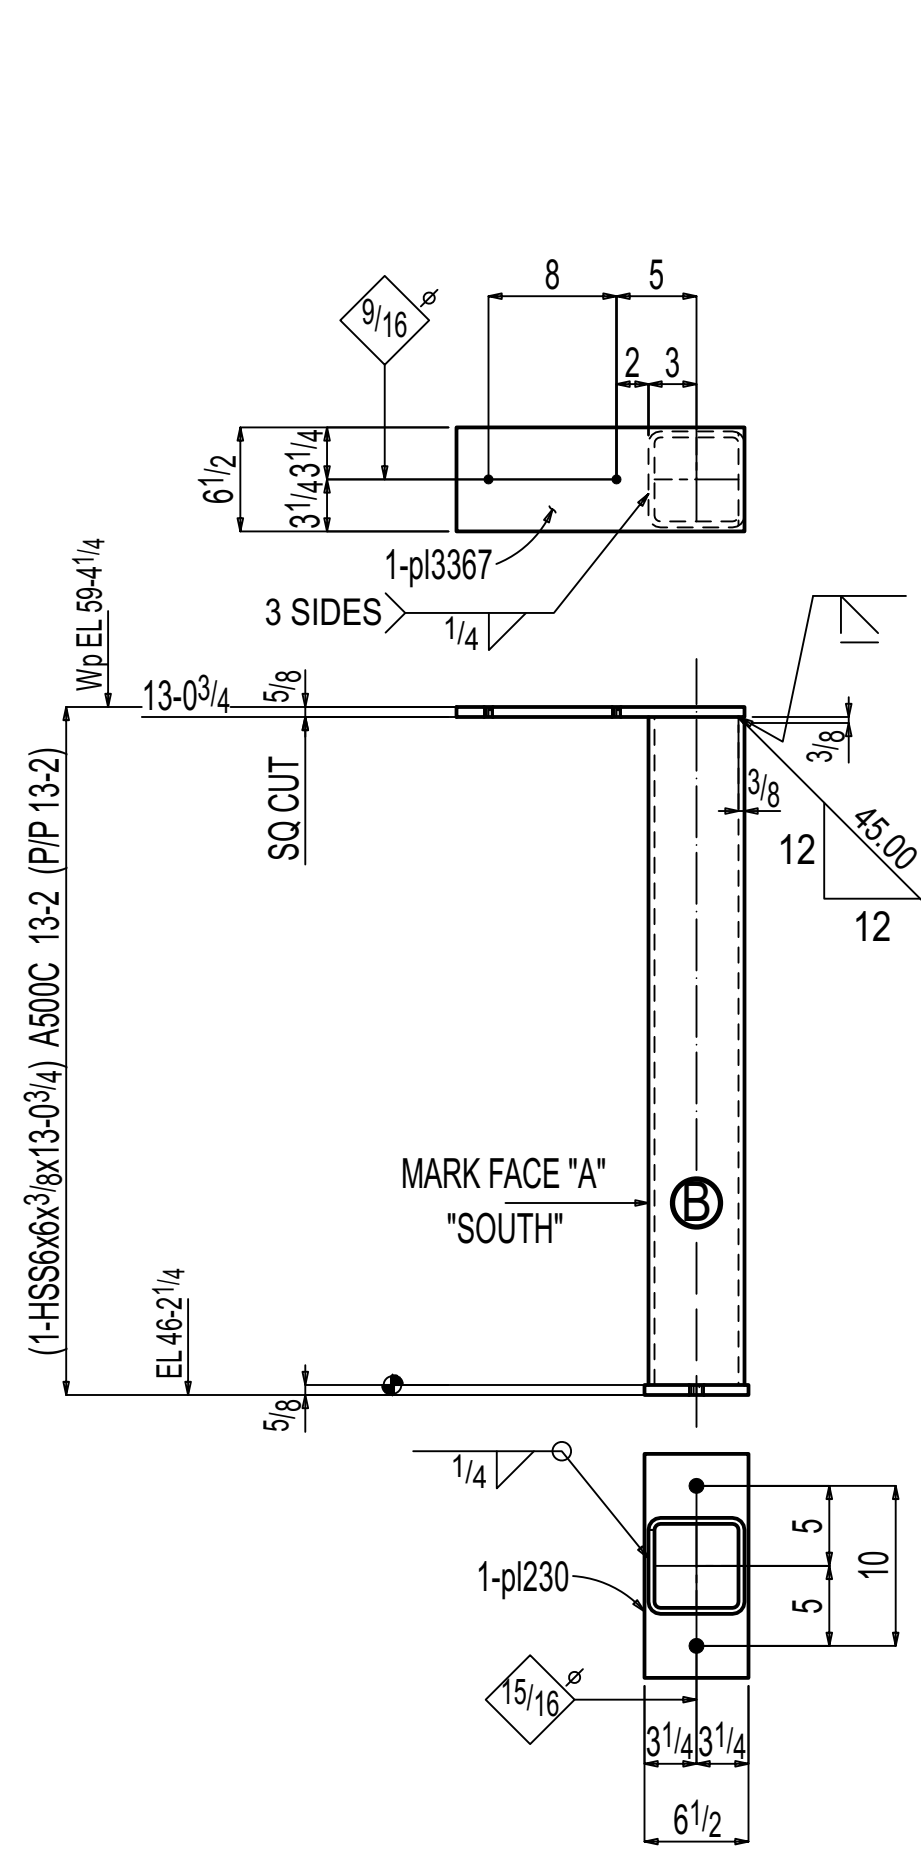


AT GRID:
AA & K

ONE COLUMN F-08.00C3

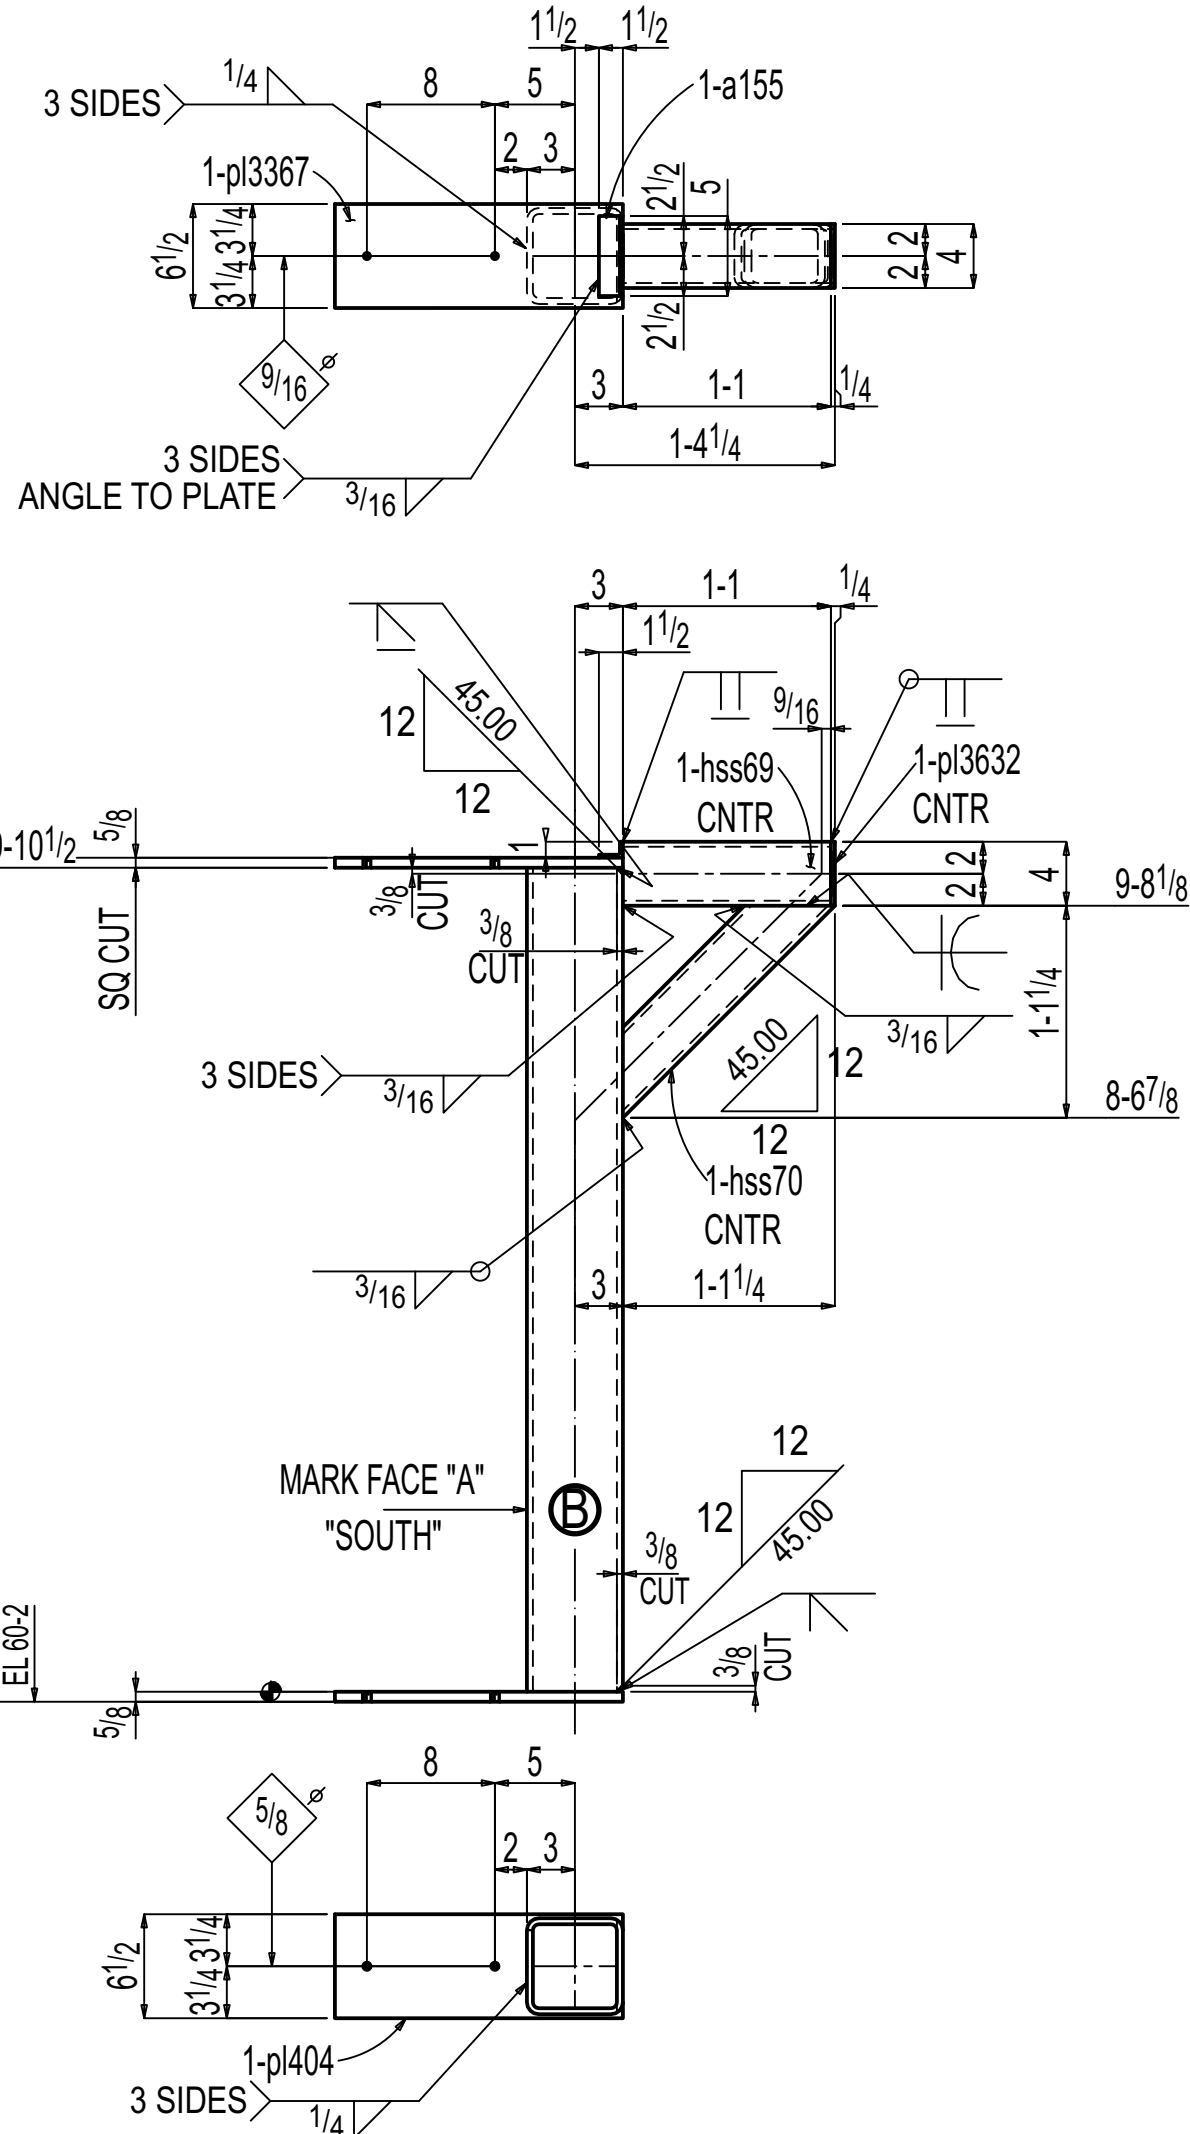

AT GRID:
AA & K

ONE COLUMN F-08.00C4

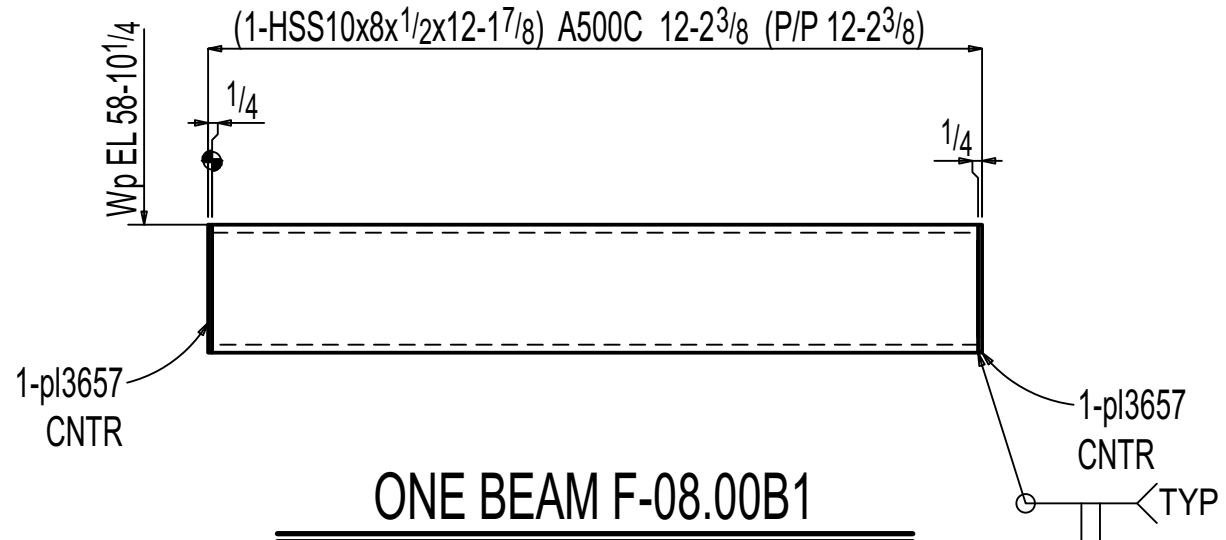

ONE BEAM F-08.00B1

PAINT :NO PAINT
PREPARATION :SSPC-SP3

General Notes			
*Structural steel shall conform to ASTM-A992.			
*Structural SQR/RND,tubing conform to ASTM A500 Grade C			
*Pipe shall conform to ASTM A53, Grade B.			
*Channels, Angles and plates shall conform to A36.			
*All bolts shall be 3/4" High strength in accordance with ASTM A325 (UNO)			
*Welding Electrodes for Carbon steel :E70xx			
5	0	For Fabrication	11-03-2025
4	D	For Re-Approval	10-24-2025
3	C	For Re-Approval	09-19-2025
2	B	For Re-Approval	06-23-2025
1	A	For Approval	02-25-2025
# of Copies	Revision/ Issue	Destination	Date

IRON FABRICATION SERVICES, LLC.

3029 M. Street, NW, Suite 202
Washington, DC 20007
Tel: 202-800-5599
Fax: 202-478-0303

Project Name and Address
MARYLAND AVENUE
Location: **1250 MARYLAND AVENUE SW
WASHINGTON, DC 20024**

Contractor:
BALFOUR BEATTY

Approved for Fabrication by: Signature

Contract # **224009** Drawing # **F-08.00**

Contract Item: **COLUMN ,BEAM**

Ref:
SOW - 08: E-08.00 - E-08.04

Date **01/ 23/ 2025** Drawing Title: **COLUMN & BEAM DETAIL**
Scale **VARIES**