
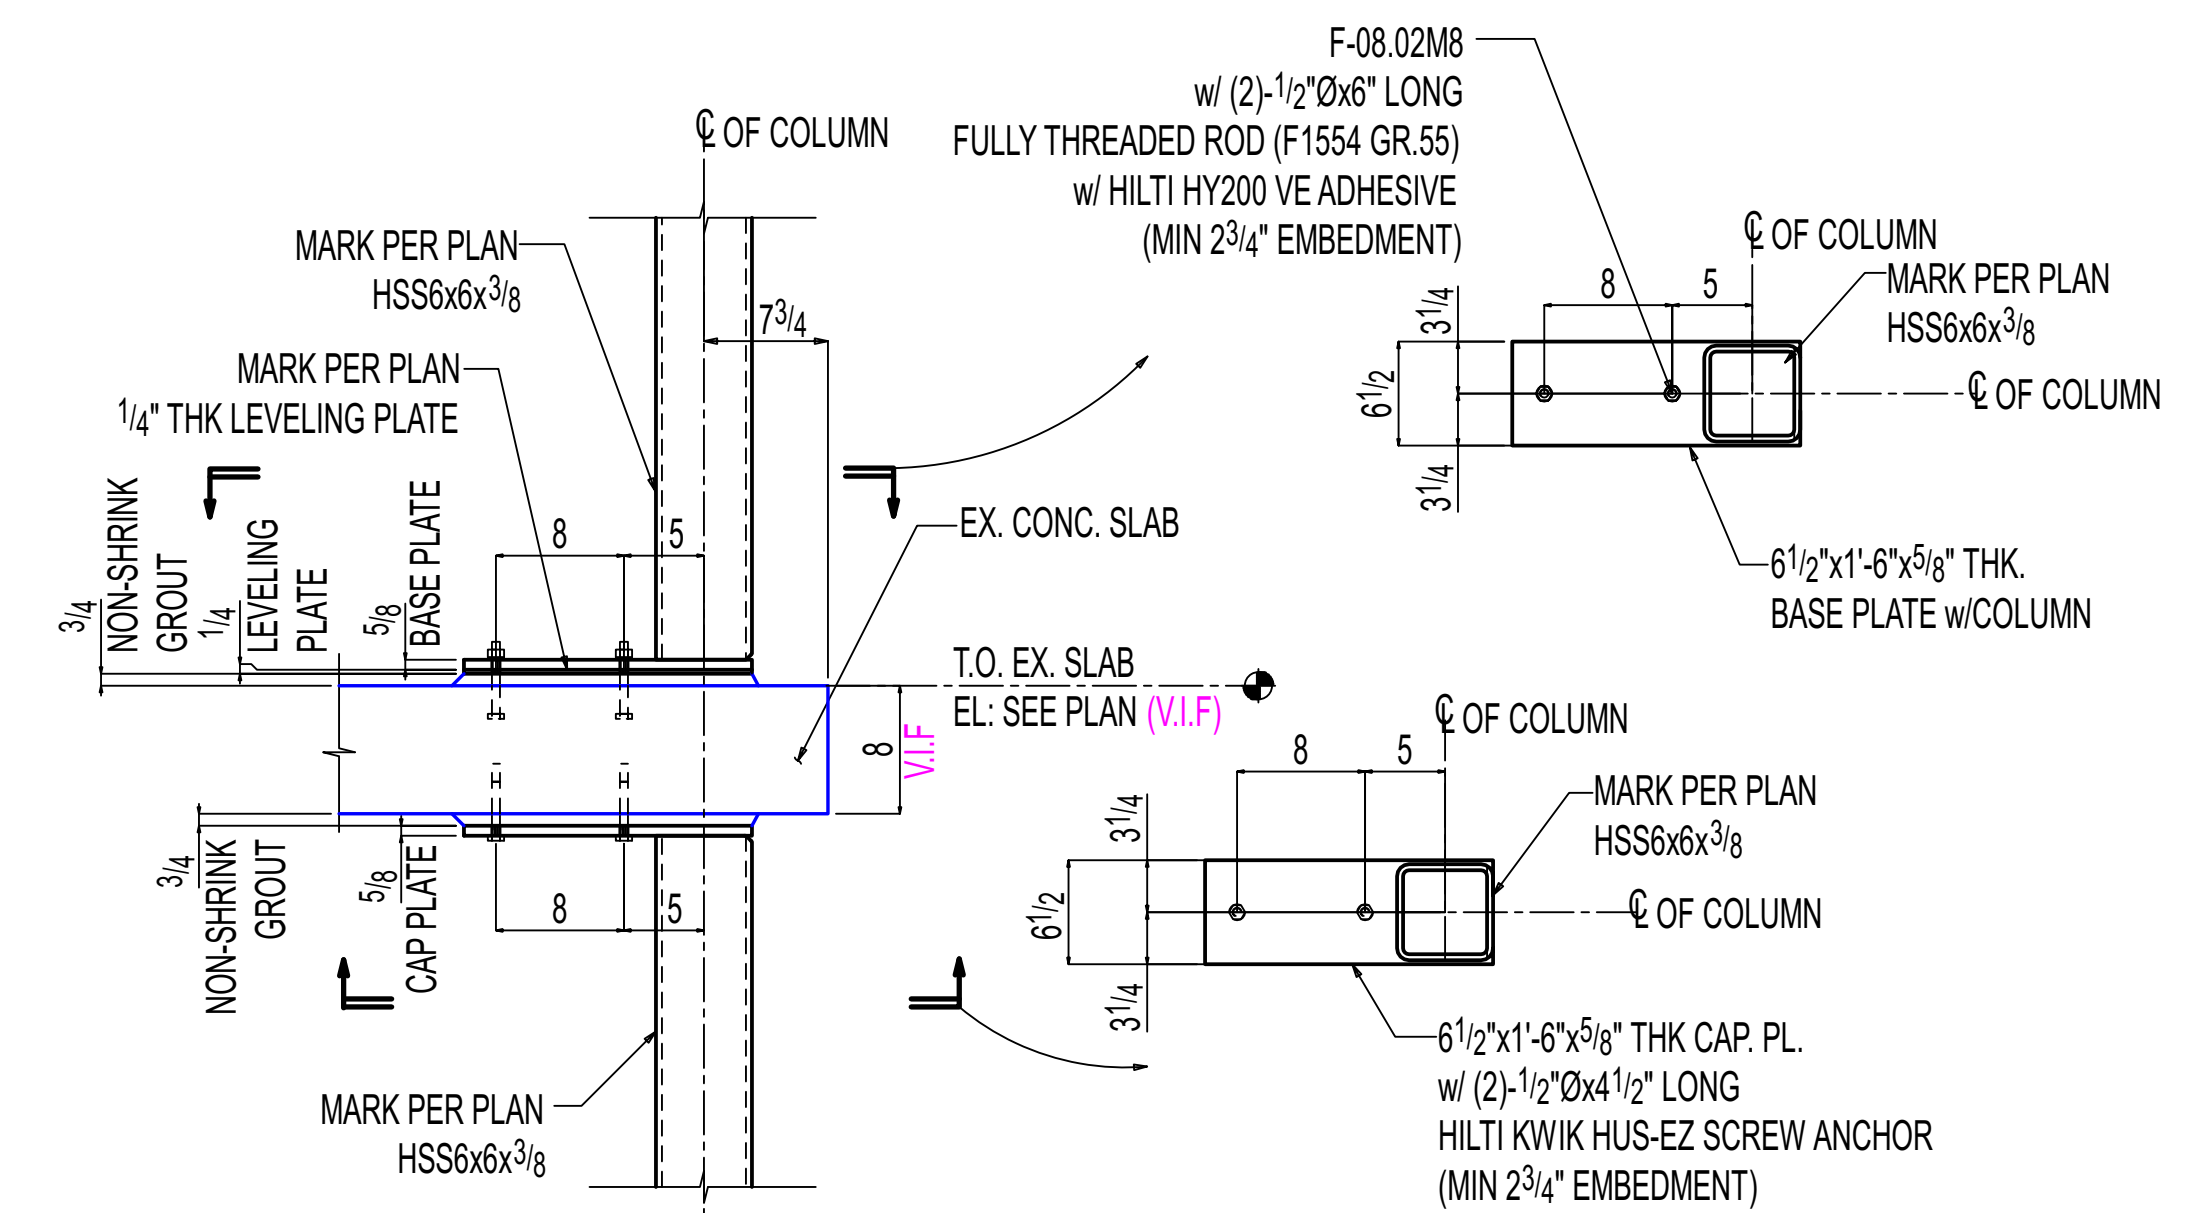


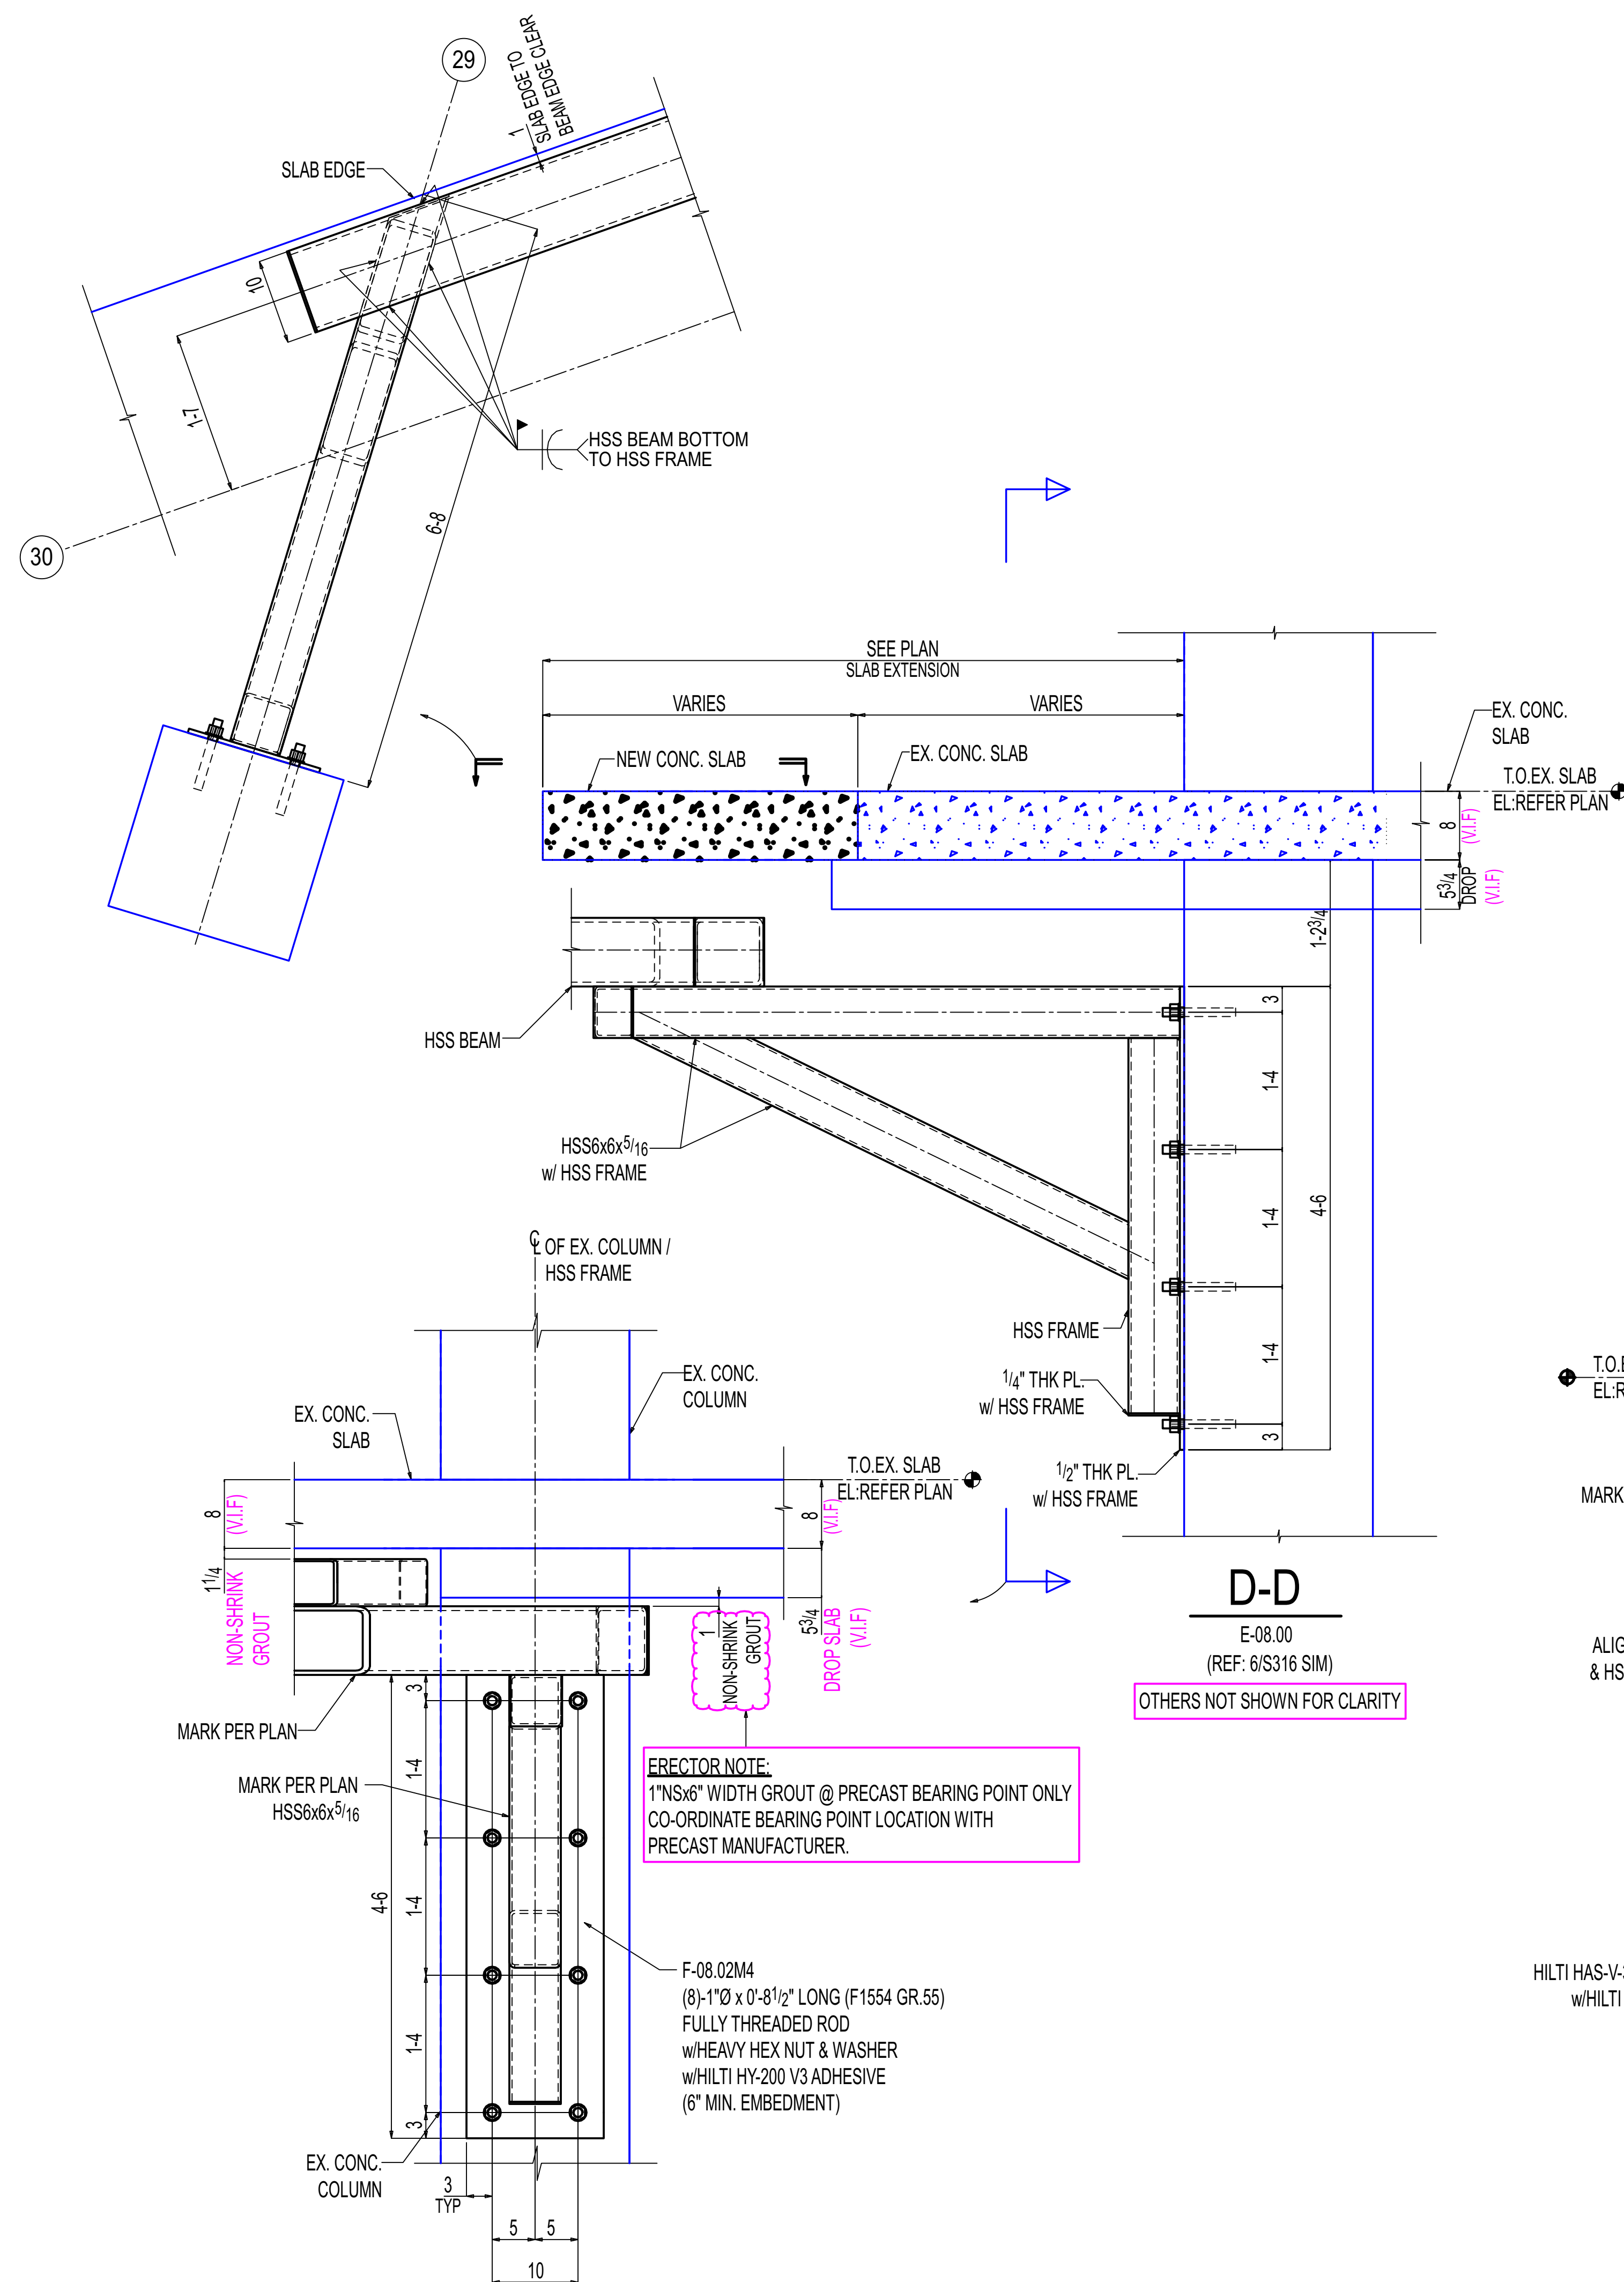


G-G

E-12.00
(REF: 3/S317)

OTHERS NOT SHOWN FOR CLARITY

ERECTOR NOTE:
1"NSx6" WIDTH GROUT @ PRECAST BEARING POINT ONLY
CO-ORDINATE BEARING POINT LOCATION WITH
PRECAST MANUFACTURER.

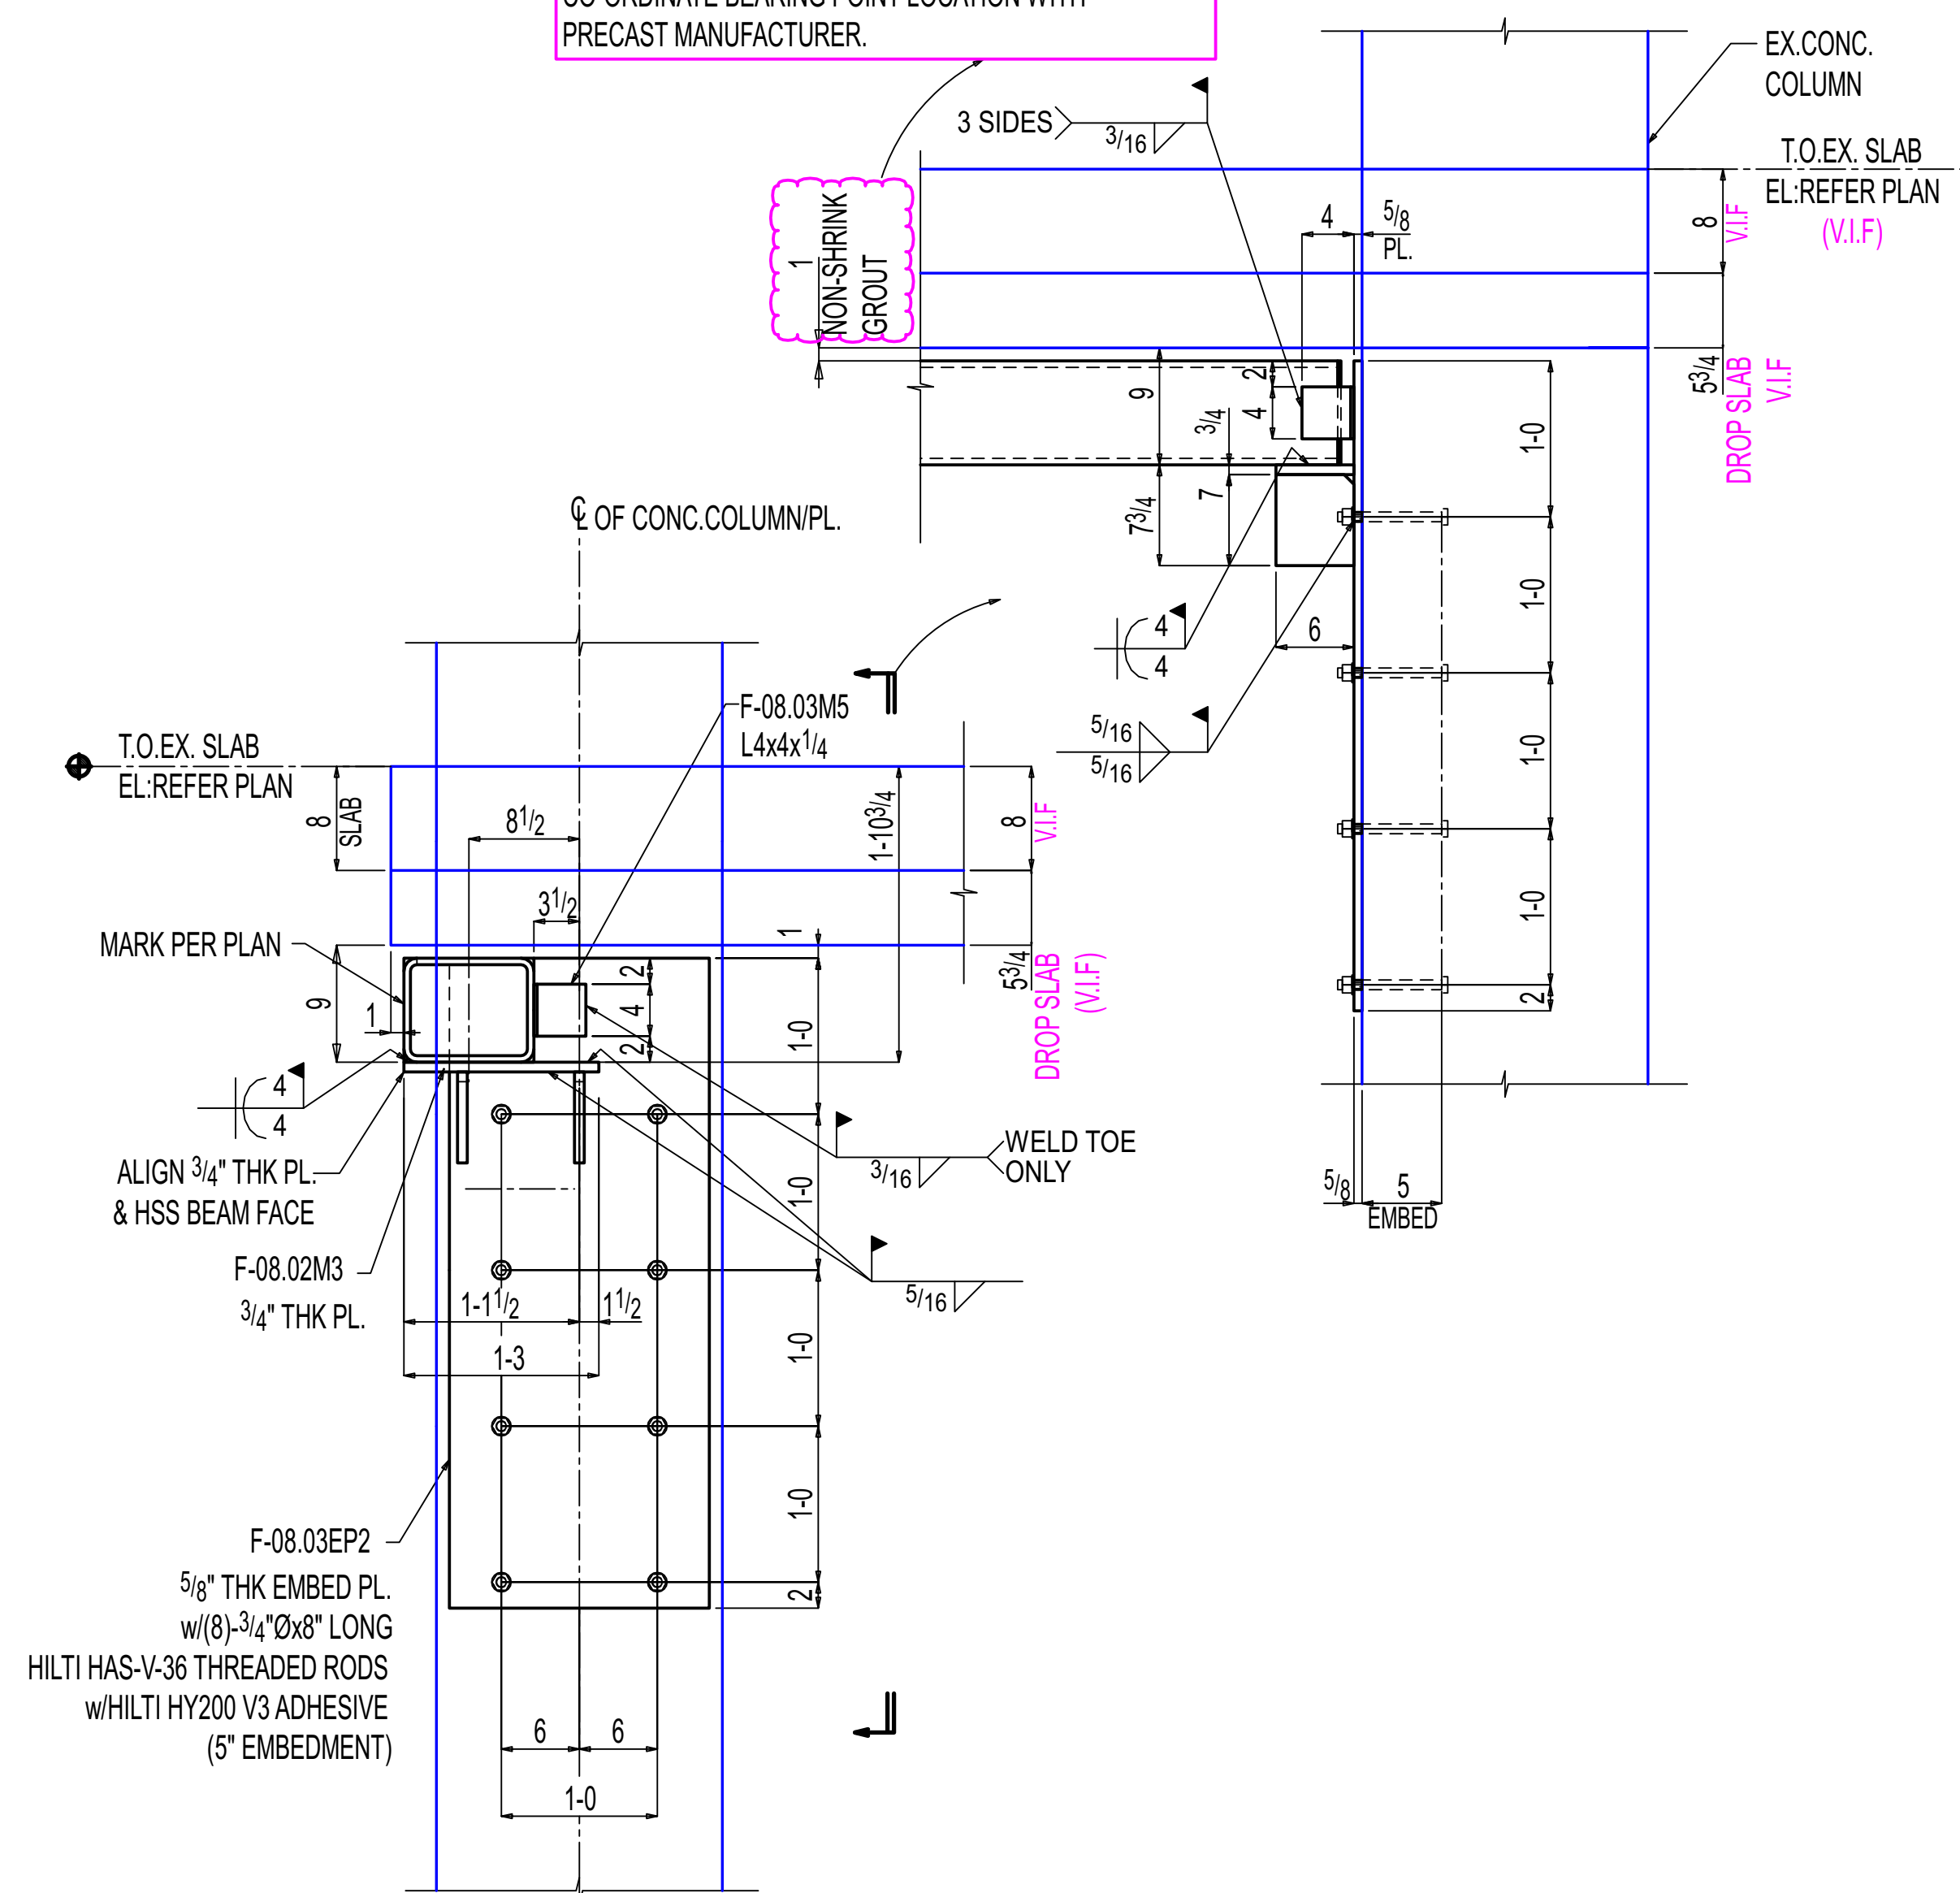

F-F

E-08.00
(REF: 6/S315)

OTHERS NOT SHOWN FOR CLARITY

General Notes

- *Structural steel shall conform to ASTM-A992.
- *Structural SQR/RND.tubing conform to ASTM A500 Grade C
- *Pipe shall conform to ASTM A53, Grade B.
- *Channels, Angles and plates shall conform to A36.
- *All bolts shall be $\frac{3}{4}$ " High strength in accordance with ASTM A325 (UNO)
- *Welding Electrodes for Carbon steel :E70xx

5	0	For Construction	11-03-2025
4	D	For Re-Approval	10-24-2025
3	C	For Re-Approval	09-19-2025
2	B	NOT IN USE	06-23-2025
1	A	For Approval	02-25-2025
# of Copies	Revision/ Issue	Destination	Date

IRON FABRICATION SERVICES, LLC.

3029 M. Street, NW, Suite 202
Washington, DC 20007
Tel: 202-800-5599
Fax: 202-478-0303

Project Name and Address
MARYLAND AVENUE

Location: **1250 MARYLAND AVENUE SW**
WASHINGTON, DC 20024

Contractor:

BALFOUR BEATTY

Approved for Fabrication by:	Signature
------------------------------	-----------

Contract # 224009	Drawing # E-08.02
--------------------------	--------------------------

Contract Item:	LEVEL-02 SLAB EXTENSION
----------------	------------------------------------

Ref: **SOW-08:3,4,5&6 / S307**

Date 01/ 20/ 2025	Drawing Title: SOW #08 LEVEL-02 NEW SLAB EXTENSION SUPPORT SECTIONS
Scale VARIES	